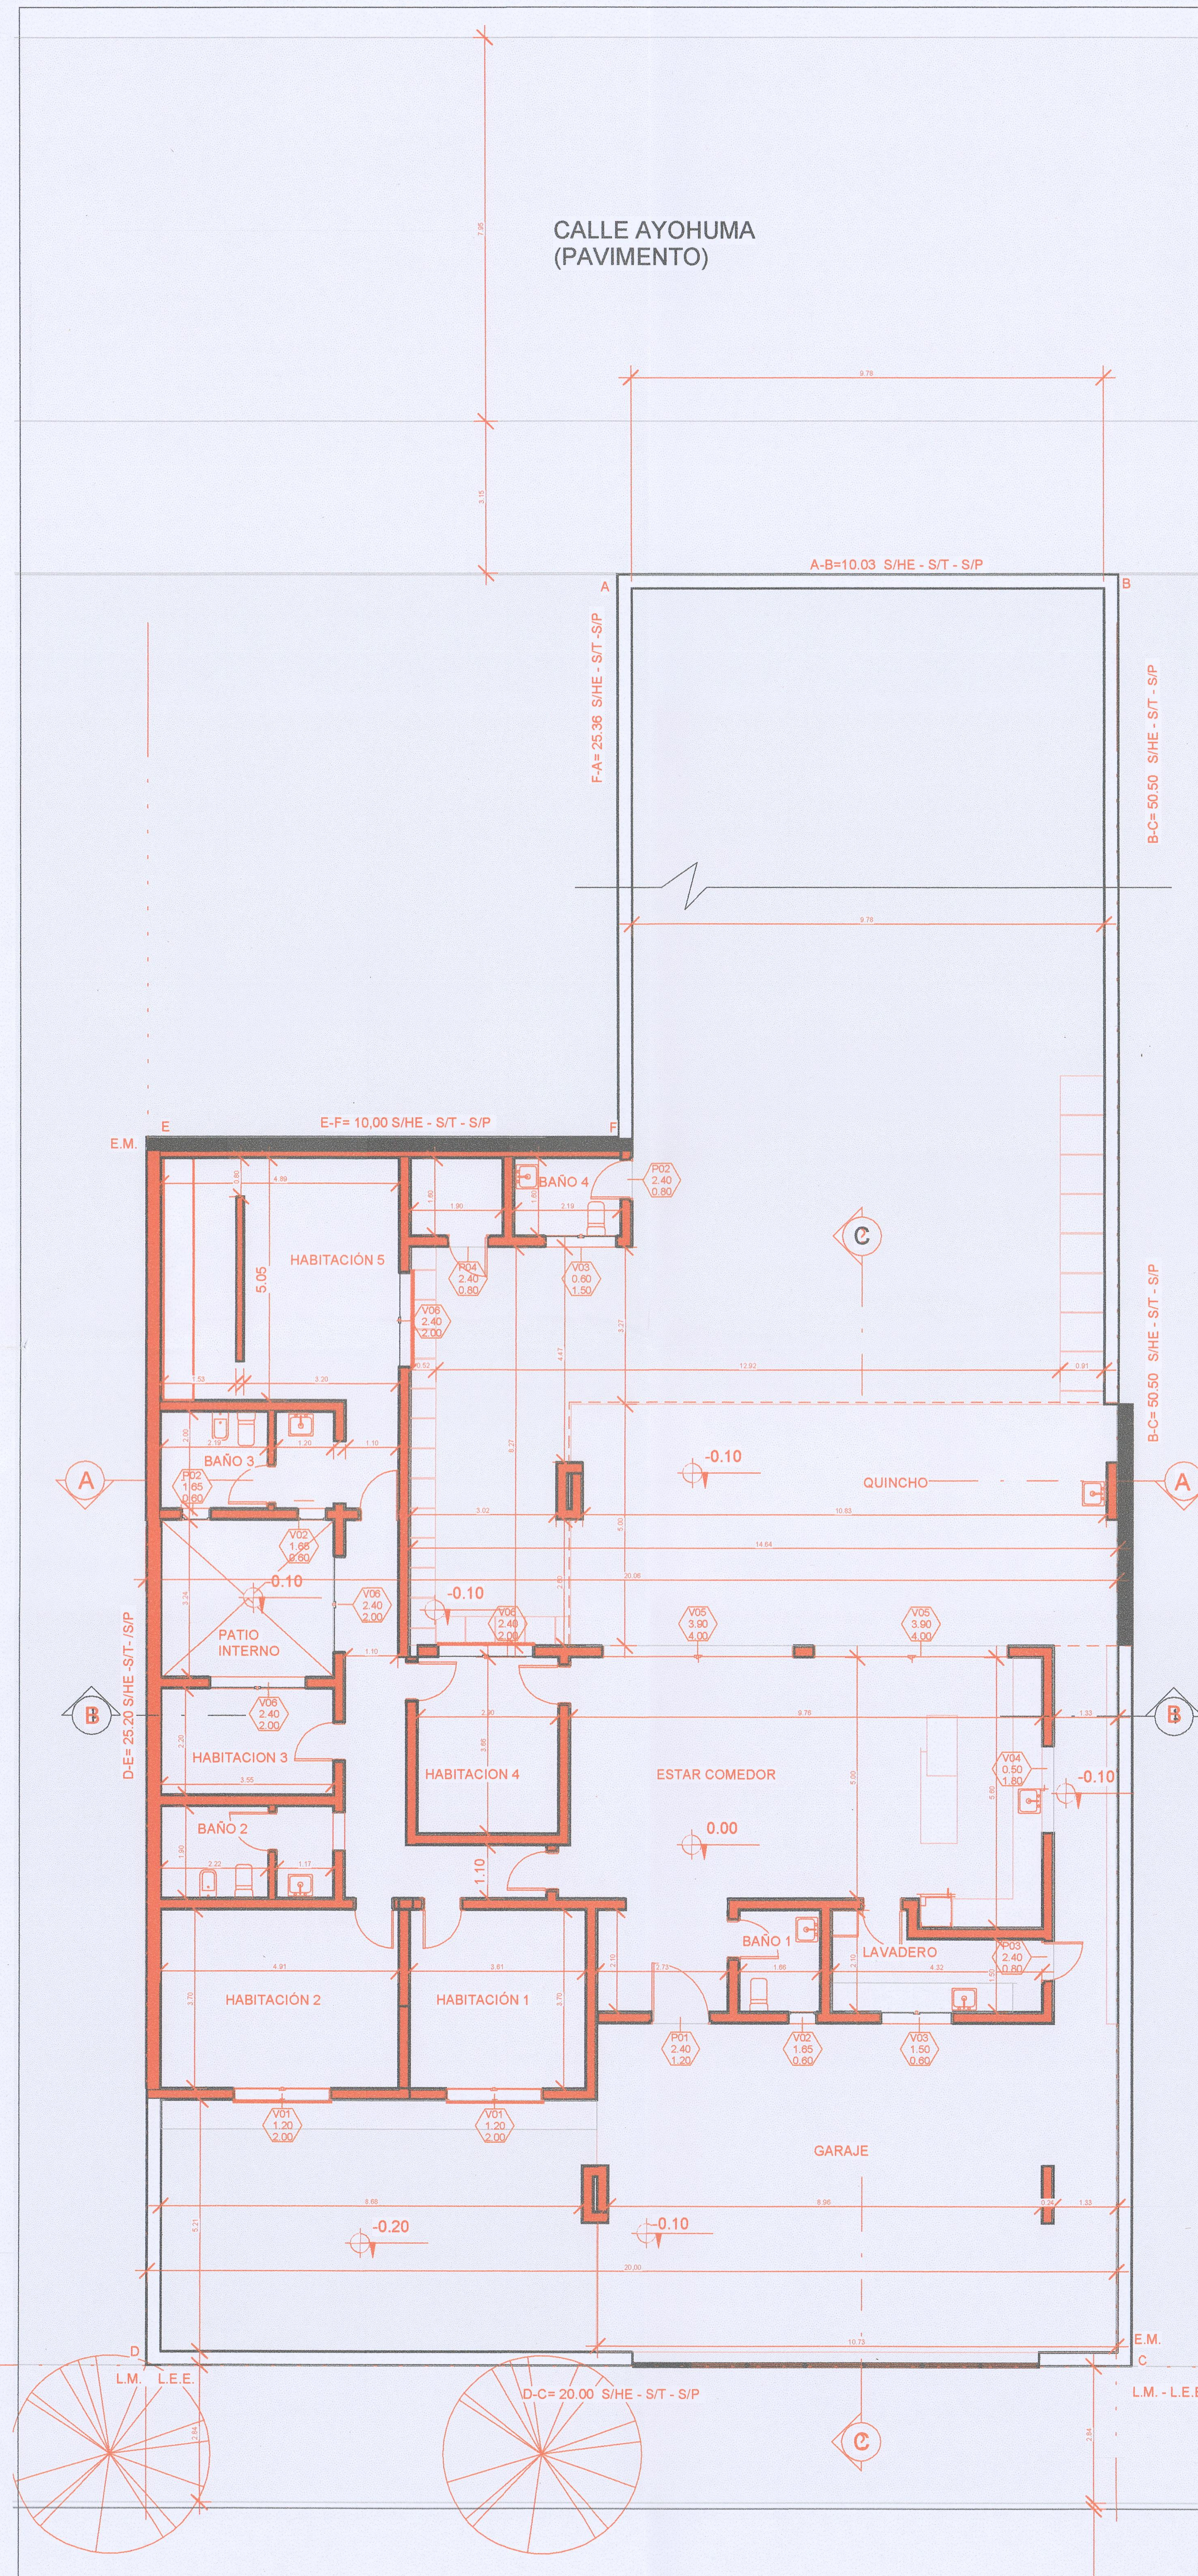

PLANTA BAJA
1:100

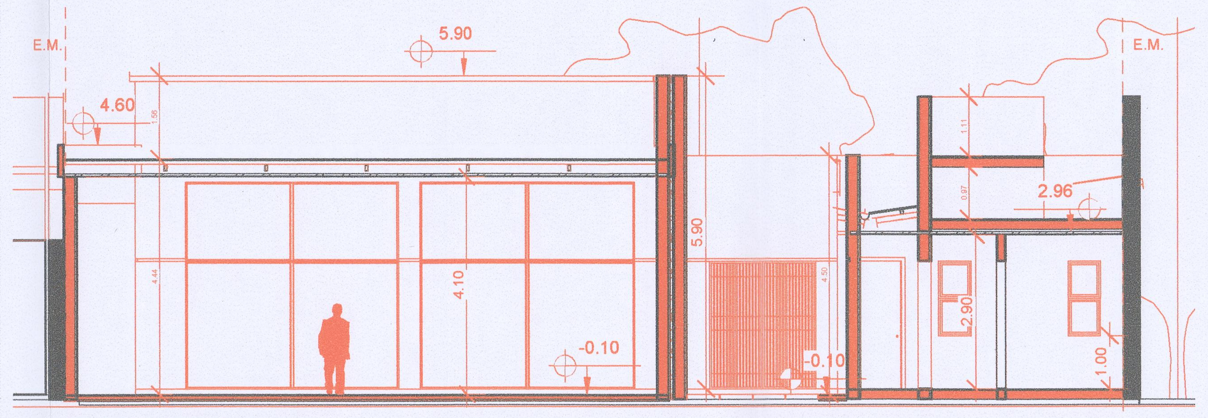

CORTE A-A
1:100

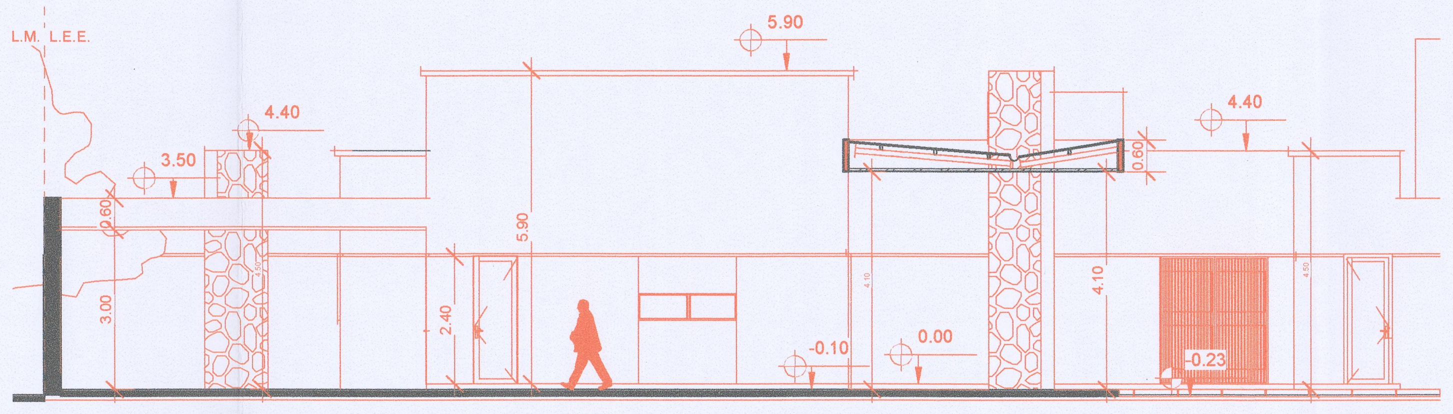

FRENTE 3
1:100

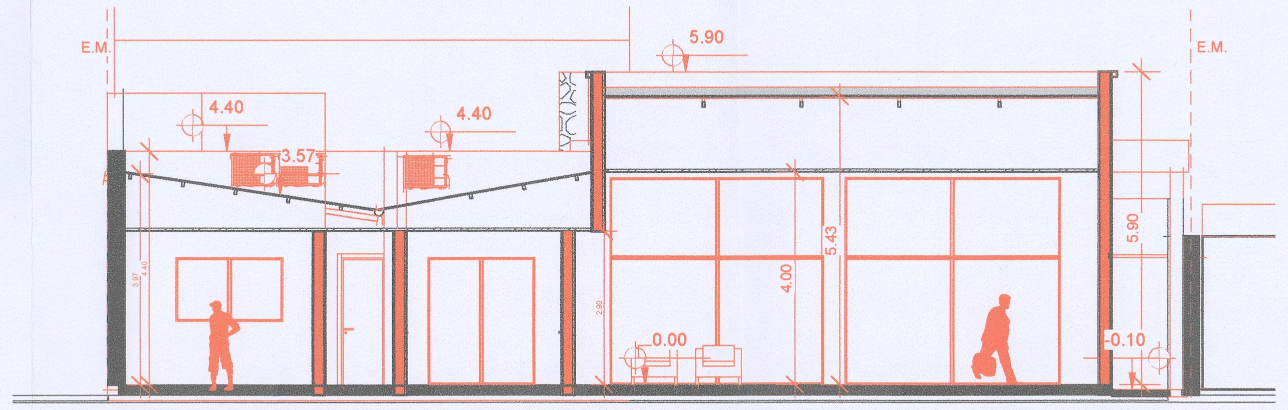

CORTE B-B
1:100

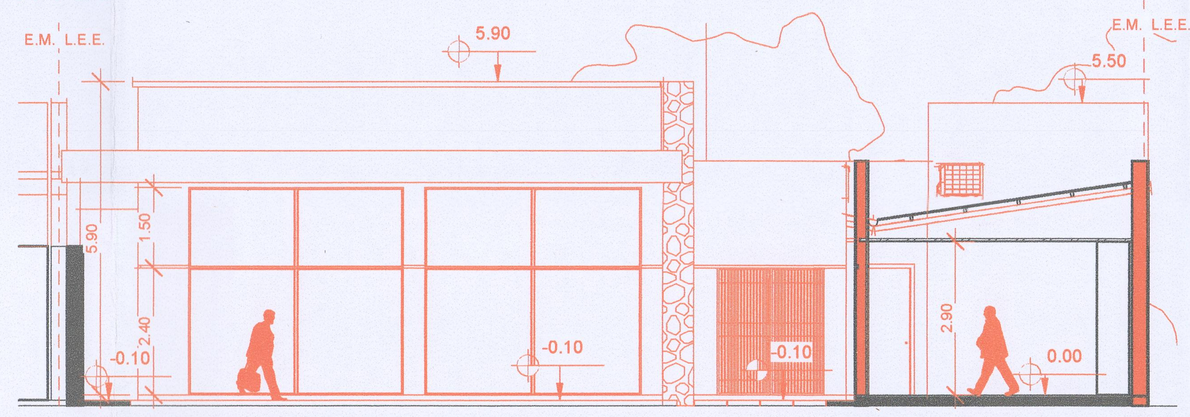

CONTRAFRENTE
1:100

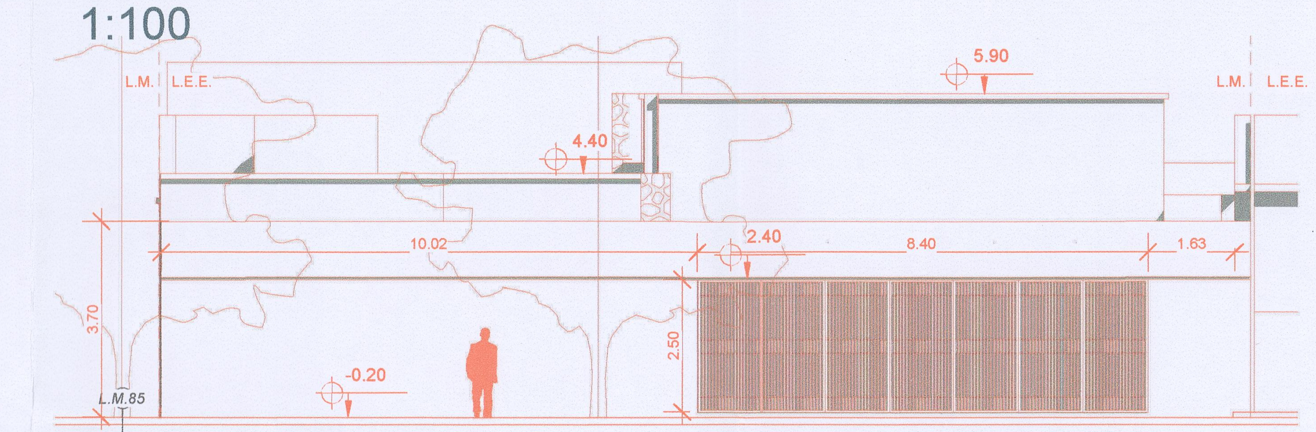

FRENTE 1 VINARA
1:100

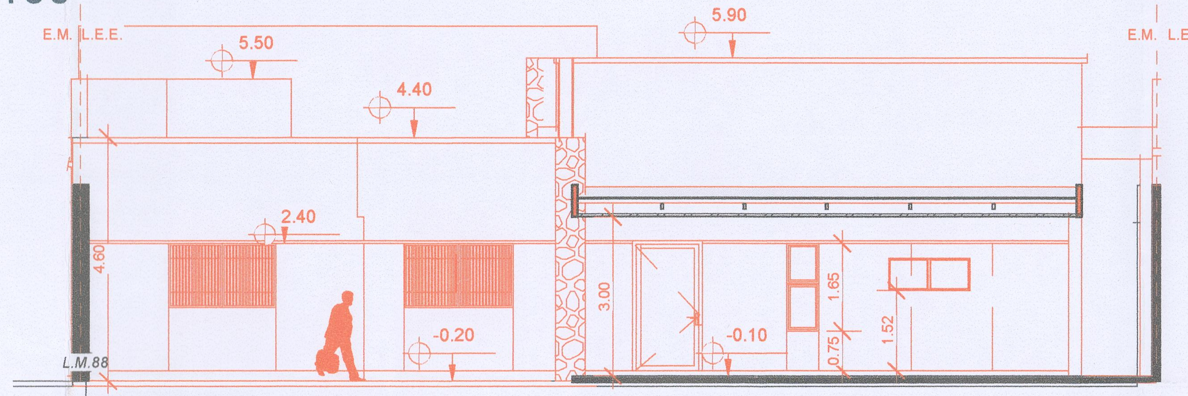

FRENTE 2
1:100

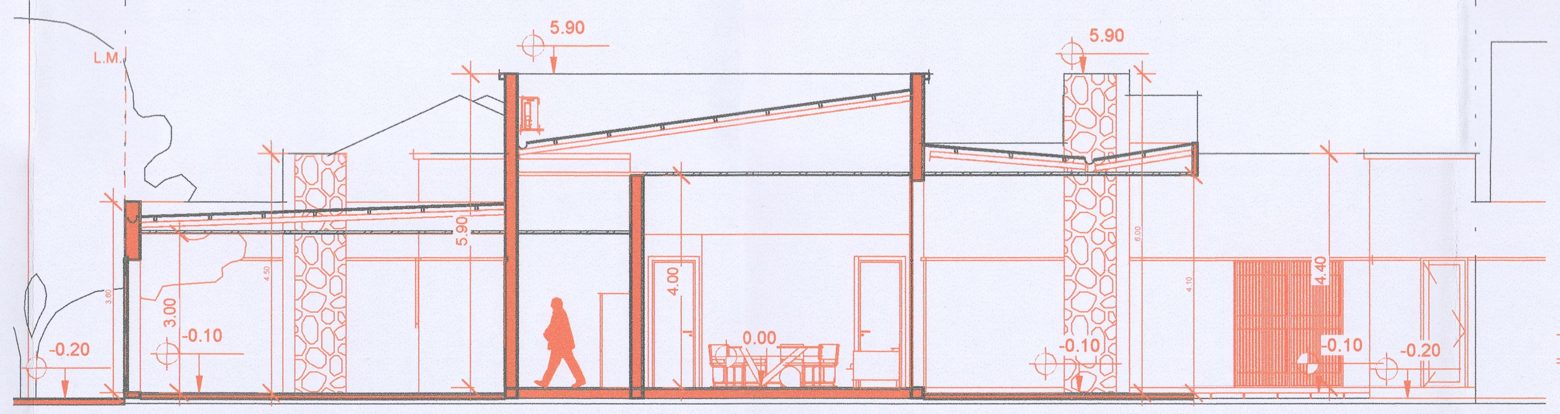

CORTE C-C
1:100

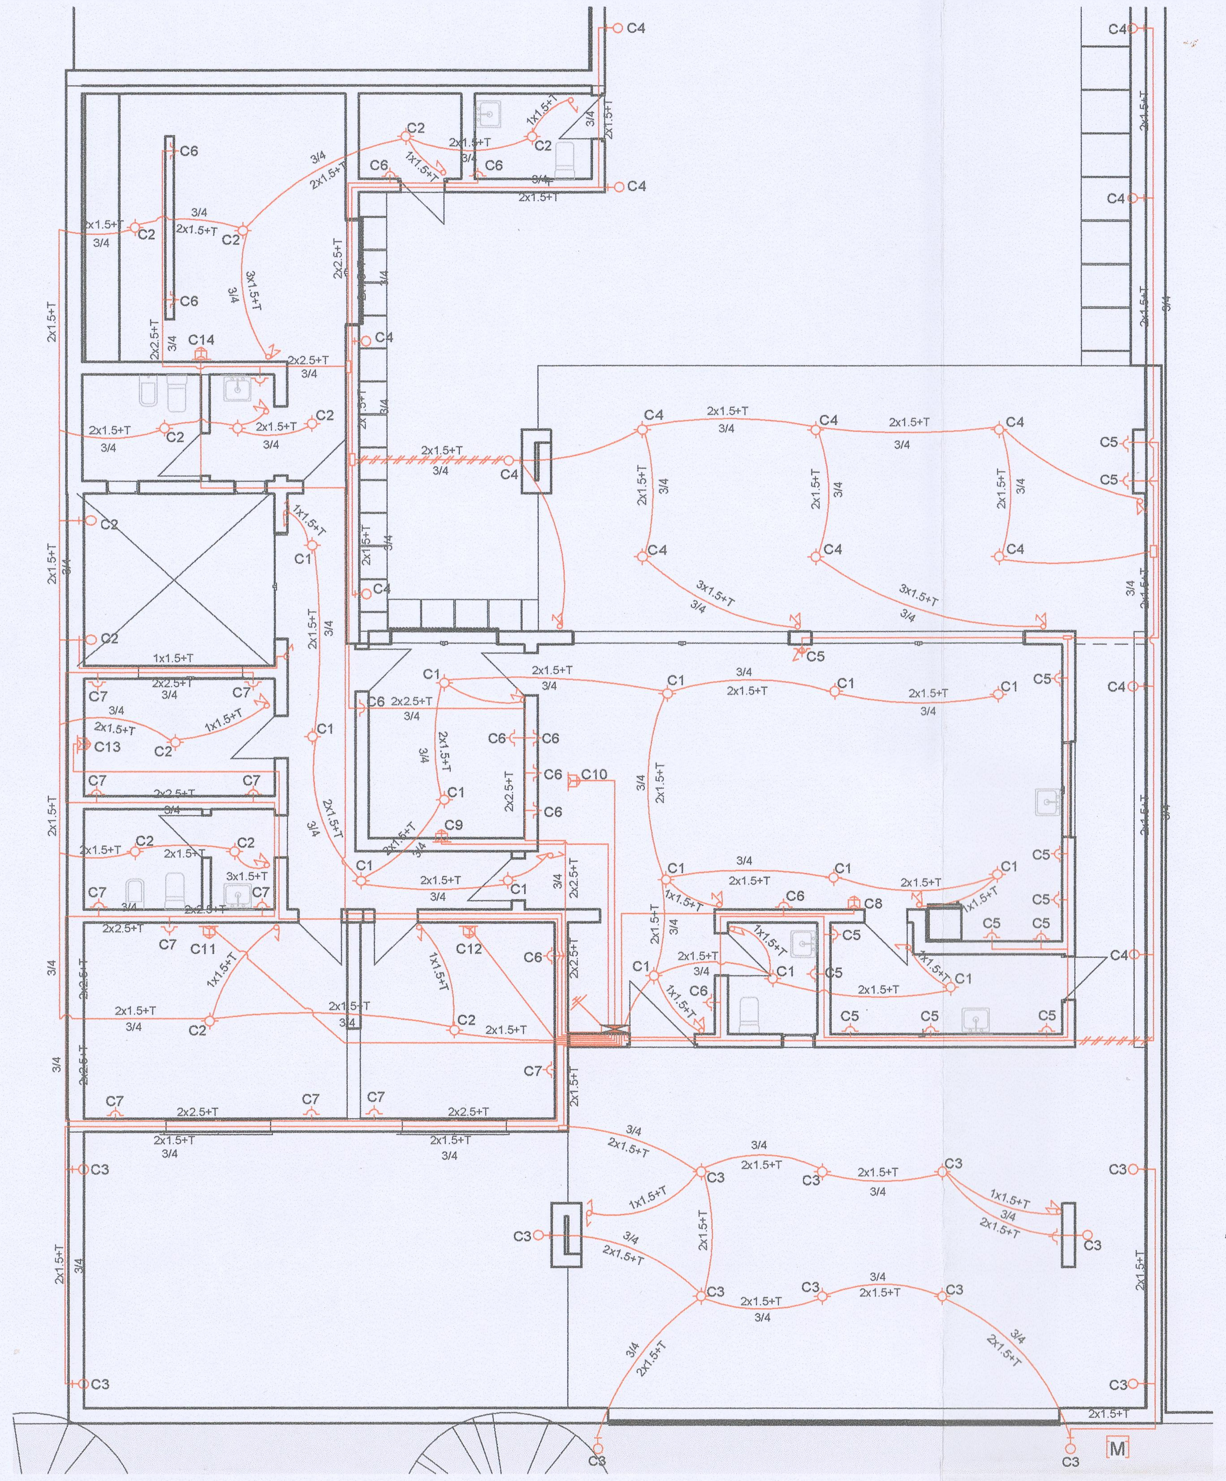

PLANTA INSTALACION ELECTRICA
ESC. 1:100

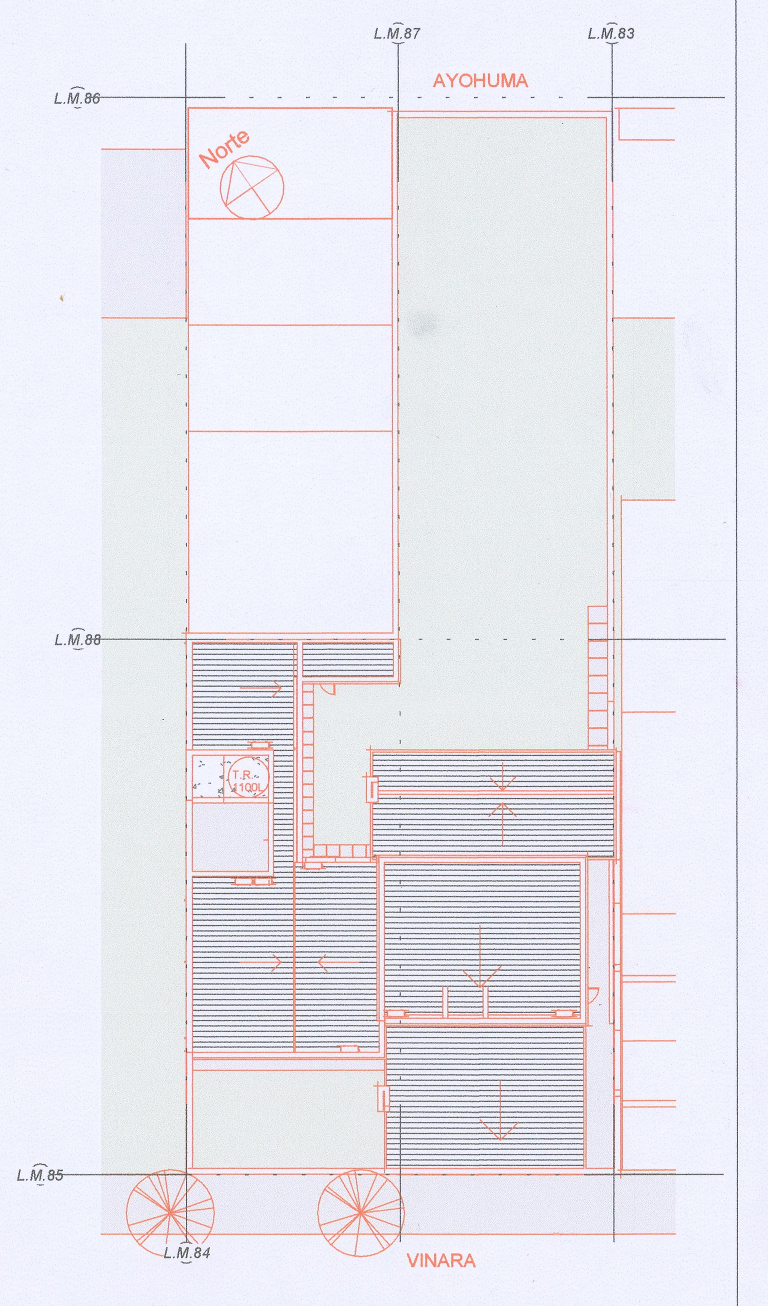

PLANTA DE TECHO
ESC. 1:250

PISO	TABLERO SECCIONAL	CIRCUITO	FASE	ILUMINACION CANT. BOCAS	ILUMINACION POT. (W)	ILUMINACION CORR. (A)	TOMACORRIENTES CANT. BOCAS	TOMACORRIENTES POT. (W)	TOMACORRIENTES CORR. (A)	AIRE ACONDICIONADO CANT. BOCAS	AIRE ACONDICIONADO POT. (W)	AIRE ACONDICIONADO CORR. (A)	OTRAS CARGAS CANT. BOCAS	OTRAS CARGAS POT. (W)	OTRAS CARGAS CORR. (A)	POT. (W)	GRADO ELECTRIFICACION	FACTOR SIMULTANEIDAD	POT MAX DEL INMUEBLE (W)
		C1 - ILUM INTERIOR		15	40	2.7													
		C2 - ILUM INTERIOR		13	40	2.4													
		C3 - ILUM INTERIOR		13	40	2.4													
		C4 - ILUM EXTERIOR		15	40	2.7													
		CT5 - TUG					10	2200	10										
		CT6 - TUG					10	2200	10										
		CT7 - TUG					11	2200	10										
		CT8 - AA								1	1100	5							
		CT9 - AA								1	1100	5							
		CT10 - AA								1	1100	5							
		CT11 - AA								1	1100	5							
		CT12 - AA								1	1100	5							
		CT13 - AA								1	1100	5							
		CT14 - AA								1	1100	5							
																14420	bajo	0.6	8652
POTENCIA TOTAL DE LA VIVIENDA																			8652
COEFICIENTE DE SIMULTANEIDAD PARA VIVIENDA																			0,6
POTENCIA MAXIMA SIMULTANEA DE LA VIVIENDA																			**5191.2**

PLANILLA DE CARGAS
ESC. 1:100

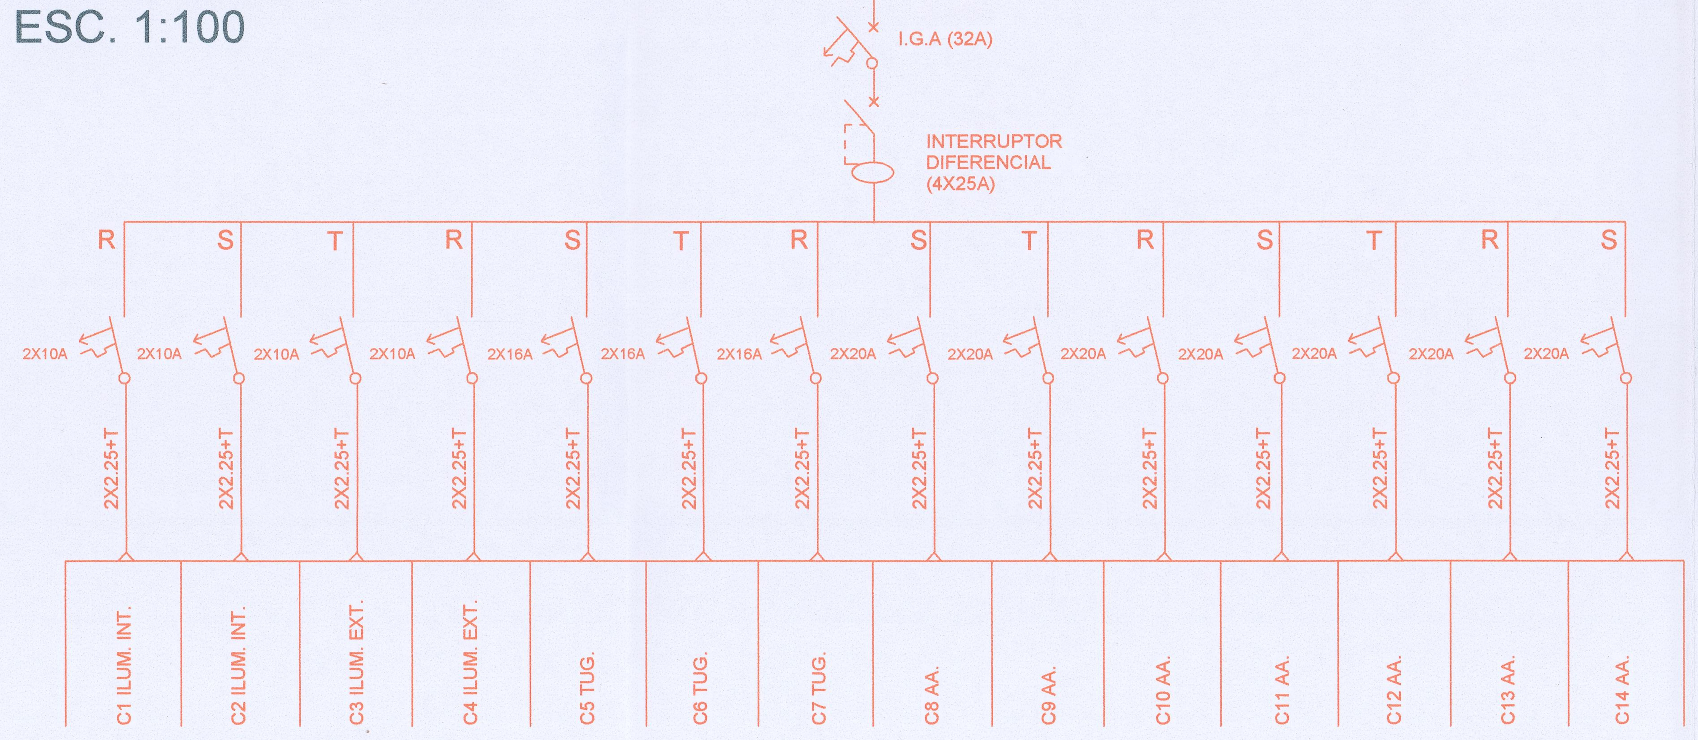

ESQUEMA UNIFILAR
ESC. 1:100

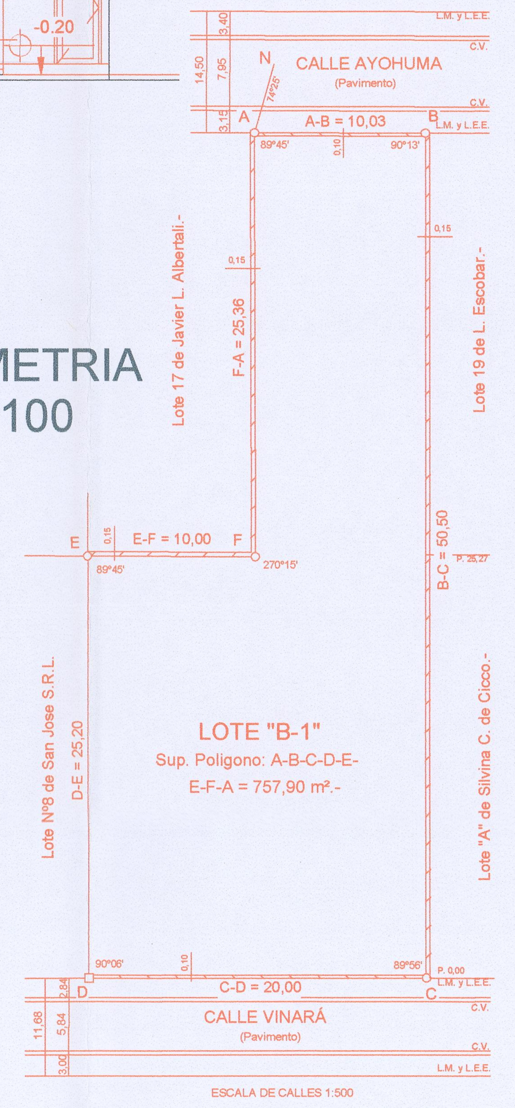

PLANIMETRIA
ESC. 1:100

PLANTA BAJA							
LOCALES	SUP.						OBS.
Designación	m2	design	ancho m	alto m	AREAS I	AREAS V	
ESTAR - COMEDOR	57.78	P01	1.20	2.40	-	2.88	
		V05	4.00	3.90	15.60	15.60	
		V05	4.00	3.90	15.60	15.60	
		V04	1.80	0.50	0.90	0.90	
LAVADERO	7.41	P02	0.80	2.40	1.92	1.92	
BAÑO 1	3.48	V02	1.65	0.60	0.90	0.90	
HABITACION 1	13.70	V01	1.20	2.00	2.40	2.40	
HABITACION 2	18.09	V01	1.20	2.00	2.40	2.40	
HABITACION 3	10.60	V06	2.40	2.00	4.80	4.80	
HABITACION 4	7.81	V06	2.40	2.00	4.80	4.80	
HABITACION 5	24,70	V06	2.40	2.00	4.80	4.80	
BAÑO 2	6.44						EXTRACTOR
BAÑO 3	6.78	V02	1.65	0.60	0.99	0.99	
		V02	1.65	0.60	0.99	0.99	
DEPOSITO	24,70	P04	0.80	2.40	-	1.92	

PLANILLA DE ILUMINACION Y VENTILACION
ESC. 1:100

DPTO.:02 ZONA: 09 MANZ.:38 PARC.:63 - 163 LEY 4683

PADRÓN INMOB.: 0101156218 DOMINIO:7S-39393 ICM: 339-R-25

25080684

DEST. DE LA OBRA: Vivienda

PROPIETARIO: Rosalia Andrea Rampulla. D.N.I. 36.045.099
CUIL: 27-36045099-1

UBICACIÓN: Vinara N°55 lote 6 mza "J" contraf. Ayohuma N°54 lote 18 mza "J"

BARRIO: Juramento

CIUDAD: Santiago del Estero

ESCALA: 1:100 y 1:200

DIRECCION DE SUELO URBANO
EXPEDIENTE 696/31/25
FECHA DE SELLADO 06 MAR. 2026
BOLETA N° 3824

140126

SUSANA ABECASSIS
Arquitecta
Secretaría Técnica
Colegio de Arquitectos SDE

SUP. TERRENO S/P - S/HE 756.02 m2
SUP. CUBIERTA Y SEMICUBIERTA TOTAL: 358 m2

PROPIETARO: Rosalia Andrea Rampulla
DOMICILIO: Av. Belgrano Sur (s) 3246 B° Cabildo.

CROQUIS DE UBICACIÓN

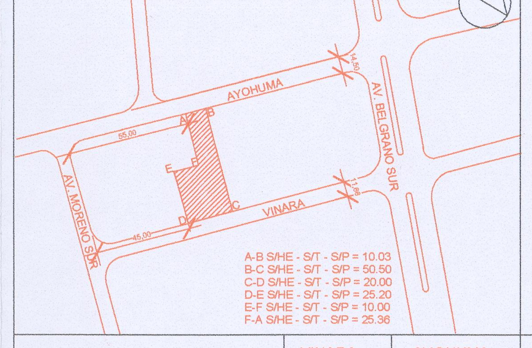

PROYECTO: ANA TAVELLA ARQUITECTA M.P. 656

D. TÉCNICA: ANA TAVELLA ARQUITECTA M.P. 656

ELECTRICIDAD:

DIRECCION DE SUELO URBANO
EXPEDIENTE 696 31 25
FECHA DE SELLADO 12 12 25
BOLETA N° 2217

	VINARA	AYOHUMA
ANCHO DE CALLE:	11.66 m	14.50 m
ANCHO DE VEREDA:	2.84 m	3.15 m
ANCHO DE CALZADA:	5.84 m	7.95 m

CATÉGORIA COLEGIO DE ARQUITECTOS
PAVIMENTO: SI
SERVICIOS CLOACALES: SI

DESIGNACIÓN:

PLANO OBRA NUEVA: ARQUITECTURA E INST. ELÉC. 1

OBSERVACIONES: 06 FEB 2026

Las referencias al Titulo de dominio son meramente indicativas, y la aprobación administrativa no valora los derechos que de ellos emergen.

PERMISO DE COMIENZO DE OBRA N° 221/2026
DIRECCION DE SUELO URBANO

MUNICIPALIDAD DE LA CIUDAD DE SANTIAGO DEL ESTERO
SECRETARIA DE ECONOMIA
APROBADO
DIRECCIÓN DE SUELO URBANO
EXPEDIENTE: 696-31-25 / 15-R-2025
FECHA: 11 MAR 2026

LEANDRO ARJONA
AREA DE VISACIONES TECNICAS
DIRECCION DE CATASTRO MUNICIPAL

ARQ. LOPEZ FEDERICO
SUBDIRECTOR
DIRECCIÓN DE SUELO URBANO
MUNICIPALIDAD DE LA CAPITAL

Arq. Cesar Marcelo Alcorta
Director D.S.U.
Municipalidad de la Capital