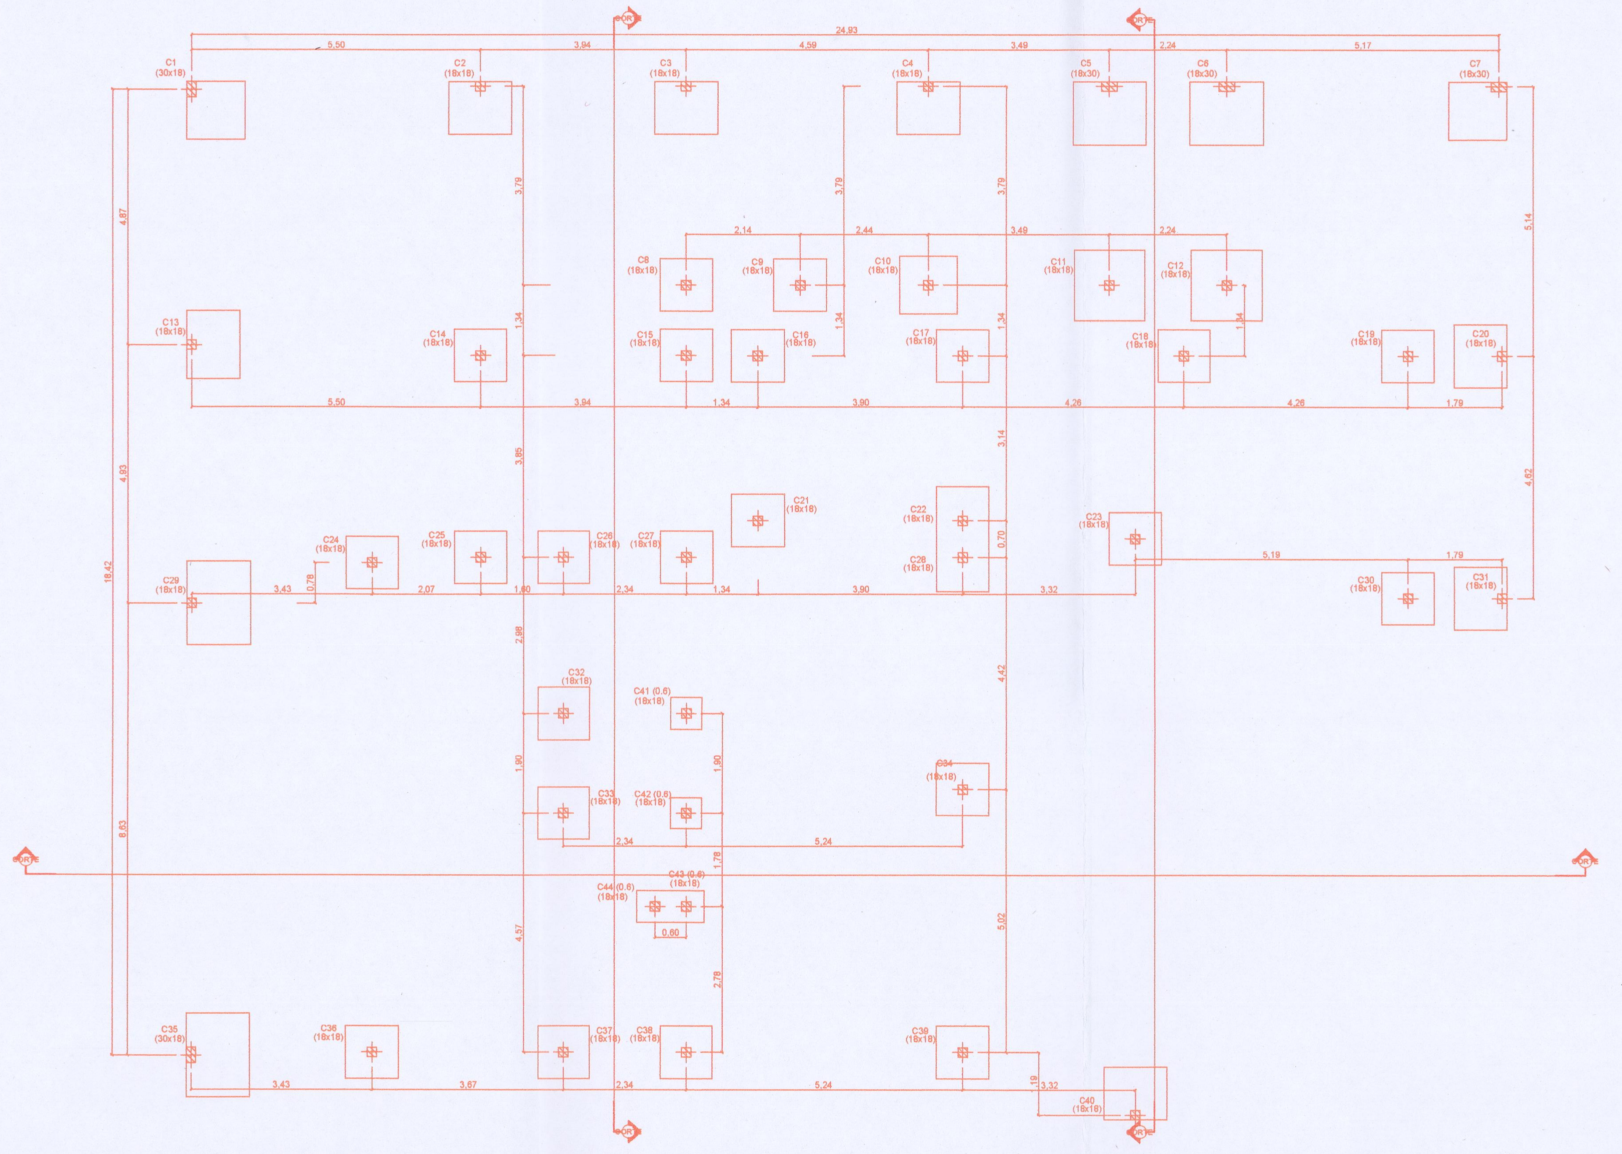

PLANTA DE REPLANTEO FUNDACIONES
ESC. 1.100

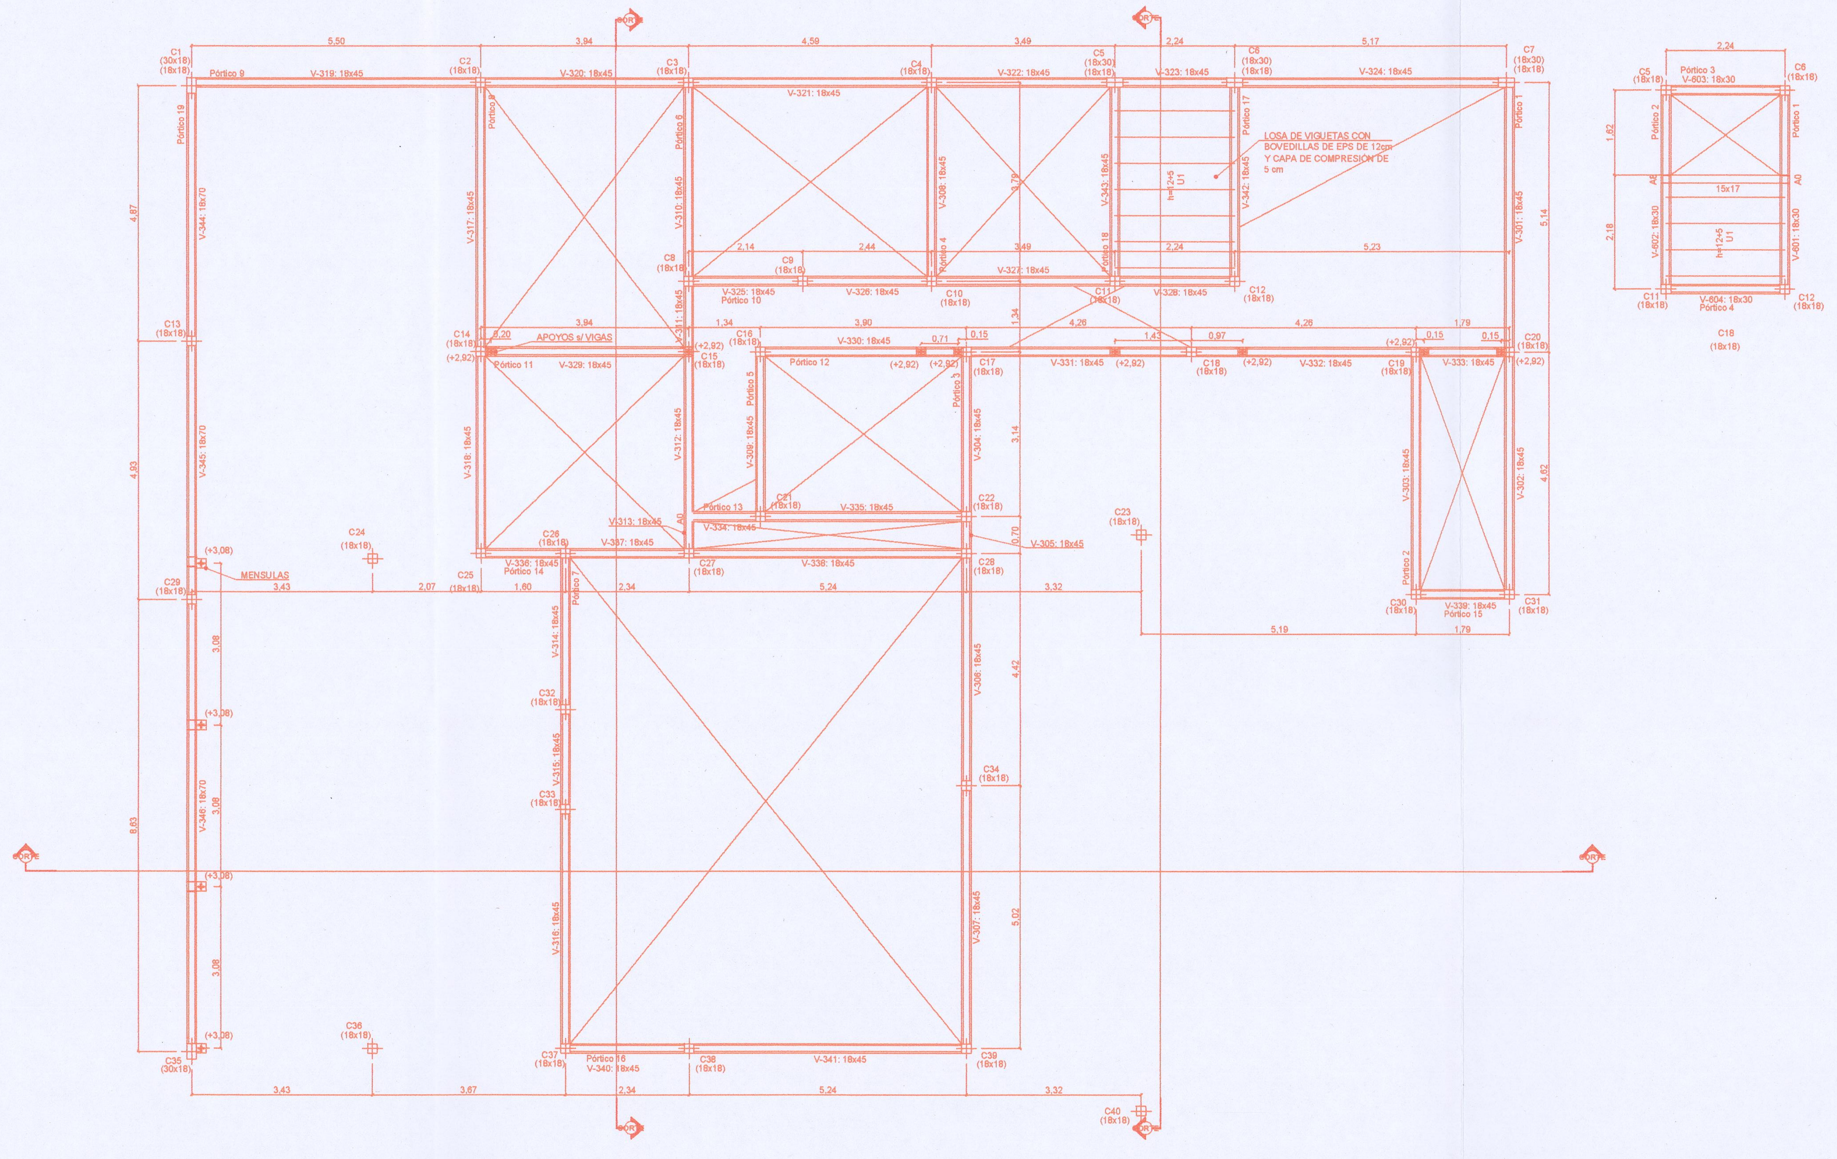

PLANTA DE ESTRUCTURA NIVEL 1
ESC. 1.100

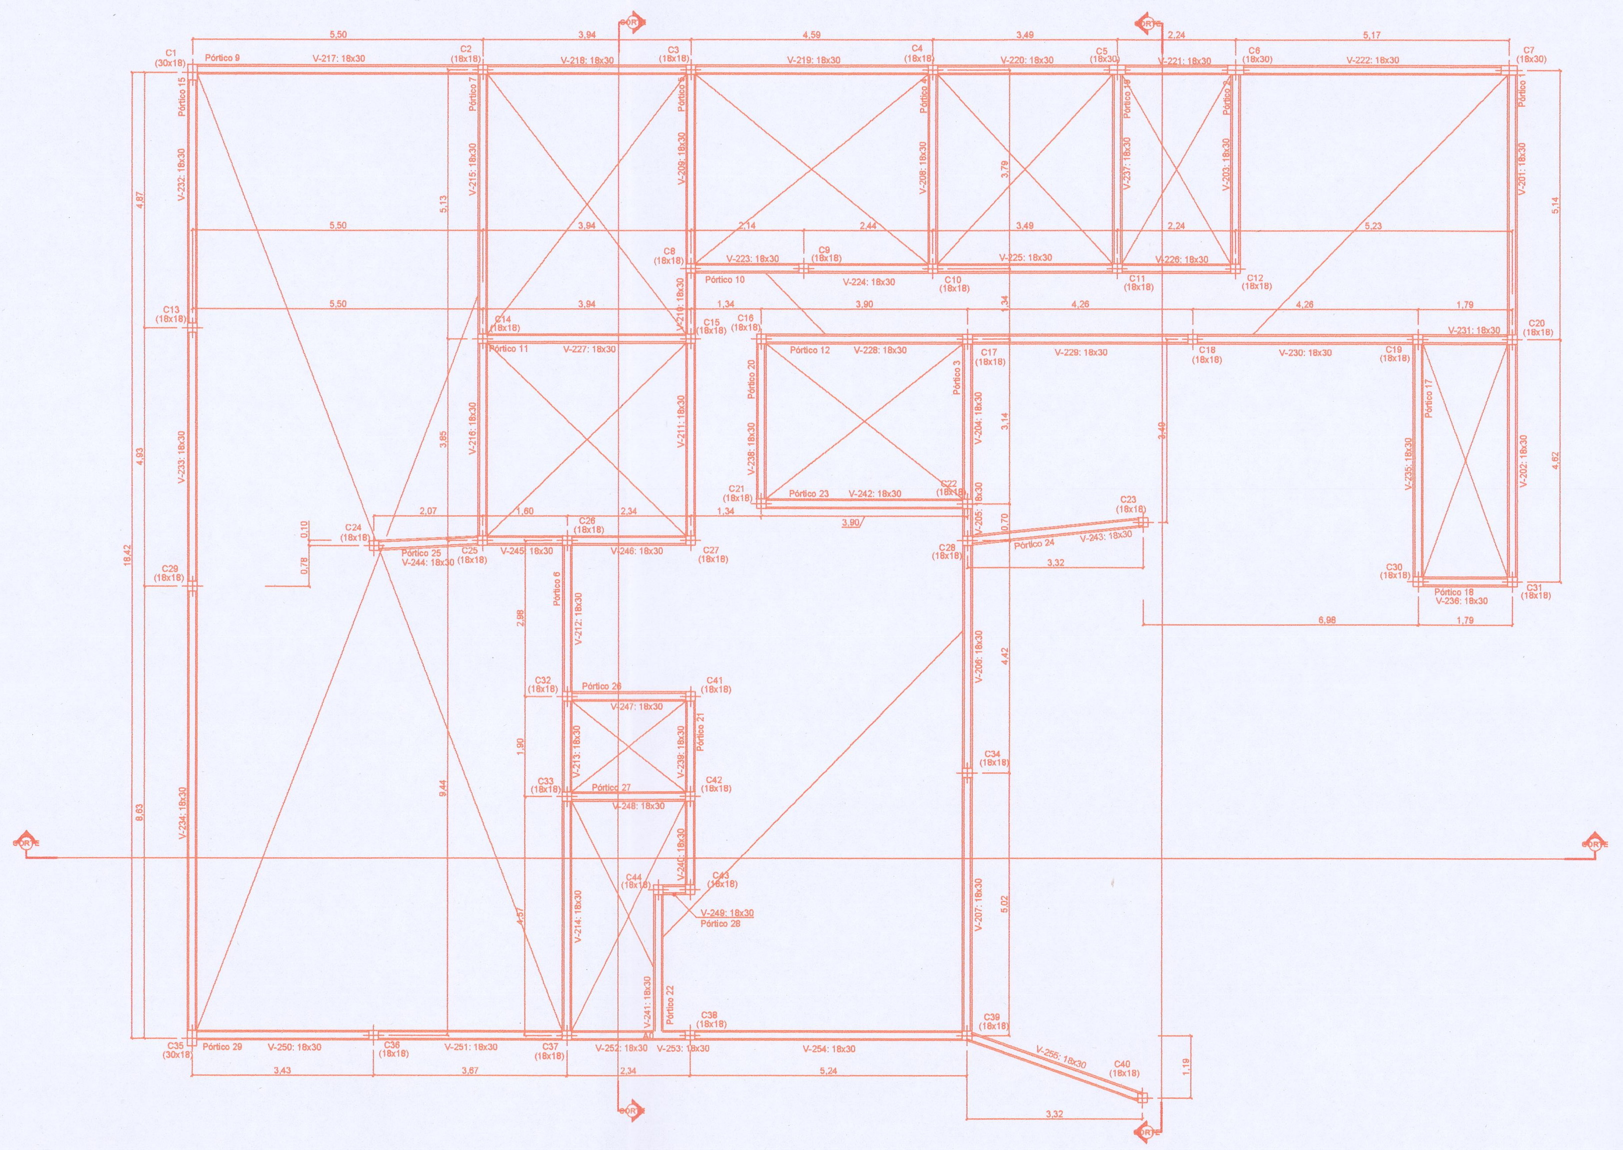

REPLANTEO ENCADENADO INFERIOR
ESC. 1.100

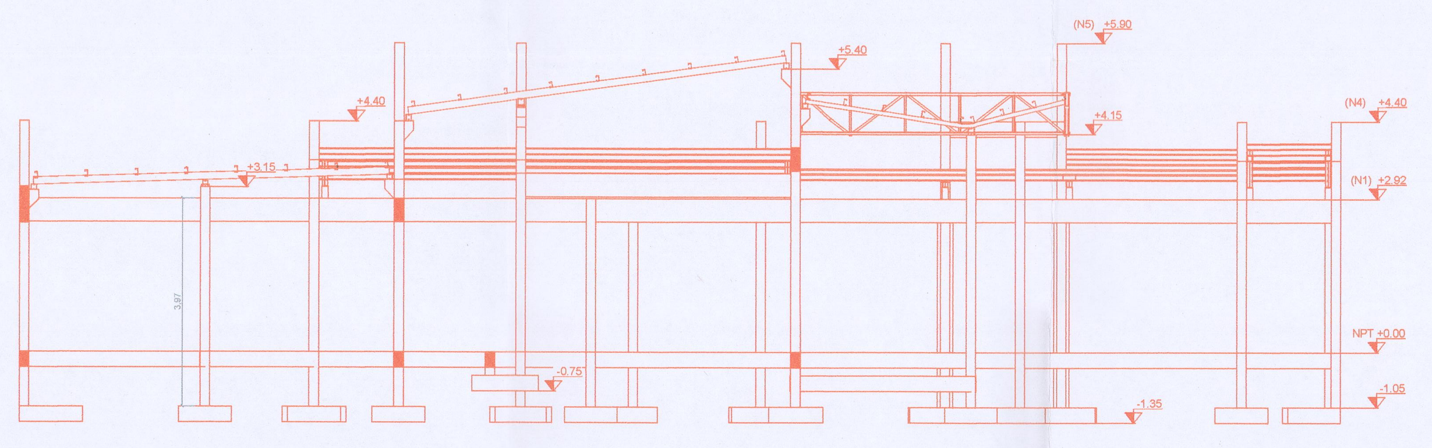

CORTE A-A
ESC. 1.100

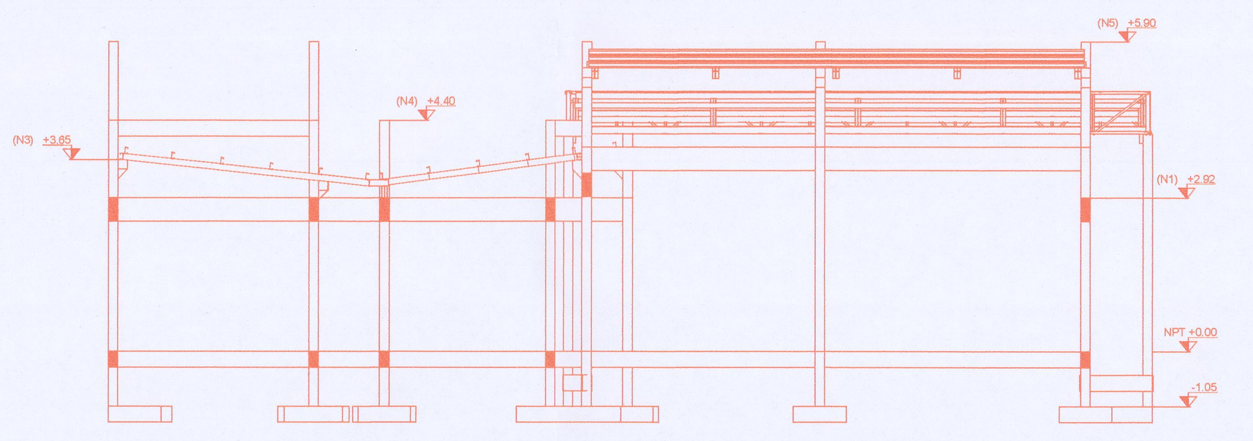

CORTE B-B
ESC. 1.100

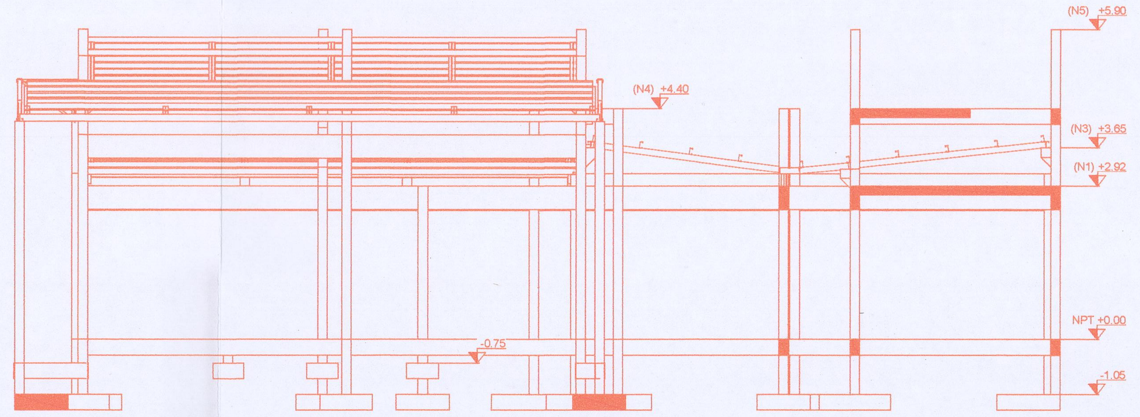

CORTE C-C
ESC. 1.100

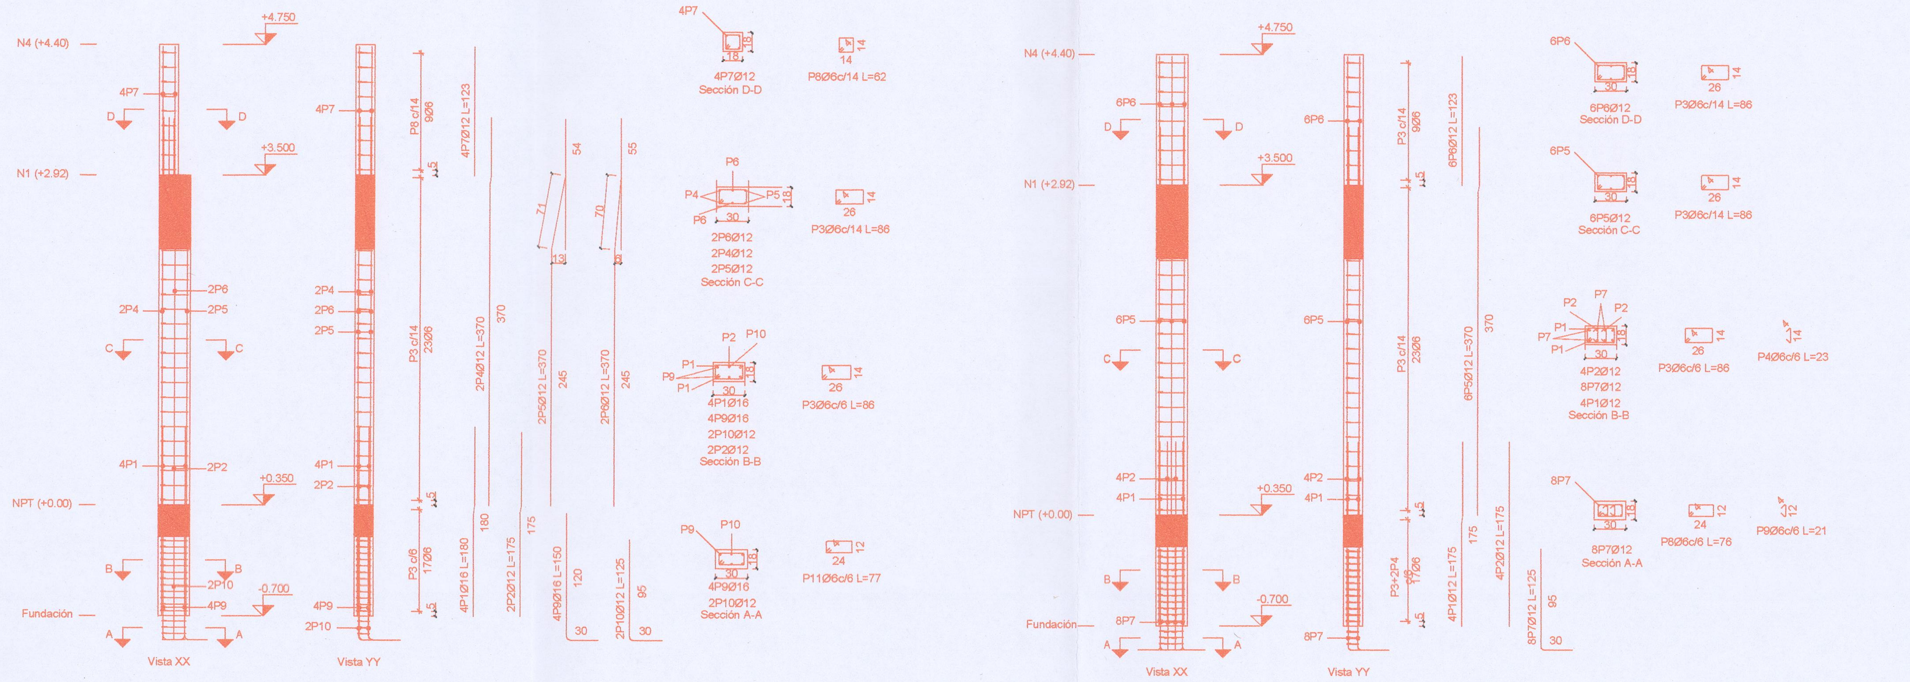

DETALLE DE PORTICOS
ESC. 1.100

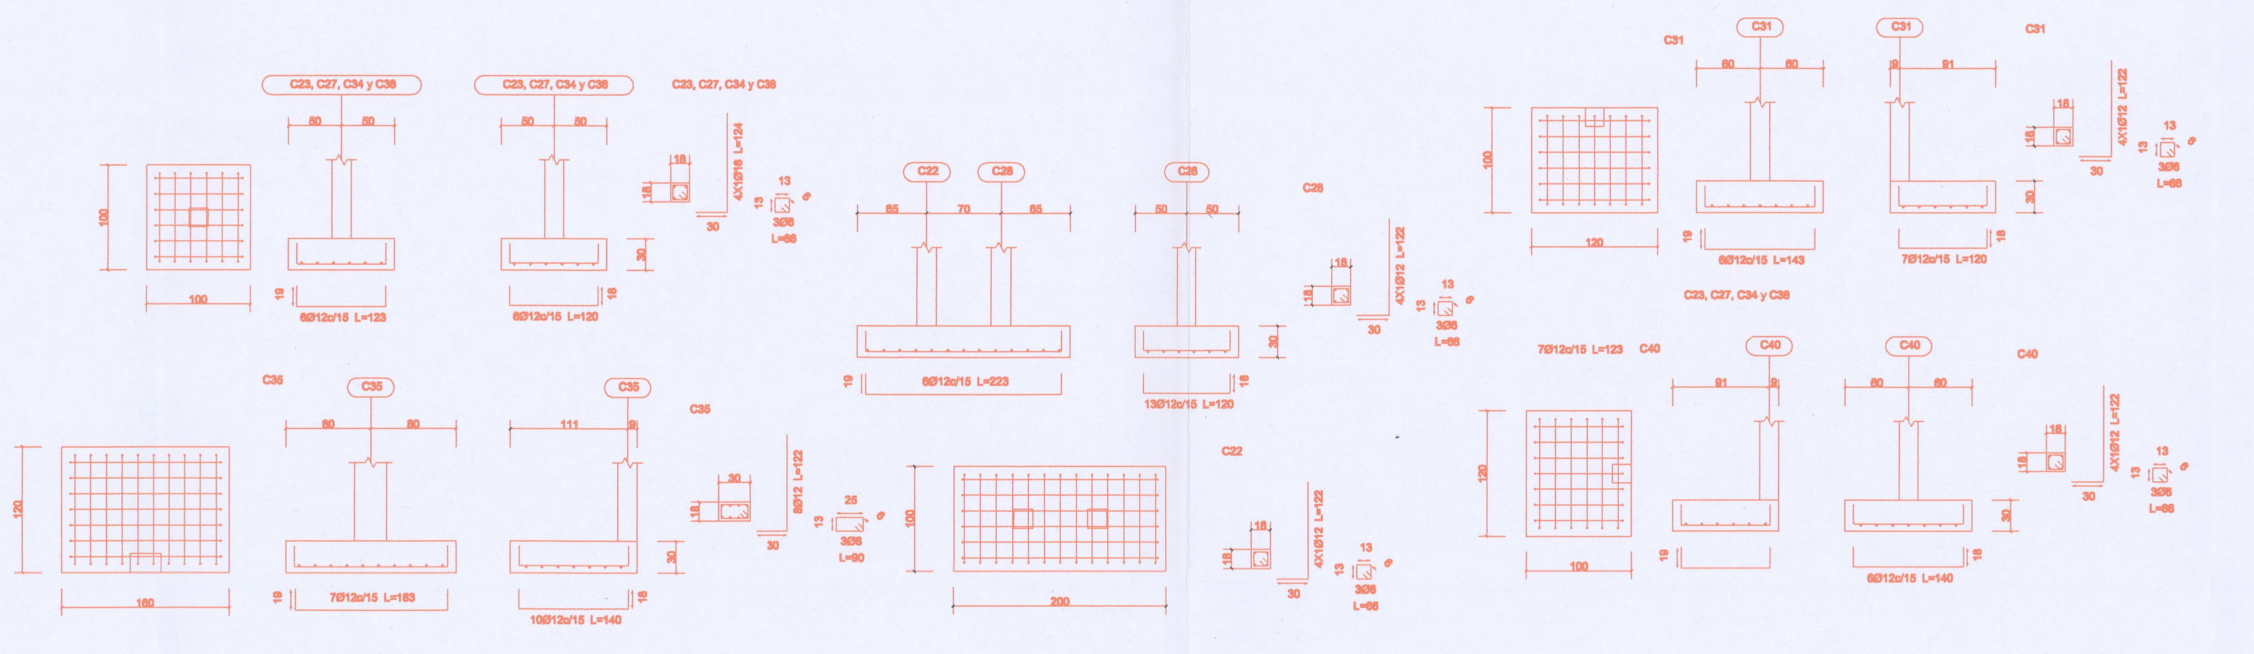

DETALLE DE FUNDACIONES
ESC. 1.100

DPTO.: 02	ZONA:09	MZA.:38	PARCELA:63 - 163
PADRÓN INMOB:0101156218		DOMINIO:7S 39.393	ICM: 339-R-25

LEY 4683

25080684

DEST. DE LA OBRA: Vivienda

PROPIETARIO: Rosalia Andrea Rampulla D.N.I. 36.045.099

UBICACIÓN: Vinara N° 55 lote 6 mza "J" contraf. Ayohuma N°54 lote 18 mza "J"

BARRIO: Juramento

CIUDAD: Santiago del Estero, Capital

ESCALA: 1:100 1:200

140126

SUSANA ABECASSIS
Arquitecta
Secretaría Técnica
Colegio de Arquitectos SDE

SUP. DEL TERRENO: 756.02 m2
SUP. CUBIERTA Y SEMICUBIERTA TOTAL: 358 m2

PROPIETARIO:
Rosalia Andrea Rampulla
DOMICILIO: Av. Belgrano (s) 3246 B° Cabildo.

CROQUIS DE UBICACION

PROYECTO: ANA TAVELLA ARQUITECTA M.P. 656

D. TÉCNICA: ANA TAVELLA ARQUITECTA M.P. 656

ELECTRICIDAD:

CATEGORIA COLEGIO DE ARQUITECTOS

	VINARA	AYOHUMA
ANCHO DE CALLE:	11.66m	14.50m
ANCHO DE VEREDA:	2.84m	3.15m
ANCHO DE CALZADA:	5.84m	7.95m

PAVIMENTO: SI
SERVICIOS CLOACALES: SI

DESIGNACIÓN:

ESTRUCTURAS 2

OBSERVACIONES: 06 FEB 2026

Las referencias al Título de dominio son meramente indicativas, y la aprobación administrativa no valora los derechos que de ellos emergen

PERMISO DE COMIENZO DE OBRA N° 221/2026
DIRECCION DE SUELO URBANO

MUNICIPALIDAD DE LA CIUDAD DE SANTIAGO DEL ESTERO
SECRETARIA DE ECONOMIA
APROBADO
DIRECCIÓN DE SUELO URBANO
EXPEDIENTE: 696-31-25/15-R-2025
FECHA: 11 MAR 2026

DIRECCION DE SUELO URBANO
EXPEDIENTE 696 31 25
FECHA DE SELLADO 12 12 25
BOLETA 2217

DIRECCION DE SUELO URBANO
EXPEDIENTE 696 31/25
FECHA DE SELLADO 06 MAR. 2026
2821

Ing. Agrim. J. LEANDRO ARJONA
JEFE DE AREA DE VISACIONES TECNICAS
DIRECCION DE CATASTRO MUNICIPAL

ARQ. LOPEZ FEDERICO
SUBDIRECTOR
DIRECCIÓN DE SUELO URBANO
MUNICIPALIDAD DE LA CAPITAL

Arq. Cesar Marcelo Alcorta
Director D.S.U.
Municipalidad de la Capital