



DETALLE DE COLECTOR DE TANQUE DE RESERVA

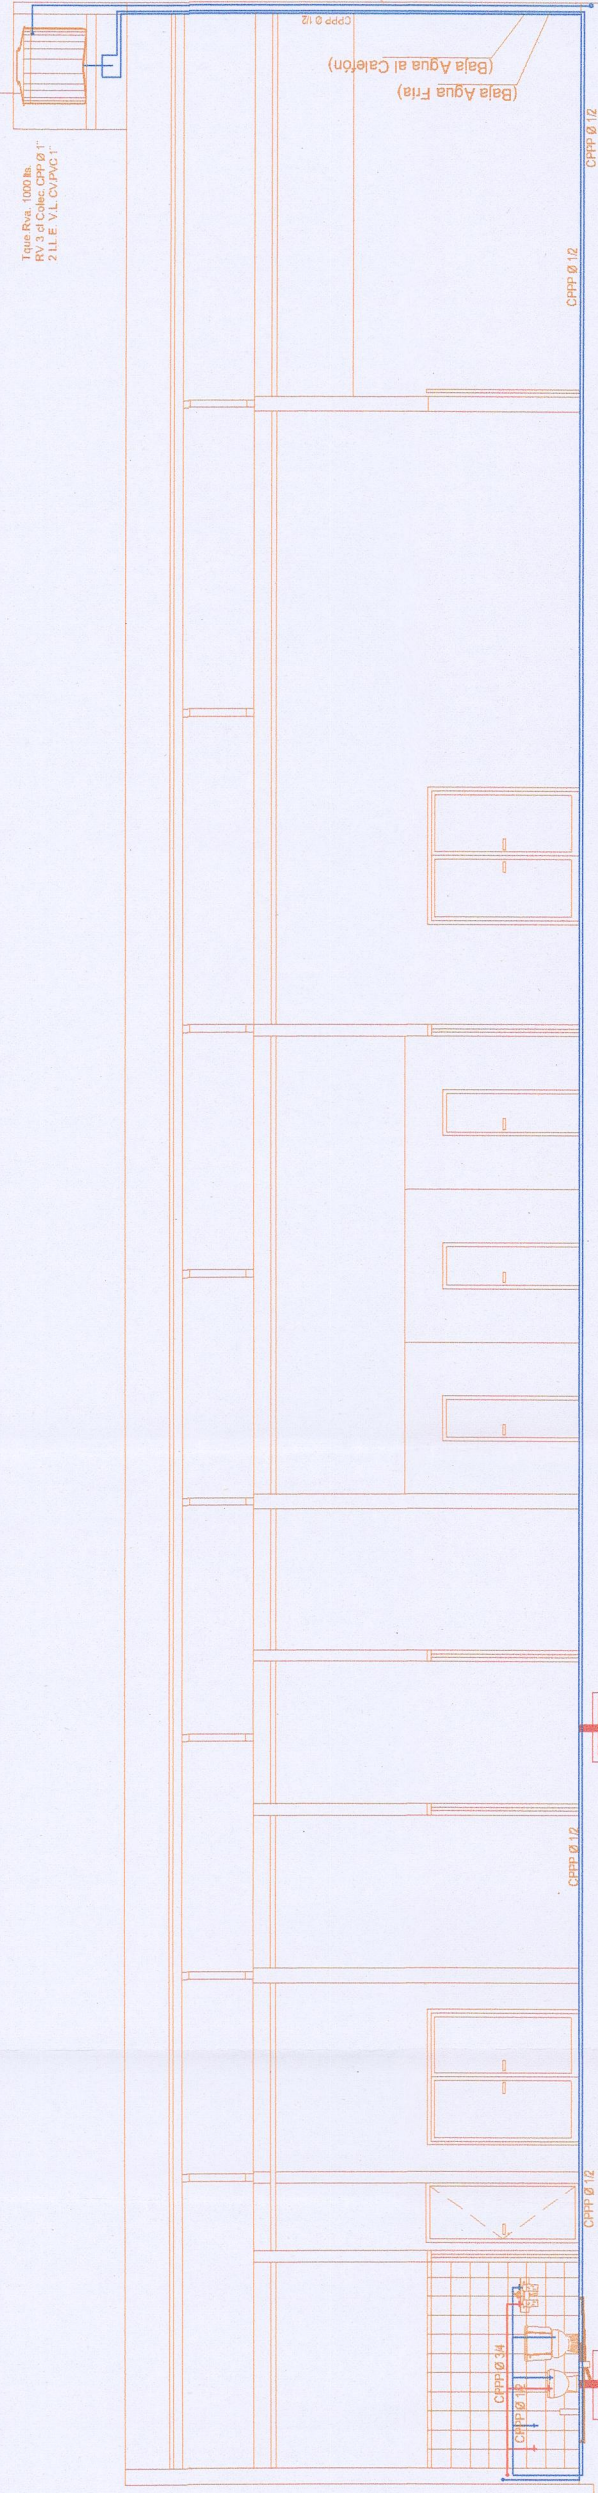

CORTE B-B

GUMERSINDO GOROSITO.

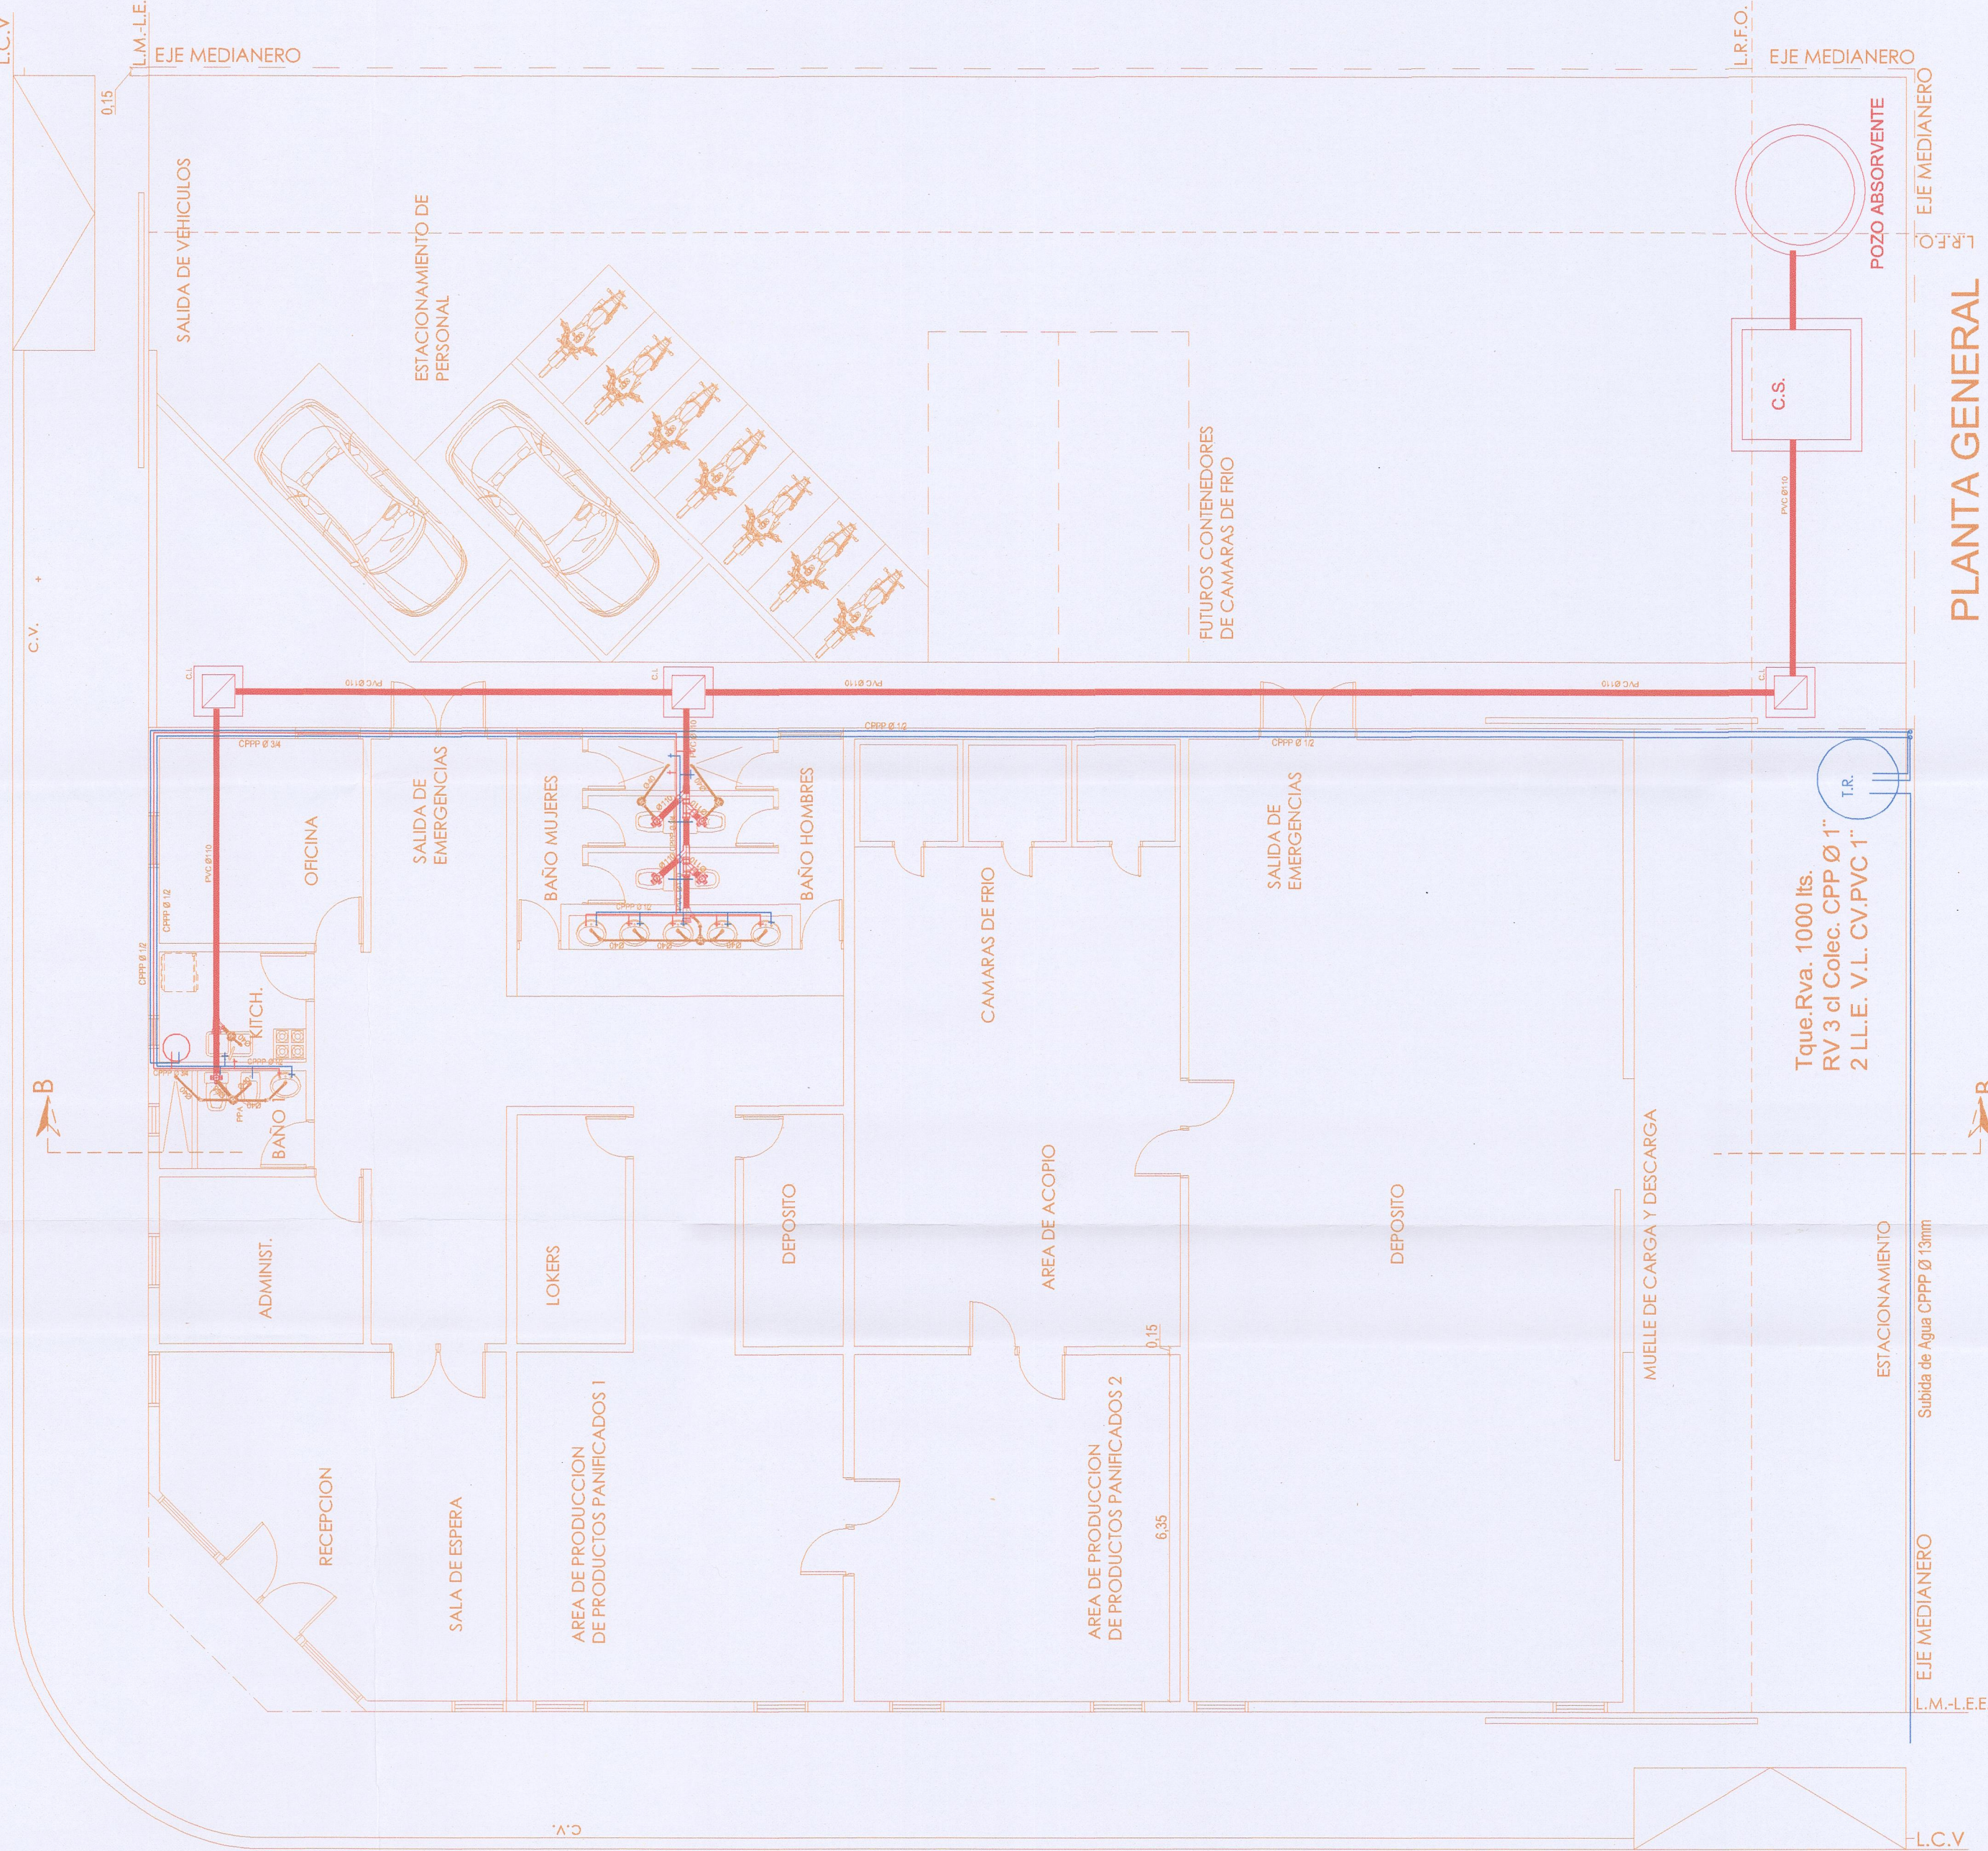


PLANTA GENERAL

DESIGNACION	Canerías de Desague.				VENTILACIÓN			
	PRIMARIAS	PLUVIALES	Nº	MAT. Ø	Nº	MAT. Ø	Nº	MAT. Ø
Tramo	1	P.V.C. 110	1	a 4 CPVC 100	—	—	—	—
	2	P.V.C. 63	1	a 4 CPVC 100	—	—	—	—
Horiz. Col.	—	—	—	—	—	—	1 1/2 P.V.C. 60	60
Columna	—	—	—	—	—	—	1 1/2 P.V.C. 60	60
P.P.A.	1-2	P.V.C. 63	ARTEFACTOS Y ACCESORIOS					
I.P.	1	P.V.C. 110	B.P.pal	I.P.DAI - L 2 C.S. - 40 Ba. Da. - 21UP				
B.ACC.	1	P.V.C. 63	B.T.	I.P.DAI - L 2 C.S. - 2 LLP				
C.ACC.	—	—	P.C.	2 C.S. SIF P.V.C. Ø 50				

DPTO.: 04 ZONA:05 MANZ.: 52 PARC.: 10/11
PADRON INMOBILIARIO: 01-01-120946 I.C.M.: 487-S-25 DOMINIO:7S-38848
DESTINO: PANIFICADORA
PROPIETARIO: SAVIGA S.R.L.
CUIT N° 30-71758128-4

UBICACION: Avenida del Trabajo S/N esq Calle Gumersindo Gorosito
BARRIO: MARIANO MORENO
DPTO.: CAPITAL
PROVINCIA: SANTIAGO DEL ESTERO
ESCALA: 1:100

SUP. TERRENO SIHE-SIT: 975.00 m2
SUP. CUBIERTA: 577.00 m2
SUP. CUBIERTA F.M.L.: 0 m2

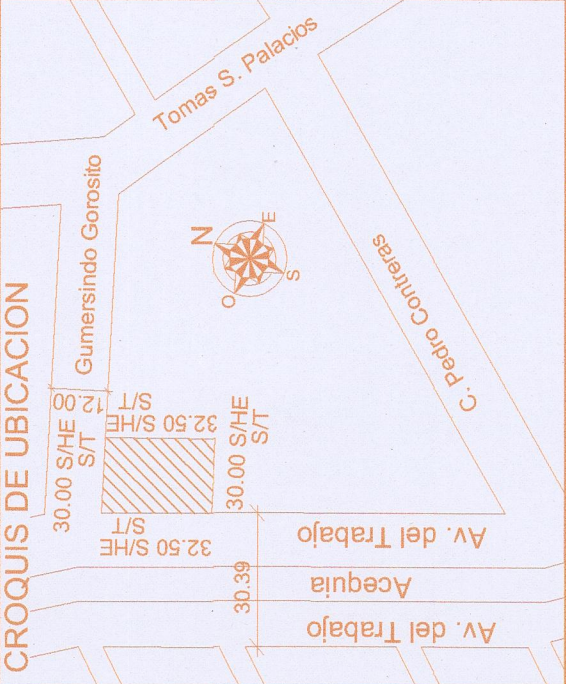

ANCHO DE CALLE	30.39 m	SI/G. Gorosito	12.00 m
ANCHO DE CALZADA	6.04 m	del trabajo	4.54 m
ANCHO DE VEREDA	3.04 m	Gorosito	3.78 m

Designacion:

PLANO DE INSTALACION SANITARIA

OBSERVACIONES: 11 FEB. 2026
Las referencias al Título de dominio son meramente indicativas, y la aprobación administrativa no valora los derechos que de ellos emergen.

APROBADO
DIRECCION DE SUELO URBANO
EXPERIENTE: 988-31-25/04-5-26
FECHA: 11-9 MAR 2026

Ing. Agrim. J. LEONORO ARJONA
DIRECTOR DE CATASTRO MUNICIPAL

Arq. Cesar Marcelo Alcorza
Director S.S.S.
Municipalidad de la Capital