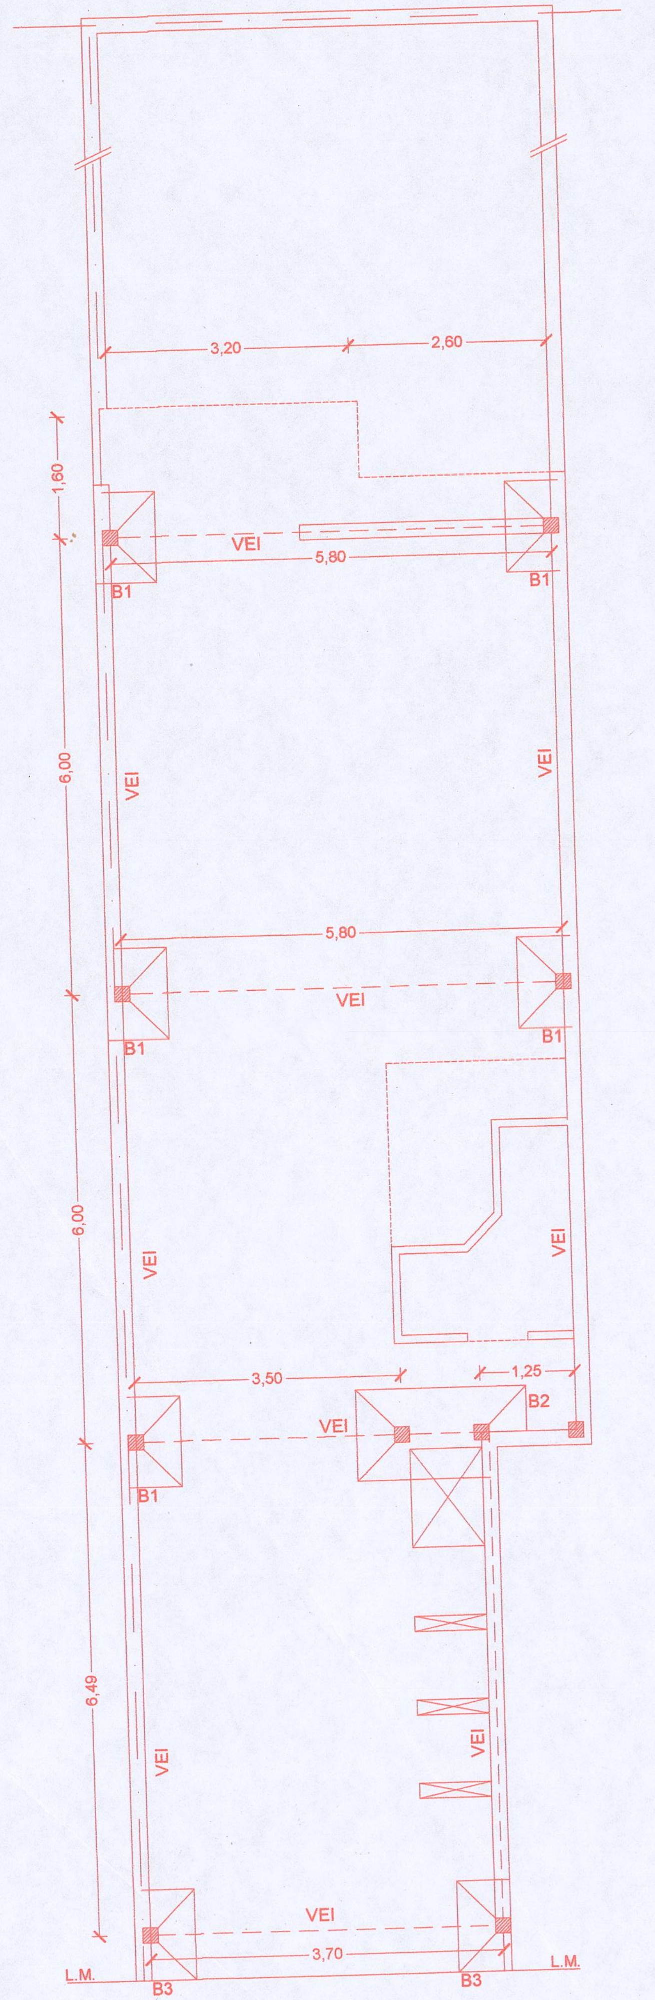

PLANTA FUNDACIONES

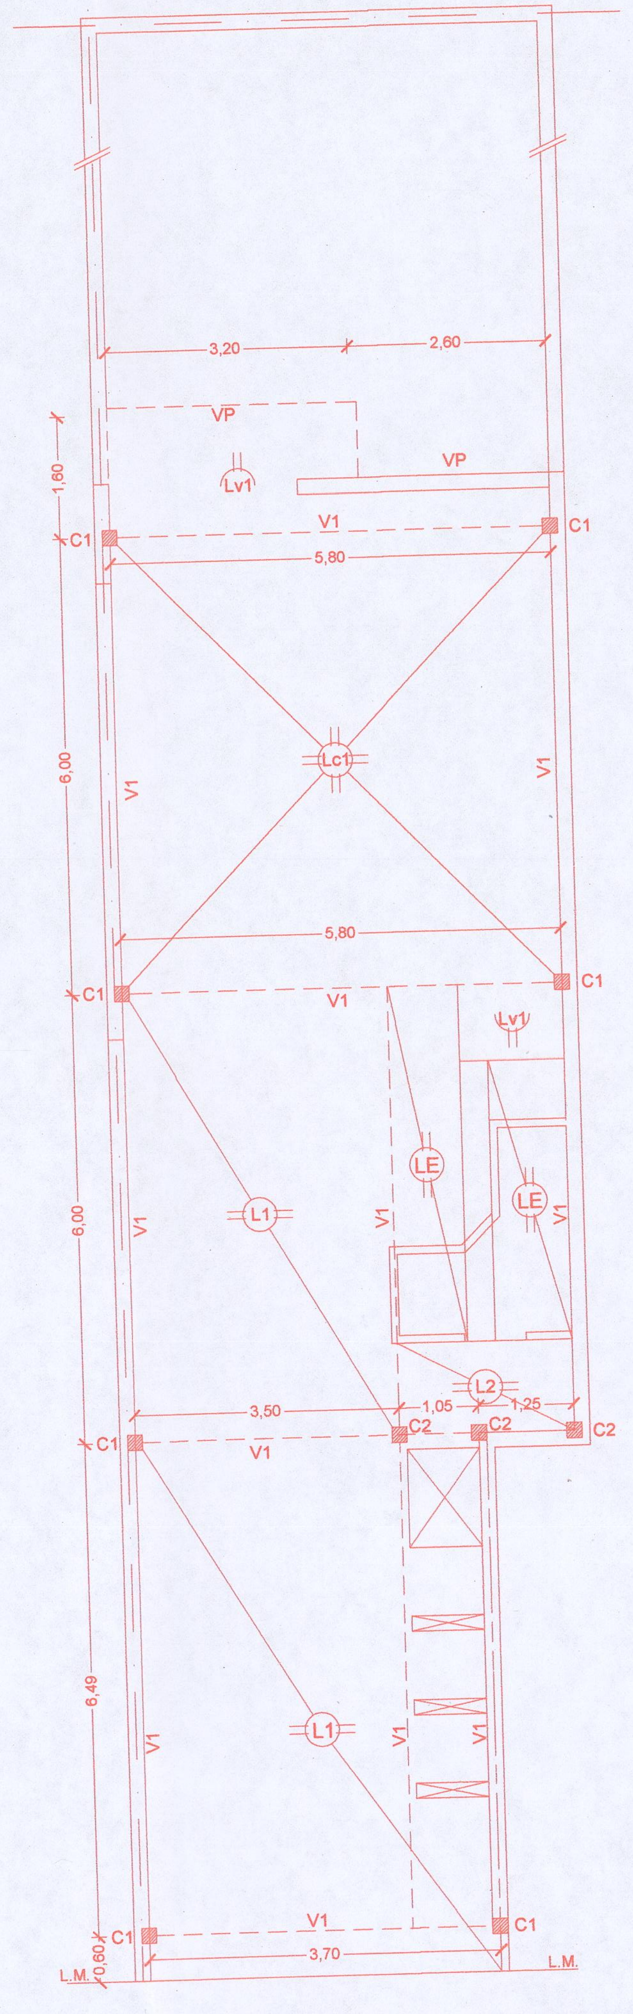

PLANTA BAJA
NIVEL +3,70

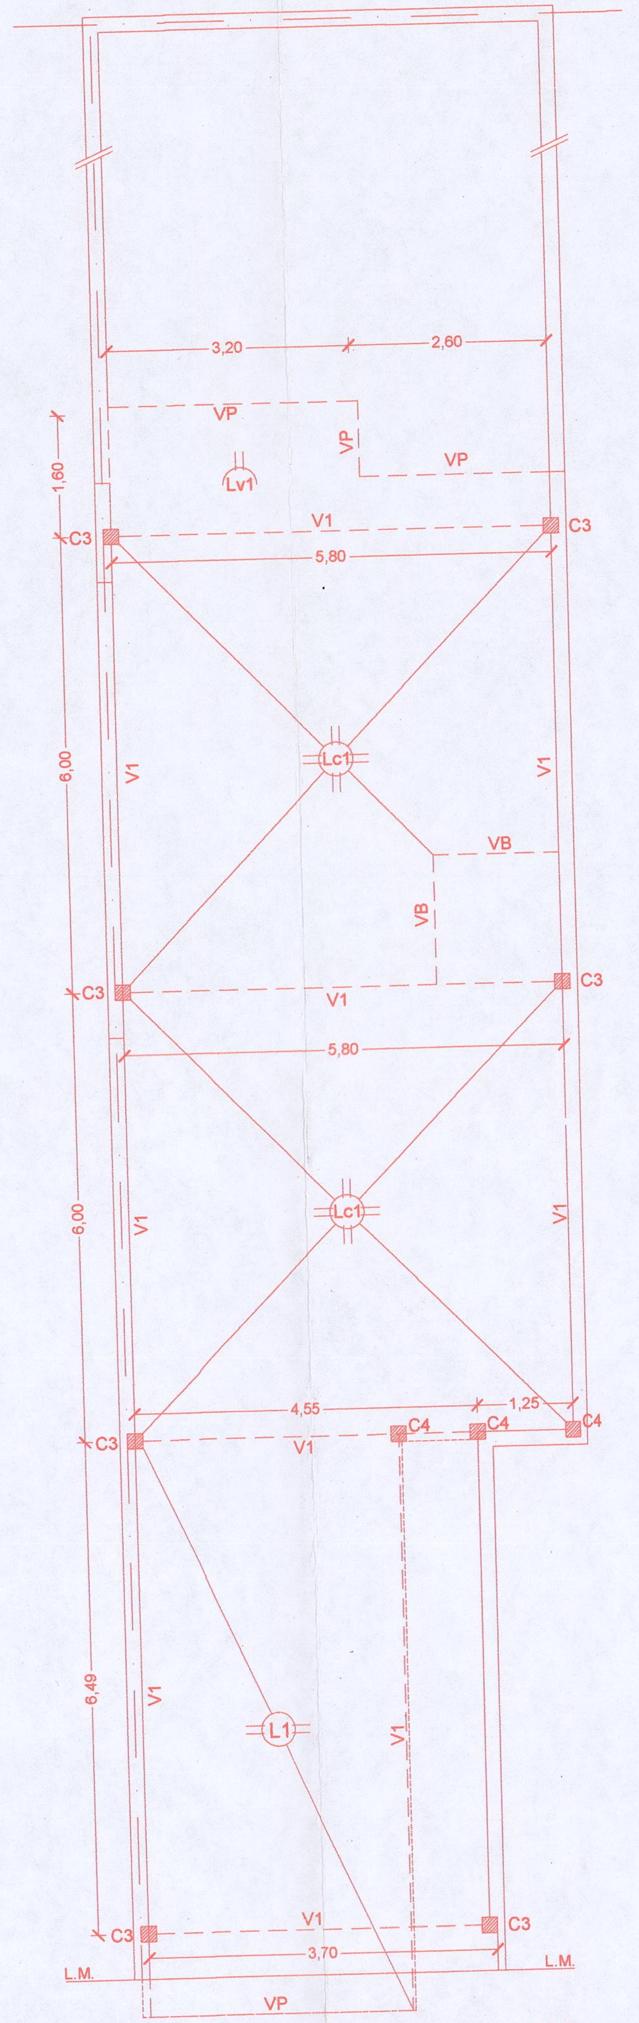

PLANTA ALTA
NIVEL +6,50

PLANILLA DE BASES

EXCENTRICAS

Hormigon - H17
Acero Tipo III - 4200 Kg/cm2

Nivel	design.	N	S	DIMENSIONES m					M	Armaduras Ax			Armaduras Ay			observaciones
		Tn/m	m2	ax	ay	d	D	h	(Tm)	cm2	Ø	Sep	cm2	Ø	Sep.	
PB	B2	1,50	1,50	1,50	1,00	0,15	0,20	0,70	1,32	4,2	10	12	3,7	10	15	
	B3	1,75	3,25	2,50	1,50	0,15	0,20	0,70	2,10	5,65	10	10	5,65	10	10	DOBLES
	VF						0,20	0,20			10			10		2 Ø POR ARRIBA 2Ø POR ABAJO ESTRIBOS Ø6 c/0,25 m.

PLANILLA DE LOSAS

UBICACION	POSICION	Luz Y/X m	q kg/m²	M tm	h_y h_x cm	D	Fe sec cm²/m	Ø mm	SEP	Fe sec cm²/m	Ø mm	SEP	REPARTICION Ø	REPARTICION SEP	OBSERVACIONES
P.B. - P.A.	Lc1	6,00	0,70	2,10	10	12,0	4,28	10	12	-	-	-	-	-	Adicionar sobre apoyo Ø12 cada 24cm.
		6,00	0,70	2,10	10	12,0	4,28	10	12	-	-	-	-	-	
	L1	3,70	0,70	0,96	10	12,0	3,25	10	15	-	-	-	6	20	
	L2	2,50	0,70	0,55	10	12,0	2,60	10	20	-	-	-	6	20	
	LV	1,50	0,70	0,79	10	12,0	-	-	-	3,12	10	20	6	20	
	LE	4,50	0,70	1,42	12	14,0	5,20	12	12	-	-	-	6	20	

PLANILLA DE VIGAS

tramos

σ_{bk}= Hormigon H17
σ_{ek}= 4200Kgs./cm2 Tipo III

nivel	design.	luz (m)	forma	p tn	q t/m	reacc tn Ra	reacc tn Rb	M (+) tm	dimensiones cm b	do	h	armadura - tramo Fet cm2	Ø	nº	Fet' cm2	nº	Ø	hierro a doblar y/o adicional A nº	Ø	B nº	Ø	tension de corte kg/cm2 σA	σB	estrib.cerr. Ø	sep cm	observaciones
PB-PA	V 1	5,80	▨	--	2,48	7,24	7,24	3,56	20	42	45	4,8	16 12	3 2	-	-	-	2	16	2	16	11.8	11.2	6	10/20	CONTINUA
	V P								15	42	45		12	4		2	10					-	-	6	15	
	V B								20	42	45		12	3		2	10							6	15	

PLANILLA DE COLUMNAS

POSIC.	FORMA	hp p	P t	Fb d1	Fb d2	Fb cm2	Fe cant	Fe Ø	Fe cm2	ESTRIBOS Ø	ESTRIBOS Sep.	W	Wpo Kg/m2	OBSERVACIONES
														Hormigon H17 Acero Tipo III=4200 Kg/m2
C1	▨	4,00	11,00	25	20	500	4	12	3,73	6	12	1,02	170	
C2	▨	4,00	4,50	20	20	400	4	12	2,56	6	15	1,02	170	
C3	▨	3,00	6,20	25	20	500	4	12	3,73	6	12	1,02	170	
C4	▨	3,00	2,25	20	20	400	4	12	3,73	6	15	1,02	170	

DETALLE DE CIMIENTOS PARA MUROS DE 0.20

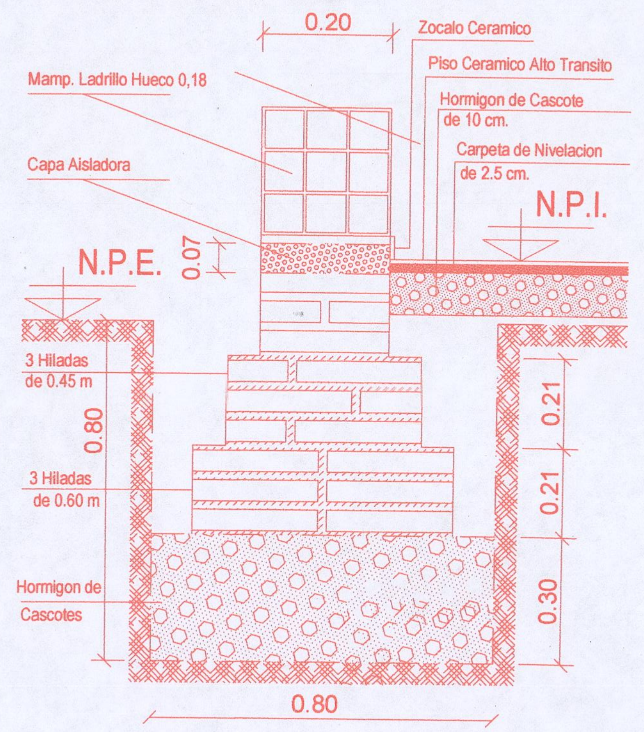

PADRON INMOBILIARIO : 1-1-2917 DOMINIO : M.F.R. 7N-6307

DESTINO DE LA OBRA : VIVIENDA UNIFAMILIAR

PROPIETARIO : SUCESIÓN DE JULIO RICARDO DIAZ
AMANDA ARGENTINA ORTÍZ GOMEZ
L.E. : 5.960.320 CUIL : 27-5960320-0

UBICACIÓN : PERÚ N° 1025
BARRIO : DR. JUAN BAUTISTA ALBERDI
CIUDAD : CAPITAL - SANTIAGO DEL ESTERO
ESCALA : 1 : 100 - 1 : 200

SECRETARIA DE PLANEAMIENTO Y OBRAS PUBLICAS
Municipalidad de la Capital
SGO. DEL ESTERO
DIREC. DE SUELO URBANO

COLEGIO DE ARQUITECTOS
LEY 5654/87
SGO. DEL ESTERO

RELEVAMIENTO Y AMPLIACION
13 AGO. 2018
Arq. Eva Luz Khairallah
SECRETARIA TECNICA
COLEGIO DE ARQUITECTOS S.D.E.

SUPERFICIE DE TERRENO :	420,00 m2 S/T - S/H.e.
SUP. CUB. EXIST. :	111,39 m2
SUP. CUBIERTA AMPL. P.B.	102,42 m2
SUP. CUBIERTA AMPL. P.A.	105,95 m2
SUP. CUB. FUERA LM	0 m2
SUP. CUBIERTA TOTAL :	319,76 m2

PROPIETARIO :
DOMICILIO : Amanda Ortiz Gomez
Nilda Diaz Lidia Diaz

RELEVAMIENTO :
DOMICILIO :
HUGO V. CAROL
ARQUITECTO - Mat. Nº 0033

PROYECTO :
DOMICILIO :
HUGO V. CAROL
ARQUITECTO - Mat. Nº 0033

DIRECCIÓN DE OBRA :
DOMICILIO :

DIRECCIÓN DE SUELO URBANO
EXPEDIENTE: 17-5-2018
FECHA DE SELLADO: 19/8/18
BOLETA 56875

CATEGORIA COLEGIO DE ARQUITECTOS: "B"

CROQUIS DE UBICACION

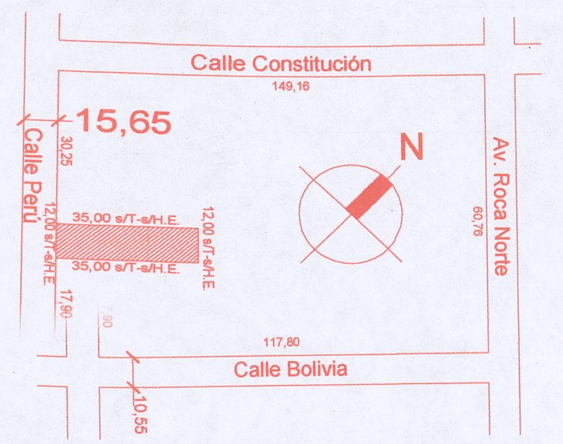

ANCHO DE CALLE : 15,65 m
ANCHO DE VEREDA : 3,85 m
ANCHO DE CALZADA : 8,00 m

PAVIMENTO : SI
SERVICIOS CLOACALES : SI

DESIGNACION :

PLANO DE ESTRUCTURAS

②

OBSERVACIONES :

24 OCT 2018
Las referencias al Título de Dominio son meramente indicativas, y la aprobación administrativa no valora los derechos que de ellos emergen

PERMISO DE COMIENZO
DE OBRA Nº 4402
DIRECCION DE SUELO URBANO

MUNICIPALIDAD DE LA CIUDAD DE SANTIAGO DEL ESTERO
SECRETARIA DE PLANEAMIENTO Y OBRAS PUBLICAS
APROBADO
DIRECCION DE SUELO URBANO
EXPEDIENTE: 17-5-2018
FECHA: 14 DIC 2018

ING. AGRIM MARIO J. LOPEZ
Dpto. CATASTRO
Direccion de Suelo Urbano

Arq. RAUL E. MARTINEZ
SERVICIO DE OBRAS PRIVADAS
DIRECCION DE SUELO URBANO

Arq. BERNARDO L. M. SANTILLAN
DIRECTOR
DIRECCION DE SUELO URBANO
MUNICIPALIDAD DE SGO. DEL ESTERO