

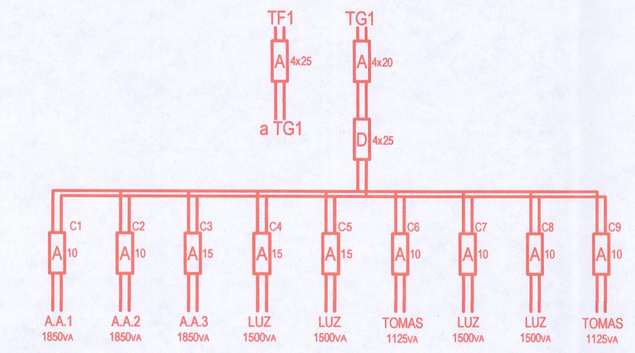


MEDIDOR	CIRCUITO Nº	CIRCUITO TIPO	TABLERO	UBICACION (NIVEL)	BOCAS ILUM.	BOCAS TOMAS	MOTORES CANT.	MOTORES H.P.	TENSION VOLTIOS	INTENS. AMPERE	POTENCIA VOLT AMPERE
M1	C1	ACU-A.A.1	TG1	PB		1			220	4.20	925
	C2	ACU-A.A.2		PB		1			220	4.20	925
	C3	ACU-A.A.3		PB		1			220	4.20	925
	C4	luces-IUG		PB	12				220	0.90	200
	C5	luces-IUG		PB	12				220	0.90	200
	C6	tomas-TUG		PB		14			220	0.90	1500
	C7	luces-IUG		PB	13				220	0.90	200
	C8	luces-IUG		PB	6				220	0.90	200
	C9	tomas-TUG		PB		14			220	0.90	1500
	TOTAL por unidad				43	31			220	18.00	6575


DETALLE DESCARGA A TIERRA

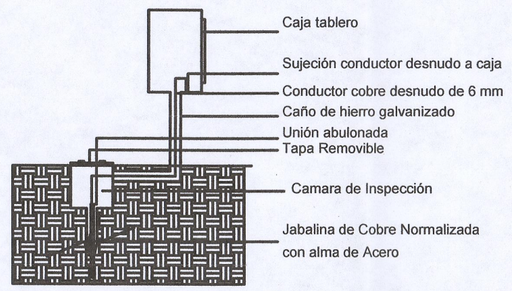


REFERENCIAS ELÉCTRICAS	
	MEDIDOR DE TOMA A TIERRA
	TABLERO PRINCIPAL
	TABLERO SECCIONAL
	BOCA DE UNO Y DOS EFECTOS
	BOCA DE PARED
	TOMA CORRIENTE
	CAJA DE DISTRIBUCIÓN
	LLAVES, UNO,DOS y TRES PUNTOS
	LINEA GENERAL
	CIRCUITO DE AIRE ACONDICIONADO
	CAÑO DE SUBIDA Y ENTRADA DE ENERGIA
	LLAVE DE COMBINACION
	PORTERO ELÉCTRICO
	TELEVISIÓN POR CABLE
	TELÉFONO

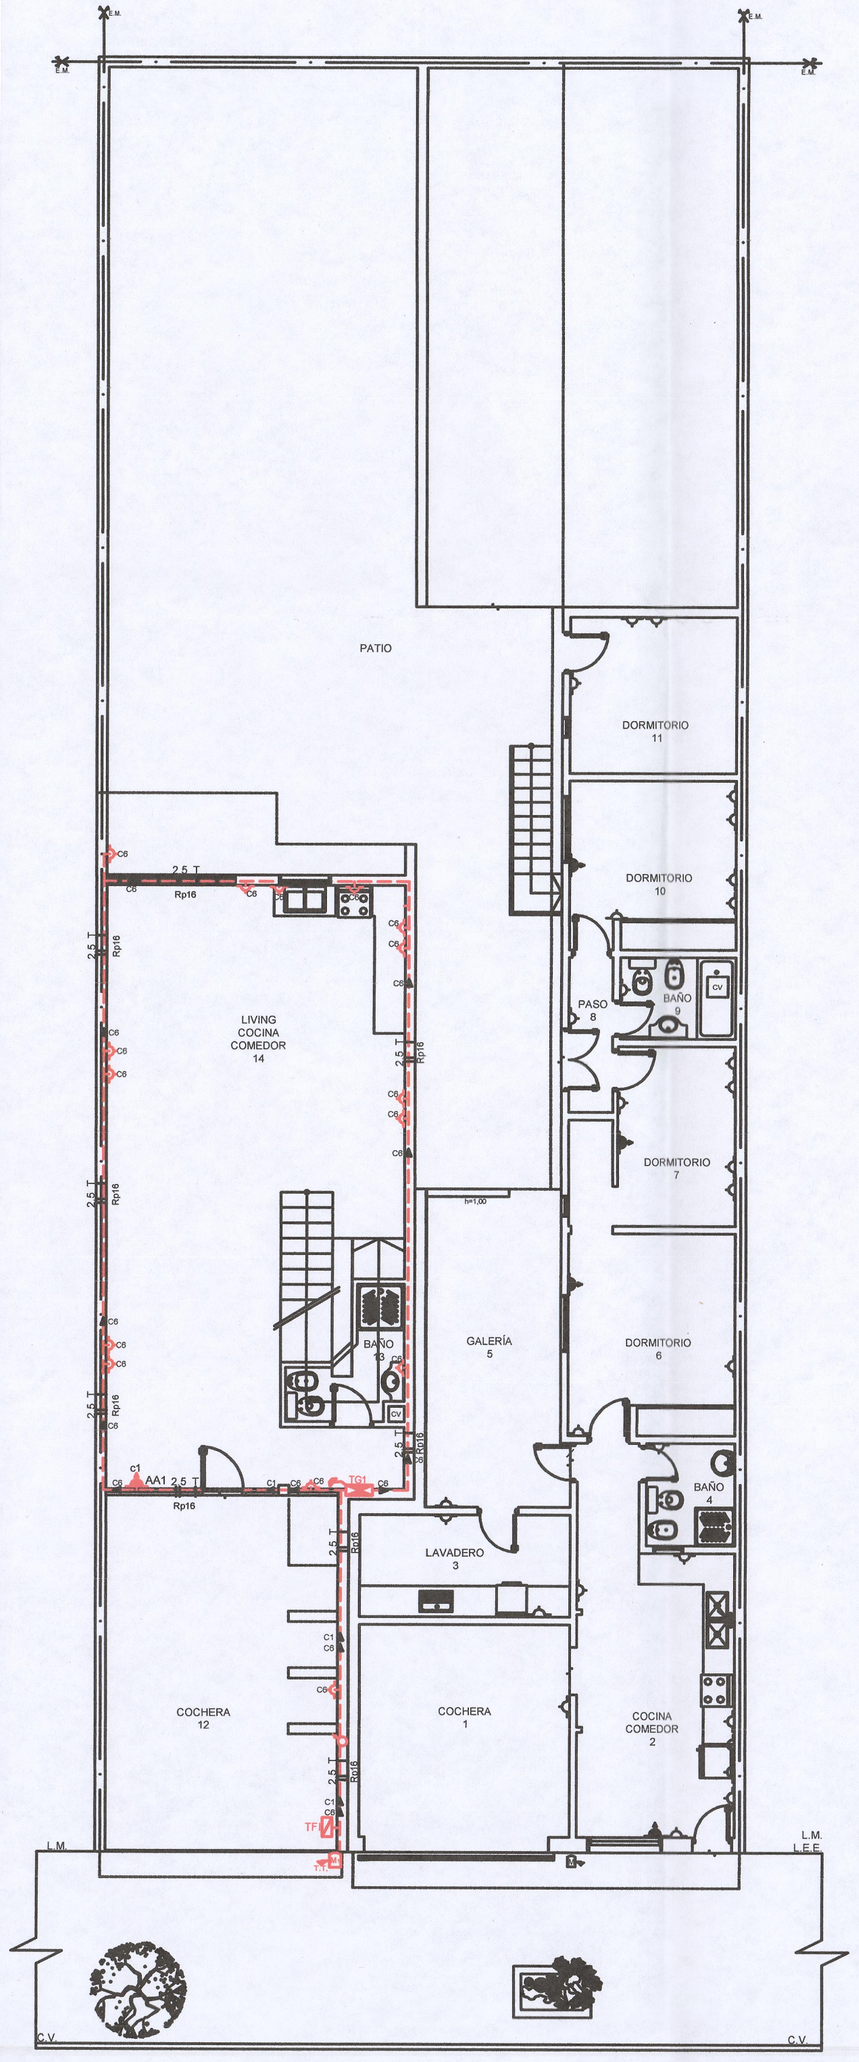


PLANTA BAJA

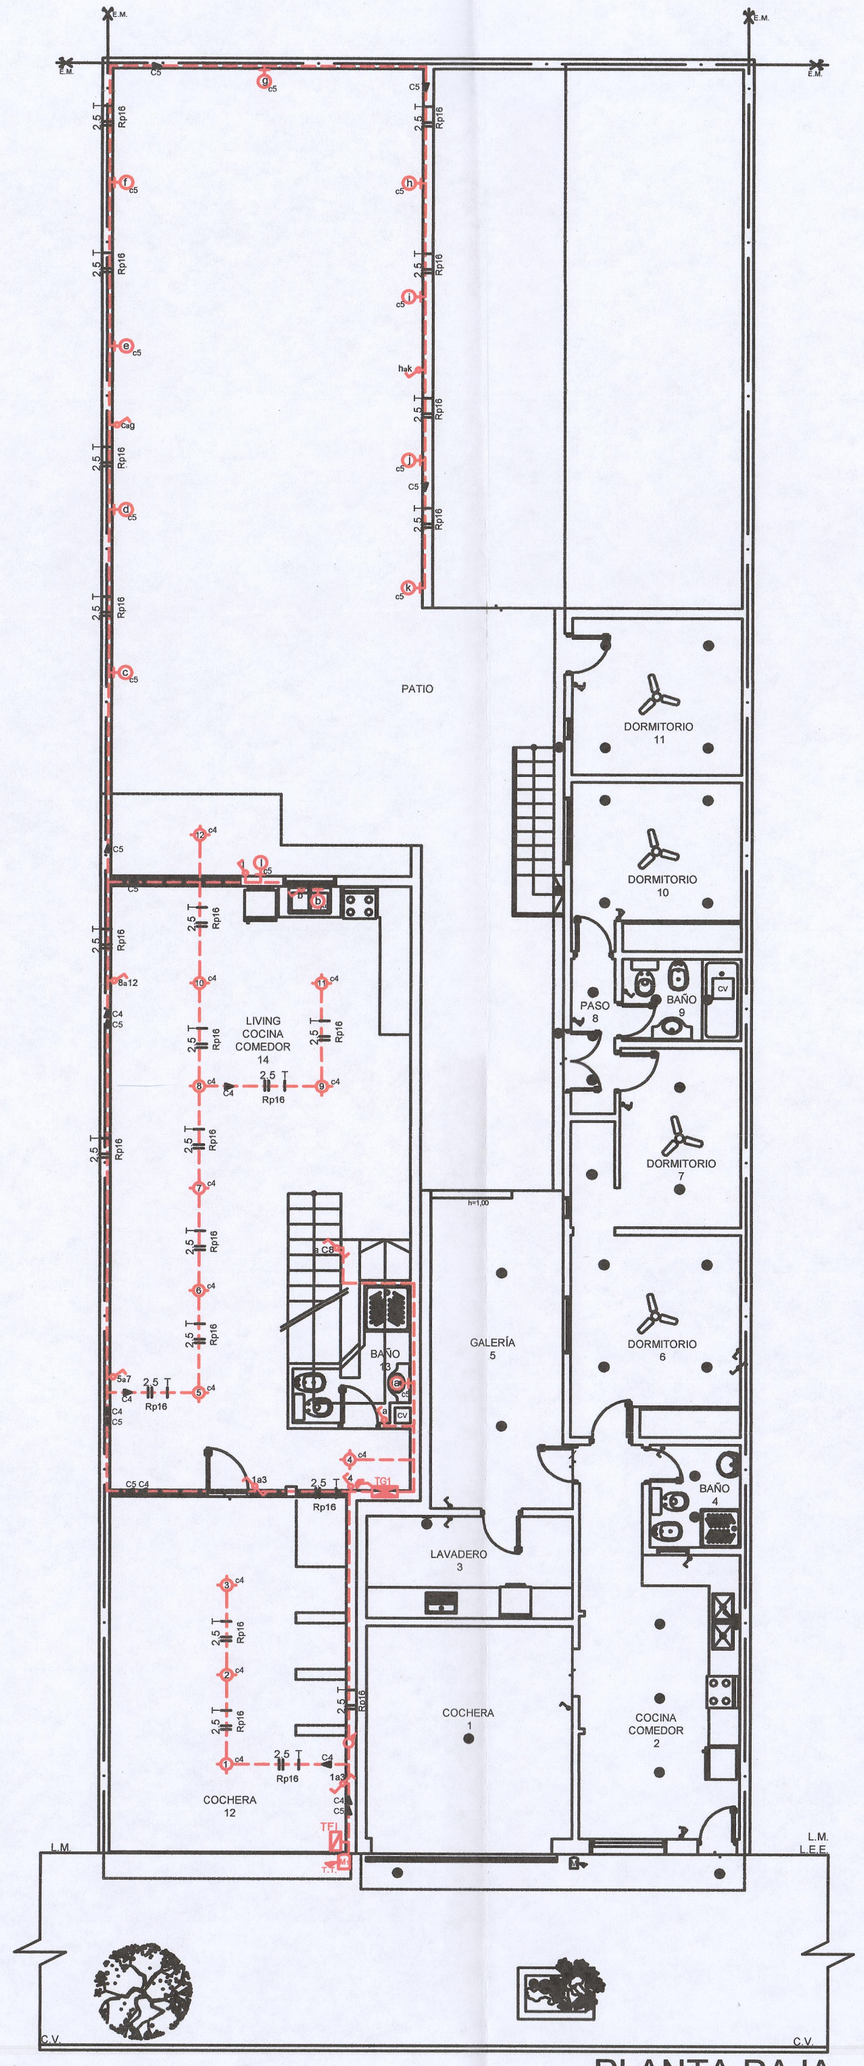

PLANTA BAJA

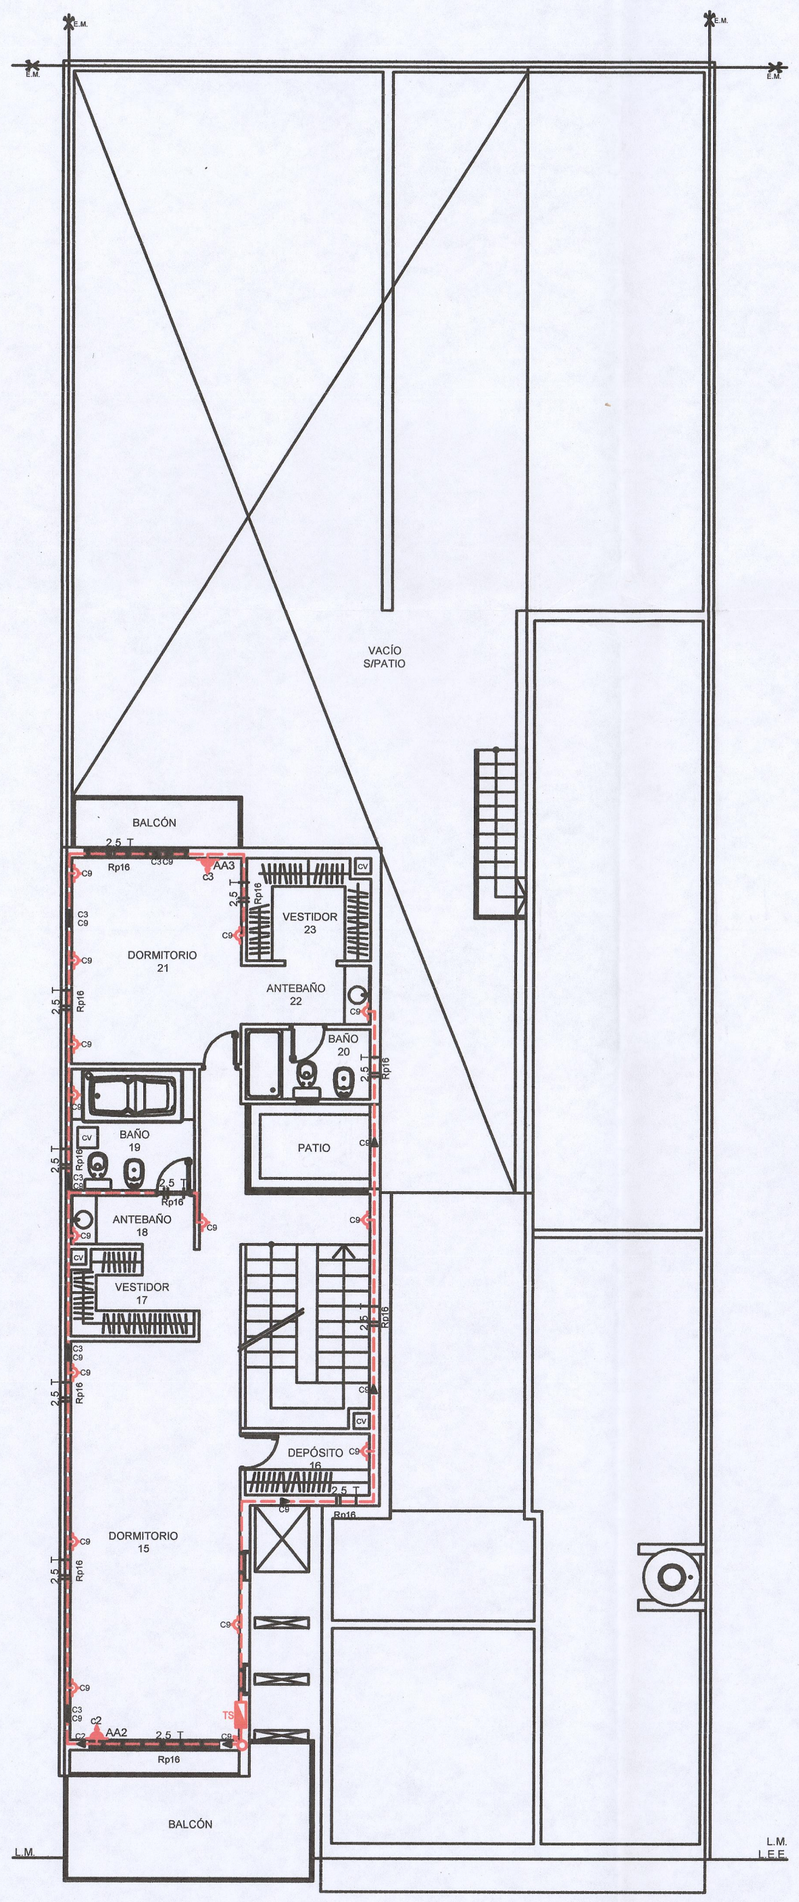

PLANTA ALTA
Tomas y A.A.

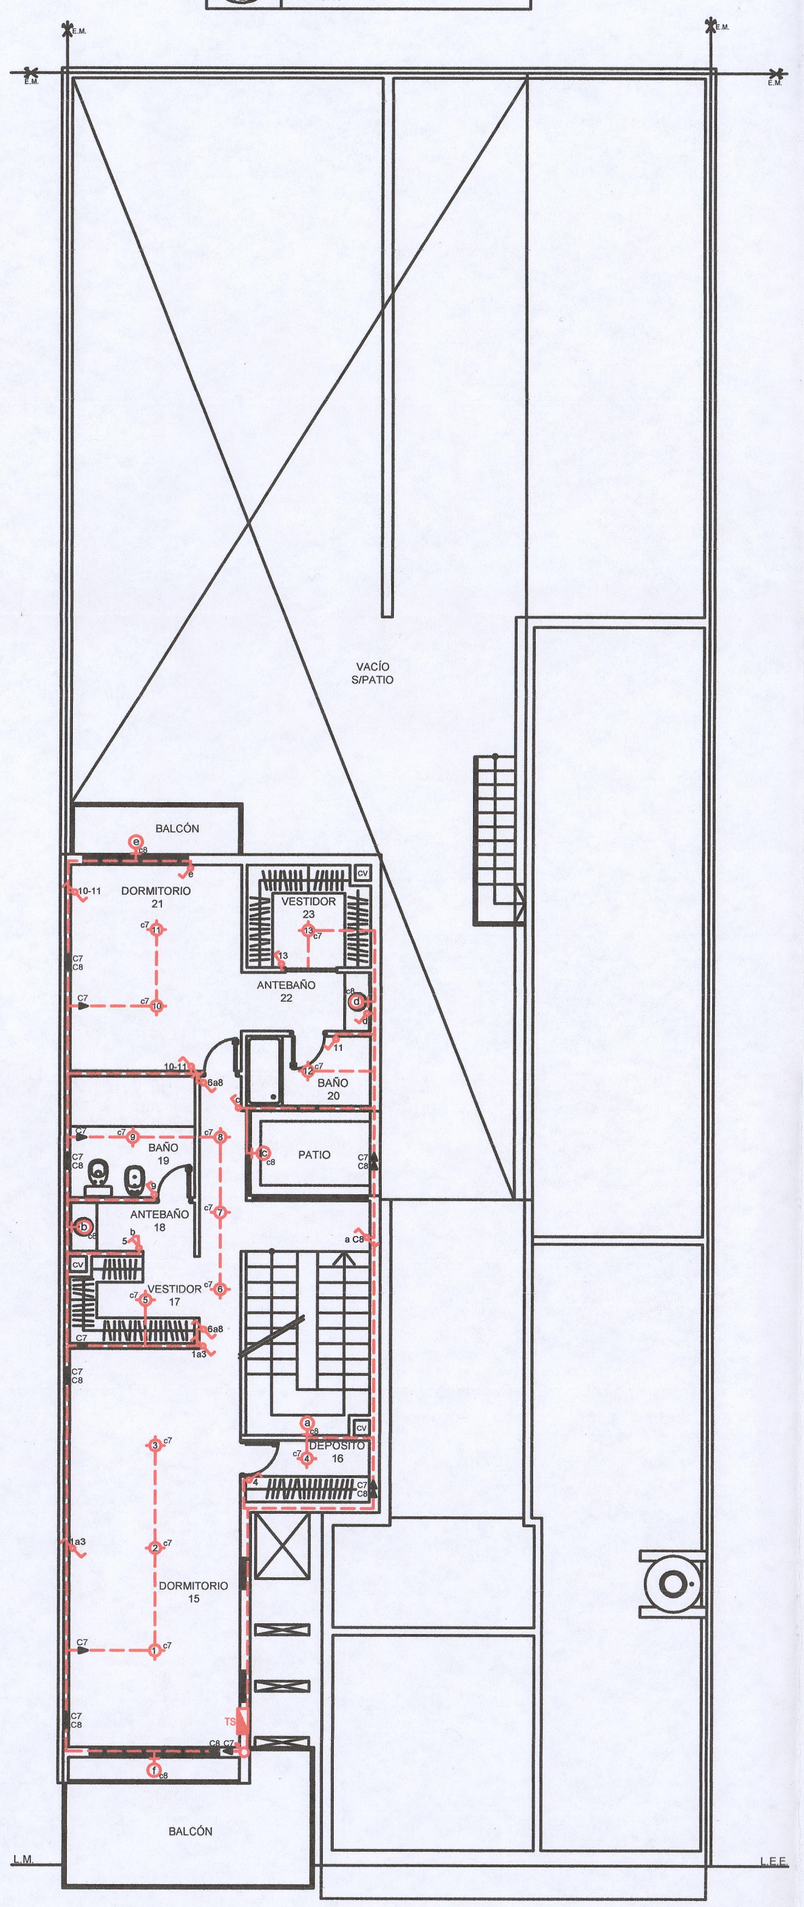

PLANTA ALTA
Centros

SINTESIS DEL PROYECTO

-DESTINO: Vivienda.
-D.P.M.S.: 11.040 VA
-Grado de Electrificación: BAJO
-Cantidad de Circuitos: 9
-Destino de los Circuitos:
4 IUG - 2 TUG - 3 ACU AA - 1 MTBF

-Seccion de los Conductores:
LP: 1(4x1x4 mm2) - Cu - IRAM 2178
CS TSG: 1(4x1x4 mm2) - Cu - IRAM 2178
Circuito IUG - MBTF: 1.5mm² - Cu - IRAM 247-3
Circuito IUE - TUG - ACU: 2.5mm² - Cu - IRAM 247-3

Corriente de Proyecto: 6.58 Kw
Tension: 220 V

Cantidad de Bocas
Iluminación: IUG 43
Tomas: TUG 31 - ACU AA 3
MBTF: 1

NOTA 1:
Todos los circuitos irán alojados en cañerías independientes, el único trazo en el dibujo representa la canalización de cada circuito.

Destino: Vivienda
Sup.: 322.01 m2
Grado de Electrificación: Bajo

NOTA: TODA LA CAÑERIA ESTARA RECORRIDA POR UN CONDUCTOR RECUBIERTO DE SECCION 2.5mm de COLOR VERDE AMARILLO PARA PUESTA A TIERRA DE LA INSTALACION ELECTRICA
RS: SIGNIFICA CAÑO METALICO DE ACERO SEMIPESADO

DIST. : 3 ZONA : 3 MANZ. : 5 PARC. : 160
PADRÓN INMOBILIARIO : 1-1-2917 DOMINIO : M.F.R. 7N-6307 I.C.M. : 982-O-2016

LEY 5854
RESELLADA
Legajo 181041


DESTINO DE LA OBRA : VIVIENDA UNIFAMILIAR

PROPIETARIO : SUCESIÓN DE JULIO RICARDO DIAZ
AMANDA ARGENTINA ORTÍZ SOMEZ
L.E. : 5.960.320 CUIL : 27-5960320-0

UBICACIÓN : PERÚ N° 1025
BARRIO : DR. JUAN BAUTISTA ALBERDI
CIUDAD : CAPITAL - SANTIAGO DEL ESTERO
ESCALA : 1 : 100 - 1 : 200

SUPERFICIE DE TERRENO :	420,00 m2 S/T - S/H.e.
SUP. CUB. EXIST. :	111,39 m2
SUP. CUBIERTA AMPL. P.B.	102,42 m2
SUP. CUBIERTA AMPL. P.A.	105,95 m2
SUP. CUB. FUERA LM	0 m2
SUP. CUBIERTA TOTAL :	319,76 m2

CROQUIS DE UBICACION

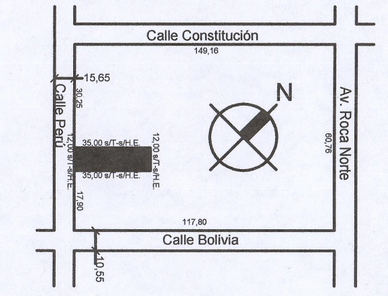

PROPIETARIO : Amanda Ortiz Somez
DOMICILIO : Julio Diaz Nilda Diaz

RELEVAMIENTO :
DOMICILIO : HUGO V. CAROL ARQUITECTO - Mat. Nº 0033

PROYECTO :
DOMICILIO : HUGO V. CAROL ARQUITECTO - Mat. Nº 0033

DIRECCIÓN DE OBRA :
DOMICILIO :

CATEGORIA COLEGIO DE ARQUITECTOS: "B"

ANCHO DE CALLE :	15,65 m
ANCHO DE VEREDA :	3,85 m
ANCHO DE CALZADA :	8,00 m
PAVIMENTO :	SI
SERVICIOS CLOACALES :	SI

DESIGNACION :
PLANO DE INSTALACIÓN ELÉCTRICA (3)

OBSERVACIONES:
Las referencias al Título de Dominio son meramente indicativas, y la aprobación administrativa no valora los derechos que de ellos emergen

PERMISO DE OBRA Nº 4402
DIRECCIÓN DE SUELO URBANO

MUNICIPALIDAD DE LA CIUDAD DE SANTIAGO DEL ESTERO
SECRETARIA DE PLANEAMIENTO Y OBRAS PUBLICAS
APROBADO
DIRECCION DE SUELO URBANO
EXPEDIENTE: 17 - S - 2018
FECHA: 14 DIC 2018

Arq. BERNARDO L. M. SANTILLAN
DIRECTOR
DIRECCION DE SUELO URBANO

Arq. RAUL E. MARTINEZ