

FACHADA

PLANTA

CORTE A-A

PLANTA DE ZAPATAS DE FUNDACIÓN

PROYECTO: 1401-01-002

FECHA: 10/10/2014

HOJA: 10/10

ESCALA: 1:50

PROYECTISTA: J. L. GARCÍA

REVISOR: J. L. GARCÍA

DESIG.	DIMENSIONES (m)		ANIL		Malla		Observaciones
	Luz (m)	Alcance (m)	ANIL (mm)	ANIL (mm)	Cubierta (mm)	Alcance (mm)	
1	0,07	0,10	0,20	0,90	6	12	100% variable
2	0,07	0,10	0,20	0,70	6	12	100% variable
3	0,07	0,10	0,20	0,90	4,2	12	100% variable

USO DE FUNDACIÓN: L.F. ESPESOR: 6 C.I.Z. min. Armadura: Malla 6 C.I. 0,30 m.

[illegible]

PLANTILLA DE COLUMNAS								Asero Tipo ADN-420 Homogén H13	
Diseño	h _p m	Homogén		Armadura		Estribos		Observaciones	
		d1 cm	d2 cm	S cm ²	N°	Sec. cm	Sep. cm		
CE1	3,40	20	20	400	4	Ø	Ø	20	

LOSAS MACIZAS										Diseño: 4200 kg/cm ²			Fecha: 130 kg/cm ²		
Posición		Dimension		Tramo				Adicional apoyo				Fa Distr.		Observaciones	
				a		b		a		Ø	Sep.				
Luz	d	cm	h	Ø	cm	Sep.	cm	Fa	Ø	Sep.	cm	cm			
L1	230	50	5	3.94	12	—	—	—	—	—	—	30			
L2	VAR	10	5.5	7.18	10	12	—	—	—	6	20	20			
L3	110	10	5.5	1.89	6	15	—	—	—	—	6.0	25			
L4	300	10	5.5	3.68	6	14	—	—	—	—	—	30			
L5	300	10	5.5	3.68	6	14	—	—	—	—	—	30			

Referencias	
	Medidor y Toma a Tierra
	Tablero General
	Centro y Brazo de Luz
	Llave de 1 y 2 polos
	Llave de combinación
	Tomacorriente
	Toma fuerza motriz
	Campanilla y pulsador
	I.T.M.
	Disyuntor diferencial

Tramos a Δ b



Dimensiones (cm)	
bo	d
30	15
h	10

[illegible]


Acero Tipo ASTM-A20		Normativa: W13					
							
Amadura - Tramo		Estribo cerrado		Observaciones			
As	Ø	Sep.	dist.				
m ²	m ²	m	cm				
2	6	0.56	6	4.2	20	unif.	* Long variable

PLANILLAS DE CARGAS ELÉCTRICAS							Observaciones
Circuit.	Iluminación		Tomacorriente		Protección Termomagn.	I (a)	
	Cant.	P (w)	Cant.	P (w)			Pot. (w)
C1	0	0	0	12	2400	2400	13.63 Bipolar 2x10(A)
C2	13	100	1300		0	1300	7.38 Bipolar 2x10(A)
C3				1	1500	1500	8.52 Bipolar 2x20(A)
C4				1	1500	1500	8.52 Bipolar 2x20(A)
C5				1	1500	1500	8.52 Bipolar 2x20(A)
Protección general							40.38 Diferencial modificado de 2x4(A)

PLANILLA DE ILUMINACION Y VENTILACION									
LOCAL			ASERTURAS			AREA			
DESIGNACION	SUP.m ²	DESIG.	ANCHO	ALTO	ILUM. VENT.	OBSERVACIONES			
ESTAR	20.44	PV1	0.8	1.05	0.84	PUERTA VENTANA			
		PV2	1.30	1.05	0.84				
		PV3	1.30	1.05	0.84				
		PV4	1.10	2.05	2.26	PUERTA VENTANA			
COMEDOR	20.78	PV4	1.10	2.05	2.26				
COCINA	13.47	PV3	0.70	1.05	0.74	PUERTA VENTANA			
		V4	1.15	1.05	1.21	VENTANA			
		V2	1.20	1.05	1.26	VENTANA			
ESCRITORIO	8.90	V2	1.20	1.05	1.26	VENTANA			
BIBLIOTECA	8.93	V2	1.20	1.05	1.26	VENTANA			
DORMITORIO	14.89	V5	0.80	0.50	0.40	VENTILUZ			
		V5	0.80	0.50	0.40	VENTILUZ			
BANO	1	2.73	V5	0.80	0.50	0.40			
BANO	2	4.76	V5	0.80	0.50	0.40			
BAVADERO	5.25	VN1	3.31	2.40	7.94	VANO			

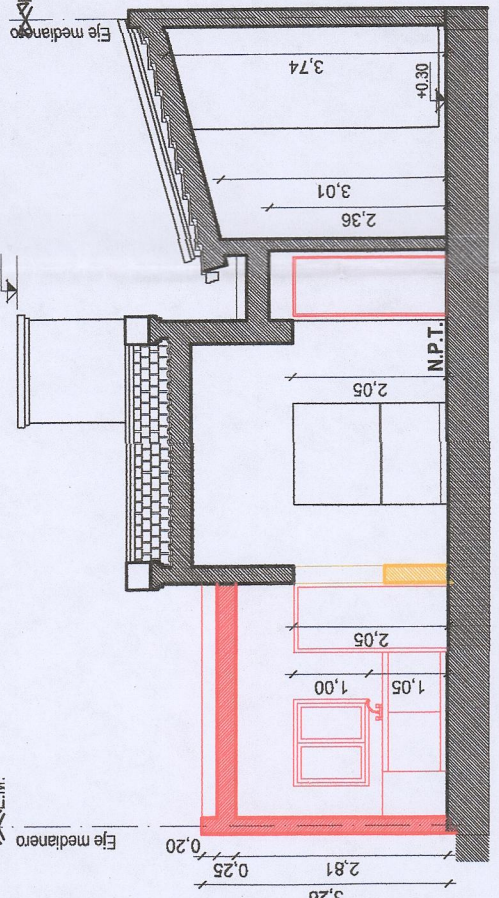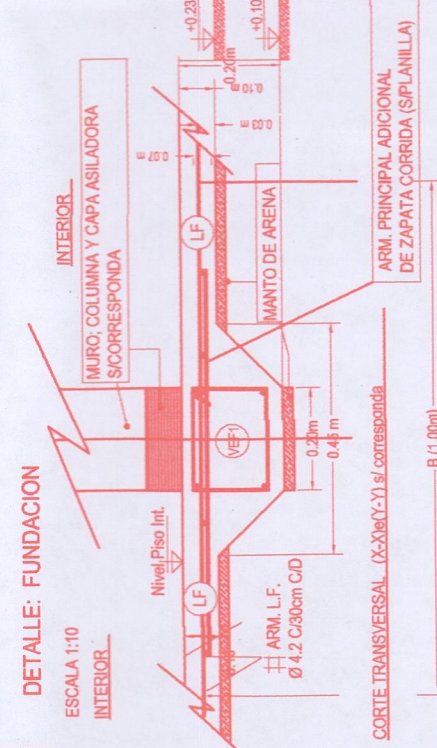

CORTE B-B

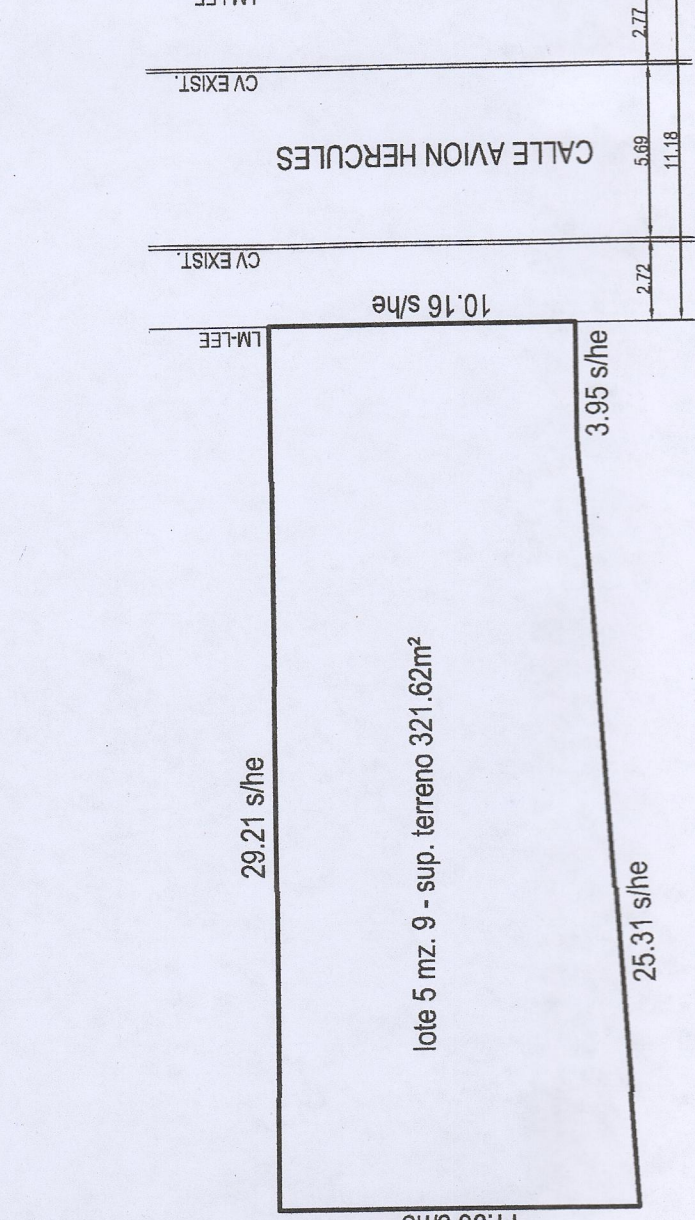

PLANIMETRIA Escala= 1:200

