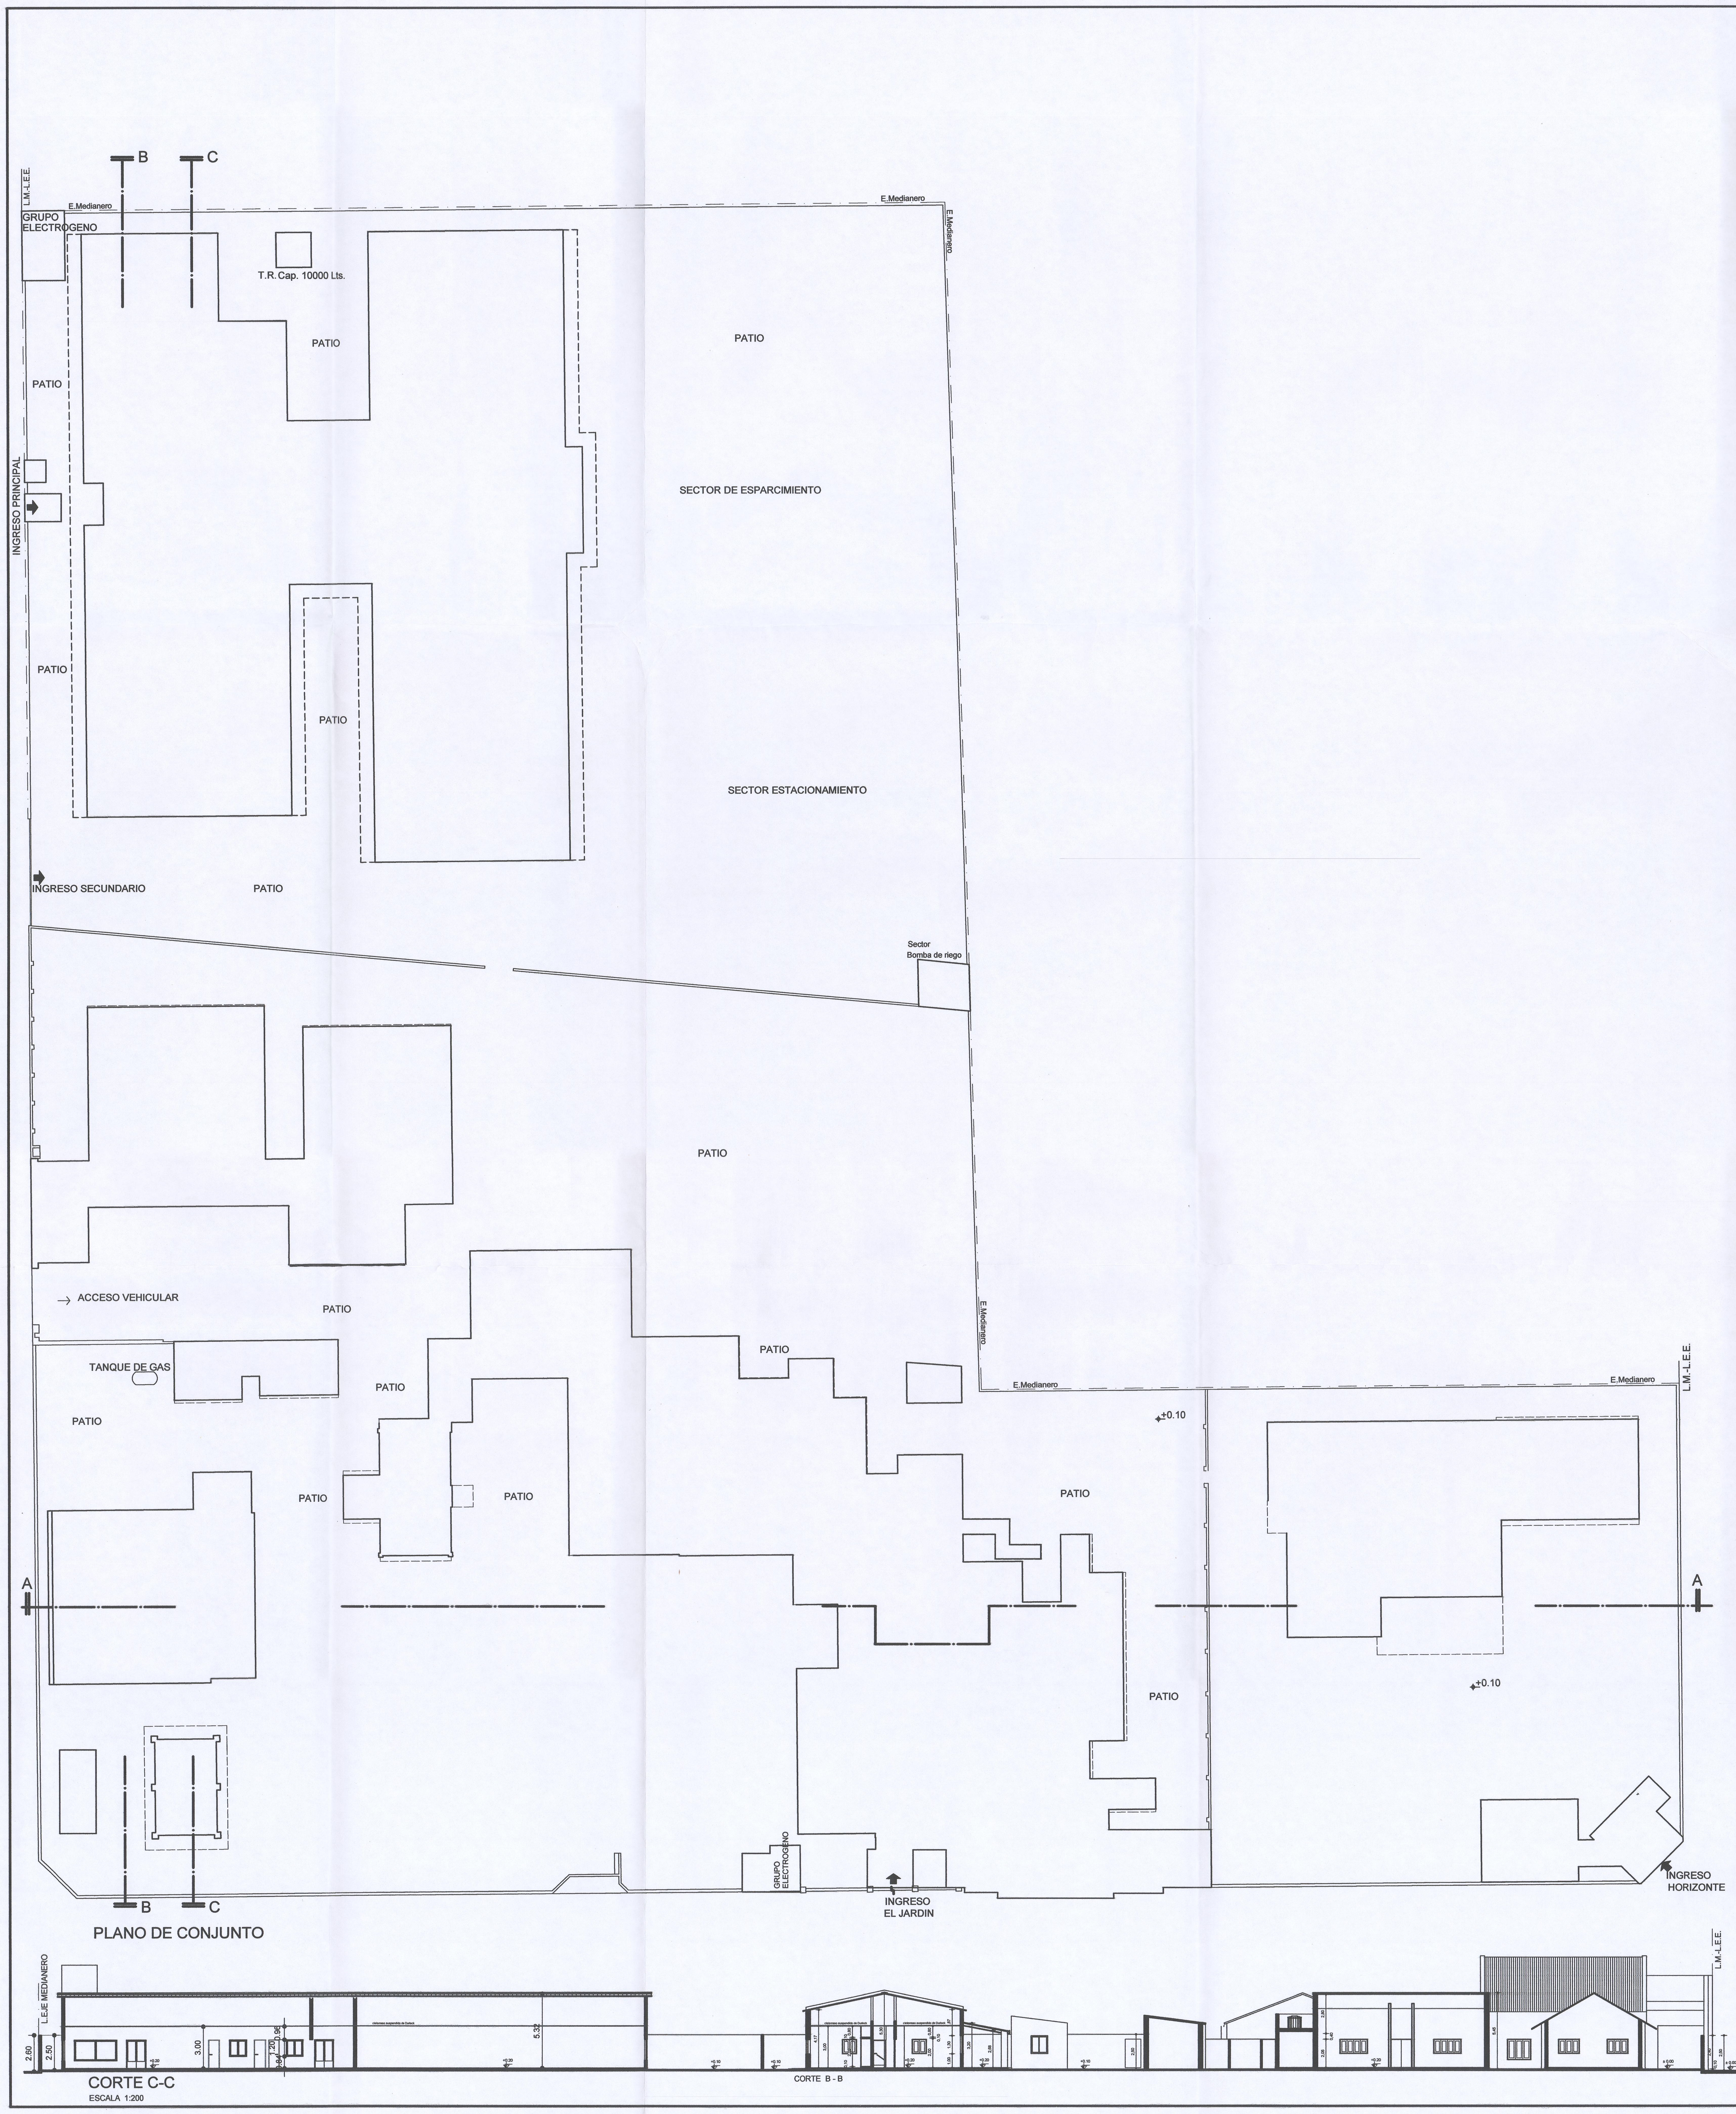

DIST. 10	ZONA 1	MZA. 14	PARC. 164/165/166/12/182	LEY 4.683
PADRON INMOBILIARIO : Nº 1-1-146.504 / Nº1-1-146.505		ICM : 62-N-2017	DOMINIO Nº 7N - 14894	200928

Destino de la Obra : ESTABLECIMIENTO SANITARIO

PROPIETARIO : EL JARDIN S.R.L.

C.U.I.T. Nº : 33-67503623-9

UBICACION : Avenida Madre de Ciudades Nº 4553 Esq.Calle Avion Pucara s/Nº Esq. Calle Aeropuerto Pajas Blancas s/Nº

BARRIO : AEROPUERTO

CIUDAD : CAPITAL - SANTIAGO DEL ESTERO

ESCALA : 1:100 - 1:200 - 1:500 .-

RELEVAMIENTO Fecha 23 MAYO 2021

SECRETARIA DE ECONOMIA – Municipalidad de la Capital SGO. DEL ESTERO – DIREC. DE SUELO URBANO

COLEGIO DE ARQUITECTOS – LEY 5654/87 – SANTIAGO DEL ESTERO

Fernanda Dargoltz – Arquitecta – Secretaria Técnica Adjunta – Colegio de Arquitectos S D E

SUP. TERRENO	s/t- s/h.e. 9.171,13 m²
SUP. CUBIERTA PLANTA BAJA	2.927,26 m²
SUP. CUBIERTA PLANTA ALTA	222,44 m²
SUP. CUBIERTA TOTAL	3.842,78 m²

PROPIETARIO
Domicilio

RELEVAMIENTO
Domicilio

DIRECCION DE SUELO URBANO – EXPEDIENTE 1-E-21 – FECHA DE SELLADO 29/07/21 – BOLETA Nº G3265

Fernando M. Barrionuevo – ARQUITECTO – M.P. Nº 0476

CROQUIS DE UBICACION

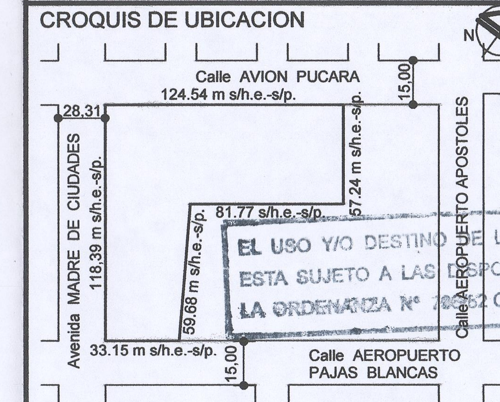

EL USO Y/O DESTINO DE LOS LOCALES ESTA SUJETO A LAS DISPOSICIONES DE LA ORDENANZA Nº 7062 CAPITULO 3.

CATEGORIA COLEGIO DE ARQUITECTOS

	COLECTORA Av. MADRE DE CIUDADES	C/ AEROPUERTO PAJAS BLANCAS	Calle PUCARA
ANCHO DE VEREDA	4.40 m	3.50 m	3,50 m
ANCHO DE CALZADA	9.30 m	8,00 m	8,00 m
ANCHO DE CALLE	19.54 m	15.00 m	15,00 m

	Av. MADRE DE CIUDADES	C/ AEROPUERTO PAJAS BLANCAS	Calle PUCARA
PAVIMENTO	SI	NO	NO
SERVICIOS CLOACALES	NO	NO	NO

DESIGNACION :

PLANO DE RELEVAMIENTO

- PLANO DE CONJUNTO Y CORTE -

(5 - 5)

OBSERVACIONES

13 AGO 2021

Las referencias al Titulo de Dominio son meramente indicativas, y la aprobación administrativa no valora los derechos que de ellos emergen.

MUNICIPALIDAD DE LA CIUDAD DE SANTIAGO DEL ESTERO
SECRETARIA DE ECONOMIA
APROBADO
DIRECCIÓN DE SUELO URBANO
EXPEDIENTE 01 - E - 2021
FECHA 03 - 09 - 2021

Ing. Agrim. MARIO J. LOPEZ
DIRECCION DE CATASTRO
MUNICIPALIDAD DE SGO. DEL ESTERO

Arq. ABRAHAM BERNARDO ROMINA
Dpto. OBRAS PRIVADAS
DIRECCION DE SUELO URBANO

Arq. BERNARDO M. SANTILLAN
DIRECTOR
DIRECCION DE SUELO URBANO
MUNICIPALIDAD DE SGO. DEL ESTERO