




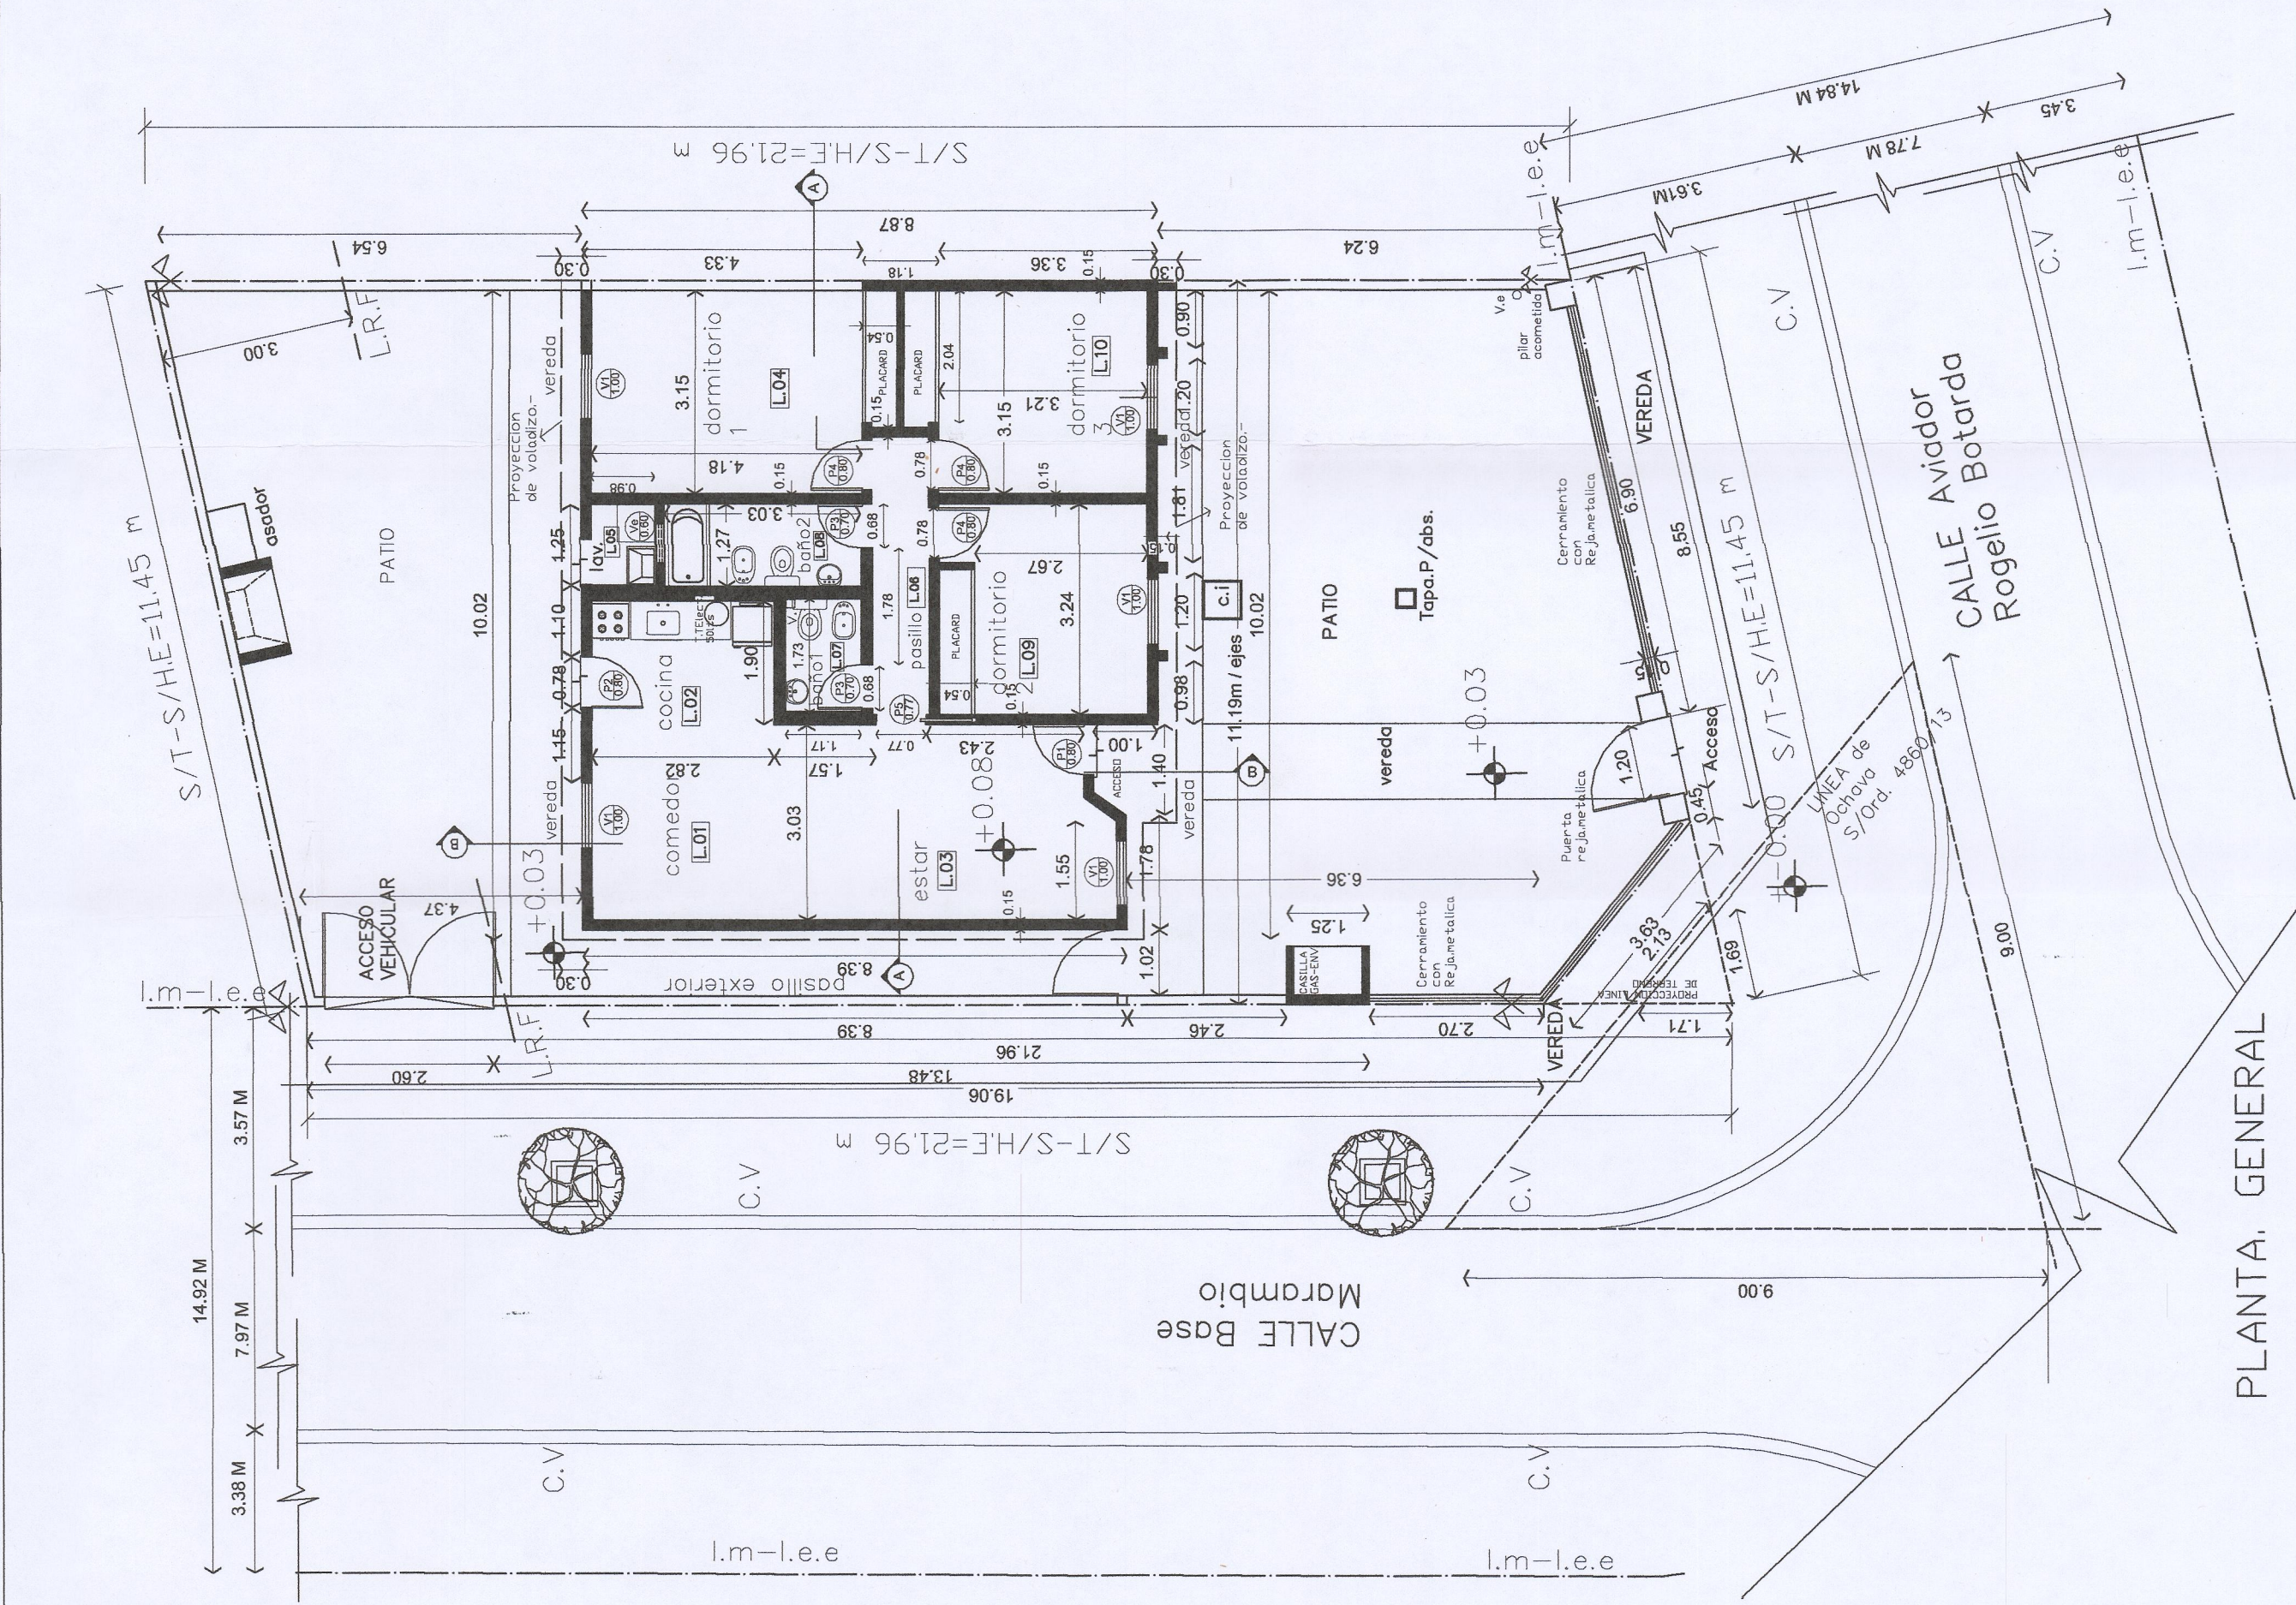


PLANTA GENERAL

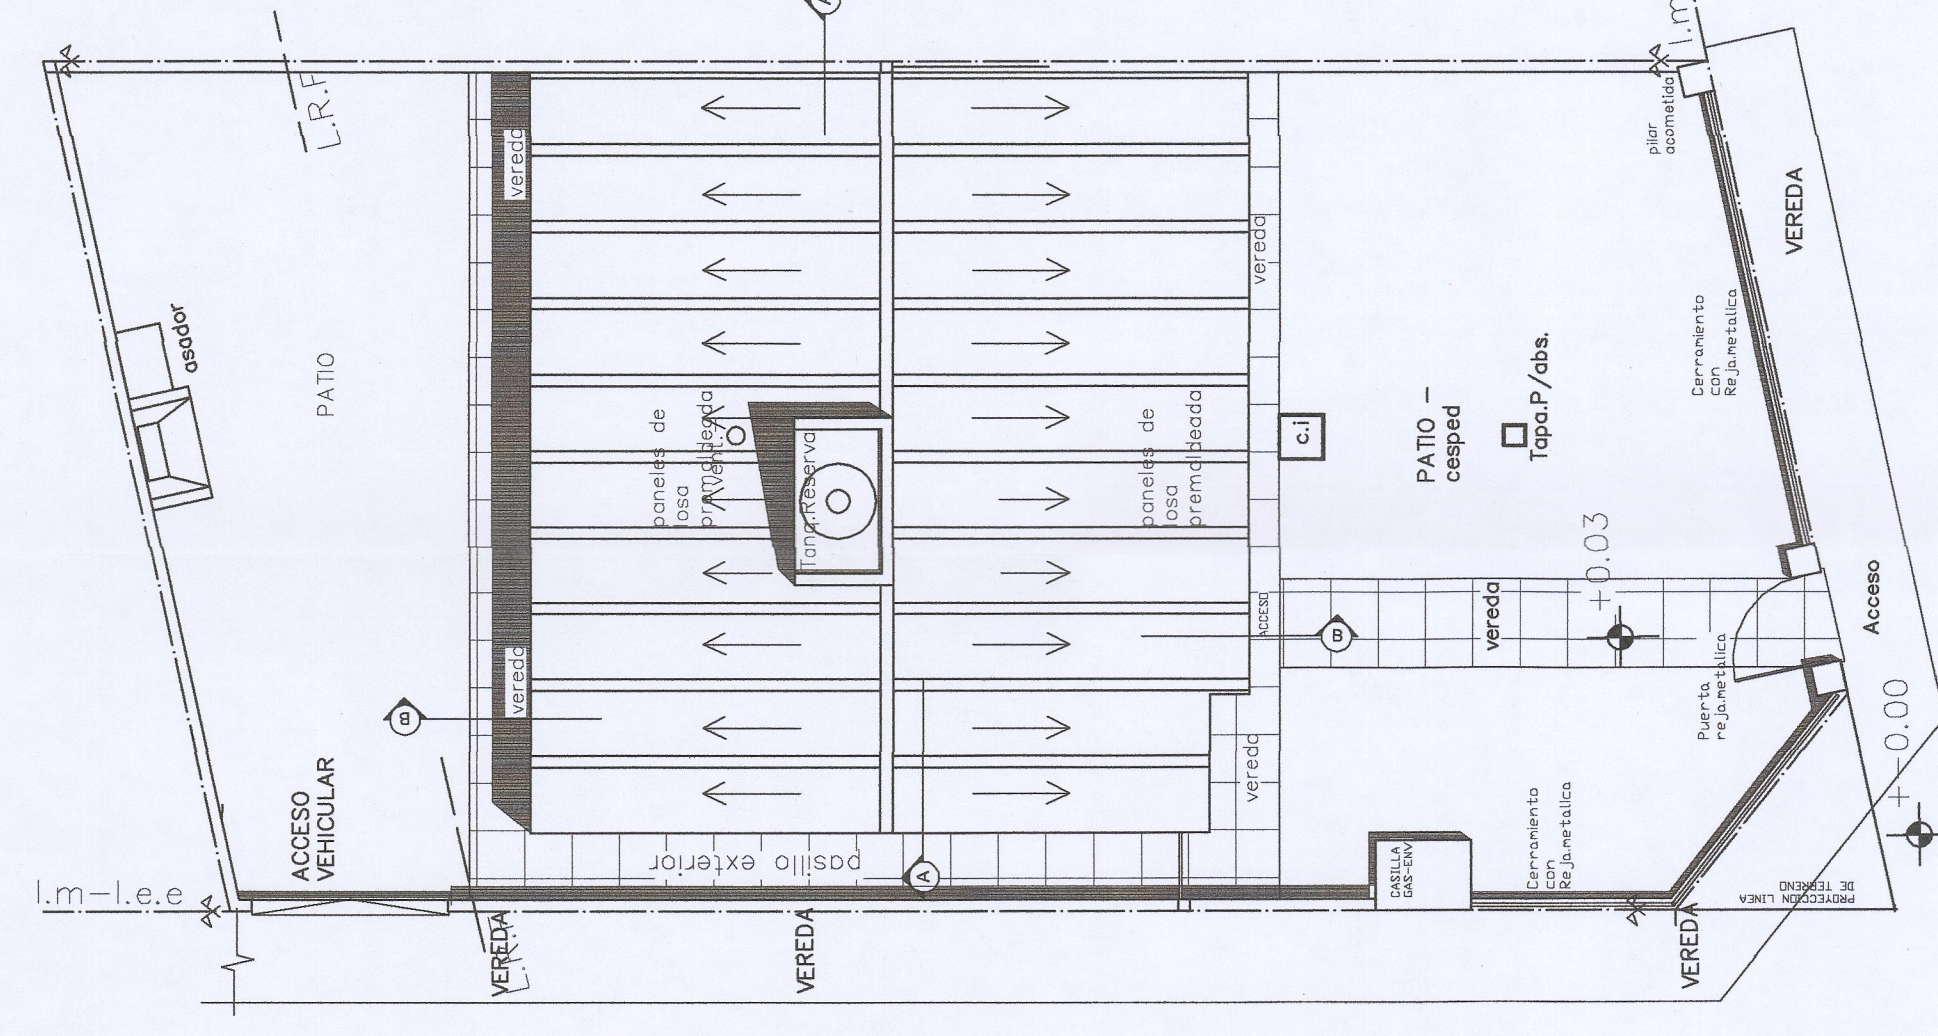


PLANTA DE TECHOS

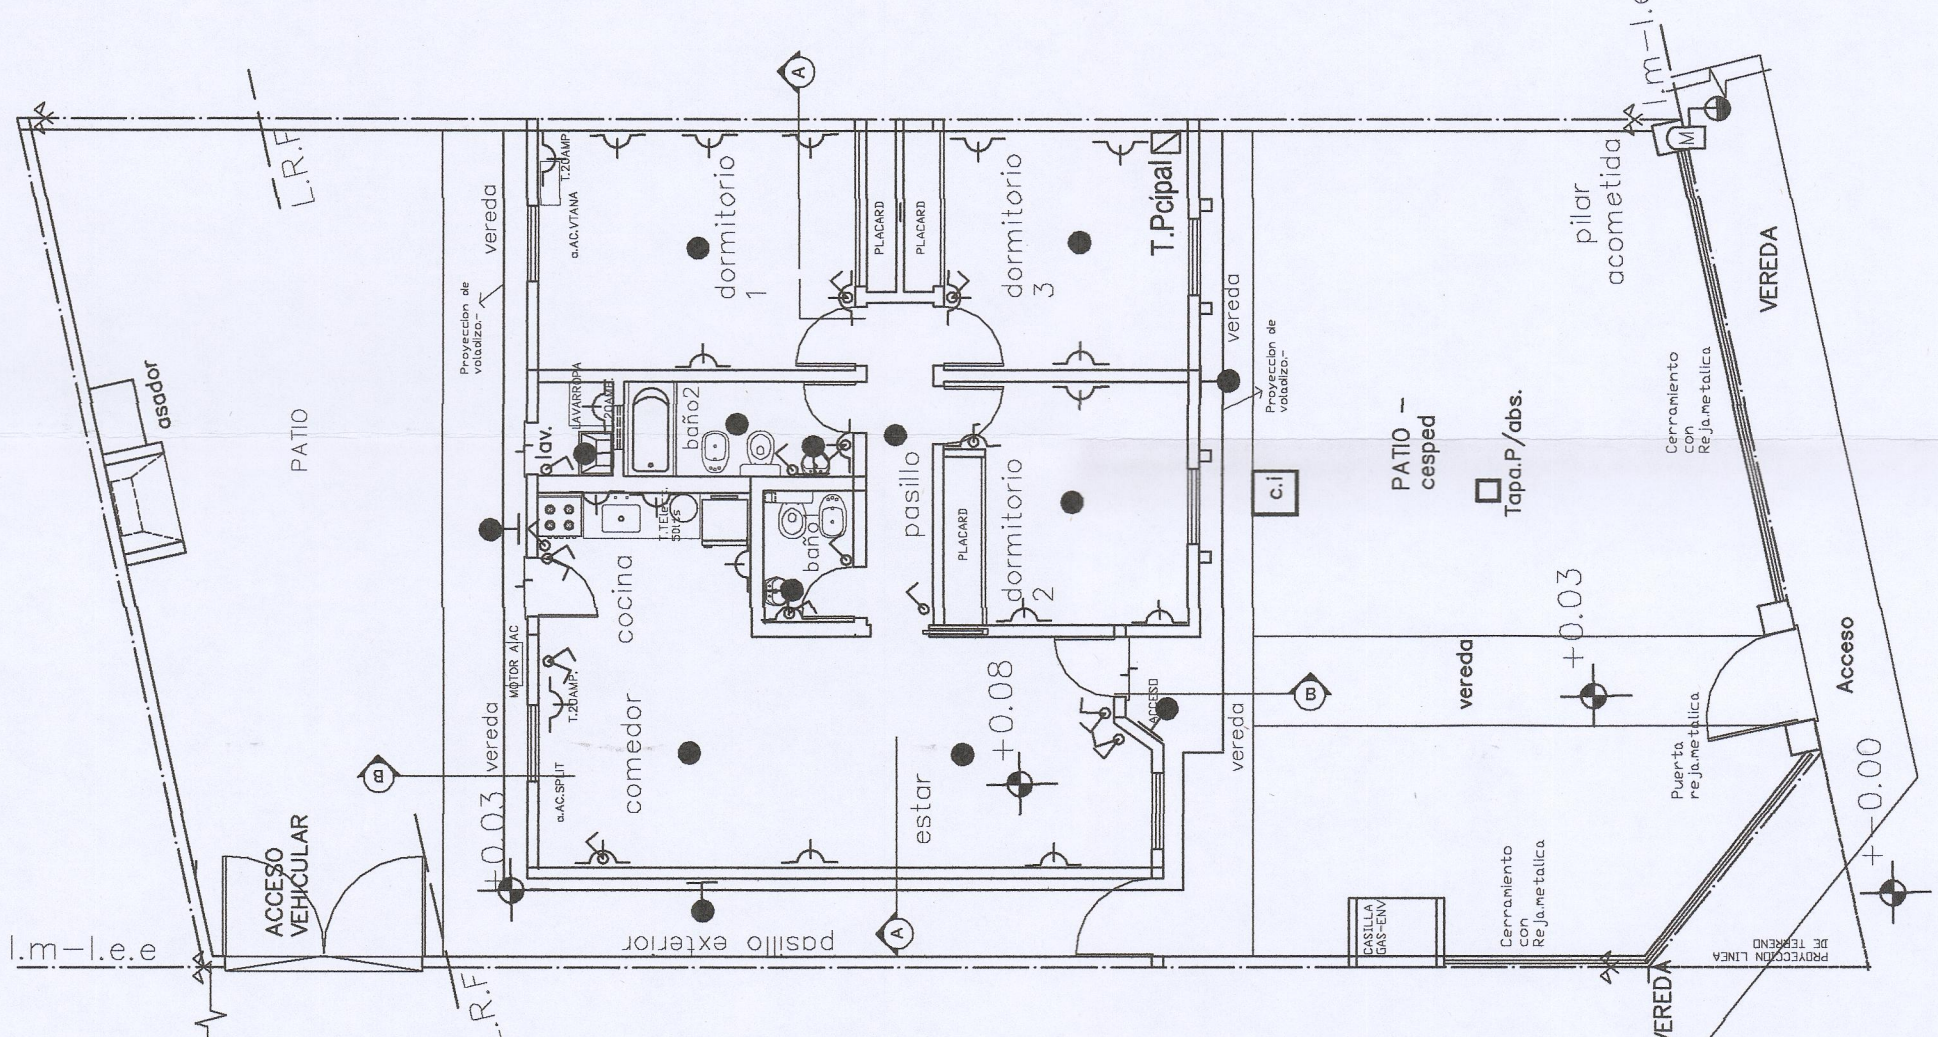


PLANTA RELEV. INSTALACION ELECTRICA

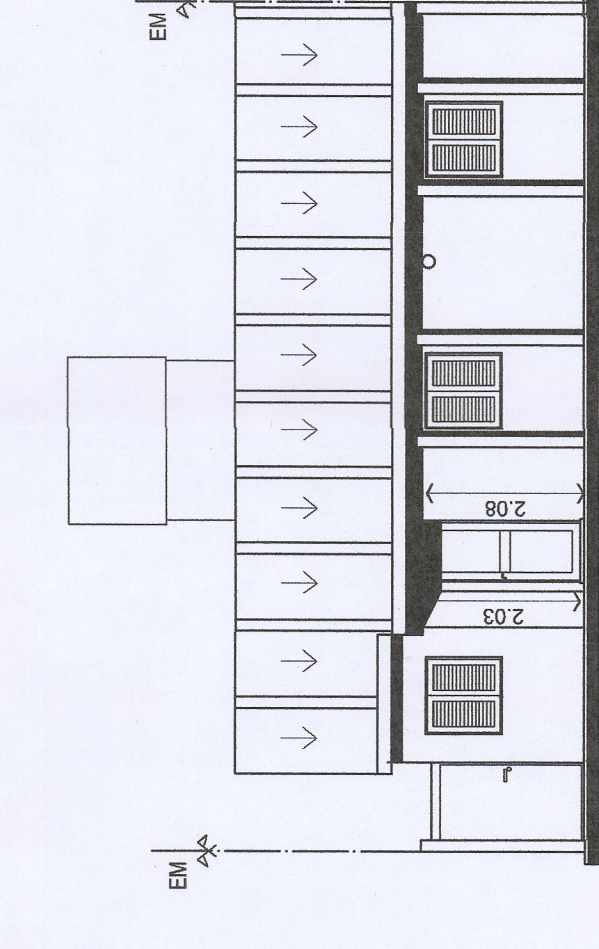

FACHADA - ESC 1:100

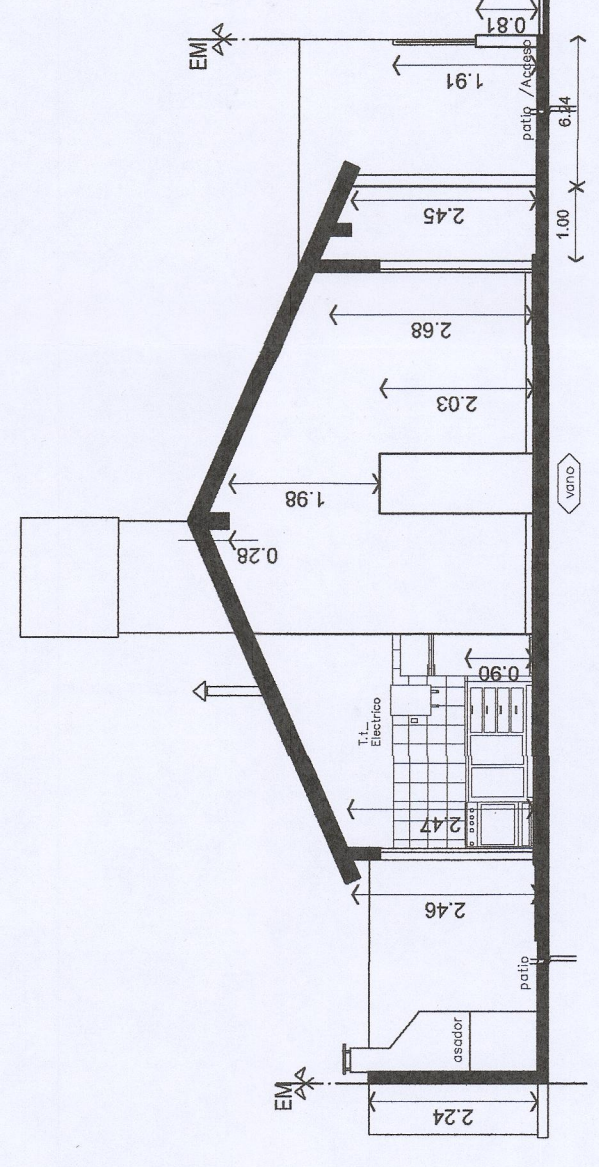

CORTE B-B - ESC 1:100

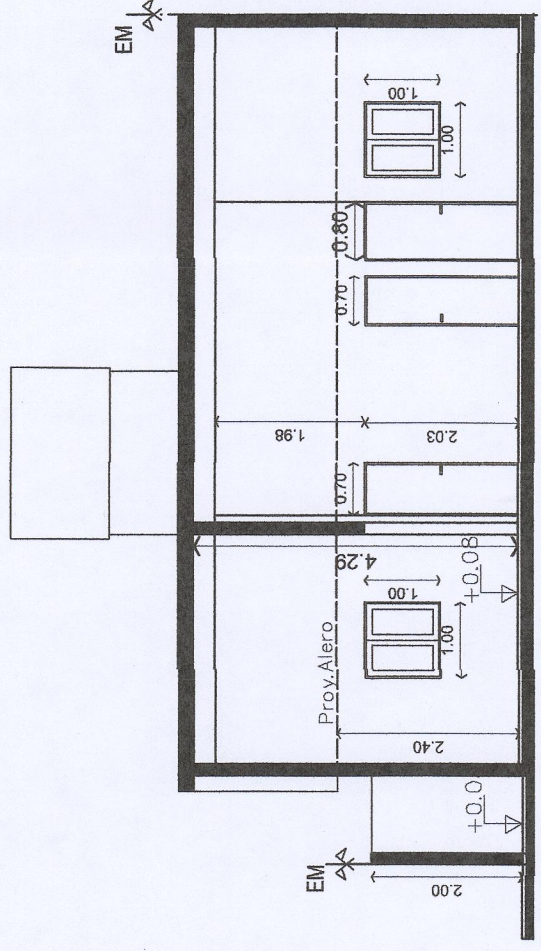


CORTE A-A - ESC 1:100

REFERENCIAS		ABERTURAS		Observaciones	
GH	Brzo de luz	Sup.	Arco	Arco	V
O	Centro de luz	m.			
1	Llave de 1 punto				
2	Caja de derivacion				
3	Tablero Principal				
4	Tablero Seccional				
5	Comodoro de ventilador				
6	Toma Tierra				
7	Fotocopia 20A.				
8	Linea Aereo				
9	Pulsador				
10	Campanilla				

Superficie Cubierta Total: 86.70 m2.

PLANIMETRIA esc: 1:250

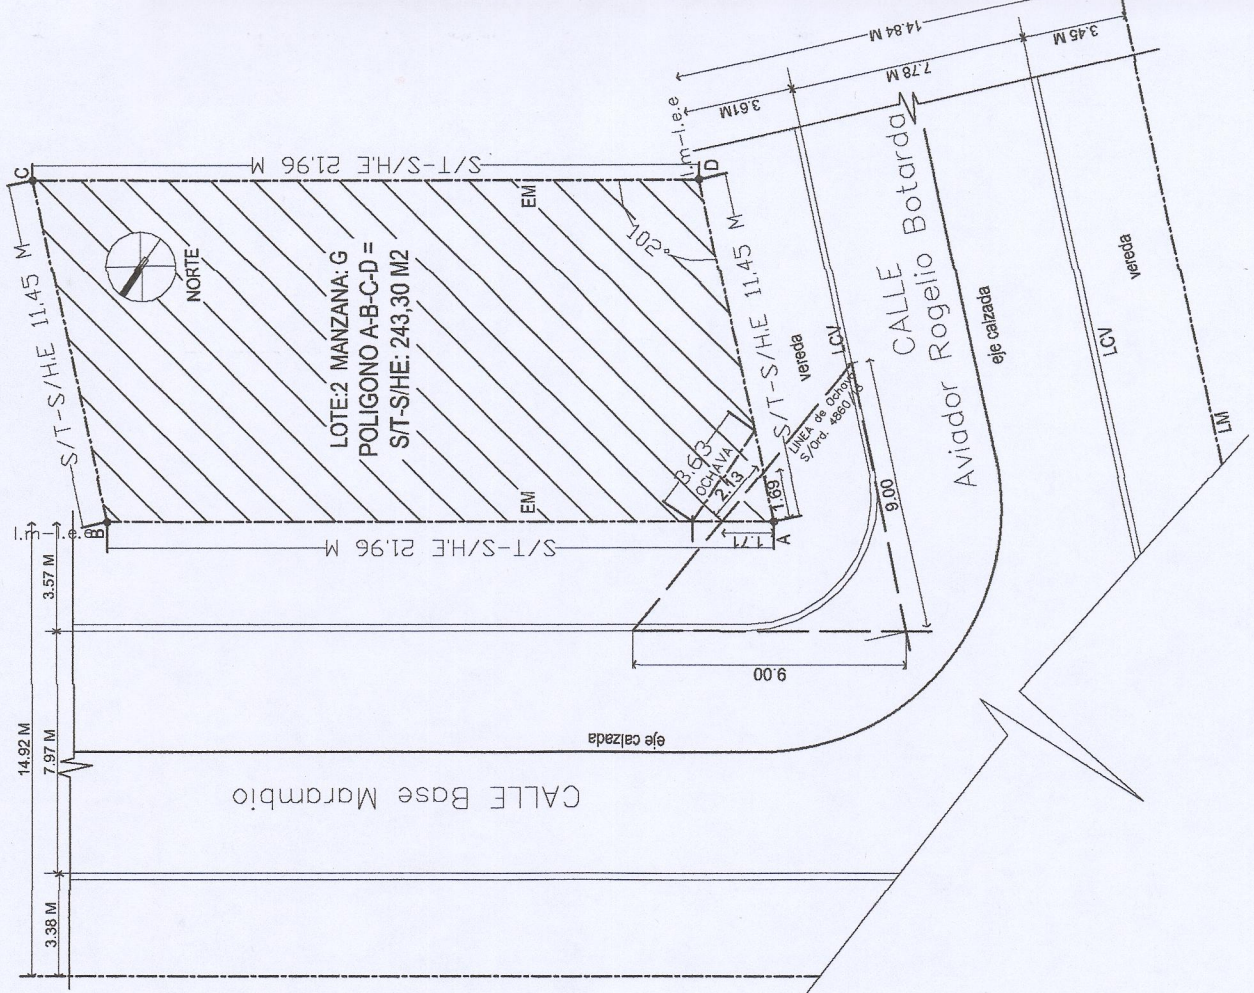

DIST: 10

ZONA: 02

MZA: 49

parc: 170 / 171

PADRON INMOBILIARIO: 01-01-98759

lcm: 232-S-25

DOMINIO: MFR N° 7m-12992

DESTINO DE LA OBRA:

VIVIENDA UNIFAMILIAR

PROPIETARIO:

AMALIA DEL CARMEN SERRANO

dni: 16.007.574

cui: 27-16007574-6

UBICACION:

Calle Aviator Rogelio Botarda esquina, Calle Base Morambio, N° 3793

BARRIO:

B° Aeropuerto.

CIUDAD:

Capital - Santiago del Estero

ESCALA:

1:100 / 1:250 / 1:500

SUP. DEL TERRENO: S/T- S/H/E: 243.30 M2

SUP. CUBIERTA TOTAL:

86.70 M2

PROPIETARIO:

Domicilio:

RELEVAMIENTO:

Domicilio:

direccion Tecnica:

Domicilio:

Electricidad:

Domicilio:

Categoria Profesional de Obra:

PAVIMENTOS:

SERVICIOS CLOACALES:

no

DESIGNACION:

C.A. Rogelio Botarda C.A. Base Morambio

ANCHO DE CALLE:

14.84 M

14.92 M

ANCHO DE VEREDA:

3.61 M

3.57 M

ANCHO DE CALZADA:

7.76 M

7.97 M

PLAN DE RELEVAMIENTO

Observaciones:

son meramente indicativas y la aprobación administrativa no valora los derechos que de ellos emanan.

APROBADO

DIRECCION DE SUELO URBANO

EXPEDIENTE: 563-31-2025/13-S-25

Ing. Arq. J. LEONARDO ARDONA

JEFE DE OFICINA DE PROYECTOS DE PROYECTOS DE PROYECTOS

Ing. Arq. J. LEONARDO ARDONA

JEFE DE OFICINA DE PROYECTOS DE PROYECTOS DE PROYECTOS