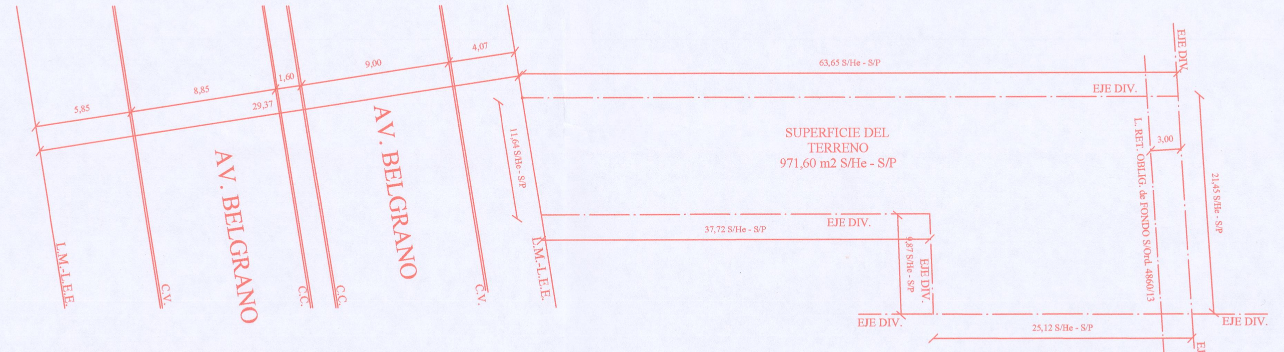

PLANIMETRIA

ESC. 1:400 - ESCALA CALLE 1:250

PLANILLA DE ILUMINACION, VENTILACION Y SUPERFICIES							
PLANTA BAJA							
LOCAL		ABERTURAS			AREAS		OBSERV.
DESIGNACION	SUPERF. m2	DESIG.	ANCHO	ALTO	ILUM.	VENT.	
PLANTA BAJA							
LOCAL COMERCIAL	100,78	V1	2,07	2,20	4,55	-----	Dos Paños Fijos de Vidrio
		PV1	2,06	2,20	4,53	4,53	Puerta Ventana
		V2	2,07	0,50	2,06	2,06	Dos Ventanas
		V3	2,06	0,50	1,03	1,03	
OFICCE	8,64	CV1	0,20	0,20	-----	0,04	Conducto de Ventilacion
BAÑO 1	2,90	CV2	0,20	0,15	-----	0,03	Conducto de Ventilacion
BAÑO 2	1,62	CV2	0,20	0,15	-----	0,03	Conducto de Ventilacion
ING./EGRESO COCH.	23,50	Vo1	4,70	2,80	13,16	13,16	Vano
COCHERAS.CIRC.	458,56	PM	4,70	2,15	10,10	10,10	Porton Metalico
		Vo2	4,04	2,80	11,31	11,31	Vano
		Vo3	6,50	2,80	18,20	18,20	Vano
		Vo4	3,60	2,80	10,08	10,08	Vano
CABINA CONTROL	2,34	V4	1,10	1,05	2,30	2,30	Dos Ventanas
BAÑO 3	1,69	CV2	0,20	0,15	-----	0,03	Conducto de Ventilacion
PLANTA PRIMER y SEGUNDO PISO							
COCHERAS.CIRC.	608,09	Vo5	6,00	1,60	9,60	9,60	Vano
		Vo6	4,50	1,60	7,20	7,20	Vano
		Vo7	4,04	1,60	6,46	6,46	Vano
		Vo8	6,50	1,60	10,40	10,40	Vano
		Vo9	3,75	1,60	6,00	6,00	Vano
PLANTA DEL TERCER PISO							
COCHERAS.CIRC.	641,27	Vo10	11,10	1,45	16,09	16,09	Vano
		Vo11	11,14	1,45	16,15	16,15	Vano
DEPOSITO	16,67	CV3	0,30	0,30	-----	0,09	Conducto de Ventilacion

PLANILLA DE SUPERFICIES

PLANTA BAJA	804,35 m2
PLANTA 1° PISO	804,35 m2
PLANTA 2° PISO	804,35 m2
PLANTA 3° PISO	804,35 m2
PLANTA SALA DE MAQUINAS	16,42 m2
F.L.M.	8,65 m2
TOTALES	3242,47m2

FACHADA S/ AVENIDA BELGRANO

DIST. : 03 ZONA : 03 MANZ. : 54 PARC. : 220 LEY 4683

PADRON INMOB. : 01-01-23002 / 01-01-93257 I.C.M. : 236 - A - 2024 DOMINIO : 7N-11010 / 7N-11011

2 4 0 2 0 1 8 8

50

DEST. DE LA OBRA : LOCAL COMERCIAL - COCHERAS (83)

PROPIETARIO : MARIO ALBERTO AYUCH
D.N.I. N° 8.130.176 - C.U.I.L./T. N° 20-08130176-0

UBICACION : AVENIDA BELGRANO (N) N° 67

BARRIO : Dr. JUAN BAUTISTA ALBERDI

CIUDAD : CAPITAL - SANTIAGO DEL ESTERO

ESCALA : 1 : 100 - 1 : 250 - 1 : 400

SUP. DE TERRENO : 971,60 m2 S/He-S/P
VER PLANILLA DE SUPERFICIE
SUP. CUBIERTA TOTAL : 3242,47 m2

CROQUIS DE UBICACION

PROPIETARIO :
DOMICILIO :

PROYECTO :
DOMICILIO :

GONZALO J. ZANNI
ARQUITECTO
M. P. 0392

DIR. TECNICA :
DOMICILIO :

RICARDO H. LOREFICE
INGENIERO CIVIL
M.P. 2955

ELECTRICIDAD :
DOMICILIO :

CATEG. COLEGIO DE ARQUITECTOS : "A"

ANCHO DE CALLE : 29,37 m
ANCHO DE VEREDA : 4,07 m
ANCHO DE CALZADA : 9,00 m

PAVIMENTO : SI
SERVICIOS CLOACALES : SI

DESIGNACION :

PLANO DE OBRA NUEVA
ARQUITECTURA

①

OBSERVACIONES : 30 JUL 2024

Las referencias al Titulo de dominio son meramente indicativas y la aprobación administrativa no afecta los derechos que de ellos emergen.

DIRECCION DE SUELO URBANO
EXPEDIENTE 139 31 24
FECHA DE ... 19 JUL 2024
BOLETA N° 9801

COLEGIO DE ARQUITECTOS SGO. DEL ESTERO
PROYECTO Y DIRECCION DE OBRA
10 JUL 2024
SUSANA ABDALA ASSIS
Arquitecta
Secretaría Técnica
Colegio de Arquitectos SDE

DIRECCION DE SUELO URBANO
EXPEDIENTE 139 31 24
FECHA DE ... 14 NOV. 2024
3361

SECRETARIA DE ECONOMIA
Municipalidad de la Capital
SGO. DEL ESTERO
DIREC. DE SUELO URBANO

EL USO Y/O DESTINO DE LOS LOCALES ESTA SUJETO A LAS DISPOSICIONES DE LA ORDENANZA N° 796/82 CAPITULO 3.

PERMISO DE COMIENZO DE OBRA N° ... DIRECCION DE SUELO URBANO
05/11/2024

MUNICIPALIDAD DE LA CIUDAD DE SANTIAGO DEL ESTERO
SECRETARIA DE ECONOMIA
APROBADO
DIRECCIÓN DE SUELO URBANO

Arq. ESTER R. CHAZ
DIRECCION DE SUELO URBANO