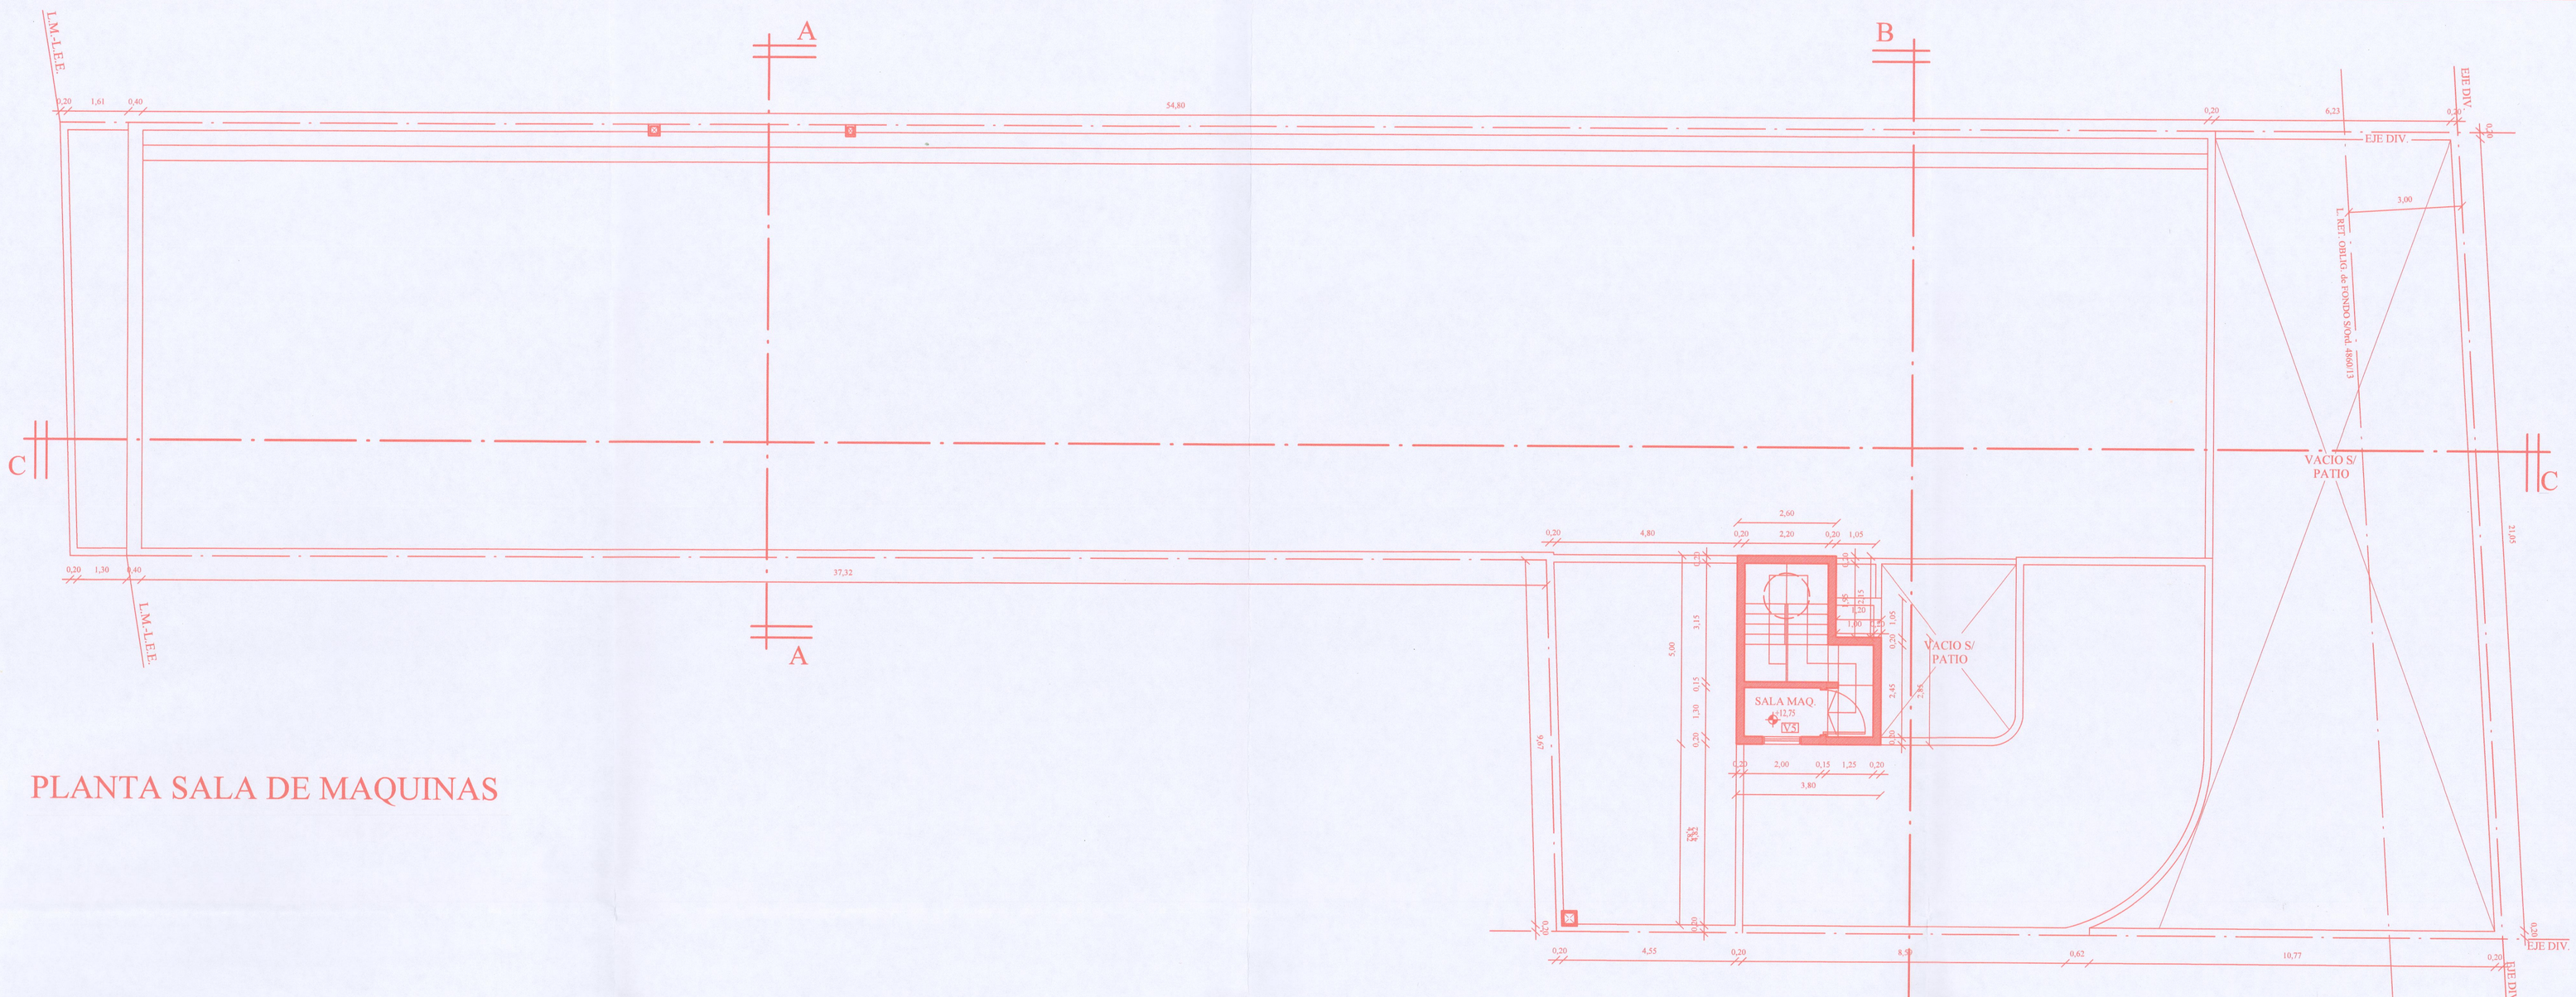

PLANTA SALA DE MAQUINAS

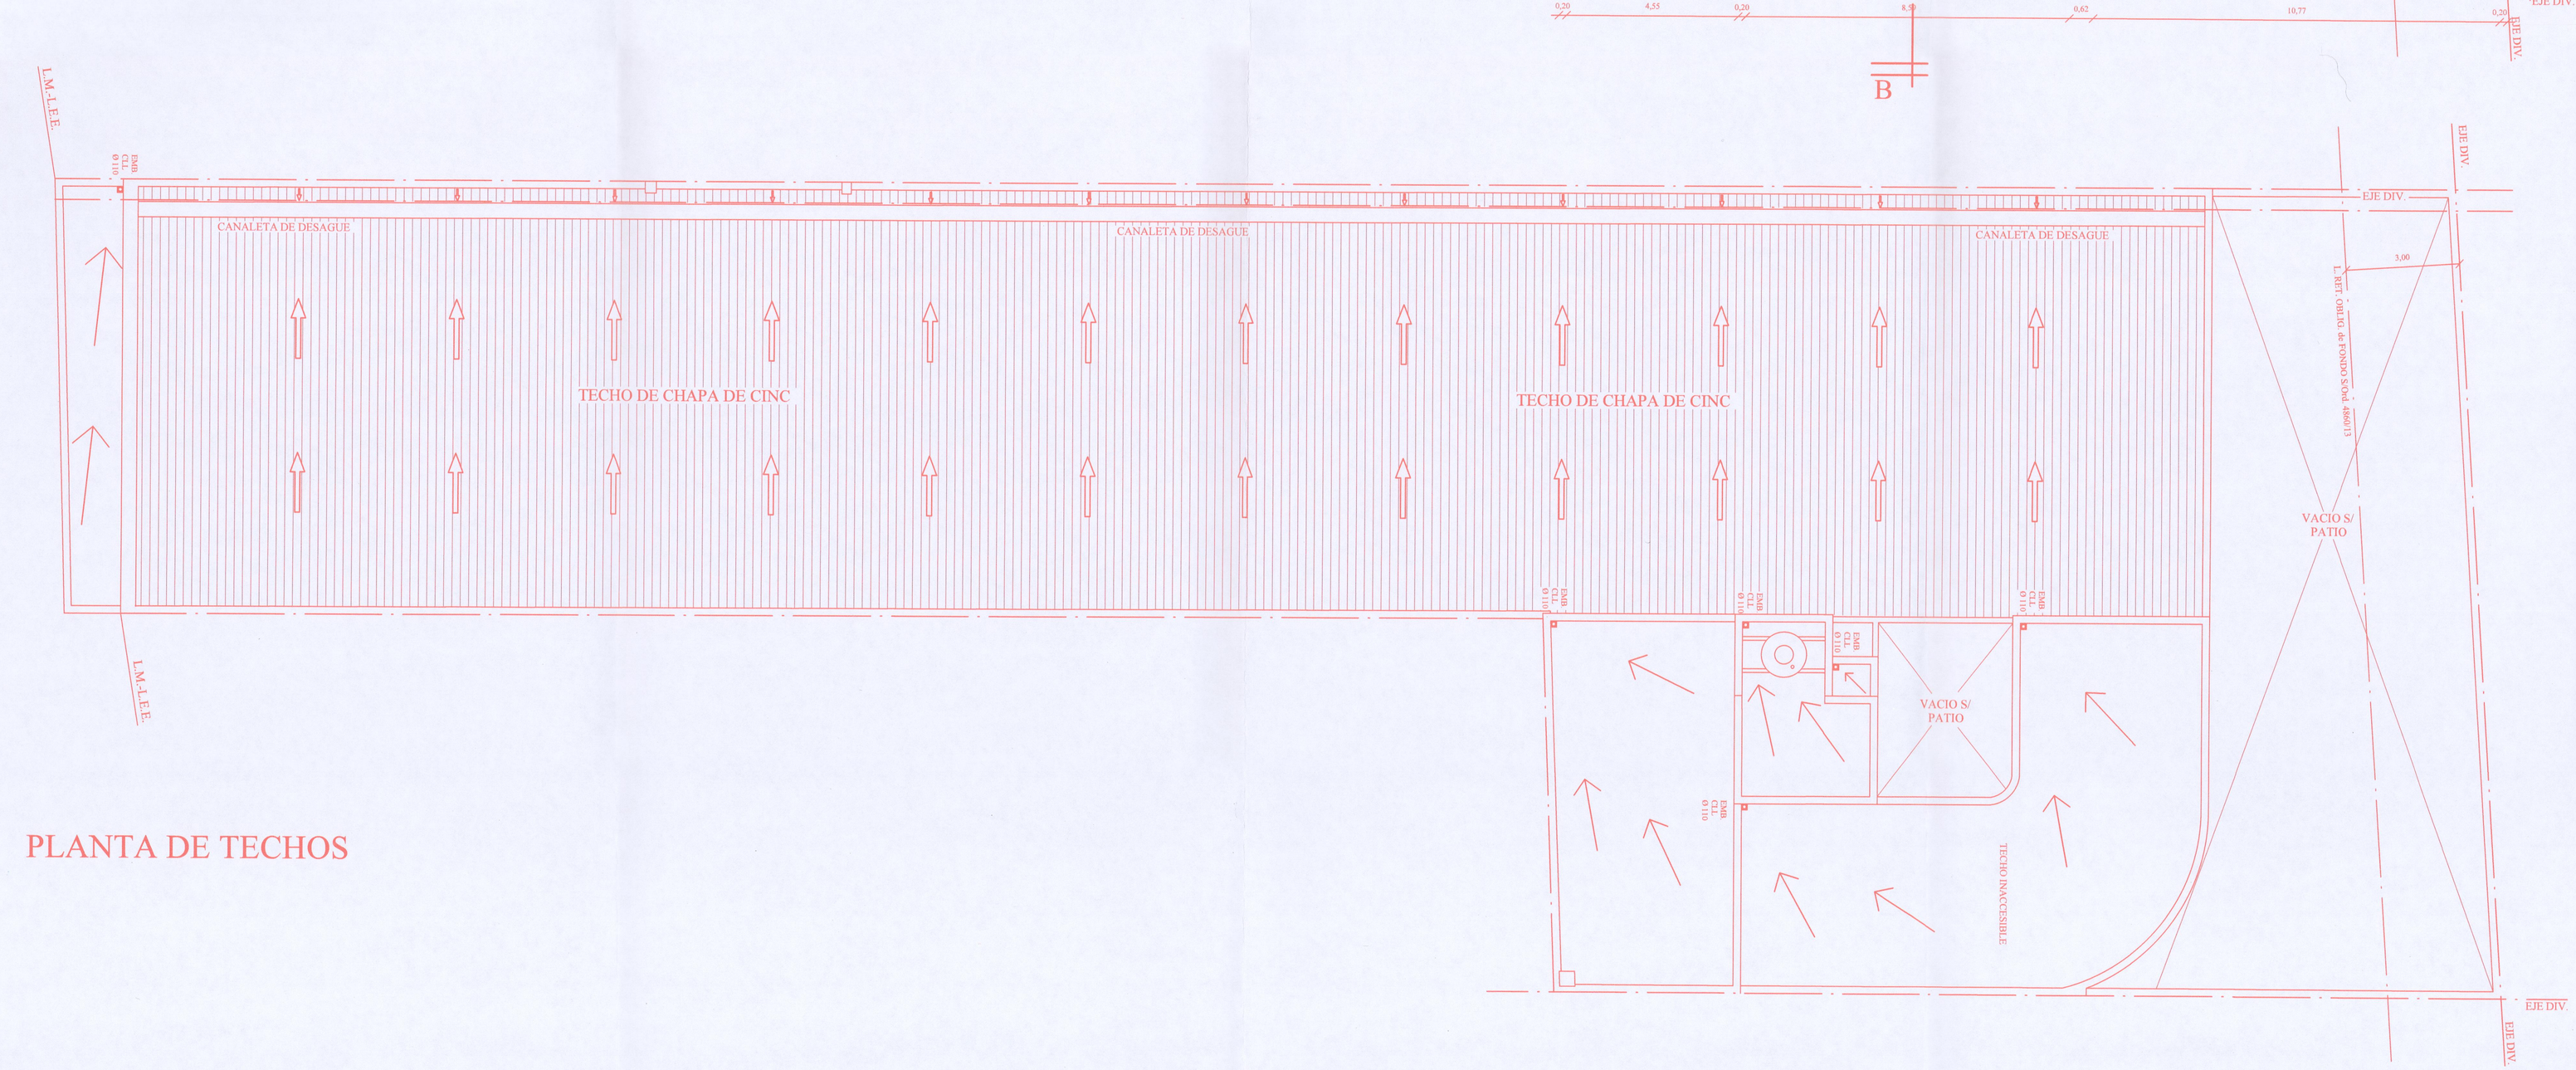

PLANTA DE TECHOS

PLANILLA DE SUPERFICIES

PLANTA BAJA	804,35 m2
PLANTA 1º PISO	804,35 m2
PLANTA 2º PISO	804,35 m2
PLANTA 3º PISO	804,35 m2
PLANTA SALA DE MAQUINAS	16,42 m2
F.L.M.	8,65 m2
TOTALES	3242,47m2

PLANILLA DE ILUMINACION, VENTILACION Y SUPERFICIES

PLANTA BAJA

LOCAL	ABERTURAS				AREAS		OBSERV.
DESIGNACION	SUPERF. m2	DESIG.	ANCHO	ALTO	ILUM.	VENT.	
PLANTA SALA DE MAQUINA							
SALA DE MAQUINA	2,59	V5	1,00	1,00	1,00	1,00	

DIST. : 03 ZONA : 03 MANZ. : 54 PARC. : 220 LEY 4683

PADRON INMOB. : 01-01-23002 / 01-01-93257 I.C.M. : 236 - A - 2024 DOMINIO : 7N-11010 / 7N-11011

DEST. DE LA OBRA : LOCAL COMERCIAL - COCHERAS (83)

PROPIETARIO : MARIO ALBERTO AYUCH
D.N.I. Nº 8.130.176 - C.U.I.L./T. Nº 20-08130176-0

UBICACION : AVENIDA BELGRANO (N) Nº 67

BARRIO : Dr. JUAN BAUTISTA ALBERDI

CIUDAD : CAPITAL - SANTIAGO DEL ESTERO

ESCALA : 1 : 100 - 1 : 400

SUP. DE TERRENO : 971,60 m2 S/He-S/P
VER PLANILLA DE SUPERFICIE
SUP. CUBIERTA TOTAL : 3242,47 m2

CROQUIS DE UBICACION

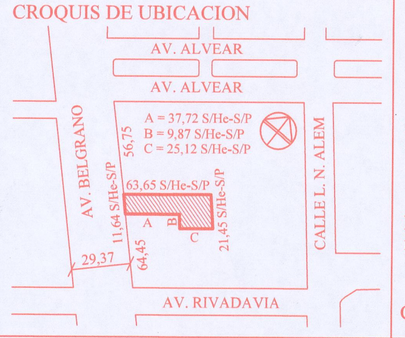

ANCHO DE CALLE : 29,37 m
ANCHO DE VEREDA : 4,07 m
ANCHO DE CALZADA : 9,00 m

DESIGNACION : PLANO DE OBRA NUEVA
ARQUITECTURA

PROPIETARIO : DOMICILIO :

PROYECTO : DOMICILIO :

DIR. TECNICO : DOMICILIO :

ELECTRICIDAD : DOMICILIO :

CALCULISTA : COLEGIO DE ARQUITECTOS
MATRICULA :
SERVICIOS SANITARIOS :

OBSERVACIONES: 30 JUL 2024
Las referencias al Título de dominio son meramente indicativas, y la aprobación administrativa no valora los derechos que de ellos emergen.

Ing. Agrim. J. LEANDRO ARJONA
JEFE DE AREA DE VISACIONES TECNICAS
DIRECCION DE CATASTRO MUNICIPAL

MUNICIPALIDAD DE LA CIUDAD DE SANTIAGO DEL ESTERO
SECRETARIA DE ECONOMIA
APROBADO
DIRECCIÓN DE SUELO URBANO
EXPEDIENTE: 132-31-2024-Corp 10-A-2024
FECHA:

PERMISO DE COMIENZO DE OBRA Nº 125/2024 05/11/2024
DIRECCION DE SUELO URBANO

Arq. ABRAHAM BERNARDO ROMINA
Dpto. OBRAS PRIVADAS
DIRECCION DE SUELO URBANO

Arq. ESTER R. CHALOM
SUB-DIRECTORA
DIRECCION DE SUELO URBANO

240201888

COLEGIO DE ARQUITECTOS
10 JUL 2024
PROYECTO Y DIRECCION DE OBRA
ALEJANDRA CASSIS
Arquitecta
Secretaria Técnica
Colegio de Arquitectos SDE

DIRECCION DE SUELO URBANO
EXPEDIENTE 132-31-24
FECHA DE ENTRADA 9 JUL 2024
FOLIO 2301

GONZALO J. ZANNI
ARQUITECTO
M.P. 0392

RICARDO A. OREFICE
INGENIERO CIVIL
M.P. 2955

SECRETARIA DE ECONOMIA
Municipalidad de la Capital
SGO. DEL ESTERO
DIRECCION DE SUELO URBANO

DIRECCION DE SUELO URBANO
EXPEDIENTE 132-31-24
FECHA DE ENTRADA 14 NOV 2024
FOLIO 3361

EL USO Y/O DESTINO DE LOS LOCALES ESTA SUJETO A LAS DISPOSICIONES DE LA ORDENANZA Nº 7982/2 CAPITULO 3.