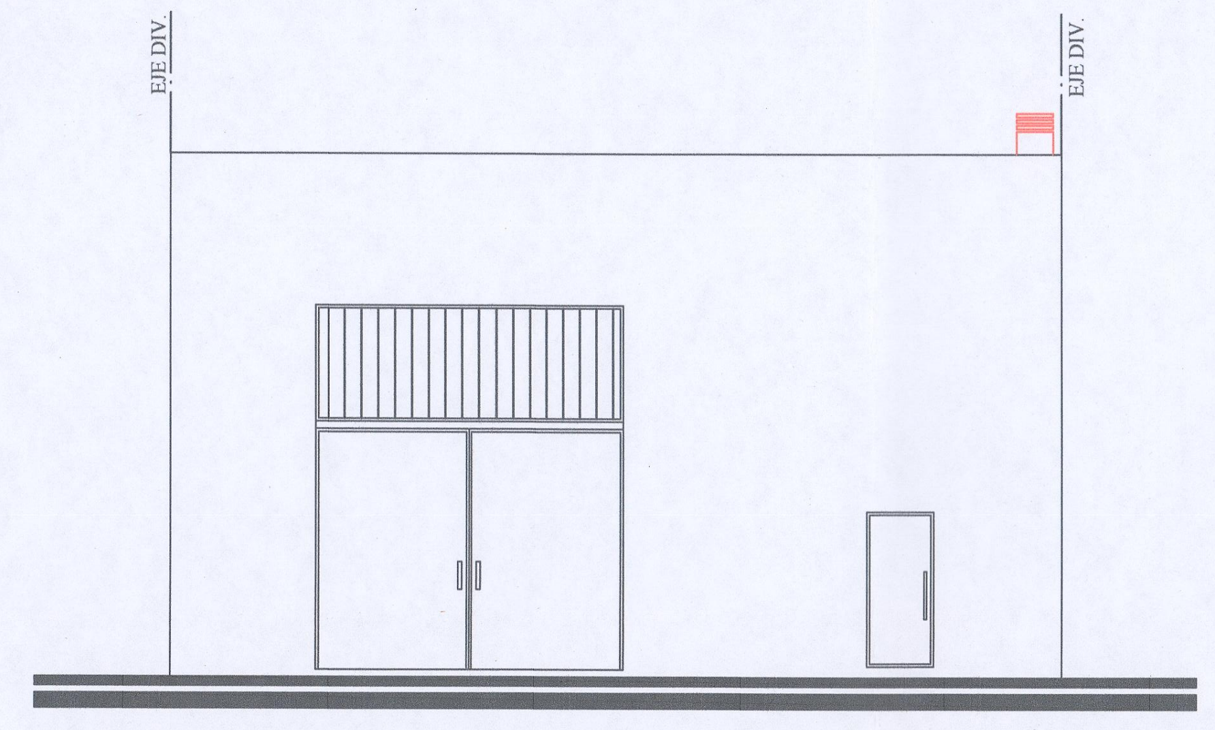

FACHADA S/ CALLE ANTONINO TABOADA

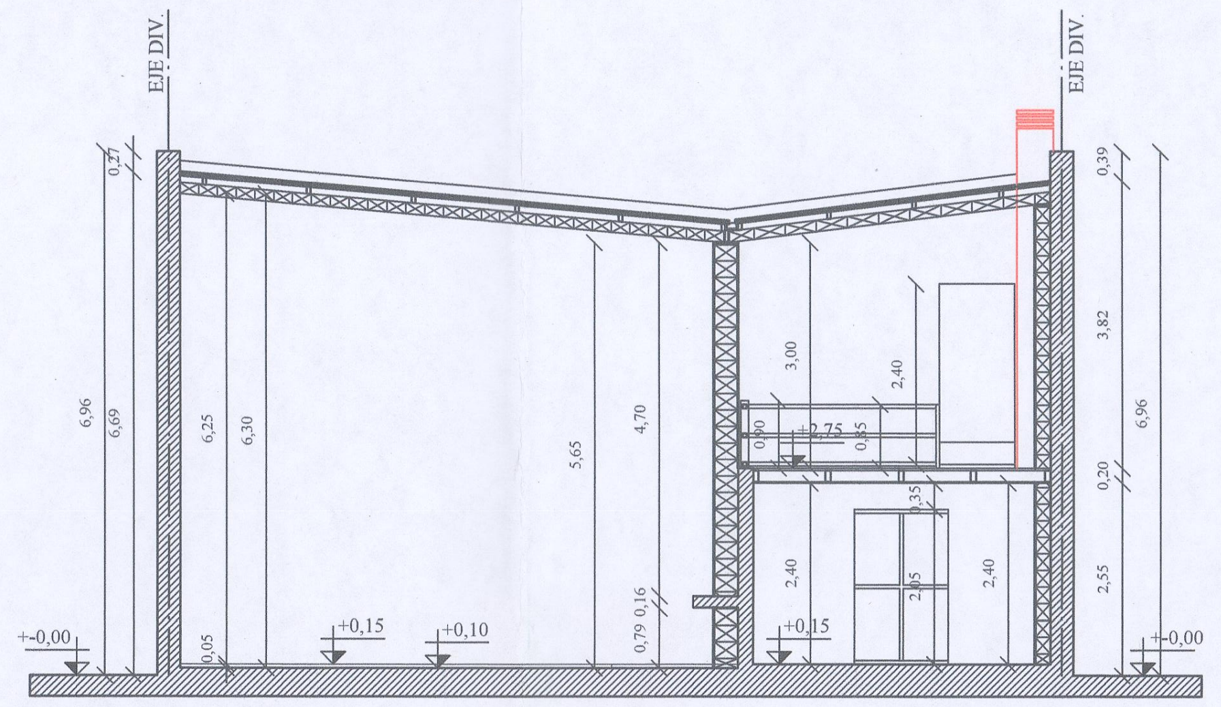

CORTE B-B

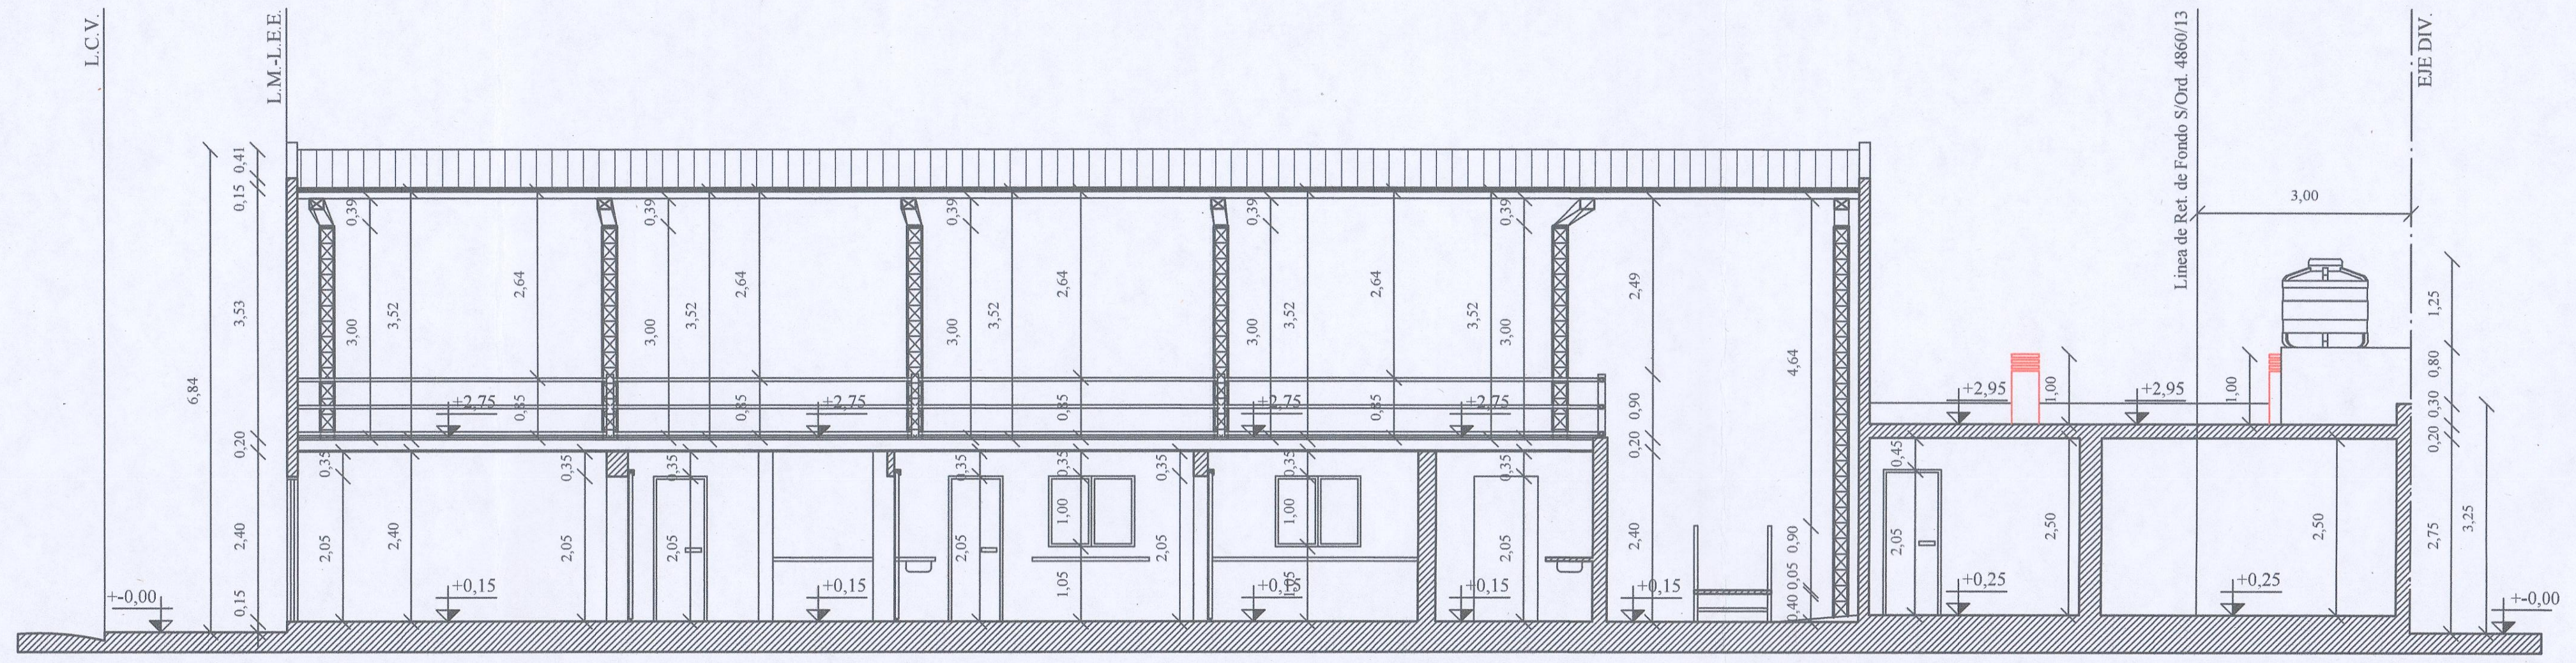

CORTE A-A

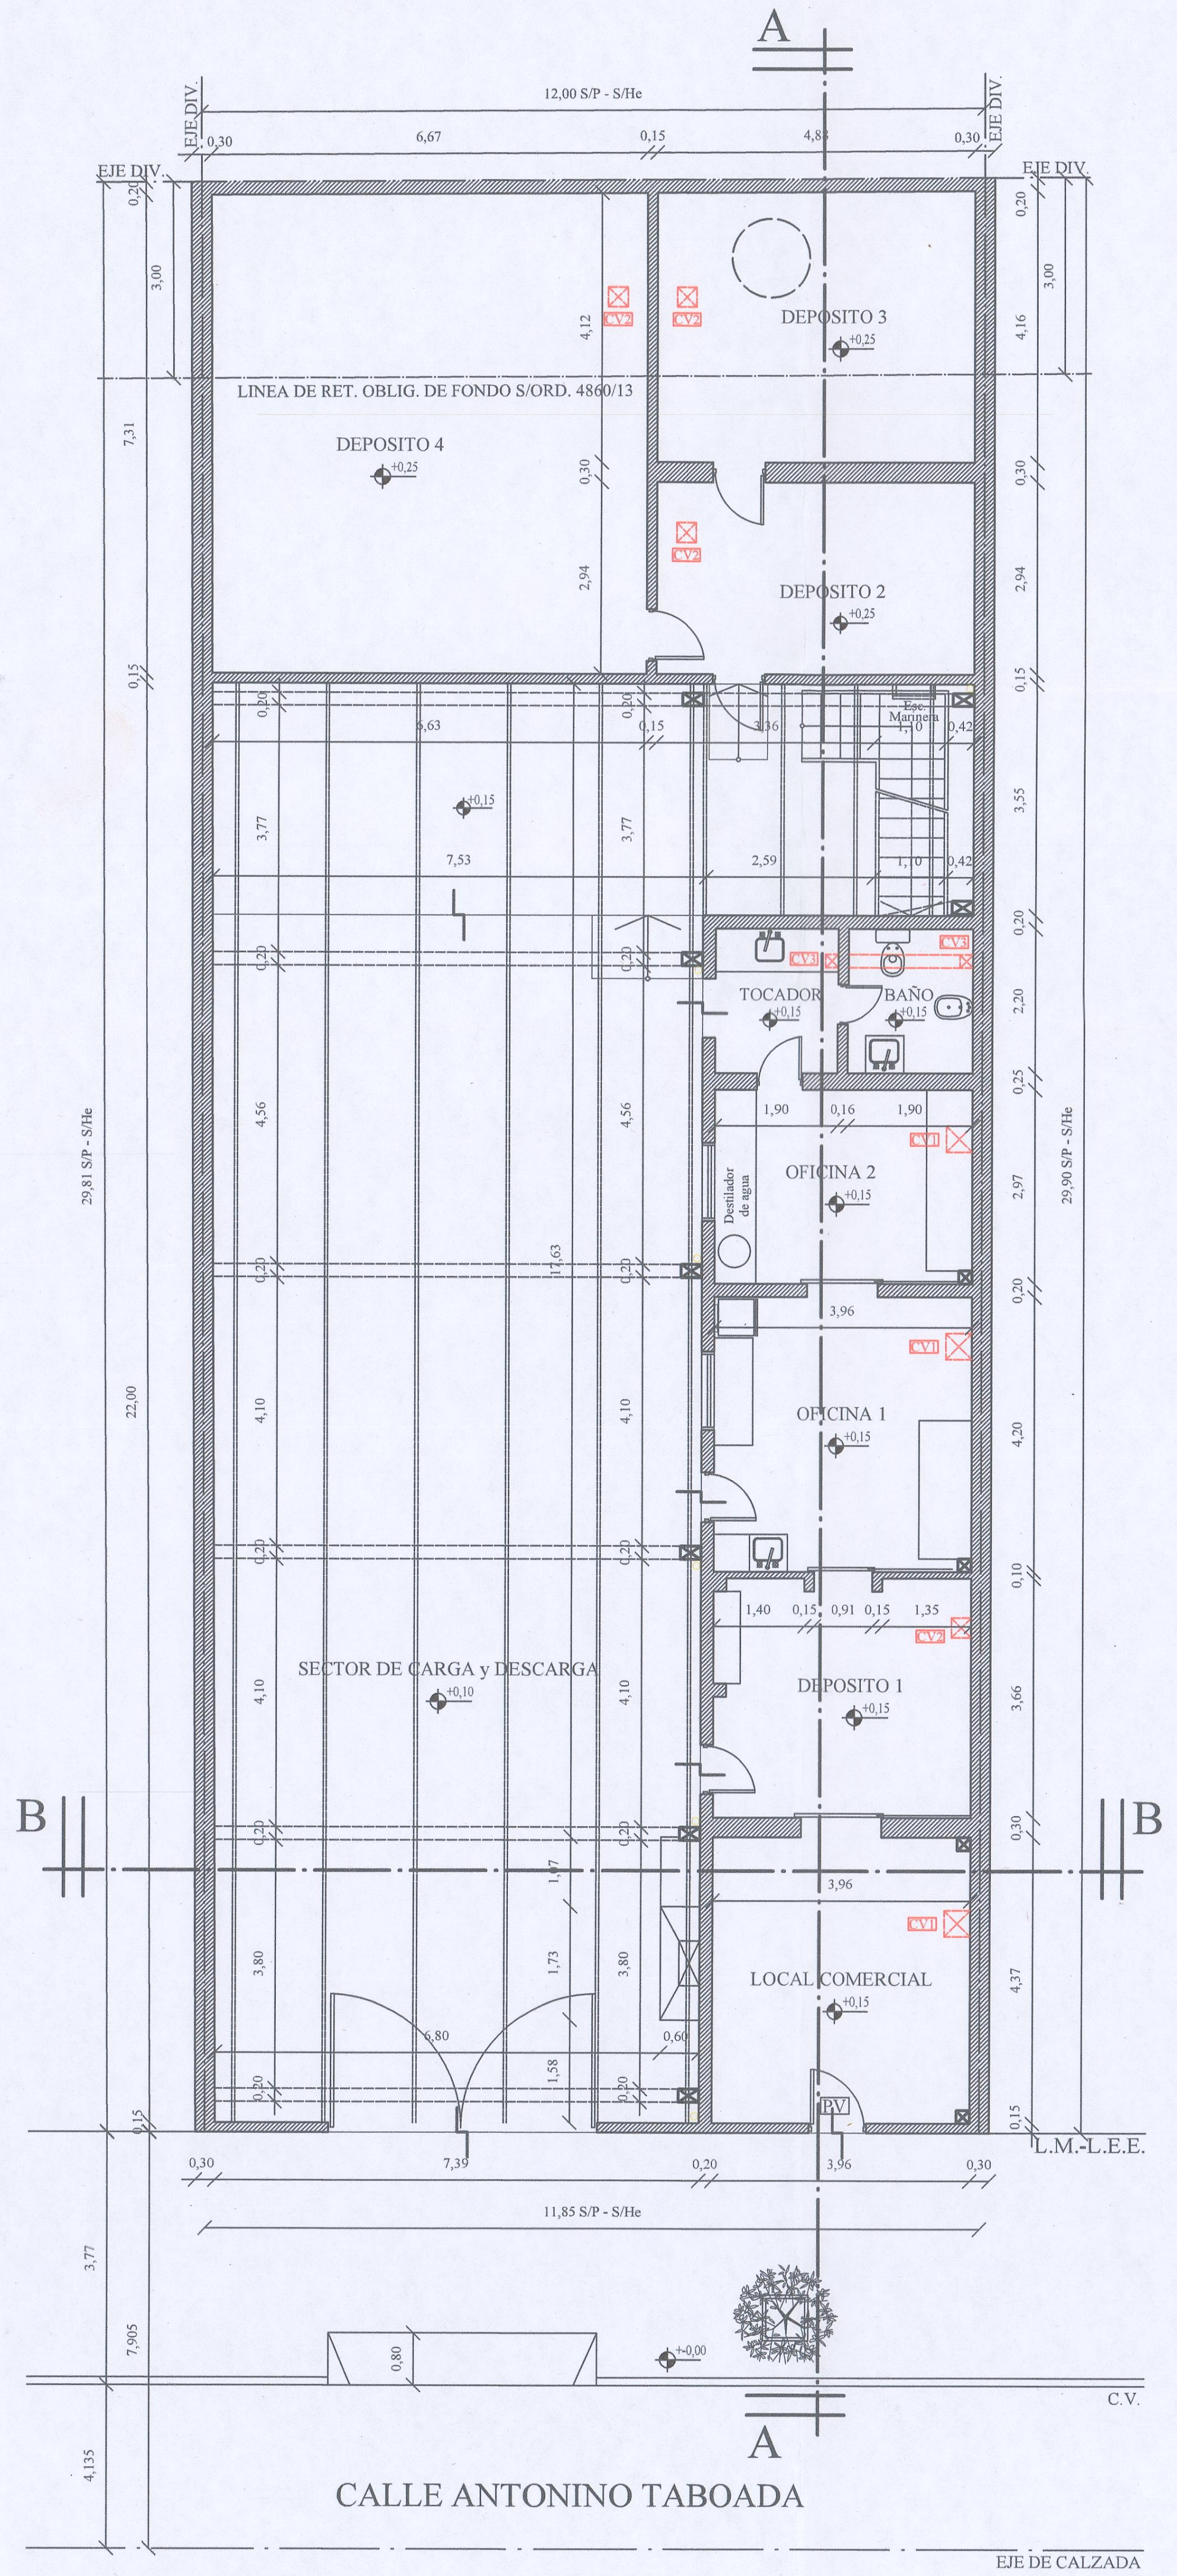

PLANTA BAJA

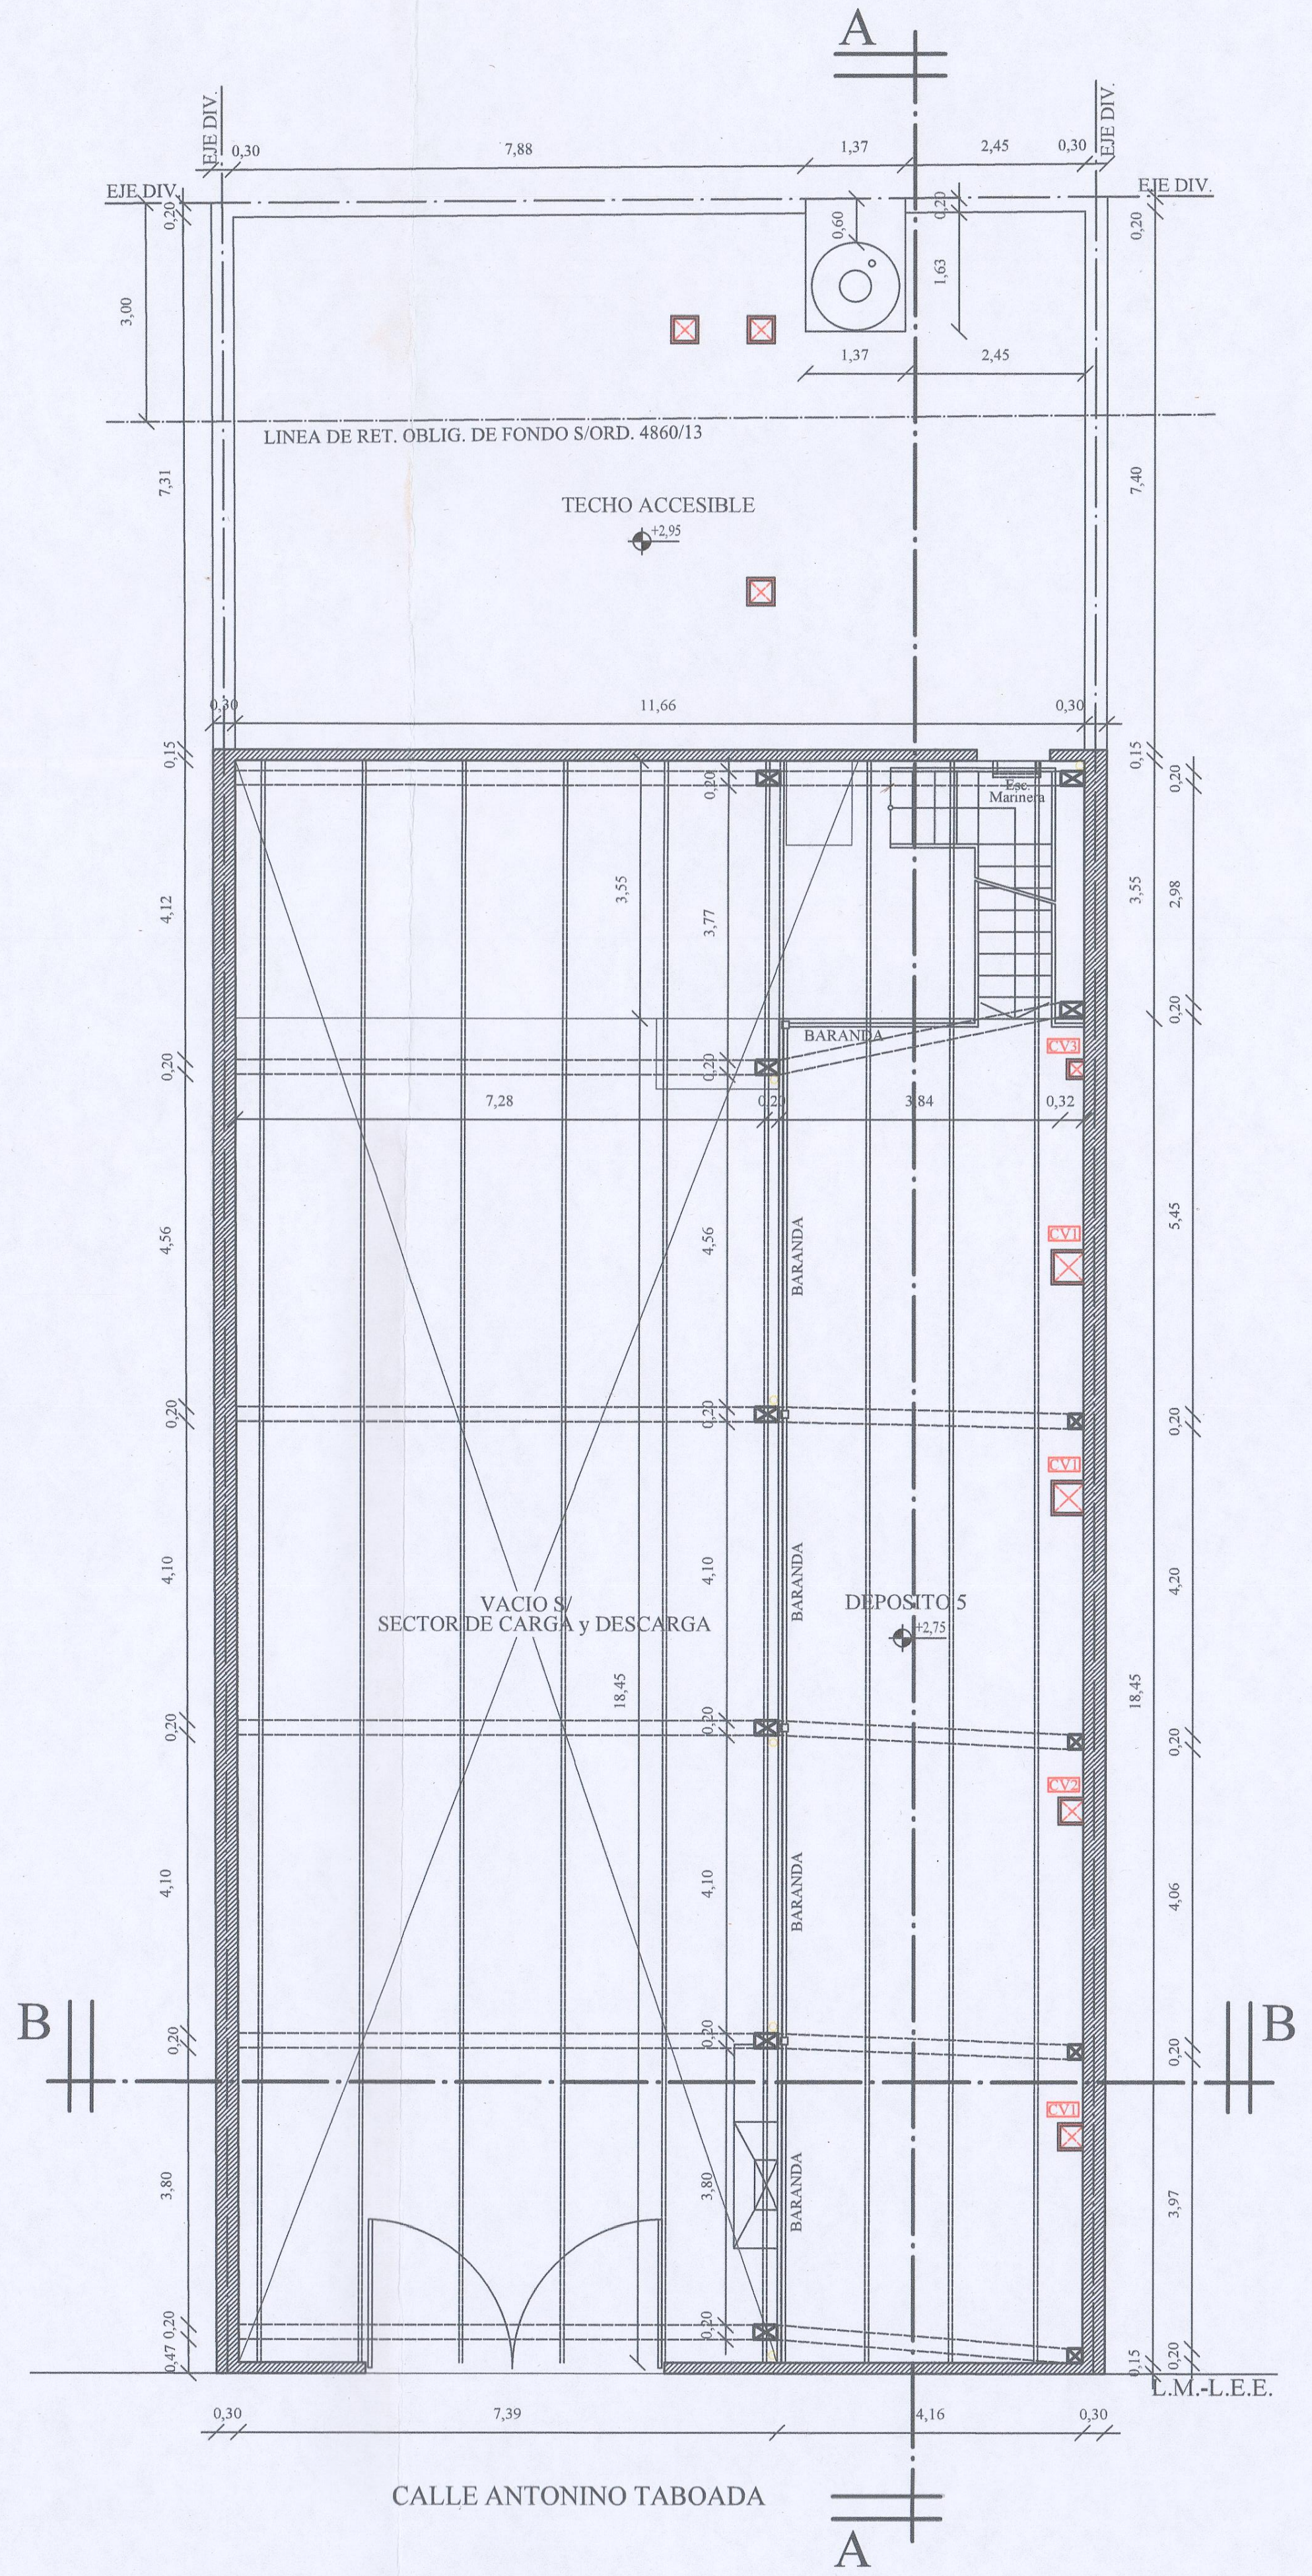
A
B
EJE DIV.
LINEA DE RET. OBLIG. DE FONDO S/ORD. 4860/13
TECHO ACCESIBLE
BARANDA
VACIO S/ SECTOR DE CARGA y DESCARGA
DEPOSITO 5
L.M.-L.E.E.
CALLE ANTONINO TABOADA

PLANTA DE ENTREPISO

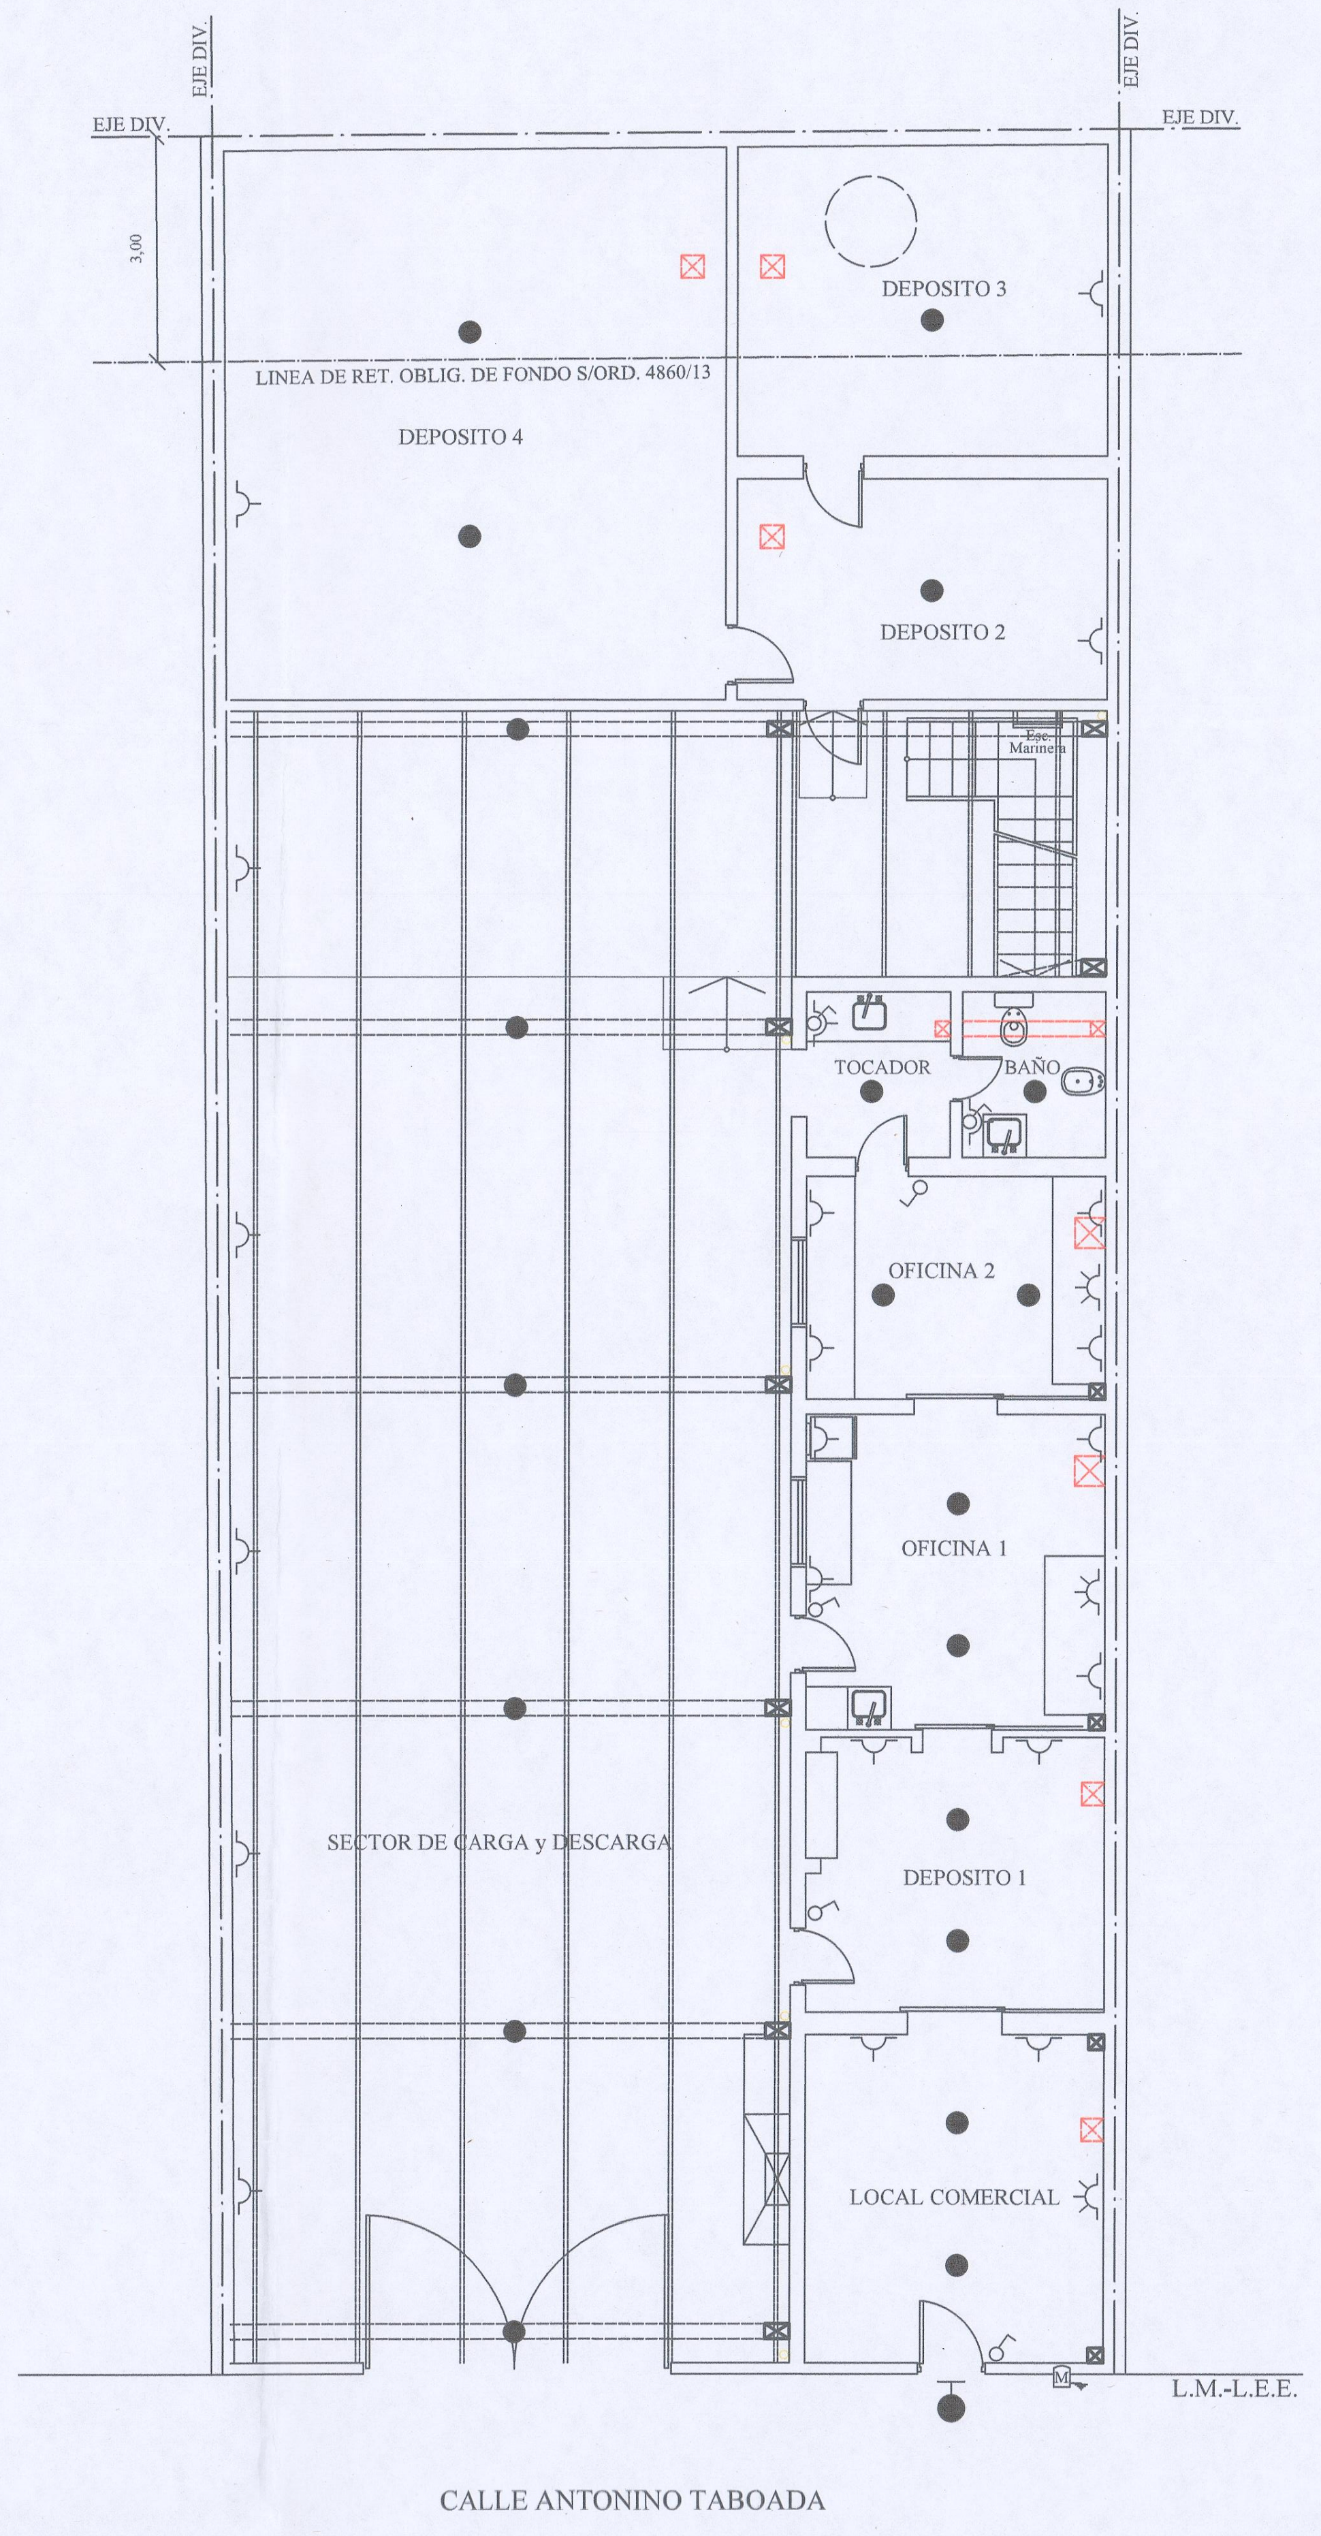

PLANTA BAJA DE ELECTRICIDAD

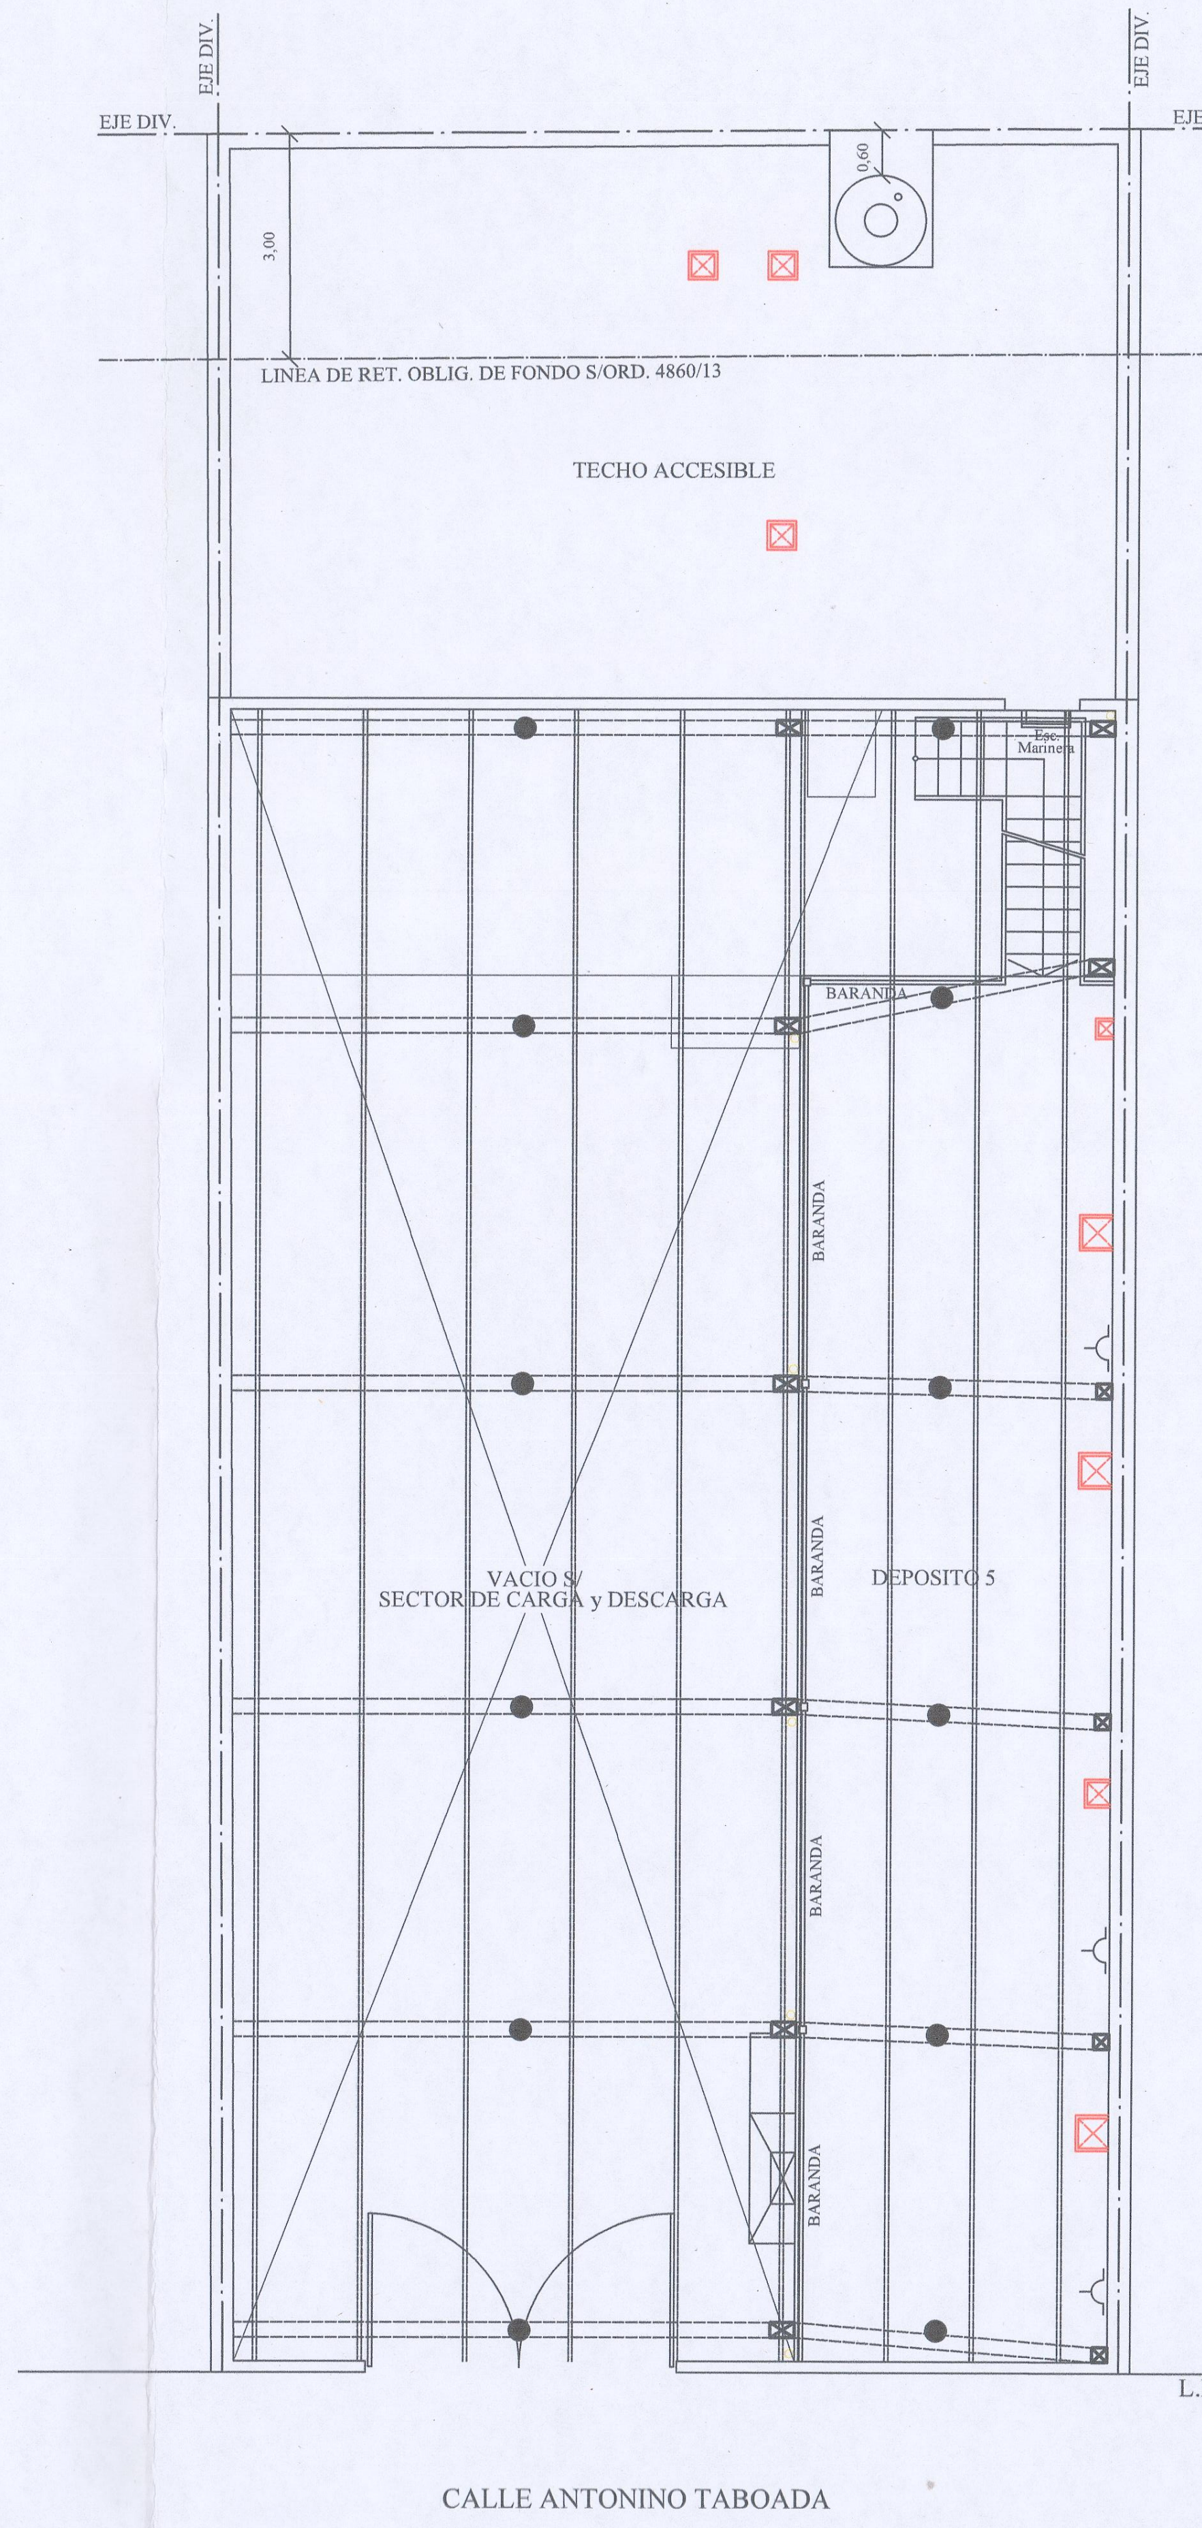
EJE DIV.
LINEA DE RET. OBLIG. DE FONDO S/ORD. 4860/13
TECHO ACCESIBLE
BARANDA
VACIO S/ SECTOR DE CARGA y DESCARGA
DEPOSITO 5
L.M.-L.E.E.
CALLE ANTONINO TABOADA

PLANTA ENTREPISO DE ELECTRICIDAD

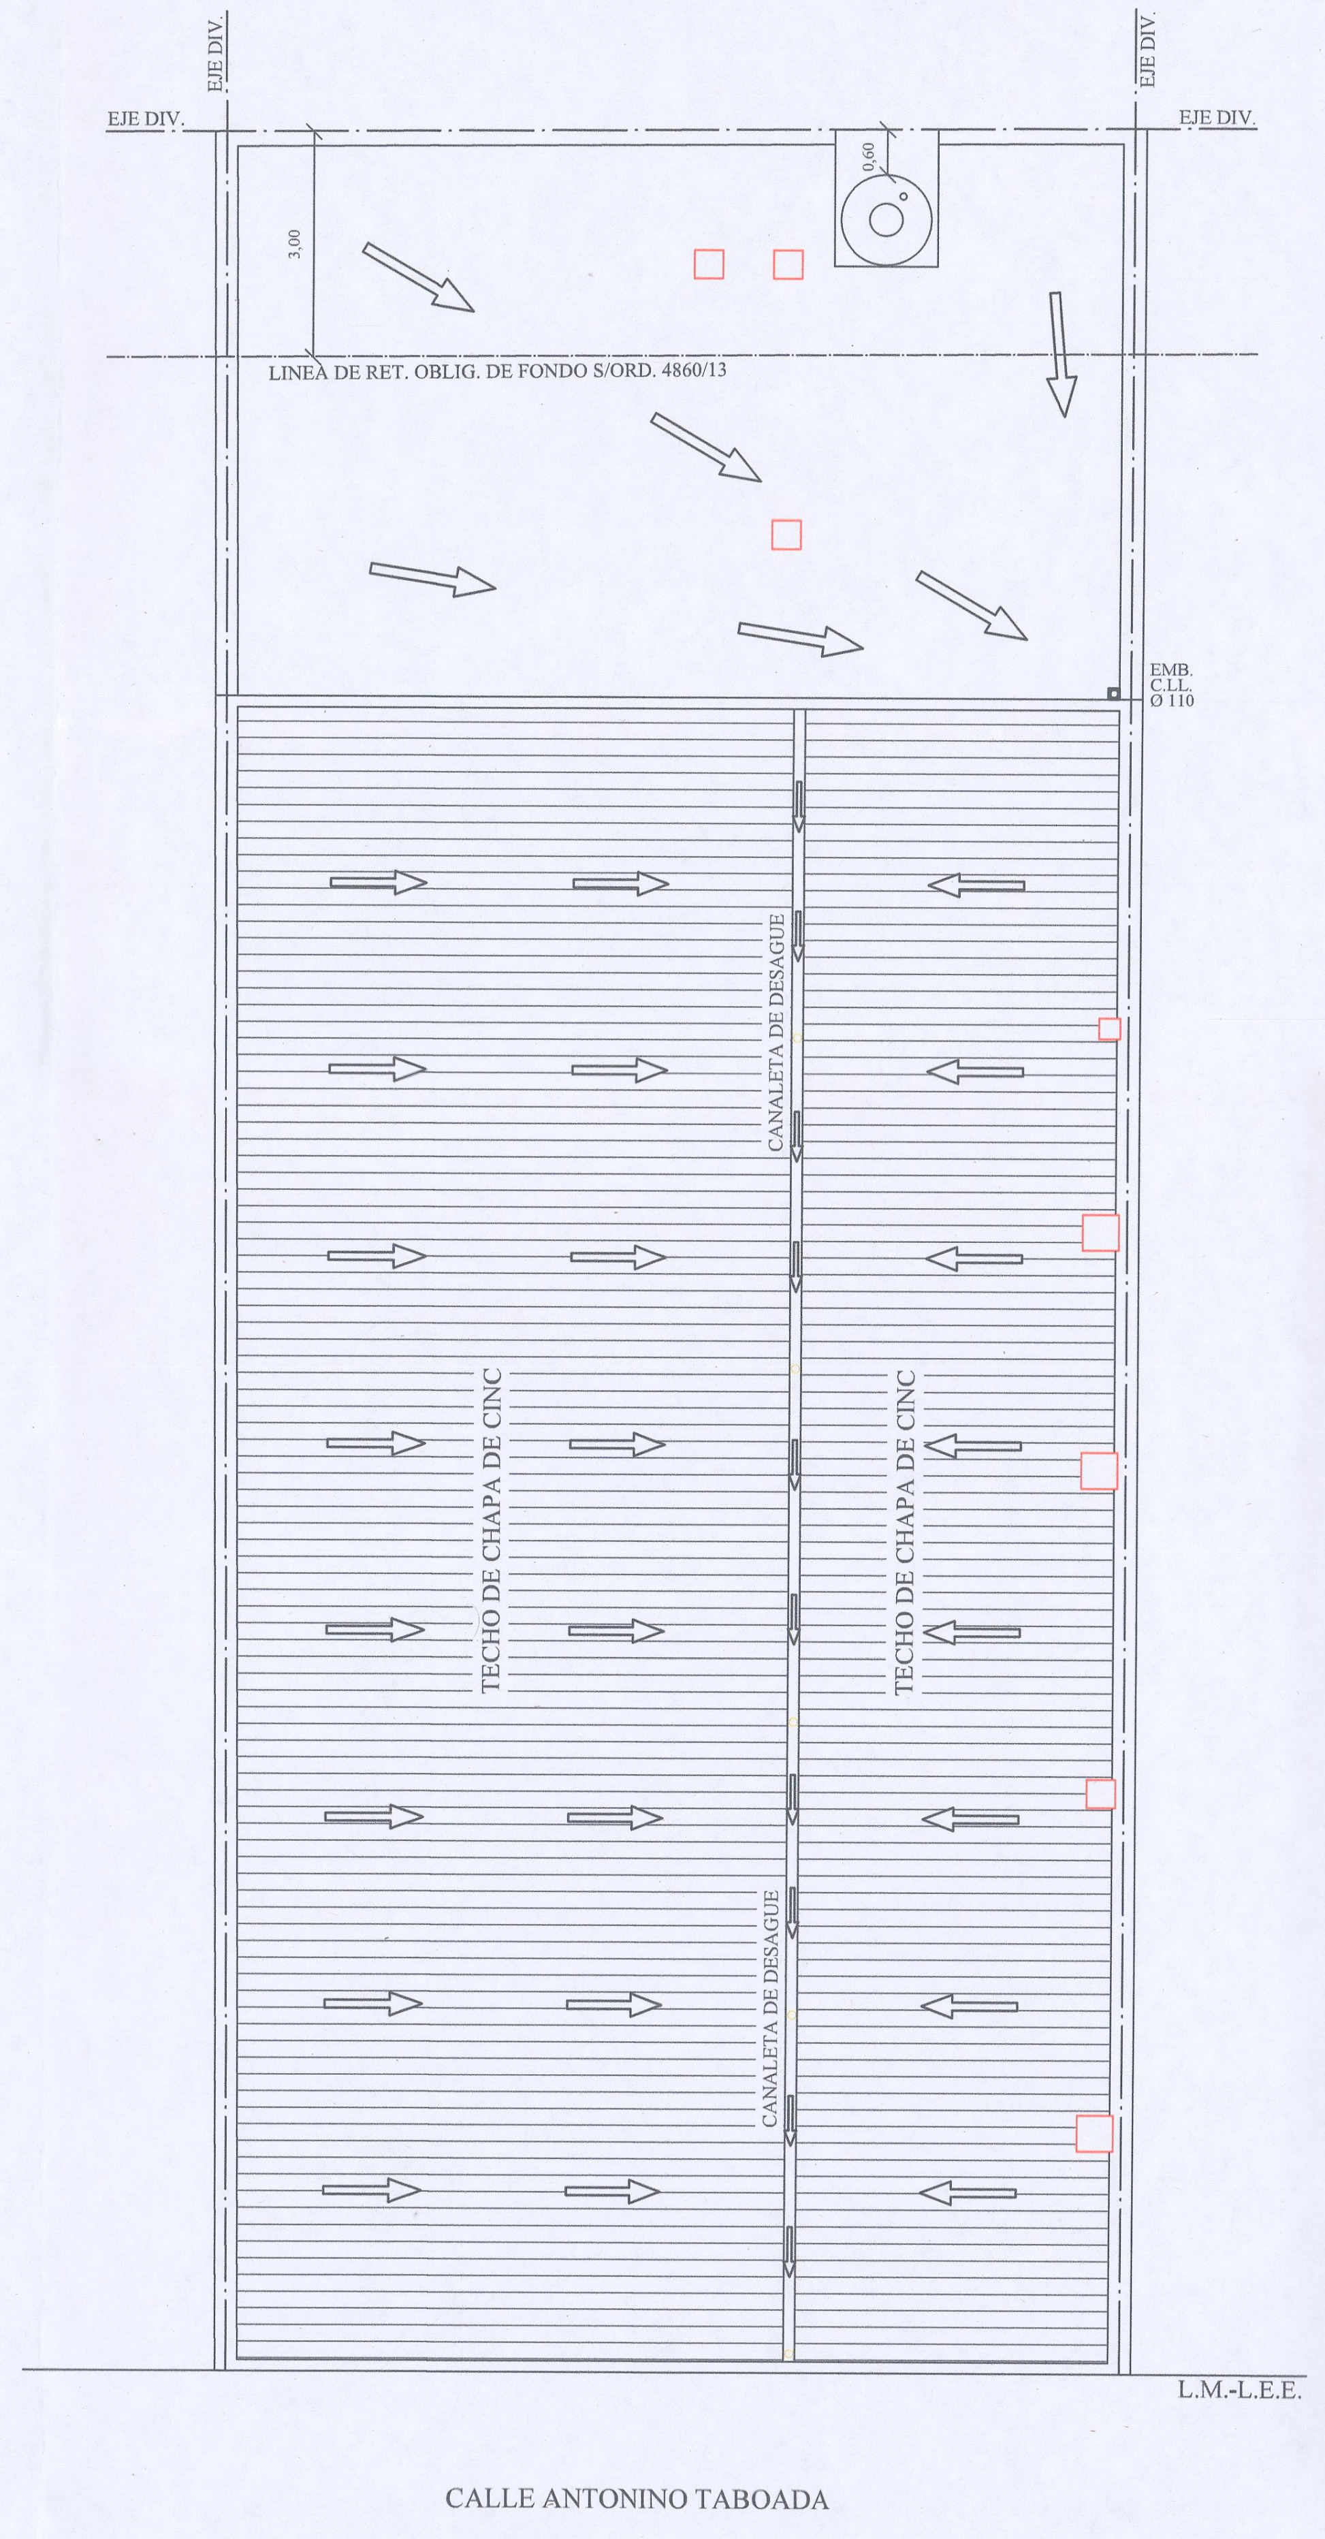

PLANTA DE TECHOS

PLANILLA DE ILUMINACION Y VENTILACION

LOCAL		ABERTURAS					OBSERVACIONES
DESIGNACION	SUPERFICIE	DESIG.	ANCHO	ALTO	AREAS I.	AREAS V.	
PLANTA BAJA							
LOCAL COMERCIAL	17,22	PV	0,90	2,05	1,84	1,84	Dos Puertas Ventanas
		CV1	0,40	0,40	......	0,16	Conducto de Ventilacion a Colocar
DEPOSITO 1	14,17	CV2	0,30	0,30	......	0,09	Conducto de Ventilacion a Colocar
OFICINA 1	16,59	CV1	0,40	0,40	......	0,16	Conducto de Ventilacion a Colocar
OFICINA 2	11,72	CV1	0,40	0,40	......	0,16	Conducto de Ventilacion a Colocar
TOCADOR	4,18	CV3	0,20	0,20	......	0,04	Conducto de Ventilacion a Colocar
BAÑO	4,18	CV3	0,20	0,20	......	0,04	Conducto de Ventilacion a Colocar
SECT. CARGA y DESC.	169,68	PM	4,10	3,20	......	13,12	Porton Metalico
		Vo	4,10	1,54	6,31	6,31	Vano
DEPOSITO 2	14,35	CV2	0,30	0,30	......	0,09	Conducto de Ventilacion a Colocar
DEPOSITO 3	20,19	CV2	0,30	0,30	......	0,09	Conducto de Ventilacion a Colocar
DEPOSITO 4	48,78	CV2	0,30	0,30	......	0,09	Conducto de Ventilacion a Colocar
PLANTA DE ENTREPISO							
DEPOSITO 5	73,29	Vo	4,10	1,54	6,31	6,31	Vano
		CV1	0,40	0,40	......	0,48	Tres Conductos de Vent. a Colocar
		CV2	0,30	0,30	......	0,09	Conducto de Ventilacion a Colocar
		CV3	0,20	0,20	......	0,04	Conducto de Ventilacion a Colocar

PLANIMETRIA
ESCALA 1:200

REFERENCIAS ELÉCTRICAS	
Ⓜ	MEDIDOR Y TOMA A TIERRA
⊠	TABLERO PRINCIPAL
◩	TABLERO SECCIONAL
● ◉	BOCA DE UNO Y DOS EFECTOS
●⊣	BOCA DE PARED
⌒	TOMA CORRIENTE
⌖	CAJA DE DISTRIBUCIÓN
⚲	LLAVES, UNO,DOS y TRES PUNTOS
⌒	LINEA GENERAL
⌒	CIRCUITO DE AIRE ACONDICIONADO
♂	CAÑO DE SUBIDA Y ENTRADA DE ENERGIA
⊓	LLAVE DE COMBINACION SIMPLE

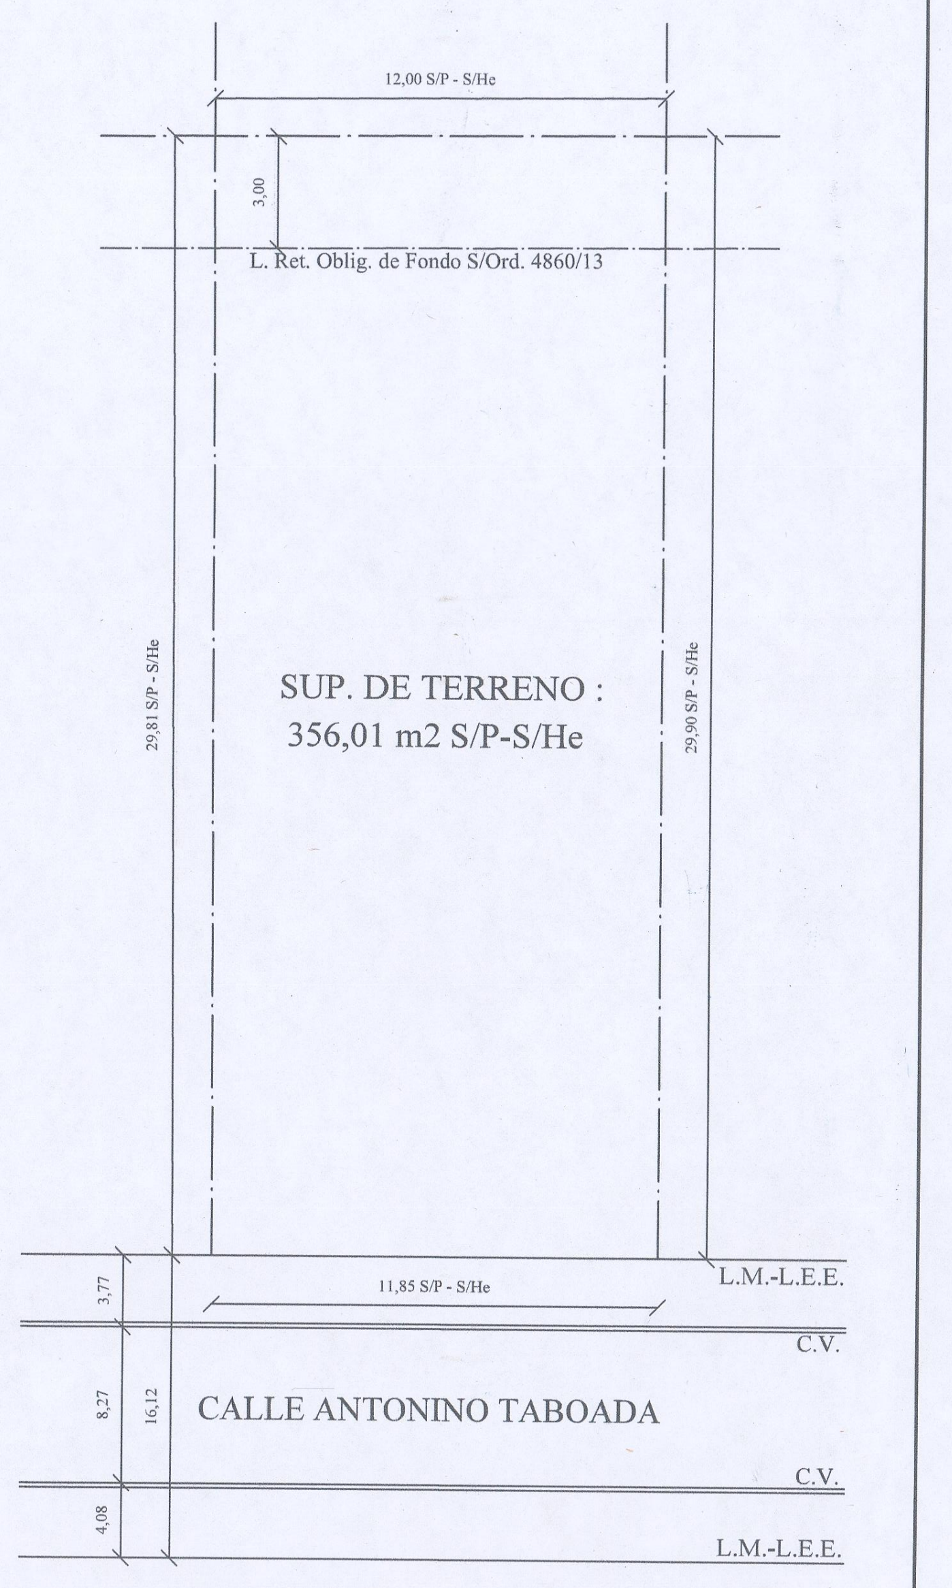

DIST. : 03 ZONA : 03 MANZ. : 02 PARC. : 100
PADRON INMOB. : 01-01-111798 / 01-01-111799 I.C.M. : 220-B-2024 DOMINIO : 7N-7995/A / 7N-7995/B

LEY 4683
VISADO ELECTRONICO
C.P.I.A. - O.T. Nº 1641910

DIRECCION DE SUELO URBANO
EXPEDIENTE 818 31 24
FECHA DE SELLADO 17 DIC. 2024
BOLETA Nº 3474

DEST. DE LA OBRA : OFICINA - DEPOSITO
PROPIETARIO : BERNARDO BAUTISTA BAILON (U.F. "A" y "B")
D.N.I. Nº 34.693.069 - C.U.I.L./T. 20-34693069-2
UBICACION : CALLE ANTONINO TABOADA Nº 448 / 452
BARRIO : Dr. JUAN BAUTISTA ALBERDI
CIUDAD : CAPITAL - SANTIAGO DEL ESTERO
ESCALA : 1 : 100 - 1 : 250

SUP. DE TERRENO : 356,01 m2 S/P-S/He
SUP. CUBIERTA PLANTA BAJA : 356,01 m2
SUP. CUBIERTA ENTREPISO : 80,16 m2
SUP. CUBIERTA TOTAL : 436,17 m2

CROQUIS DE UBICACION

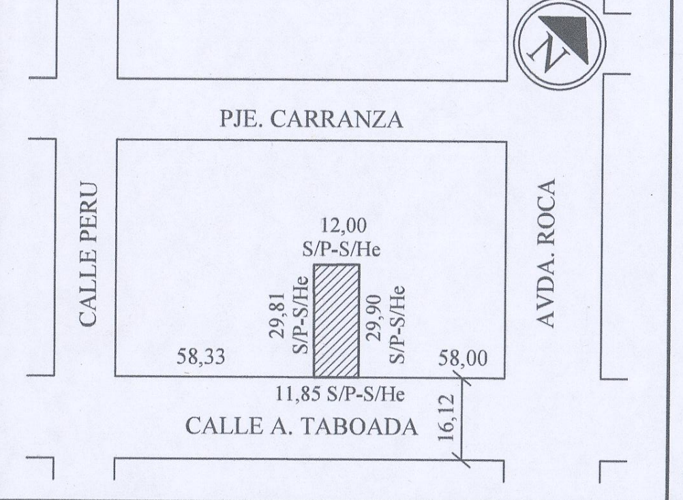

PROPIETARIO :
DOMICILIO :

RELEVAMIENTO :
AGUSTIN BAILON
INGENIERO CIVIL
M.P. Nº 3579
DOMICILIO :

ELECTRICIDAD :
DOMICILIO :

EL USO Y/O DESTINO DE LOS LOCALES
ESTA SUJETO A LAS DISPOSICIONES DE
LA ORDENANZA Nº 796/82 CAPITULO 3.

DIRECCION DE SUELO URBANO
EXPEDIENTE 818 31 24
FECHA DE SELLADO 31 ENE. 2025
BOLETA Nº 3677

CATEG. DEL CONSEJO DE INGENIEROS : "A"

ANCHO DE CALLE : 16,12 m
ANCHO DE VEREDA : 3,77 m
ANCHO DE CALZADA : 8,27 m

PAVIMENTO : SI
SERVICIOS CLOACALES : SI

DIREC. DE SUELO URBANO

DESIGNACION : PLANO DE RELEVAMIENTO

OBSERVACIONES :

15 ENE. 2025
Las referencias al Titulo de dominio son meramente indicativas, y la aprobación administrativa no valora los derechos que de ellos emergen.

MUNICIPALIDAD DE LA CIUDAD DE SANTIAGO DEL ESTERO
SECRETARIA DE ECONOMIA
APROBADO
DIRECCIÓN DE SUELO URBANO
EXPEDIENTE: 818-31-2024 - Corp. 12-B-2024
FECHA: 28 MAR 2025

Ing. Agrim. LEANDRO ARJONA
JEFE DE AREA DE VISACIONES TECNICAS
DIRECCION DE CATASTRO MUNICIPAL

Arq. ABRAHAM BERNARDO ROMINA
Dpto. OBRAS PRIVADAS
DIRECCION DE SUELO URBANO

Arq. ESTER R. CHALOM
SUB-DIRECTORA
DIRECCION DE SUELO URBANO