




ESQUEMA DE PILOTES

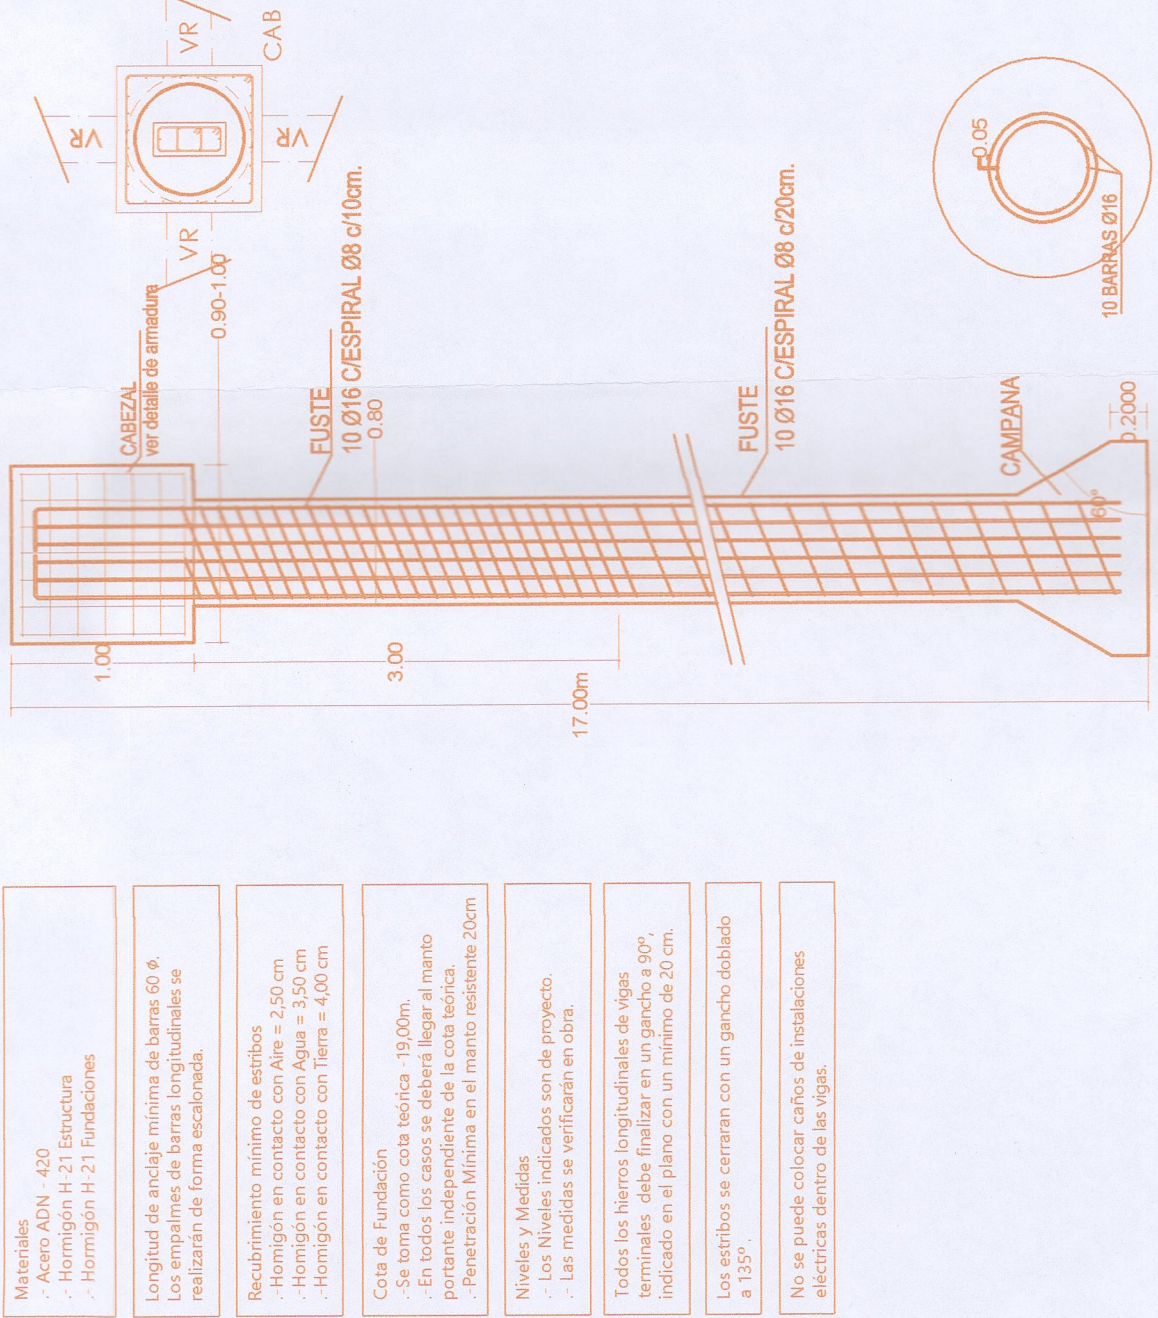


Esquema armado riostras

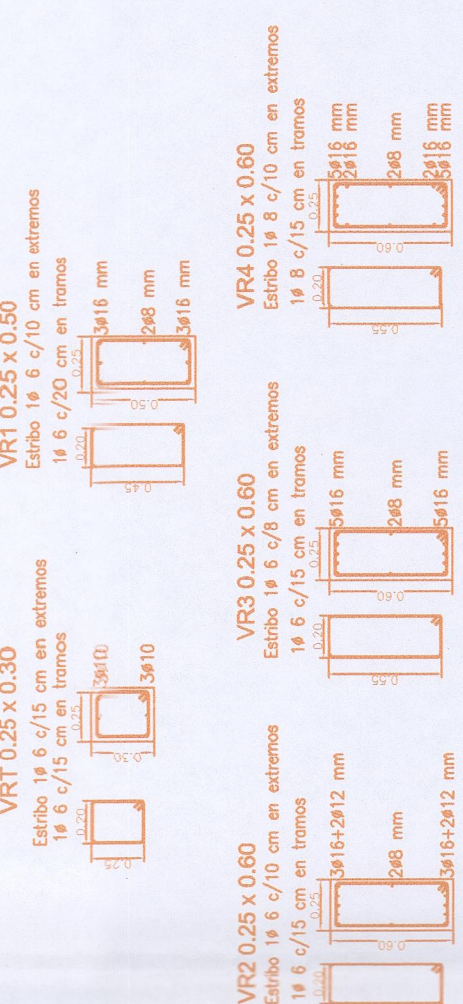


Longitudes de Anclaje y Empalme

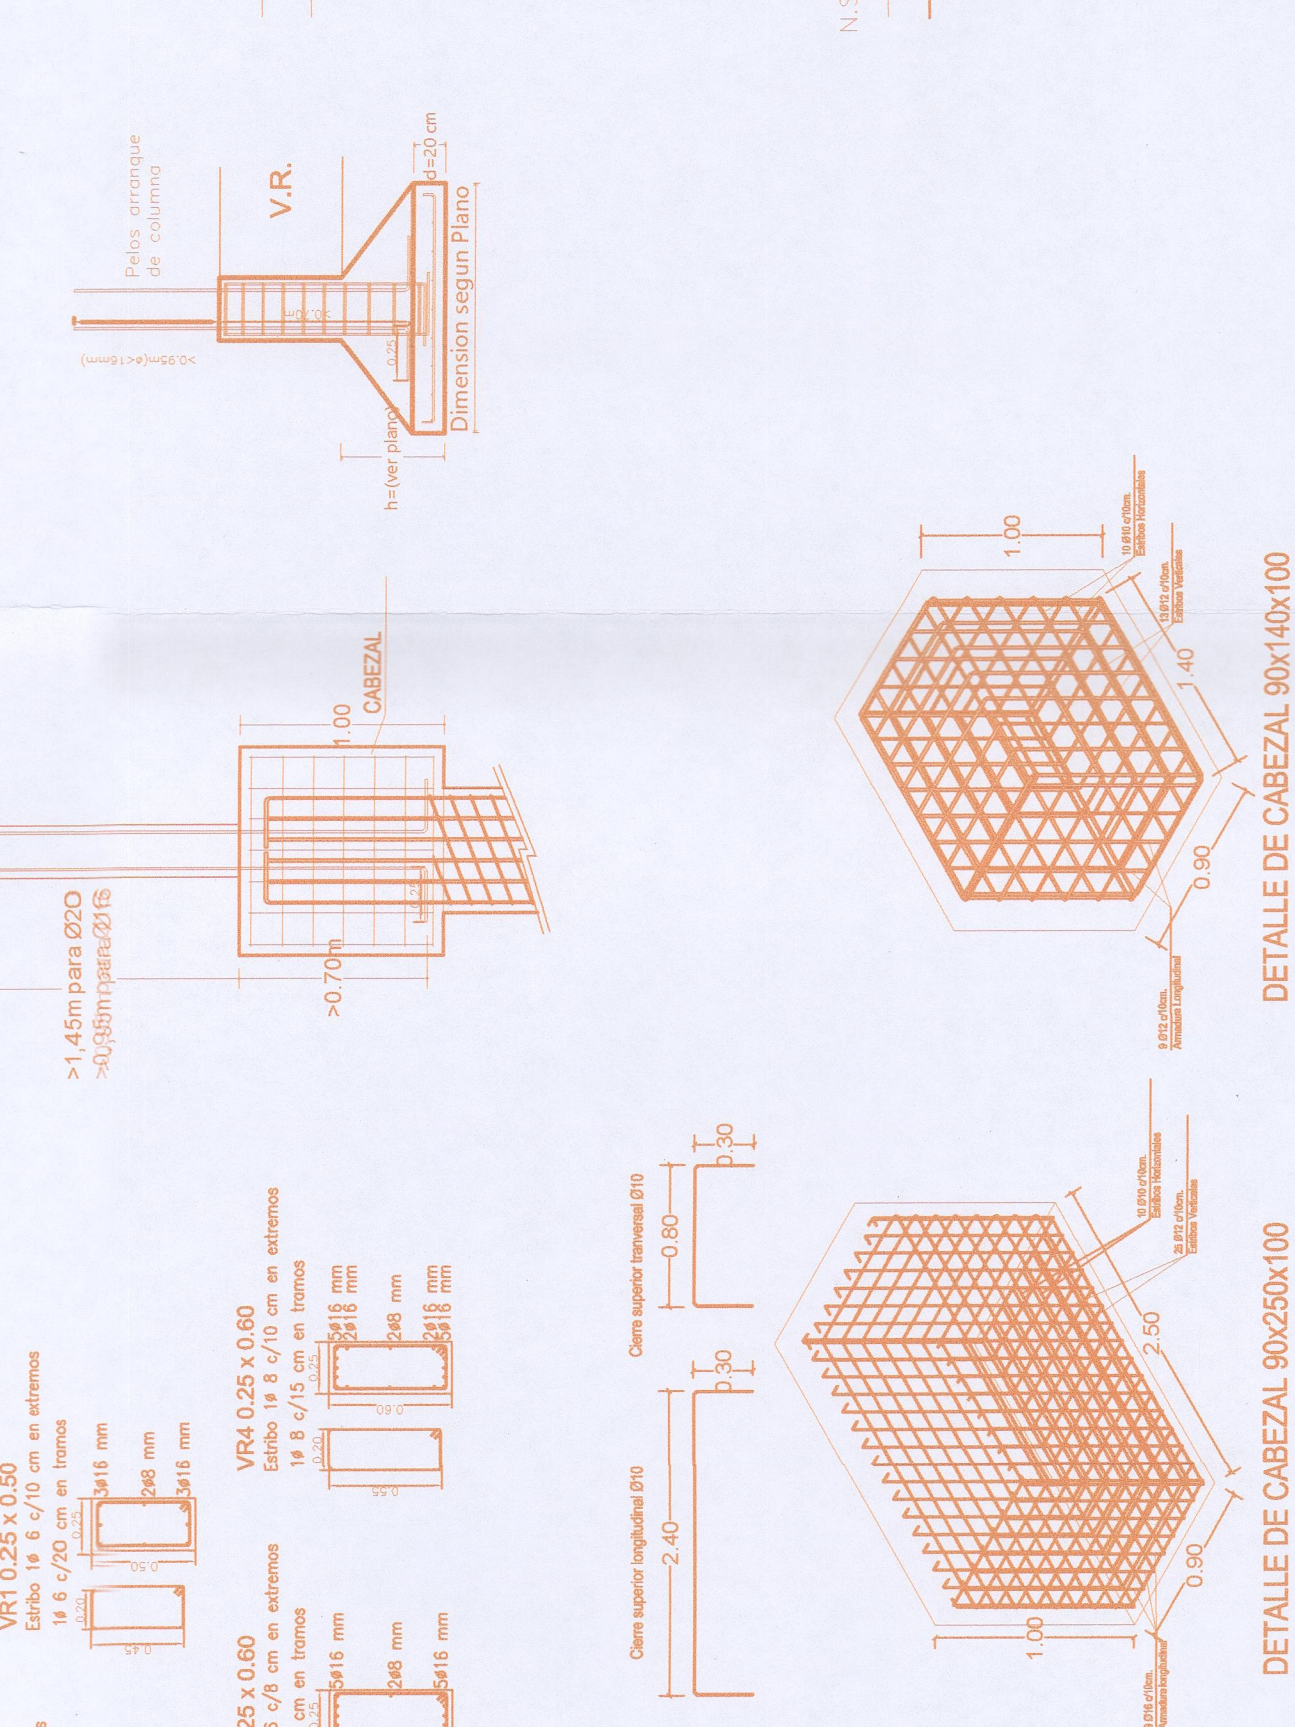

PLANTA DE FUNDACION
Sobre SUELO
Escala: 1:100

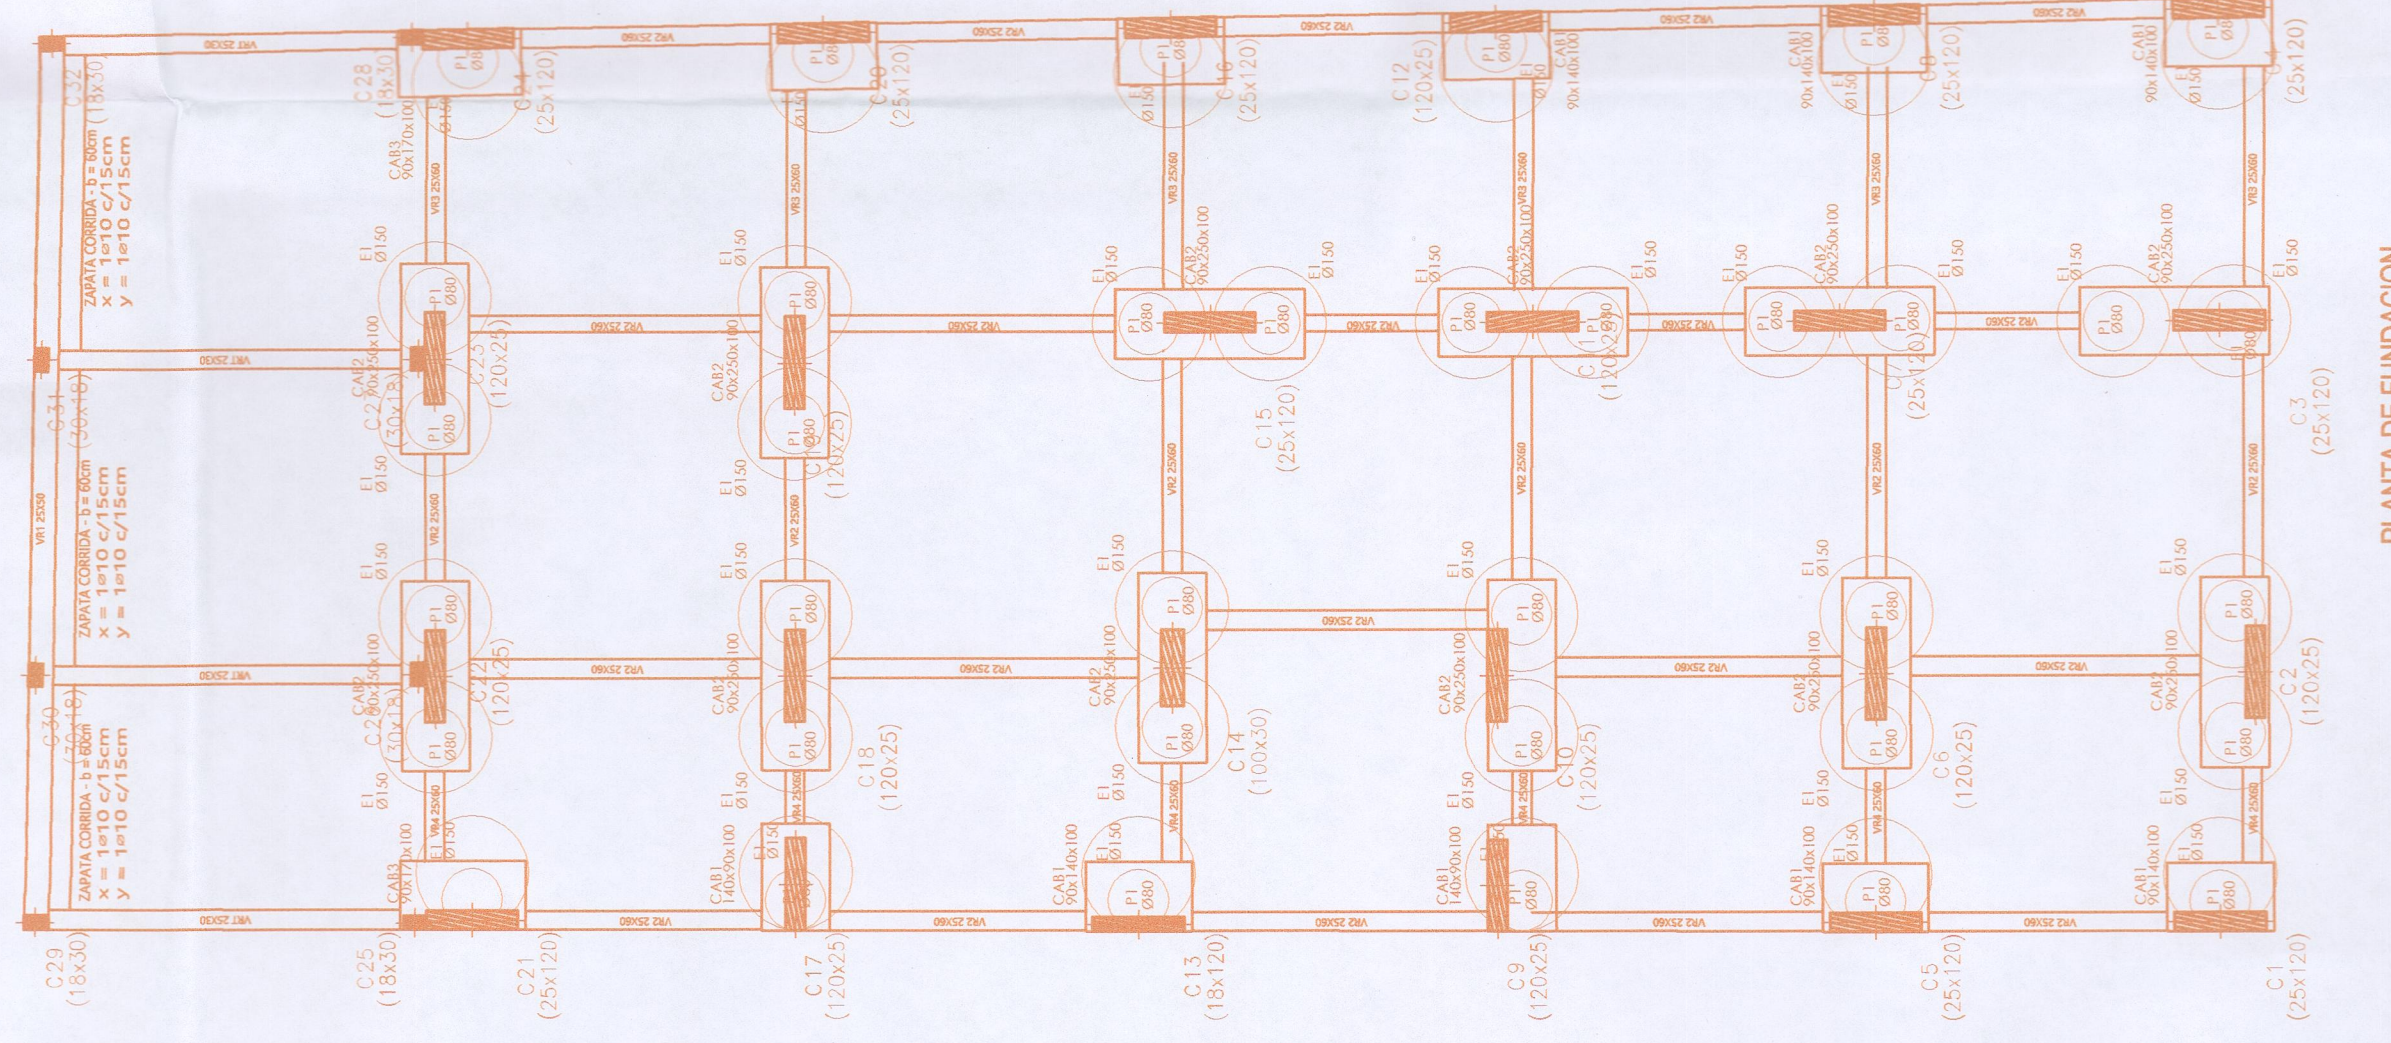


PLANTA DE FUNDACION
Sobre SUELO
Escala: 1:100

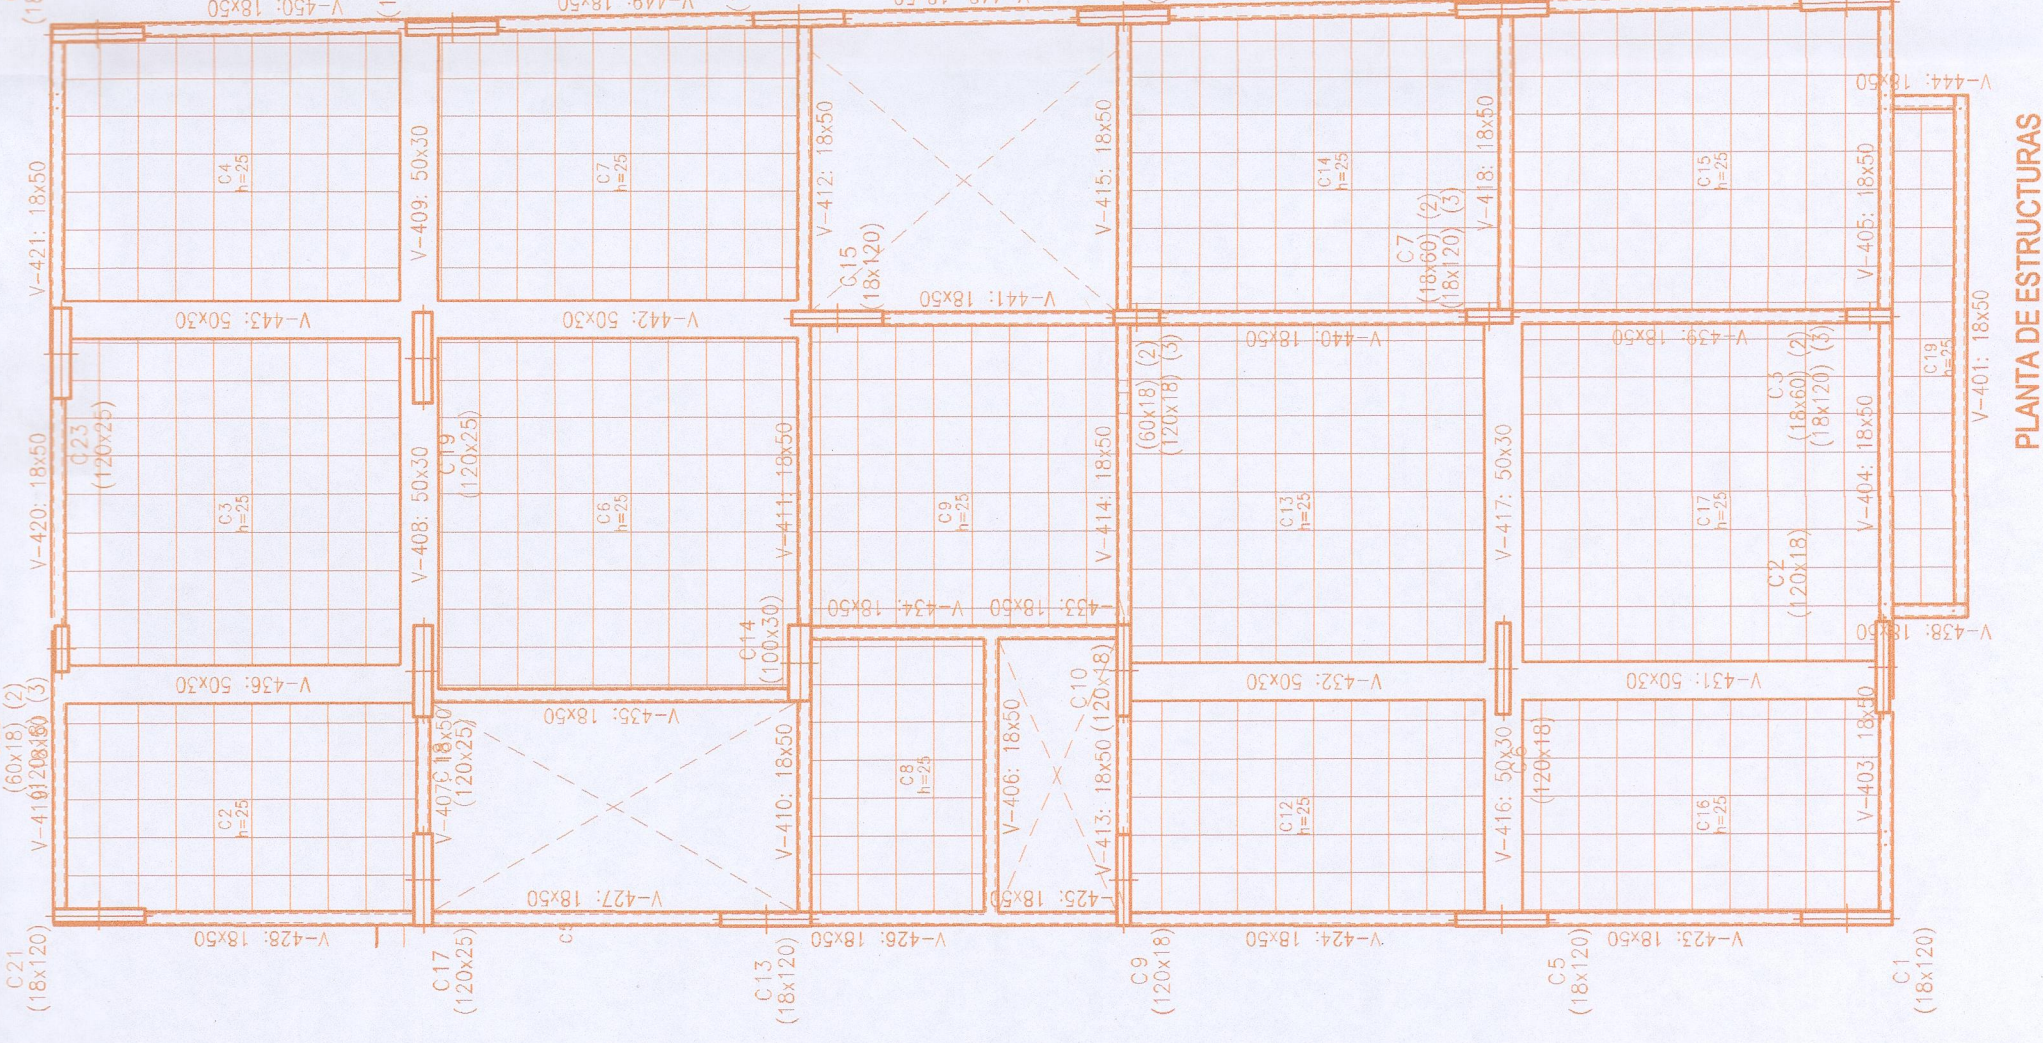


PLANTA DE ESTRUCTURAS
Sobre PISO 0

PLANTA DE ESTRUCTURAS
Sobre PISO 1

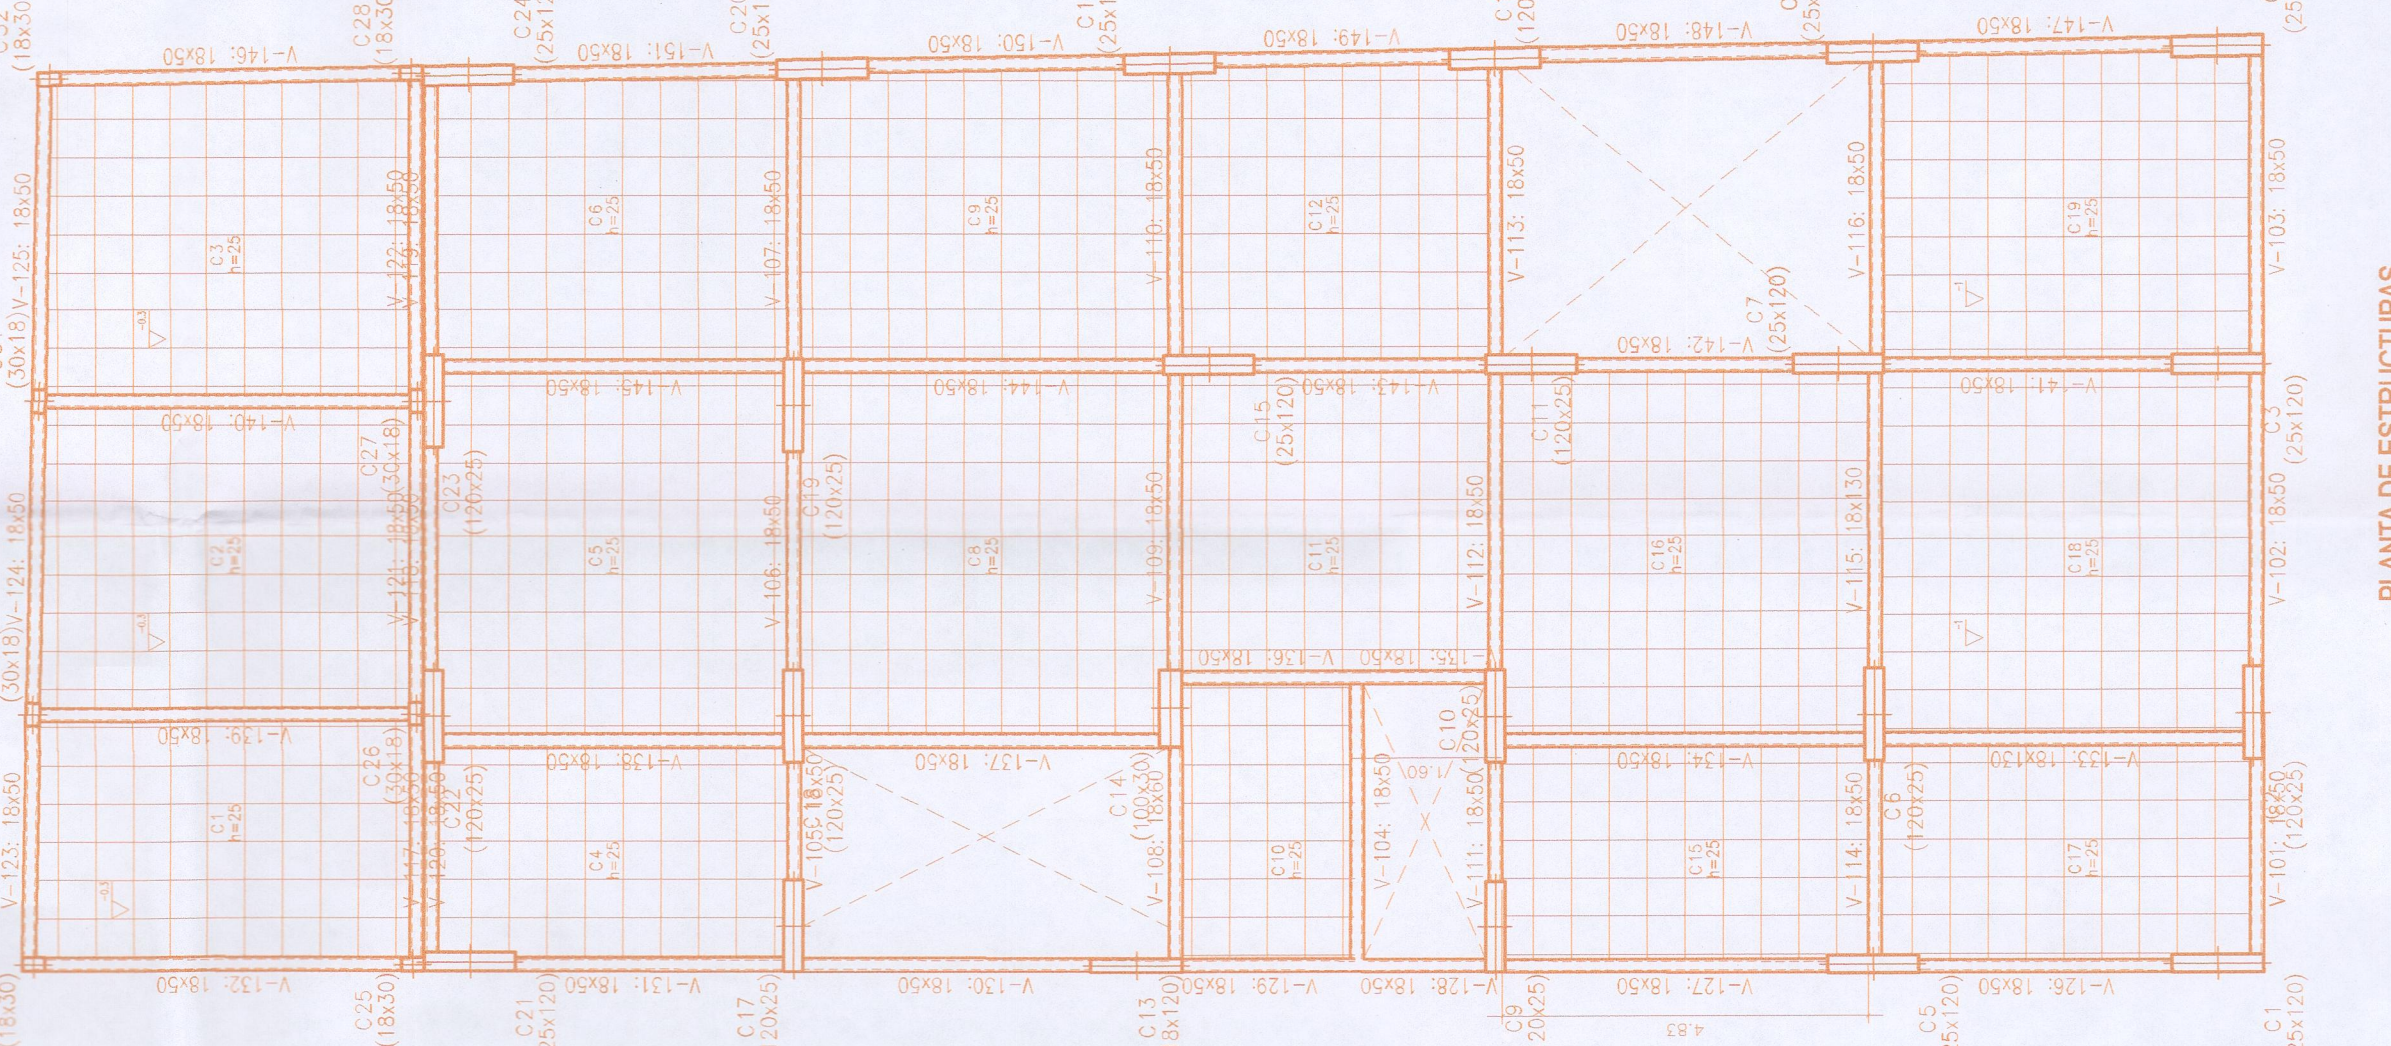


PLANTA DE ESTRUCTURAS
Sobre PISO 2

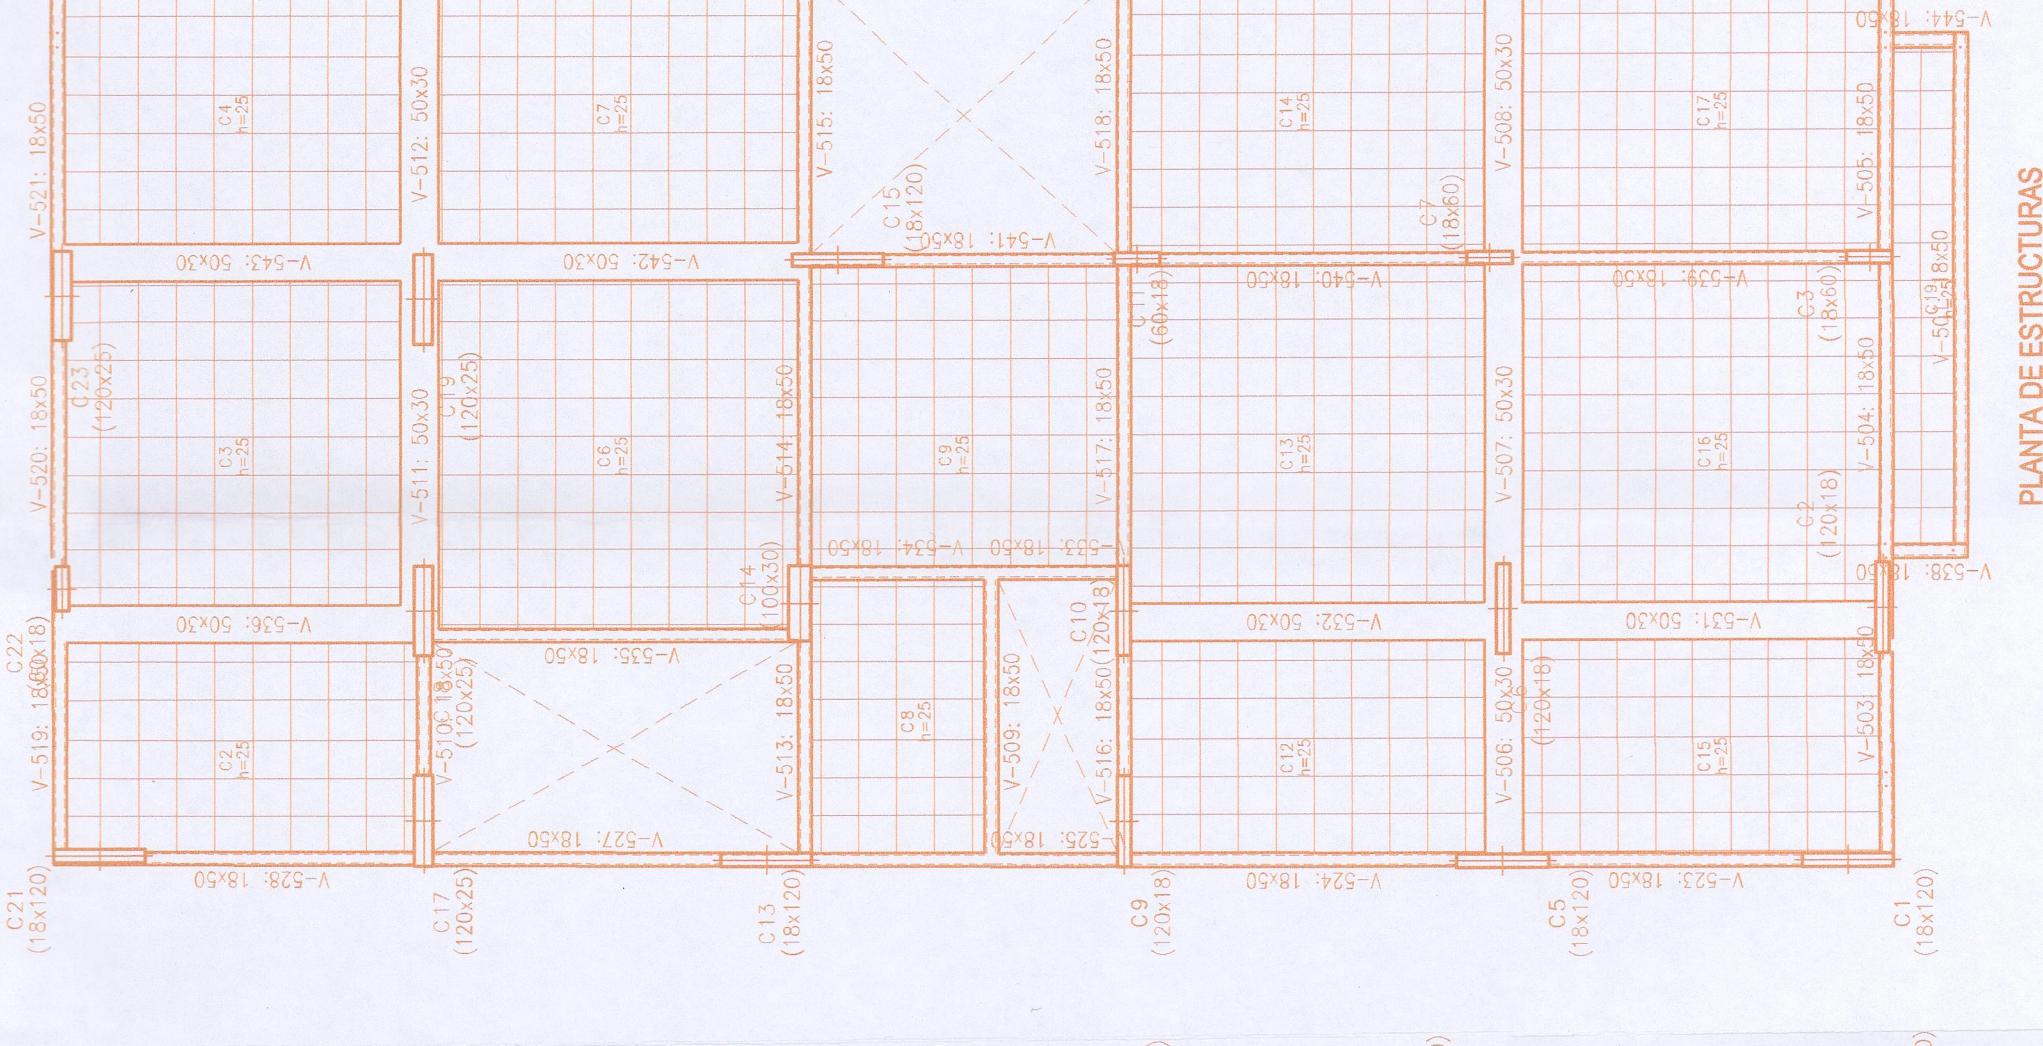


PLANTA DE ESTRUCTURAS
Sobre PISO 3

PLANTA DE ESTRUCTURAS
Sobre PISO 4

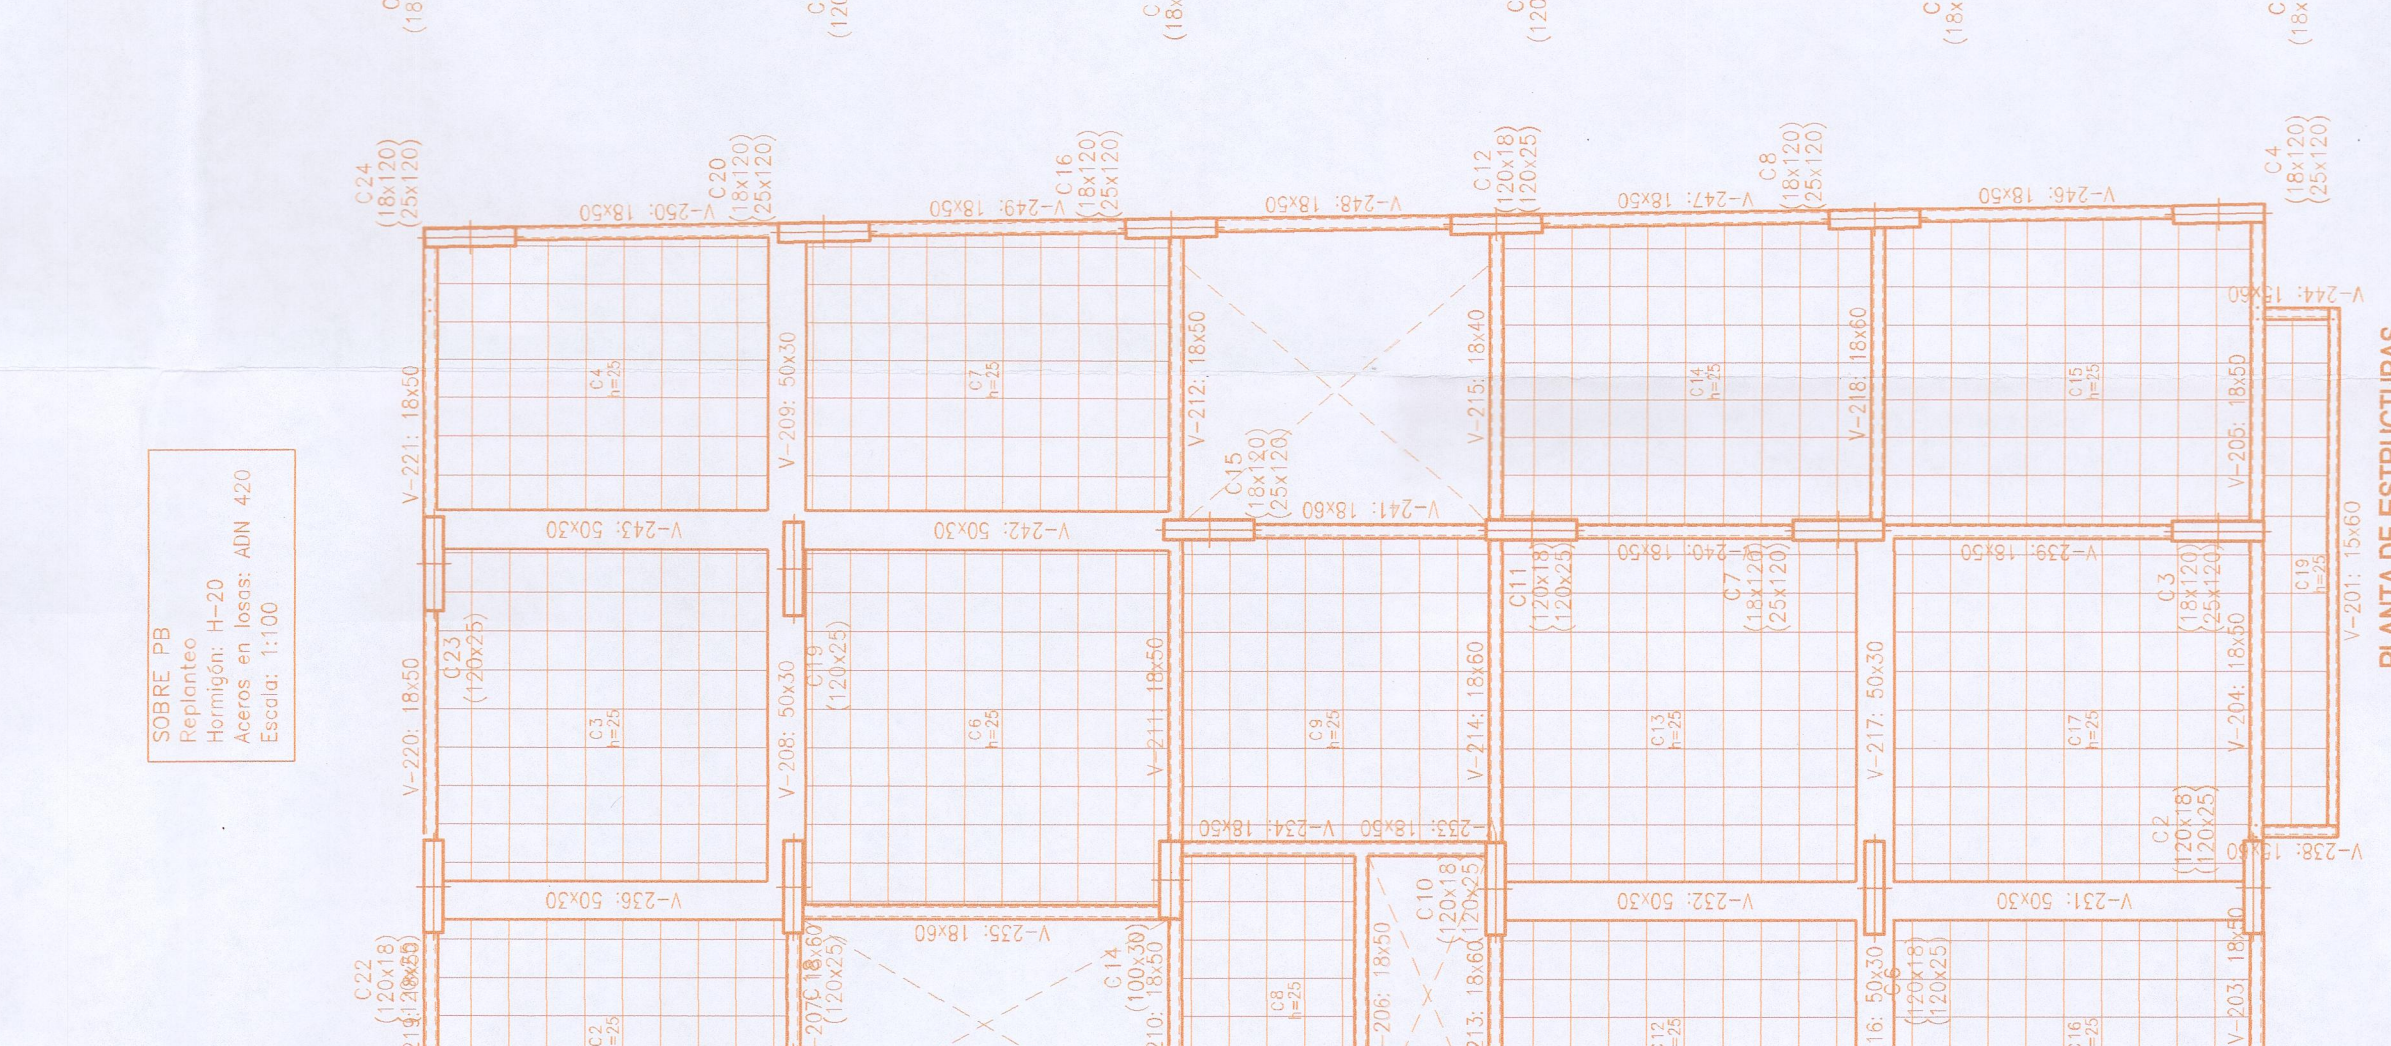


PLANTA DE ESTRUCTURAS
Sobre PISO 5

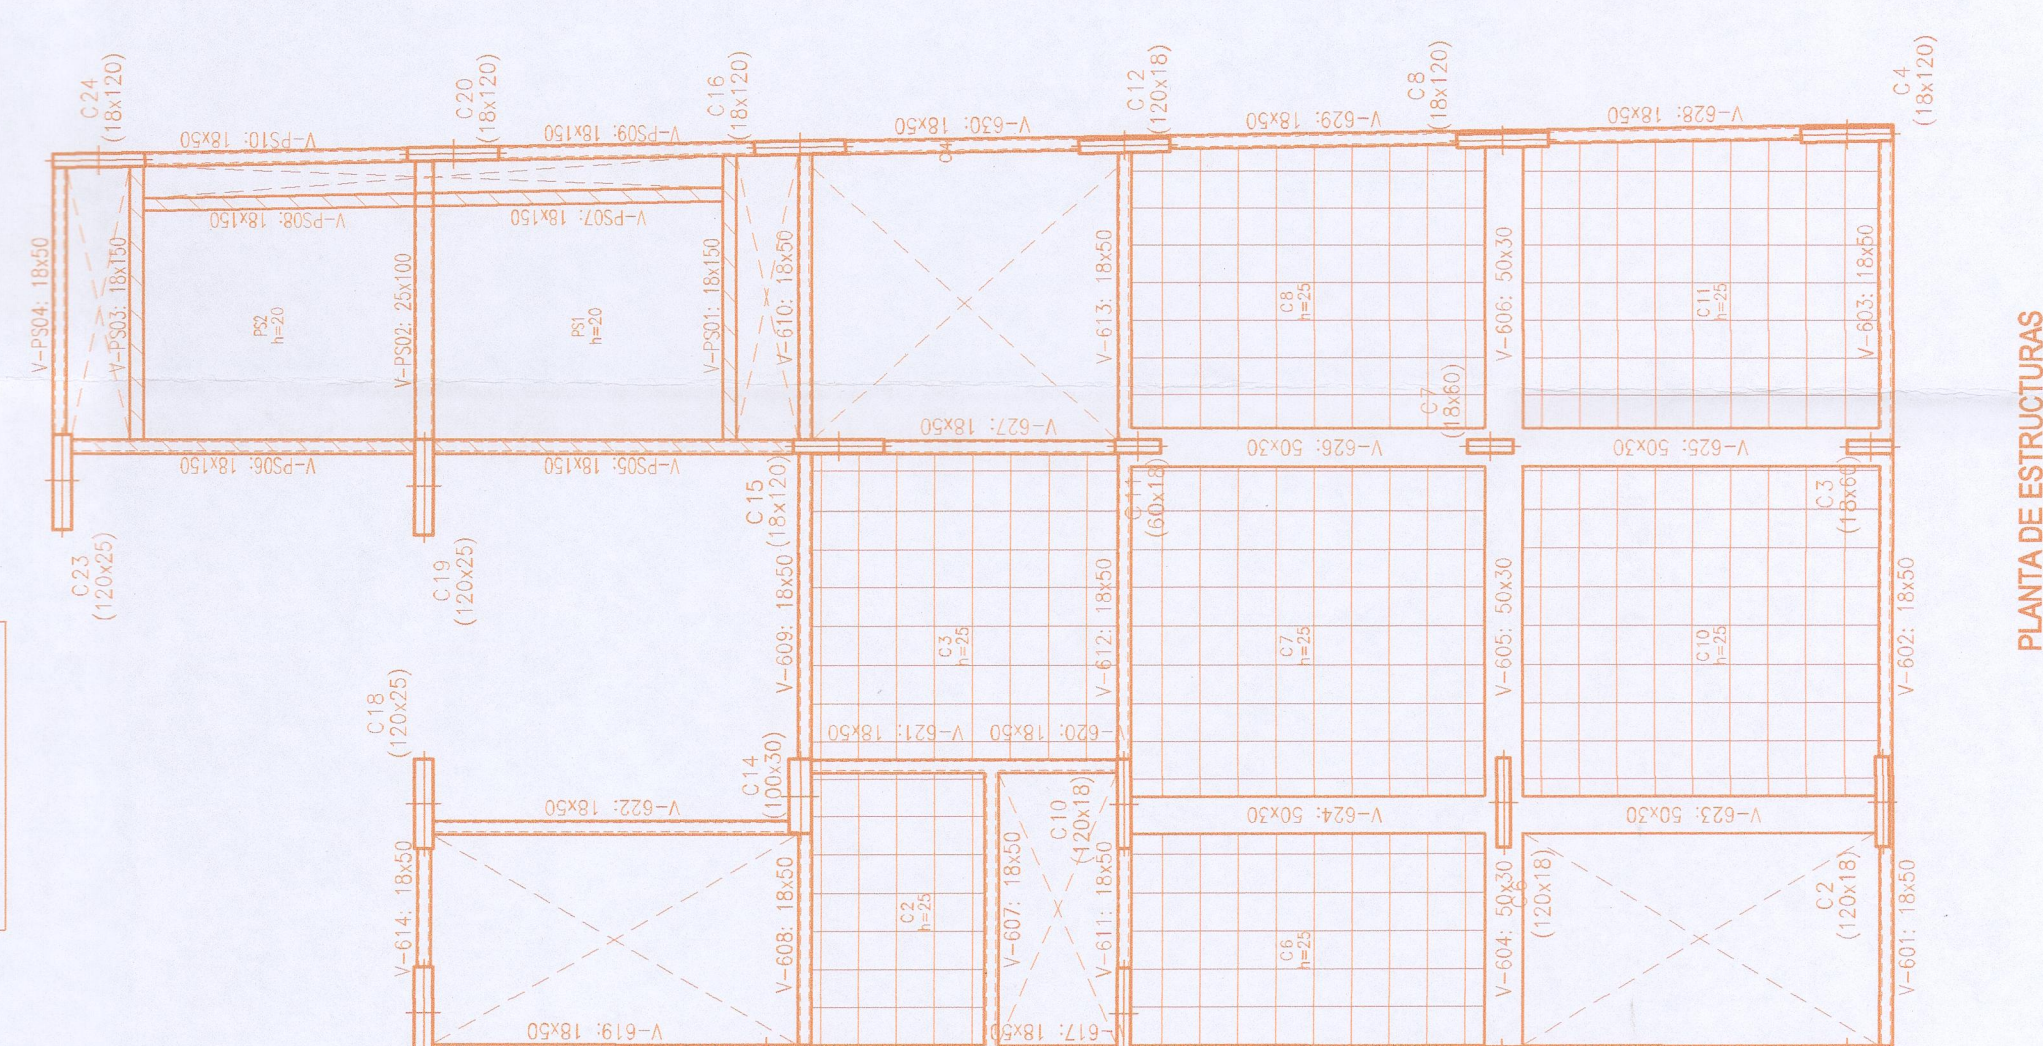


PLANTA DE ESTRUCTURAS
Sobre PISO 6

PLANTA DE ESTRUCTURAS
Sobre PISO 7

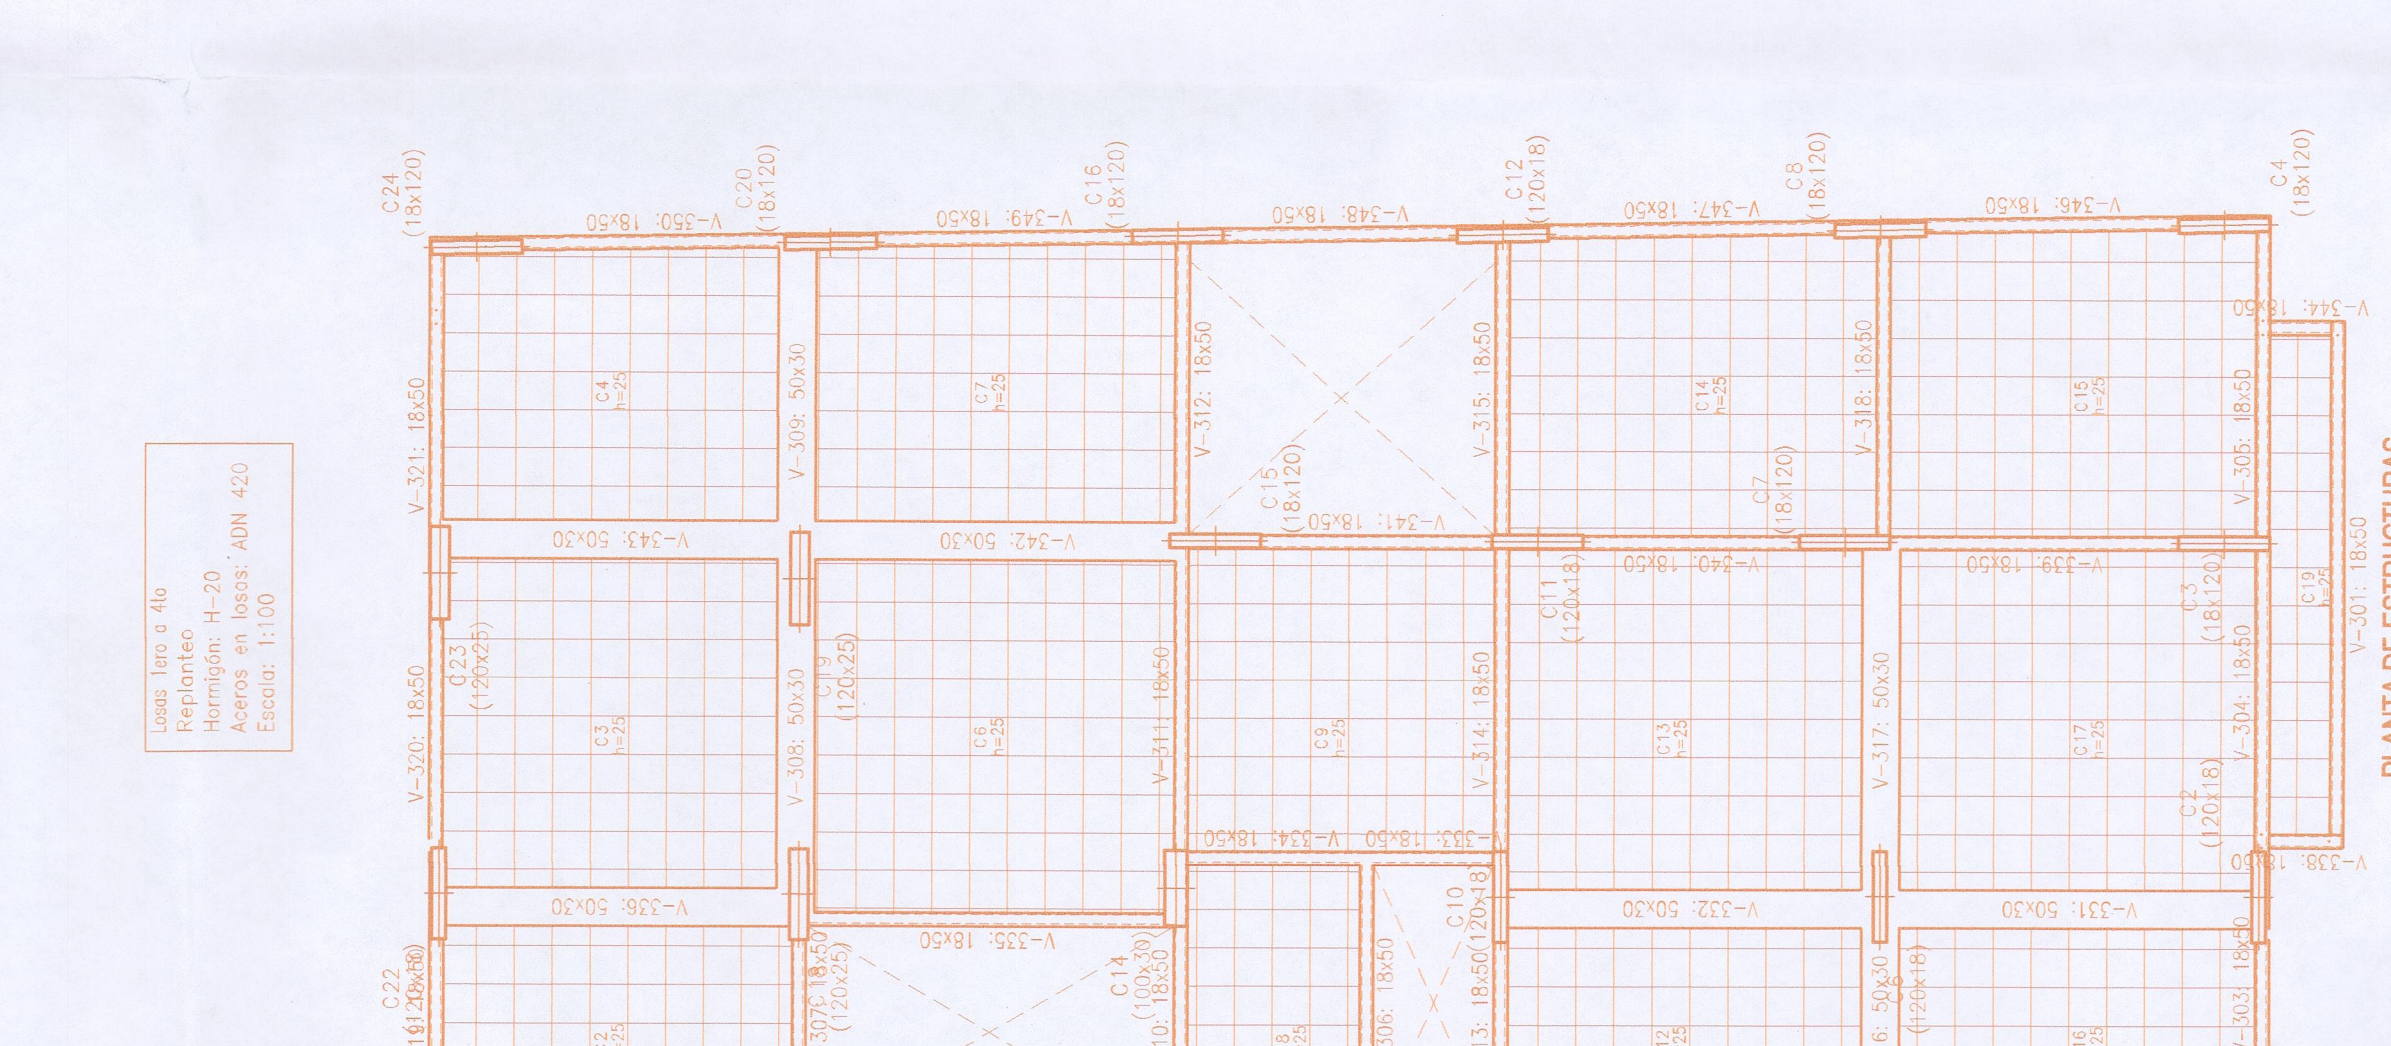

PLANTA DE ESTRUCTURAS
Sobre PISO 8

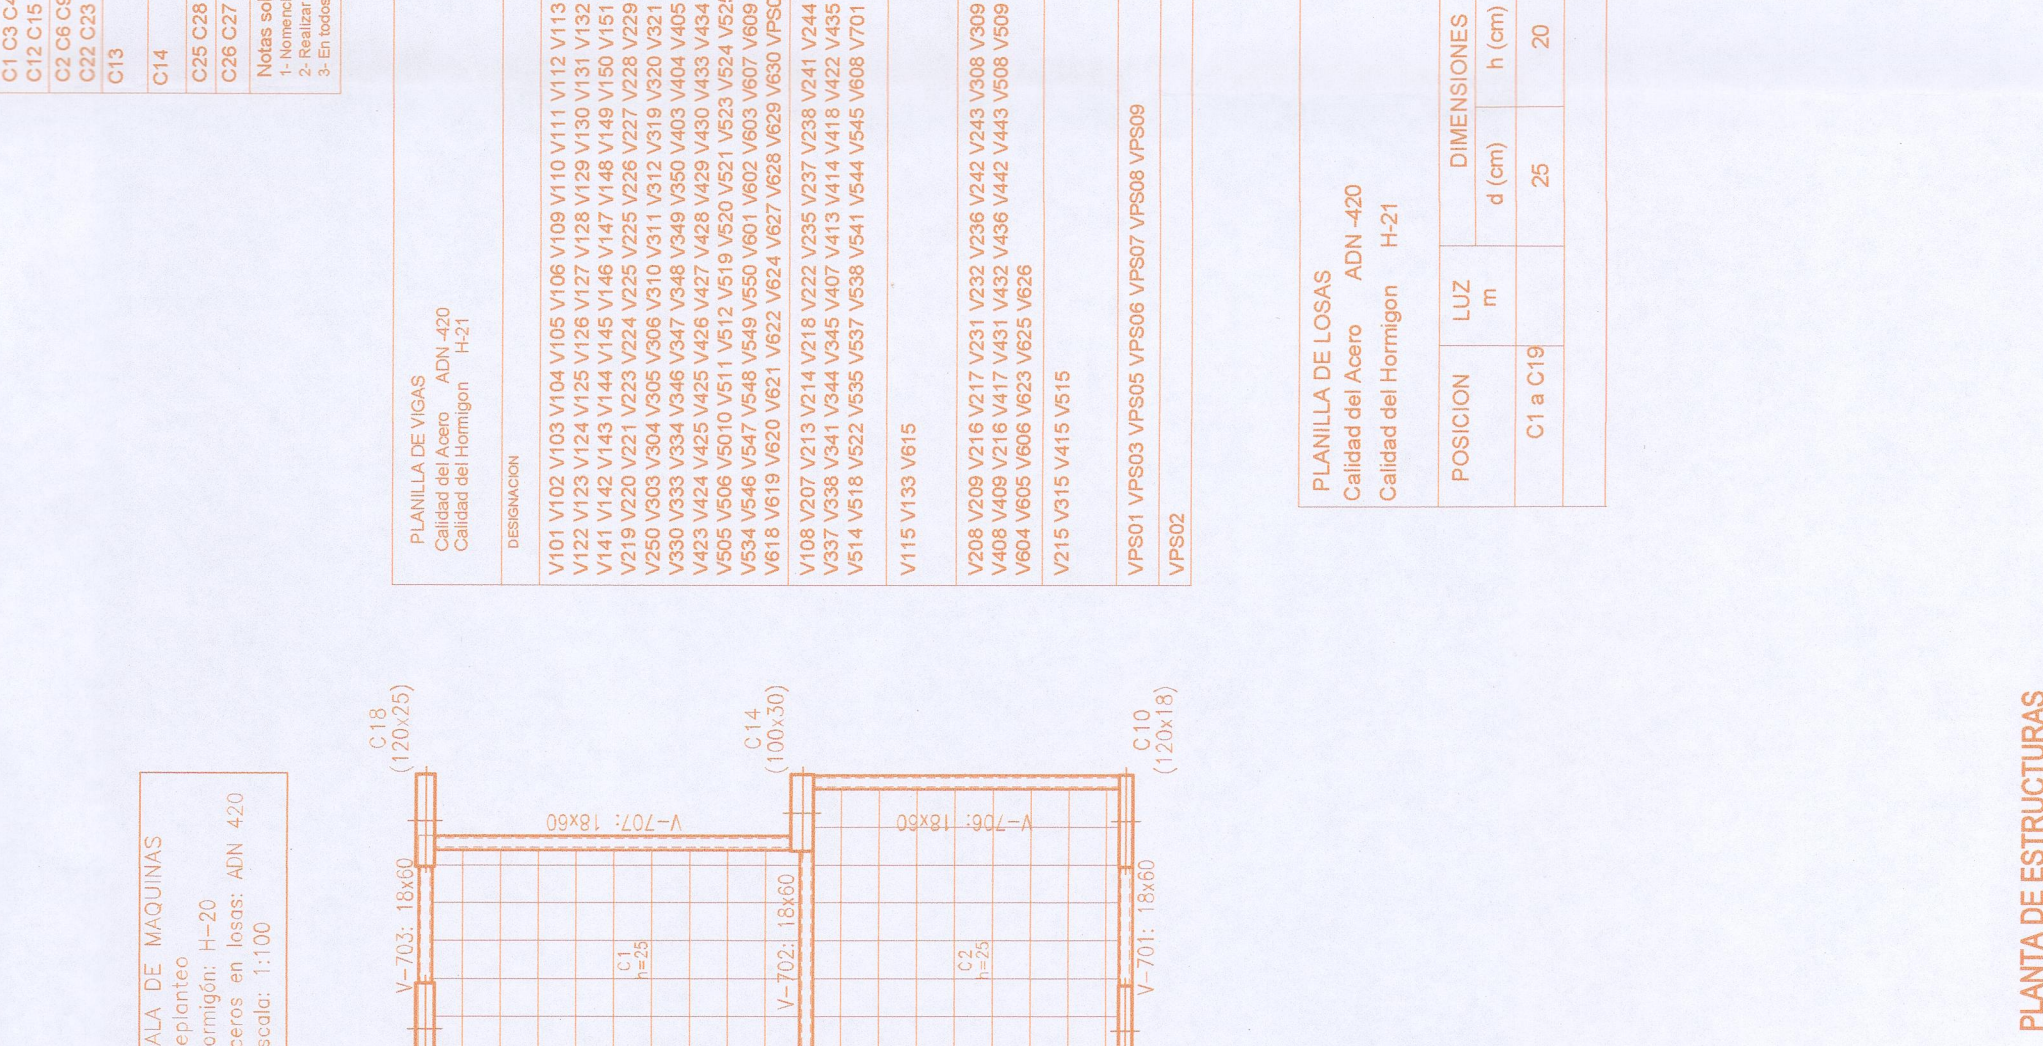


PLANTA DE ESTRUCTURAS
Sobre PISO 9

PLANTA DE ESTRUCTURAS
Sobre PISO 10




PLANTA DE ESTRUCTURAS
Sobre PISO 11

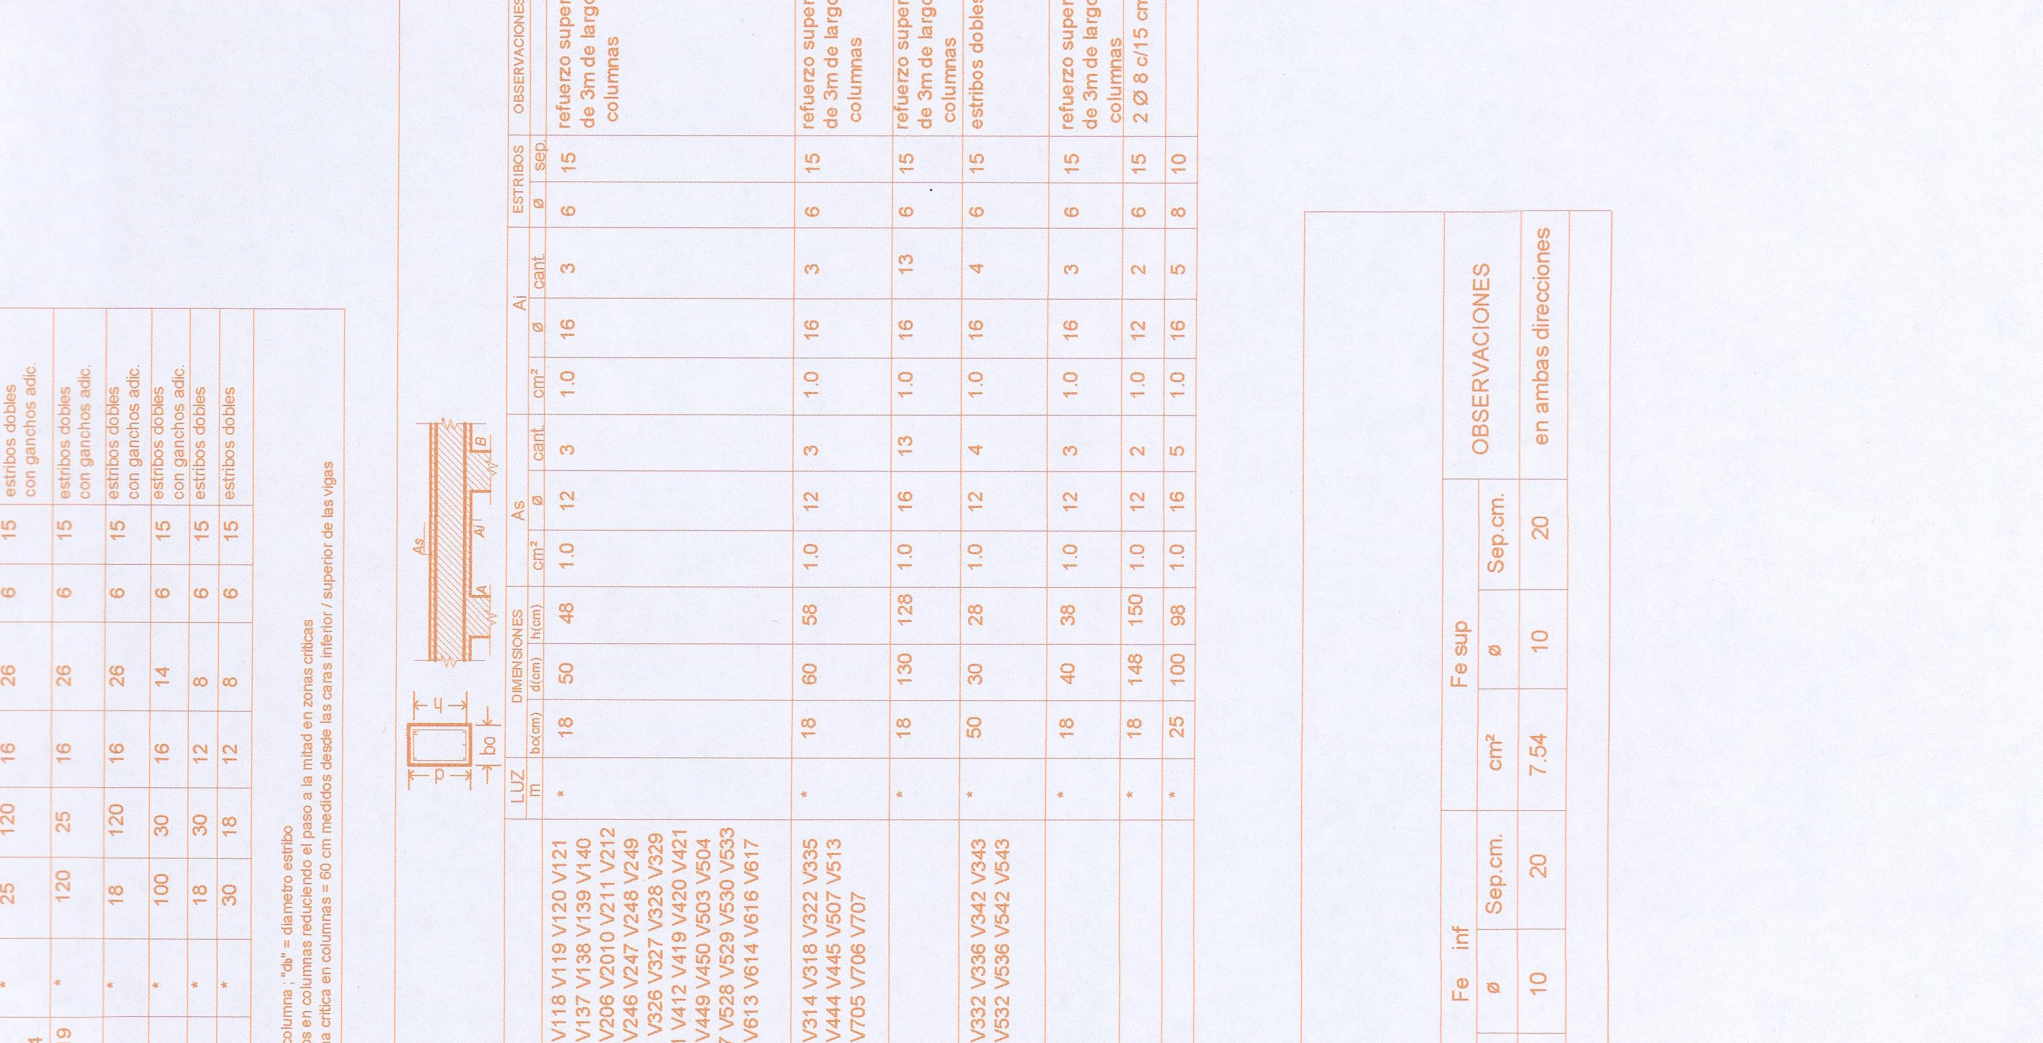


PLANTA DE ESTRUCTURAS
Sobre PISO 12

PLANTA DE ESTRUCTURAS
Sobre PISO 13

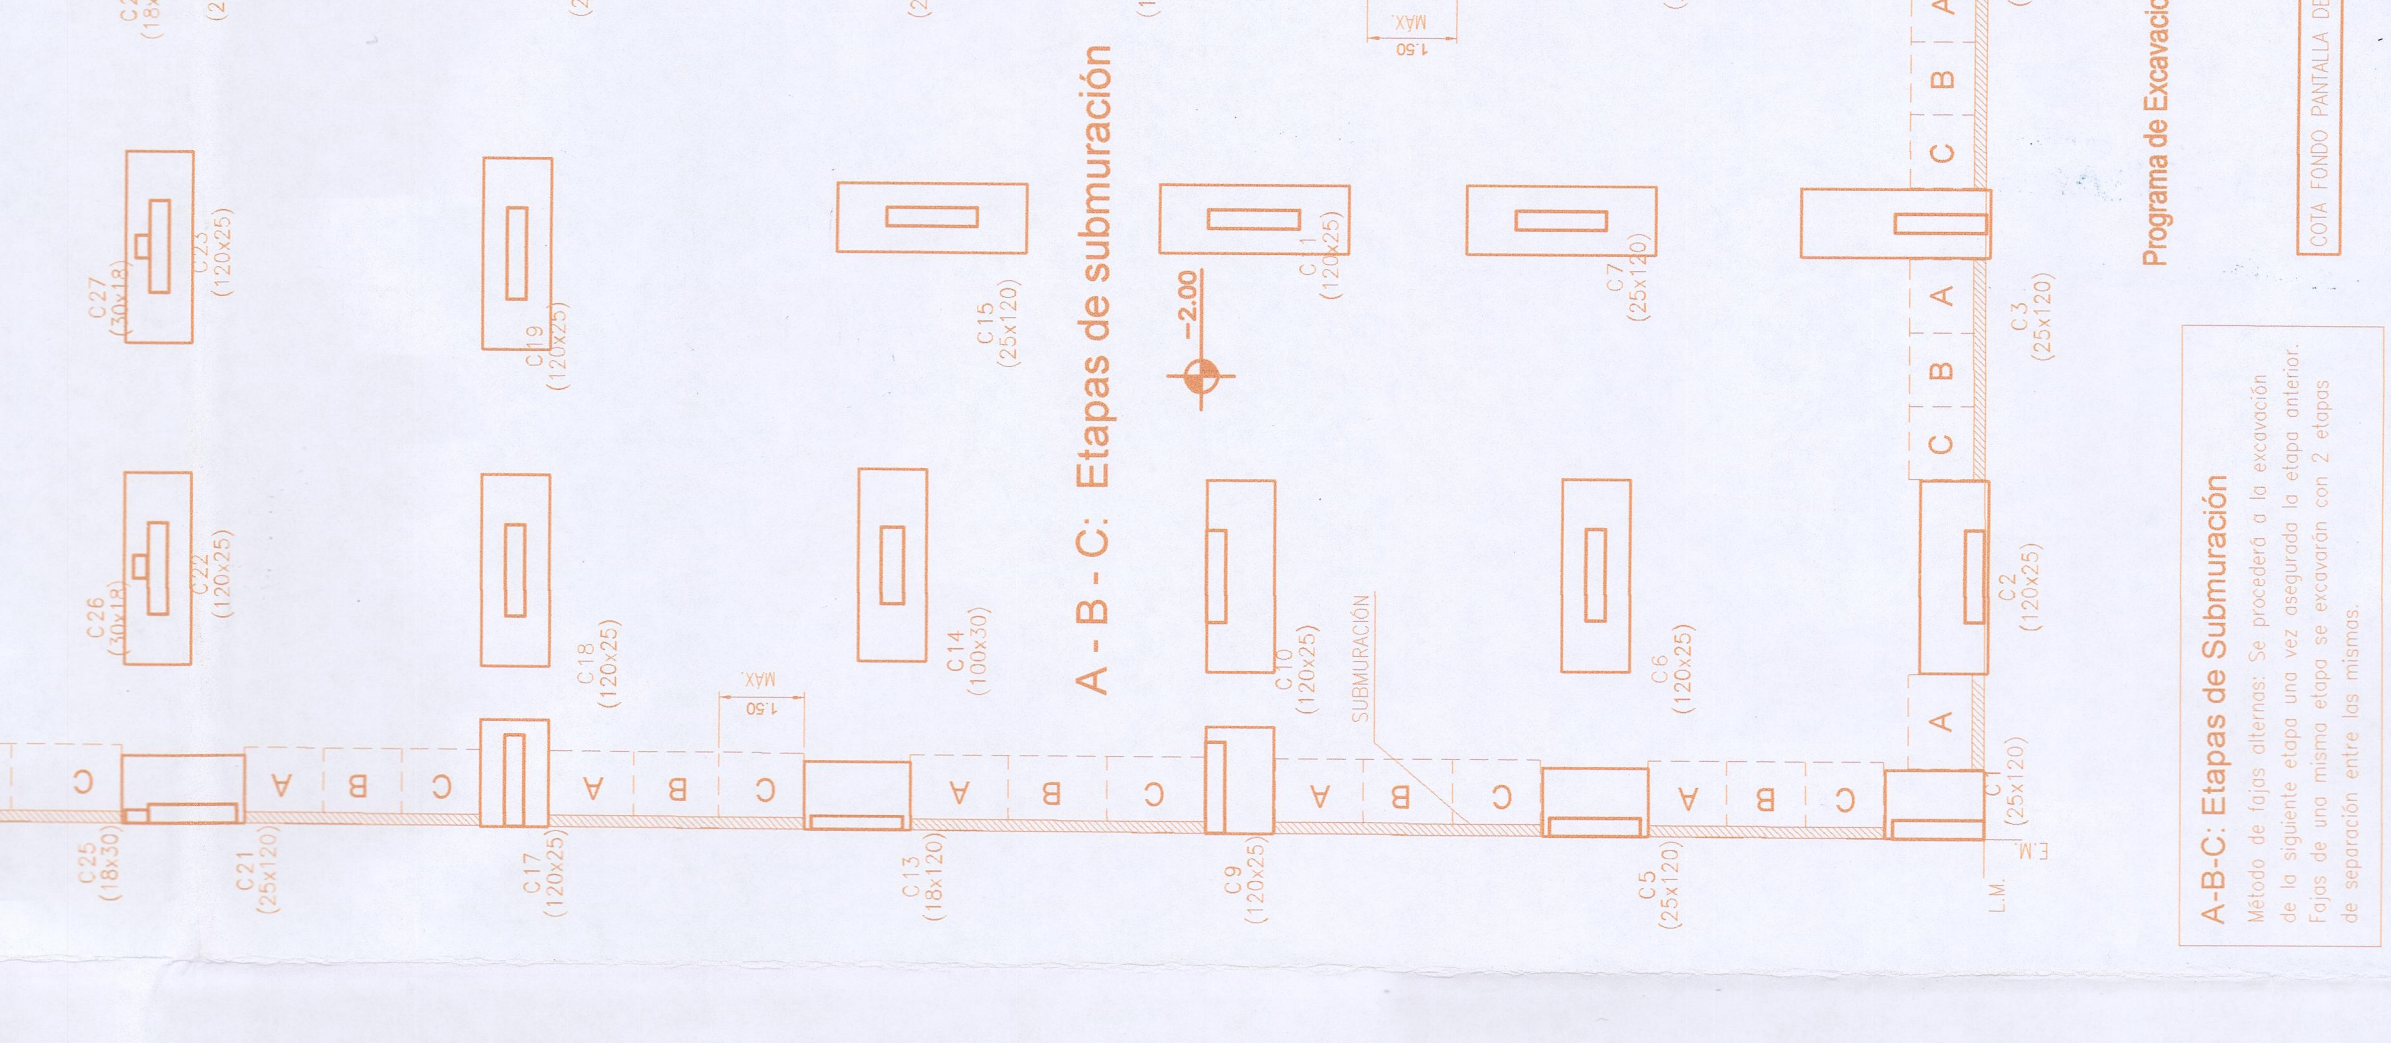


PLANTA DE ESTRUCTURAS
Sobre PISO 14

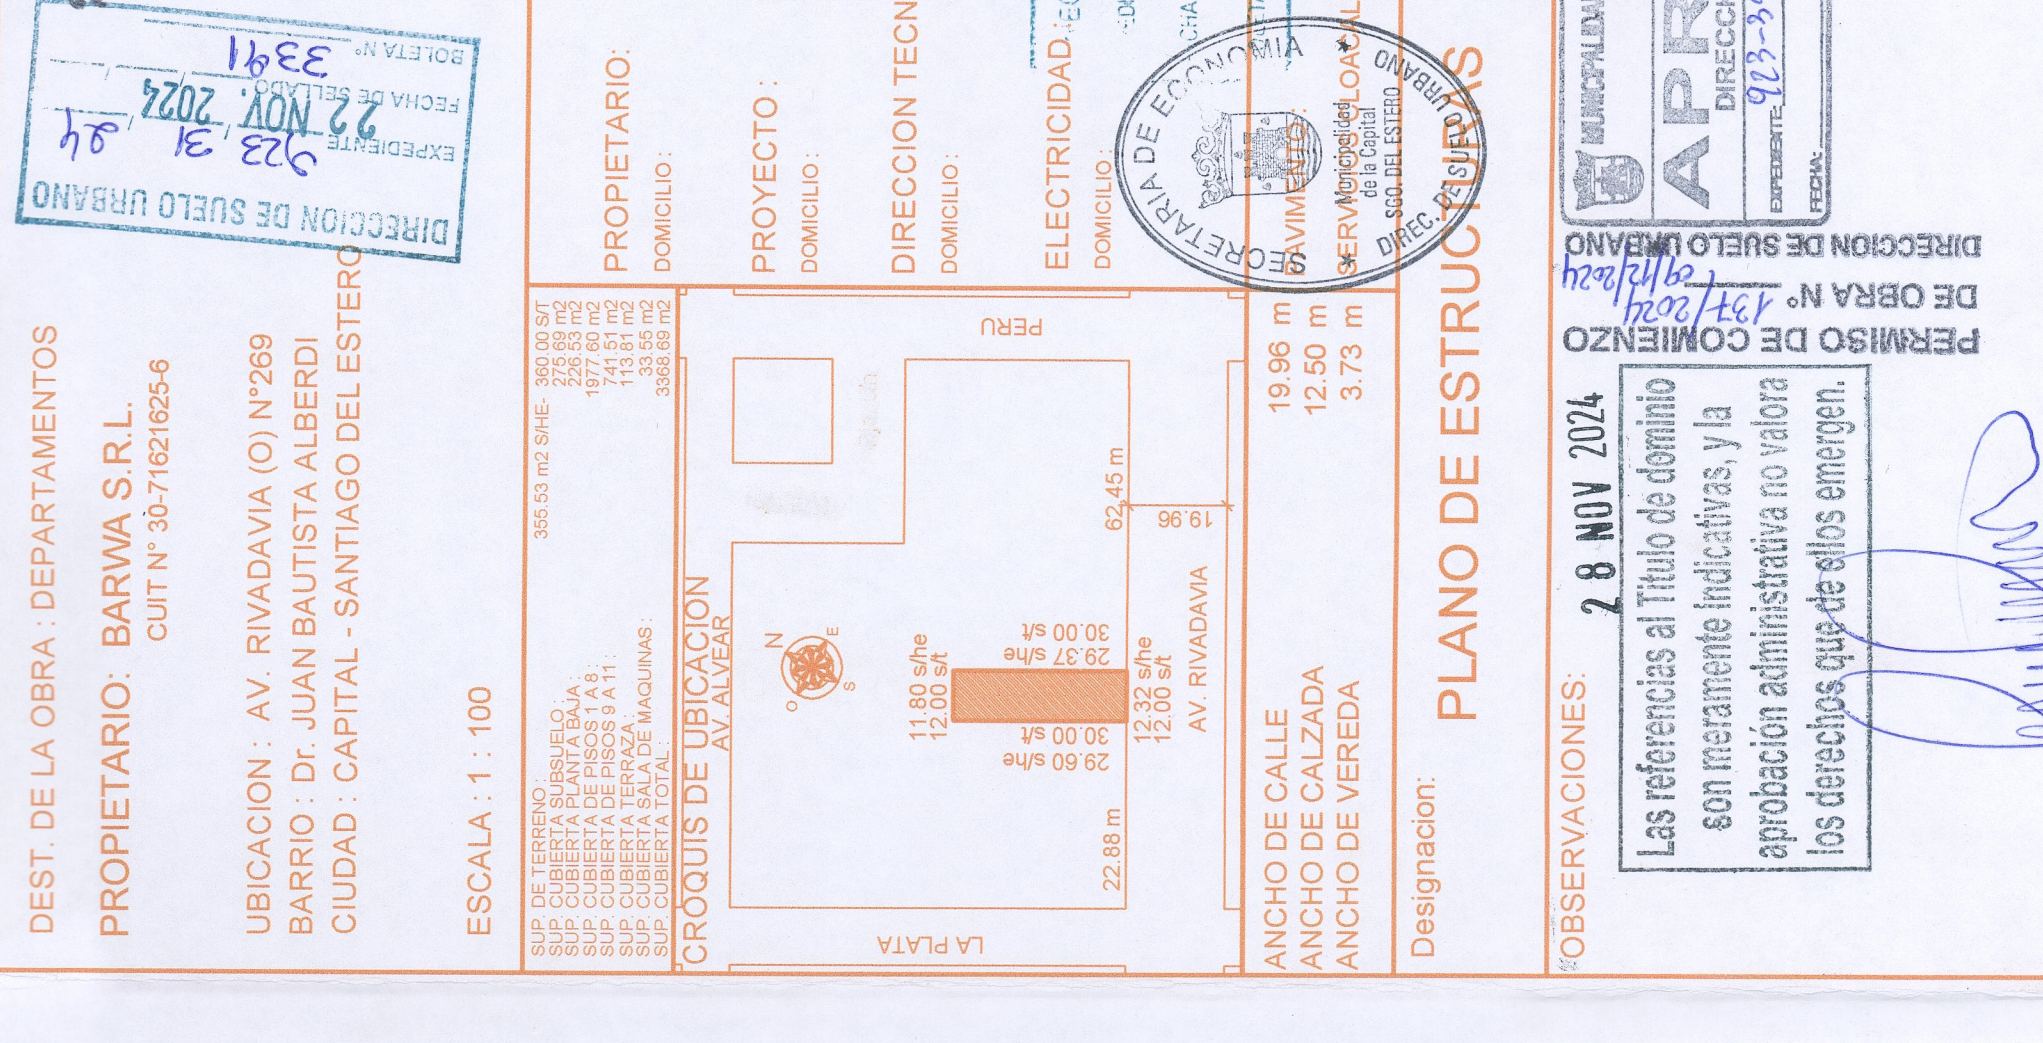


PLANTA DE ESTRUCTURAS
Sobre PISO 15

PLANTA DE ESTRUCTURAS
Sobre PISO 16

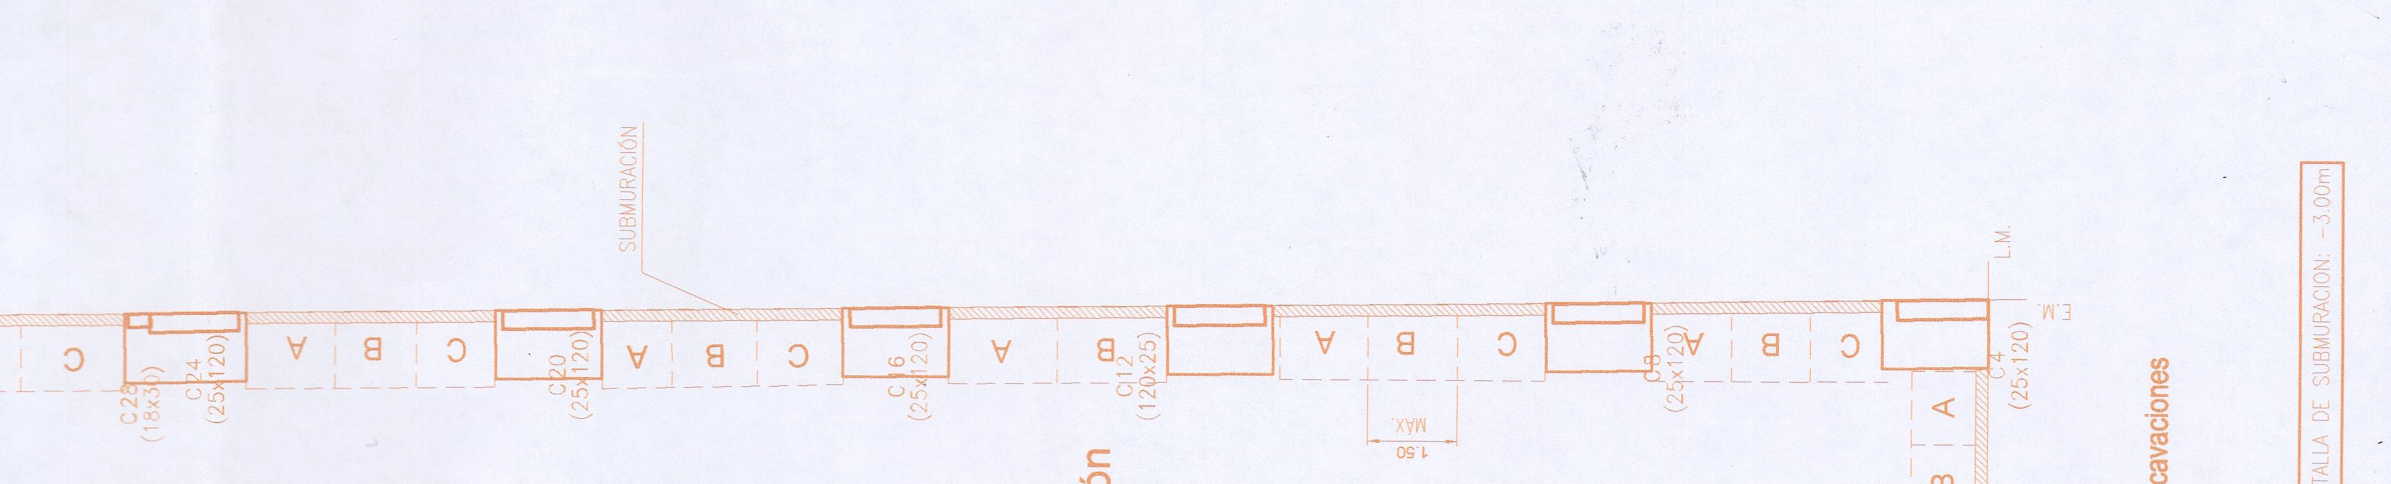

PLANTA DE ESTRUCTURAS
Sobre PISO 17

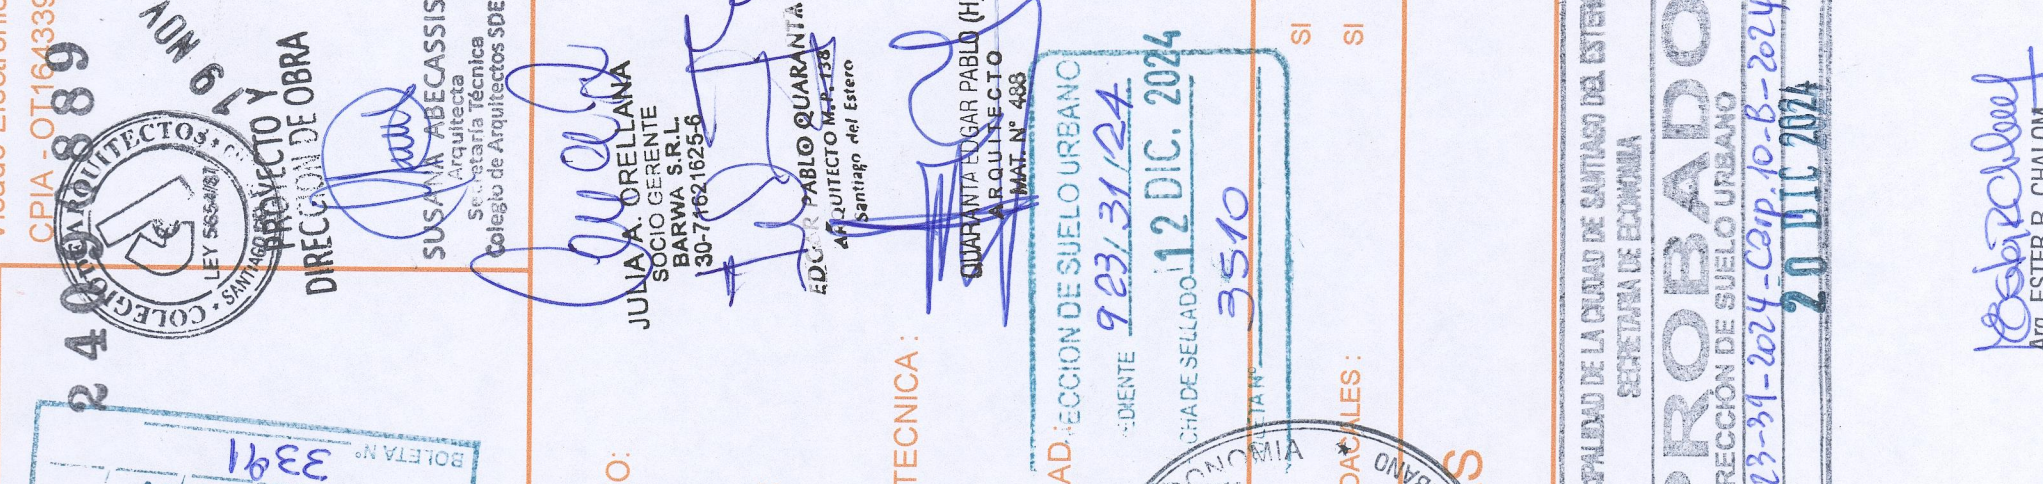

PLANTA DE ESTRUCTURAS
Sobre PISO 18