PLANILLA DE PERFIL ESTRUCTURAL "C" -

DESIG.	DIMENSIONES (en mm) h	a	d	e	PESO TEORICO Kg/ml	SECCION F cm2	Jx cm4	Wx CM1	Ix cm	Jy cm4	Wy CM1	Iy cm	GRAFICA
C.M.1	120	50	20	2.00	6.03	7.68	496.36	49.64	8.04	67.70	12.12	2.97	SIMPLE
V.M.1	140	60	20	2.00	8.09	9.31	705.01	79.85	10.08	91.96	19.77	6.13	DOBLE

PLANILLA DE CHAPAS

Cubierta de chapa autoportante trapezoidal
N° 24 0.5 mm peso 4200 Kg/Cm2

Pos	F Cm2	W Cm3	Carga admi.	Onda	d Largo Kg/m2	b Cm	OBS.
A	0.55	5.14	2472	9	9.35	110	

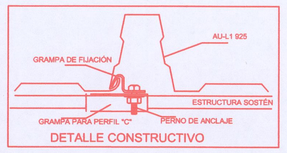

DETALLE CONSTRUCTIVO

LOSAS MACIZAS

Posición	Dimens. luz	d	h	Armadura Tramo Fe	Ø	Sep	Adic. apoyo Fe	Ø	sep	Fe Distr. Ø	sep	Observaciones: bk= 130Kgs./cm2 ak= 4200Kgs./cm2
	m	cm	cm	cm2	mm	cm	cm2	mm	cm	mm	cm	
LE	VAR	10	8.5	3.50	8	8	——	——	——	6.0	25	LOSA ESCALERA

LOSAS ESCALERAS

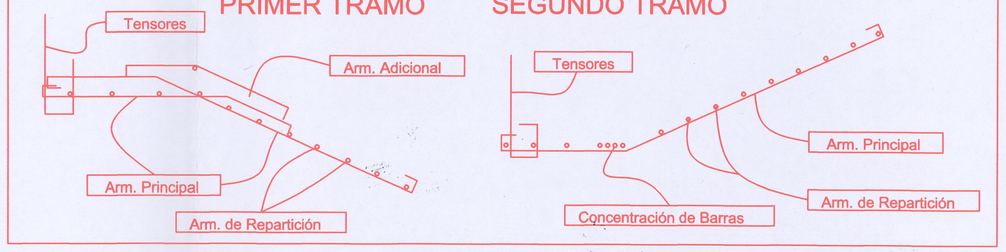

PLANILLA DE VIGUETAS (Utilizar estas viguetas o con armadura coincidente)

SERIES	(L1)(L2) ASTER	A1	A2	B1	B2	C	D	E
LARGOS(m)	1,00 a 3,00	3,10 a 3,40	3,50 a 3,80	3,90 a 4,20	4,30 a 4,60	4,70 a 5,40	5,50 a 6,20	6,30 a 7,20
ARMADURA	2 x 2Ø2,4	1 x 3Ø2,4 1 x 2Ø2,4	3 x 2Ø2,4	2 x 3Ø2,4 1 x 2Ø2,4	3 x 3Ø2,4	2 x 2Ø2,4 2 x 3Ø2,4	2 x 2Ø2,4 3 x 3Ø2,4	2 x 2Ø2,4 4 x 3Ø2,4
SECCION TOTAL	18 mm2	22,5 mm2	27 mm2	36 mm2	40,7 mm2	45,1 mm2	58,7 mm2	72,3 mm2

CAPA DE COMPRESION = 5 cm MALLA SIMA Ø4,2c/25cm

Refuerzo de 2 viguetas Paralelas

Refuerzo de 3 viguetas Paralelas

Refuerzo de vigueta transversal

DETALLE LOSA DE VIGUETAS DOBLE ENTREPISO

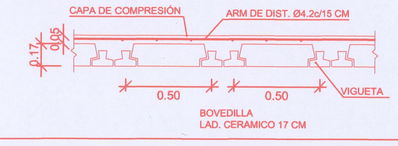

PLANILLA DE BASES DE HORMIGON ARMADO

EXCENTRICAS CENTRADAS

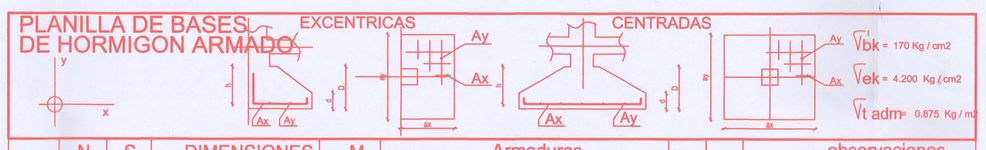

DESIG.	N Tn	S m2	DIMENSIONES m ax	ay	d	D	h	M (Tm)	Armaduras Ax cm2	Ax Nº	Ax Ø	Ay cm2	Ay Nº	Ay Ø	σc Kg/cm2	σt Kg/cm2	observaciones
B 1	19.33	3.015	0.80	0.80	0.15	0.475	0.565	4.05	9.13	15	12	8.13	15	12	3.89	3.97	
B 2	18.95	2.015	1.00	1.00	0.15	0.475	0.425	3.17	7.05	15	10	7.31	15	10	2.85	2.97	

NOTA: Profundidad de Excavación - Fundaciones (Df= - 1.20 m)

DETALLE FUNDACION CORRIDA EJE DE MURO (ZC)

ZC 60x20
VN 20x40

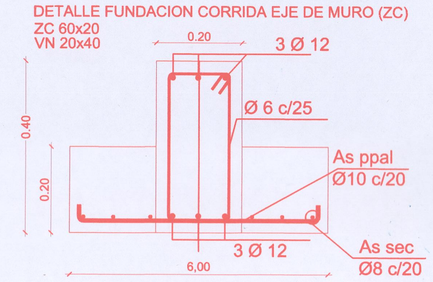

DETALLE FUNDACION CORRIDA EXCENTRICA (ZC) (MEDIANERAS)

ZC 60x20
VN 20x40

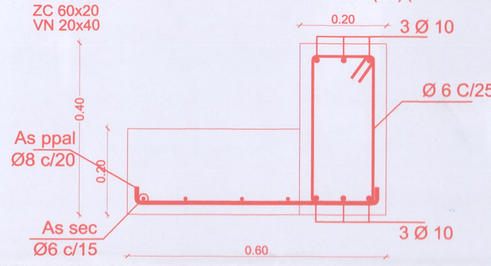

PLANILLA DE COLUMNAS

Bk= 170Kgs./cm2
Ak= 4200Kgs./cm2

Design.	hp. m	fe Hormigon d1 cm	d2 cm	S cm2	fe Armadura Nº	Ø	Sec. cm	Estribos Ø	Sep. cm	Observaciones
CE	VAR.	18	18	289	4	8	1.12	6	20	CUADRADA
C1	VAR.	18	18	345	4	10	1.09	6	15	CUADRADA

PLANILLA DE VIGAS

Bk= 130 Kg./cm2
Ak= 4200 Kg./cm2

Desig.	Luz (m)	Dimensiones bo (cm)	h (cm)	do (cm)	Armad. - tramo A1 Nº	Ø	AS Nº	Ø	Armad - apoyo A Nº	Ø	B Nº	Ø	Estribos Ø	sep.	Observaciones
V.E.S.	*	18	18	20	2	8	2	8	2	8	2	8	6	20	* variable
V.1	*	18	18	20	2	10	2	10	2	10	2	10	6	15	* variable
V.2	*	18	18	20	2	12	2	12	2	12	2	12	6	15	* variable

DETALLE DE CANALETA EN COCHERA

ESCALA: GRAFICA EJE MEDIANERO

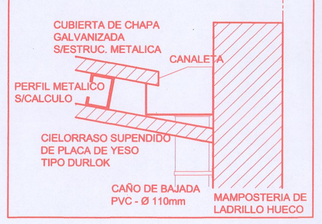

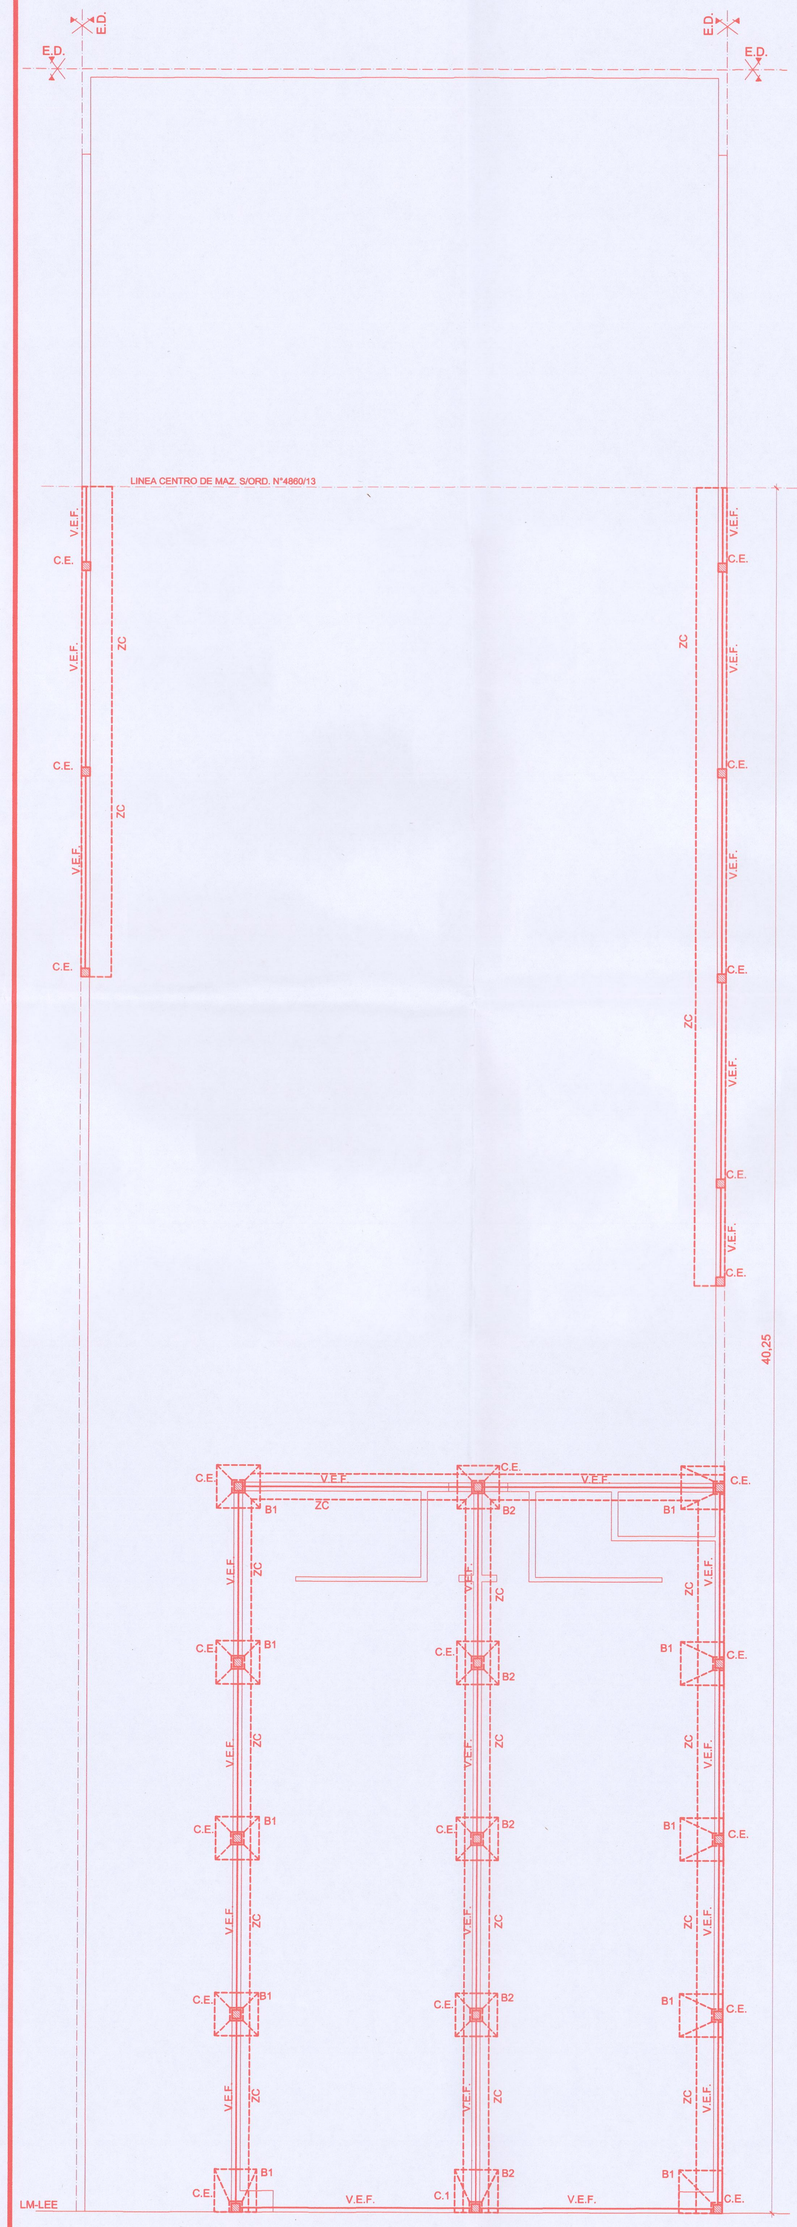

PLANTA FUNDACION

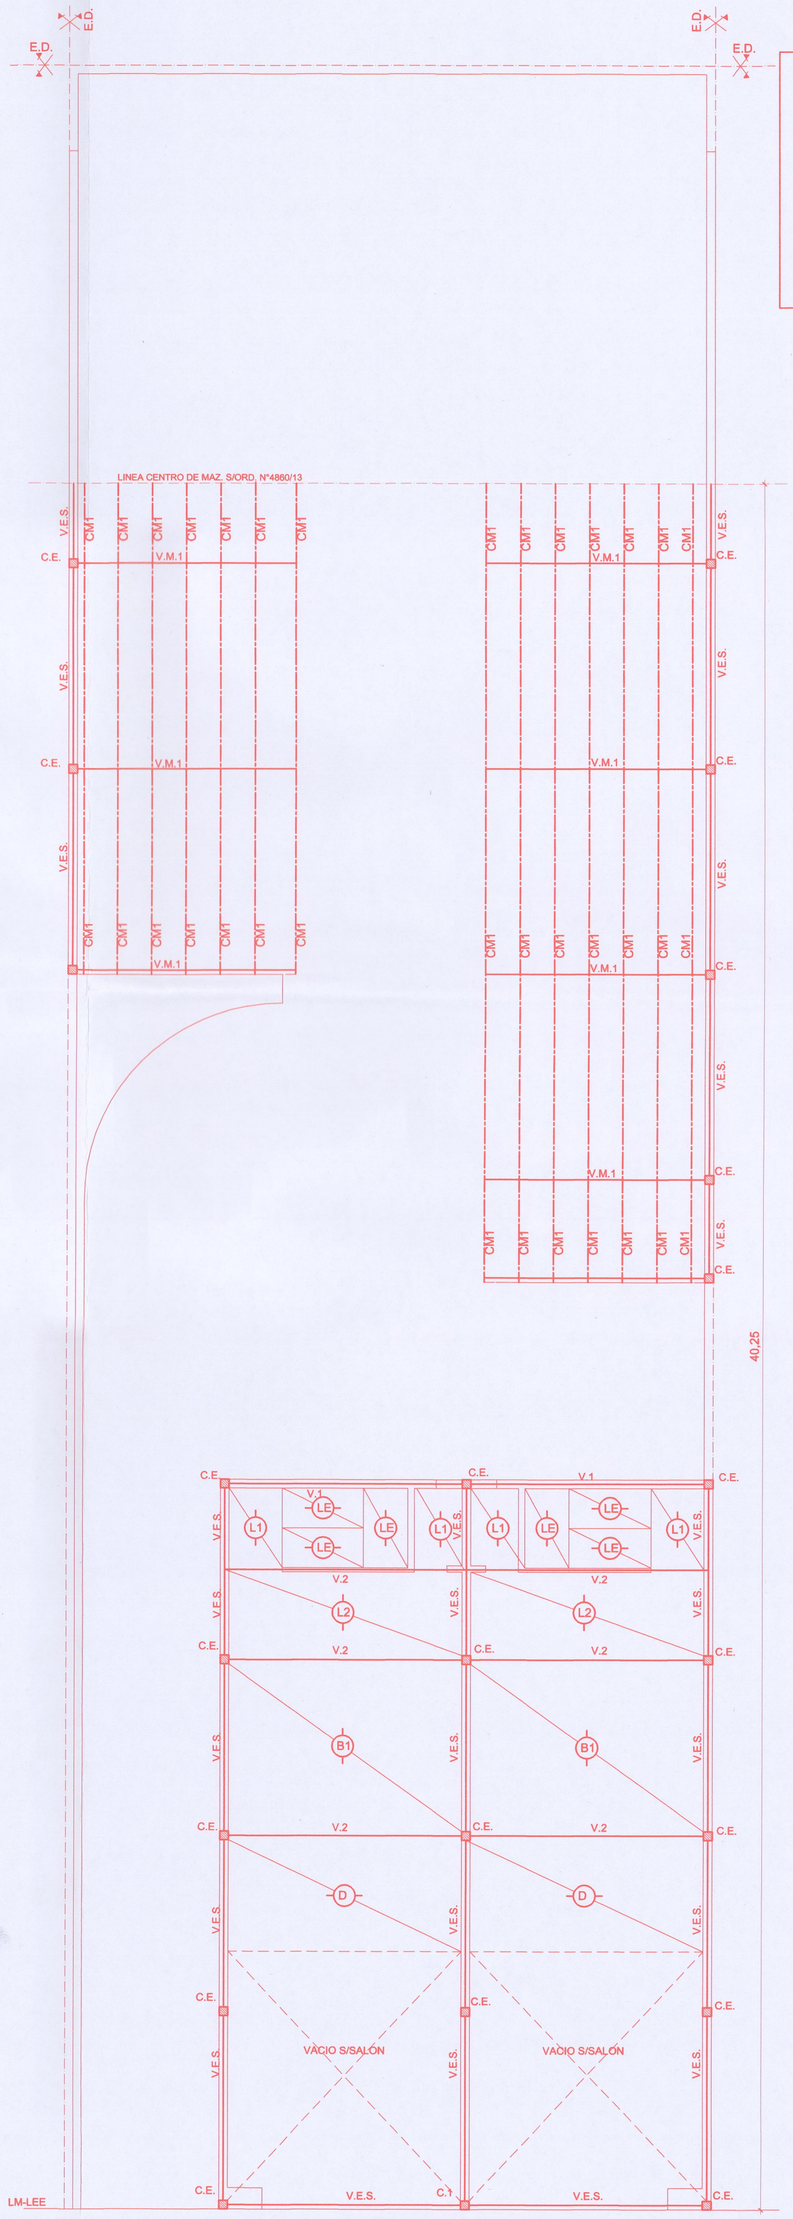

PLANTA ESTRUCTURA

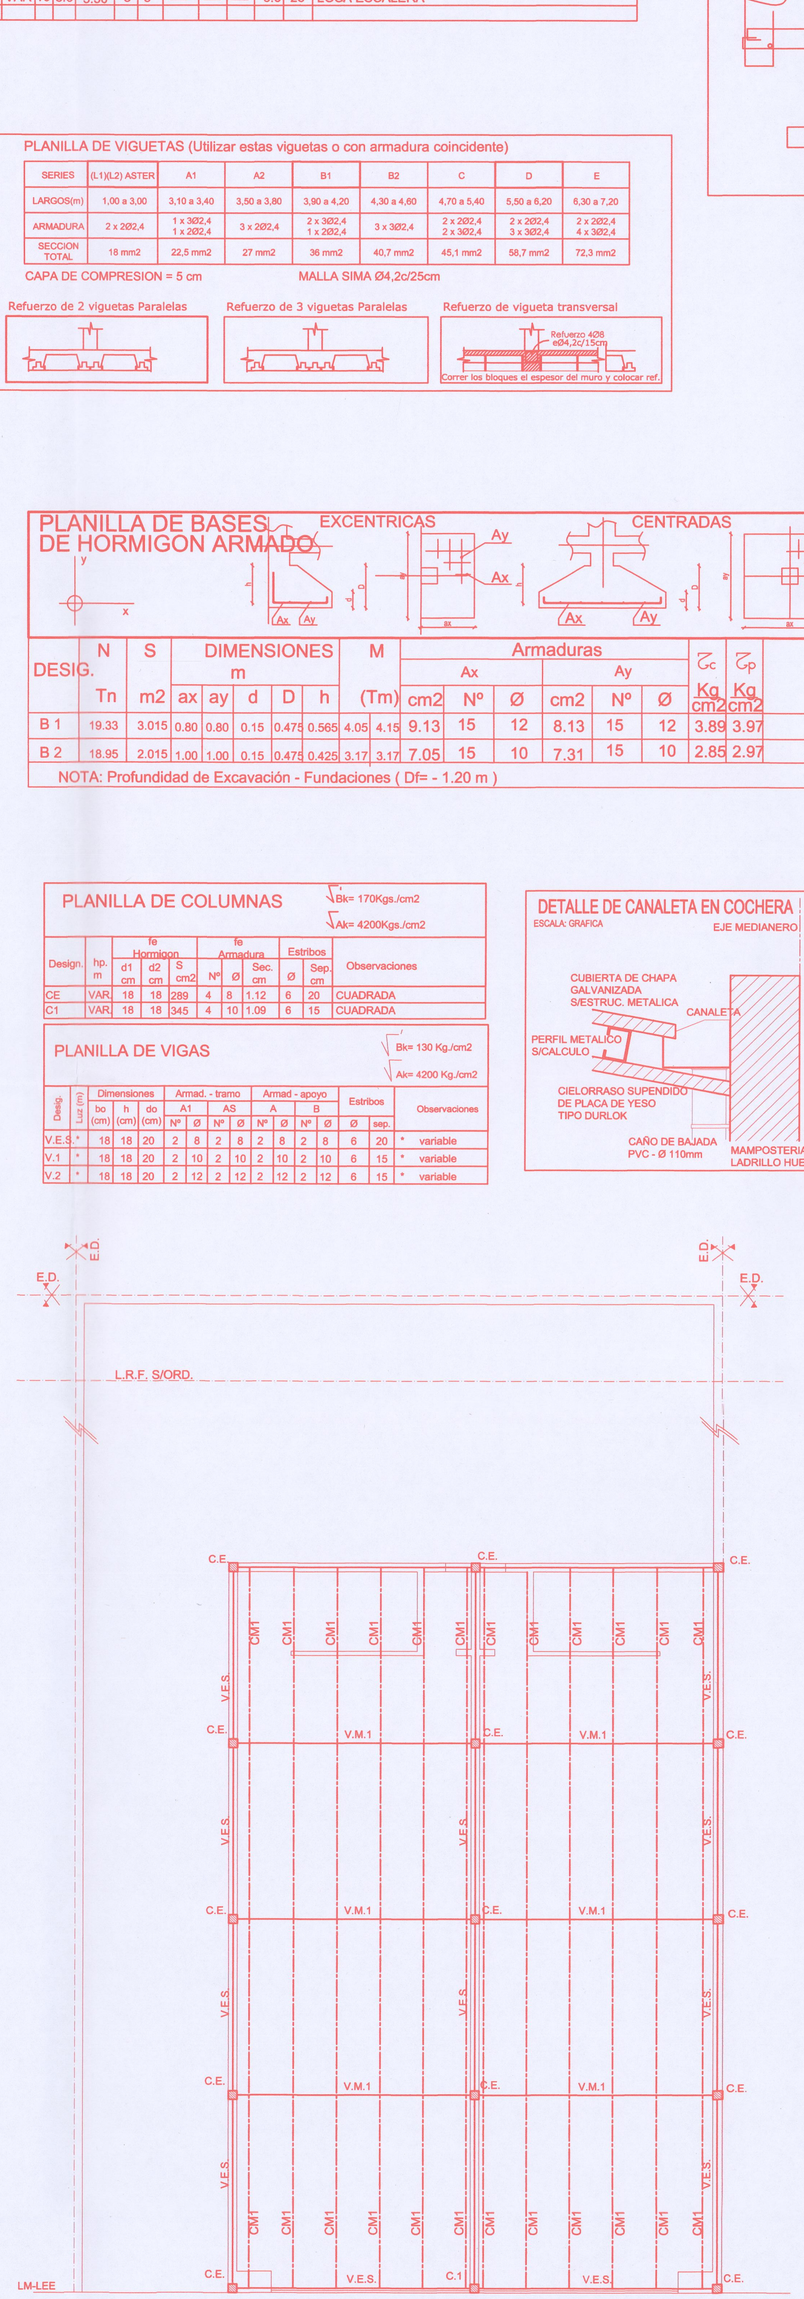

PLANTA ESTRUCTURA

Distr. 3 Zona 3 Manz. 26 Parc. 160

PADRON N°01-01-003403 ICM: EXPTE. N°395-B-25 MFR N°7N-

DESTINO DE LA OBRA: LOCAL COMERCIAL (2) DOS ESTACIONAMIENTO MENSUAL

PROPIETARIO: NESTOR RAUL BOUZON
DNI N°13.775.124

UBICACION: AVENIDA HIPOLITO YRIGOYEN N°102
BARRIO: JUAN BAUTISTA ALBERDI
CIUDAD: SGO. DEL ESTERO
ESCALA: 1:100 - 1:250

PROYECTO Y DIRECCIÓN DE OBRA
16 12 25
VIVIANA ABECASSIS
Arquitecta
Secretaria Técnica
Consejo de Arquitectos SDE

SUP. TERRENO:	S/HE - S/T	775,70 m²
SUP. CUBIERTA PLANTA BAJA		334,57 m²
SUP. CUBIERTA PLANTA ALTA		125.40 m²
SUP. CUBIERTA TOTAL		459.97 m²

Croquis de Ubicacion:

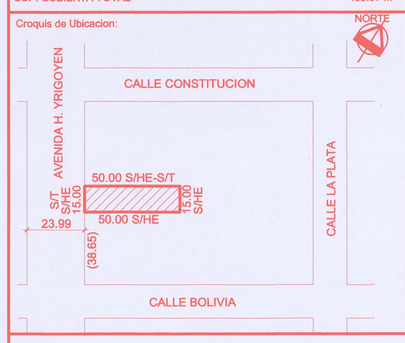

Propietario:
Domicilio:

Proyecto:
Domicilio: Julio D. Ruiz Almada ARQUITECTO M.P.N° 0931

D. Tecnica:
Domicilio: Oscar Alfredo Briz ARQUITECTO M.P.C.A.S.E. N° 0633

Electricidad:
Domicilio:

Categoria : "B"

ANCHO DE CALLE:	23.99 mts.
ANCHO DE CALZADA:	12.17 mts.
ANCHO DE VEREDA:	5.77 - 6.05 mts.

PAVIMENTO: SI
SERVICIOS CLOACALES:

DIRECCION DE SUELO URBANO EXPEDIENTE 849 / 31 / 2025 06 FEB. 2026 FECHA DE SELLADO 2626

Designacion:

PLANO OBRA NUEVA
PLANO DE ESTRUCTURAS - PLANILLA Y DETALLES Lamina 2-2

OBSERVACIONES: 21 ENE 2026

Las referencias al Titulo de dominio son meramente indicativas, y la aprobación administrativa no valora los derechos que de ellos emerjan

PERMISO DE COMIENZO DE OBRA N° 211/2026
DIRECCION DE SUELO URBANO

MUNICIPALIDAD DE LA CIUDAD DE SANTIAGO DEL ESTERO
SECRETARIA DE ECONOMIA
APROBADO
DIRECCIÓN DE SUELO URBANO
EXPEDIENTE: 849-31-25 / 01-B-26
FECHA: 17 FEB 2026

Ing. Andrés J. LEANDRO ARJONA
JEFE DE AREA DE VISACIONES TECNICAS
DIRECCION DE CATASTRO MUNICIPAL

Arq. ABRAHAM BERNARDO ROMINA
Dpto. OBRAS PRIVADAS
DIRECCION DE SUELO URBANO

Arq. Cesar Marcelo Alcorta
Director D.S.U.
Municipalidad de la Capital

COLEGIO DE ARQUITECTOS LEY 9554/87 SANTIAGO DEL ESTERO
2510087936

SECRETARIA DE CONTROL URBANO DIRECC. DE SUELO URBANO Municipalidad de la Capital SGO. DEL ESTERO

DIRECCION DE SUELO URBANO EXPEDIENTE 849 / 31 / 25 FECHA DE SELLADO 16 / 01 / 26 BOLETA N°