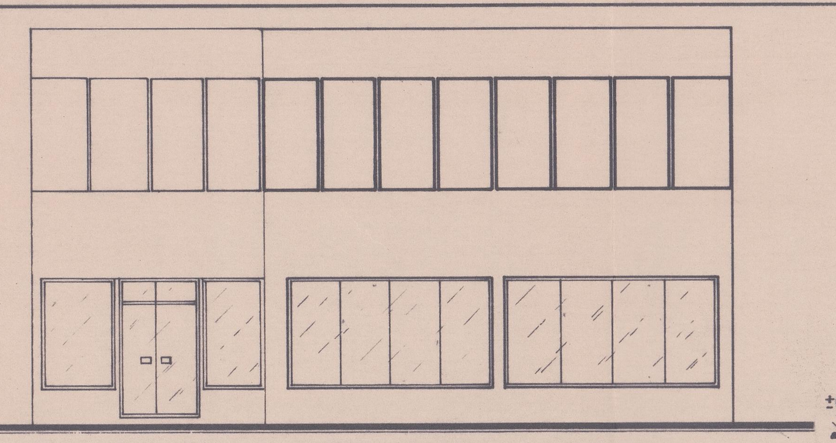

FACHADA SOBRE AVENIDA HIPOLITO IRIGOYEN

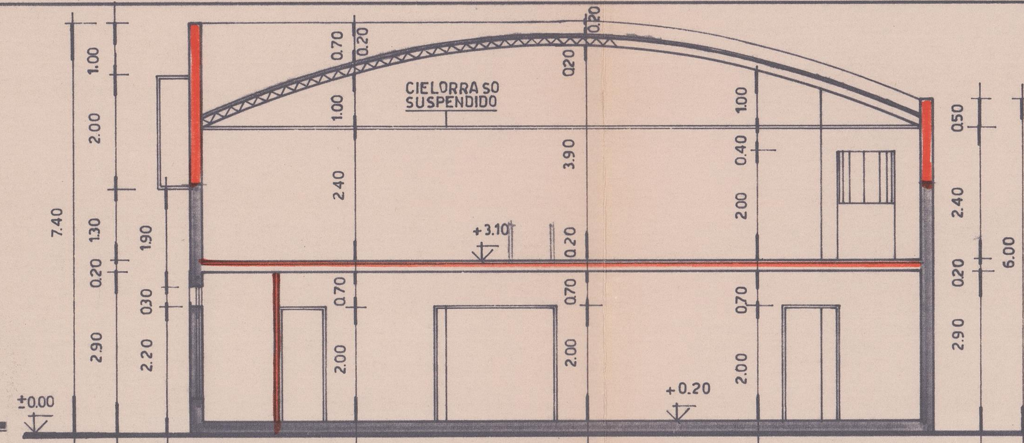

CORTE A - B

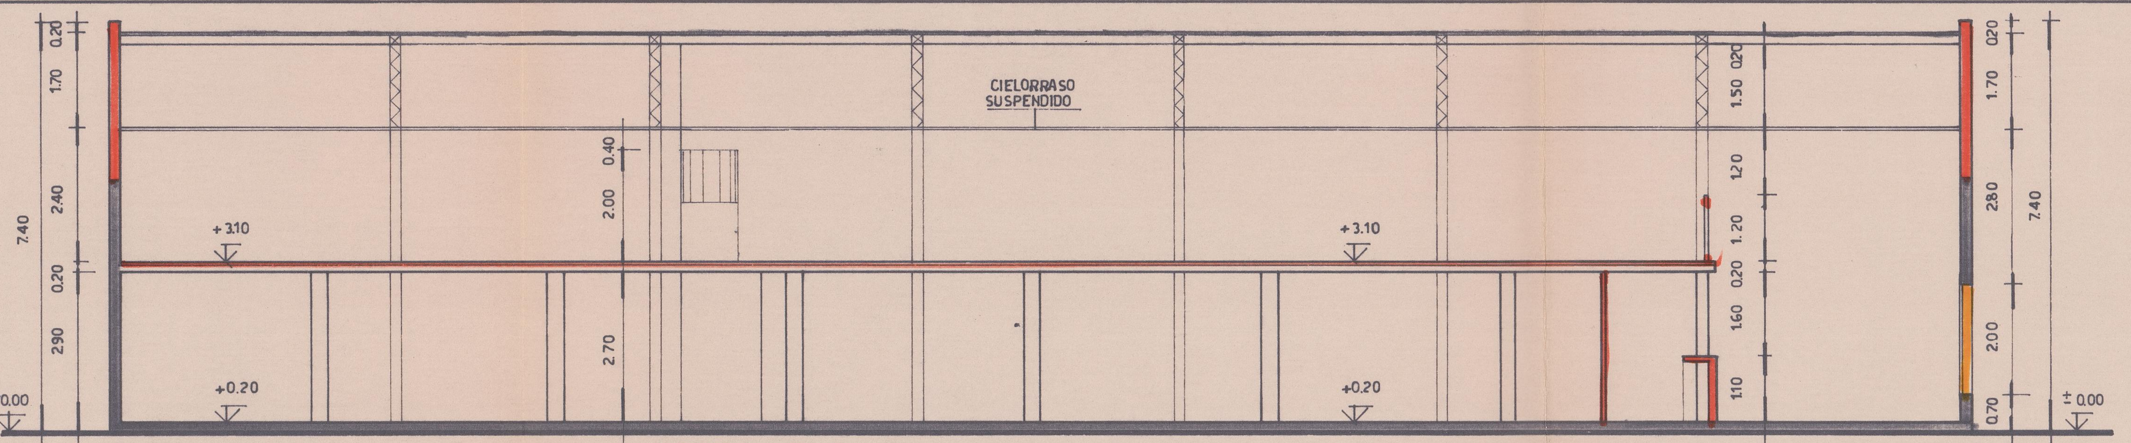

CORTE C-D

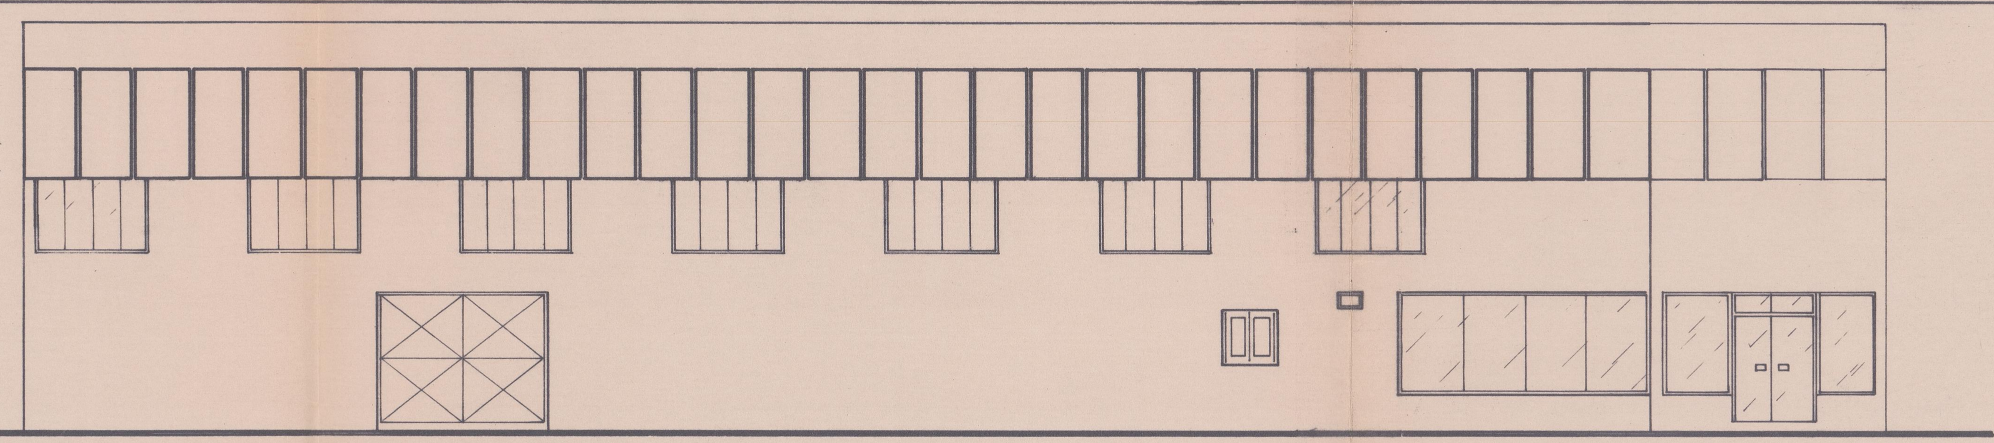

FACHADA SOBRE CALLE SANTA CRUZ

PLANILLA DE CARGAS

NIVEL	TABLERO	CIRCUITO	BOCAS LUZ 75	BOCAS TOMAS 200	POTENCIA LUZ	POTENCIA TOMAS	POTENCIA TOTAL	CORRIENTE (A)	PROTEC. TERMOMAG.	DISYUNTOR DIFERENCIAL
P.B.	T.P.	1	8	2	600	400	1000	4.5	1X10A	40A
		2	7	2	525	400	925	4.2	1X10A	40A
		3	8	3	600	600	1200	5.4	1X10A	40A
		4	4	2	300	400	700	3.8	1X10A	40A
P.E.	T.S.	1	5	—	375	—	375	1.7	1X10A	40A
		2	5	—	375	—	375	1.7	1X10A	40A

DIAGRAMA UNIFILAR

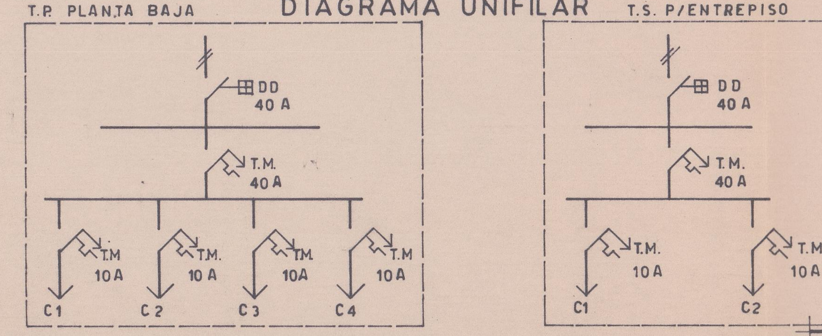

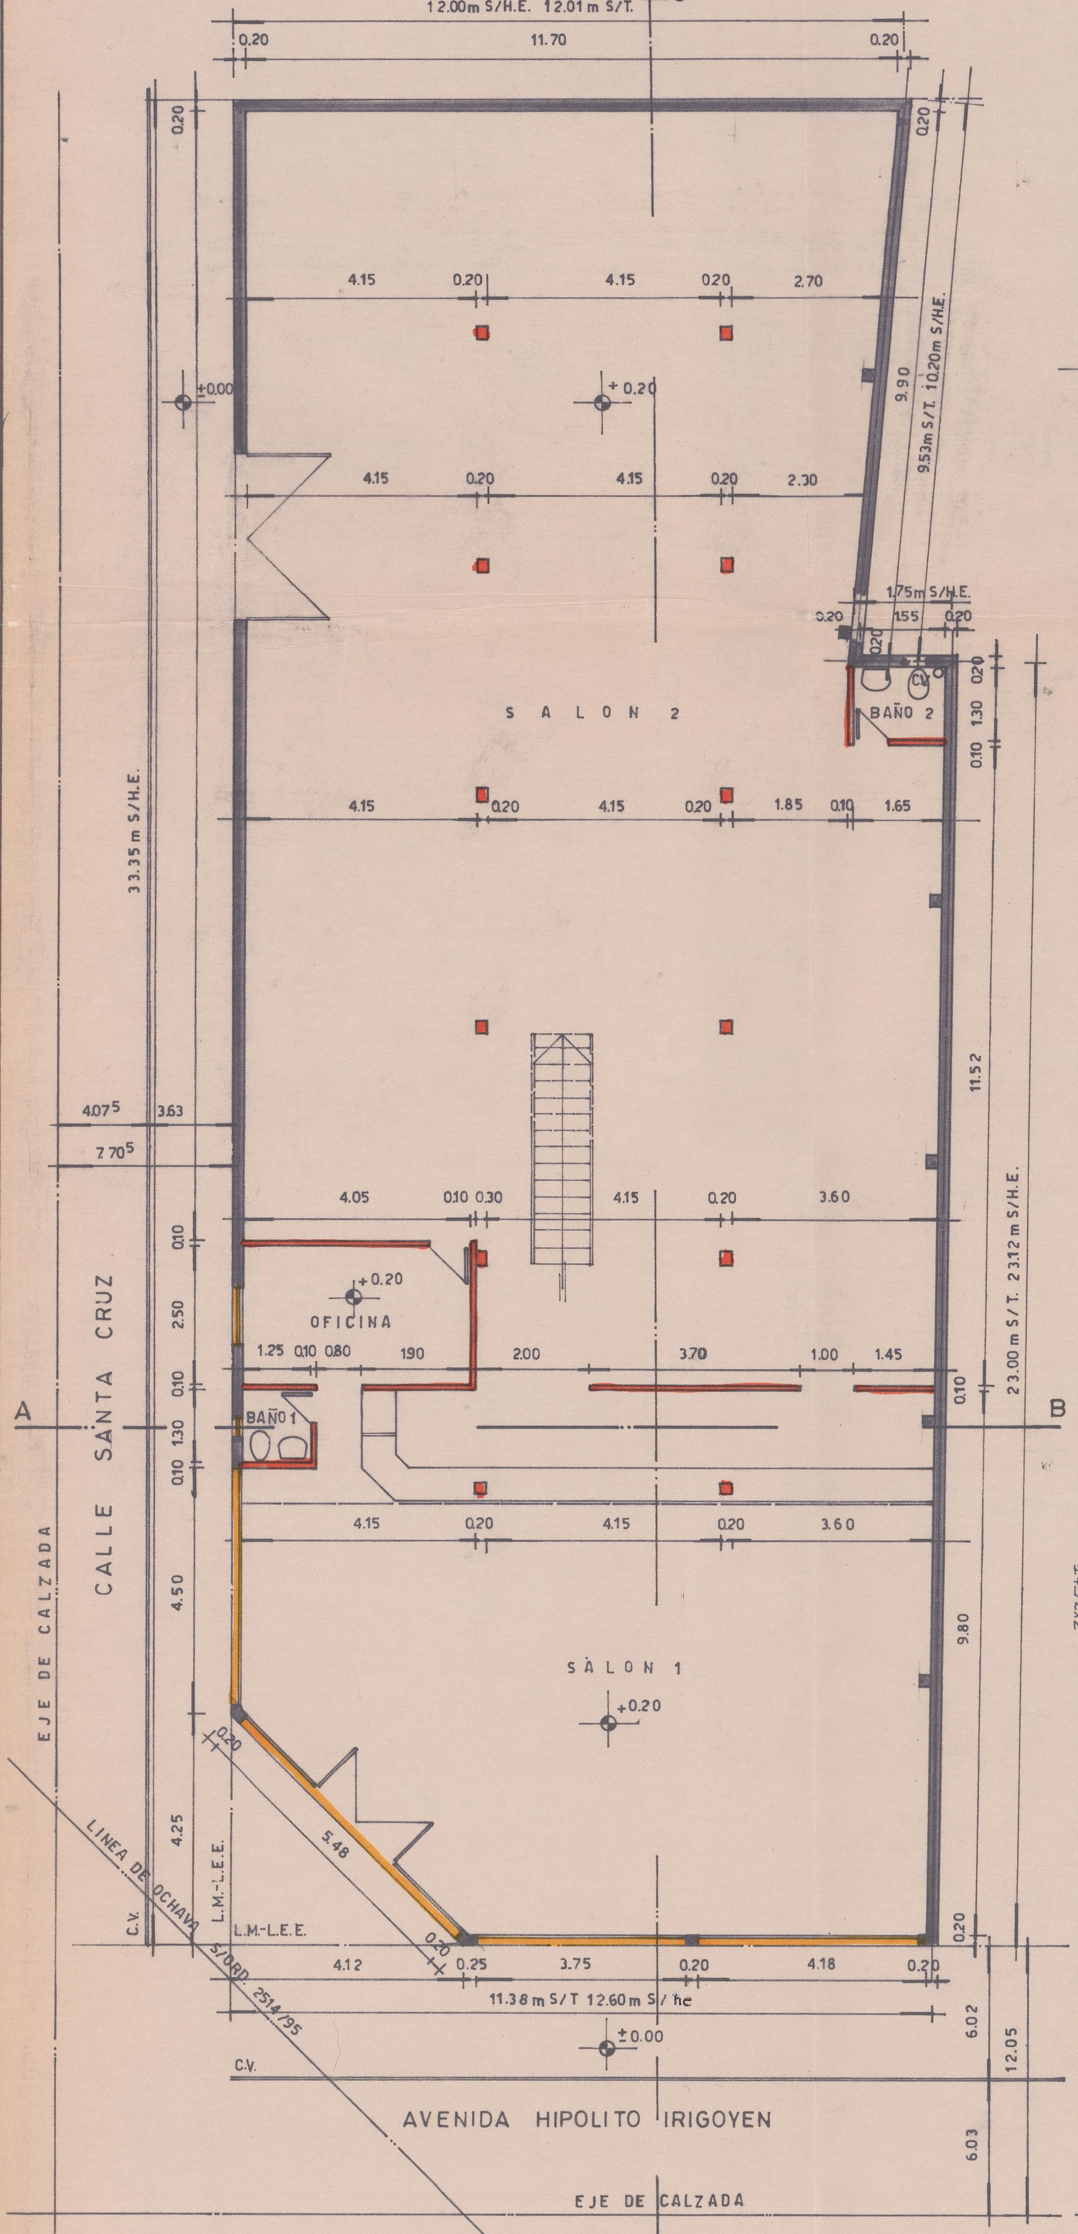

PLANTA BAJA

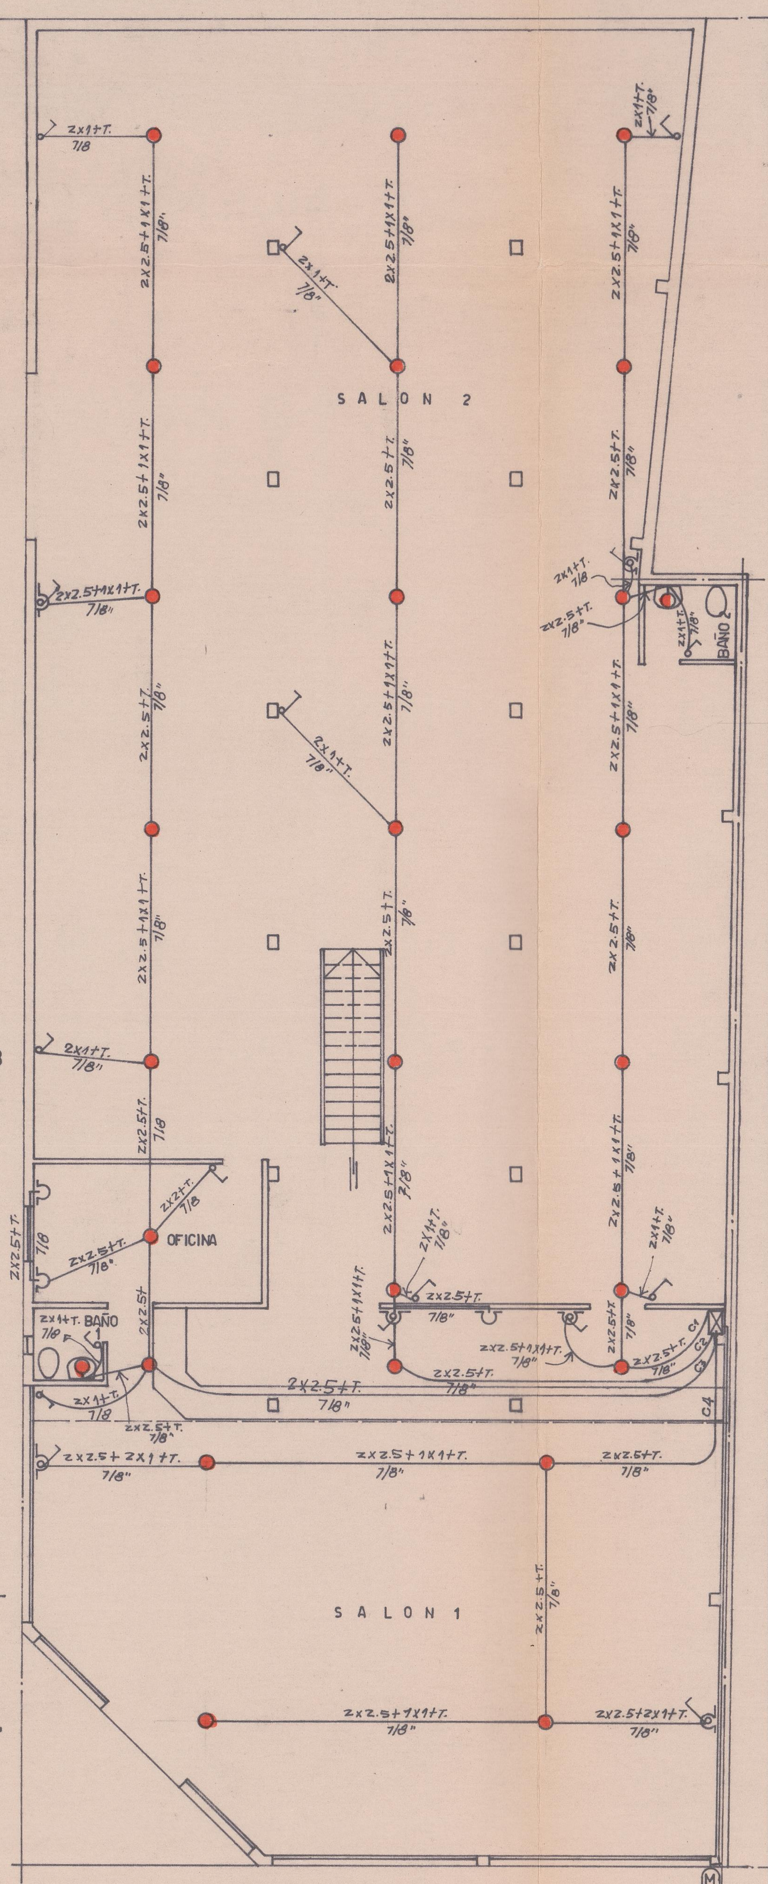

PLANTA BAJA DE ELECTRICIDAD

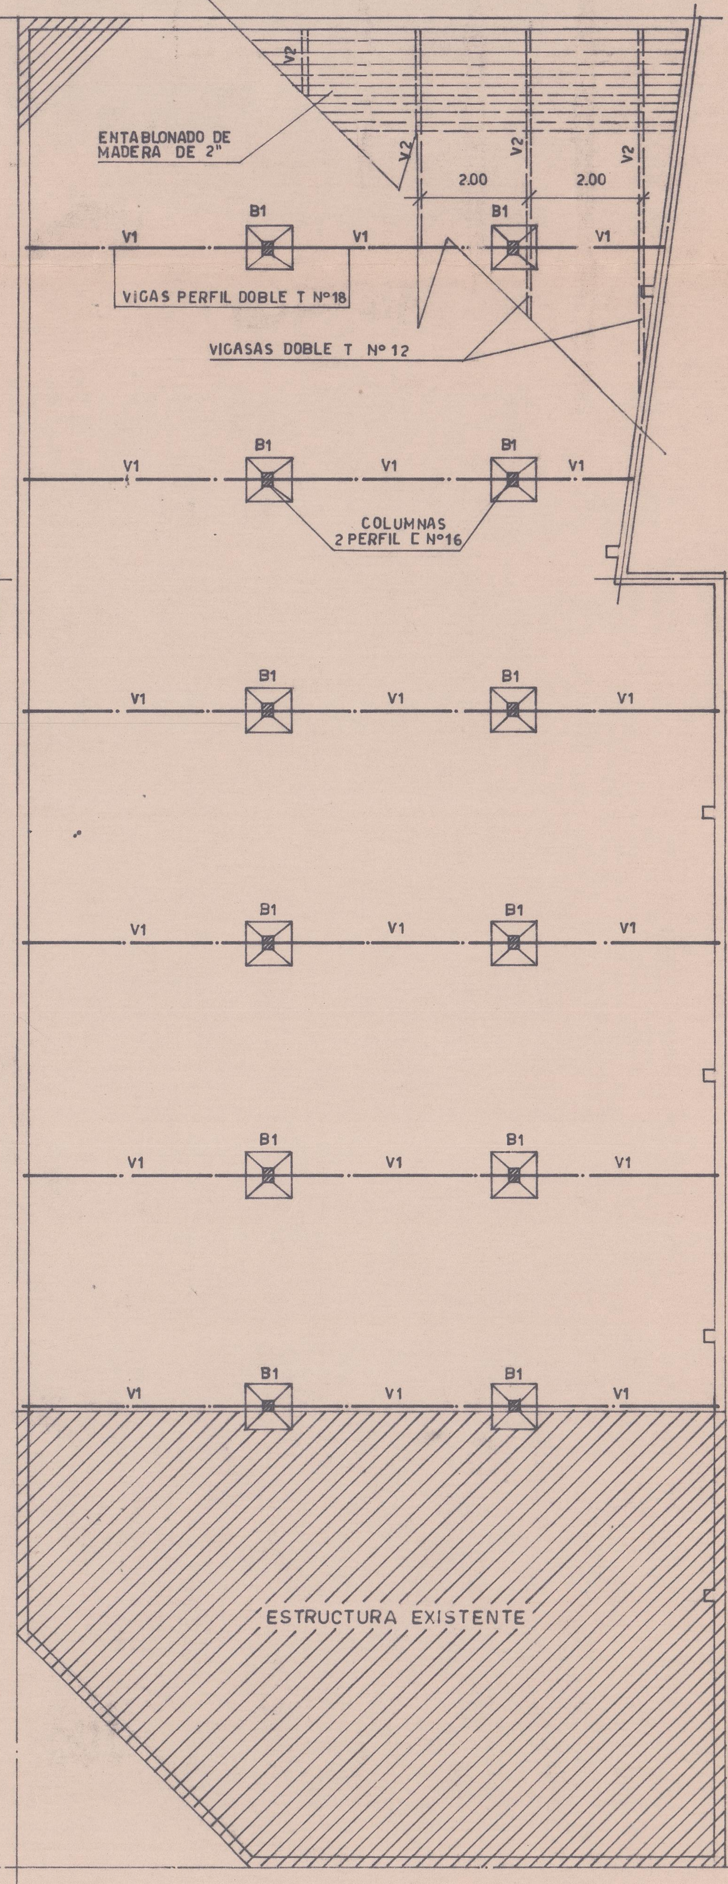

PLANTA BAJA DE ESTRUCTURA - ENTREPISO

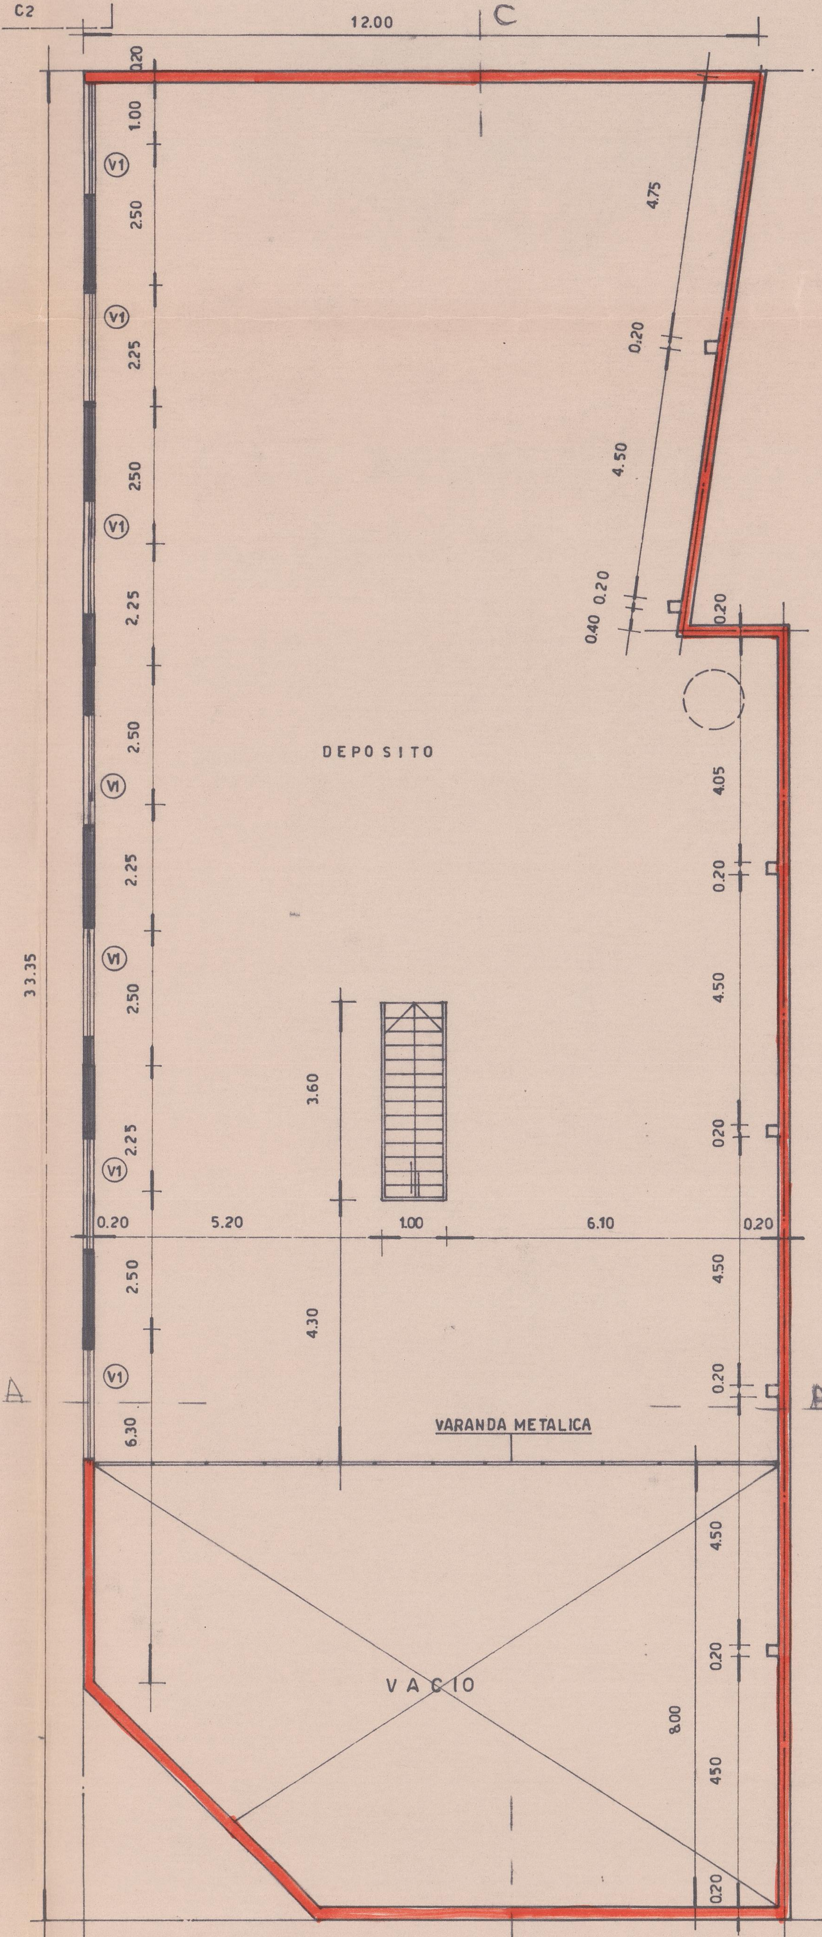

PLANTA ENTREPISO

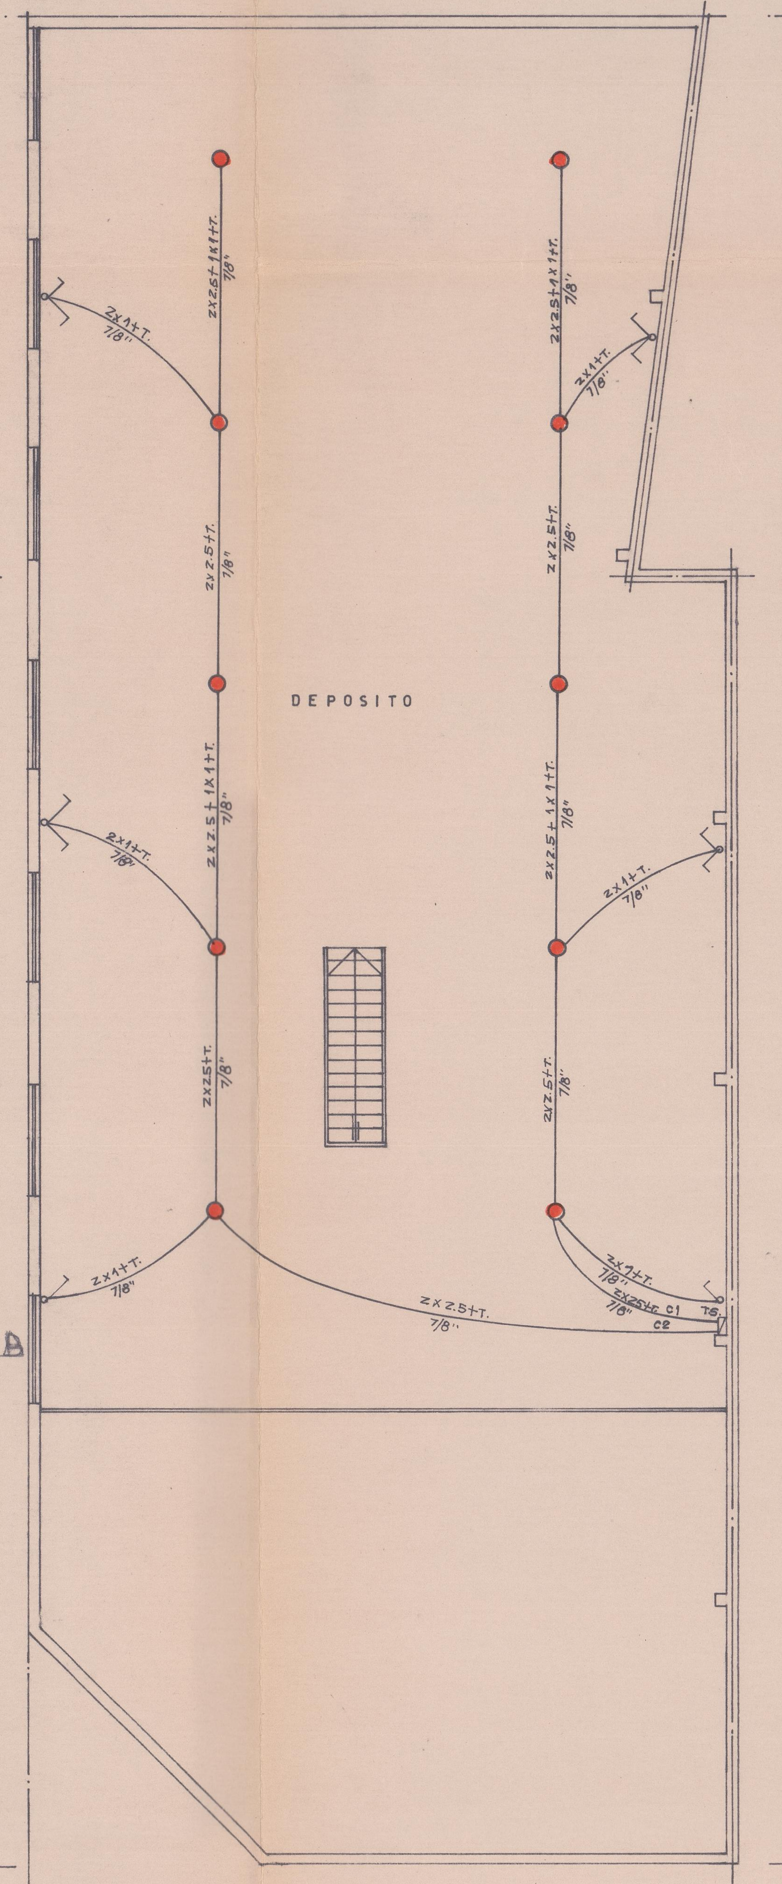

PLANTA ENTREPISO DE ELECTRICIDAD

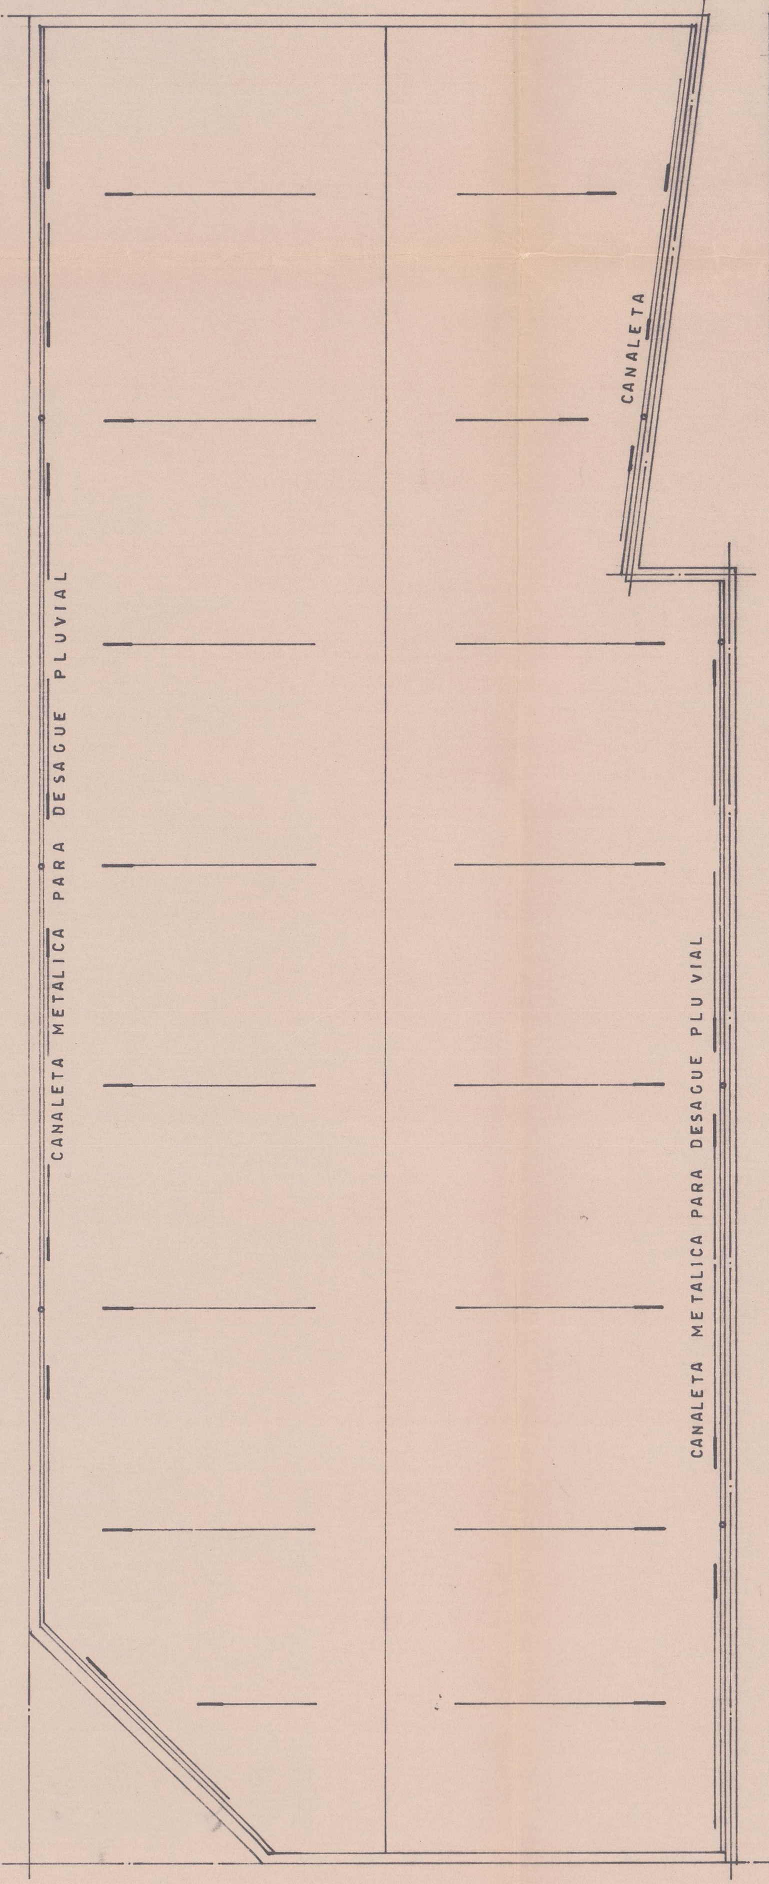

PLANTA DE TECHO EXISTENTE

DETALLE DE ENTABLONADO

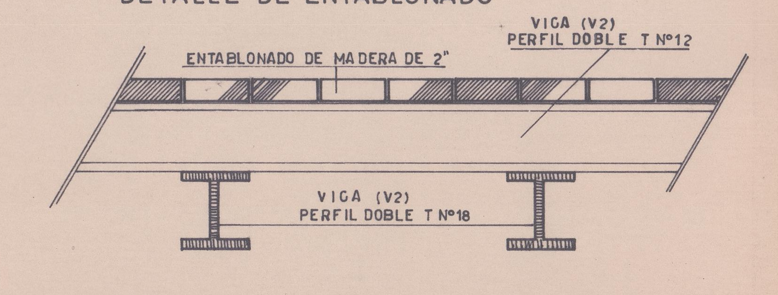

DETALLE BASE Y COLUMNA

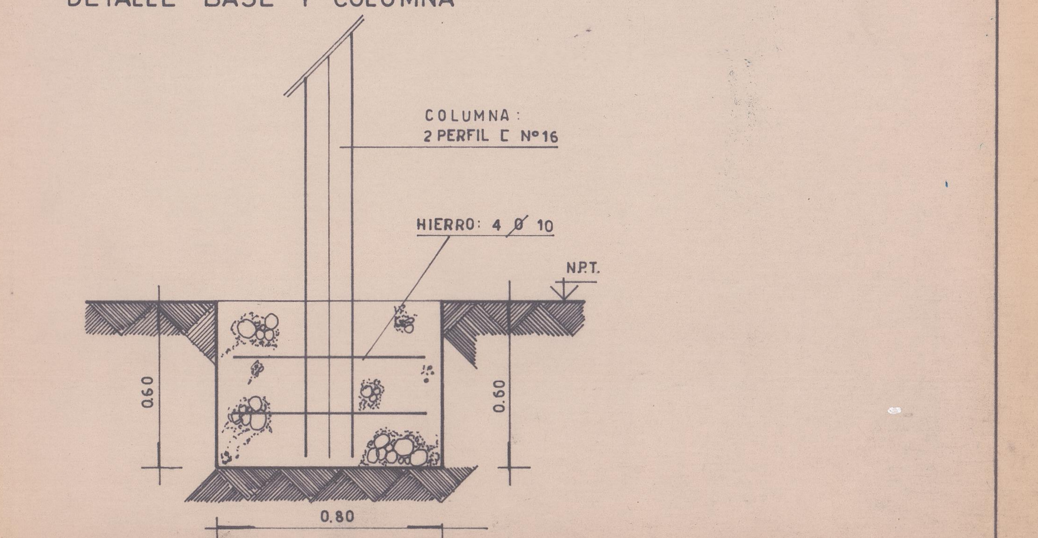

PLANILLA DE ILUMINACION Y VENTILACION

LOCAL DESIGNACIONES	LOCAL SUPERFICIES	ABERTURAS DESIG.	ABERTURAS ANCHO	ABERTURAS ALTO	AREAS I.	AREAS V.	OBSER.
SALON 1	108.86	V1	1.80	2.00	7.20	7.20	CANT. 2
"	"	P1	2.00	2.00	4.00	4.00	
BAÑO 1	1.62	V2	0.30	0.30	0.09	0.09	
OFICINA	10.12	V3	1.20	1.00	1.20	1.20	
SALON 2	250.98	P2	3.00	2.50	7.50	7.50	I. Y V. INSUF.
BAÑO 2	2.14	C.V	0.10	010	0.01	0.01	
DEPOSITO (Entrepiso)	287.07	V1	2.10	2.00	2940	2940	CANT. 7

DETALLE DE OCHAVA

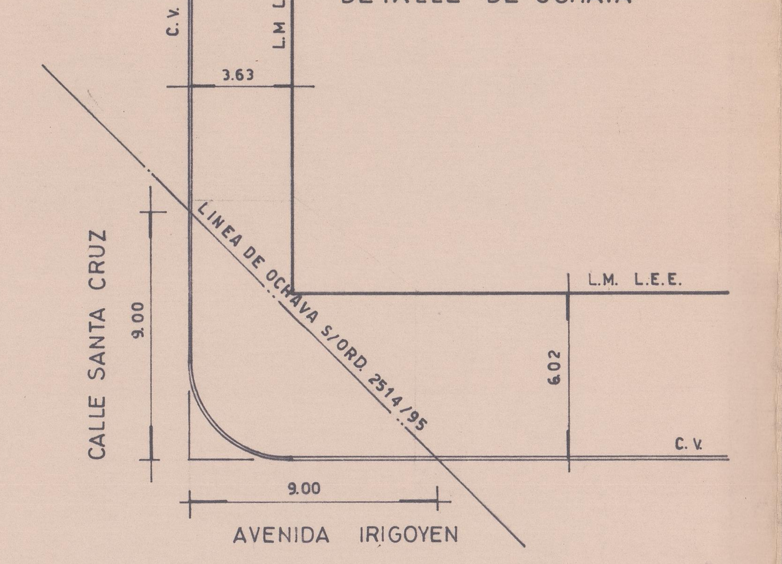

DETALLE DE CANALETA

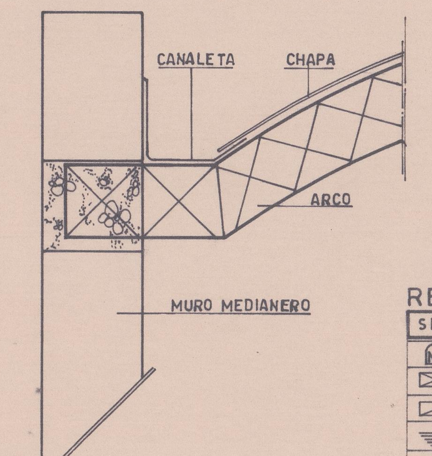

REFERENCIAS

SIG.	DESIGNACIONES
	MEDIDOR
	TABLERO GENERAL
	TABLERO SECUNDARIO
	TOMA A TIERRA
	CENTRO DE LUZ
	BRAZO DE LUZ
	TOMA CORRIENTE
	LLAVE Y TOMA
	LLAVE DE 1 PUNTO
	LLAVE DE COMBINACION
	PULSADOR
	CAMPANILLA P/ TIMBRE

DIST. 3 ZONA 3 MZA. 36 PARC. 180/181
Padron Inmobiliario Nº 1-1-39381 1-1-39382 Dominio Nº 7N-1575 Y 7N-1577 _ 29/11/04

Destino de la Obra: LOCAL COMERCIAL CON DEPOSITO DE AUTOPARTES._

PROPIEDAD DE: CALCHA S.A.

UBICACION: AVENIDA HIPOLITO IRIGOYEN Nº 806 ESQ. CALLE SANTA CRUZ Nº 250._

BARRIO: DR. JUAN BAUTISTA ALBERDI

CIUDAD: CAPITAL - SANTIAGO DEL ESTERO

ESCALA: 1:100 - 1:200 -

SUP. TERRENO 398.37 m2 S/H.E.
SUP. CUBIERTA PLANTA BAJA 398.37 m2
SUP. CUBIERTA PLANTA DE ENTREPISO 306.32 m2
SUP. CUBIERTA F.L.M. ——
SUP. CUBIERTA TOTAL 704.69 m2

CROQUIS DE UBICACION

CALLE BOLIVIA — CALLE ABSALON ROJAS — AVENIDA HIPOLITO IRIGOYEN — CALLE SANTA CRUZ
1_9.53 m s/t - 10.20 ms/h.e.
2_1.75 m s/h.e.
23.92
23.00 ms/t. 23.12 m s/h.e.
12.00 ms/h.e. 12.01 m s/t.
11.38 ms/t. 12.60 ms/h.e.
33.35 m s/h.e.
14.96

PROPIETARIO Domicilio
RELEVAMIENTO Domicilio
PROYECTO Domicilio
DIRECCION TECNICA Domicilio
INSTALACION ELECTRICA Domicilio
CATEGORIA COLEGIO DE ARQUITECTOS

	S/H. IRIGOYEN	S/SANTA CRUZ
ANCHO DE VEREDA	6.02 m	3.63 m
ANCHO DE CALZADA	12.06 m	8.15 m
ANCHO DE CALLE	23.92 m	14.96 m

PAVIMENTO: SI
SERVICIOS CLOACALES: NO

DESIGNACION

PLANO DE MODIFICACION Y AMPLIACION

OBSERVACIONES

0 2 MAR 2005
Las referencias al Titulo de Dominio son meramente indicativas, y la aprobación administrativa no valora los derechos que de ellos emergen.
CARLOS EDUARDO BANCO
Ing. Agrimensor
Dirección de Suelo Urbano

DIRECCION DE SUELO URBANO
ORD. AMNISTIA 2659/96
DCTO. 25. P. 00

MUNICIPALIDAD DE LA CIUDAD DE SANTIAGO DEL ESTERO
SECRETARIA DE PLANEAMIENTO Y DESARROLLO URBANO
APROBADO
DIRECCION DE SUELO URBANO
EXPEDIENTE: 3-C-05.
FECHA: 04 MAR. 2005

Ing. LUIS ALBERTO LUNA
Encargado Area Suelo Urbano
MUNICIPALIDAD DE LA CAPITAL

PERMISO DE COMIENZO DE OBRA Nº 2395.

COLEGIO DE ARQUITECTOS
Legajo 050141
RELEVAMIENTO PROYECTO DIRECCION DE OBRA
Fecha 18 FEB. 2005
Vo. Bo. Colegio de Arquitectos

Municipalidad de La Capital
Sgo. del Estero
SECRETARIA DE PLANEAMIENTO Y DESARROLLO URBANO
DIRECCION DE SUELO URBANO

CARLOS GIAMBRONI
ARQUITECTO

DIRECCION DE SUELO URBANO
EXPEDIENTE 3-C-05
FECHA DE SELLADO 21/02/05
BOLETA 1765