
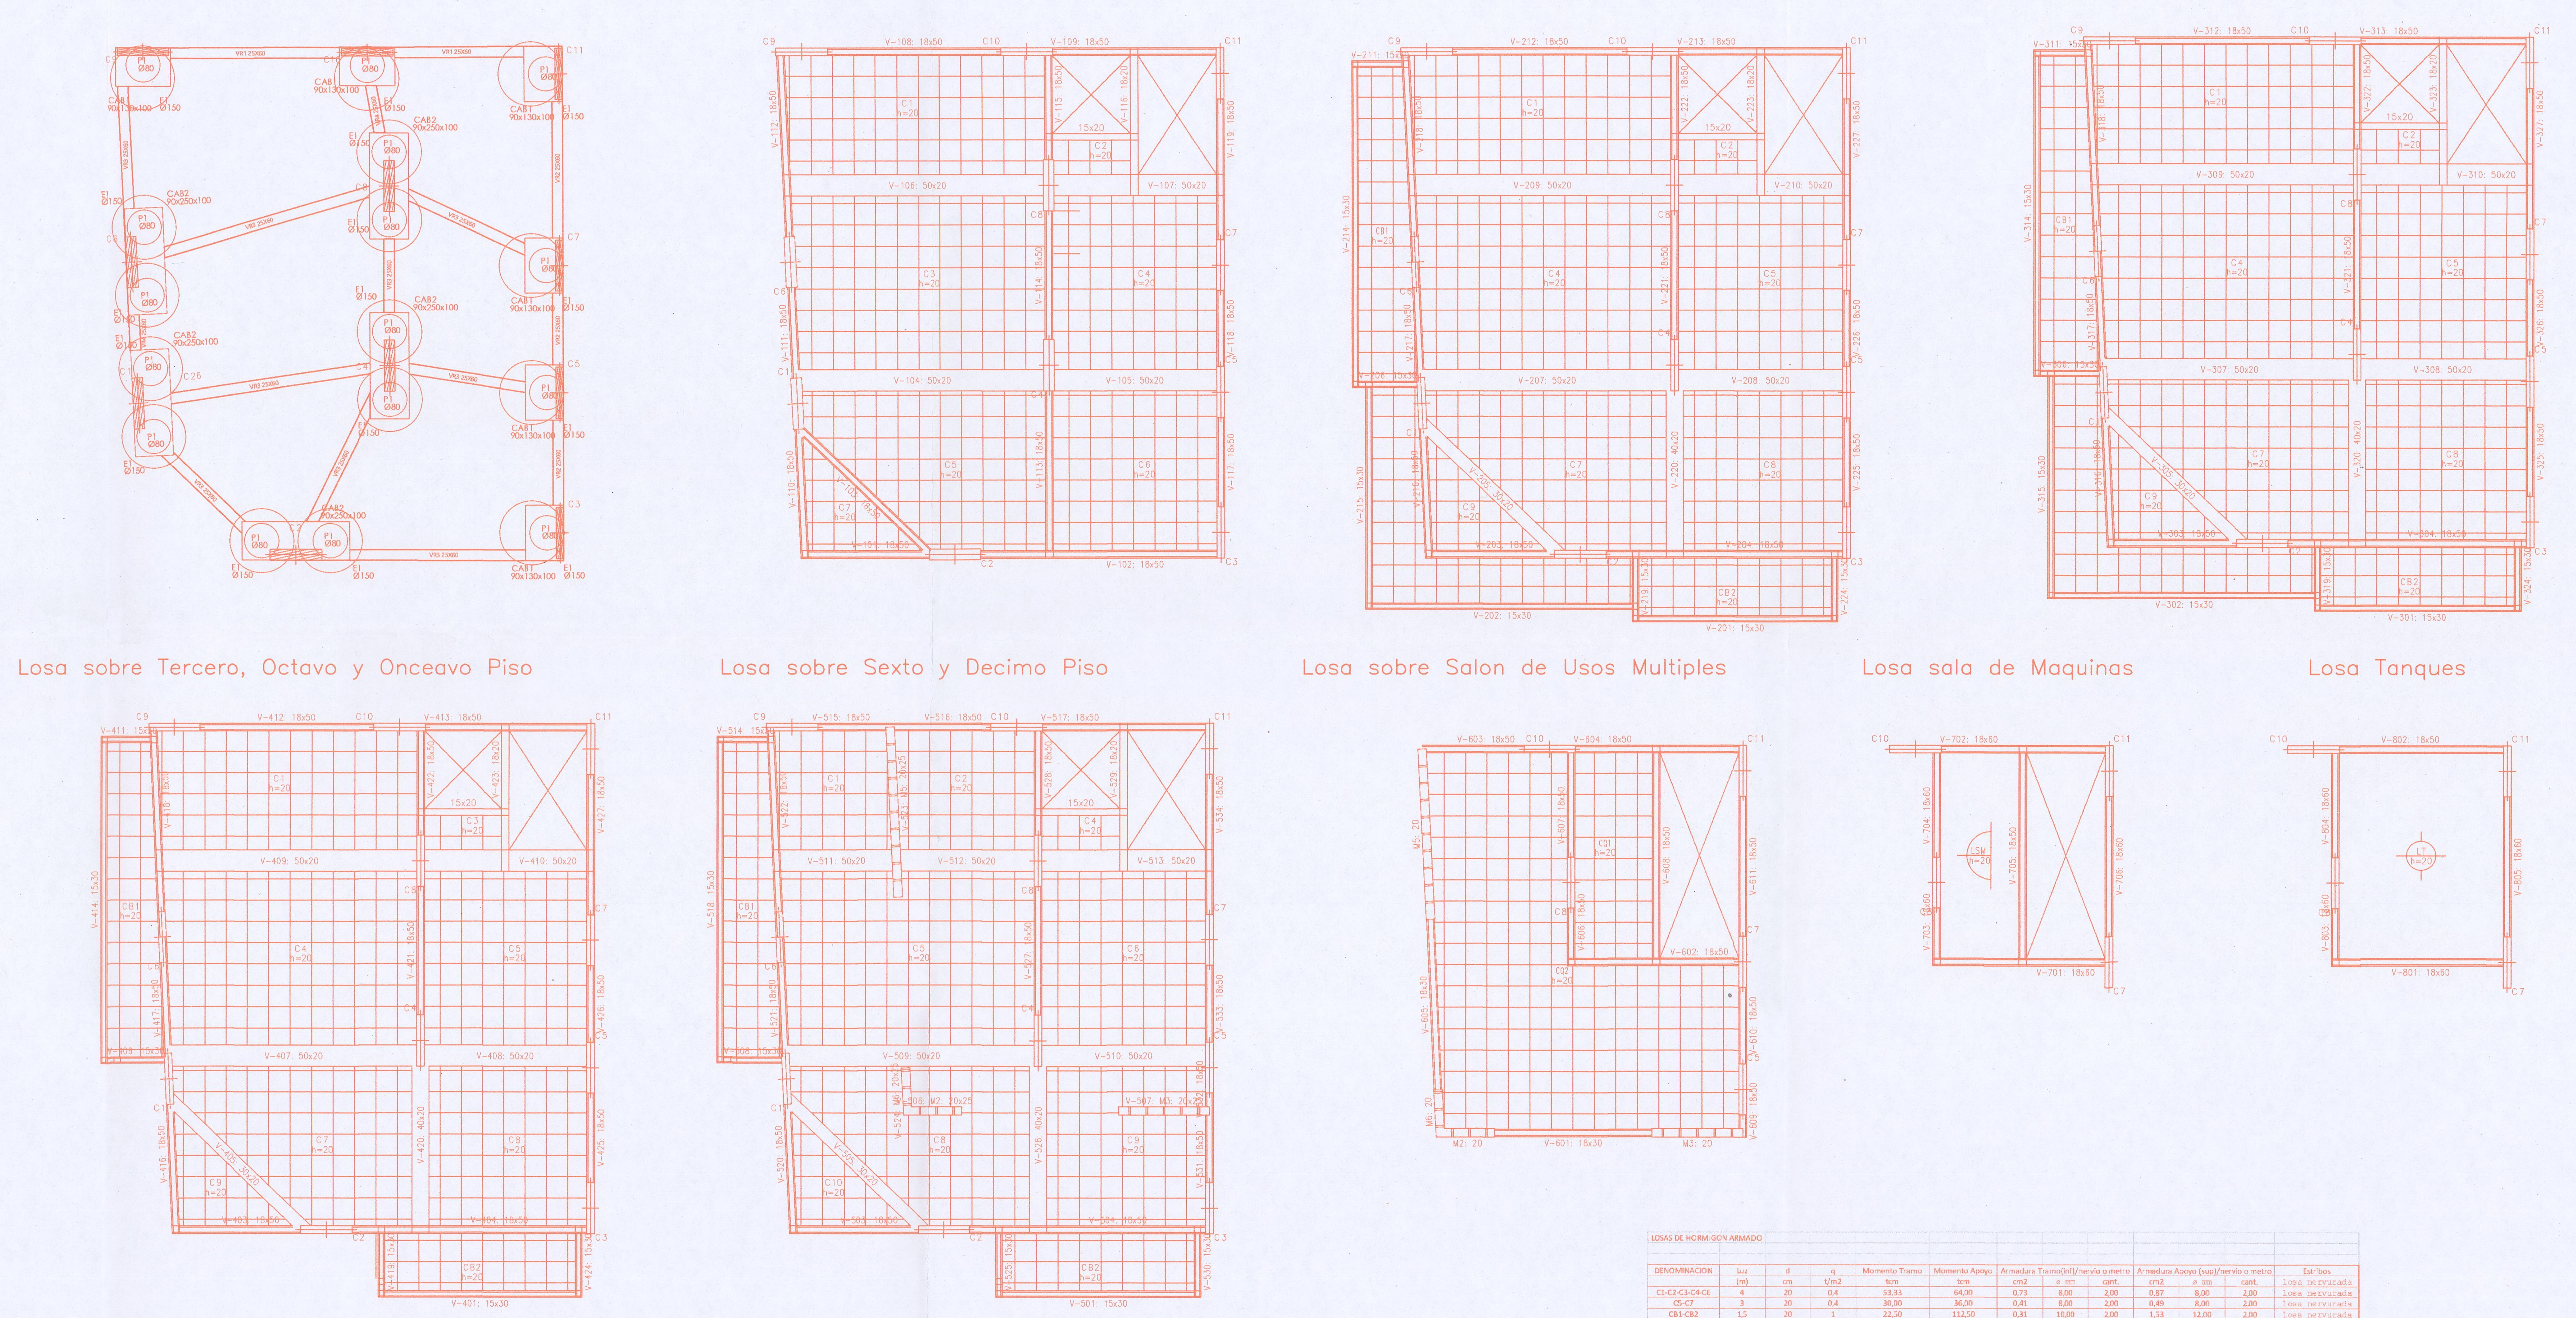


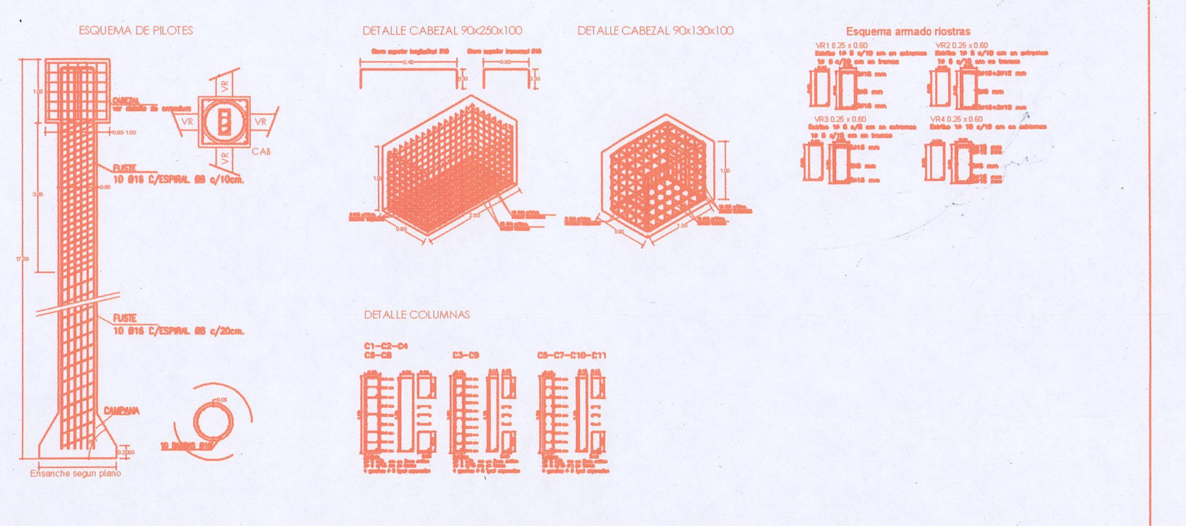

NOTA PILOTES

(1) SE UTILIZARA ARMADURA HELICOIDAL DENSIFICANDO LOS PRIMEROS 3 m

DISTRITO 03	ZONA 03	MANZANA 040	PARCELA 260/261	LEY 4683 CPIA OT 1646723
PADRÓN INMOBILIARIO 0101014630	DOMINIO: 7N-12803	ICM: 100-C-25		

DESTINO DE LA OBRA: EDIFICIO DE DPTOS. Y 1 LOCAL COMERCIAL

POSEEDOR: COMMUNITY S.R.L. CUIT: 30-71833201-6

PERMUTA DE INMUEBLE POR UNIDADES A CONSTRUIR CELEBRADO ANTE CARMEN VENEGAS DE KARAM, ESCRIBANA ADSCRIPTA AL REGISTRO NOTARIAL N° 11

UBICACIÓN: Av. ALVEAR N°203 ESQ. CALLE ABSALON ROJAS S/N°

BARRIO: JUAN BAUTISTA ALBERDI

CIUDAD: SANTIAGO DEL ESTERO (CAPITAL)


ESCALAS: 1:100 1:200

SUP. DEL TERRENO S/P121.56M2: , S/HE: 121.56M2

VER PLANILLA DE SUP

SUP. CUBIERTA TOTAL 1634.35M2

CROQUIS DE UBICACIÓN

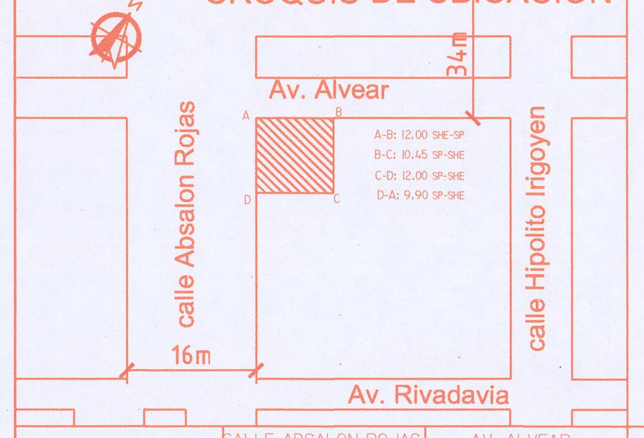

	CALLE ABSALON ROJAS	AV. ALVEAR
ANCHO DE CALLE	16.00M SP-SHE	34.00 SP-SHE
ANCHO DE CALZADA	9.03M SP-SHE	6.00M SP-SHE
ANCHO DE VEREDA	3.43M SP-SHE	4.74M SP-HE

POSEEDOR
DOMICILIO

COMMUNITY SRL
RAMIRO SALGADO
Socio Gerente

PROYECTO
DOMICILIO

MUNAR JUAN PABLO
INGENIERO CIVIL
M.P. 200.076

DIRECCIÓN TÉCNICA
DOMICILIO

CATEGORÍA

PAVIMENTO	SI
SERVICIOS CLOACALES	SI

DESIGNACIÓN

PLANO DE OBRA NUEVA

ESTRUCTURA

OBSERVACIONES

19 JUN 2025

Las referencias al Titulo de dominio son meramente indicativas, y la aprobación administrativa no valora los derechos que de ellos emergen

Ing. Agrim. J. LEANDRO ARJONA
JEFE DE AREA DE VISACIONES TECNICAS
DIRECCION DE CATASTRO MUNICIPAL

PERMISO DE COMIENZO DE OBRA N° 174/2025 24/06/2025
DIRECCION DE SUELO URBANO

Arq. ABRAHAM BERNARDO ROMINA
Dpto. OBRAS PRIVADAS
DIRECCION DE SUELO URBANO

MUNICIPALIDAD DE LA CIUDAD DE SANTIAGO DEL ESTERO
SECRETARIA DE ECONOMIA
APROBADO
DIRECCIÓN DE SUELO URBANO
EXPEDIENTE: 232-31-2025-Carp-09-C-2025
FECHA: 15 JUL 2025

Arq. Cesar Marcelo Alcorta
Director D.S.U.
Municipalidad de la Capital

SECRETARIA DE ECONOMIA
Municipalidad de la Capital
SGO. DEL ESTERO
DIREC. DE SUELO URBANO

DIRECCION DE SUELO URBANO
EXPEDIENTE 232 31 25
FECHA 12 JUN 2025
BOLETA 856

EL USO Y/O DESTINO DE LOS LOCALES ESTA SUJETO A LAS DISPOSICIONES DE LA ORDENANZA N° 796/82 CAPITULO 3.

DIRECCION DE SUELO URBANO
EXPEDIENTE 232 31/25
FECHA DE SELLADO 03 JUL. 2025
BOLETA N° 952