


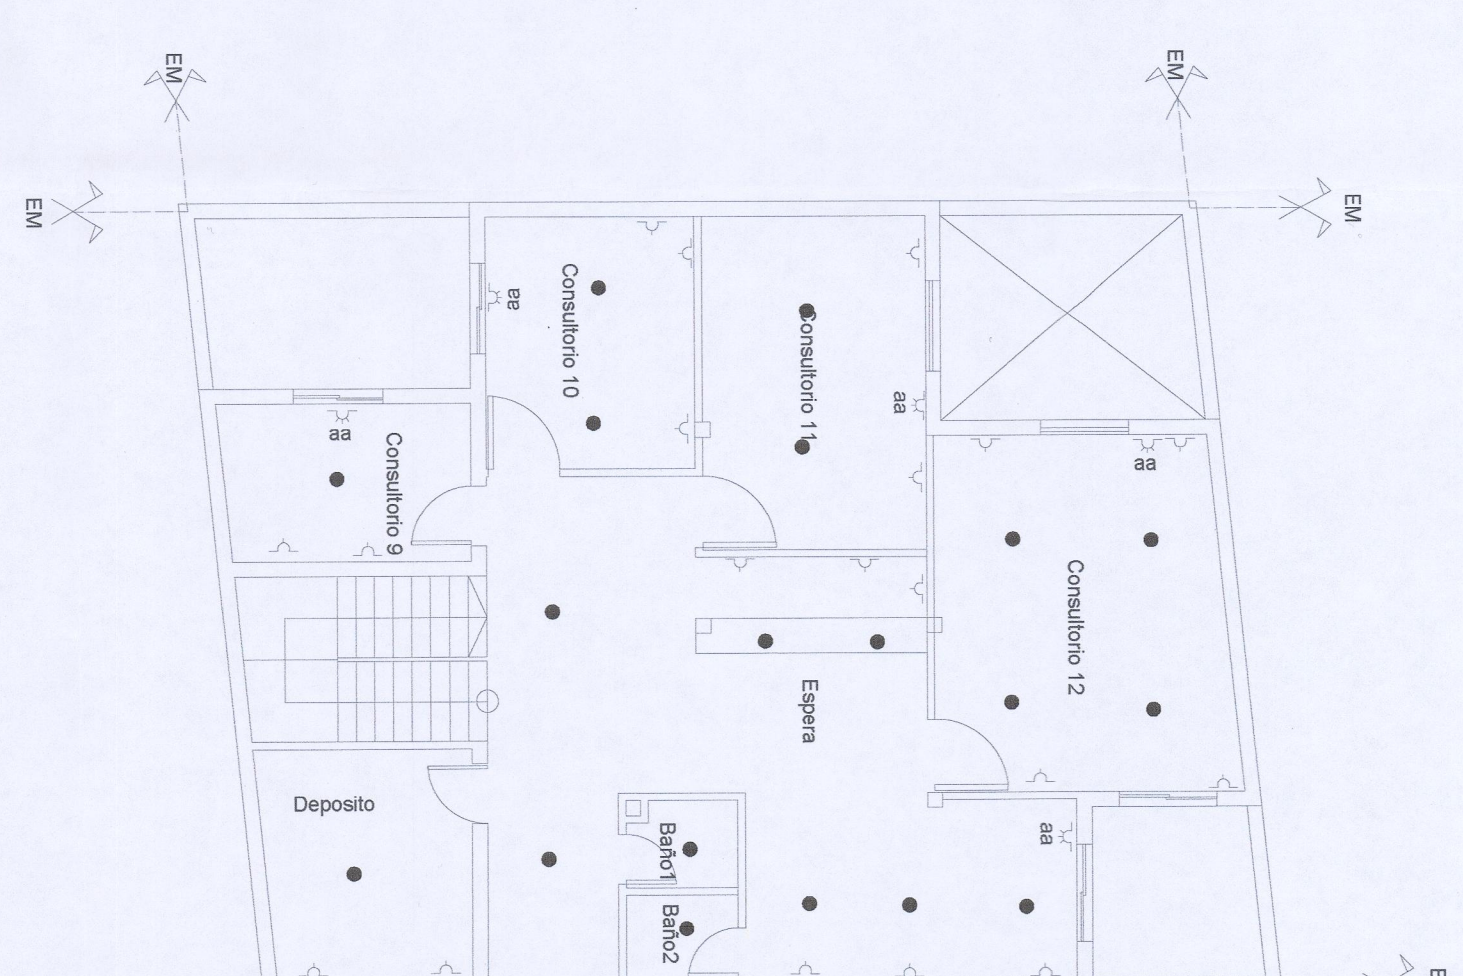

AV. ABSALON ROJAS

PLANTA 1
PISO

PLANTA 2º PISC

PLANTA 3º PISC

CORTE B-B

CORTÉ A-A

FACHAD

Las referencias al régimen dominicano son meramente indicativas y la aprobación administrativa no valora los derechos que de ellos emergen.

SECRETARIA DE ECONOMIA

APROBADO

DIRECCION DE SUELO URBANO

INSTRUMENTO: 279-31-2024 CORP. 41-D-202

FECHA: 27/11/2025

EL USO Y/O DESTINO DE LOS LOCALES
ESTA SUJETO A LAS DISPOSICIONES DE
LA ORDENANZA N° 796/82 CAPITULO 3.

[illegible][illegible]

DIST.: 03 ZONA: 03 MANZ.: 41 PARC.: 100 LEY 4683
 PADRON INMOB.: 1-1-04848 I.C.M.: 125-D/12 DOMINIO: 7N-1485
 7N-6925
 DEST. DE LA OBRA: CONSULTORIOS - DEPARTAMENTOS (17) 220263
 PROPIETARIOS: ALBERTO SANCHEZ JOZANI

0.93 0.30 2

13.93

2,10 0,5

3,69