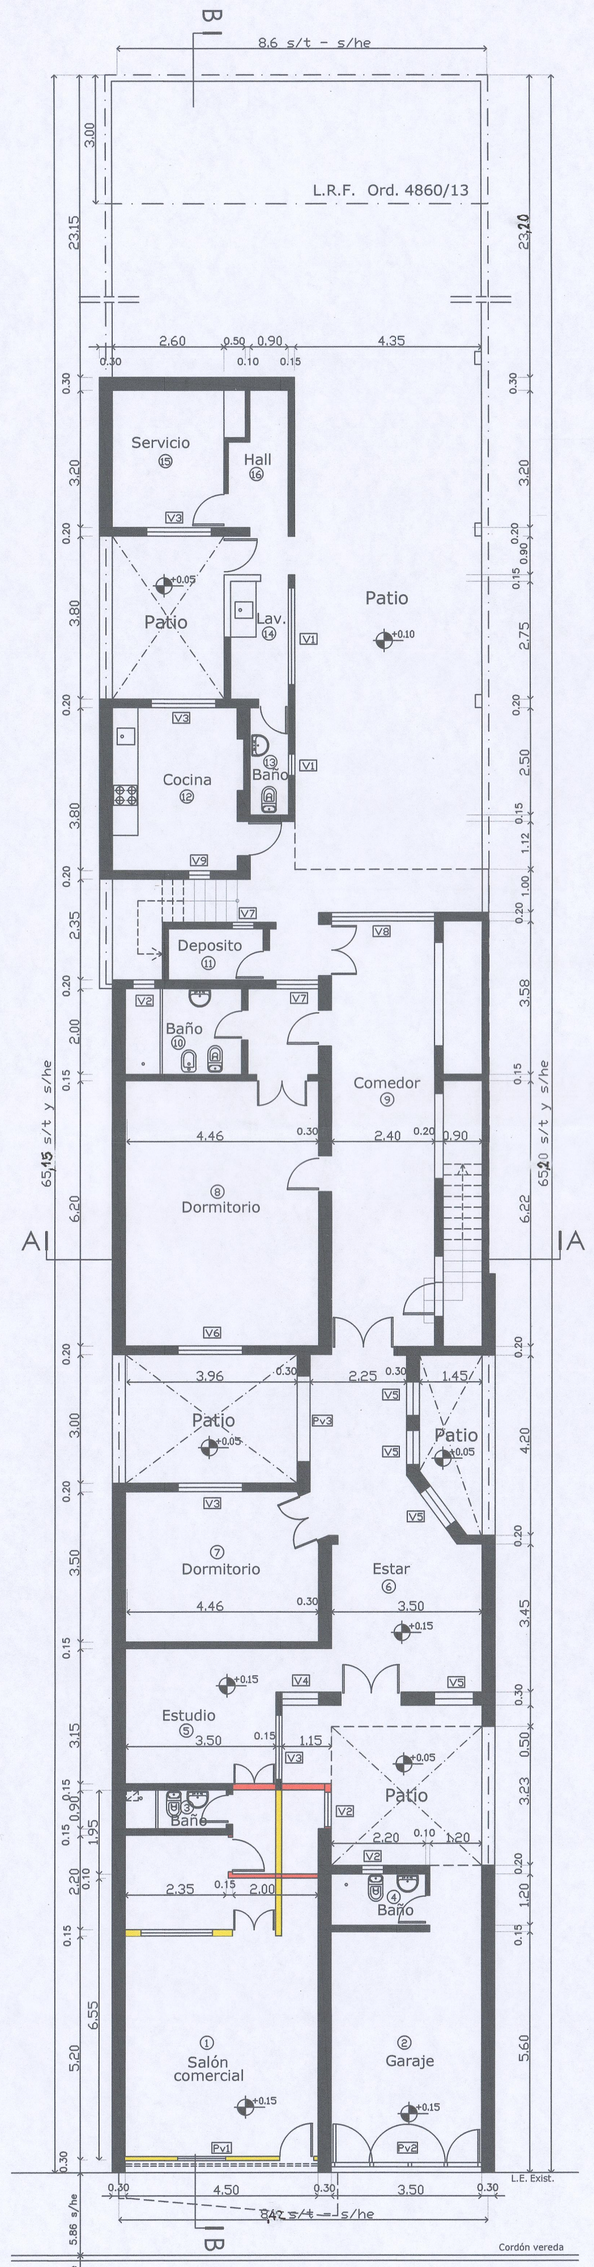

PLANTA Esc. 1:100

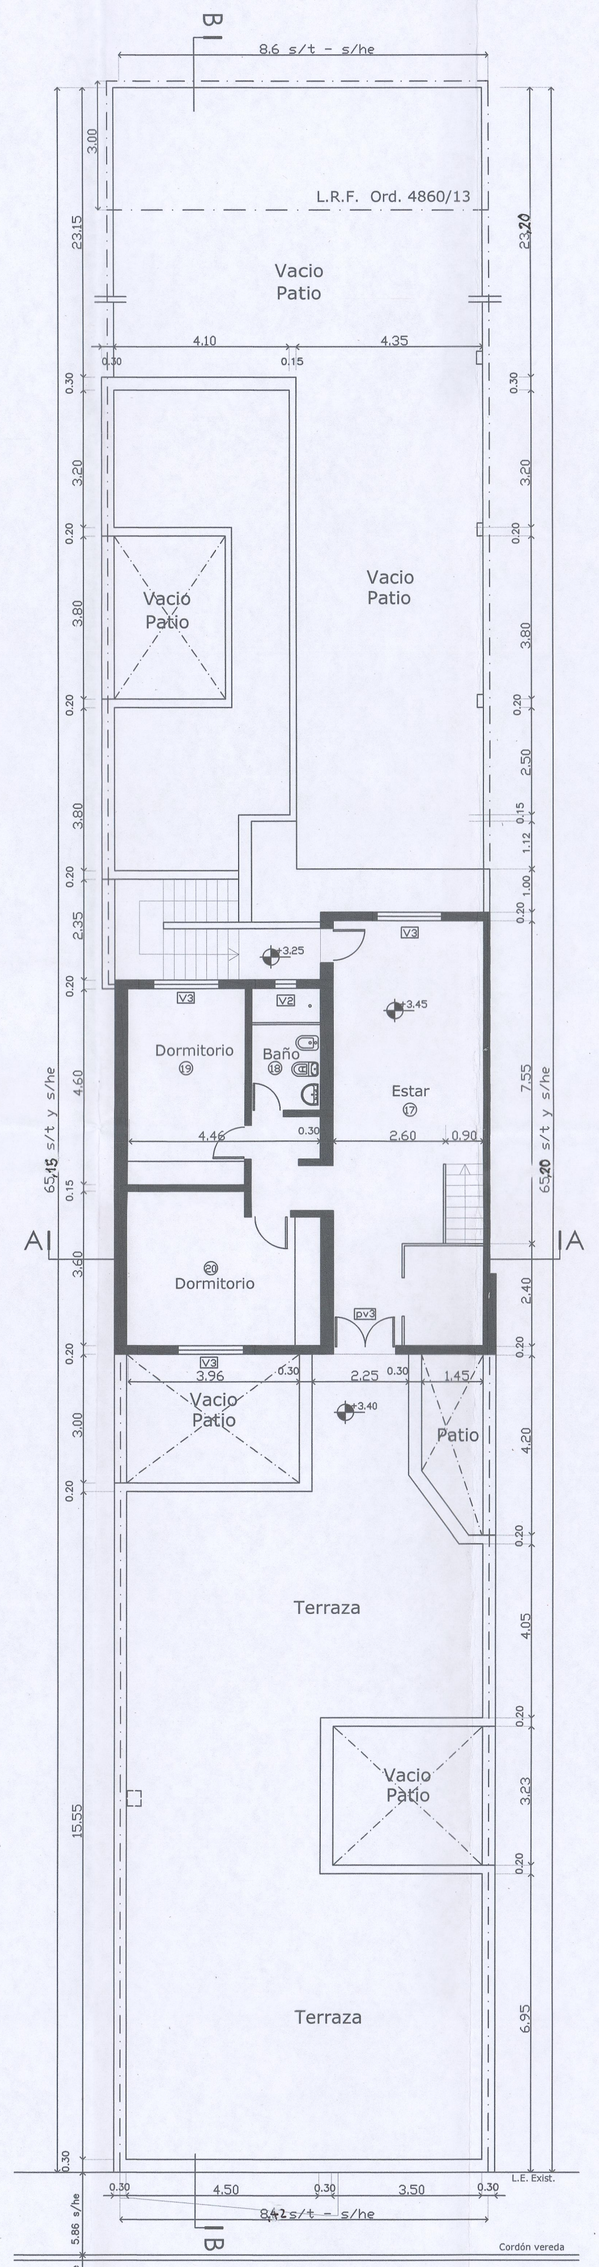

PLANTA ALTA Esc. 1:100

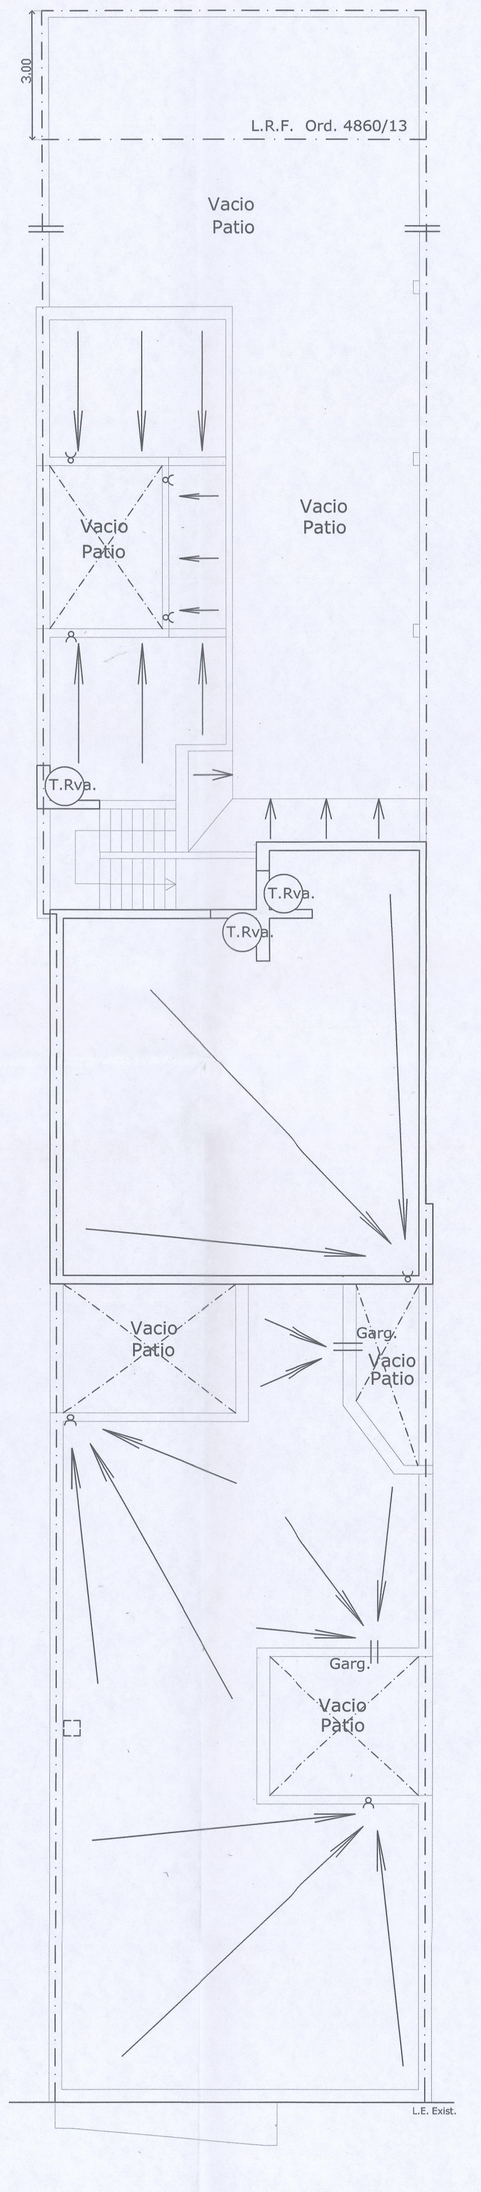

PLANTA DE TECHO Esc. 1:100

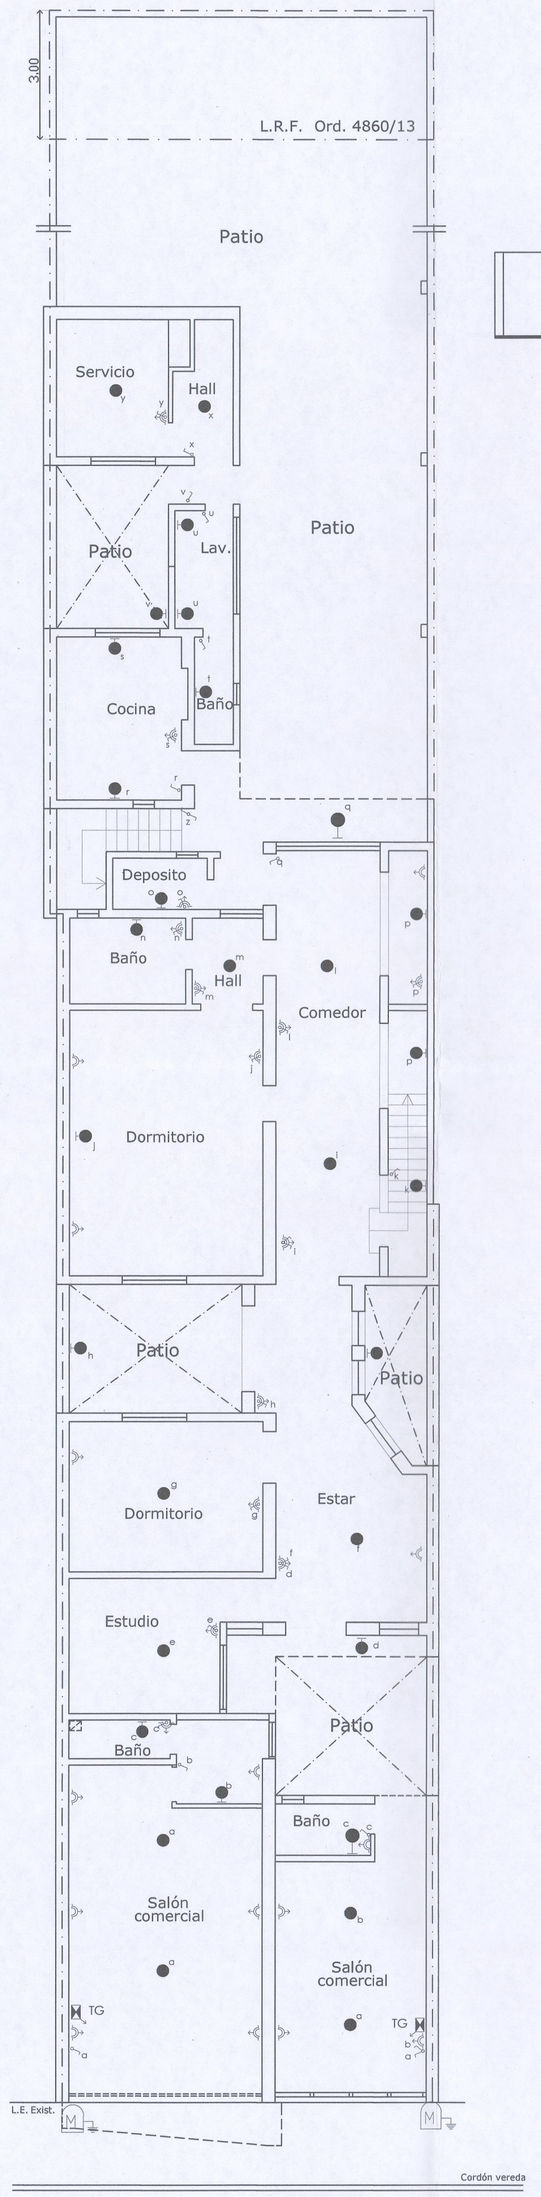

INST. ELECTRICA P.B. Esc. :100

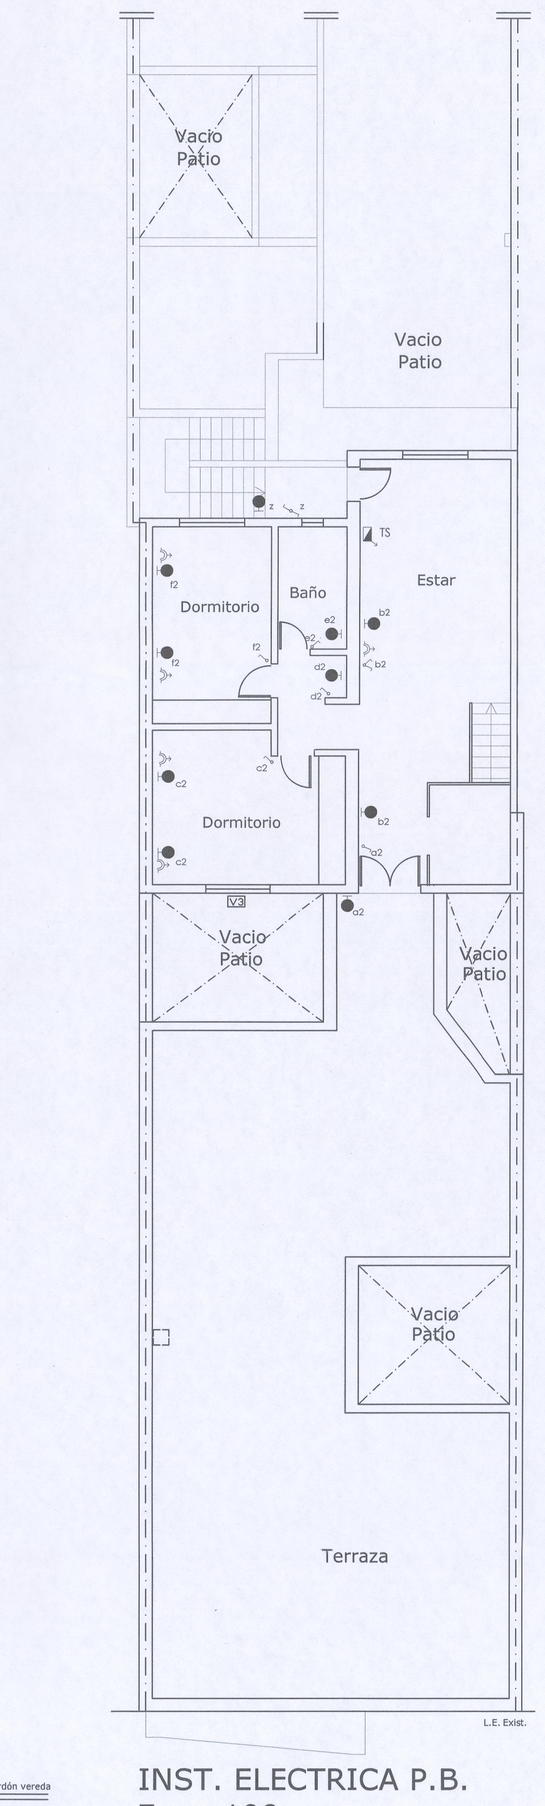

INST. ELECTRICA P.B. Esc. :100

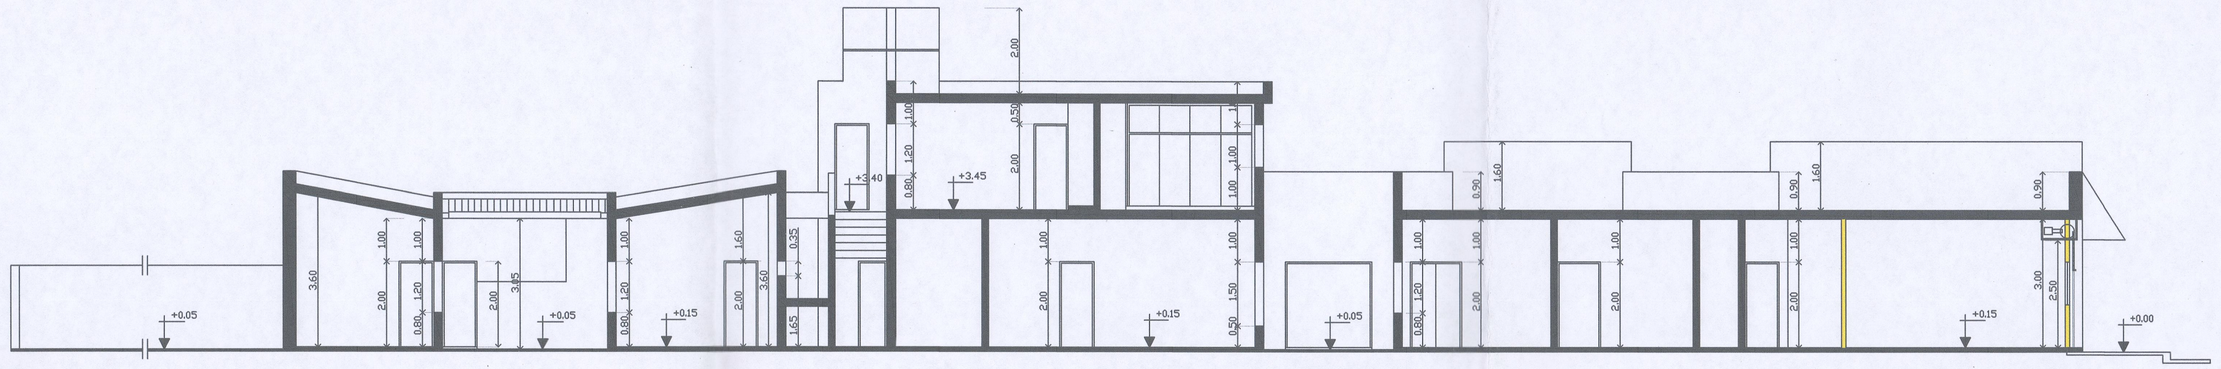

CORTE B-B Esc. 1:100

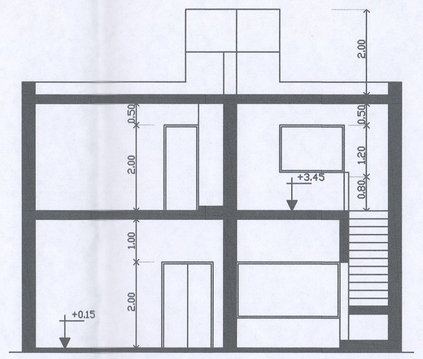

CORTE A-A Esc. 1:100

PLANILLA DE ILUMINACION Y VENTILACION

LOCAL			ABERTURAS					OBSERVACIONES
Desig. del Local		Sup. m2	Desig.	Ancho	Alto	Areas I	Areas V	
Salon comercial	(1)	33.07	Pv1	4.50	2.50	11.25	11.25	Cortina autom.
Garaje	(2)	18.04	Pv2	3.50	3.00	10.50	10.50	Porton Ventana
Baño	(3)	2.11	C1	0,30	0,40	0.12	0.12	Cond. ventilacion
Baño	(4)	2.64	V2	0,50	0,40	0.20	0.20	Ventiluz
Estudio	(5)	12.25	V3	1,50	1,20	6.78	6.78	Puerta ventana y Ventana
Estar	(6)	14.89	V4	1,90	1,20	6.16	6.16	2 Ventanas
Dormitorio	(7)	15.75	V3	1,50	1,20	1.80	1.80	Ventana
Dormitorio	(8)	27.90	V6	2,00	1,50	3.00	3.00	Ventana
Comedor	(9)	23.88	V8	2,40	1,40	3.36	3,36	Ventana
Baño	(10)	5.40	V2	0,50	0,40	0,20	0,20	Ventiluz
Deposito	(11)	2.64	V2	0,50	0,60	0,30	0,30	Ventiluz
Cocina	(12)	11.02	V4	1,90	1,20	2.10	2.10	2 Ventanas
Baño	(13)	2.25	V2	0,50	0,40	0,36	0,36	Ventiluz
Lavadero	(14)	3.75	V8	2,40	1,40	3.36	3.36	Ventana
Servicio	(15)	0.32	V3	1,50	1,20	1,80	1,80	Ventana
Hall	(16)	3.20	-	0,90	2,00	1,80	1,80	-
Estar	(17)	34.82	V3	1,50	2,10	4,95	4,95	Puerta ventana y Ventana
Baño	(18)	4.56	V11	0,80	0,60	0,48	0,48	Ventiluz
Dormitorio	(19)	11.00	V3	1,50	1,20	1,80	1,80	Ventana
Dormitorio	(20)	13.35	V3	1,50	1,20	1,80	1,80	Ventana

PLANIMETRIA Esc. 1:200

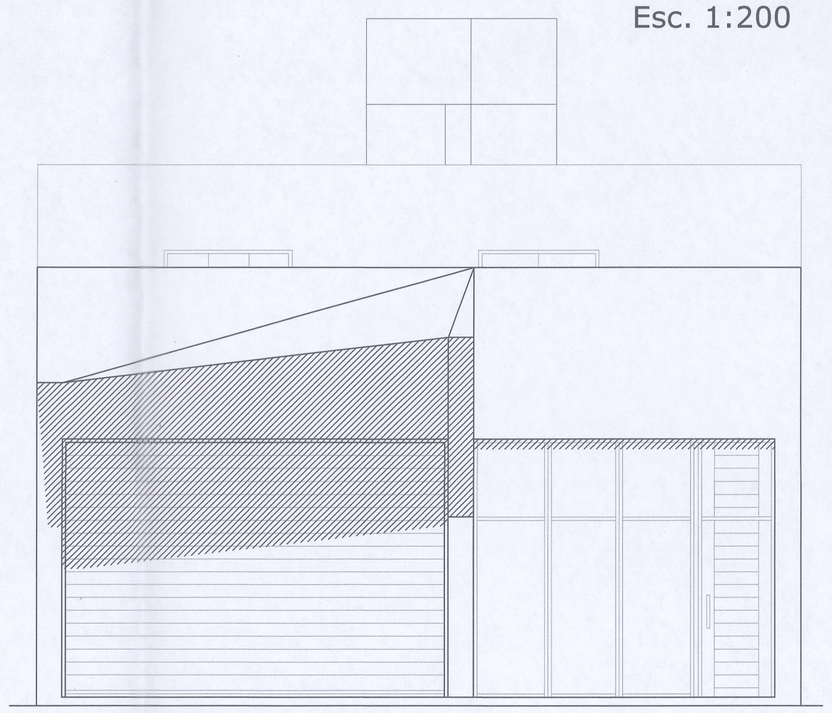

FRENTE Esc. 1:50

Referencias	
	Medidor y toma a tierra
	Tablero General
	Tablero Seccional
	Centro y brazo de luz
	Llave de 1 y 2 puntos
	Tomacorrientes
	Pulsador y Campanilla

Diagrama Unifilar

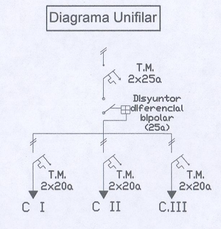

NOTA:

EXISTE UN EXCEDENTE O DIFERENCIA DE MEDIDAS SEGUN HECHOS EXISTENTES CON RESPECTO AL TITULO QUE ES EXCLUSIVA RESPONSABILIDAD DEL PROPIETARIO.-

FIRMA DEL POPIETARIO

DIST.: 3 ZONA: 3 MANZ.: 32 PARC.: 160

PADRON INM.: 0101002201 ICM:222-B-2024 DOMINIO:7N5685

LEY Nº 4683

DESTINO DE LA OBRA : Vivienda y local comercial

PROPIETARIO

Fagalde Carolina Ruth CUIT 23-26570416-4

Fagalde Ana Lia CUIT 27-26570416-1

UBICACION : Hipolito Irigoyen N° 441

BARRIO : Juan B. Alberdi

CIUDAD : Santiago del estero

ESCALA : 1:50 - 1:100 - 1:200

DIRECCION DE SUELO URBANO EXPEDIENTE 559/31/24 FECHA DE INGRESO 28 NOV. 2024 BOLETA Nº 3431

VISADO ELECTRONICO C.P.I.A. OT N° 1641764

SUP. TERRENO S/T y S/He	559,13 m2
SUP. CUBIERTA P.B. S/He	296,20 m2
SUP. CUBIERTA P.A. S/He	84,11 m2
SUP. TOTAL	380,31 m2

CROQUIS DE UBICACION

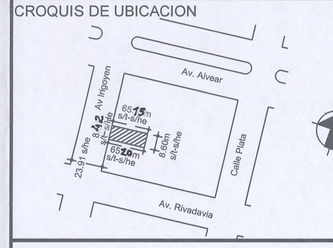

PROPIETARIO : Dom.:

PROYECTO : Dom.:

D. TECNICA : Dom.:

ELECTRICIDAD : Dom.:

CAT. CONS. PROF.:

CHRISTIAN J. ACOSTA M.M.O. M.P. 50.356

ANCHO DE CALLE :	23,91 m
ANCHO DE VEREDA :	5,86 m
ANCHO DE CALZADA :	12,31m
PAVIMENTO :	
SERVICIOS CLOACALES :	

DESIGNACION :

PLANO DE RELEVAMIENTO Y MODIFICACION

OBSERVACIONES : 12 NOV 2024

Las referencias al Título de dominio son meramente indicativas, y la aprobación administrativa no valora los derechos que de ellos emergen.

PERMISO DE COMIENZO DE OBRA Nº 193/2024 DIRECCION DE SUELO URBANO

MUNICIPALIDAD DE LA CIUDAD DE SANTIAGO DEL ESTERO SECRETARIA DE ECONOMIA

APROBADO DIRECCIÓN DE SUELO URBANO EXPEDIENTE 559-31-2024-Corp. 04-F-2024 FECHA: 28 NOV 2024

Arq. BERNARDO C. M. SANTILLAN DIRECTOR DIRECCION DE SUELO URBANO MUNICIPALIDAD DE SGO. DEL ESTERO

DIRECCION DE SUELO URBANO EXPEDIENTE 559-31-2024 FOLIO 31 FECHA 28 NOV 2024

EL PROYECTO DESTINO DE LOS LOCALES ESTA SUJETO A LAS DISPOSICIONES DE LA ORDENANZA Nº 7863/22 CAPITULO 3.