



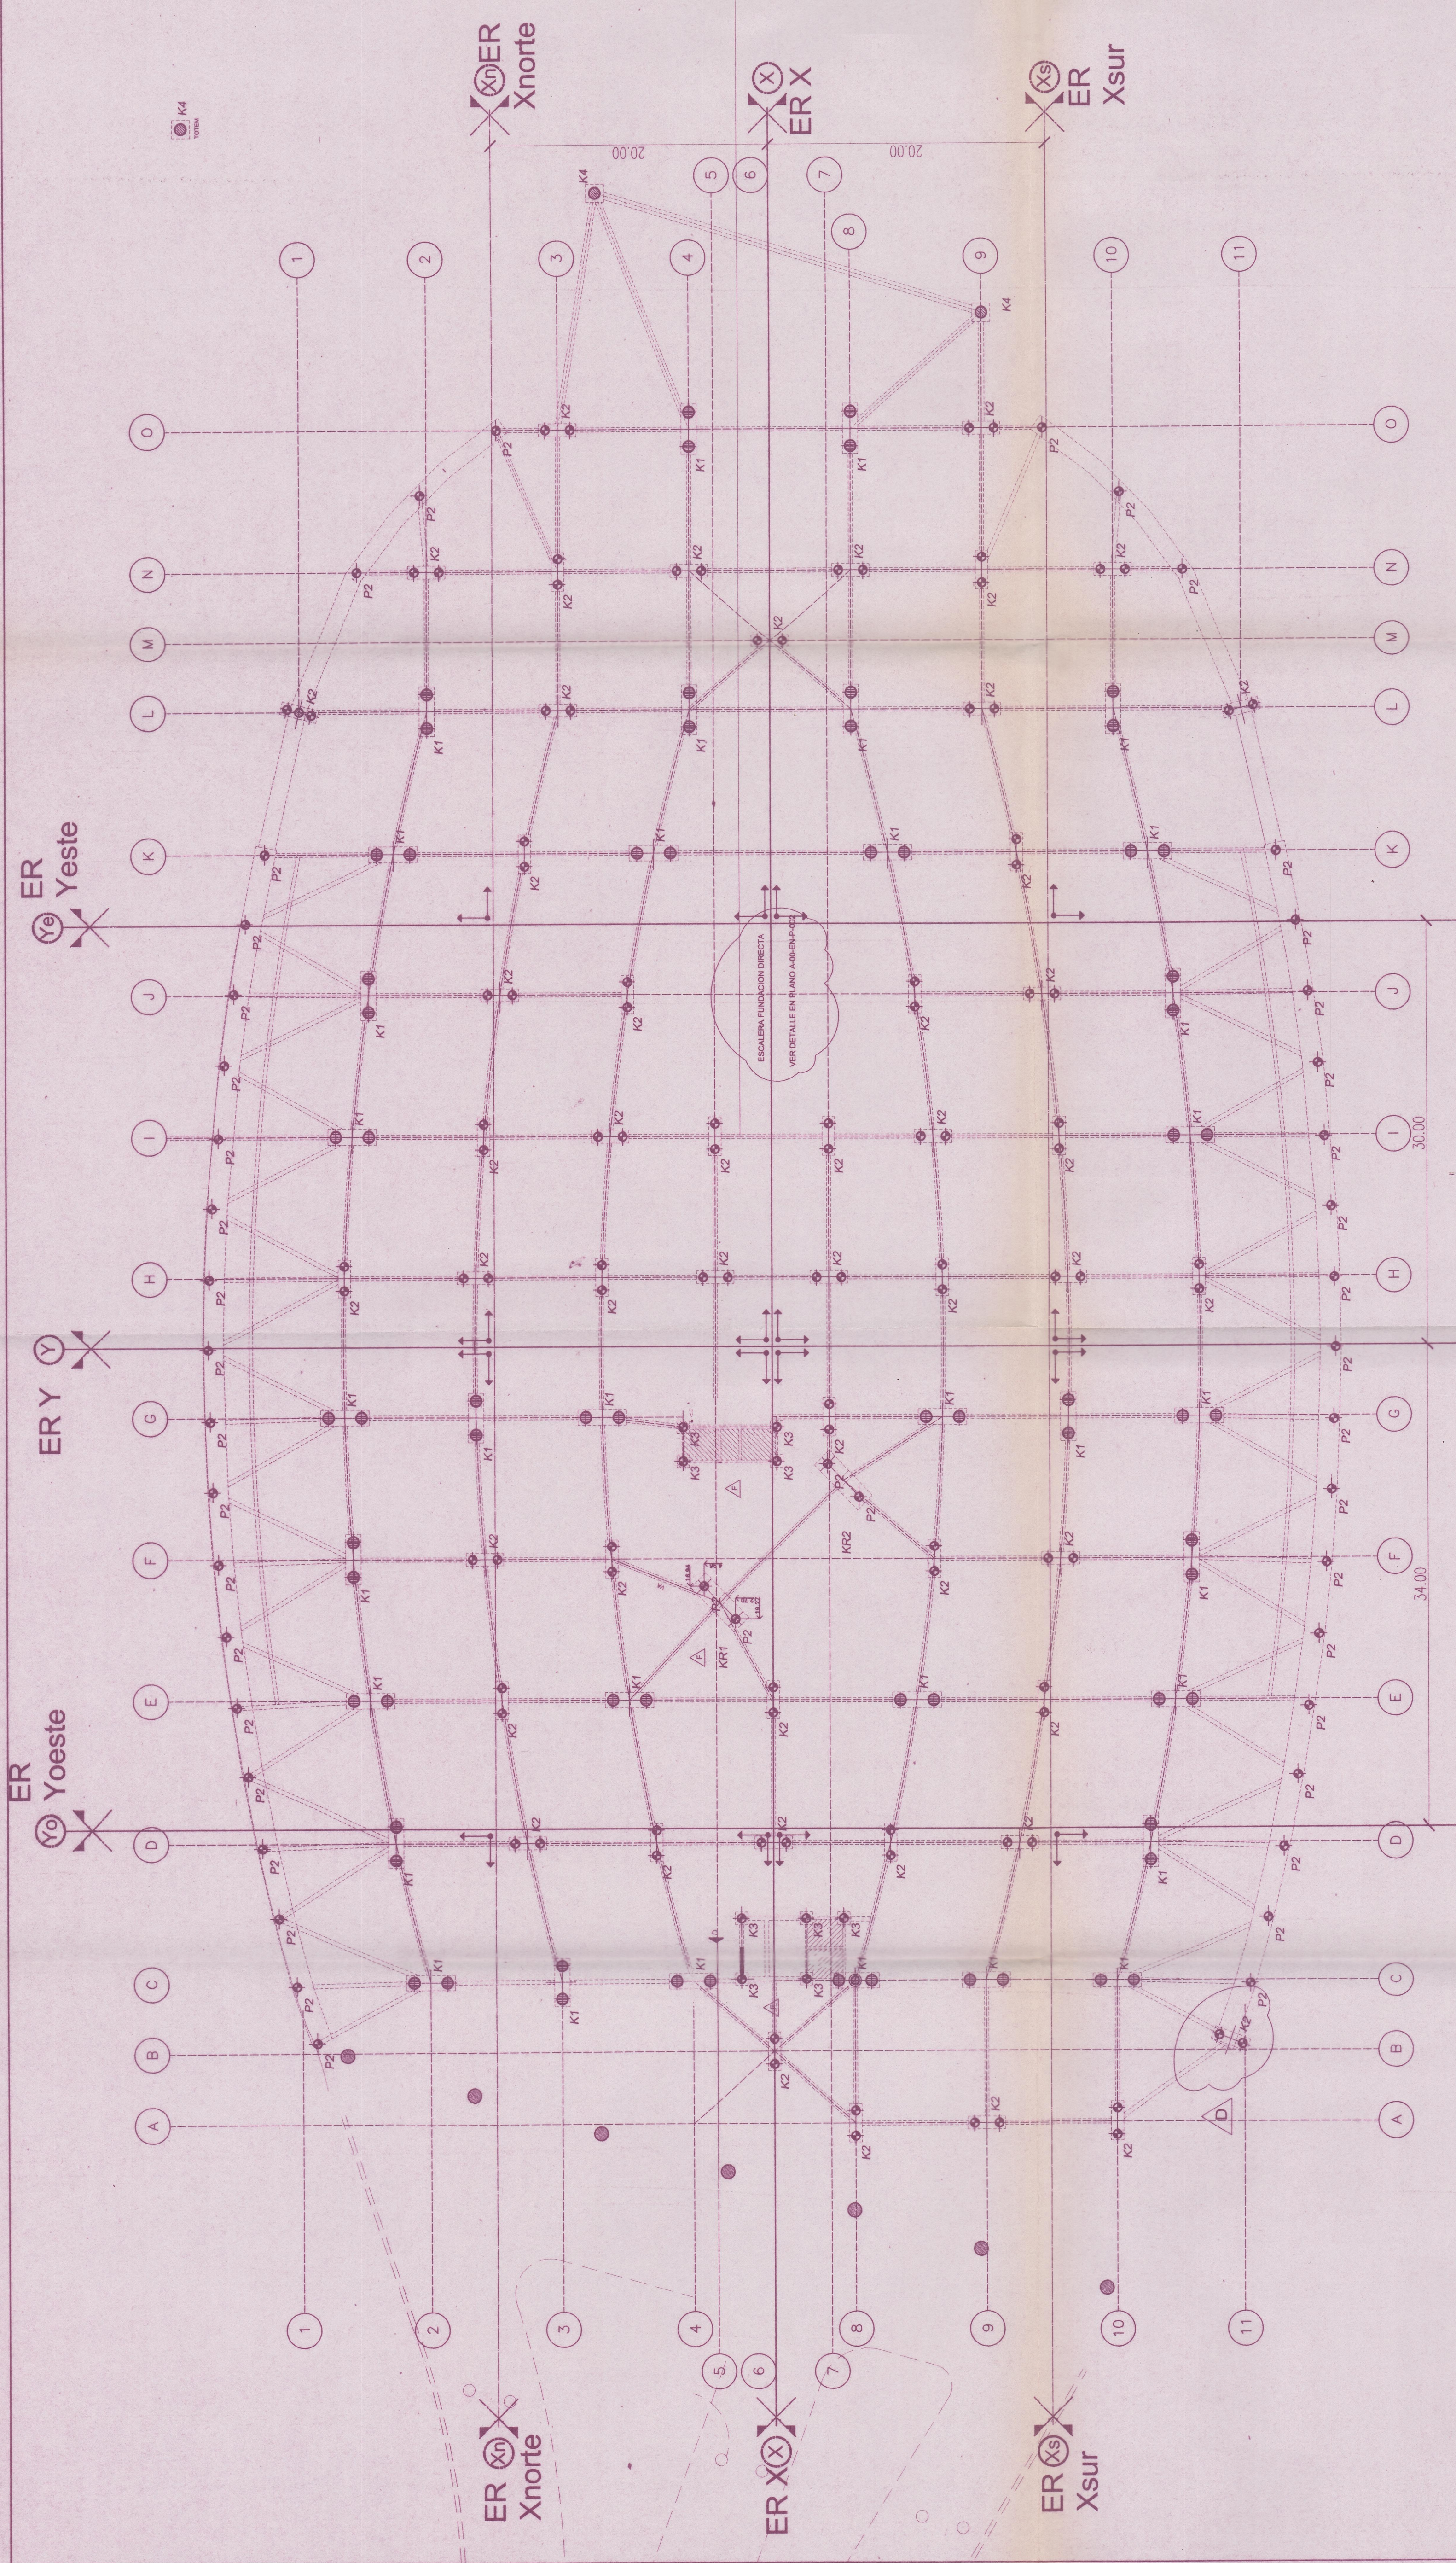


PLANTA DE PILOTAJE


CABEZAL K4
1.30 x 1.30 x 1.00
1 PILOTE □80 (P3)
PLANTA

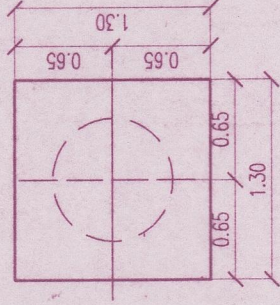


CABEZAL K3
0.90 x 0.90 x 1.00
1 PILOTE □60 (P2)
PLANTA

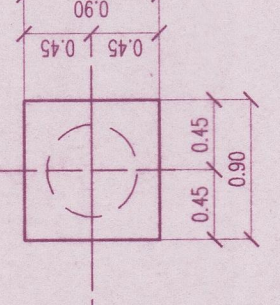


CABEZAL K2
2.70 x 0.90 x 1.00
2 PILOTES □60 (P2)
PLANTA

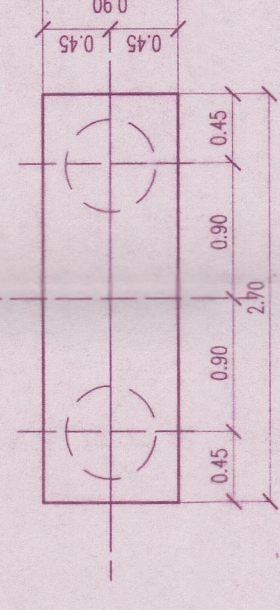

CABEZAL K1
3.50 x 1.10 x 1.20
2 PILOTES □80 (P1)
PLANTA

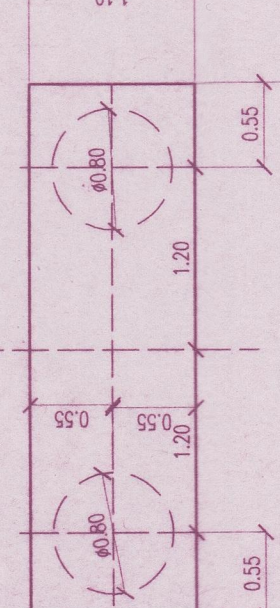

VISTA

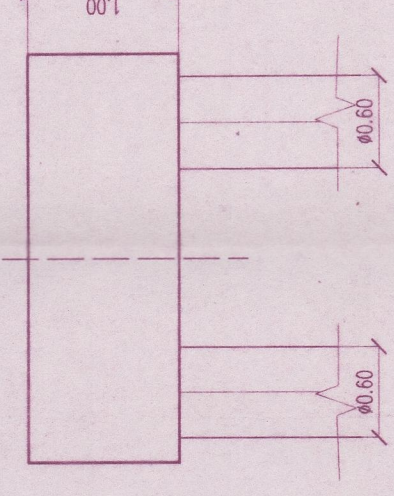

VISTA



REFERENCIAS

PILOTE Ø80

PILOTE Ø60

PILOTE Ø80

P1

P2

P3

CALIDAD DE MATERIALES:
HORMIGON H21(PILOTES)
HORMIGON H30(ESTRUCTURA)
ACERO BARRAS ADN 420
RECUBRIMIENTO:
PILOTES :7CM
VF: 3CM

DISTRITO: 03 ZONA: 03 MANZANA: 11 PARCELA: 11
PADRON INMOBILIARIO: 1-1-92811 DOMINIO : N°119973281 año 1974 d Capital

Destino de la Obra : Estación Terminal de Omnibus

Propietario : Gobierno de la Provincia de Santiago del Estero

Calle : Chaco s/n - Peru s/n - Chacabucos/n - Av. Roca s/n -

Barrio : Juan Bautista Alberdi

Ciudad : Capital - Santiago del Estero

Escala : 1:500

Superficie terreno: 16883.19 m2
Superficie cubierta P: 8229.47m2
Superficie cubierta T: 1278.86 m2
Superficie cubierta Terraza :
Superficie total: 9308.155 m2

CROQUIS de Ubicación

PROYECTO: Ing. Carlos E. Ibañez
domicilio: Rivadavia 346
Chacabucos y Peru

DIRECCION TECNICA: Ing. Carlos E. Ibañez
domicilio: Rivadavia 346
Chacabucos y Peru

ELECTRICIDAD: Ing. Carlos E. Ibañez
domicilio: Rivadavia 346
Chacabucos y Peru

CATEGORIA OBRA : "A"

PERMISO DE COMIENZO DE OBRA N°

07 OCT 2008

Las referencias en este plano son válidas para la DIRECCION DE SUELO URBANO

EXPEDIENTE: 16147-S-0207

17 OCT 2008

Carol

Municipalidad de Sgo. del Estero

PLAN DE OBRA NUEVA
ESTRUCTURA- PLANTA DE PILOTAJE

OBSERVACIONES:

07 OCT 2008

Las referencias en este plano son válidas para la DIRECCION DE SUELO URBANO

EXPEDIENTE: 16147-S-0207

17 OCT 2008

Carol

Municipalidad de Sgo. del Estero