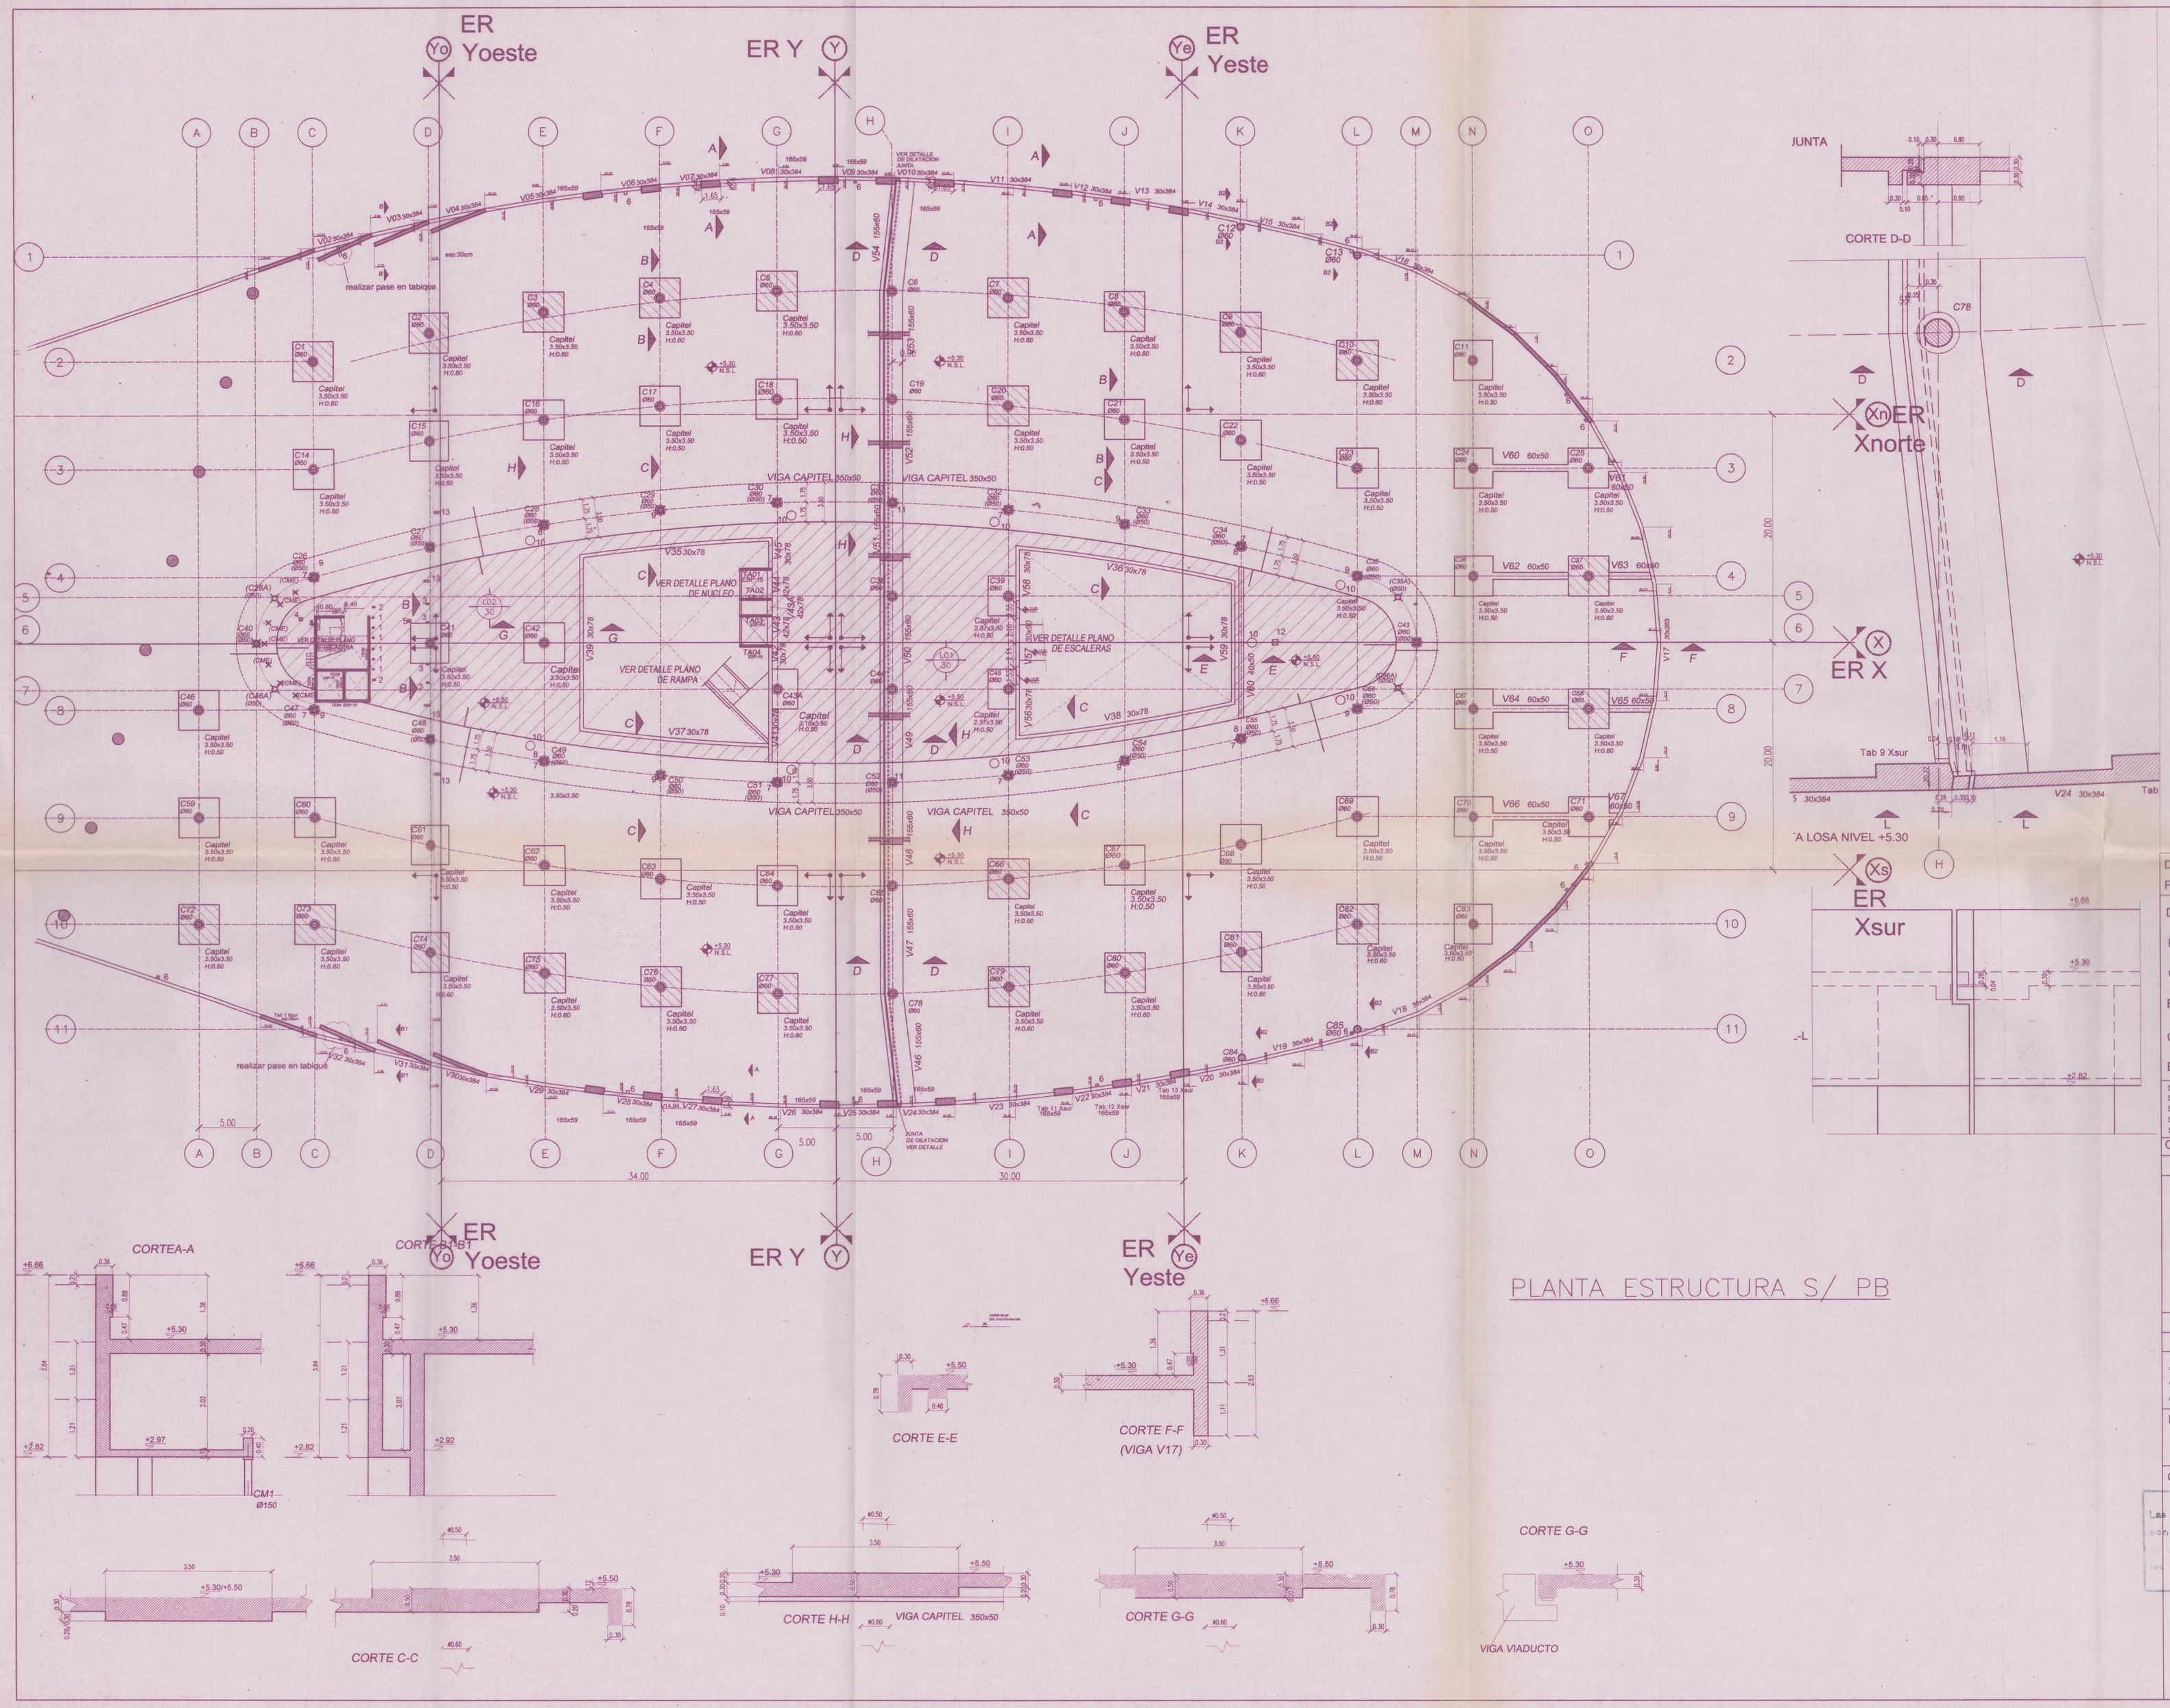

CALIDAD DE MATERIALES:
HORMIGON H21(PILOTES)
HORMIGON H30(ESTRUCTURA)
ACERO BARRAS ADN 420
RECUBRIMIENTO:
PILOTES :5CM
VF: 3CM

DISTRITO: 03 ZONA: 03 MANZANA :11 PARCELA :
PADRON INMOBILIARIO: 1-1-92811 DOMINIO : Nº1190F°3291 año 1974 d.Capital

Destino de la Obra : Estación Terminal de Omnibus

Propietario : Gobierno de la Provincia de Santiago del Estero

Calle : Chaco s/n - Peru s/n - Chacabucos/n - Av. Roca s/n .-

Barrio : Juan Bautista Alberdi

Ciudad : Capital - Santiago del Estero

Escala :1:500

Superficie terreno: 16883.19 m2 FOS: 100%
Superficie cubierta P. Baja: 8029.475m2 FOT: 9
Superficie cubierta 1º Piso: 1278.68 m2 FOT: 9 X 16458.157 m2
Superficie cubierta Terraza: - FOT: 148123.00 m2
Superficie total: 9308.155 m2

Croquis de Ubicación

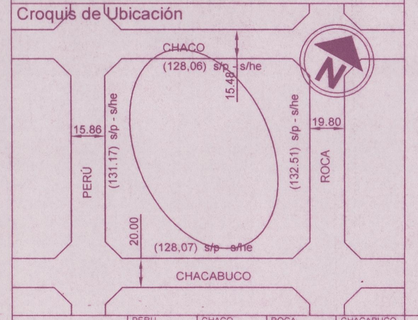

	PERU	CHACO	ROCA	CHACABUCO
ancho de calle :	15.86 m	15.48 m	19.80 m	20.00 m
ancho de calzada :	8.25 m	8.16 m	12.52 m	12.00 m
ancho de vereda:	3.80 m	3.72 m	3.80 m	4.00 m

PAVIMENTO: Si
SERVICIOS: Si

PROPIETARIO:Gob. Provincia. Sgo. del Estero
domicilio : Chacabuco y Perú

PROYECTO:Ing. Carlos E. Ibañez
domicilio: Rivadavia 348

DIRECCION TECNICA: Ing. Carlos E. Ibañez
domicilio: Rivadavia 348

ELECTRICIDAD: Ing. Carlos E. Ibañez
domicilio: Rivadavia 348

CATEGORIA OBRA: "A"

PERMISO DE COMIENZO DE OBRA Nº

DESIGNACION : PLANO DE OBRA NUEVA
ESTRUCTURA- PLANTA ESTRUCTURA S/PB

E3

OBSERVACIONES :

07 OCT 2008
Las referencias al Título de Dominio son mínimas [illegible] vas, y la [illegible] no valora [illegible] los derechos [illegible] emergen.

MUNICIPALIDAD DE LA CIUDAD DE SANTIAGO DEL ESTERO
SECRETARIA DE PLANEAMIENTO Y OBRAS PUBLICAS
APROBADO
DIRECCION DE SUELO URBANO
EXPEDIENTE: 18147-S-2007
FECHA: 07 OCT 2008

Arq. HUGO V. CAROL
Director de Suelo Urbano
Municipalidad de Sgo. del Estero

Tarea Proyecto y Dirección de Obras
FECHA 07 OCT 2008
Nº 21174