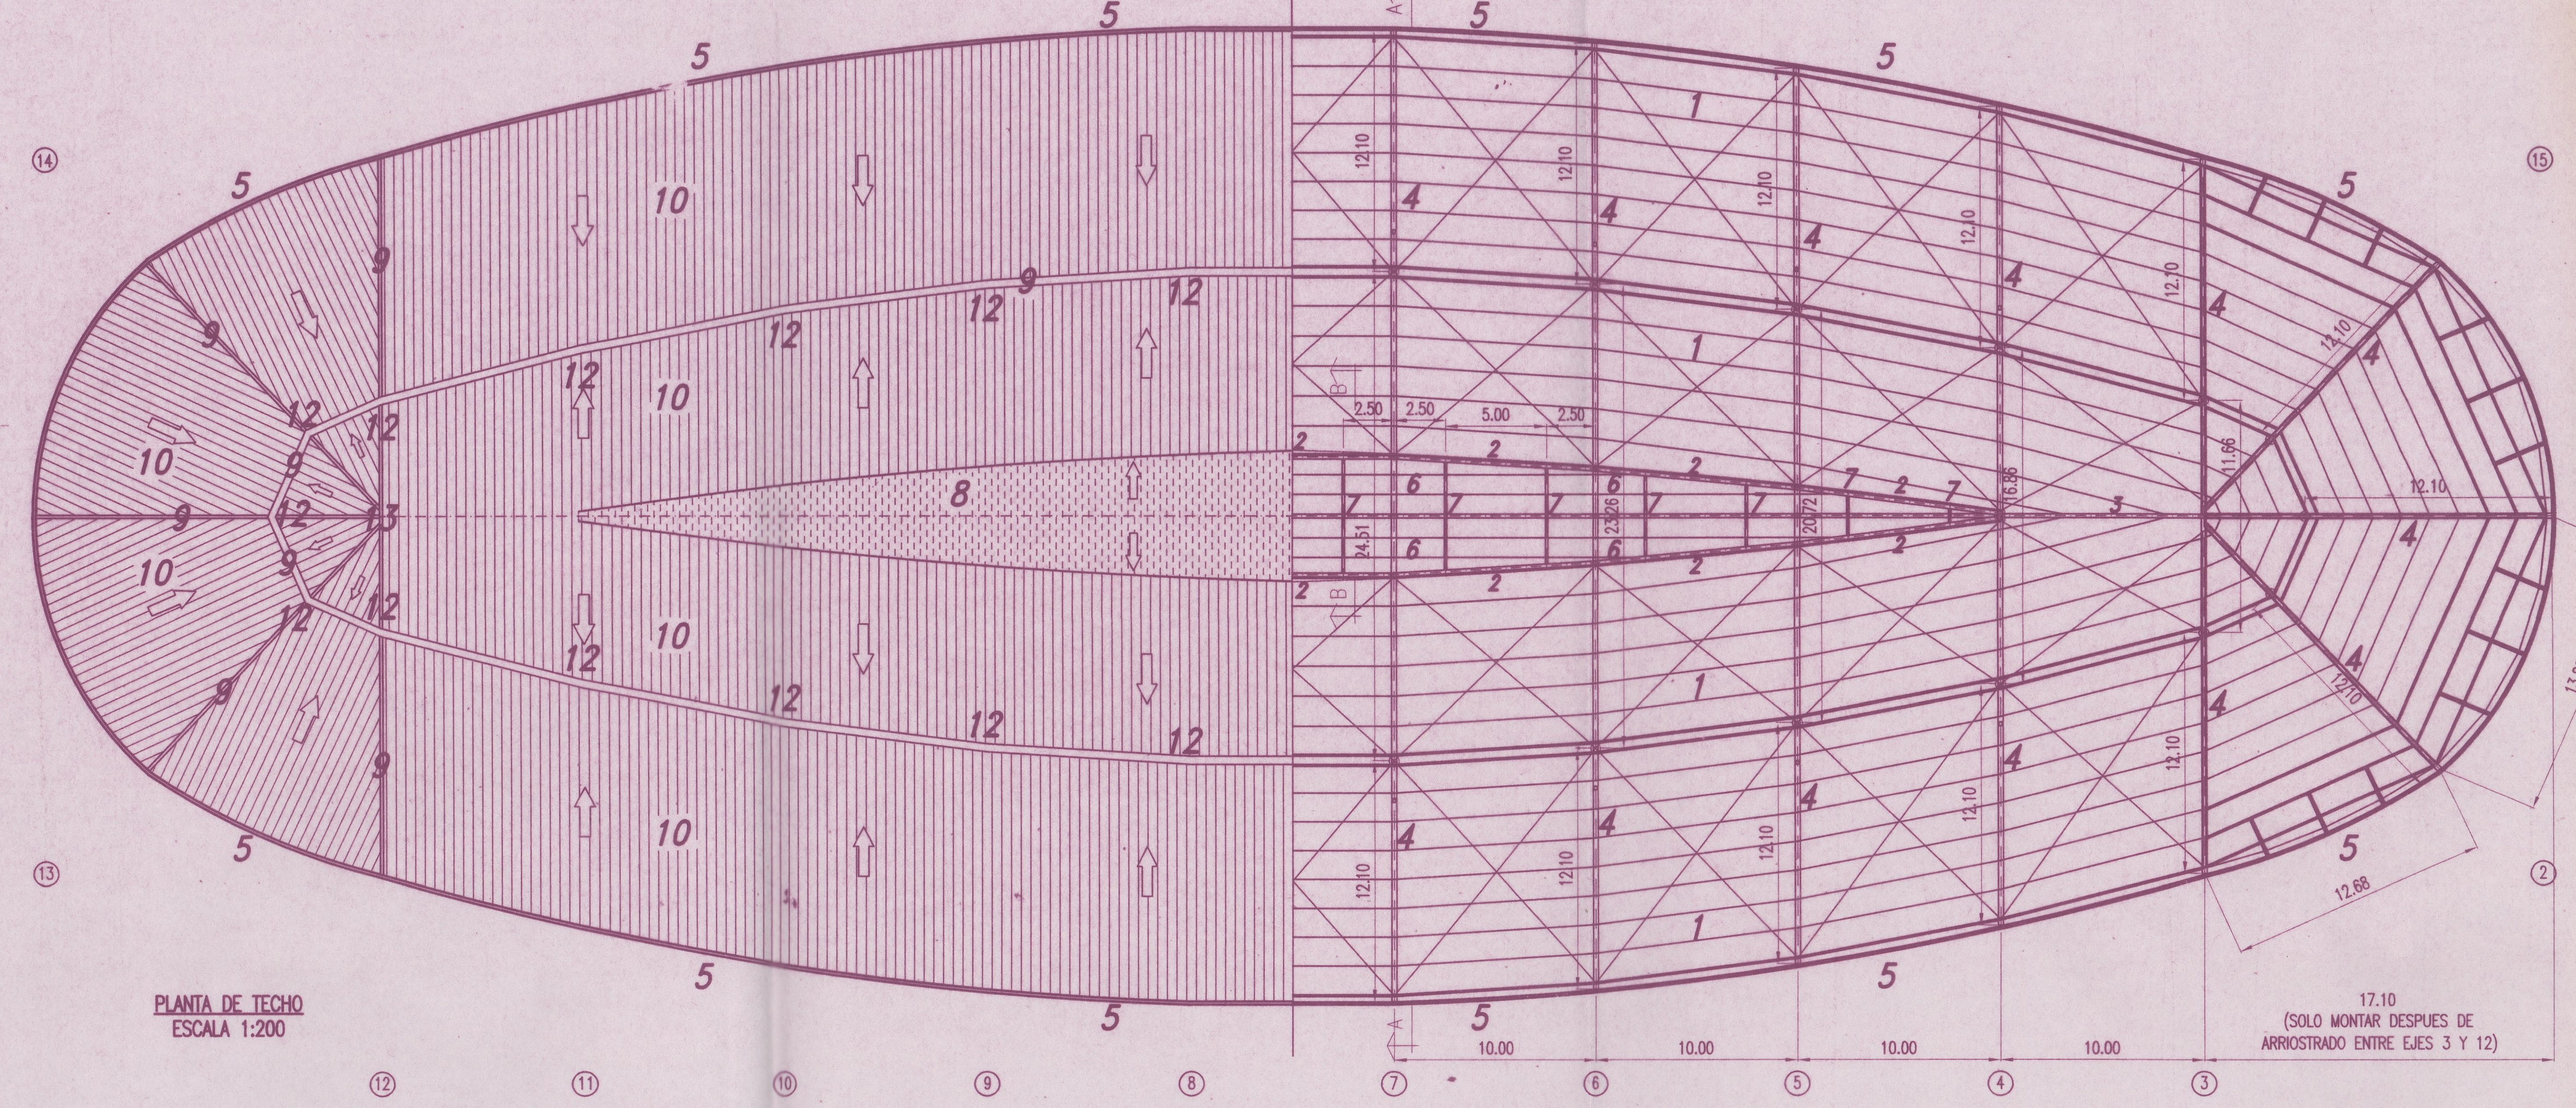

PLANTA DE ESTRUCTURA METALICA

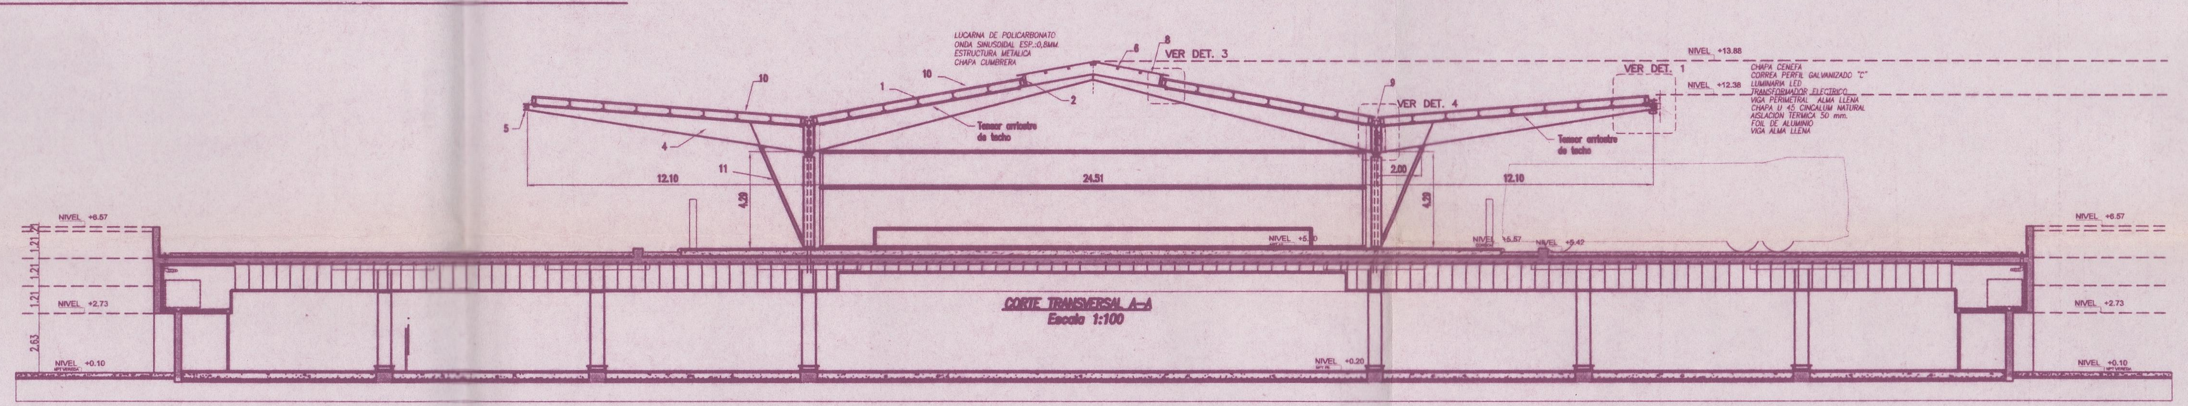

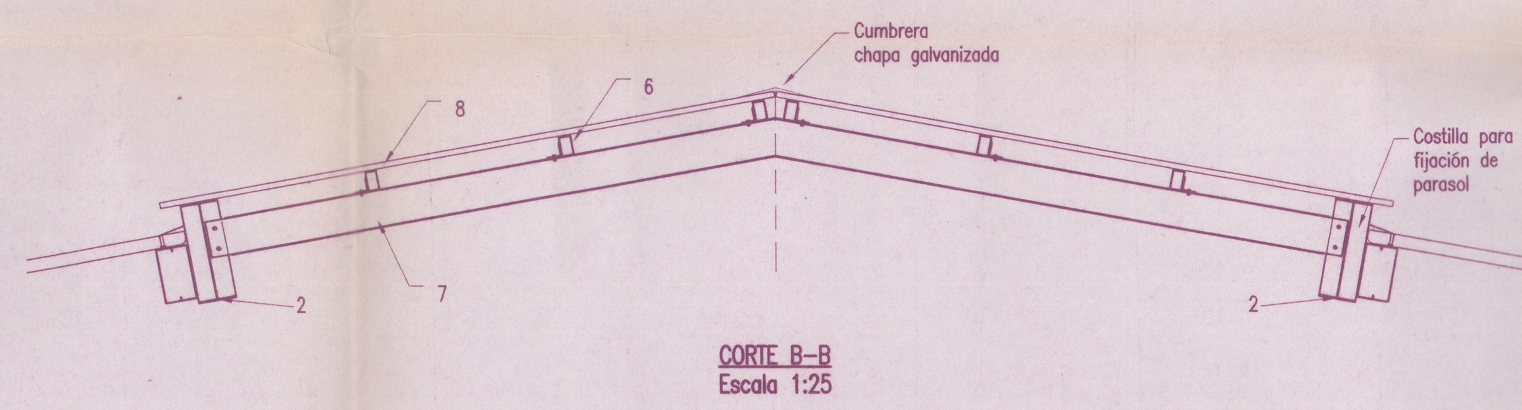

REFERENCIAS

1 CORREAS PERFILES GALVANIZADOS
2 VIGA INFERIOR ALMA LLENA DE LUCARNA
3 VIGAS CUMBRERA ALMA LLENA
4 VIGAS PRINCIPALES ALMA LLENA
5 VIGA CENEFA ALMA LLENA PERIMETRAL. Facetada en la zona de mayor radio
6 TUBOS RECTANGULARES SOPORTE DE POLICARBONATO
7 PORTICOS DE ALMA LLENA DE LUCARNA
8 LUCARNA DE POLICARBONATO SINUSOIDAL 0.8 MM SOBRE TUBOS GALVANIZADOS
9 CANALETA BWG 22 CINCALUM NATURAL
10 U 45 BWG 22 CINCALUM NATURAL CON ALEACION TERMICA DE LANA DE VIDRIO CON FOIL DE ALUMINIO DE 50 MM
11 PUNTAL CAÑO REDONDO
12 BAJADA PLUVIAL
13 PARARRAYOS IONICO
14 NOTA: ESTRUCTURA SEGUN CALCULO PINTURA 120 MICRONES DE EPOXI

PARASOLES

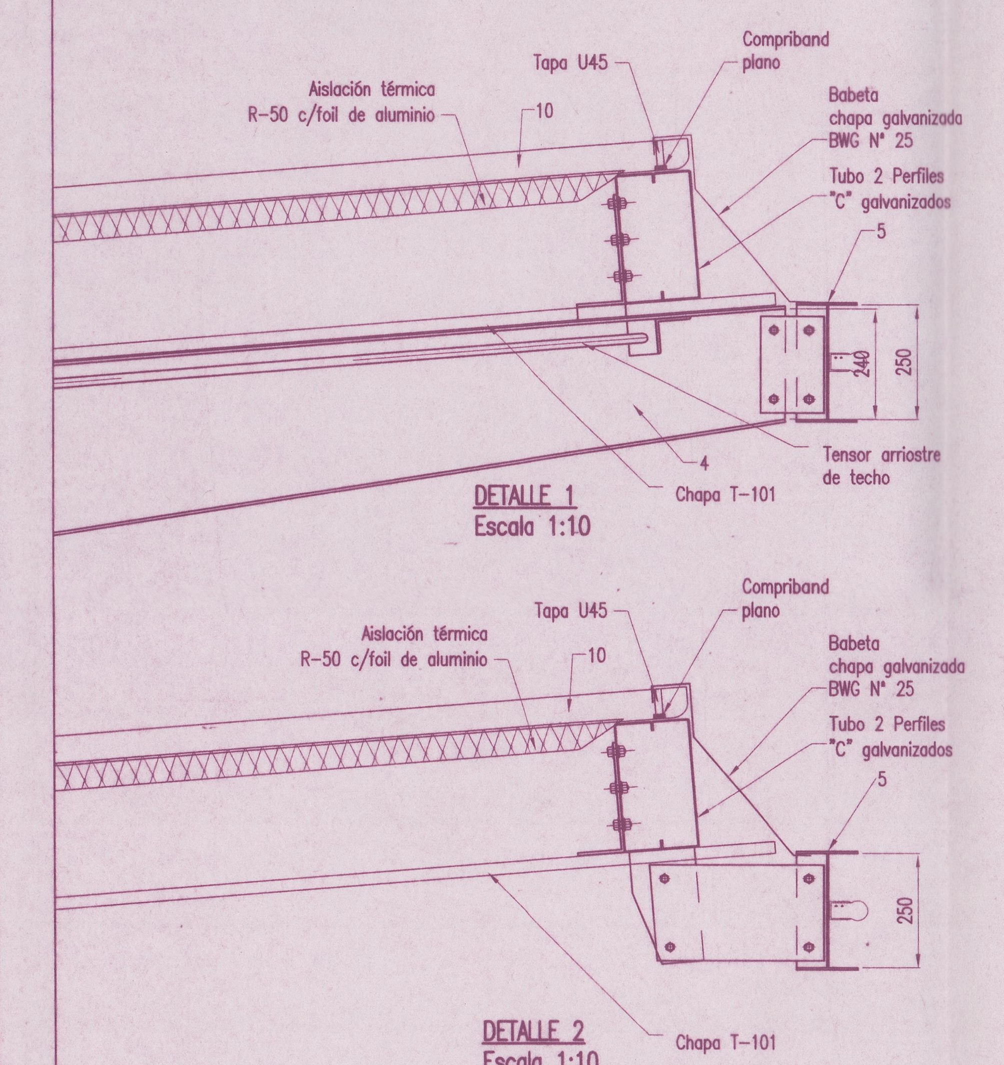

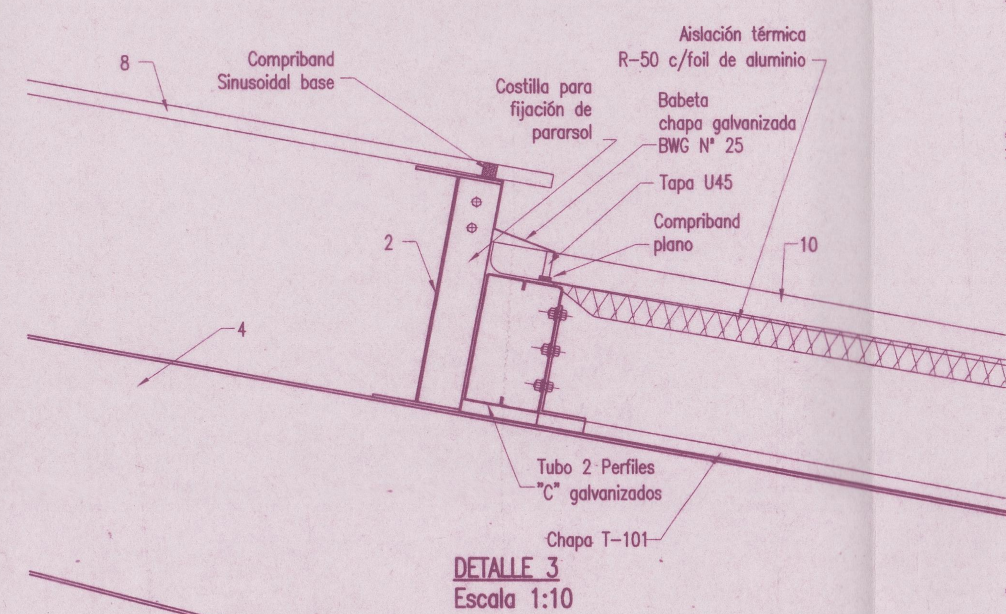

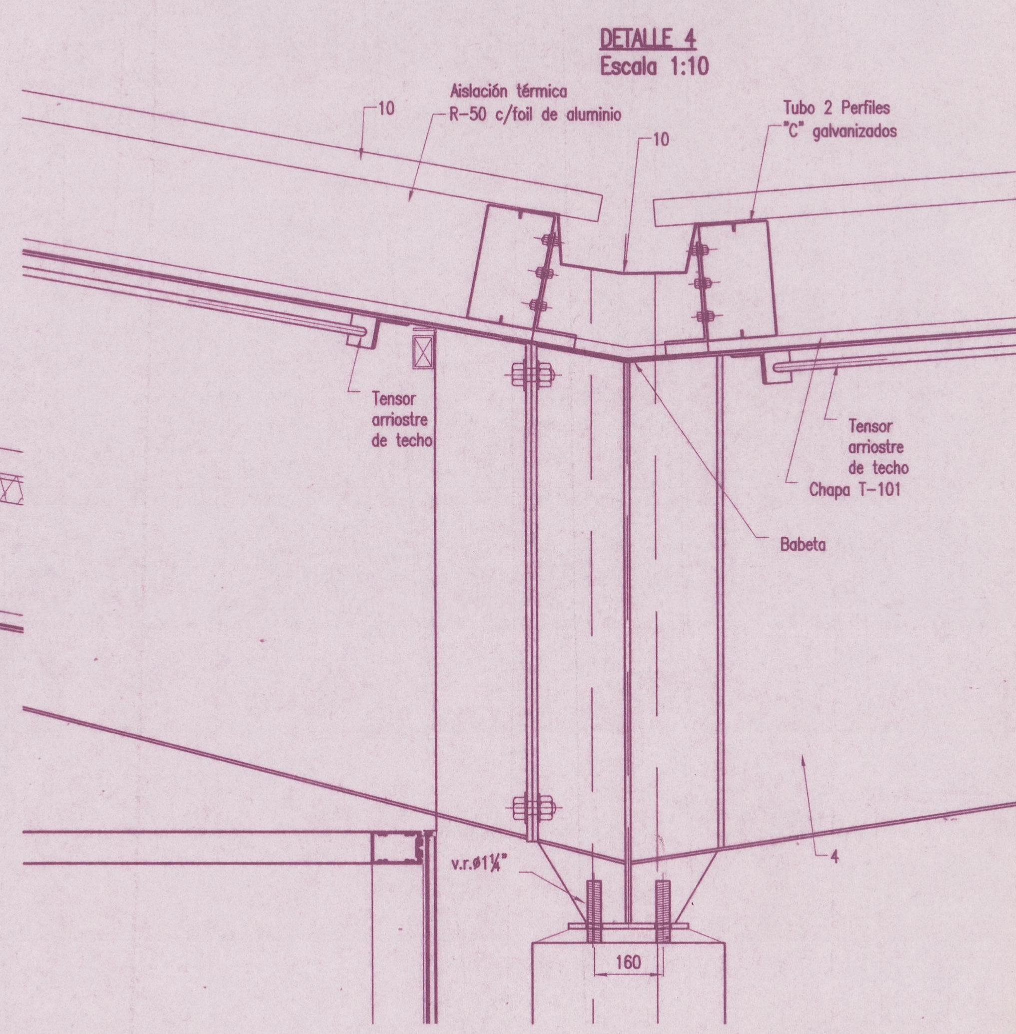

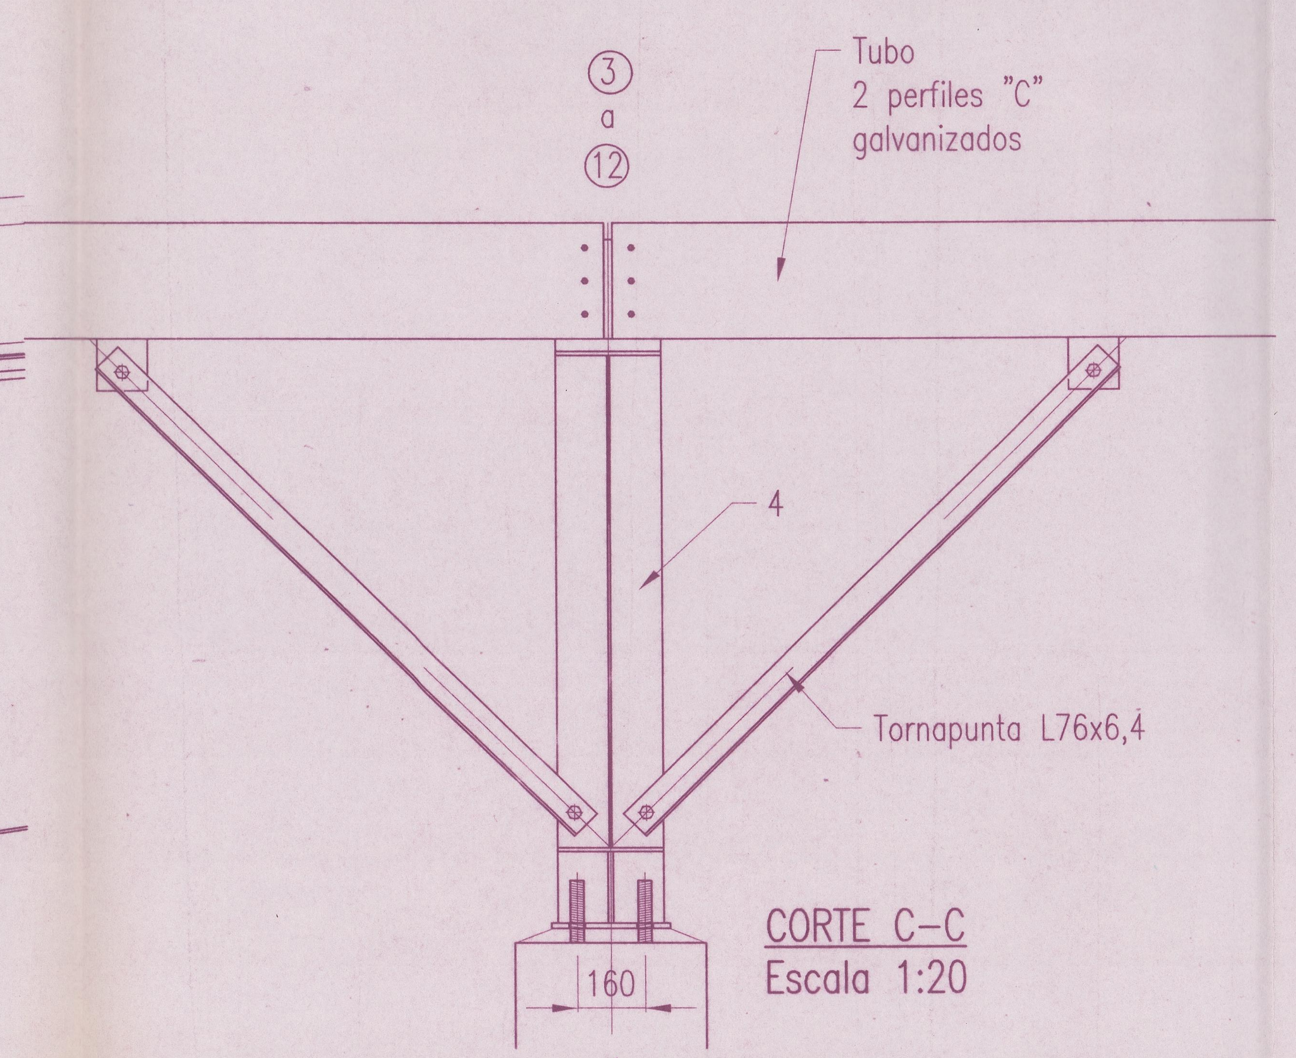

DISTRITO: 03 ZONA: 03 MANZANA :11 PARCELA :

PADRON INMOBILIARIO: 1-1-92811 DOMINIO : Nº1190Fº3291 año 1974 d.Capital

Destino de la Obra : Estación Terminal de Omnibus

Propietario : Gobierno de la Provincia de Santiago del Estero

Calle : Chaco s/n - Peru s/n - Chacabucos/n - Av. Roca s/n .-

Barrio : Juan Bautista Alberdi

Ciudad : Capital - Santiago del Estero

Escala :1:500

Superficie terreno: 16883.19 m2
Superficie cubierta P. Baja: 8029.475m2
Superficie cubierta 1º Piso: 1278.68 m2
Superficie cubierta Terraza: -
Superficie total: 9308.155 m2

FOS: 100%
FOT: 9
FOT: 9 X 16458.157 m2
FOT: 148123.00 m2

Croquis de Ubicación

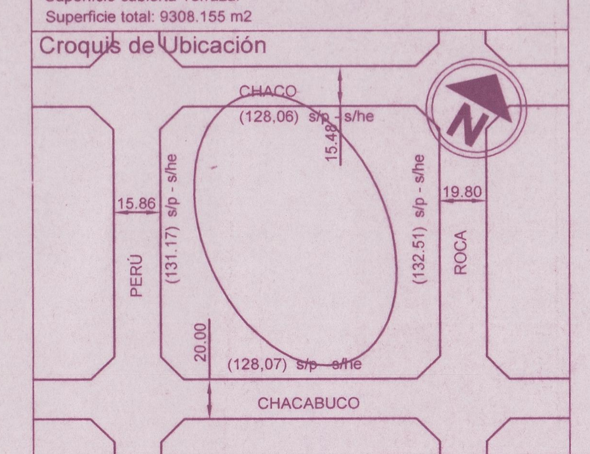

PROPIETARIO:Gob. Provincia Sgo. del Estero
domicilio : Chacabuco y Perú

PROYECTO:Ing. Carlos E. Ibañez
domicilio: Rivadavia 348

DIRECCION TECNICA: Ing. Carlos E. Ibañez
domicilio: Rivadavia 348

ELECTRICIDAD::Ing. Carlos E. Ibañez
domicilio: Rivadavia 348

CATEGORIA OBRA: "A"

	PERU	CHACO	ROCA	CHACABUCO
ancho de calle :	15.86 m	15.48 m	19.80 m	20.00 m
ancho de calzada :	8.25 m	8.16 m	12.52 m	12.00 m
ancho de vereda	3.80 m	3.72 m	3.80 m	4.00 m

PAVIMENTO SI
SERVICIOS CLOACALES SI

PERMISO DE COMIENZO DE OBRA Nº

DESIGNACION : **PLANO DE OBRA NUEVA**

PLANO DE ESTRUCTURA CUBIERTA METALICA

E4

OBSERVACIONES :

07 OCT 2008

MUNICIPALIDAD DE LA CIUDAD DE SANTIAGO DEL ESTERO
SECRETARIA DE PLANEAMIENTO Y OBRAS PUBLICAS
APROBADO
DIRECCION DE SUELO URBANO
EXPEDIENTE: 18147-S-2007
FECHA: 17 OCT 2008

Arq. HUGO V. CAROL
Director de Suelo Urbano
Municipalidad de Sgo. del Estero

Ing. LUIS ALBERTO LUNA
MUNICIPALIDAD DE LA CAPITAL

Tarea Proyecto y Dirección de Obras
FECHA 23 JUL 2008
2174

Arq. TOSCANO
ASESOR - INSPECTOR DE OBRA
Secretaría Planeamiento y Coordinación

CARLOS E. IBAÑEZ
ING. EN CONSTRUCCIONES
REP. TECNICO - RIVASA
M.P. Nº 93.036

SECRETARIA DE PLANEAMIENTO Y DESARROLLO URBANO
Municipalidad de la Capital
SGO. DEL ESTERO
DIREC. DE SUELO URBANO