


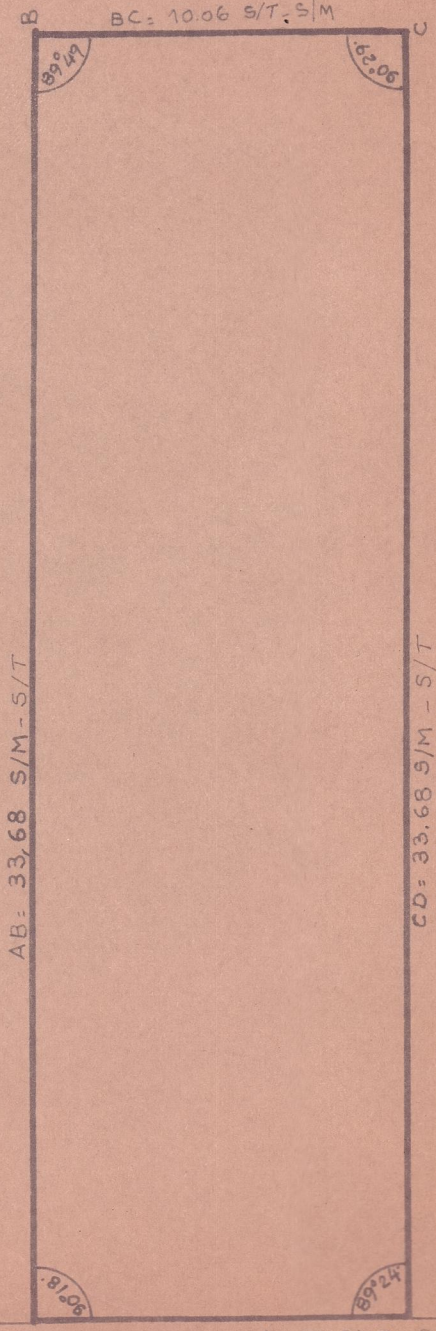

TERRENO
DIST. 3 ZONA 3 MANZ 39 PARC. MANZ. LOTE.

obra propiedad del Sr.
ALICIA IRENE MAROSTICA DE ABATE
calle: ABSALON ROJAS 639
barrio: NORTE
ciudad: Santiago del Estero

superf. terreno 340.33
superf. cubierta 67.41
superf. balcones fuera LM


proprietario: *Victoria J. 9% de Abate*
proyectista domicilio:
domicilio:
direc. técnico domicilio:
ejecución domicilio:
servicios cloacales
pavimento




APROBADO
REC. DE OBRAS HIG. Y A.P.B.
FECHA 14-4-70

AG. ANTONIO A. PALOMO
Ingeniero en Obras Civiles
Eduardo J. Palomo

CORTE 1-1

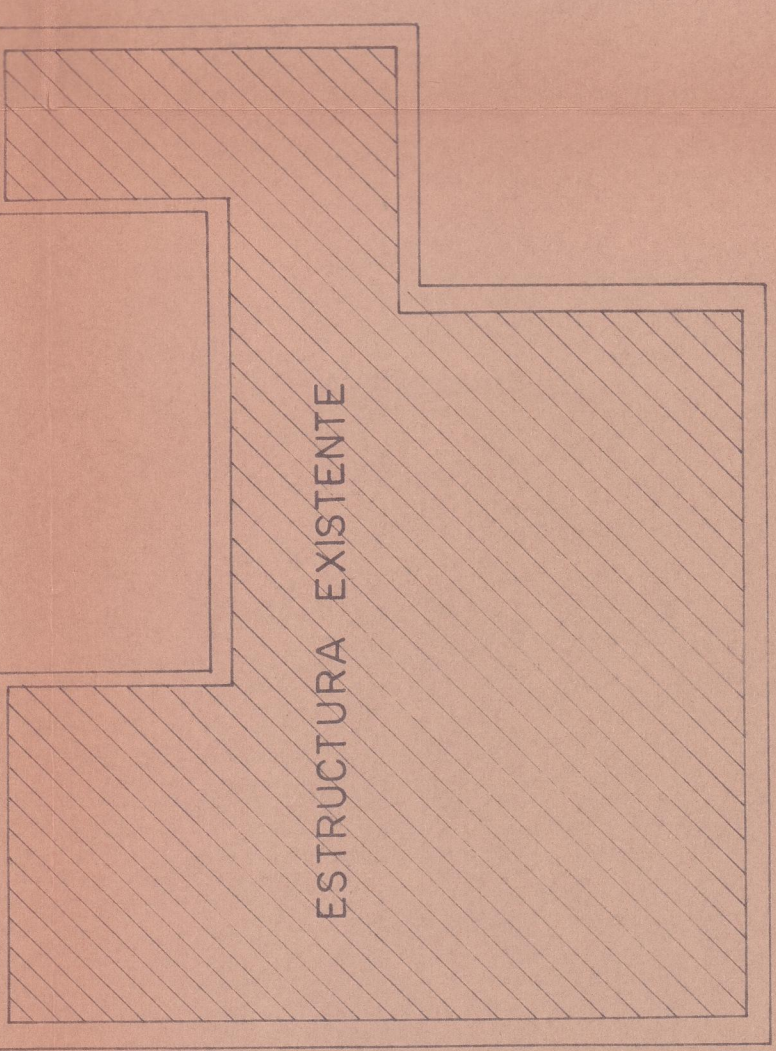


CORTE 2-2

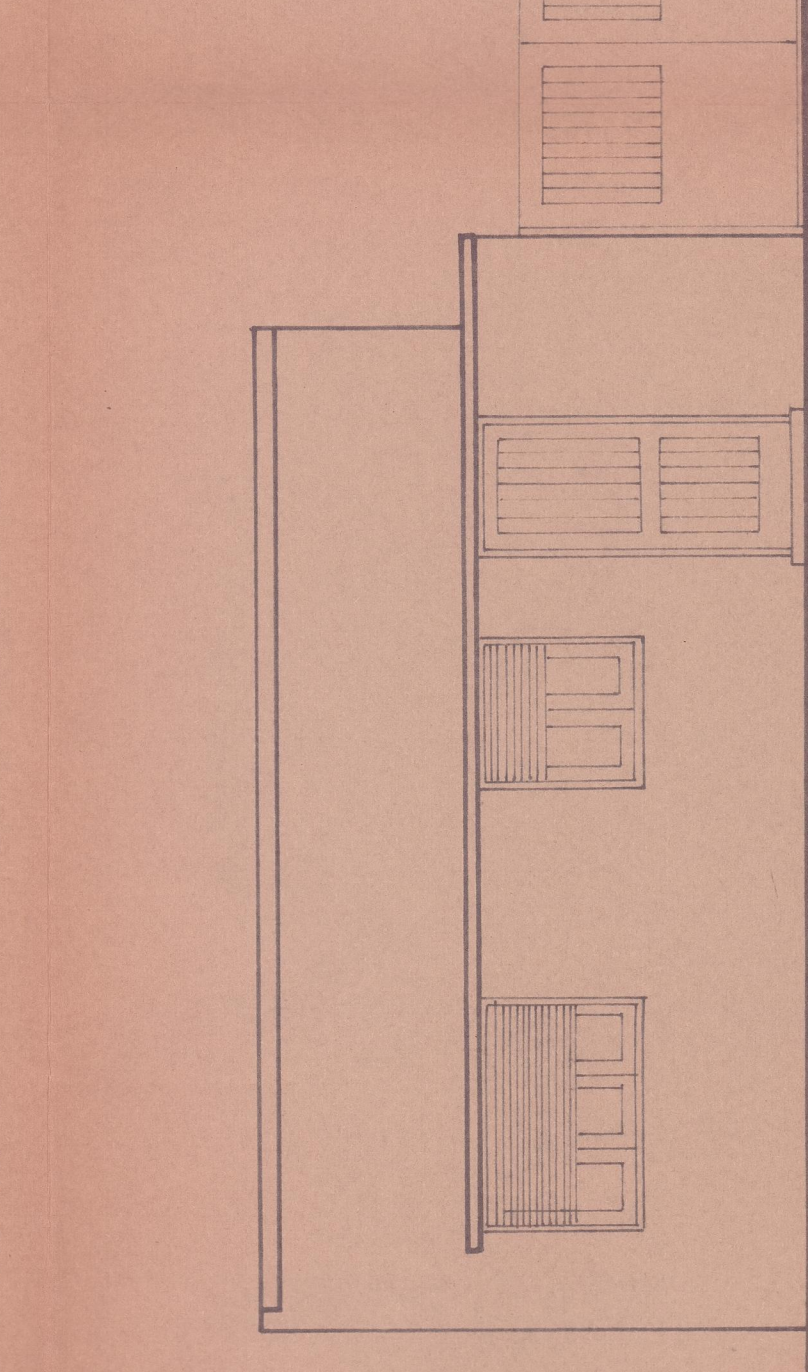

ABERTURAS

DESIG	DIMENSIONES		AREA
	ANCHO	ALTO	
V1	1.50	1.70	1.50
V2	1.00	1.70	0.58
V3	1.20	1.70	0.87
V4	1.70	1.70	1.24
V5	1.80	0.40	0.40

FACHADA

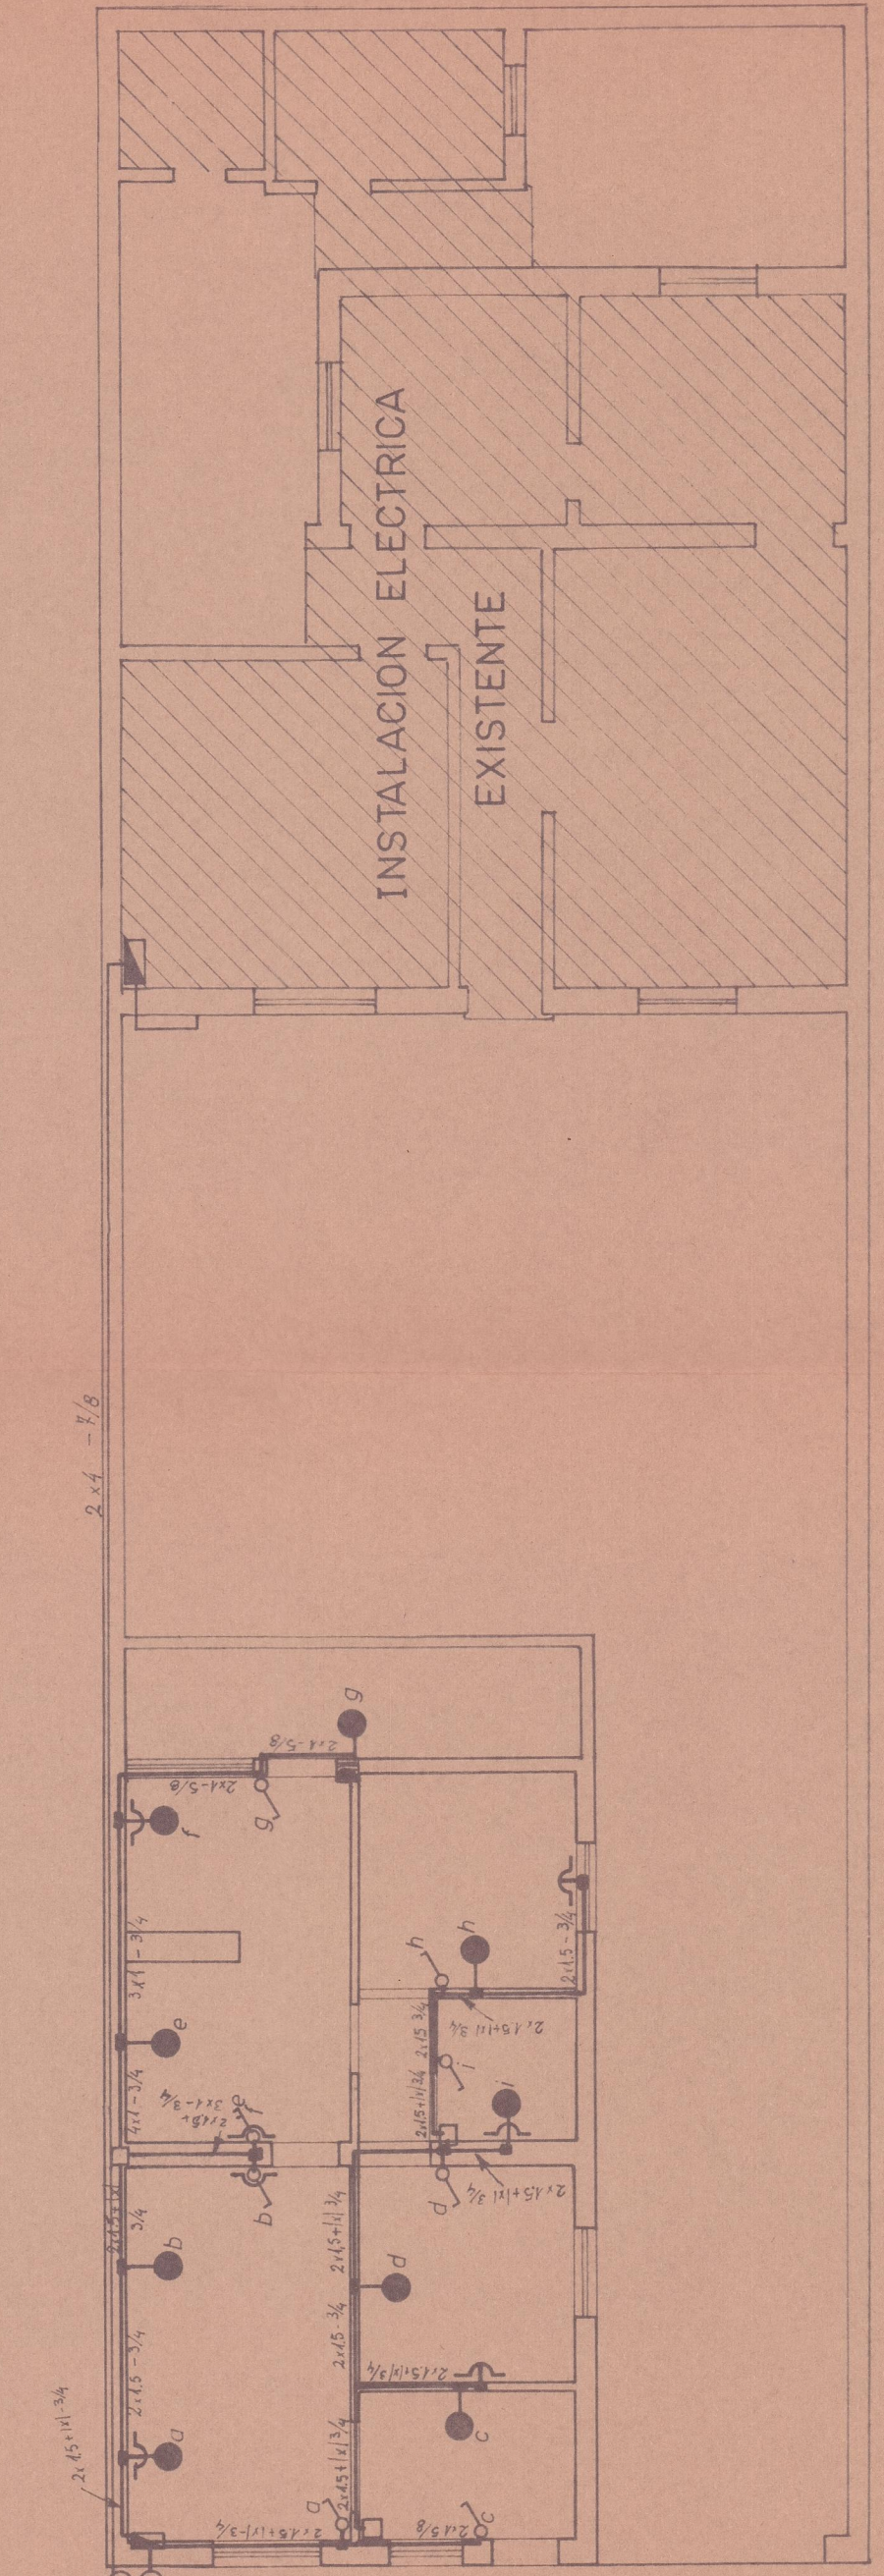


INSTALACION ELECTRICA

- M1 Medidor vivienda existente (solicitar A.Y.E.E.)
M2 " " a refaccionar (existente)



PLANTA DE HORMIGON EXISTENTE

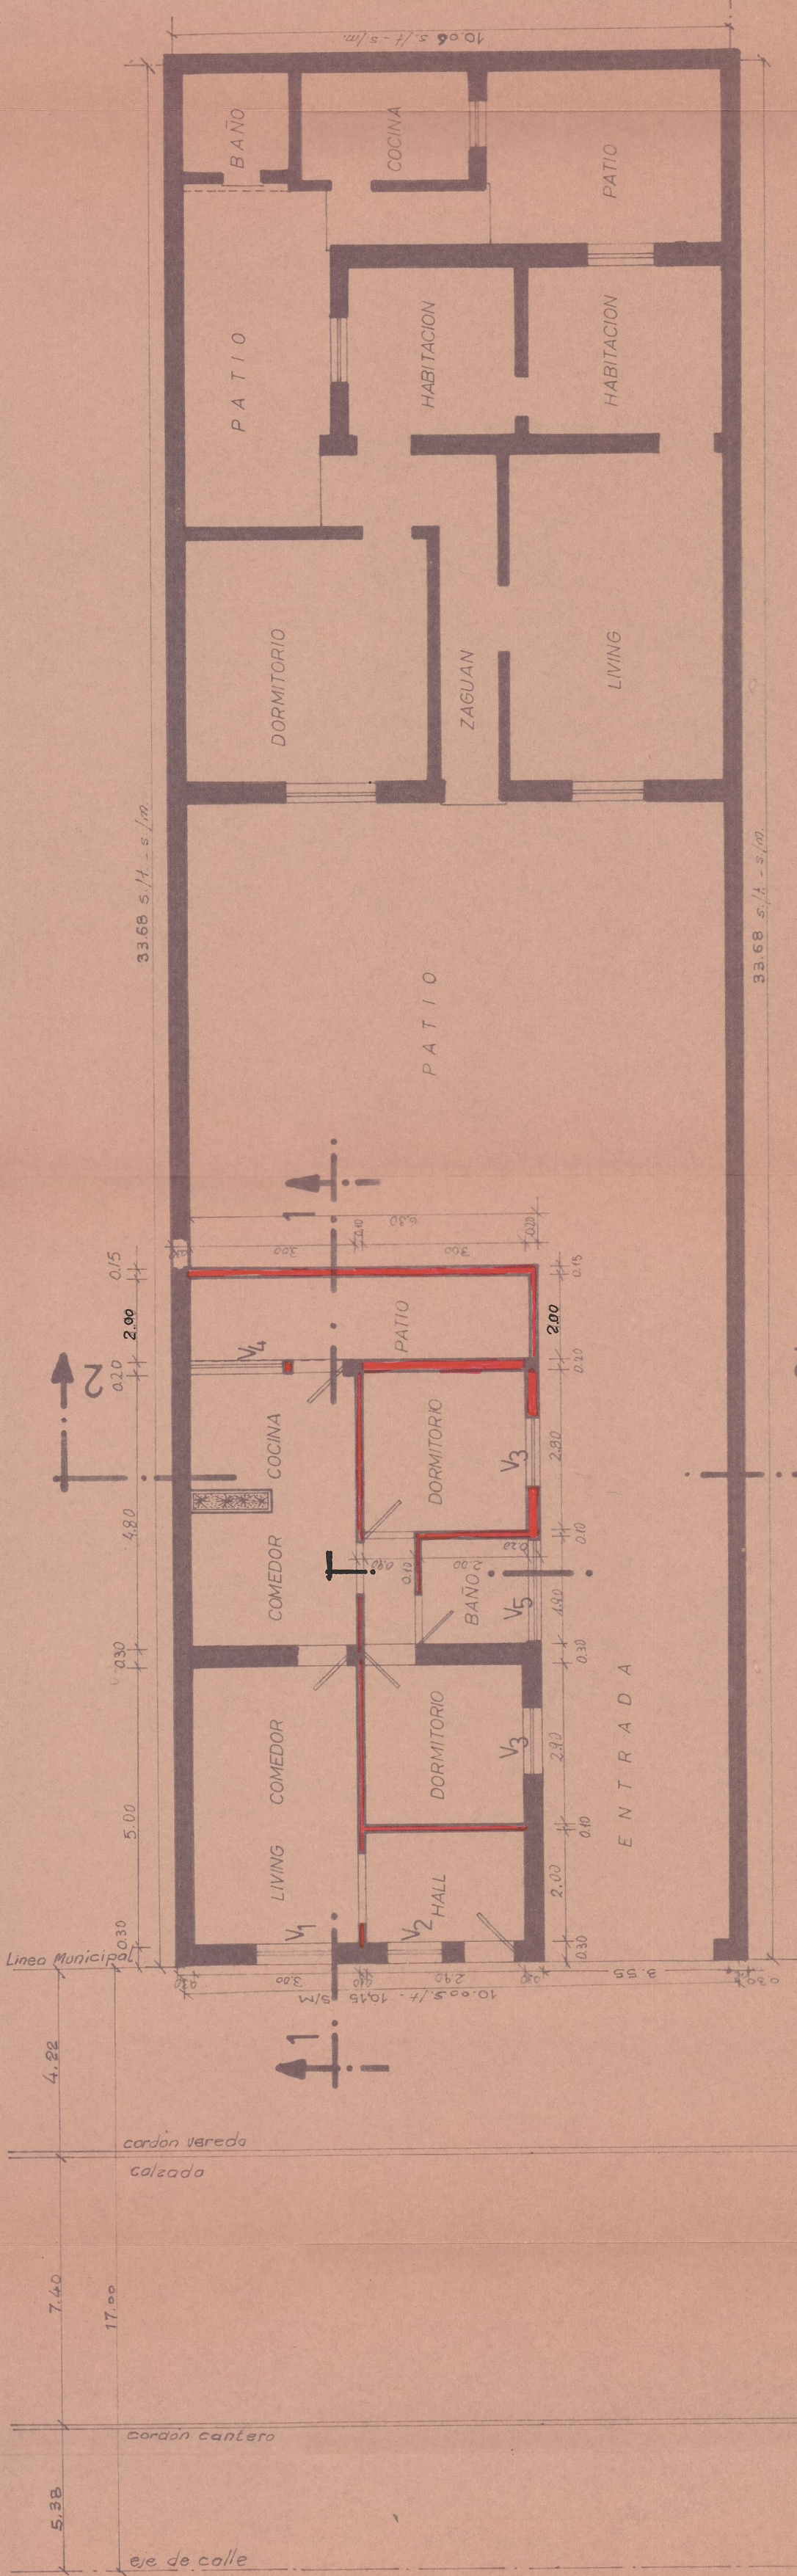

PLANTA