
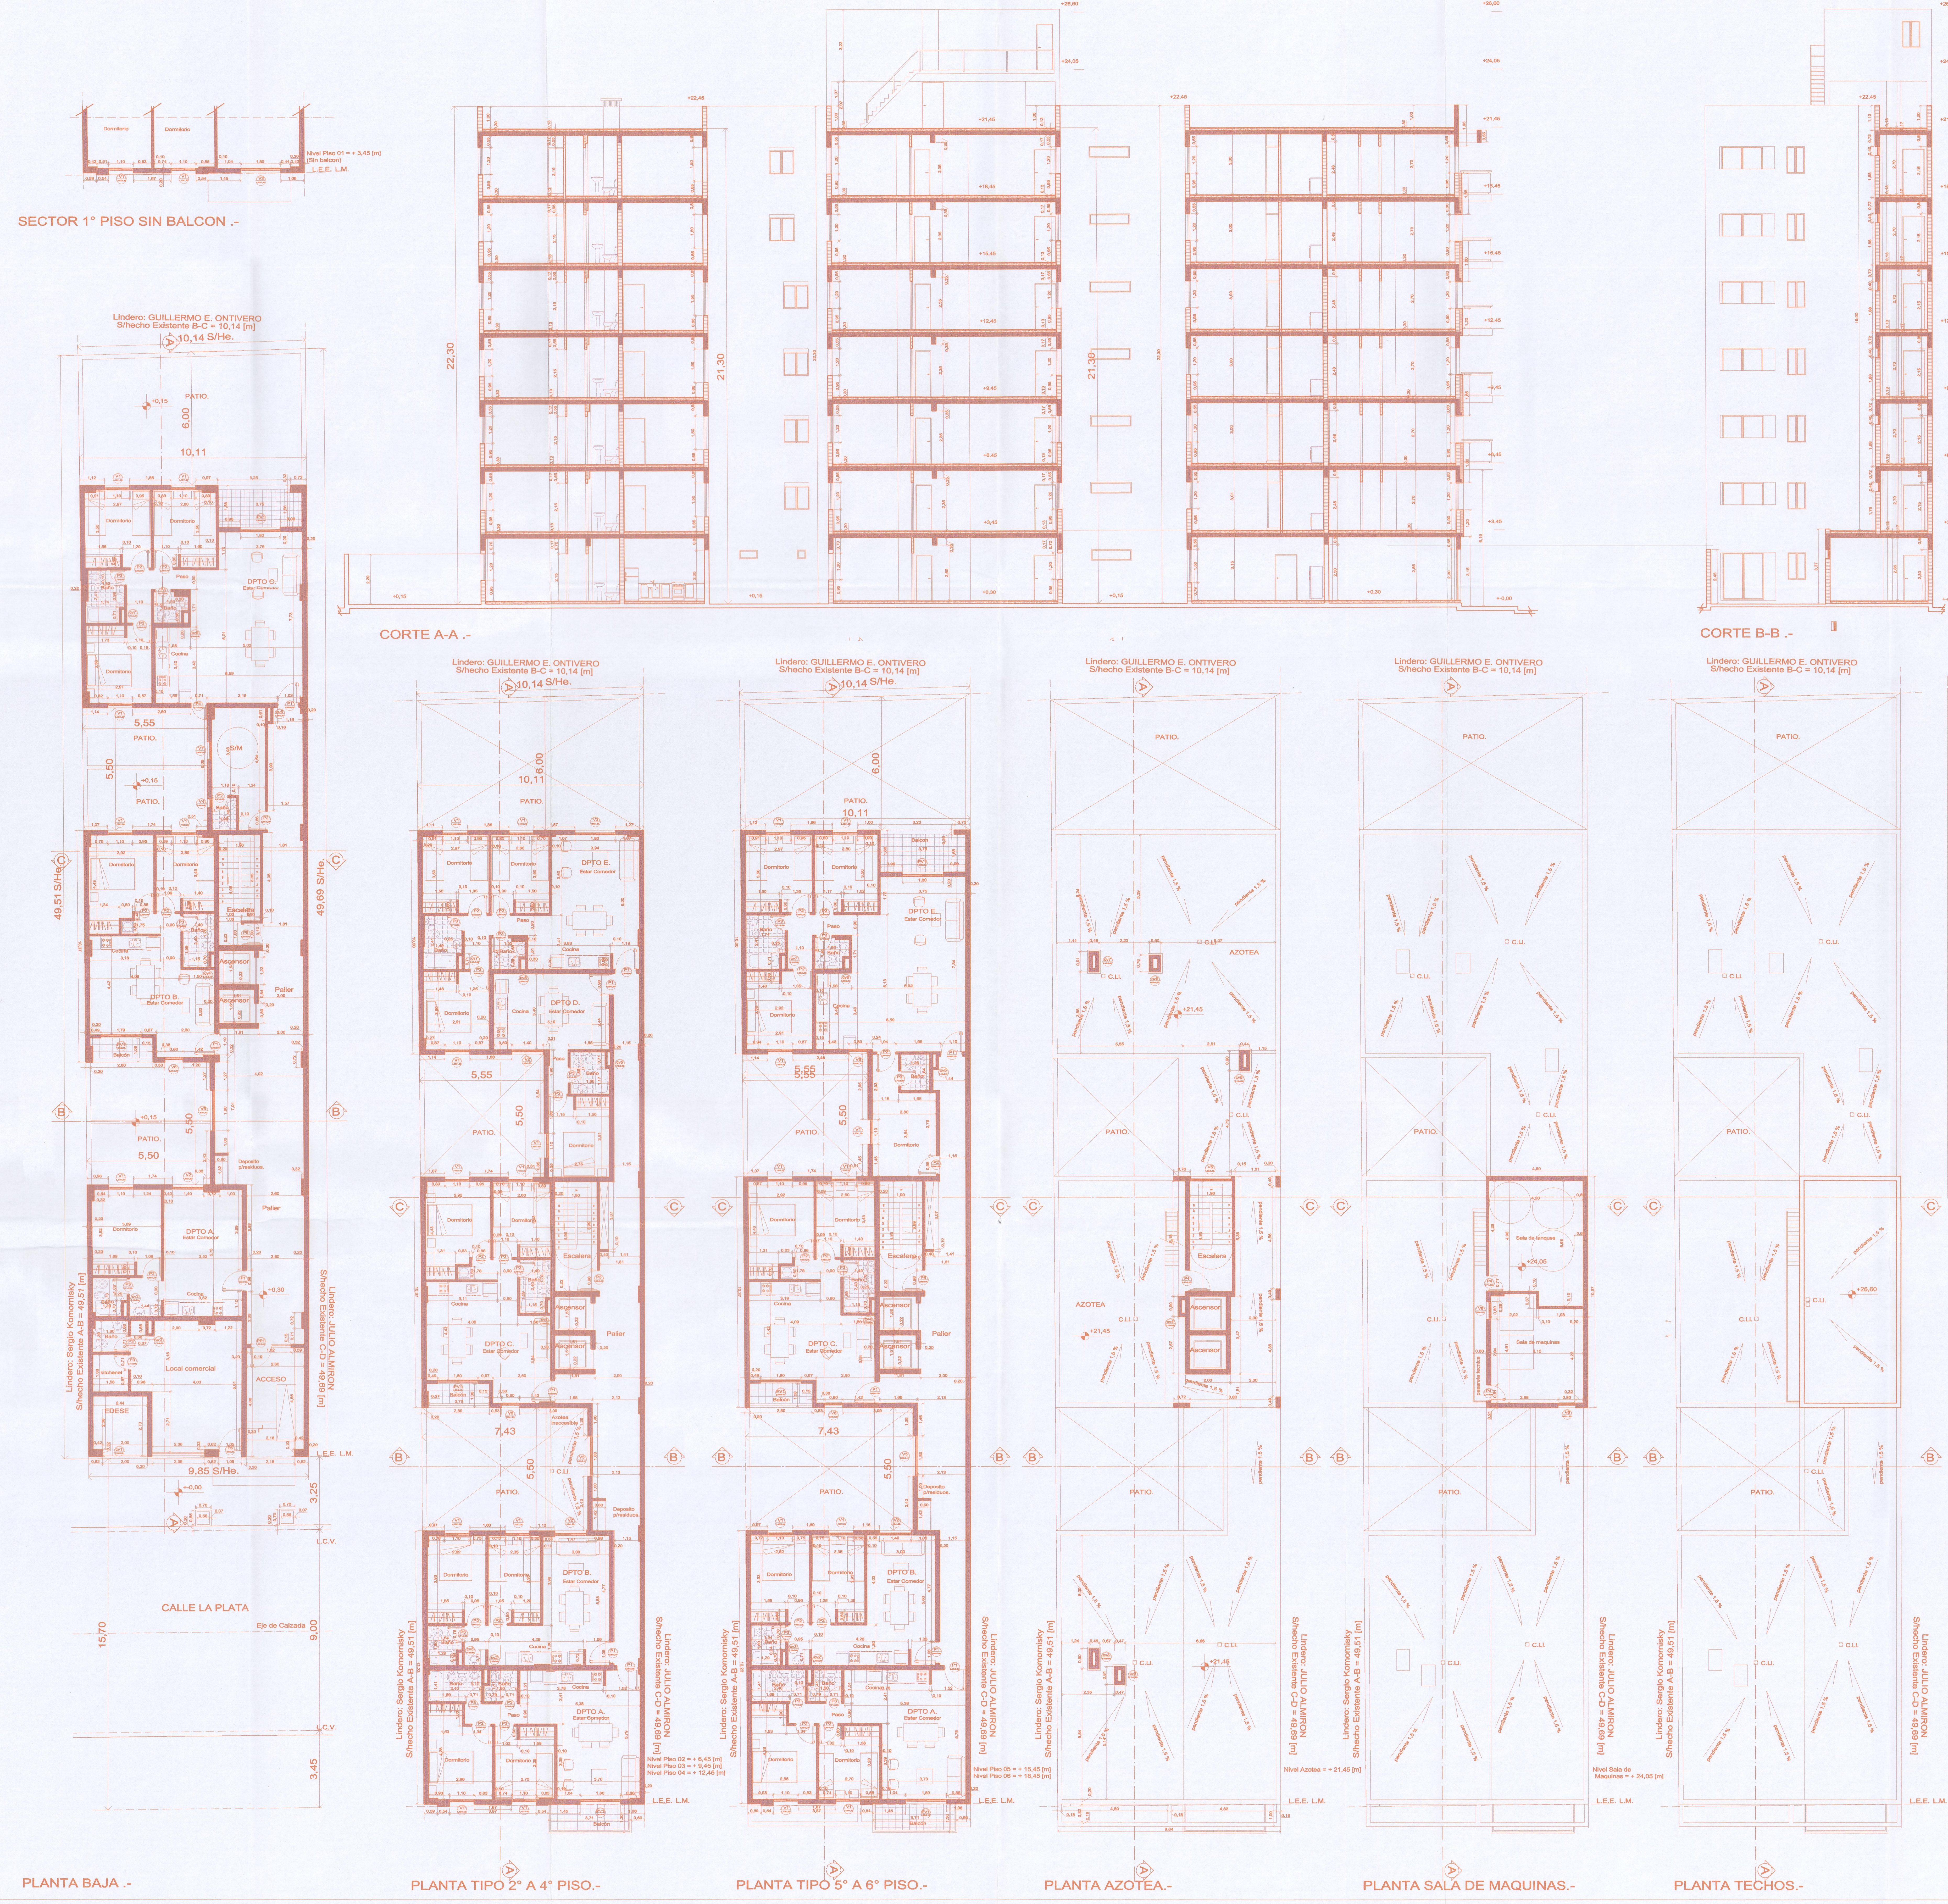


PLANILLA DE ILUMINACIÓN Y VENTILACIÓN									
LOCAL				ABERTURA					OBSERVACIONES
PLANTA		Designación	Superficie	Designación	Ancho [m]	Alto [m]	Superficie % Iluminacion	Superficie % Ventilacion	
PLANTA BAJA	HALL	EDESE	6,20 m²	CV7	0,45	0,45	——	0,20	Ventilacion forzada por extractor
		ACCESO	41,00 m²	P0A	1,80	2,15	——	——	
		BAÑO SALA DE MAQUINAS	1,60 m²	V4	0,40	0,40	0,16	0,16	
		SALA DE MAQUINAS	11,50 m²	V7	0,80	0,40	0,32	0,32	
	LOCAL COM.	LOCAL	63,80 m²	V5	1,60	0,40	3,90	2,15	
		BAÑO KITCHENET	6,00 m²	V4	0,40	0,40	0,16	0,16	
	Dpto A	ESTAR COMEDOR COCINA	20,65 m²	PV1	1,80	2,15	3,87	1,93	
				V6	1,10	1,10	1,21	0,65	
		DORMITORIO 01	12,00m²	V1	1,10	1,20	1,32	0,66	
		BAÑO	3,30 m²	CV3	0,15	0,60	——	0,085	
	Dpto B	ESTAR COMEDOR COCINA	20,65 m²	PV1	1,80	2,15	3,87	1,93	
				V6	1,10	1,10	1,21	0,65	
		DORMITORIO 01	12,00m²	V1	1,10	1,20	1,32	0,66	
		DORMITORIO 02	9,00m²	V1	1,10	1,20	1,32	0,66	
		BAÑO	3,30 m²	CV3	0,15	0,60	——	0,085	
	Dpto C	ESTAR COMEDOR COCINA	26,50 m²	PV1	1,80	2,15	3,90	2,15	
				P4	0,71	2,05	0,72	1,45	
		DORMITORIO 01	10,20 m²	V1	1,10	1,20	1,32	0,66	
		DORMITORIO 02	10,40 m²	V1	1,10	1,20	1,32	0,66	
		DORMITORIO 03	9,10 m²	V1	1,10	1,20	1,32	0,66	
		BAÑO 01	3,50 m²	CV6	0,15	0,60	——	0,09	
		BAÑO 02	2,00m²	V4	0,40	0,40	0,16	0,16	
PISO 01-06	Dpto A	ESTAR COMEDOR COCINA	25,60 m²	PV1	1,80	2,15	3,87	1,93	
		DORMITORIO 01	10,20m²	V1	1,10	1,20	1,32	0,66	
		DORMITORIO 02	9,30m²	V1	1,10	1,20	1,32	0,66	
		BAÑO 01	3,30 m²	CV1	0,15	0,50	——	0,075	
		BAÑO 02	2,10 m²	CV1	0,15	0,50	——	0,075	
	Dpto B	ESTAR COMEDOR COCINA	20,35 m²	V2	1,60	1,20	1,92	0,96	
		DORMITORIO 01	10,20m²	V1	1,10	1,20	1,32	0,66	
		DORMITORIO 02	9,30m²	V1	1,10	1,20	1,32	0,66	
		BAÑO 01	2,76 m²	CV2	0,15	0,50	——	0,075	
	Dpto C	ESTAR COMEDOR COCINA	20,65 m²	PV1	1,80	2,15	3,87	1,93	
				V6	1,10	1,10	1,21	0,65	
		DORMITORIO 01	12,00m²	V1	1,10	1,20	1,32	0,66	
		DORMITORIO 02	9,00m²	V1	1,10	1,20	1,32	0,66	
		BAÑO	3,17 m²	CV3	0,15	0,60	——	0,085	
	Dpto D	ESTAR COMEDOR COCINA	17,63 m²	V2	1,60	1,20	1,92	0,96	
		DORMITORIO 01	9,95m²	V1	1,10	1,20	1,32	0,66	
		BAÑO 01	2,76 m²	CV3	0,15	0,60	——	0,085	
	Dpto E	ESTAR COMEDOR COCINA	26,50 m²	PV1	1,80	2,15	3,90	2,15	
				P4	0,71	2,05	0,72	1,45	
		DORMITORIO 01	10,20 m²	V1	1,10	1,20	1,32	0,66	
		DORMITORIO 02	10,40 m²	V1	1,10	1,20	1,32	0,66	
		DORMITORIO 03	9,10 m²	V1	1,10	1,20	1,32	0,66	
		BAÑO 01	3,50 m²	CV6	0,15	0,60	——	0,09	
		BAÑO 02	2,00m²	V4	0,40	0,40	0,16	0,16	
Areas Comunes		PASILLO	55,00 m²	——	——	——	——	——	
AZOTEA		PALIER	1,25 m²	P4	0,71	2,05	0,72	1,45	
SALA DE MAQUINAS/ TANQUES			40,85 m²	V6	1,10	1,10	1,21	1,21	

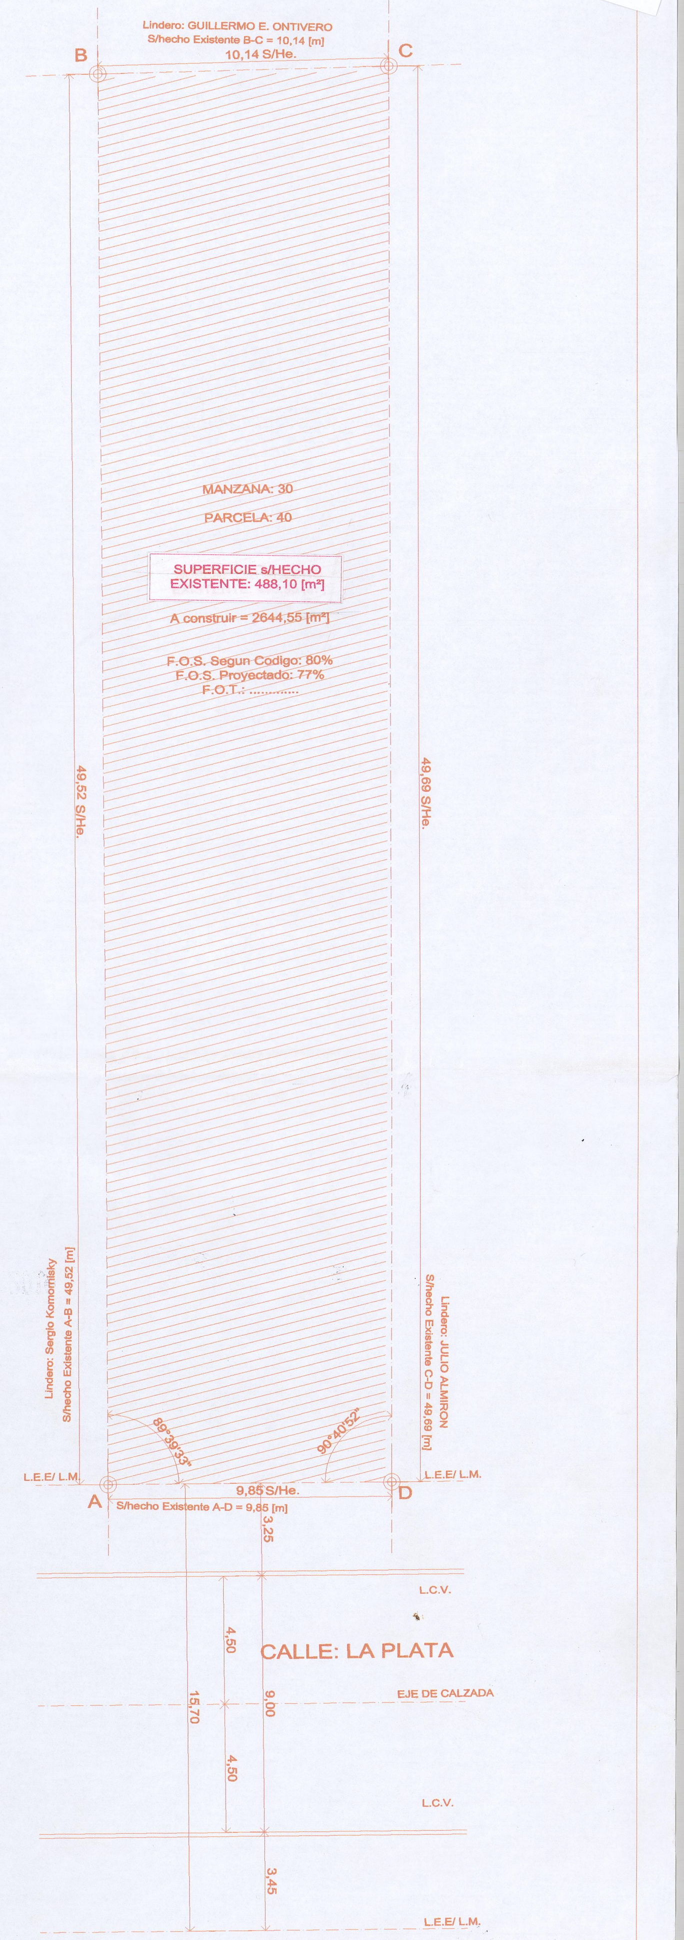


PLANIMETRIA. ESC: 1:150 .-

NOTA 1: EXISTE UN EXCEDENTE O DIFERENCIA DE MEDIDAS S/He. CON RESPECTO AL TITULO QUE ES EXCLUSIVA RESPONSABILIDAD DEL O LOS PROPIETARIOS

NOTA 2: LAS VENTILACIONES DE BAÑO QUE NO DAN AL EXTERIOR SERÁN POR CONDUCTO CON EXTRACTOR.

NOTA 3: LAS MEDIDAS DE ANCHO DE CALLE, CALZADA Y VEREDAS S/He. FUERON VERIFICADAS EN OBRA.

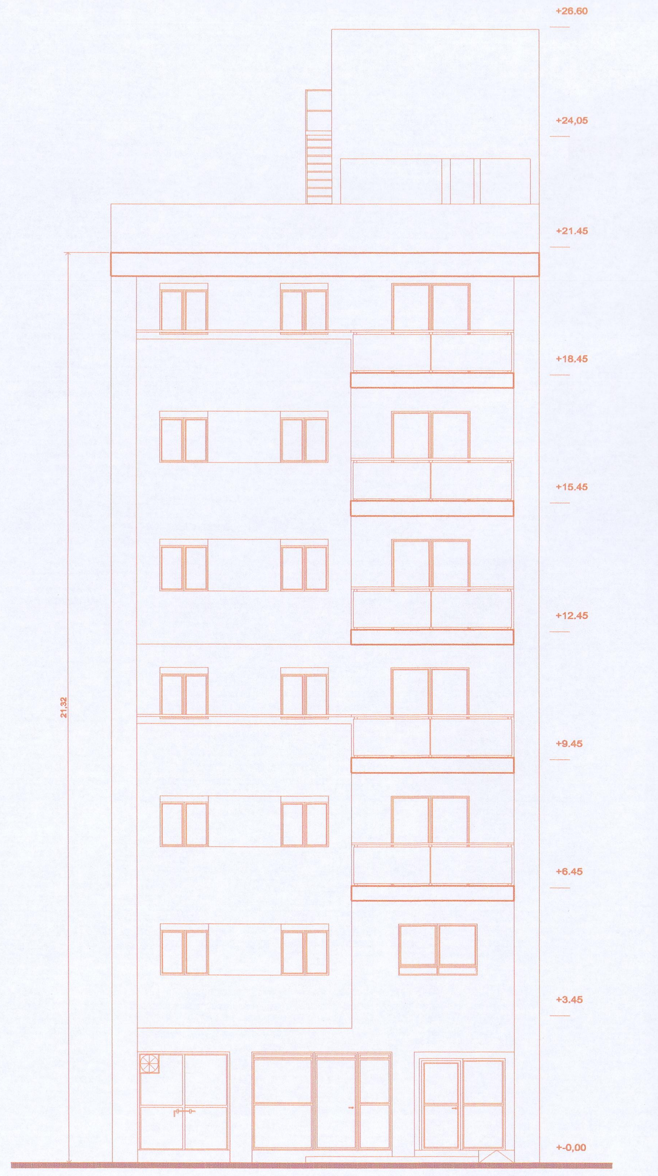

FACHADA.-

DISTR.: 03 ZONA: 03 MANZANA: 30 PARCELA: 40
PADRON INMOBILIARIO Nº: 1-1-1609 ICM: DOMINIO:

DESTINO: Edificio de Departamentos (31 un.) + Local Comercial.-

POSEEDOR: OSCAR ZAMBOLIN.- DNI nº:17.340.728 CUIL nº:20-17340728-9

APODERADO de HERMINIA MICULAN.- DNI nº:3.694.602 CUIL nº:23-03694602-4

NOTA: Poseedor segun Acta de requerimiento N°120, Folio N° 26 del libro ... Registro Notarial N° 3. Notario Dr. Felipe Ledesma

UBICACION: Calle La Plata n° 680.-
BARRIO: Juan Bautista Alberdi.-
LOCALIDAD: Santiago Del Estero (Capital).-
ESCALAS: 1:100 / 150.-

Superficie del Terreno: s/he: 488,10 m²
Superficie a Construir: 2644,55 m²

CROQUIS DE UBICACION:
Chaco — La Plata — Chacabuco — H. Yrigoyen
24,00 9,85 15,70 97,73
S/He. B-C = 10,14 [m]

	La Plata s/He E.
ANCHO DE CALLE	15,70 [m]
ANCHO DE VEREDA	3,25 [m]
ANCHO DE CALZADA	9,00 [m]

POSEEDOR:
Domicilio:
PROYECTO: Arq. PABLO GOGNA Arquitecto Mat. Prof. Nº 0243
Domicilio:
Dir. TECNICA: Arq. PABLO GOGNA Arquitecto Mat. Prof. Nº 0243
Domicilio:
CATEGORIA DEL C.A.S.E.: A
PAVIMENTO: SI
SERVICIOS CLOACALES: SI

DESIGNACION: OBRA NUEVA 01-ARQUITECTURA

OBSERVACIONES: Las referencias al título de Dominio son meramente indicativas, y la aprobación administrativa no valora los derechos que de ellos emergen

02 MAY 2019

186051
COLEGIO DE ARQUITECTOS LEY 5554/87 SANTIAGO DEL ESTERO
15 MAR 2019
PROYECTO Y DIRECCION DE OBRA
SUSANA ABECASSIS Arquitecta Secretaria Técnica Adjunta Colegio de Arquitectos S D E

SECRETARIA DE ECONOMIA Municipalidad de la Capital SGO. DEL ESTERO DIREC. DE SUELO URBANO

MUNICIPALIDAD DE LA CIUDAD DE SANTIAGO DEL ESTERO SECRETARIA DE ECONOMIA
APROBADO
DIRECCIÓN DE SUELO URBANO
EXPEDIENTE 07-M-2019
FECHA 18/01/2021

Arq. ESTER R. CHALOM SUB-DIRECTORA DIRECCION DE SUELO URBANO

PERMISO DE COMIENZO DE OBRA Nº 4574 DIRECCION DE SUELO URBANO
ANDRES FEDERICO LOPEZ ARQUITECTO - M.P. 456 DEPARTAMENTO INSPECTORES DIRECCION DE SUELO URBANO

M.G. ALEJANDRO J. LOPEZ Dirección de Suelo Urbano

DIRECCION ... EXPE 07-M-2019 FECHA ...