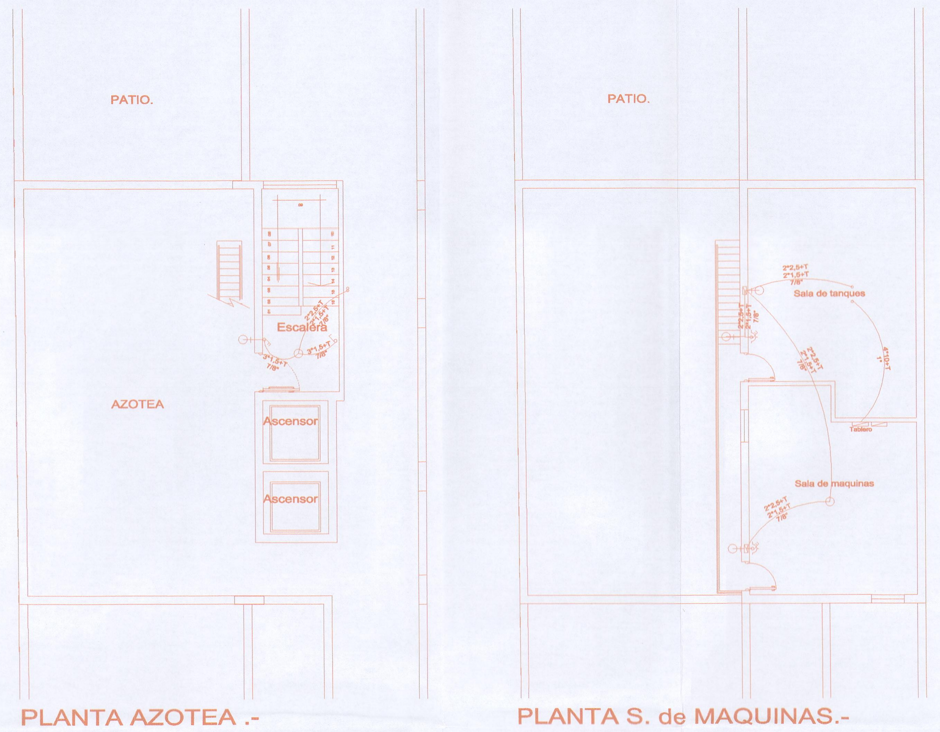

PLANTA AZOTEA .-

PLANTA S. de MAQUINAS.-

DETALLE DE PUESTA A TIERRA.-

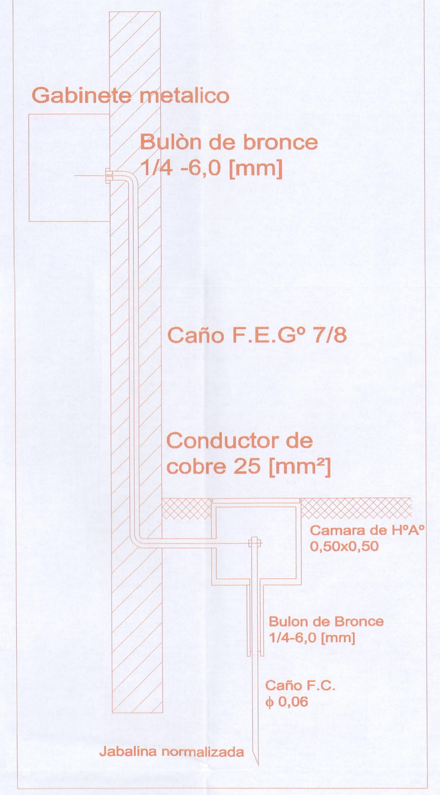

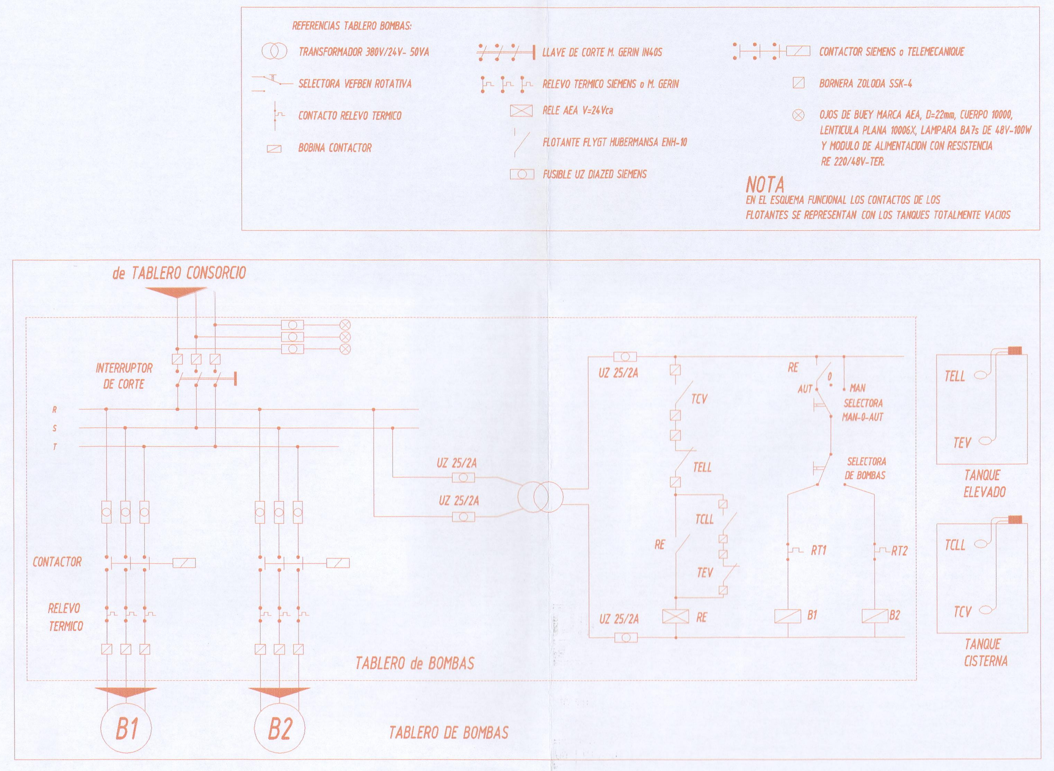

SIMBOLOGIA.-

- -Caño corrugado iluminacion y tomas (caracteristicas indicadas en planos).-
- -Caño corrugado tomas de A.A. (caracteristicas indicadas en planos).-
- -Cañeria de P.V.C. enterrada.-
- -Centro de iluminacion.-
- -Aplique.-
- -Toma monofasico.-
- -Llave con toma monofasico.-
- -Llave de efectos.-
- -Llave con temporizador.-
- -Cañeria montantes de cables electricos.-
- -Tablero seccional.-
- -Caja de pase (dimensiones indicadas en planos).-
- -T.G.: Tablero General.-
- -Tomacorriente monofasico 16A para circuito de A.A..-
- -Detector de movimientos.-
- -Pulsador Campanillas.-
- -Campanilla (Timbre).-

NOTAS:

1- Todas las cañerias no indicadas seran de un diametro no menor a 7/8.

2- Toda la cañeria sera recorrida por un conductor verde-amarillo para puesta a tierra de 2,50 [mm²] de seccion.

3-Todos los cables colocador en cañerias seran unipolres flexibles de cobre aislado con P.V.C. antillama, tension nominal 450/750 V - NORMA I.R.A.M. 2183, y seran de la seccion indicada en los planos.

4- Las llaves de efectos se colocaran en cajas de 100x50x42 [mm] a 1,20 [m] del Nivel de Piso Teminado (N.P.T.) y a 0,15 [m] dela jamba de la puerta.

5- Los tomacorrientes se colocaran en cajas de 100x50x42 [mm] a 0,30 [m] del N.P.T. sobre la mesada se colocaran a 1,20 [m] del N.P.T. y enlos baños se colocaran a 1,20 del N.P.T.

6-Los apliques se colocaran a 2,20 [m] del N.P.T.

7- Las cajas de paso se colocaran a 0,20 [m] por debajo del cielo raso o losas. en caso de cielorrasos desmontables o con tapa de acceso las cajas de paso se colocaran sobre el cielorraso.

8- Para los casos especiales las alturas de los temacorrientes, apliques, llaves y cajas de paso seran indicadas en los planos.

9- Las jabalinas indicadas en los planos seran de caracteristicas segun el terreno para lograr las resistencias correspondientes, con tomacable y caja de inspeccion 25x25 HºAº. La misma se conectara a la pat. general.

PUESTO DE MEDICION MULTIPLE SEGUN TIPICO CONSTRUCTIVO E.D.E.S.E. S.A.

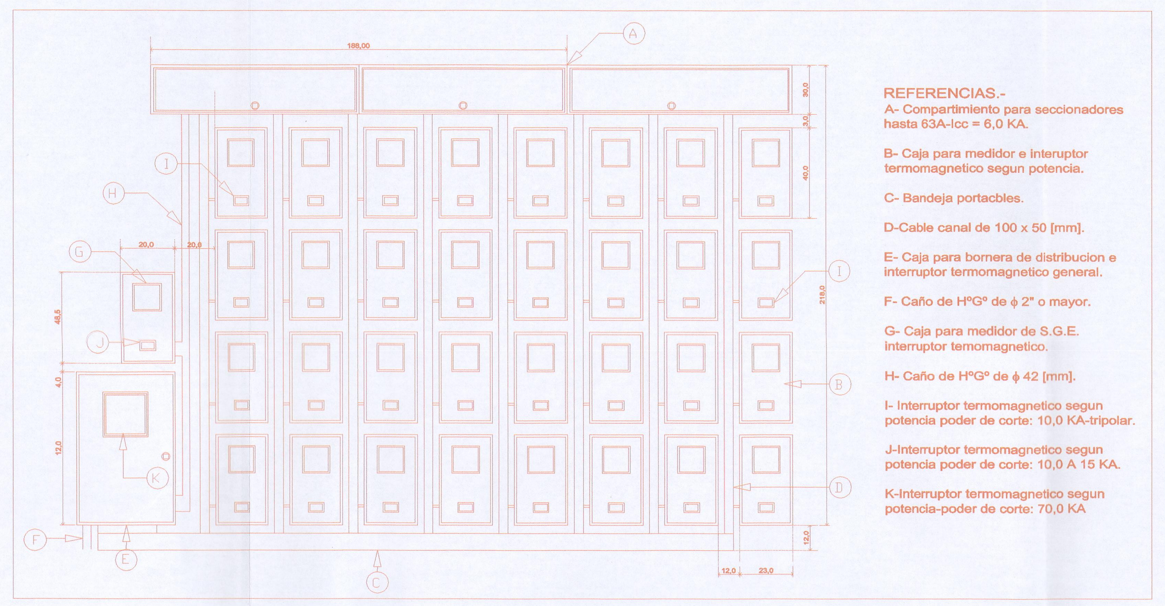

DIAGRAMA MONTANTE DE SEÑALES DEBILES.-

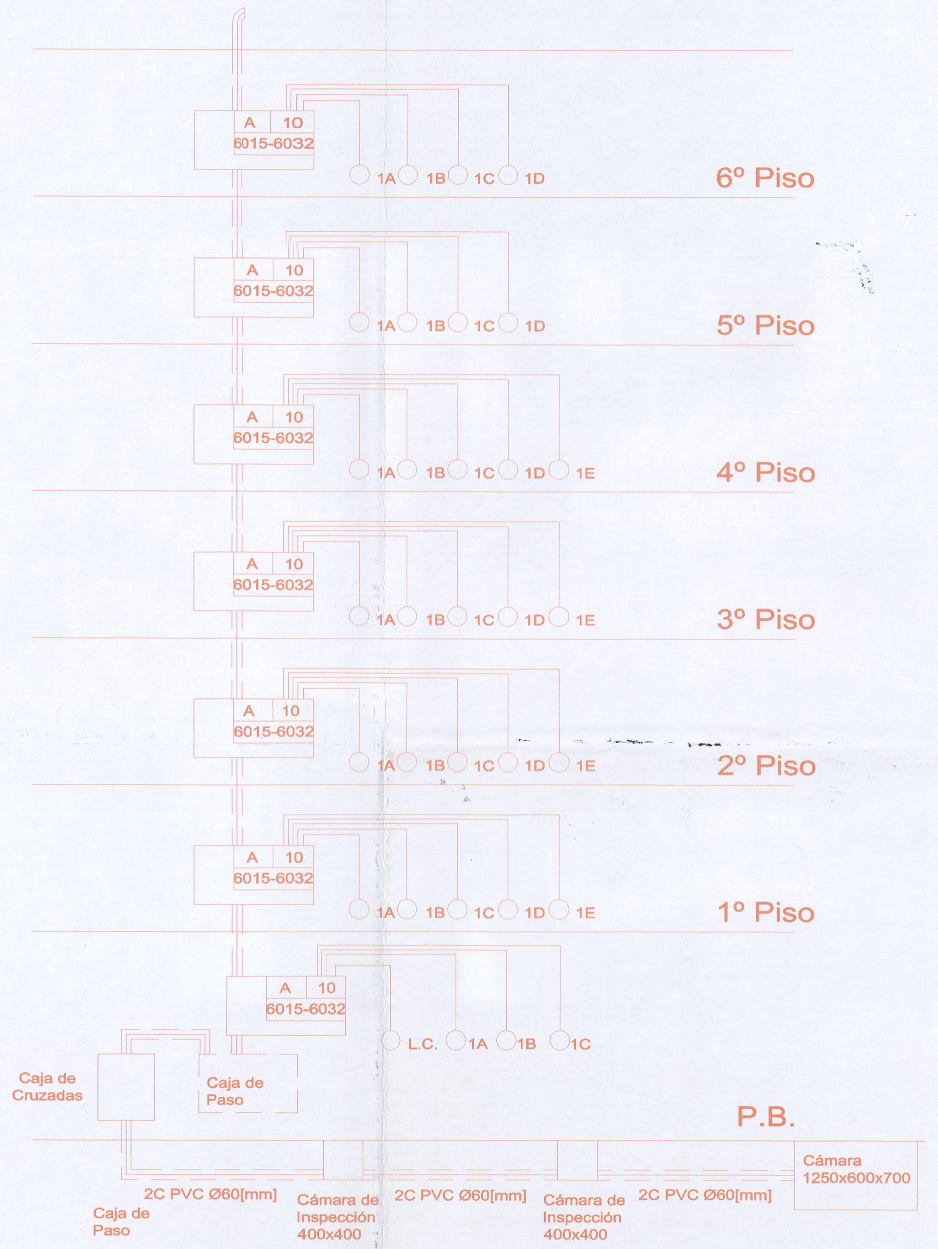

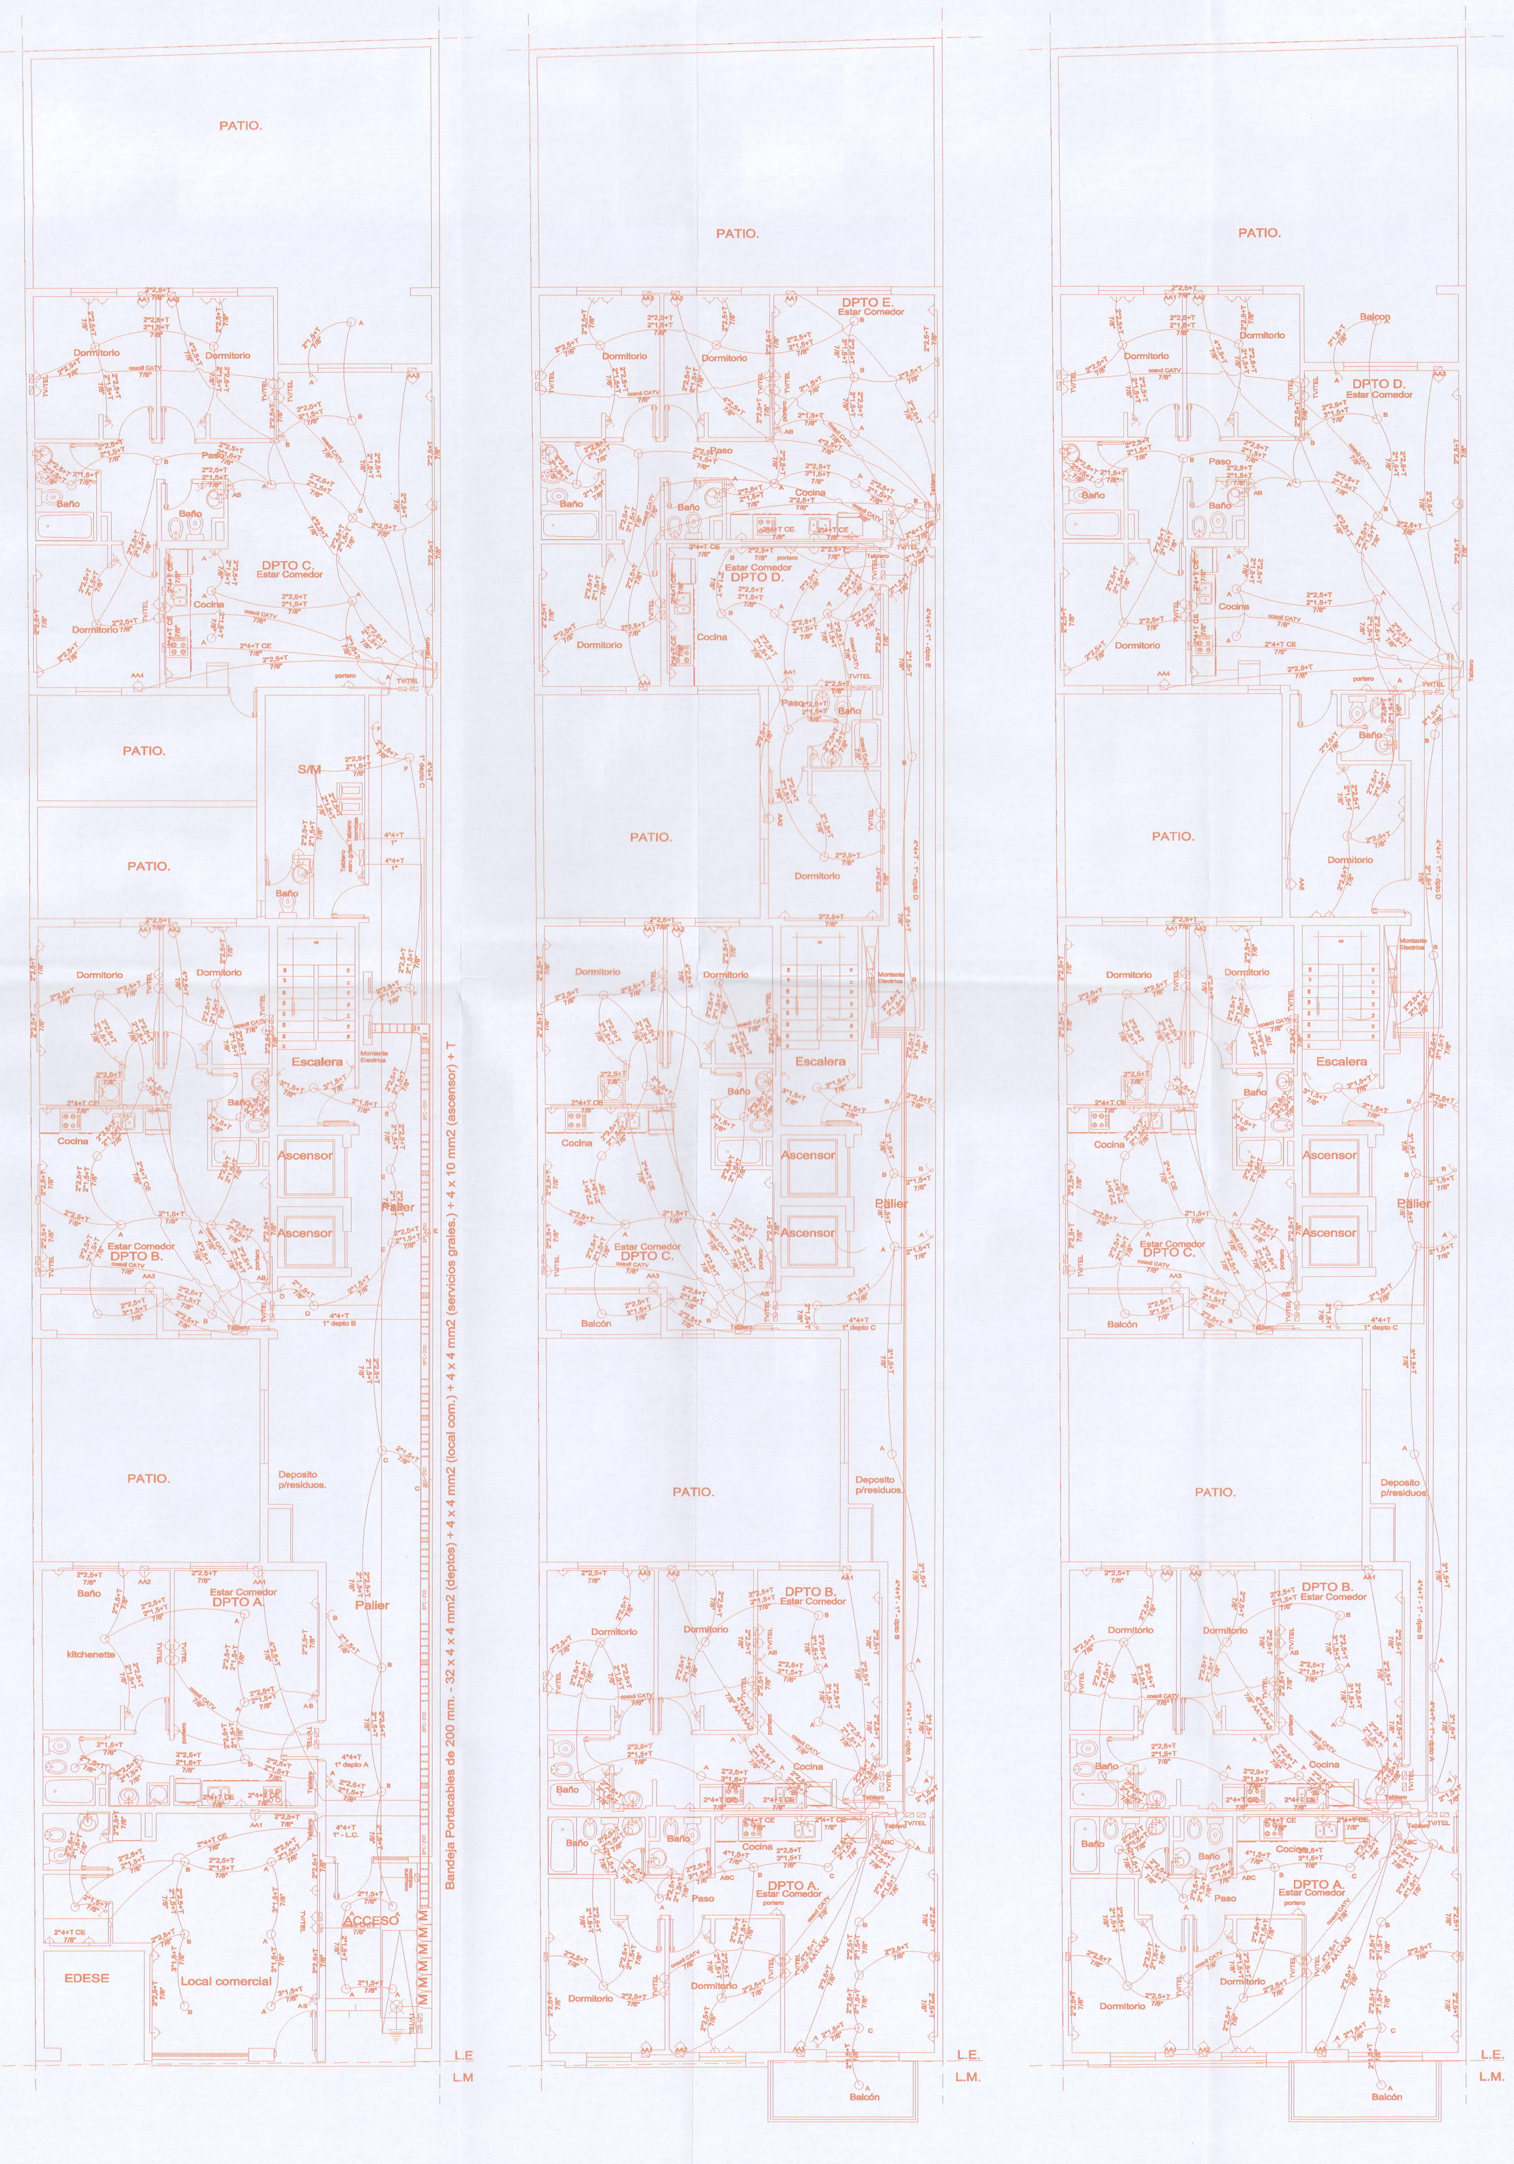

PLANTA BAJA .-

PLANTA TIPO 1 a 4 .-

PLANTA TIPO 5 a 6 .-

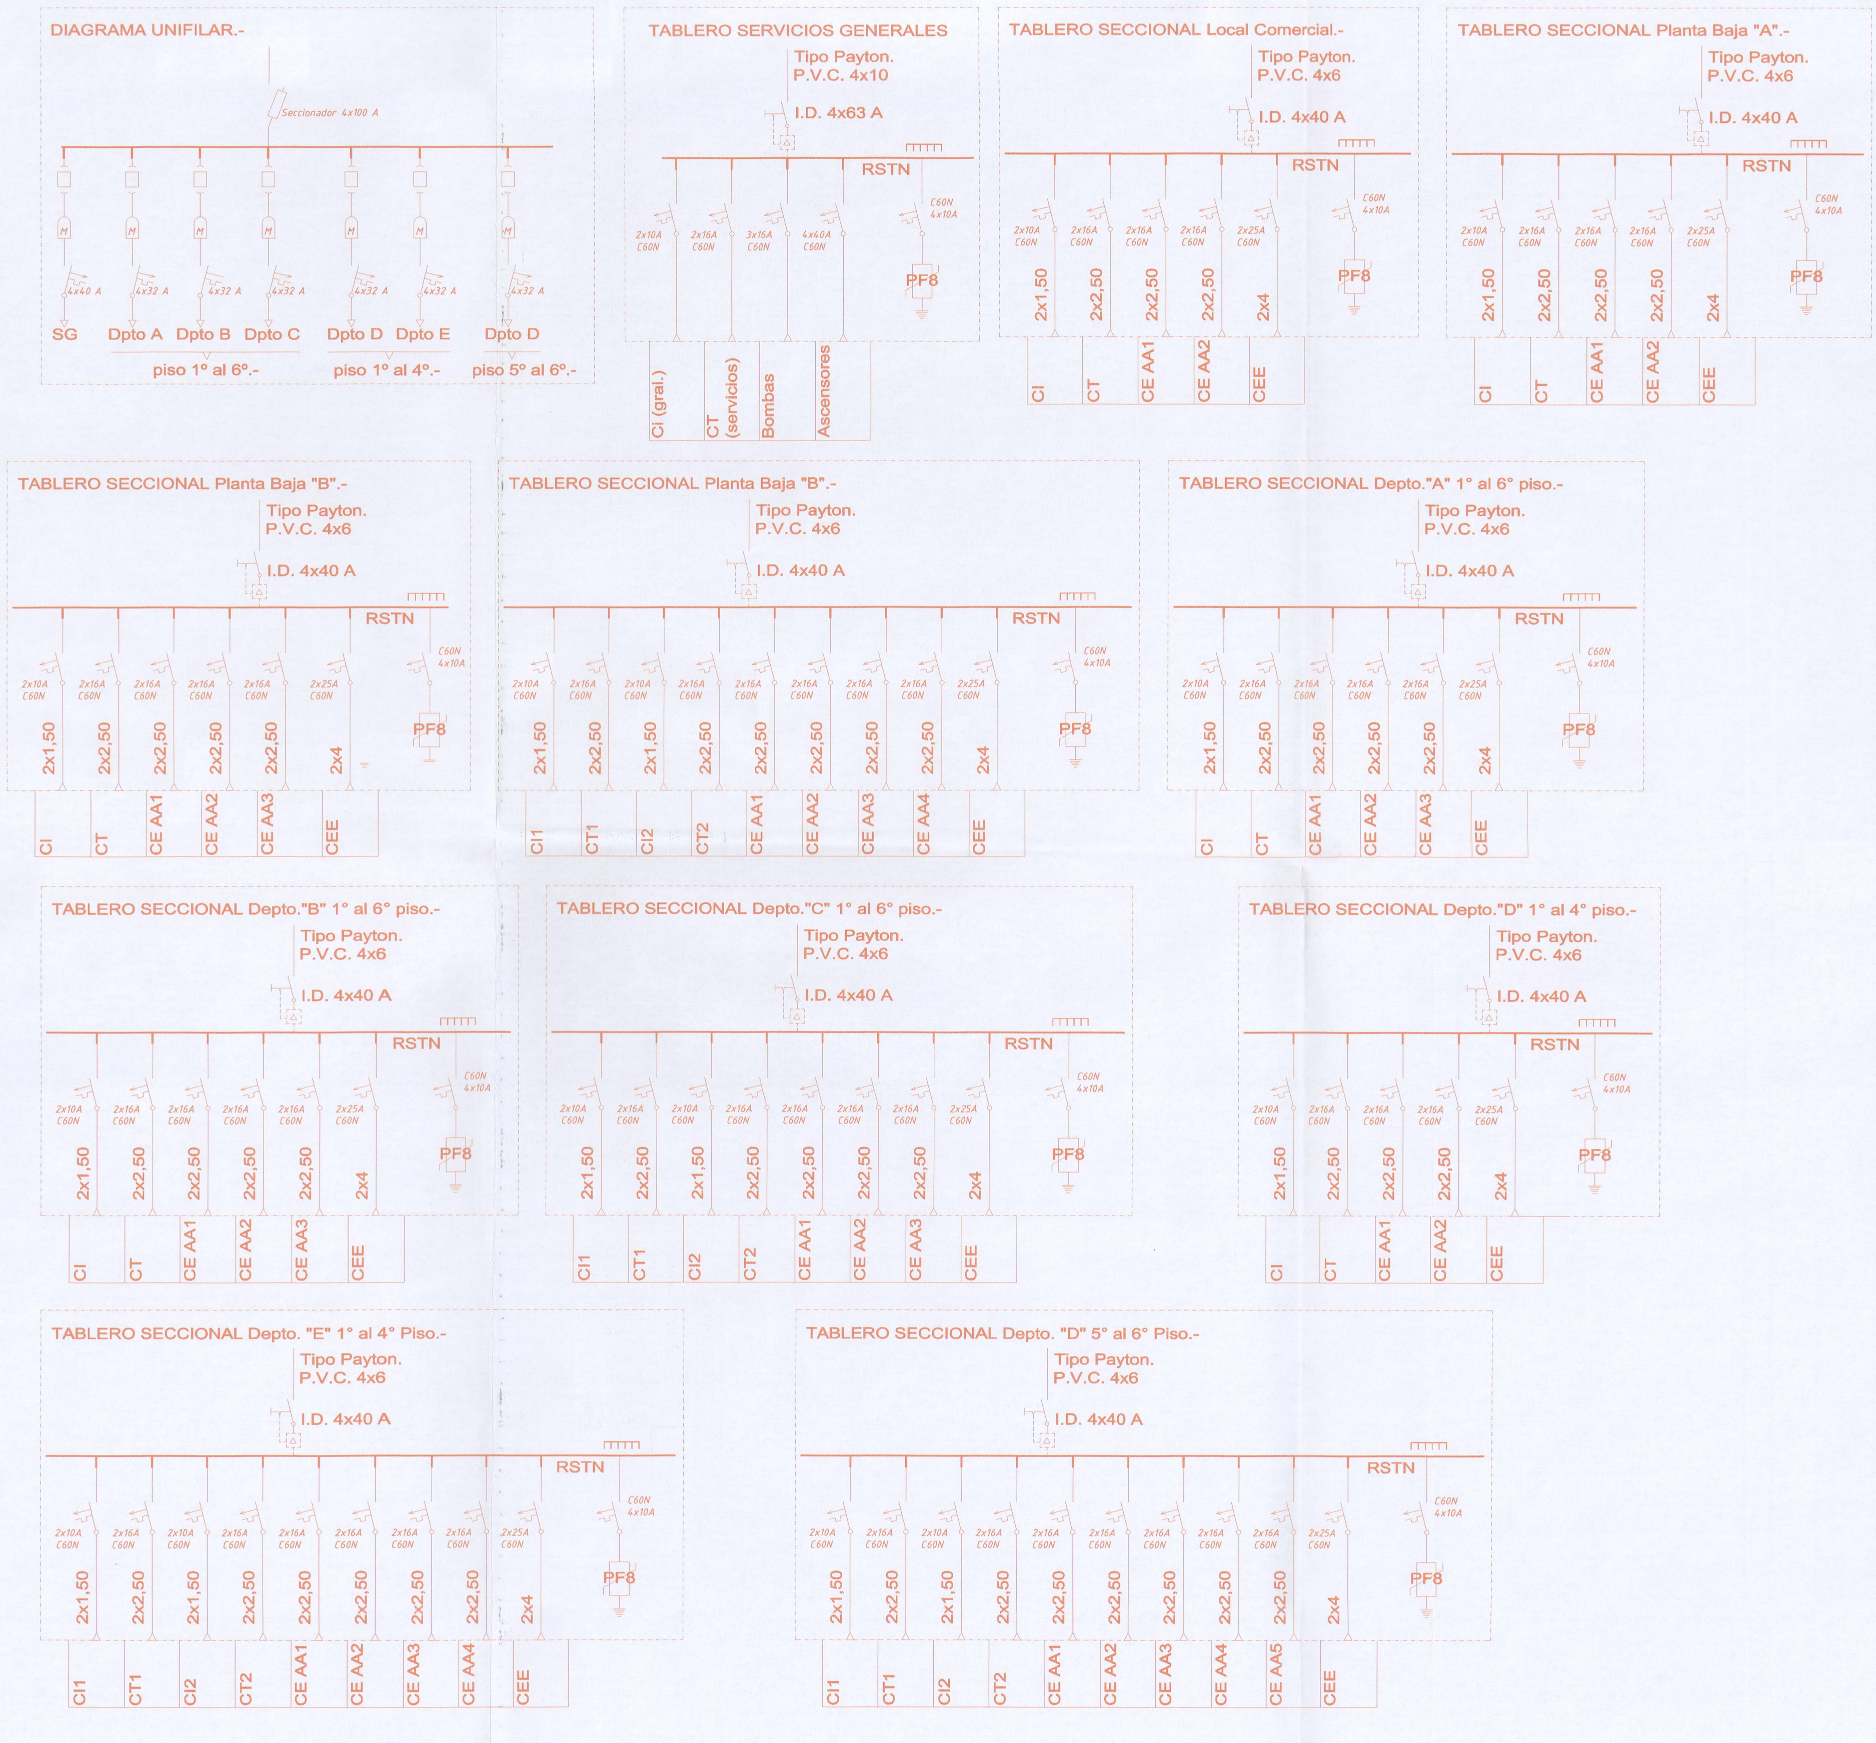

PLANILLA DE CALCULO EDIFICIO CALLE PLATA

Desig.	Circuito (Número)	Bocas (Potencia unitaria) Luz W 10	18	60	75	Toma W 100	200	1000	2500	4000	Potencia Luz (Watt)	Toma (Watt)	Pot.Tot (W)	Int. Total (A)	Pot. Tot. Fac Sim. 0,66 (W)	Cor. Tot. fact. sim. 0,66 (A)	Secc. de cable (mm2)	Calibre Prot. (A)	Calibre Prot. dif (A)
Tablero de servicios generales	Bba. Agua							1			0	1000	1000	1,8	1000,0	1,8	2,5	16	40 A
	Asc.								1		0	2500	2500	4,5	2500,0	4,5	2,5	40	
	Luz Ext1	82									820	0	820	4,4	820,0	4,4	4	16	
	Tomas						8				0	1600	1600	8,6	1600,0	8,6	4	25	
	Total										820	5100							
	Simultaneidad (0,8)						0,80				656	4080							
	Corriente maxima trifasica prevista (A)=								8,5		Seccion de cables 3 x 10 mm2+ 1 x 6 mm2								
Planta baja – Local comercial	CI		8								144	0	144	0,8	144,0	0,8	1,5	10	40 A
	CT						8				0	1600	1600	8,6	1600,0	8,6	2,5	16	
	CAA1								1		0	2500	2500	13,4	1650,0	8,8	2,5	16	
	CE									1	0	4000	4000	21,4	4000,0	21,4	4	25	
	Total										144	8100							
	Simultaneidad (0,8)						0,8				115,2	6480							
	Corriente maxima trifasica prevista (A)=								11,8		Seccion de cables 4 x 4 mm2								
Planta baja – Departamento A	CI		10								180	0	180	1,0	180,0	1,0	1,5	10	40 A
	CT						8				0	1600	1600	8,6	1600,0	8,6	2,5	16	
	CAA1								1		0	2500	2500	13,4	1650,0	8,8	2,5	16	
	CAA2								1		0	2500	2500	13,4	1658,8	8,8	2,5	16	
	CE									1	0	4000	4000	21,4	4000,0	21,4	4	25	
	Total										180	10600							
	Simultaneidad (0,8)						0,8				144	8480							
	Corriente maxima trifasica prevista (A)=								15,4		Seccion de cables 4 x 4 mm2								
Planta baja – Departamento B	CI		10								0	0	0	0,0	0,0	0,0	1,5	10	40 A
	CT						8				0	64	64	0,3	64,0	0,3	2,5	16	
	CAA1								1		0	0	0	0,0	0,0	0,0	2,5	16	
	CAA2								1		0	0	0	0,0	0,0	0,0	2,5	16	
	CAA3								1		0	0	0	0,0	0,0	0,0	2,5	16	
	CE									1	0	0	0	0,0	0,0	0,0	4	25	
	Total										0	64							
	Simultaneidad (0,8)						0,8				0	51,2							
	Corriente maxima trifasica prevista (A)=								0,1		Seccion de cables 4 x 4 mm2								
Planta baja – Departamento C	CI1		9								162		162	0,9	162,0	0,9	1,5	10	40 A
	CI2		5								90		90	0,5	90,0	0,5	1,5	10	
	CT1						6					1200	1200	6,4	1200,0	6,4	2,5	16	
	CT2						10					2000	2000	10,7	2000,0	10,7	2,5	16	
	CAA1								1			2500	2500	13,4	2500,0	13,4	2,5	16	
	CAA2								1			2500	2500	13,4	2500,0	13,4	2,5	16	
	CAA3								1			2500	2500	13,4	2500,0	13,4	2,5	16	
	CE									1		4000	4000	21,4	4000,0	21,4	4	25	
	Total										252	14700							
	Simultaneidad (0,8)						0,8				201,6	11760							
	Corriente maxima trifasica prevista (A)=								21,4		Seccion de cables 4 x 4 mm2								
Pisos desde el 1° al 6° – Departamento A	CI		11								198	0	198	1,1	198,0	1,1			40 A
	CT						10				0	2000	2000	10,7	2000,0	10,7			
	CAA1								1		0	2500	2500	13,4	1650,0	8,8			
	CAA2								1		0	2500	2500	13,4	1658,8	8,8			
	CAA3								1		0	2500	2500	13,4	2500,0	13,4			
	CE									1	0	4000	4000	21,4	4000,0	21,4			
	Total										198	13500							
	Simultaneidad (0,8)						0,8				158,4	10800							
	Corriente maxima trifasica prevista (A)=								19,6		Seccion de cables 4 x 4 mm2								
	TOTAL DEPARTAMENTOS A (6 SEIS)								6		1188	64800							
Pisos desde el 1° al 6° – Departamento B	CI		10								180	0	180	1,0	180,0	1,0			40 A
	CT						12				0	2400	2400	12,8	2400,0	12,8			
	CAA1								1		0	2500	2500	13,4	1650,0	8,8			
	CAA2								1		0	2500	2500	13,4	1658,8	8,8			
	CAA3								1		0	2500	2500	13,4	2500,0	13,4			
	CE									1	0	4000	4000	21,4	4000,0	21,4			
	Total										180	13900							
	Simultaneidad (0,8)						0,8				144	11120							
	Corriente maxima trifasica prevista (A)=								20,2		Seccion de cables 4 x 4 mm2								
	TOTAL DEPARTAMENTOS A (6 SEIS)								6		1080	66720							
Pisos desde el 1° al 6° – Departamento C	CI1		6								108	0	108	0,6	108,0	0,6			40 A
	CI2		4								72	0	72	0,4	72,0	0,4			
	CT1						4				0	800	800	4,3	800,0	4,3			
	CT2						6				0	1200	1200	6,4	1200,0	6,4			
	CAA1								1		0	2500	2500	13,4	2500,0	13,4			
	CAA2								1		0	2500	2500	13,4	2500,0	13,4			
	CAA3								1		0	2500	2500	13,4	2500,0	13,4			
	CE									1	0	4000	4000	21,4	4000,0	21,4			
	Total										180	13500							
	Simultaneidad (0,8)						0,8				144	10800							
	Corriente maxima trifasica prevista (A)=								19,6		Seccion de cables 4 x 4 mm2								
	TOTAL DEPARTAMENTOS A (6 SEIS)								6		864	64800							
Pisos desde el 1° al 6° – Departamento D	CI		7								126	0	126	0,7	126,0	0,7			40 A
	CT						7				0	1400	1400	7,5	1400,0	7,5			
	CAA1								1		0	2500	2500	13,4	1650,0	8,8			
	CAA2								1		0	2500	2500	13,4	1658,8	8,8			
	CAA3								1		0	2500	2500	13,4	2500,0	13,4			
	CE									1	0	4000	4000	21,4	4000,0	21,4			
	Total										126	12900							
	Simultaneidad (0,8)						0,8	0			100,8	10320							
	Corriente maxima trifasica prevista (A)=								18,6		Seccion de cables 4 x 4 mm2								
	TOTAL DEPARTAMENTOS A (6 SEIS)								6		604,8	61920							
Pisos desde el 1° al 6° – Departamento E	CI1		8								144	0	144	0,8	144,0	0,8			40 A
	CI2		5								90	0	90	0,5	90,0	0,5			
	CT1						6				0	1200	1200	6,4	1200,0	6,4			
	CT2						9				0	1800	1800	9,6	1800,0	9,6			
	CAA1								1		0	2500	2500	13,4	2500,0	13,4			
	CAA2								1		0	2500	2500	13,4	2500,0	13,4			
	CAA3								1		0	2500	2500	13,4	2500,0	13,4			
	CE									1	0	4000	4000	21,4	4000,0	21,4			
	TOTAL										234	14500							
	Corriente maxima trifasica prevista (A)=								26,4		Seccion de cables 4 x 4 mm2								
	TOTAL DEPARTAMENTOS A (6 SEIS)								6		1404	87000							
TOTAL	Simultaneidad edificio								0,4		2503	150416							

Suma de potencias (KW)	152,9
Corriente trifasica equilibrada (A)	273,7
Maxima corriente desbalanceada (A)	328,4
Potencia a solicitar en la factibilidad (KW)	168

DIAGRAMA DE MONTANTE

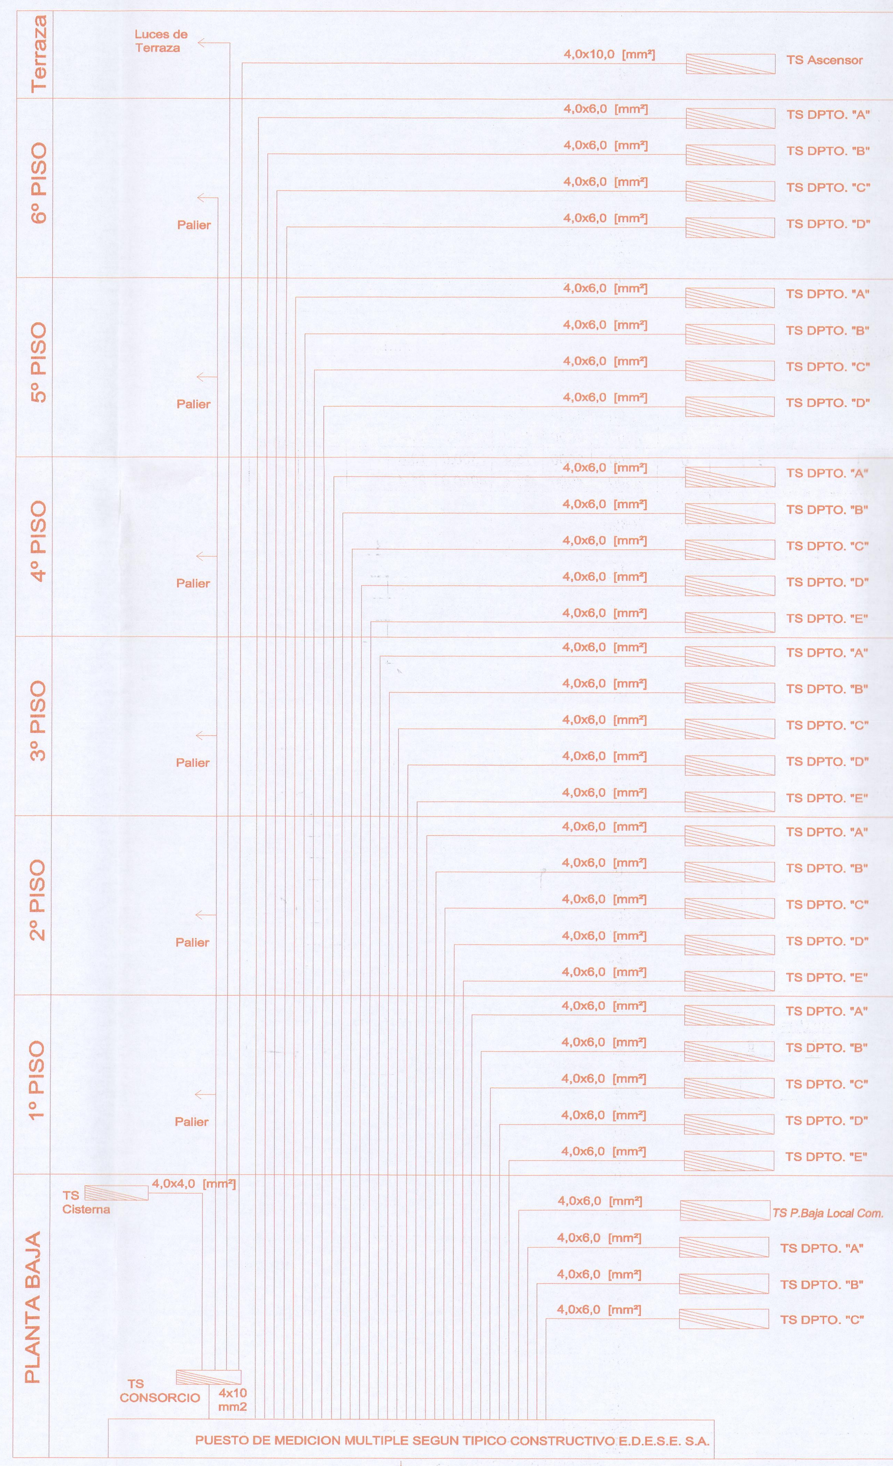

DISTR.: 03 ZONA: 03 MANZANA: 30 PARCELA: 40

PADRON INMOBILIARIO Nº: 1-1-1609 ICM: DOMINIO:

186051

DESTINO: Edificio de Departamentos (31 un.) + Local Comercial.-

POSEEDOR: OSCAR ZAMBOLIN.- DNI n°:17.340.728 CUIL n°:20-17340728-9

APODERADO de HERMINIA MICULAN.- DNI n°:3.694.602 CUIL n°:23-03694602-4

NOTA: Poseedor segun Acta de requerimiento N°120, Folio N° 280 del libro N°126. Registro Notarial N° 3. Notario Dr. Felipe Ledesma

UBICACION: Calle La Plata n° 680.-

BARRIO: Juan Bautista Alberdi.-

LOCALIDAD: Santiago Del Estero (Capital).-

ESCALAS: 1:100 / 150.-

Colegio de Arquitectos Ley 5654/87 Santiago del Estero — 15 MAR 2019

Secretaria de Economia – Municipalidad de la Capital Sgo. del Estero – Direc. de Suelo Urbano

PROYECTO Y DIRECCION DE OBRA – SUSANA ABECASSIS, Arquitecta, Secretaria Técnica Adjunta, Colegio de Arquitectos S D E

Superficie del Terreno: s/he: 488,10 m²

Superficie a Construir: 2644,55 m²

PROPIETARIO:

Domicilio:

CROQUIS DE UBICACION:

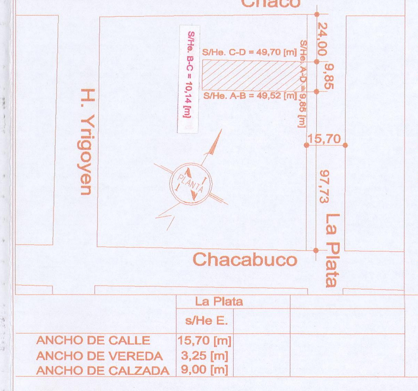

PROYECTO: Arq. PABLO GOGNA Arquitecto Mat. Prof. Nº 0243

Domicilio:

Dir. TECNICA: Arq. PABLO GOGNA Arquitecto Mat. Prof. Nº 0243

Domicilio:

CATEGORIA DEL C.A.S.E.

	La Plata s/He E.
ANCHO DE CALLE	15,70 [m]
ANCHO DE VEREDA	3,25 [m]
ANCHO DE CALZADA	9,00 [m]

PAVIMENTO:

SERVICIOS CLOACALES:

DESIGNACION: OBRA NUEVA

01-ELECTRICIDAD

OBSERVACIONES:

02 MAY 2019 — Las referencias al Titulo de Dominio son meramente indicativas, y la aprobación administrativa no valora los derechos que de ellos emergen

MUNICIPALIDAD DE LA CIUDAD DE SANTIAGO DEL ESTERO – SECRETARIA DE ECONOMIA – APROBADO – DIRECCION DE SUELO URBANO – EXPEDIENTE: 07-M-2019 – FECHA: 18/01/2021