



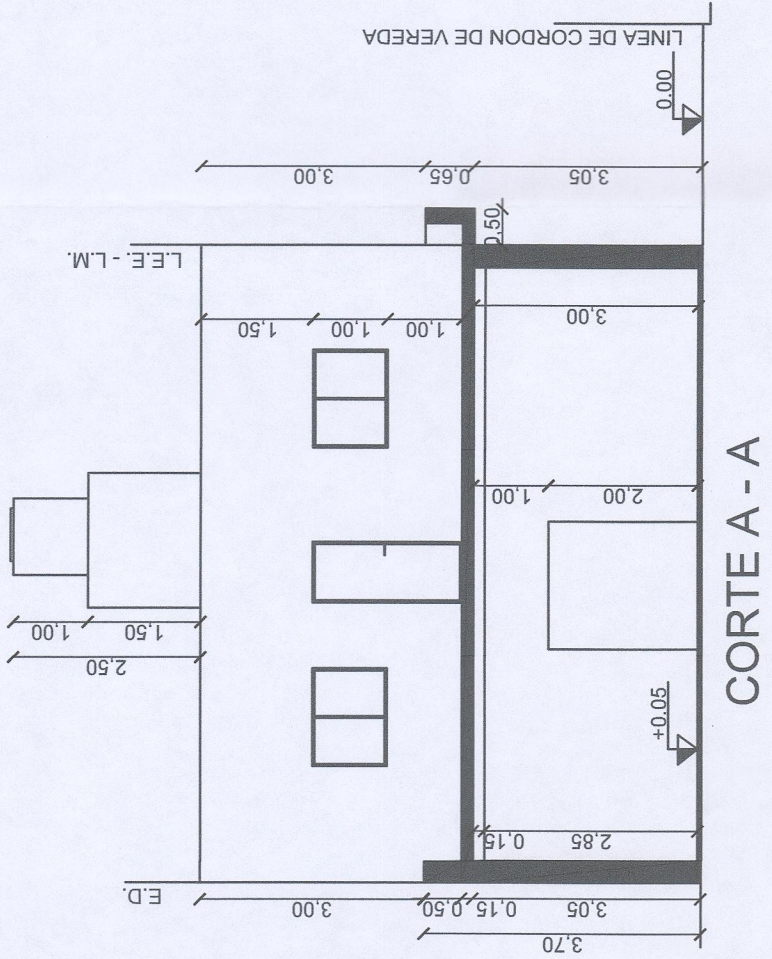


CORTE A - A

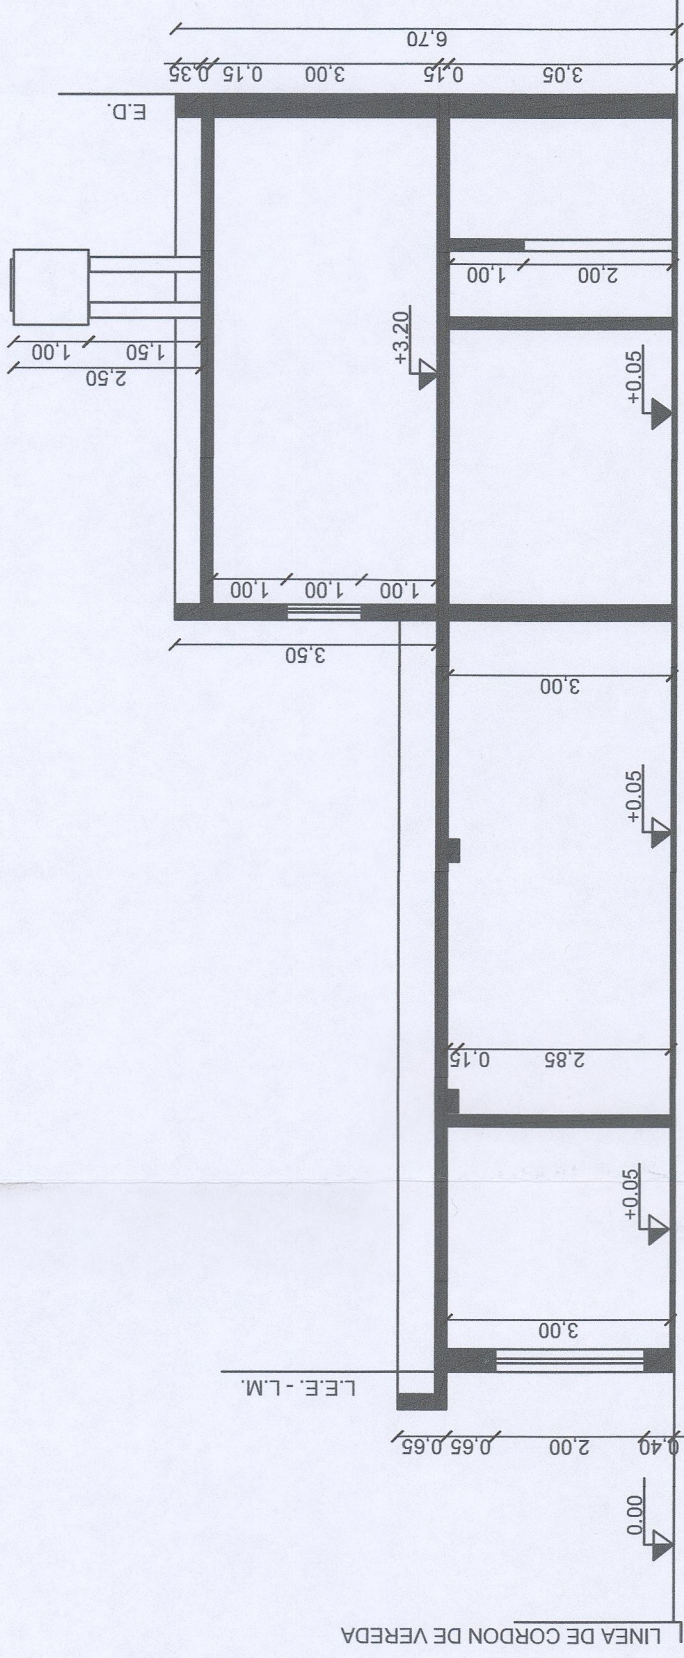

CORTE B - B

REFERENCIAS ELÉCTRICAS

	MEDIDOR Y TOMA A TIERRA
	TABLERO PRINCIPAL
	BOCA DE UNO Y DOS EFECTOS
	BOCA DE PARED
	TOMA CORRIENTE

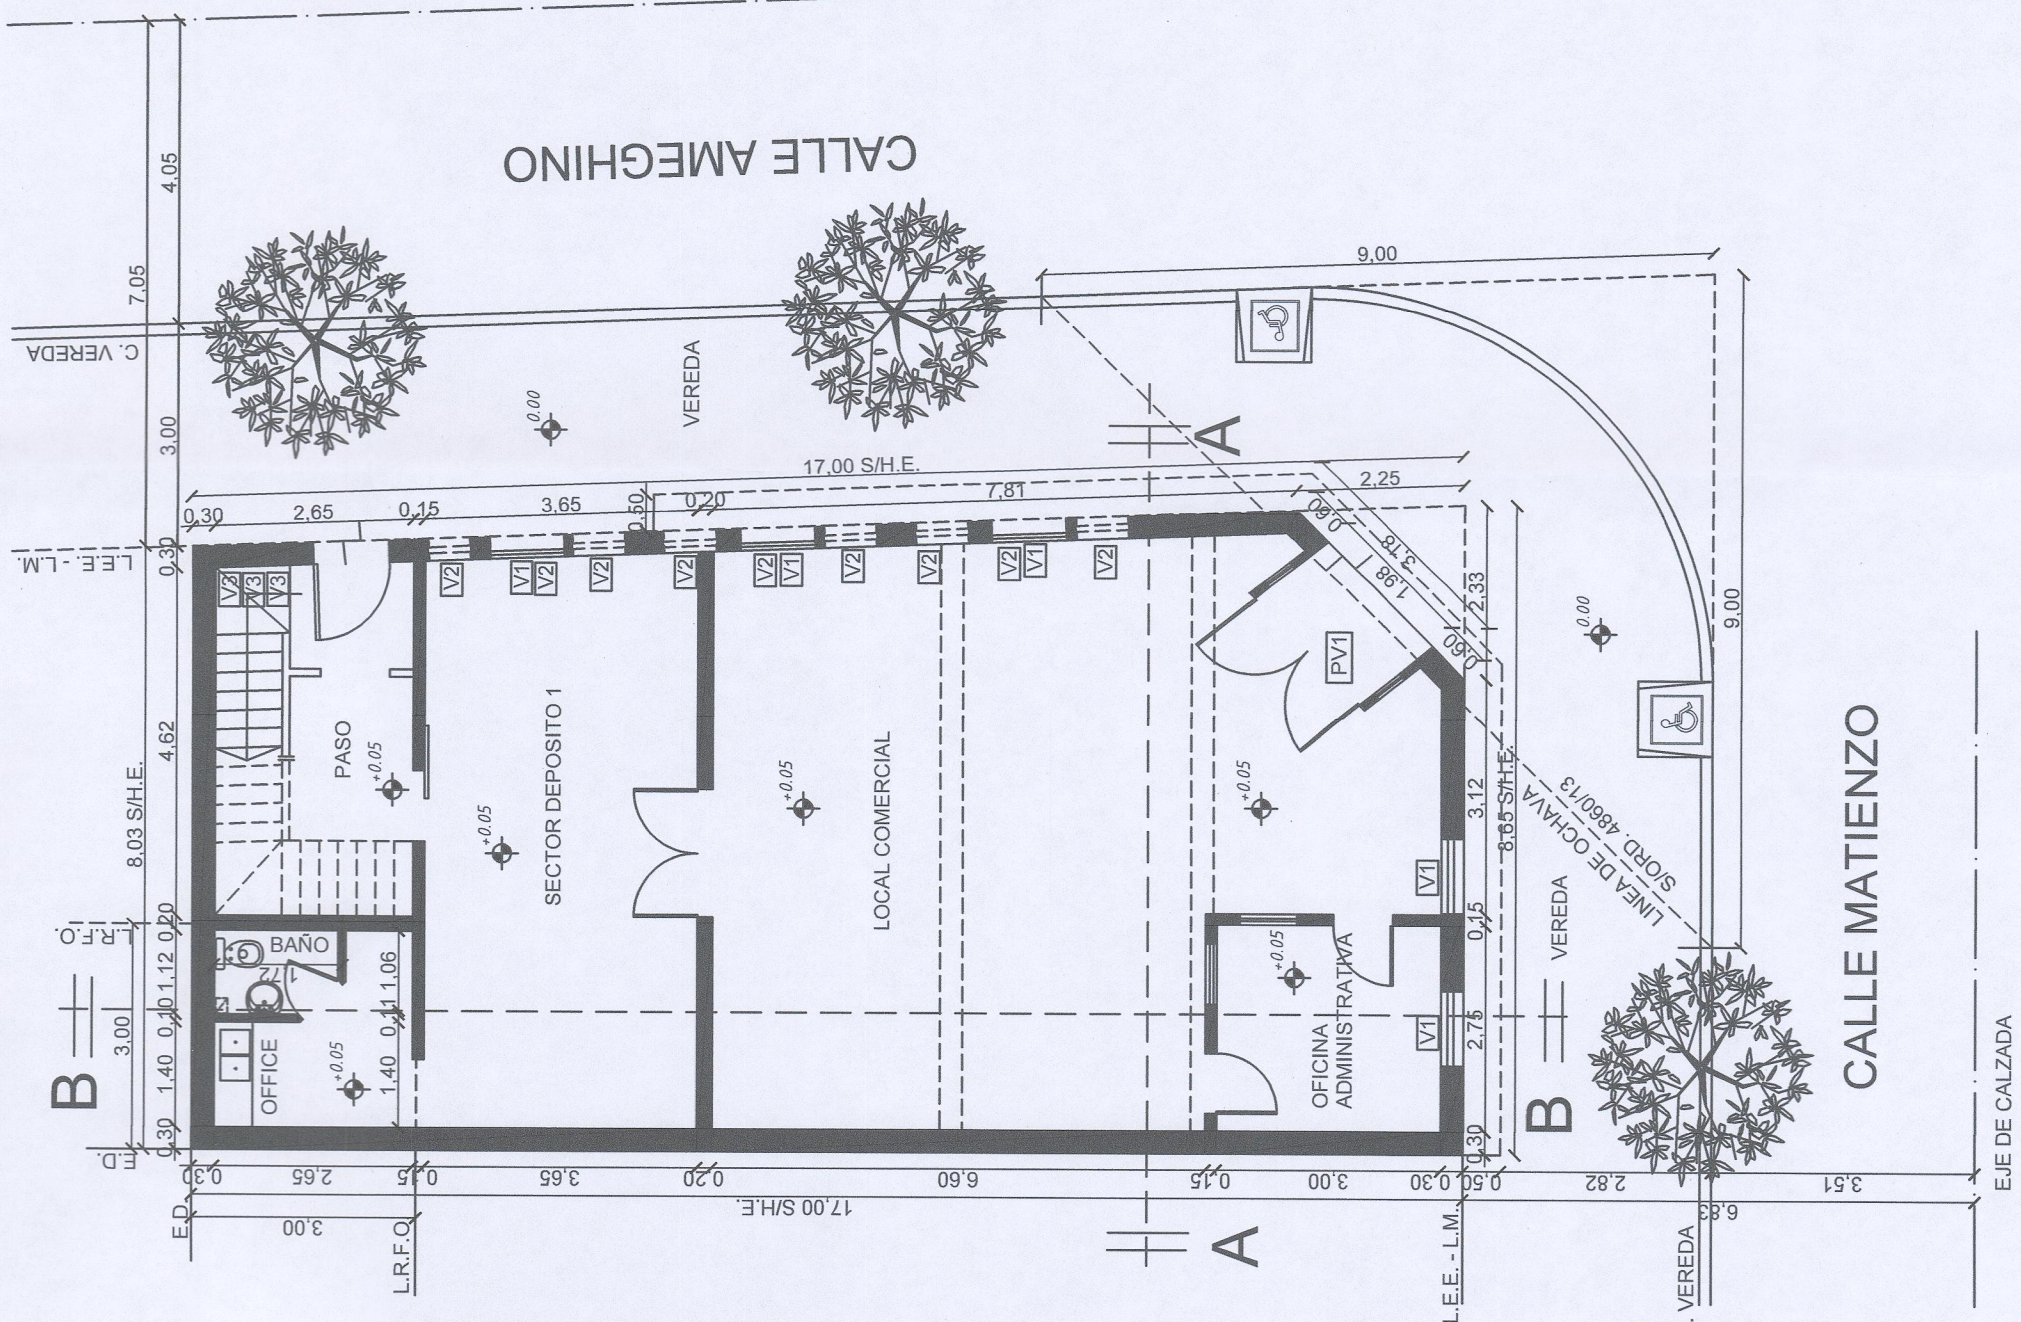


PLANTA


PLANILLA DE ILUMINACION, VENTILACION Y SUPERFICIES									
LOCAL	SUPERF. DESIG.	ABERTURAS			ÁREAS			OBSERV.	TRES UNIDADES
		DESIG.	ANCHO	ALTO	ILUM.	VENT.	VENT.		
LOCAL COMERCIAL	63.25	V1	1.00	2.00	2.00	2.00	2.00	TRES UNIDADES	
		V2	0.80	0.40	0.32	0.32	0.32	CINCO UNIDADES	
		PV1	1.98	2.00	3.96	3.96	3.96		
OFICINA ADM.	8.25	V1	1.00	2.00	2.00	2.00	2.00	TRES UNIDADES	
SECTOR DEPOSITO	28.15	V1	1.00	2.00	2.00	2.00	2.00	Cuatro unidades	
		V2	0.80	0.40	0.32	0.32	0.32	TRES UNIDADES	
PASO	12.35	V3	0.30	0.30	0.09	0.09	0.09	TRES UNIDADES	
BANO	1.85	C.V.	0.40	0.40	0.16	0.16	0.16	COND. VENT.	
PLANTA ALTA									
SECTOR DEPOSITO 2	37.10	V4	1.50	1.50	2.25	2.25	2.25	TRES UNIDADES	

PLANTA ENTREPISO

PLANTA ENTREPISO ELECTRICIDAD

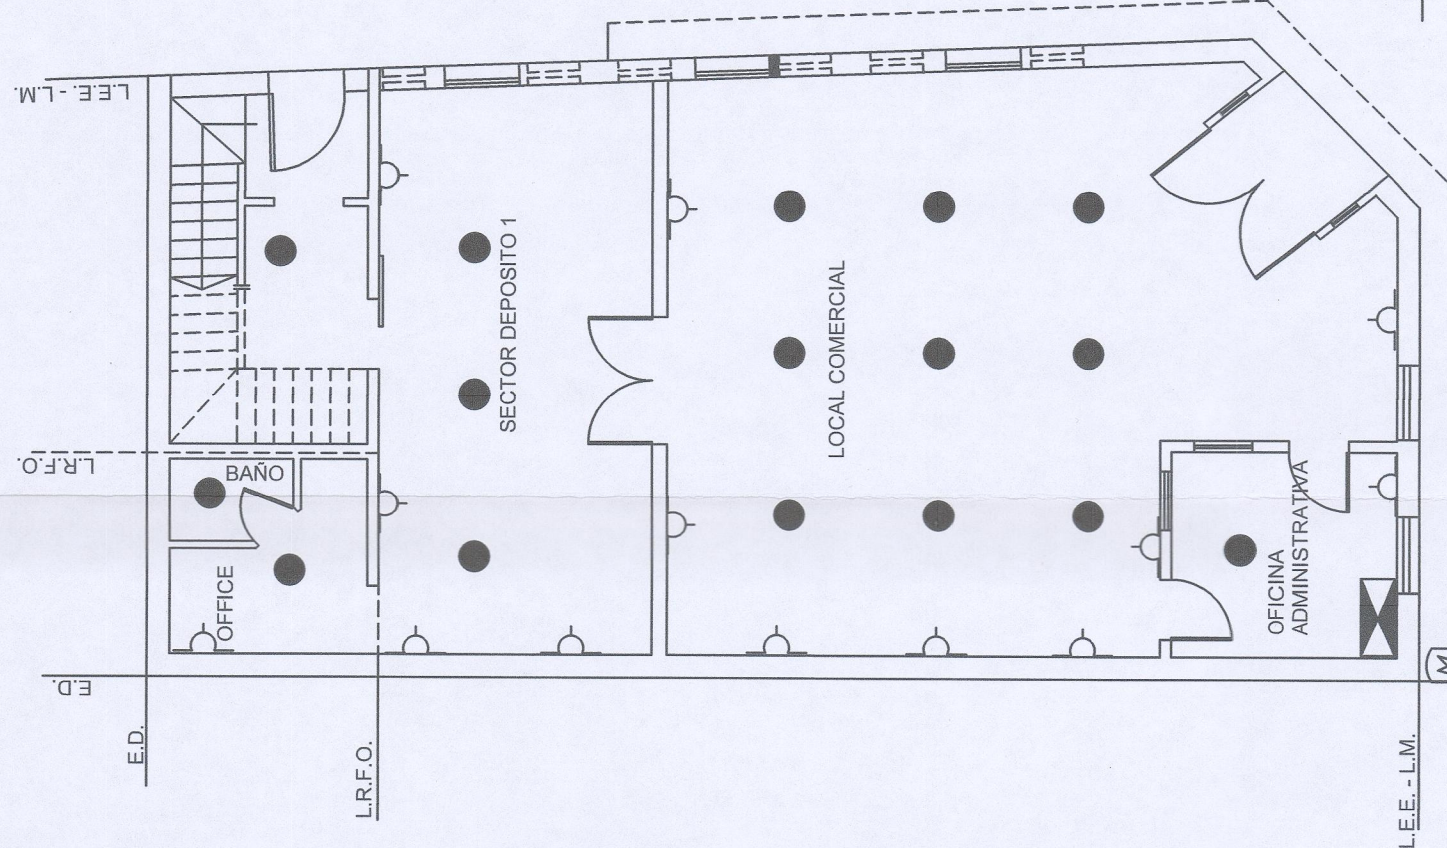

PLANTA DE ELECTRICIDAD

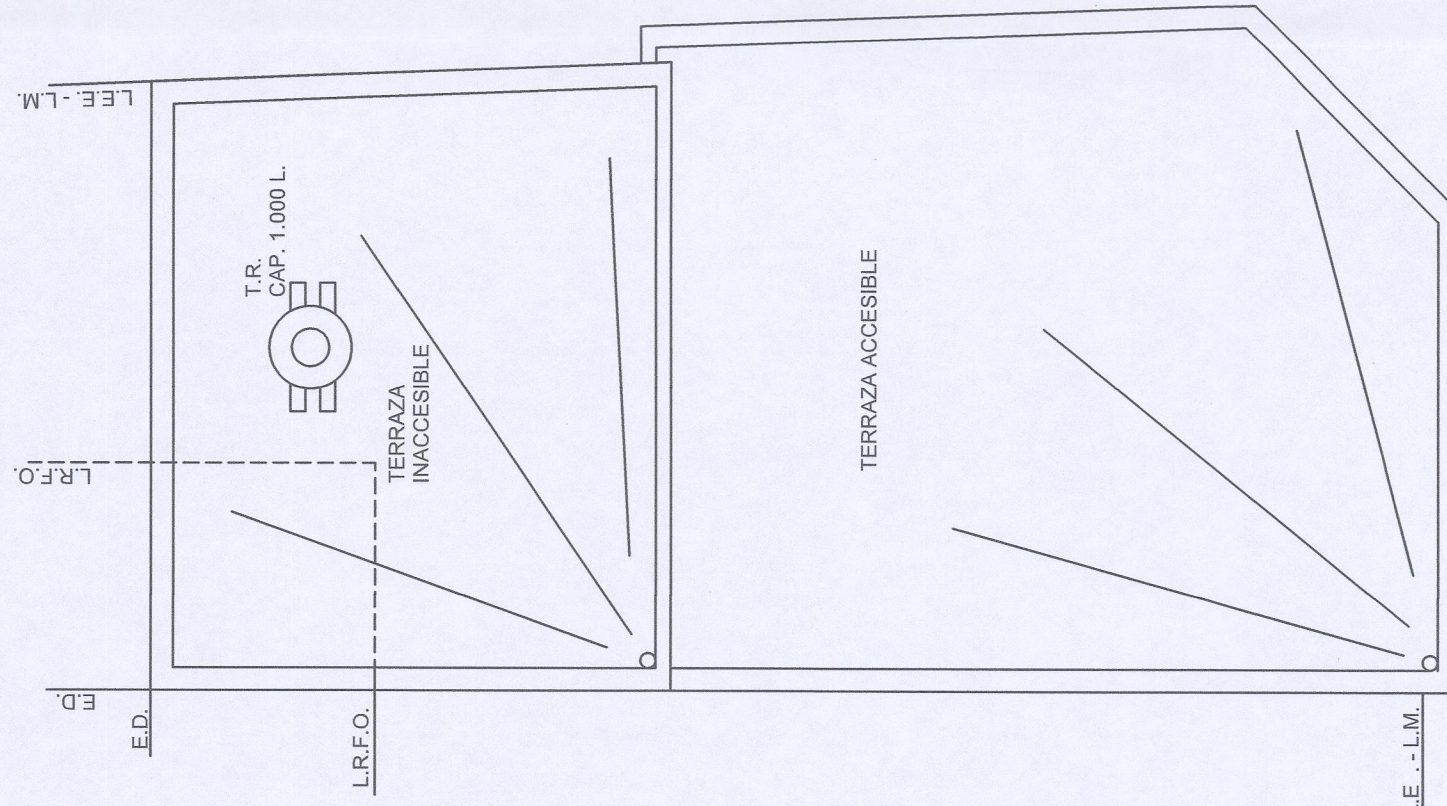


PLANTA DE TECHOS



PLANIMETRIA ESCALA 1:200

DETALLE DE OCHAVA
ESCALA 1:100

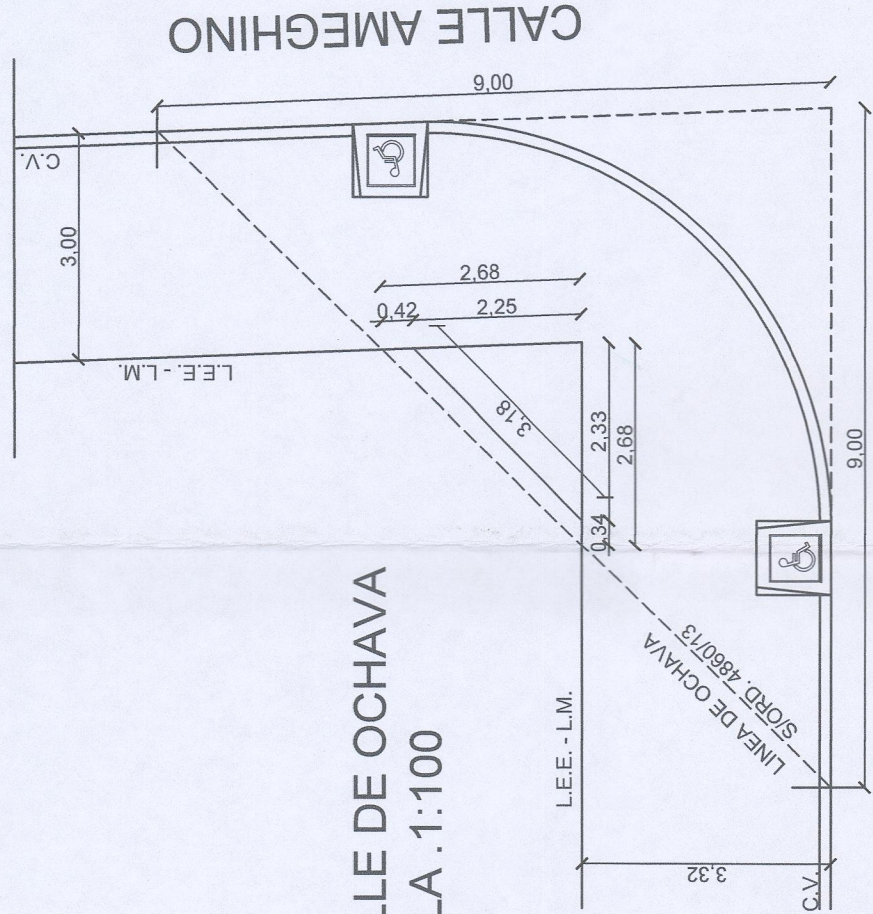

CALLE MATIENZO

CALLE AMEGHINO

FACHADA SOBRE CALLE MATIENZO

FACHADA SOBRE CALLE AMEGHINO