
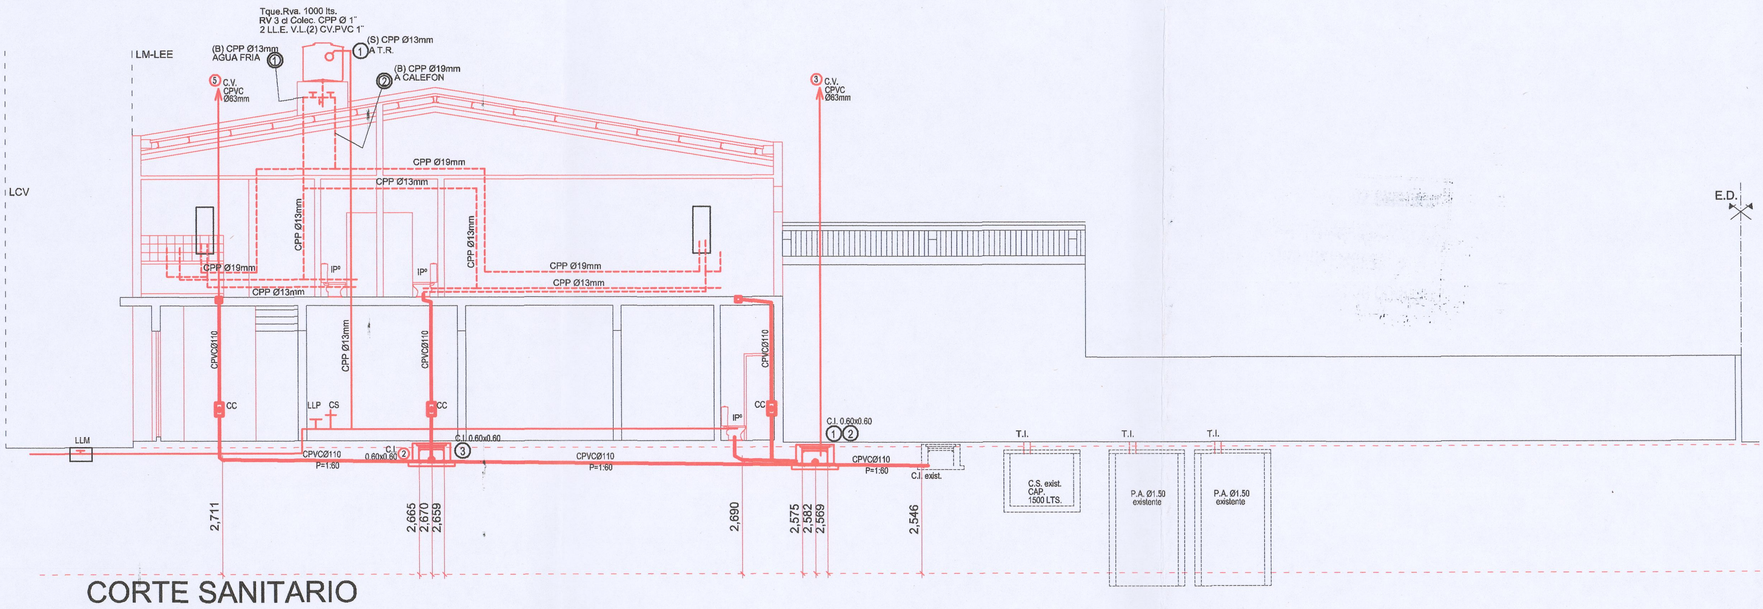



CORTE SANITARIO

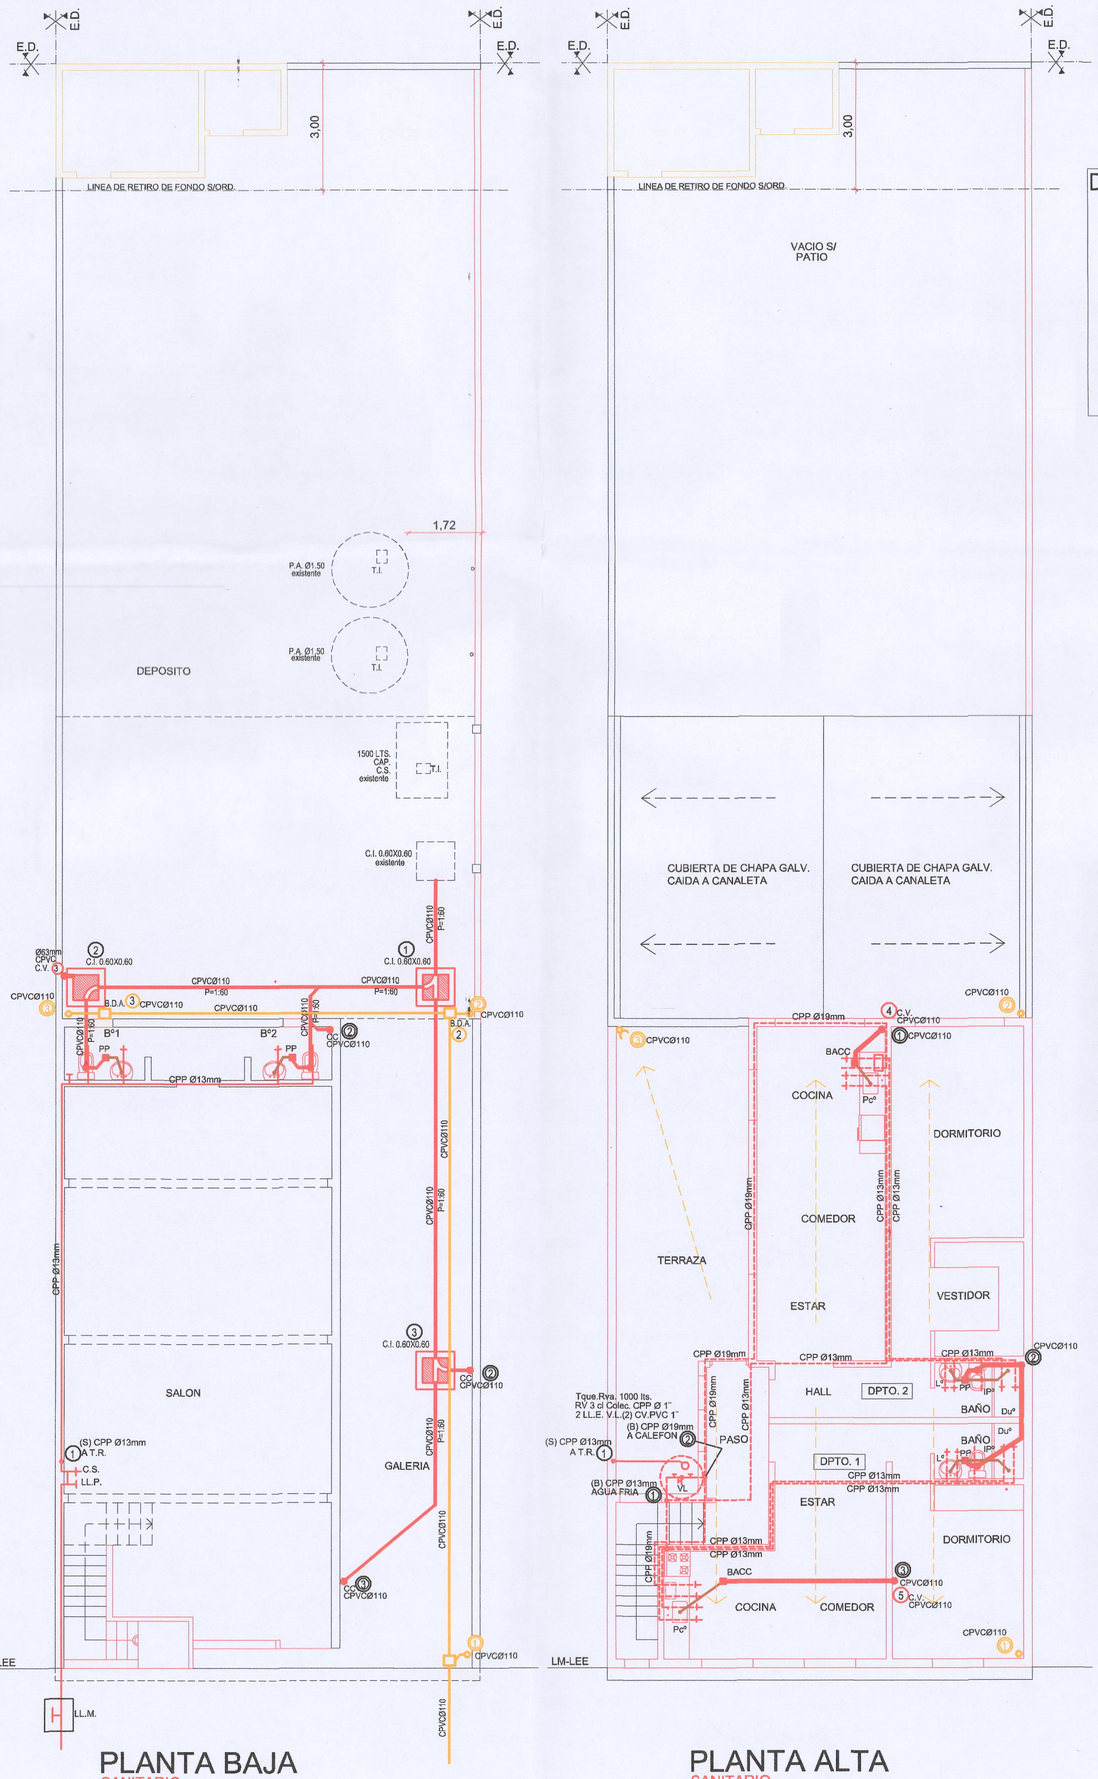

PLANTA BAJA
SANITARIO

PLANTA ALTA
SANITARIO

DETALLE DE TANQUE S/ TECHO

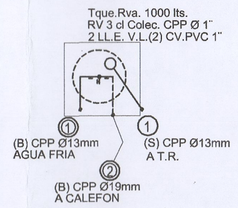

Cuadro de Resumen

DESIGNACION	Cañerías de Desagüe. PRIMARIAS Nº	MAT.	Ø	PLUVIALES Nº	MAT.	Ø	VENTILACIÓN Nº	MAT.	Ø
Tramo	4	P.V.C.	110	1 a 2	CPVC	110	1 - 3	P.V.C.	63
Horiz. Col.	2	P.V.C.	110	1 a 2	CPVC	110			
Columna	1 a 3	CPVC	110	1 a 3	CPVC	110	1 - 3	P.V.C.	63
P.P.	4	P.V.C.	63	—	—	—	ARTEFACTOS Y ACCESORIOS		
B.ACC.	2	P.V.C.	110	—	—	—	DPTO. 1 BAÑO	I.P.-Lº-2CS-1LL.P-Dº-2CS DES.C.P.V.C. Ø40	
I°P°	4	P.V.C.	110	—	—	—	DPTO. 2 BAÑO		
B.D.A.	—	—	—	3	P.V.C.	110	DPTO. 1 COCINA	1 P.C. Ac. Inox. 1 C.S. - SIF. Iny. PVC Ø50	
C.C.	3	P.V.C.	110	—	—	—	DPTO. 2 COCINA	1 P.C. Ac. Inox. 1 C.S. - SIF. Iny. PVC Ø50	
							L.COMER. BAÑO	(2) I.P.-Dº-2CS DES.C.P.V.C. Ø40	

Distr. 6 Zona 1 Manz. 32 Parc. 160

PADRON Nº01-01-018841 ICM: Expte. N°345-A-2025 MFR Nº 7S-0050(18/9/1974)

LEY Nº4682

CPIA ORDEN DE TRABAJO Nº1650205

DESTINO DE LA OBRA: LOCAL COMERCIAL C/DEPOSITO DEPARTAMENTOS (2) DOS.-

PROPIETARIO: NOEMI ROXANA AIDA ALVARES
DNI Nº25.584.235 CUIL Nº27-25584235-3


UBICACION: COLECTORA ABALOS Nº4670
BARRIO: ALMIRANTE BROWN
CIUDAD: SGO. DEL ESTERO
ESCALA: 1:100 - 1:250

DIRECCION DE CATASTRO — EXPEDIENTE 7-51-31-25 — FECHA DE SELLADO 06 NOV. 2025 — BOLETA Nº 1895

SECRETARIA DE ECONOMIA — Municipalidad de la Capital SGO. DEL ESTERO — DIREC. DE SUELO URBANO

SUP. TERRENO:	S/HE - S/P - S/T	380.00 m²
SUP. CUBIERTA A DEMOLER		80.60 m²
SUP. CUBIERTA P. BAJA EXISTENTE		225.00 m²
SUP. CUBIERTA P. ALTA AMPLIACION		122.05 m²
SUP. CUBIERTA TOTAL		347.05 m²

Croquis de Ubicacion:

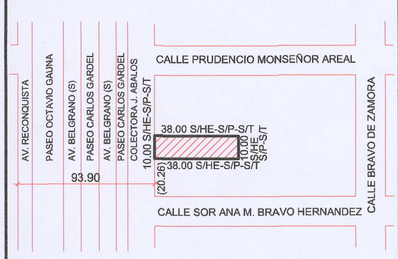

Propietario:
Domicilio:

Relevamiento:
Domicilio:

Proyecto:
Domicilio:

RAMON VELARDE — M. M. DE OBRAS — MAT. PROF. Nº 742

D. Tecnica:
Domicilio:

Electricidad:
Domicilio:

Categoria : "B"

ANCHO DE CALLE:	93.90 mts.	PAVIMENTO:	SI
ANCHO DE CALZADA:	8.14 mts.	SERVICIOS CLOACALES:	NO
ANCHO DE VEREDA:	3.74 mts.		

DIRECCION DE CATASTRO — EXPEDIENTE 7-51-31-25 — FECHA 29/11/25 — BOLETA Nº 2385

PLANO RELEVAMIENTO - AMPLIACION Y MODIFICACION
PLANO SANITARIO

OBSERVACIONES:

17 NOV 2025

Las referencias al Título de dominio son meramente indicativas, y la aprobación administrativa no valora los derechos que de ellos emergen.

PERMISO DE COMIENZO DE OBRA Nº 7-51-24/25 DIRECCION DE SUELO URBANO

MUNICIPALIDAD DE LA CIUDAD DE SANTIAGO DEL ESTERO — SECRETARIA DE ECONOMIA — APROBADO — DIRECCION DE SUELO URBANO — EXPEDIENTE 7-51-31-2025 10-A Dif. 1/25 — FECHA 13 ENE 2026

Ing. Agrim. J. LEANDRO ARJONA — JEFE DE AREA DE VISACIONES TECNICAS — DIRECCION DE CATASTRO MUNICIPAL

Arq. ABRAHAM BERNARDO ROMINA — Dpto. OBRAS PRIVADAS — DIRECCION DE SUELO URBANO

Arq. Cesar Marcelo Alcorta — Director D.S.U. — Municipalidad de la Capital