
## PLANILLA DE ILUMINACION Y VENTILACION


| | Design. | LOCAL Designación | LOCAL Sup. | ABERTURAS Desig. | ABERTURAS Ancho | ABERTURAS Alto | Areas Ilum. | Areas Vent. | Obseraciones |
|---|---|---|---|---|---|---|---|---|---|
| PLANTA BAJA | Tipo A (2 ud) | Hall - escalera | 11.33 | P1 | 1.00 | 2.20 | — | 2.20 | Puerta |
| | | | | LV | 0.20 | 1.20 | 0.24 | — | Lad. Vidrio |
| | | Toilette | 2.16 | CV | 0.20 | 0.20 | — | 0.04 | Cond. Vent. |
| | | Cocina | 9.75 | V1 | 1.50 | 1.10 | 1.65 | 0.83 | Corrediza |
| | | | | P2 | 0.80 | 2.20 | — | 1.76 | Puerta |
| | | Estar-Comedor | 34.80 | PV1 | 2.50 | 2.20 | 11.00 | 5.50 | Corrediza. 2ud. |
| | Tipo B (4 ud) | Hall | 12.35 | P1 | 1.00 | 2.20 | — | 2.20 | Puerta |
| | | | | P2 | 0.80 | 2.20 | — | 1.76 | Puerta |
| | | Toilette | 2.64 | V3 | 0.60 | 1.35 | 0.81 | 0.40 | Abrir + fijo |
| | | Cocina | 7.08 | V4 | 1.20 | 1.10 | 1.32 | 0.66 | Corrediza |
| | | Estar-Comedor | 31.50 | PV1 | 2.50 | 2.20 | 11.00 | 5.50 | Corrediza. 2ud. |
| | Tipo C (1 ud) | Hall | 9.20 | P1 | 1.00 | 2.20 | — | 2.20 | Puerta |
| | | | | LV | 0.20 | 1.20 | 0.24 | — | Lad. Vidrio |
| | | Toilette | 2.46 | V3 | 0.60 | 1.35 | 0.81 | 0.40 | Abrir + fijo |
| | | Cocina | 9.11 | V4 | 1.20 | 1.10 | 1.32 | 0.66 | Corrediza |
| | | Estar-Comedor | 31.50 | PV1 | 2.50 | 2.20 | 16.50 | 8.25 | Corrediza. 3ud. |

## PLANILLA DE ILUMINACION Y VENTILACION


| | Design. | LOCAL Designación | LOCAL Sup. | ABERTURAS Desig. | ABERTURAS Ancho | ABERTURAS Alto | Areas Ilum. | Areas Vent. | Obseraciones |
|---|---|---|---|---|---|---|---|---|---|
| PLANTA ALTA | Tipo A (2 ud) | Dormitorio 1 | 13.14 | V2 | 1.20 | 1.20 | 1.44 | 0.72 | Corrediza |
| | | Antebaño 1 | 3.30 | CV | 0.20 | 0.20 | — | 0.04 | Cond. Vent. |
| | | Baño 1 | 4.40 | V3 | 0.60 | 1.35 | 0.81 | 0.40 | de Abrir + fijo |
| | | Dormitorio 2 | 12.46 | V2 | 1.20 | 1.20 | 1.44 | 0.72 | Corrediza |
| | | Pasillo | 6.30 | V3.1 | 0.60 | 1.35 | 0.81 | 0.81 | de Abrir |
| | | Dormitorio 3 | 13.98 | PV2 | 1.40 | 2.20 | 3.08 | 1.54 | Corrediza |
| | | Antebaño 2 | 2.98 | CV | 0.20 | 0.20 | — | 0.04 | Cond. Vent. |
| | | Baño 2 | 3.93 | V3 | 0.60 | 1.35 | 0.81 | 0.40 | de Abrir + fijo |
| | Tipo B (4 ud) | Escalera | 3.95 | LV | 0.20 | 1.20 | 0.24 | — | Lad. Vidrio |
| | | Dormitorio 1 | 12.92 | PV2 | 1.40 | 2.20 | 3.08 | 1.54 | Corrediza |
| | | Antebaño | 3.23 | V3 | 0.60 | 1.35 | 0.81 | 0.40 | de Abrir + fijo |
| | | Baño | 3.23 | V3 | 0.60 | 1.35 | 0.81 | 0.40 | de Abrir + fijo |
| | | Dormitorio 2 | 16.80 | V5 | 0.80 | 1.85 | 2.96 | 2.16 | Abrir + fijo 2ud |
| | Tipo C (1 ud) | Dormitorio 1 | 17.45 | PV3 | 1.50 | 2.20 | 3.30 | 1.65 | Corrediza |
| | | | | V6 | 1.40 | 1.20 | 1.68 | 0.84 | Corrediza |
| | | Pasillo dorm. | 4.20 | V3 | 0.60 | 1.35 | 1.62 | 0.81 | Abrir + fijo 2ud |
| | | Antebaño 1 | 4.05 | V3 | 0.60 | 1.35 | 0.81 | 0.40 | de Abrir + fijo |
| | | Baño 1 | 3.23 | V3 | 0.60 | 1.35 | 0.81 | 0.40 | de Abrir + fijo |
| | | Dormitorio 2 | 13.20 | V6 | 1.40 | 1.20 | 1.68 | 0.84 | Corrediza |
| | | Antebaño 2 | 2.92 | V3 | 0.60 | 1.35 | 0.81 | 0.40 | de Abrir + fijo |
| | | Baño 2 | 3.23 | V3 | 0.60 | 1.35 | 0.81 | 0.40 | de Abrir + fijo |
| | | Dormitorio 3 | 13.44 | V6 | 1.40 | 1.20 | 1.68 | 0.84 | Corrediza |

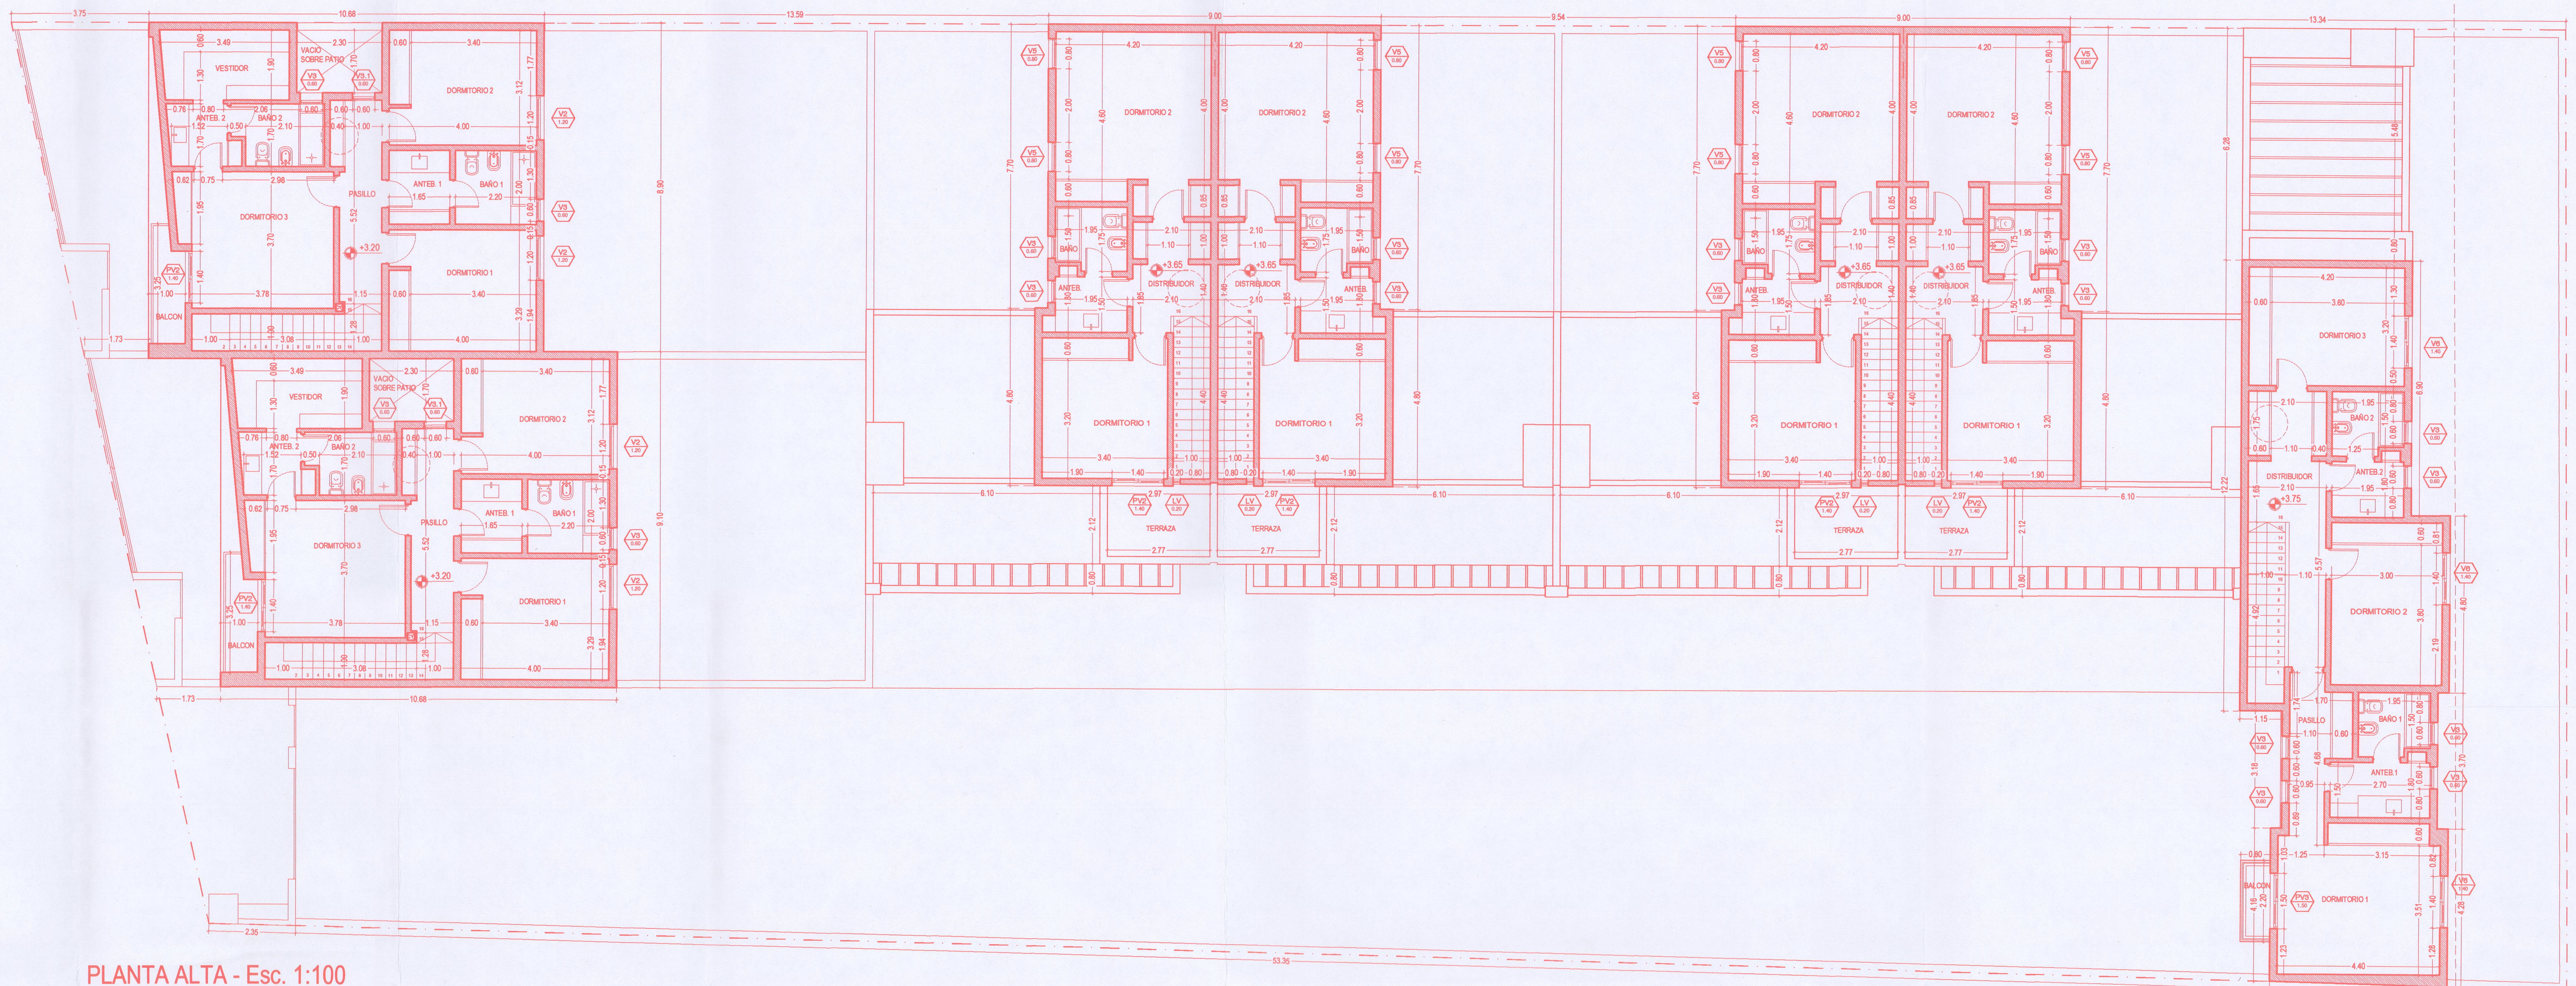


PLANTA ALTA - Esc. 1:100

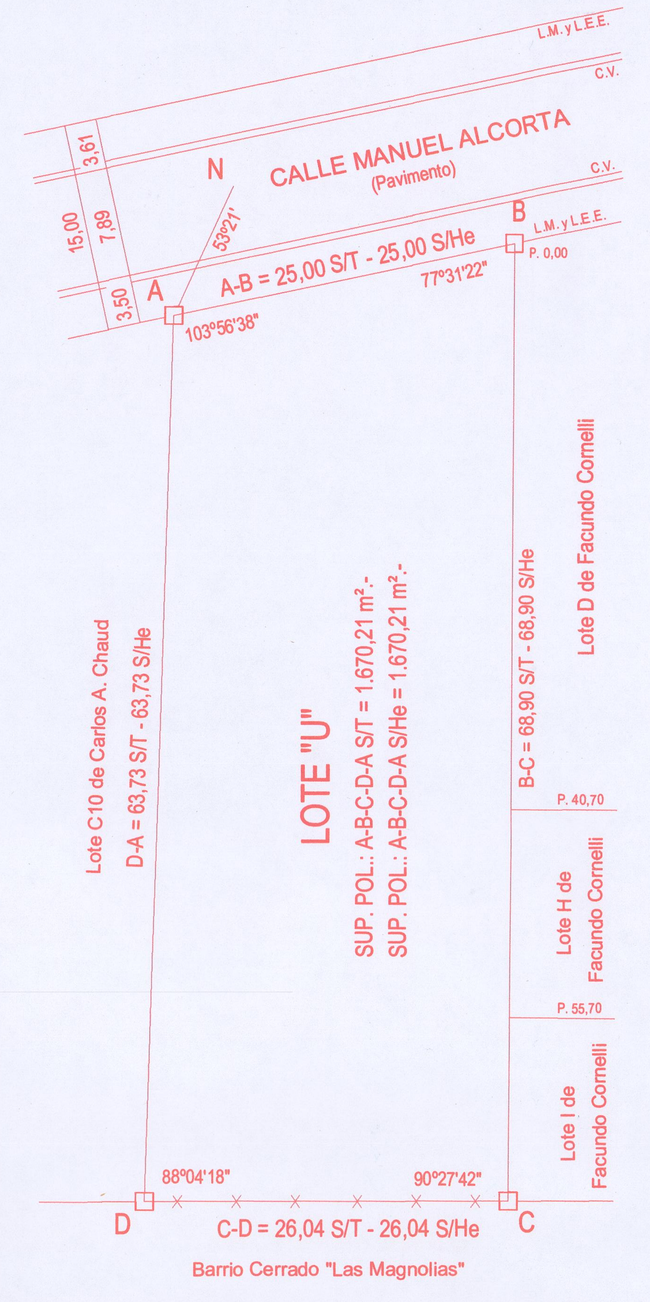


PLANIMETRIA - Esc. 1:400

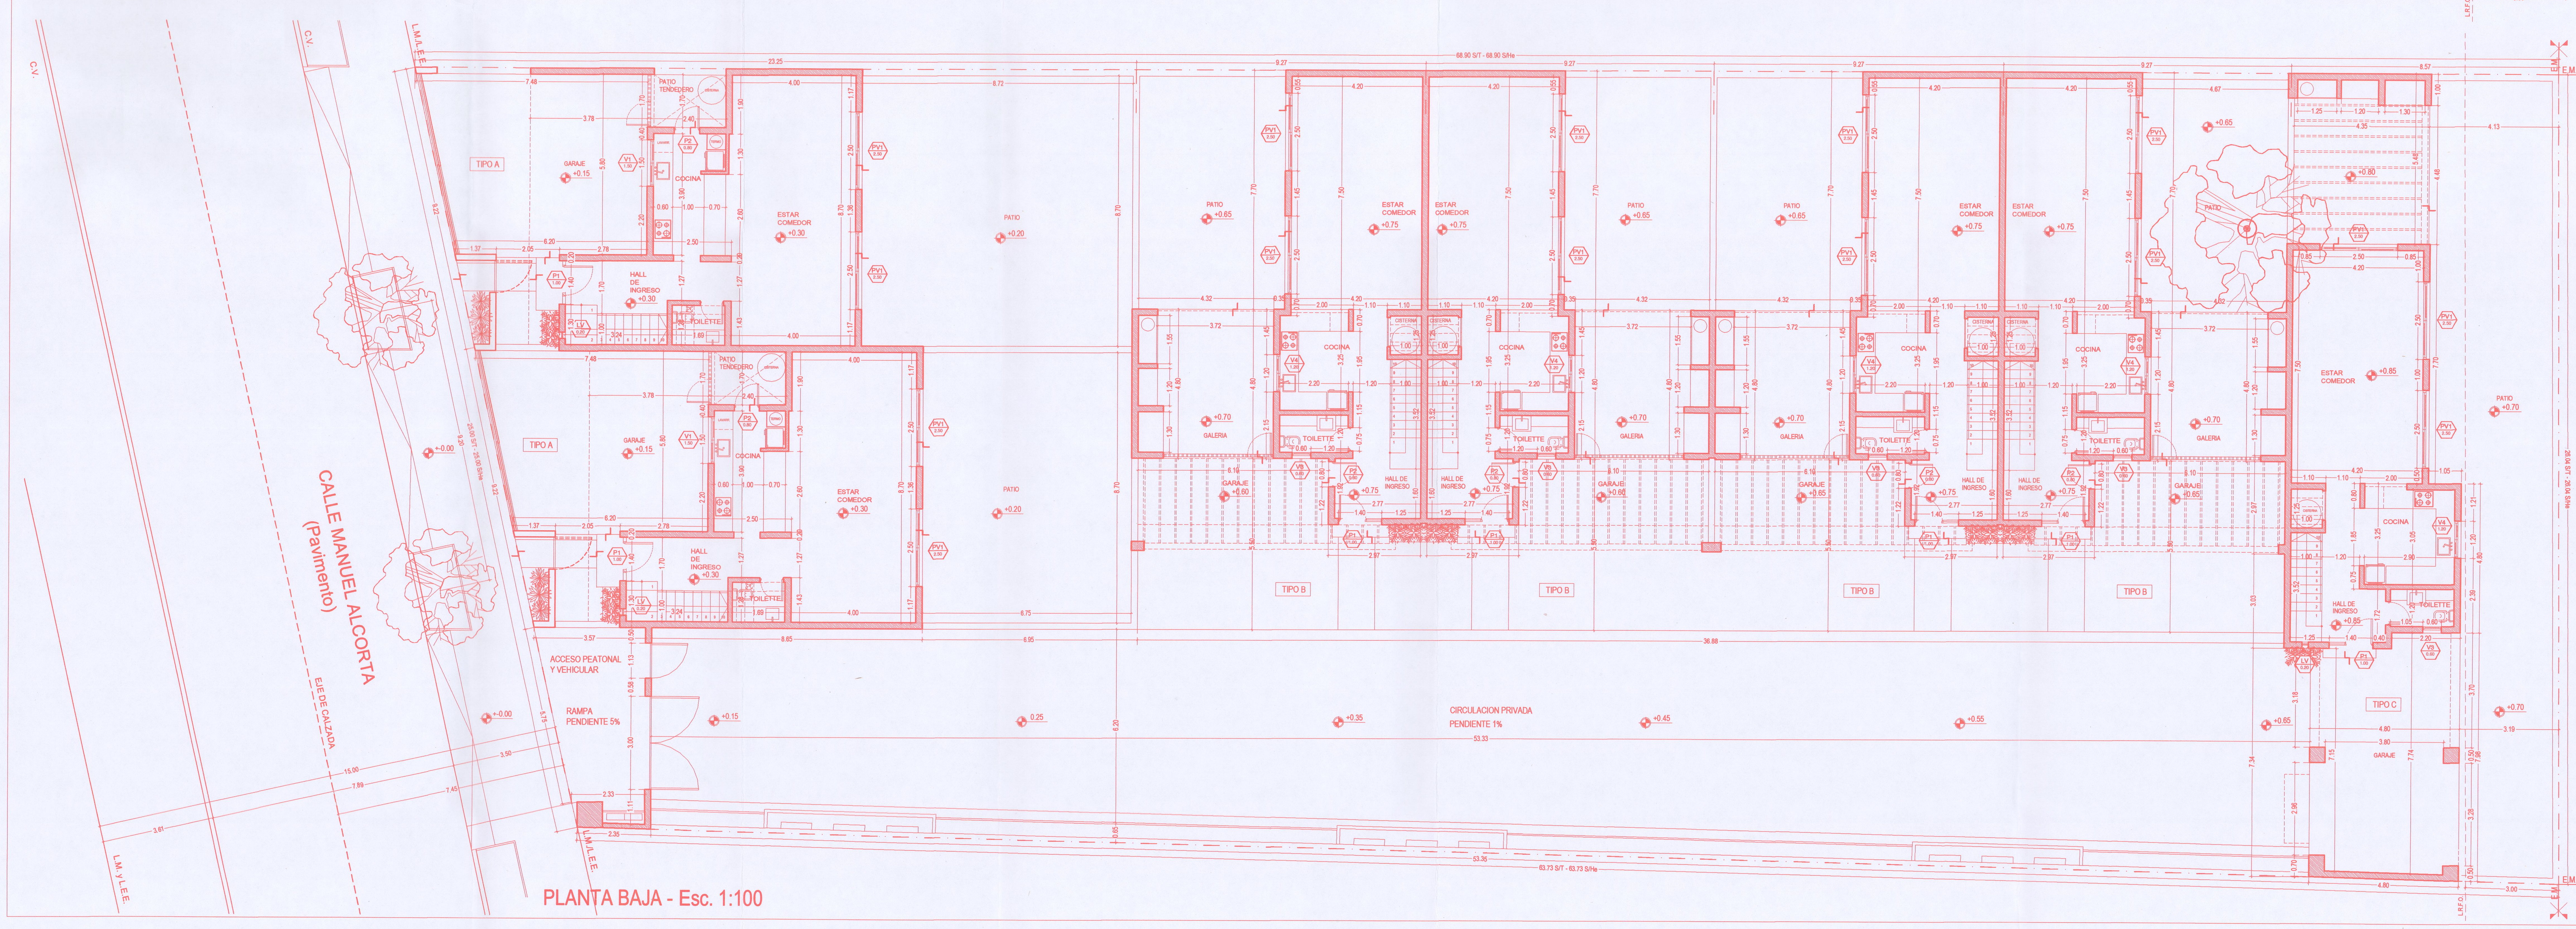


PLANTA BAJA - Esc. 1:100

| | | | |
|---|---|---|---|
| DISTR: 02 | ZONA: 06 | MANZ.: 60 | PARCELA: 545 |
| PADRON INM: 01-01-970236 | | DOMINIO: 7S-39263 | ICM: 42-A-2025 |

LEY 4683

2508067 7

DESTINO DE LA OBRA: 7 DUPLEX

PROPIETARIO: ARCE JOSE AGUSTIN

DNI Nº: 28.048.544 CUIL/T Nº: 20-28048544-7

UBICACIÓN: CALLE MANUEL ALCORTA Nº 525

BARRIO: ALMIRANTE BROWN

CIUDAD: CAPITAL (SANTIAGO DEL ESTERO)

ESCALA: 1:100


DIRECCION DE SUELO URBANO — EXPEDIENTE 684/31/25 — FECHA DE SELLADO 12 NOV. 2025 — BOLETA Nº 203

COLEGIO DE ARQUITECTOS — LEY 5554/87 — SANTIAGO DEL ESTERO — PROYECTO / DIRECCION DE OBRA — 07 11 25

SUSANA ABECASSIS, Arquitecta, Secretaria Técnica, Colegio de Arquitectos SDE

| | |
|---|---|
| SUP. DEL TERRENO S/T y S/He: | 1670,21 m2 S/T y 1670,21m2 S/He |
| SUP. CUBIERTA PLANTA BAJA: | 684,25 m2 |
| SUP. CUBIERTA PLANTA 1º: | 511,09 m2 |
| SUP. CUBIERTA TOTAL: | 1195,34 m2 |

CROQUIS DE UBICACIÓN

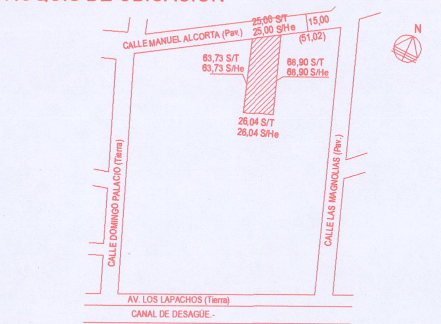


PROPIETARIO: ARCE JOSE AGUSTIN

DOMICILIO: REPUBLICA DE SIRIA Nº 64

PROYECTO:
DOMICILIO:
EDUARDO I. M. ARQUITECTO M.P. 174

DIRECCIÓN TÉCNICA:
DOMICILIO:
EDUARDO I. M. ARQUITECTO M.P. 174

INSTALACIÓN ELECTRICA:
DOMICILIO:
EDUARDO I. M. ARQUITECTO M.P. 174

CATEGORÍA CONSEJO PROFESIONAL "B":

SECRETARIA DE ECONOMIA — Municipalidad de la Capital SGO. DEL ESTERO — DIREC. DE SUELO URBANO

| | | | |
|---|---|---|---|
| ANCHO DE CALLE: | 15,00m | PAVIMENTO: | SI |
| ANCHO DE VEREDA: | 3,50m | SERVICIOS CLOACALES: | NO |
| ANCHO DE CALZADA: | 7,89m | | |

DESIGNACIÓN:

# PROYECTO _ PLANTAS / OBRA NUEVA 01

OBSERVACIONES:

26 NOV 2025

Las referencias al Titulo de dominio son meramente indicativas, y la aprobación administrativa no valora los derechos que de ellos emergen.

PERMISO DE COMIENZO DE OBRA Nº 204/2025 — DIRECCION DE SUELO URBANO

MUNICIPALIDAD DE LA CIUDAD DE SANTIAGO DEL ESTERO — SECRETARIA DE ECONOMIA

APROBADO — DIRECCIÓN DE SUELO URBANO

EXPEDIENTE: 689-31-25 11-A-2025

FECHA: 06 ENE 2026

Ing. Agrim. J. LEANDRO ARJONA, JEFE DE AREA DE VISACIONES TECNICAS

Arq. FEDERICO LOPEZ, JEFE DE SERVICIO, DPTO. OBRAS PRIVADAS, DIRECCION DE SUELO URBANO

Arq. Cesar Marcelo Alcorta, Director D.S.U., Municipalidad de la Capital