




DETALLE CIMIENTOS

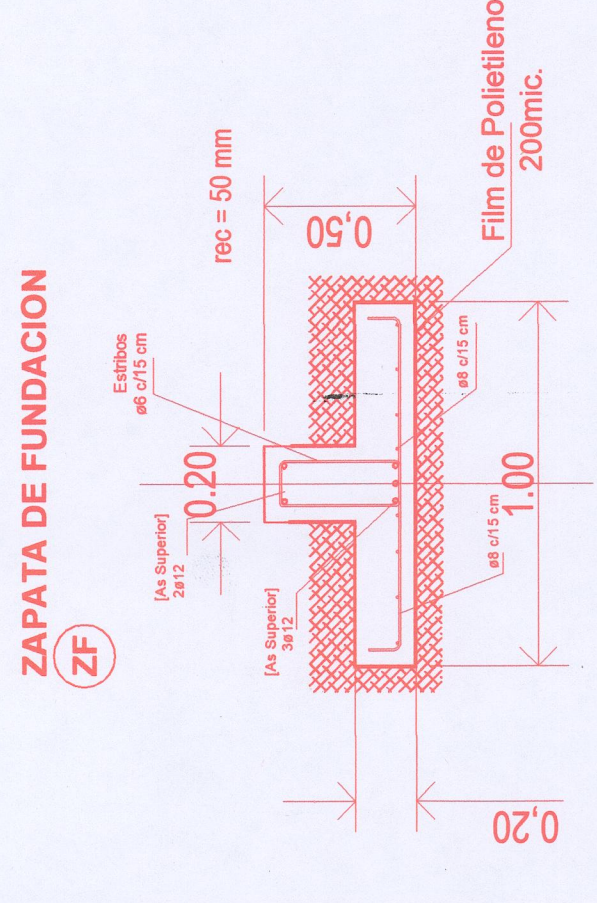





ZAPATA DE FUNDACION EXCENTRICA

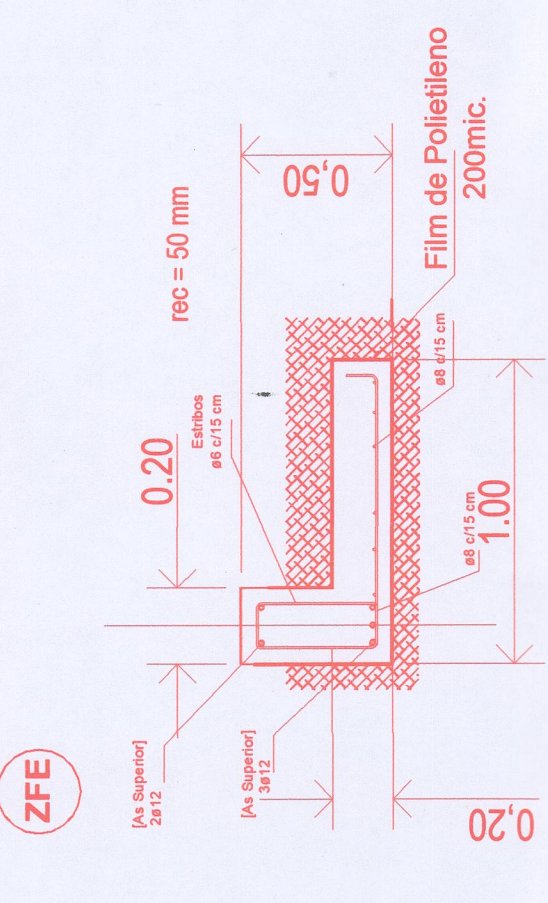


DETALLE COLUMNAS

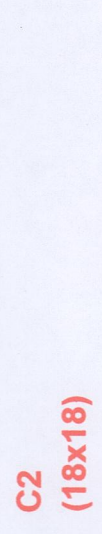

DETALLE VIGAS

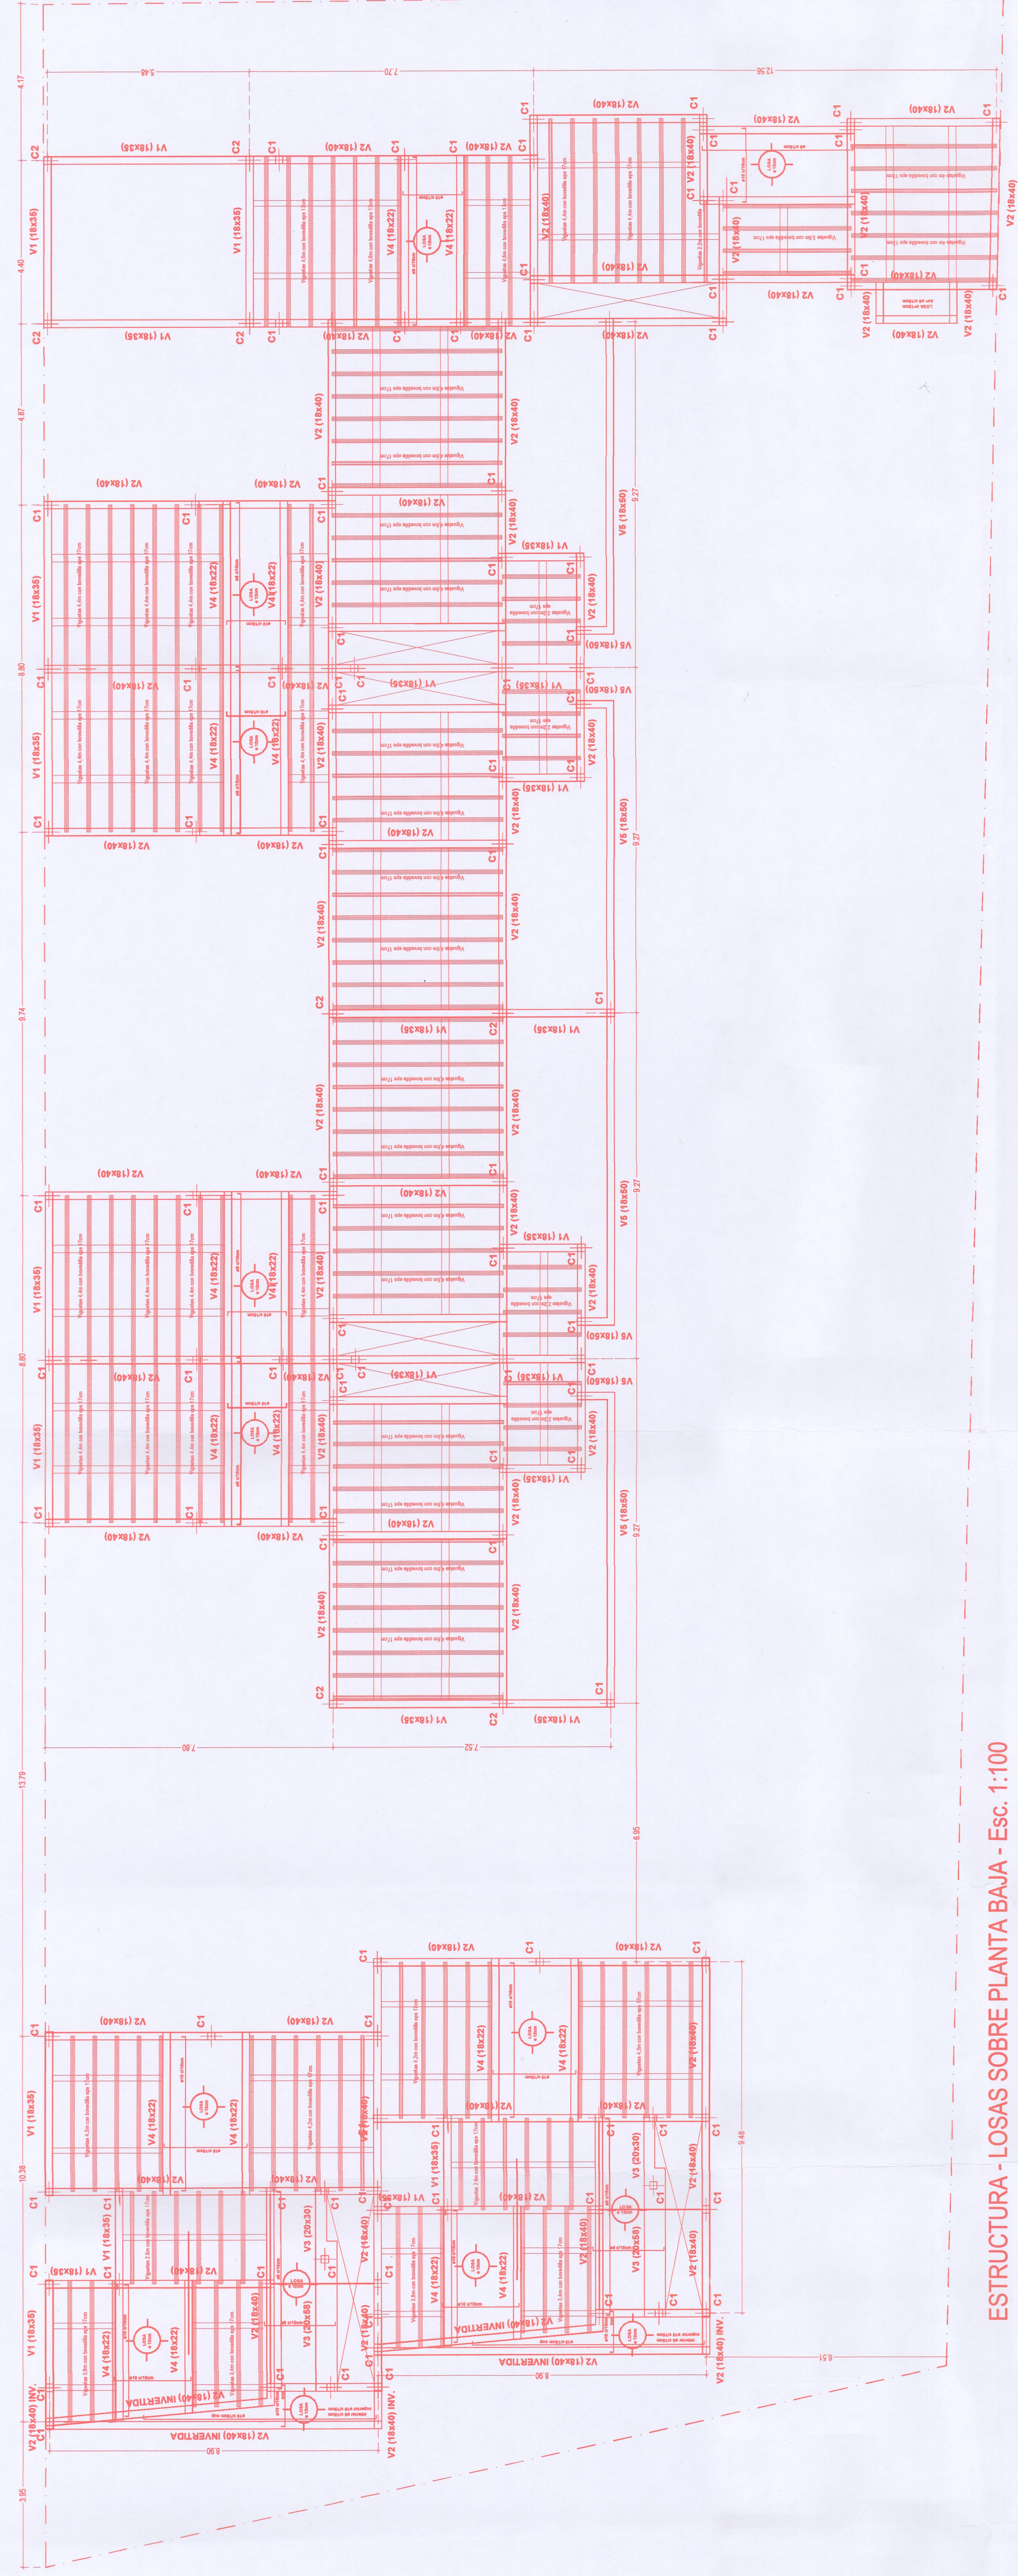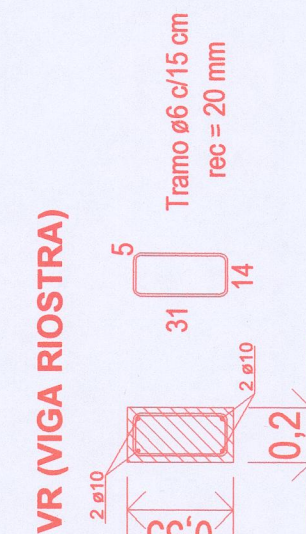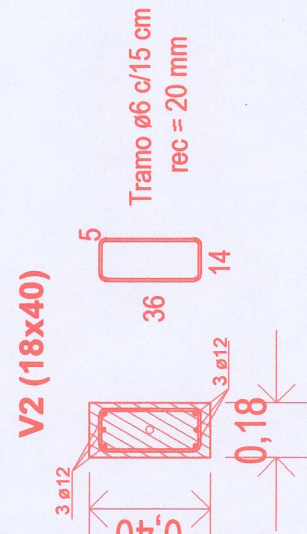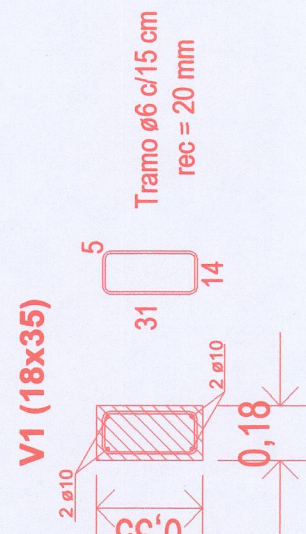

ESTRUCTURA - LOSAS SOBRE PLANTA BAJA - Esc. 1:100

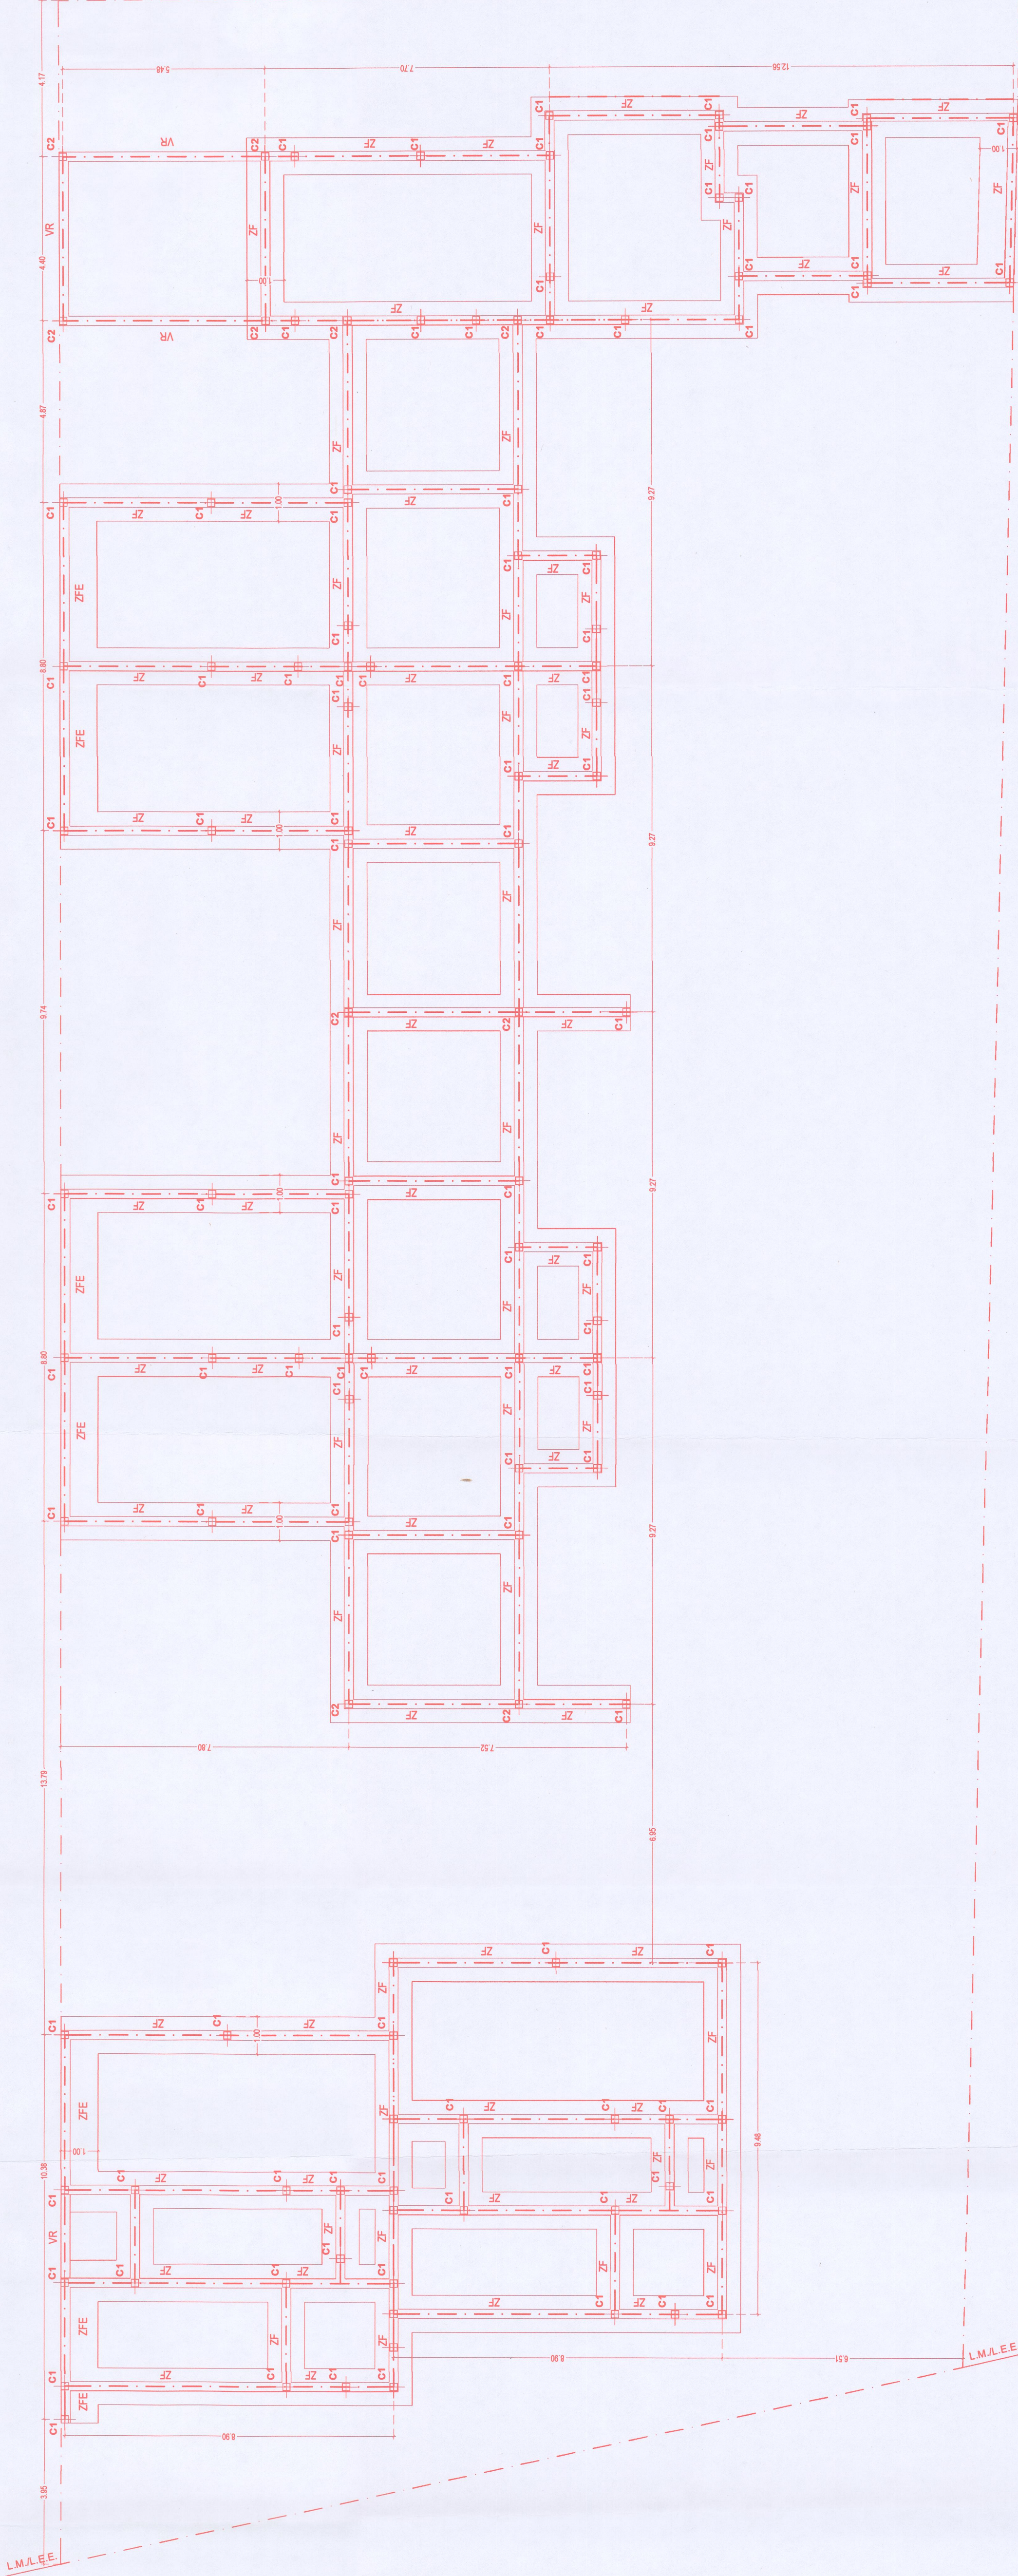


ESTRUCTURA - PLANTA DE FUNDACION - Esc. 1:100


DETALLE VIGAS

VIGA DE SECCION VARIABLE

V3 (20x30)

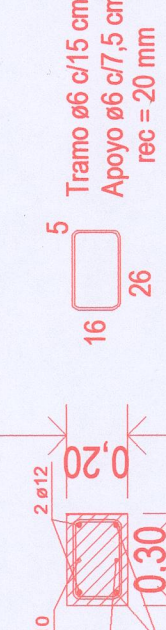


V2 (20x58)

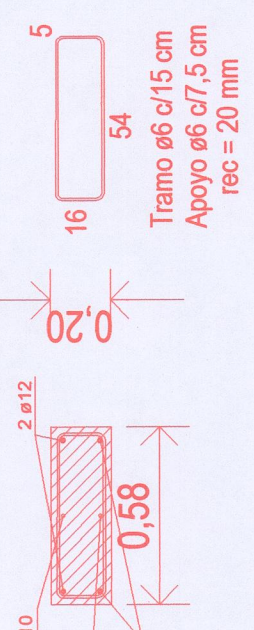


DETALLE TRANSICION LOSA DE VIGUETAS CON LOSA LLENA PARA BANDEJAS SANITARIAS

V4 (18x22)

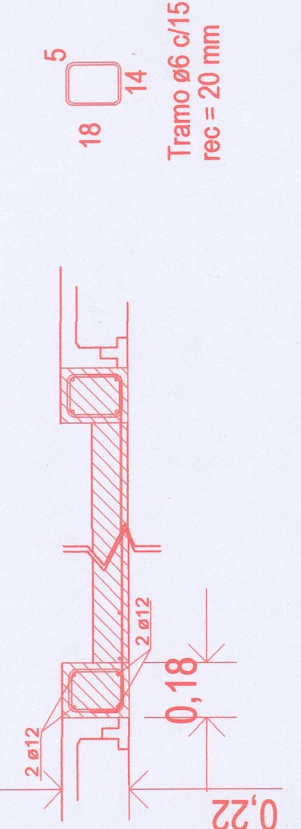


DETALLE VIGA INVERTIDA EN LOSA DE VIGUETAS

V2 (18x40)

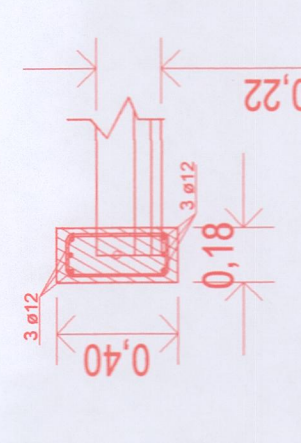

V5 (18x40)

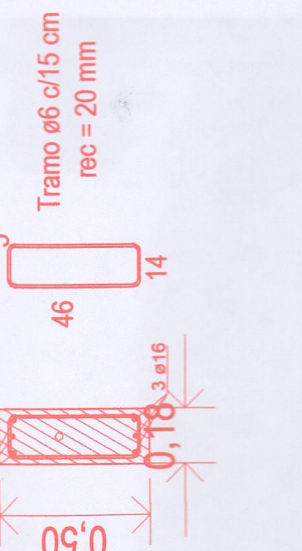

DISTR: 02	ZONA: 06	MANZ: 60	PARCELA: 545	25080677
PADRON INM: 01-01-970236	DOMINIO: 75-39293	ICM: 42-A-2025		
DESTINO DE LA OBRA: 7 DUPLEX				
PROPIETARIO: ARCE JOSE AGUSTIN				
DNI N°: 28.048.544				
UBICACION: CALLE MANUEL ALCORTA N° 525				
BARRIO: ALMIRANTE BROWN				
CIUDAD: CAPITAL (SANTIAGO DEL ESTERO)				
ESCALA: 1:100				
PROPIETARIO: ARCE JOSE AGUSTIN				
DOMICILIO: REPUBLICA DE SAN CARLOS				
PROYECTO: DOMICILIO				
DIRECCION TECNICA: EDUARDO LOPEZ				
INSTALACION ELECTRICA: EDUARDO LOPEZ				
CATEGORIA: CONDOMINIO PROFESIONAL 1°				
PAVIMENTO: 15.00m				
SERVICIOS CLOACALES: 3.50m				
DESIGNACION: 7.60m				
OBSERVACIONES: 2 6 NOV 2025				
ESTRUCTURA - PLANTAS - DETALLES				
MUNICIPALIDAD DE LA CIUDAD DE SANTIAGO DEL ESTERO				
SECRETARIA DE ECONOMIA				
APROBADO				
DIRECCION DE SUELO URBANO				
PERMISO DE COMIENZO DE OBRA N° 204-2025				
26 NOV 2025				
Las referencias al título de dominio son meramente indicativas y la aprobación administrativa no valora los derechos que de ellos emanan.				
EDUARDO LOPEZ				
DIRECTOR D.S.U.				
Ap. Edgar Marcelo Alarcón				
DIRECTOR DE SUELO URBANO				