PLANILLA DE CARGAS - TIPO A

	Circuito	Luz	Tomas		Luz	Tomas	Total		Termomagnética	Diferencial
		100 w	200 w	1000 w			(W)	(A)		
TG1 PB	1	8	—	—	800	—	800	3,63	2 x 10 A	2 x 40 A
	2	7	—	—	700	—	700	3,18	2 x 10 A	
	3	—	15	—	—	3000	3000	13,64	2 x 16 A	
	4	—	—	1	—	1000	1000	4,54	2 x 20 A	
TS1 PA	5	11	—	—	1100	—	1100	5,00	2 x 10 A	2 x 40 A
	6	—	12	—	—	2400	2400	10,91	2 x 16 A	
	7	—	—	3	—	3000	3000	13,64	2 x 20 A	
						Potencia Total	12000	54,54		
						Fac. de Simultaneidad 60%	7200	32,72		

PLANILLA DE CARGAS - TIPO B

	Circuito	Luz	Tomas		Luz	Tomas	Total		Termomagnética	Diferencial
		100 w	200 w	1000 w			(W)	(A)		
TG1 PB	1	9	—	—	900	—	900	4,09	2 x 10 A	2 x 40 A
	2	7	—	—	700	—	700	3,18	2 x 10 A	
	3	—	15	—	—	3000	3000	13,64	2 x 16 A	
	4	—	—	1	—	1000	1000	4,54	2 x 20 A	
TS1 PA	5	8	—	—	800	—	800	3,63	2 x 10 A	2 x 40 A
	6	—	9	—	—	1800	1800	8,18	2 x 16 A	
	7	—	—	2	—	2000	2000	9,09	2 x 20 A	
						Potencia Total	10000	46,36		
						Fac. de Simultaneidad 60%	6120	27,82		

PLANILLA DE CARGAS - TIPO C

	Circuito	Luz	Tomas		Luz	Tomas	Total		Termomagnética	Diferencial
		100 w	200 w	1000 w			(W)	(A)		
TG1 PB	1	8	—	—	800	—	800	3,63	2 x 10 A	2 x 40 A
	2	9	—	—	900	—	900	4,09	2 x 10 A	
	3	—	14	—	—	2800	2800	12,73	2 x 16 A	
	4	—	—	1	—	1000	1000	4,54	2 x 20 A	
TS1 PA	5	11	—	—	1100	—	1100	5,00	2 x 10 A	2 x 40 A
	6	—	15	—	—	3000	3000	13,64	2 x 16 A	
	7	—	—	3	—	3000	3000	13,64	2 x 20 A	
						Potencia Total	12600	57,27		
						Fac. de Simultaneidad 60%	7560	34,36		

DIAGRAMA UNIFILAR TIPO A - B - C

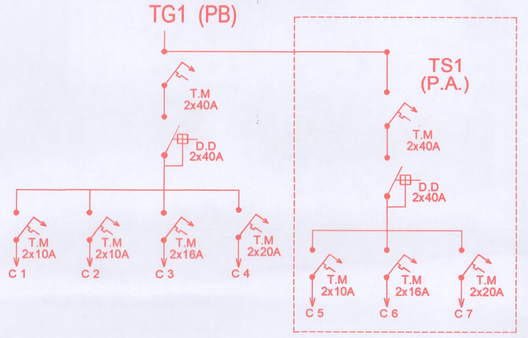

DIAGRAMA UNIFILAR SERVICIOS GENERALES TG

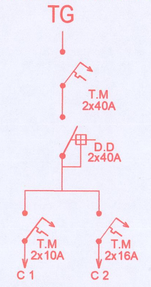

PLANILLA DE CARGAS SERVICIOS GENERALES. MONOFASICO

	Circuito	Luz	Tomas		Luz	Tomas	Total		Termomagnética	Diferencial
		100 w	200 w	1000 w			(W)	(A)		
TG	1	13	—	—	1300	—	1300	5,91	2 x 10 A	2 x 40 A
	2	—	3	—	—	600	600	2,72	2 x 16 A	
						Potencia Total	1900	8,63		
						Fac. de Simultaneidad 60%	1140	5,18		

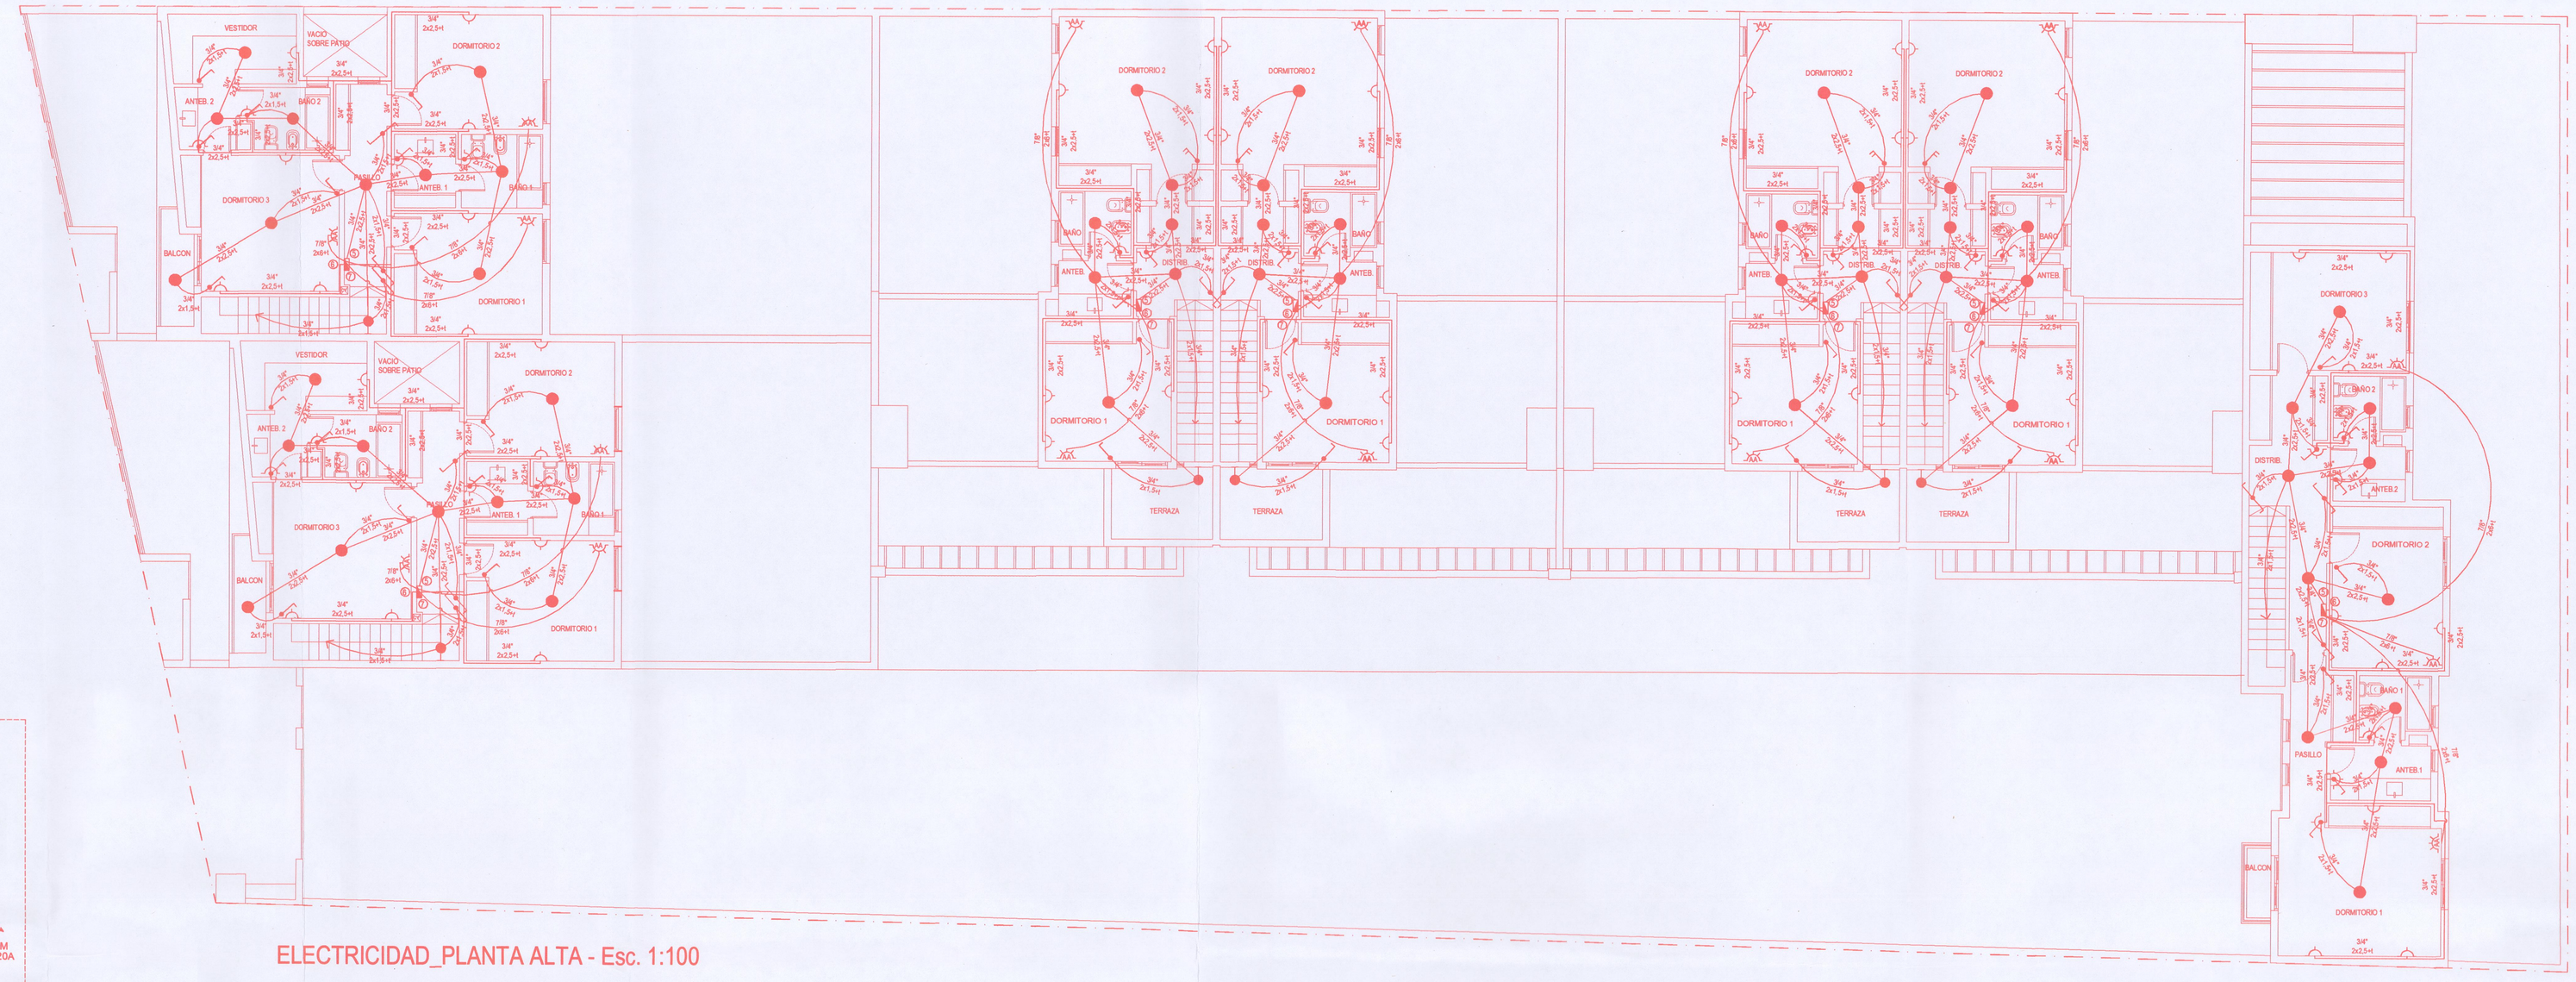

ELECTRICIDAD_PLANTA ALTA - Esc. 1:100

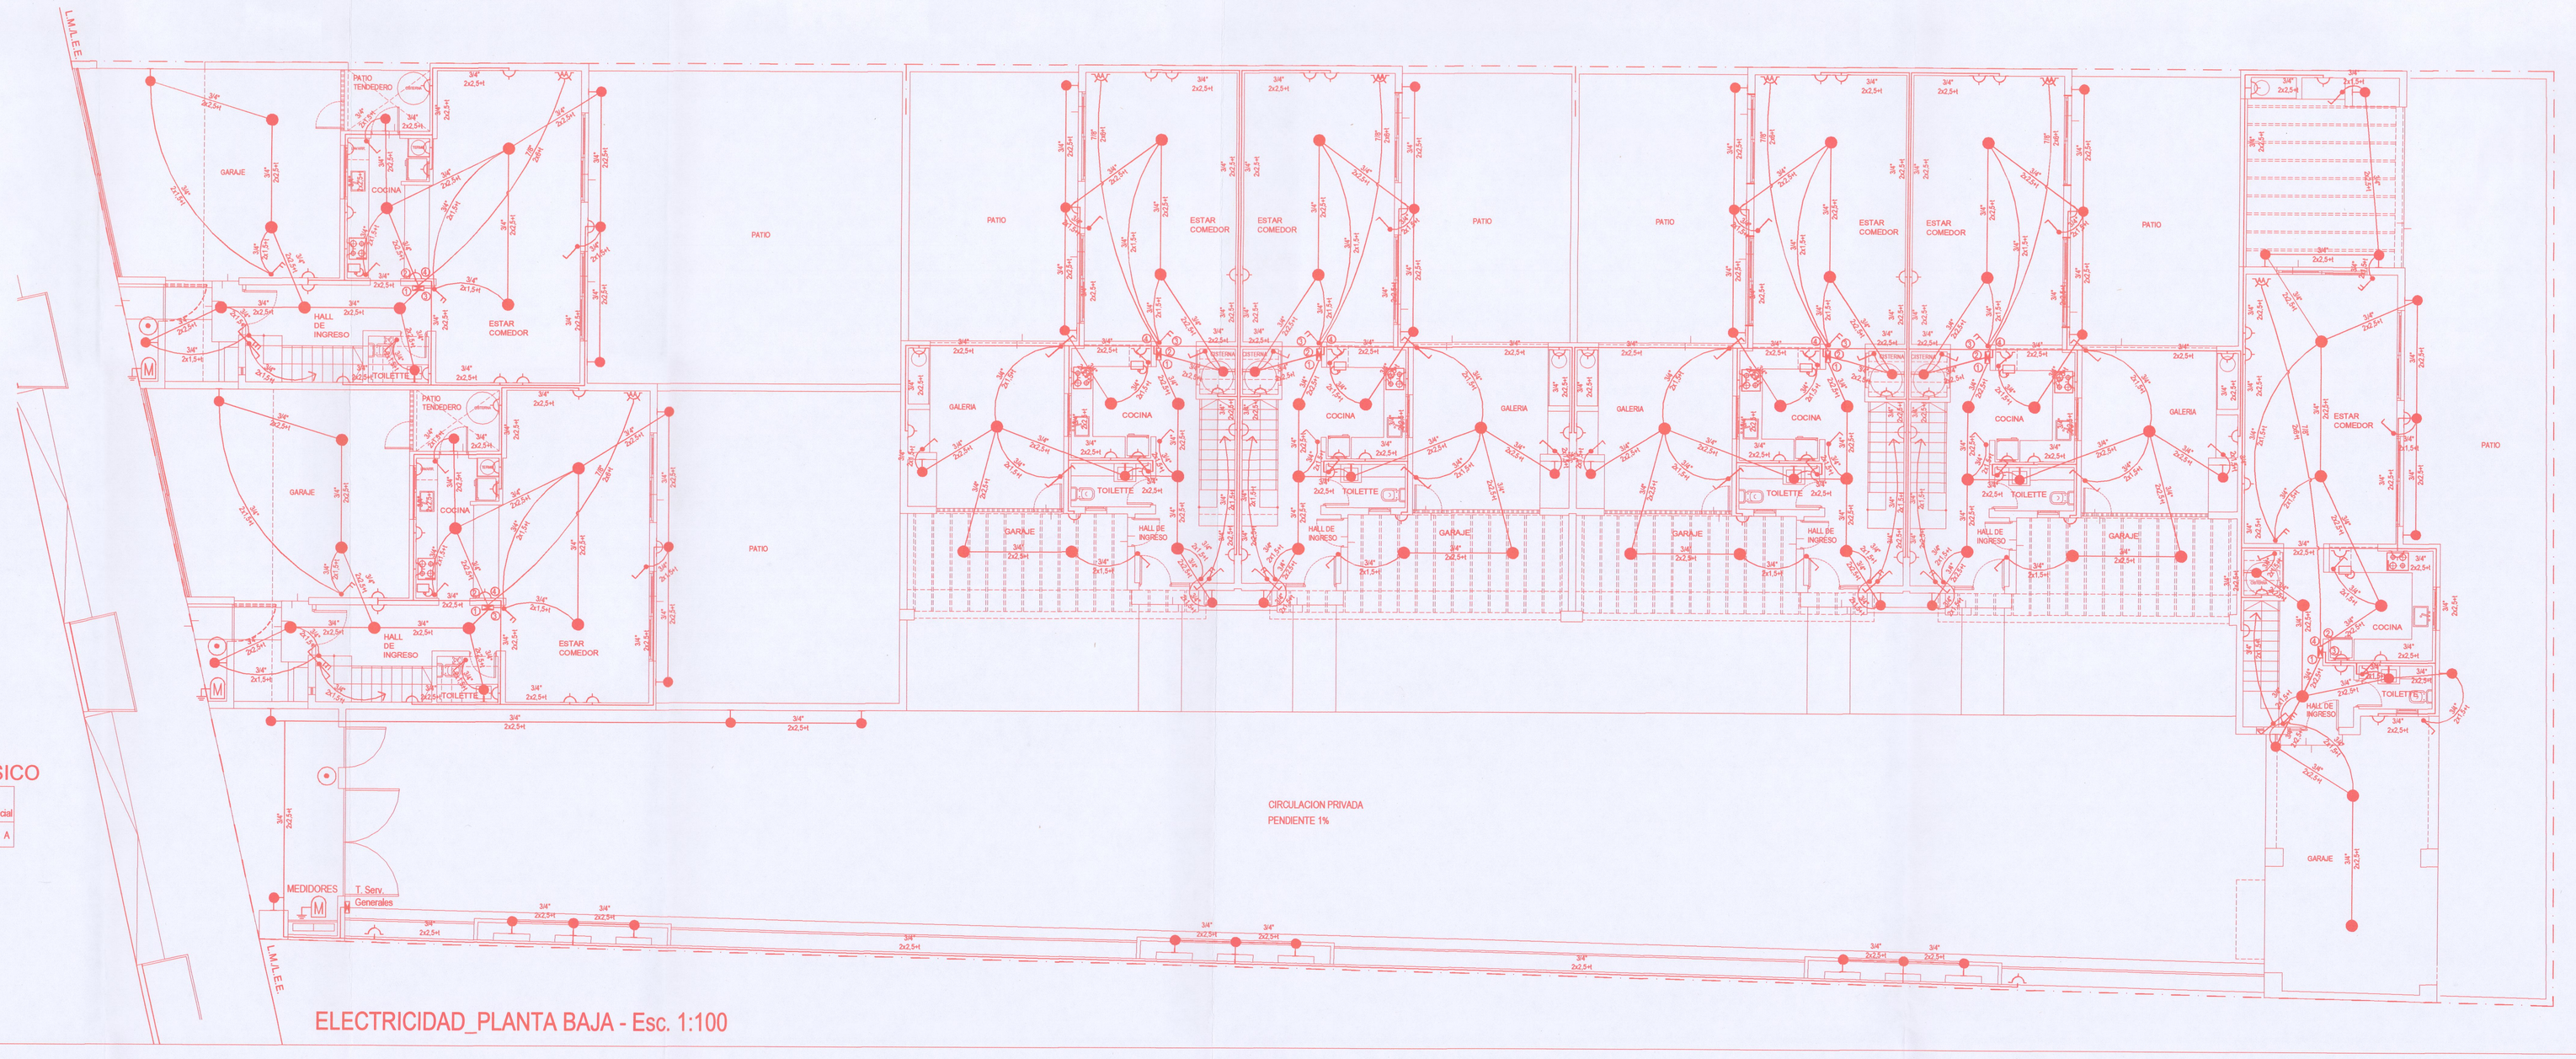

ELECTRICIDAD_PLANTA BAJA - Esc. 1:100

PUESTA A TIERRA

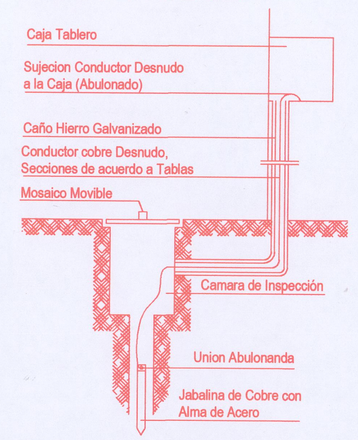

REFERENCIAS

	Medidor y Toma a Tierra
	Tablero General
	Tablero Secundario
	Centro y Brazo de Luz
	Tomacorriente
	Llave y Tomacorriente
	Llave de 1 y 2 puntos
	Llave combinada
	Campanilla y Pulsador

DISTR: 02 ZONA: 06 MANZ.: 60 PARCELA: 545

PADRON INM: 01-01-970236 DOMINIO: 7S-39263 ICM: 42-A-2025

LEY 6982

25080677

DESTINO DE LA OBRA: 7 DUPLEX

PROPIETARIO: ARCE JOSE AGUSTIN

DNI Nº: 28.048.544 CUIL/T Nº: 20-28048544-7

UBICACIÓN: CALLE MANUEL ALCORTA Nº 525

BARRIO: ALMIRANTE BROWN

CIUDAD: CAPITAL (SANTIAGO DEL ESTERO)

ESCALA: 1:100

PROYECTO Y DIRECCION DE OBRA

SUSANA PECASSIS

Colegio de Arquitectos SDE

SUP. DEL TERRENO S/T y S/Mz	1670,21 m2 S/T y 1670,21m2 S/Mz
SUP. CUBIERTA PLANTA BAJA:	684,25 m2
SUP. CUBIERTA PLANTA 1º:	511,09 m2
SUP. CUBIERTA TOTAL:	1195,34 m2

CROQUIS DE UBICACIÓN

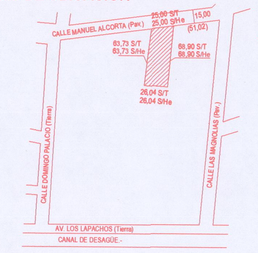

ANCHO DE CALLE:	15,00m
ANCHO DE VEREDA:	3,50m
ANCHO DE CALZADA:	7,89m

PROPIETARIO: ARCE JOSE AGUSTIN

DOMICILIO: REPUBLICA DE SIRIA Nº 64

PROYECTO: EDUARDO L. MURIAS ARQUITECTO M.P. 174

DIRECCIÓN TÉCNICA: EDUARDO L. MURIAS ARQUITECTO M.P. 174

INSTALACIÓN ELECTRICA: EDUARDO L. MURIAS ARQUITECTO M.P. 174

CATEGORIA CONSEJO PROFESIONAL

PAVIMENTO: SI

SERVICIOS COLOACALES: NO

DESIGNACIÓN:

INSTALACION ELECTRICA _ PLANTAS

05

DIRECCIÓN DE SUELO URBANO EXPEDIENTE 689-31-25 FOLIO 12 NOV 2025 2013

OBSERVACIONES:

26 NOV 2025

Las referencias al Titulo de dominio son meramente indicativas, y la aprebación administrativa no valora los derechos que de ellos emergen.

MUNICIPALIDAD DE LA CIUDAD DE SANTIAGO DEL ESTERO
SECRETARIA DE ECONOMIA
APROBADO
DIRECCION DE SUELO URBANO
EXPEDIENTE 689-31-25 Nº M-A-2025
FOLIO
12 NOV 2025

PERMISO DE COMIENZO DE OBRA Nº 2689-2025
DIRECCION DE SUELO URBANO

Arq. LEANDRO ARJONA
JEFE DE AREA DE VISACIONES TECNICAS
DIRECCION DE CATASTRO MUNICIPAL

Arq. FEDERICO LOPEZ
JEFE DE SERVICIO
DPTO. OBRAS PRIVADAS
DIRECCION DE SUELO URBANO

Arq. César Marcelo Acosta
Director D.S.U.
Municipalidad de la Capital