



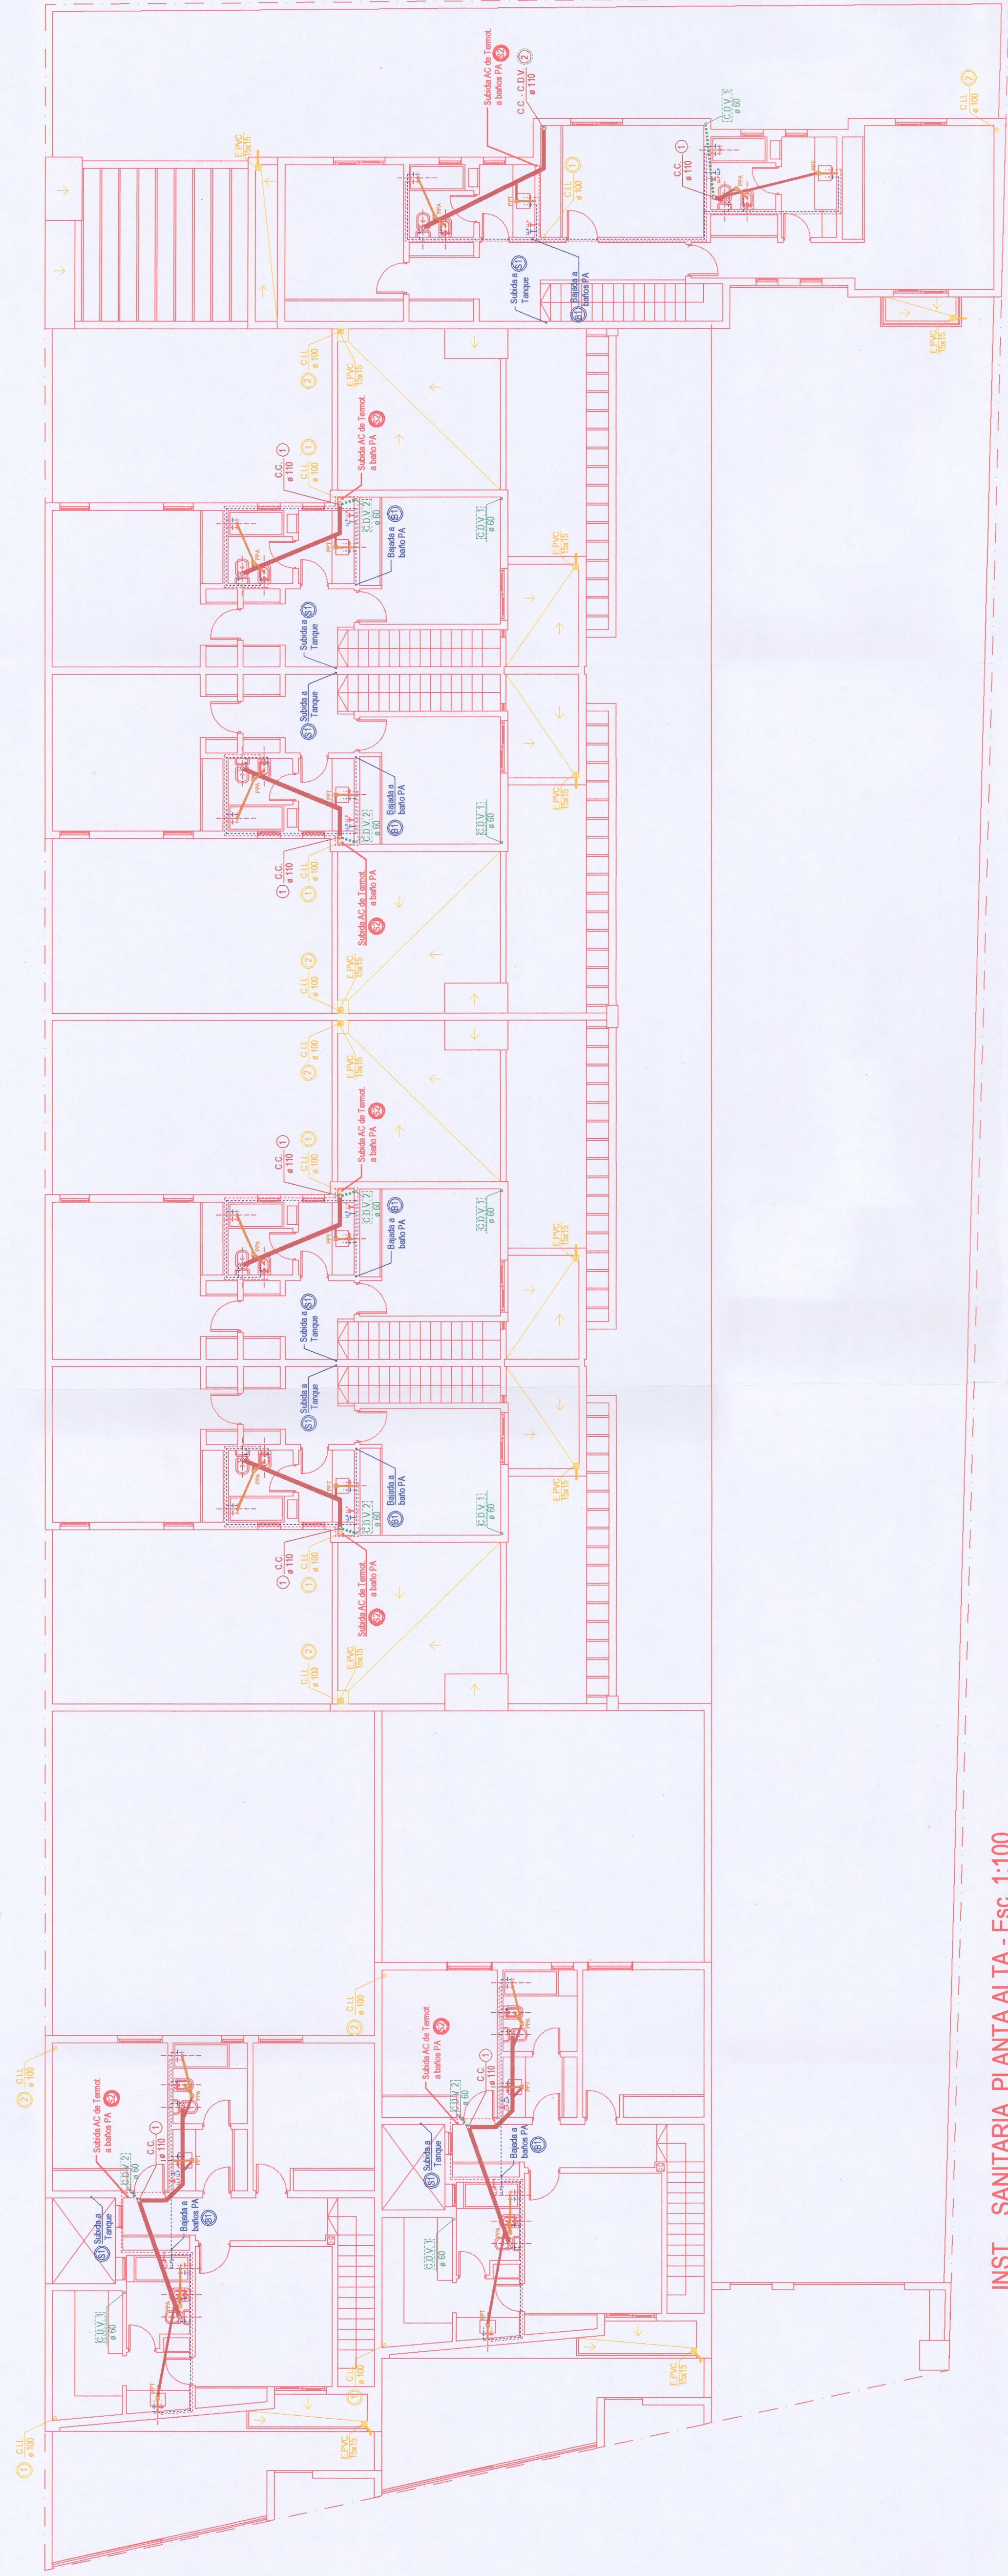

INST. SANITARIA_PLANTA ALTA - Esc. 1:100

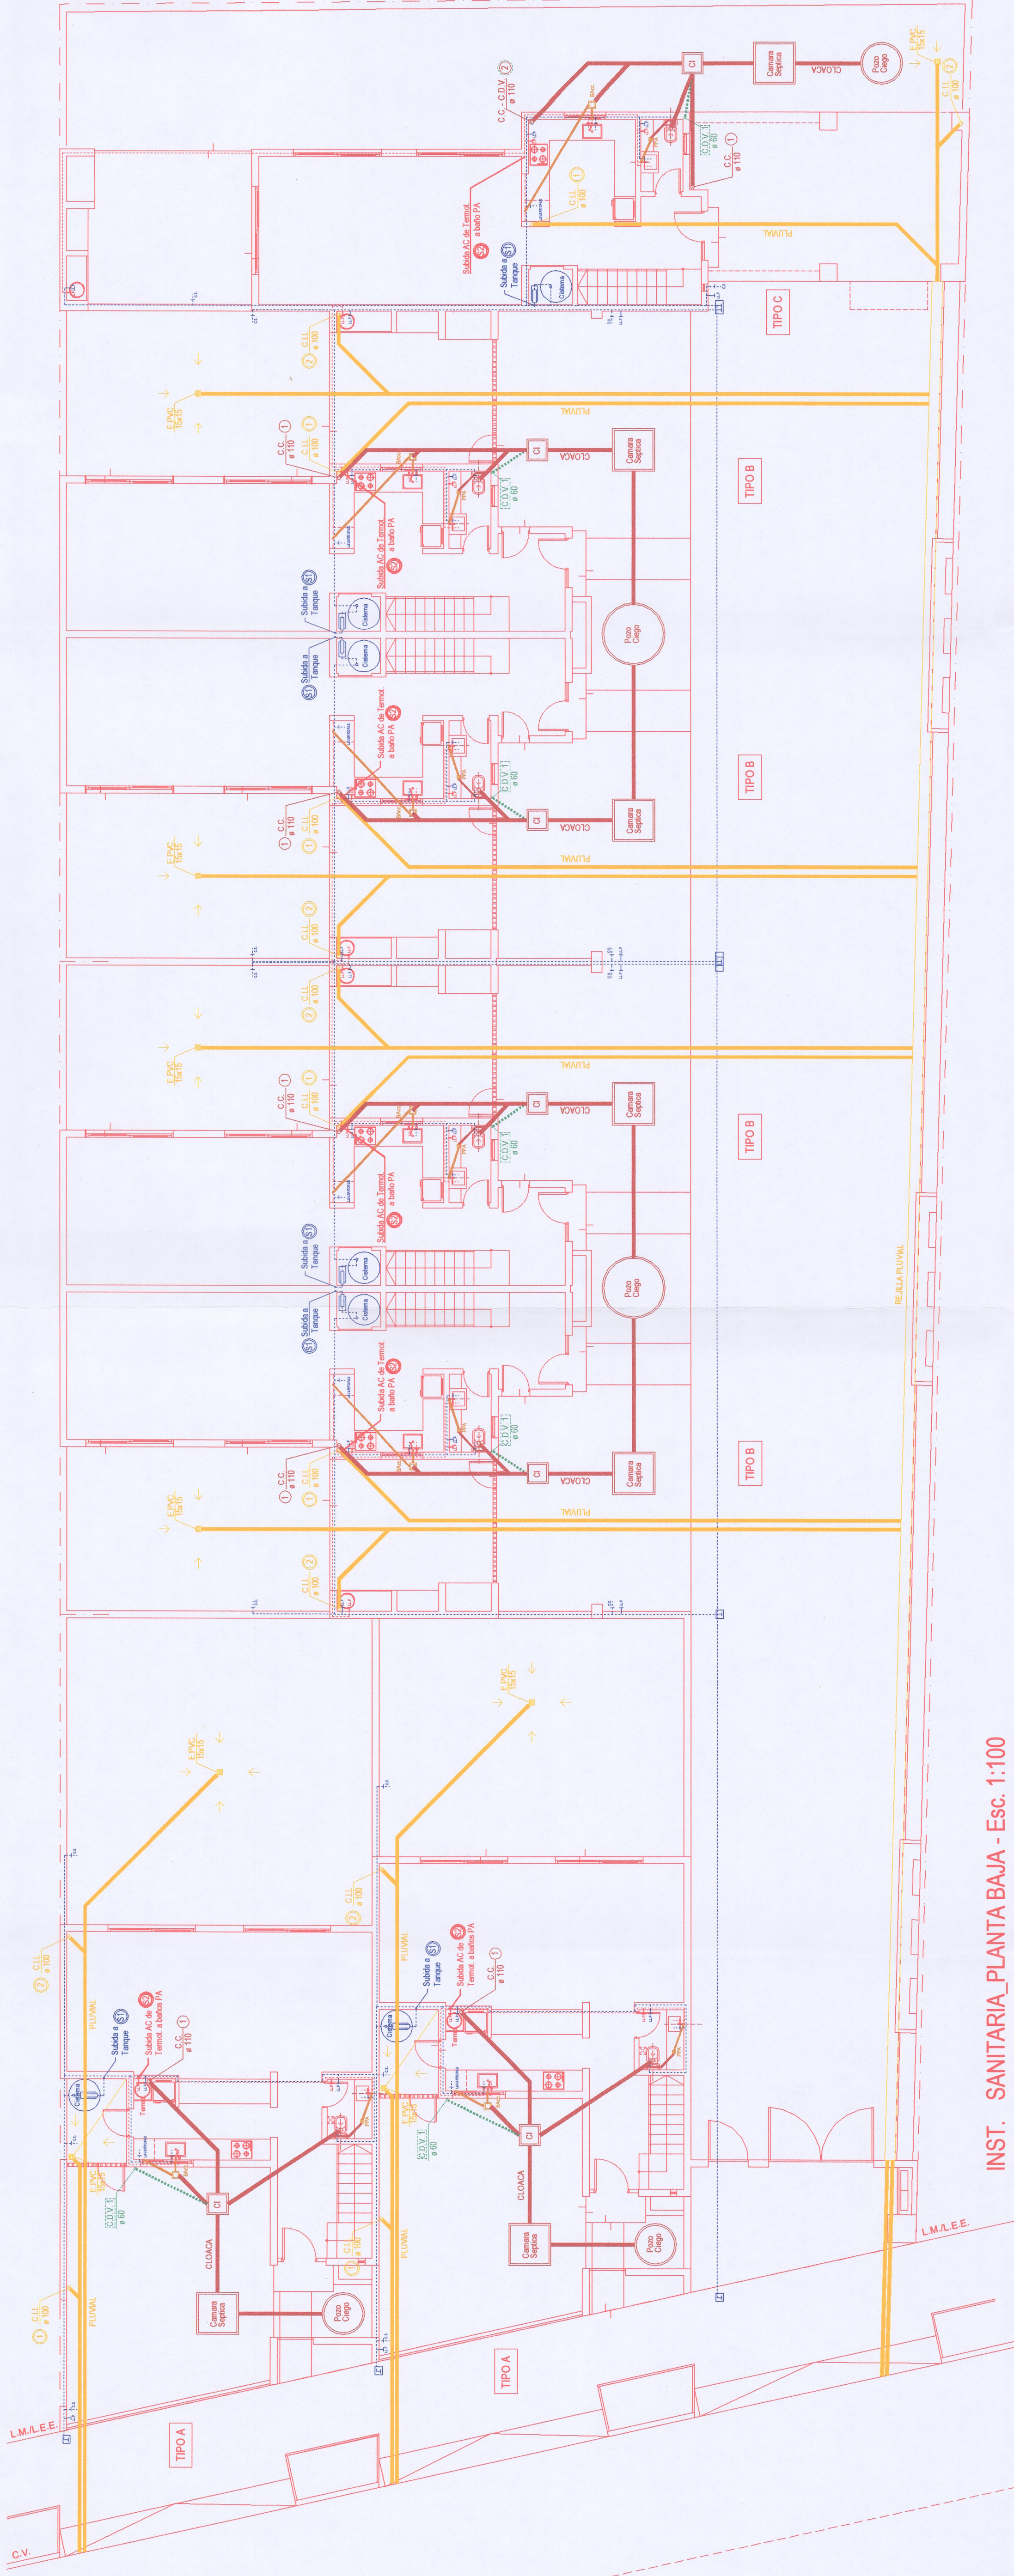

INST. SANITARIA_PLANTA BAJA - Esc. 1:100

CUADRO DE RESUMEN - TIPO A						
Designación	CÁMERAS DESAGÜES			Privadas		
	Primarias	Ø	N°	Mat.	Ø	ARTEFACTOS
Tiempo	1-5	PVC 110	2	PVC	100	Valvulo IP (D.A.1'X2.5' 8-T GABERIA
						Baño 2 IP (D.A.1'X2.5' 8-T GABERIA
Hor. Cal.						
Columna	1	PVC 110	2	PVC	100	P.C 2X2 DESG P.V.C 50
P.P.	5	PVC 63	Nº	CÁMERAS DE AGUA FRIA		
						P.L. —
						①
IP.	3	PVC 110		MATERIALES Y DIAMETRO		
B. Acc.	1	PVC 63				

CUADRO DE RESUMEN - TIPO B									
Designación	CÁMERAS DESAGÜES					ARTERFACTOS			
	Primarias			Privadas					
	N°	Mat.	Ø	N°	Mat.	Ø	Detalle	IP (D.A.)	2° S.T. TUBERÍA
Tiempo	1-4	P.V.C 110	2	P.V.C 110	2	P.V.C 100		IP (D.A.)	2° S.T. TUBERÍA
Hor. Cal.	-	-	-	-	-	-			
Columna	1	P.V.C 110	2	P.V.C 110	2	P.V.C 100	P.C	20.5 DESG. P.V.C 50	
P.P.	3	P.V.C 63					P.L	-	

CUADRO DE RESUMEN - TIPO C									
Designación	CÁMERAS DESAGÜES					CÁMERAS DE AGUA FRÍA			
	Primarias		Privadas			CÁMERAS DE AGUA FRÍA		MATERIALES Y DIAMETRO	
	N°	Mat.	Ø	N°	Mat.	Ø	N°	Mat.	Ø
Tiempo	1-5	P.V.C 110	2	P.V.C 100	100				
Hor. Cal.	—	—	—	—	—				
Columna	2	P.V.C 110	2	P.V.C 100	P.C	100	205 Ø630, P.V.C 50		
P.P.	5	P.V.C 63			P.L	Ø	—		
I.P.	3	P.V.C 110							
B. Aco.	1	P.V.C 63							

DISTR. 02
PAUCON N.M. 01-01-970236

ZONA: 06
MANZ.: 60
DOMINIO: 75-39283

PARCELA: 545
FOLIO: 42-A-2025

LEY: 468

DESTINO DE LA OBRA: 7 DUPLEX

PROPIETARIO: ARCE JOSE AGUSTIN

DNI N°: 28.046.544

UBICACIÓN: CALLE MANUEL ALCORTA N° 525

BARRIO: ALMIRANTE BROWN

CIUDAD: CAPITAL (SANTIAGO DEL ESTERO)

ESCALA: 1:100

SECRETARÍA DE ECONOMÍA
SECRETARÍA DE ECONOMÍA
SECRETARÍA DE ECONOMÍA

26080677

071125

SECRETARÍA DE ECONOMÍA
SECRETARÍA DE ECONOMÍA
SECRETARÍA DE ECONOMÍA

PROPIETARIO: ARCE JOSE AGUSTIN

DOMICILIO: REPUBLICA DE CHINA N° 84

PROYECTO: DOMICILIO

DIRECCIÓN TÉCNICA: DOMICILIO

INSTALACIÓN ELÉCTRICA: DOMICILIO

CATEGORÍA: CONSEJO PROFESIONAL N° 172

PROYECTO: DOMICILIO

DIRECCIÓN TÉCNICA: DOMICILIO

INSTALACIÓN ELÉCTRICA: DOMICILIO

CATEGORÍA: CONSEJO PROFESIONAL N° 172

PROYECTO: DOMICILIO

DIRECCIÓN TÉCNICA: DOMICILIO

INSTALACIÓN ELÉCTRICA: DOMICILIO

CATEGORÍA: CONSEJO PROFESIONAL N° 172

OBSERVACIONES: 26 NOV 2025

INSTALACION SANITARIA _ PLANTAS

06

SECRETARÍA DE ECONOMÍA
SECRETARÍA DE ECONOMÍA
SECRETARÍA DE ECONOMÍA

26080677

071125

SECRETARÍA DE ECONOMÍA
SECRETARÍA DE ECONOMÍA
SECRETARÍA DE ECONOMÍA

SECRETARÍA DE ECONOMÍA
SECRETARÍA DE ECONOMÍA
SECRETARÍA DE ECONOMÍA

26080677

071125

SECRETARÍA DE ECONOMÍA
SECRETARÍA DE ECONOMÍA
SECRETARÍA DE ECONOMÍA