


DETALLE DE BASES CENTRADAS B1 1.20x1.20
Esc.: 1:25


Esc.: 1:25

B1 1.20x1.20
COTA DE IMPLANTE: - 0.90 m

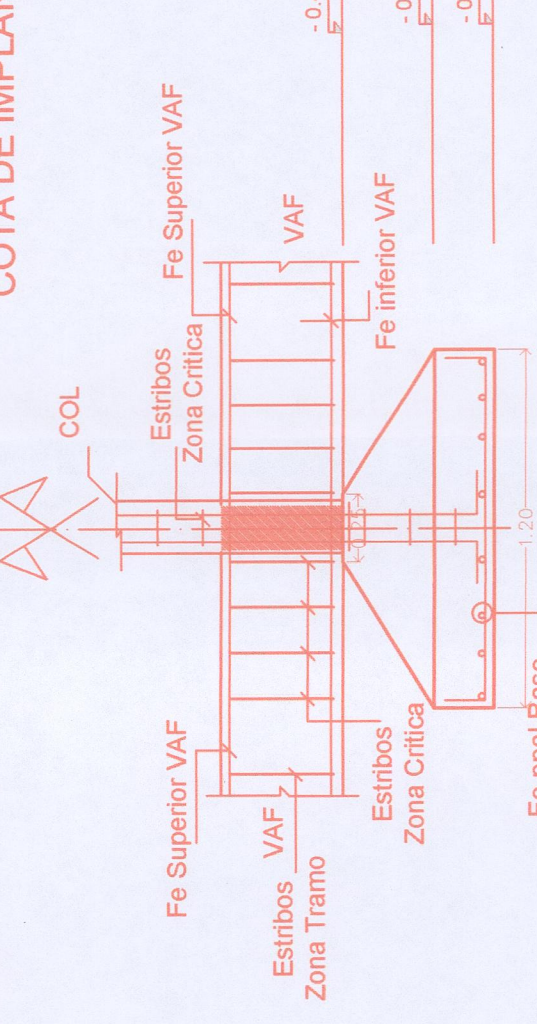


DETALLE DE BASES CENTRADAS B3 0.80x0.80

Esc.: 1:25

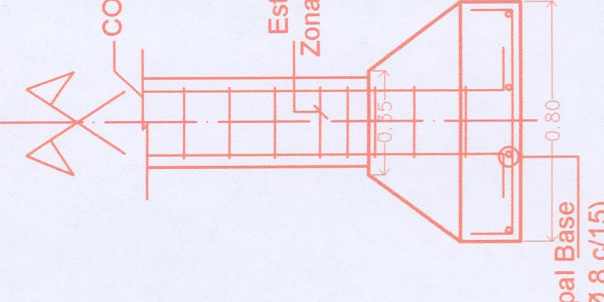


DETALLE DADO DE H°A° 0.80x0.80x0.80

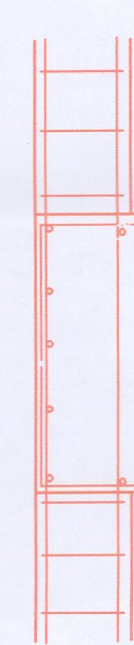


DETALLE DE BASES CENTRADAS B2 1 40x1.40

Esc.: 1:25

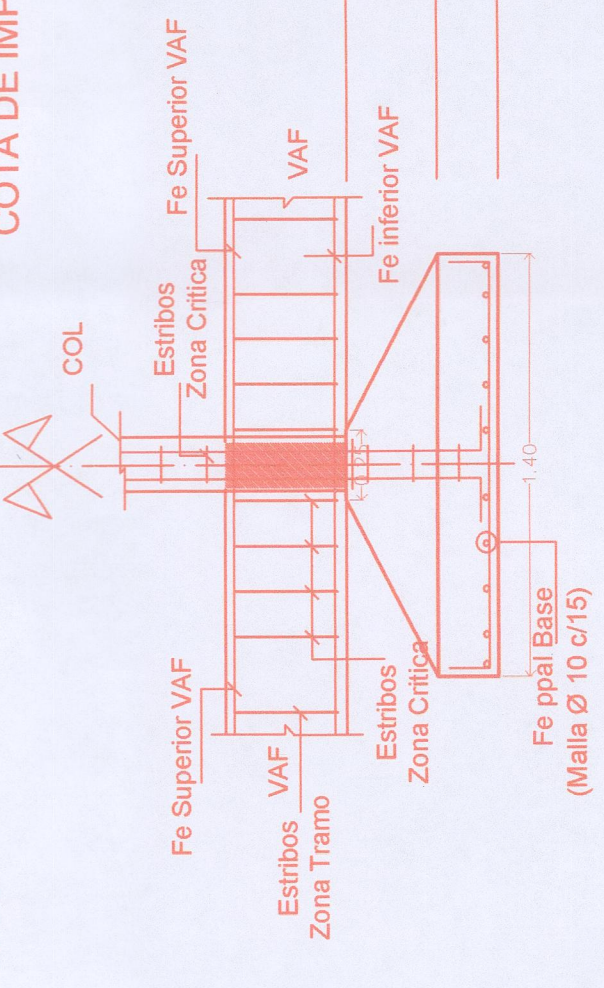

DETALLE DE BASES COMBINADA BC1 1.20x2.40


Esc.: 1:25

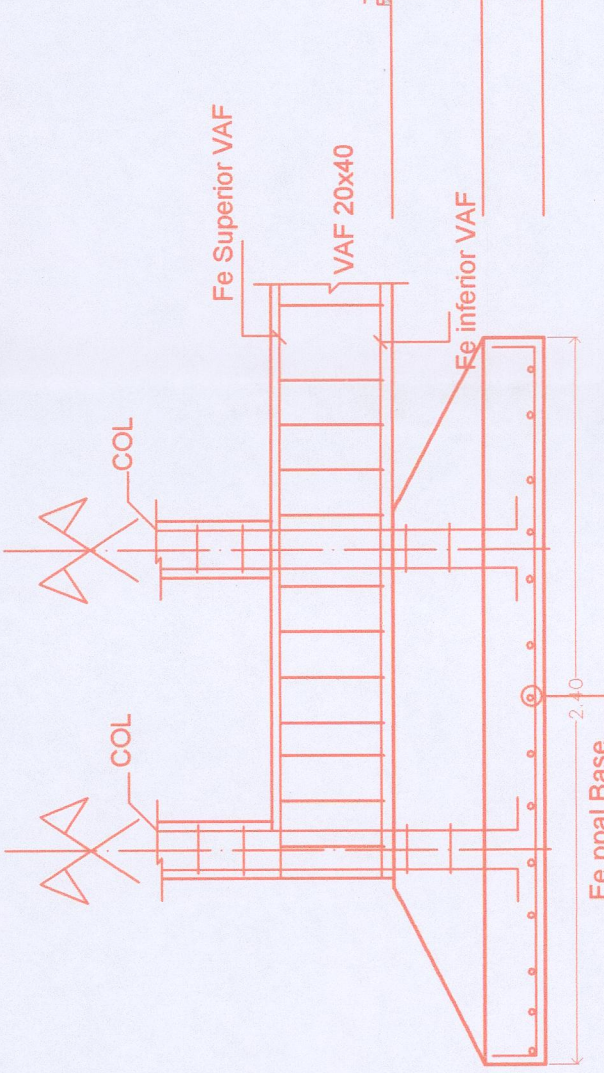


DETALLE DE VIGAS / NIVEL FUNDACIONES

Esc.: 1:10

VAF 20x40

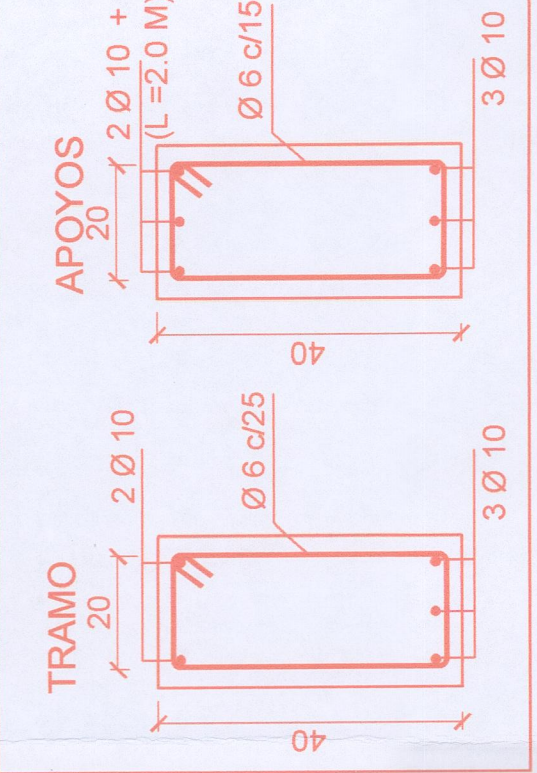


VEF 20x20

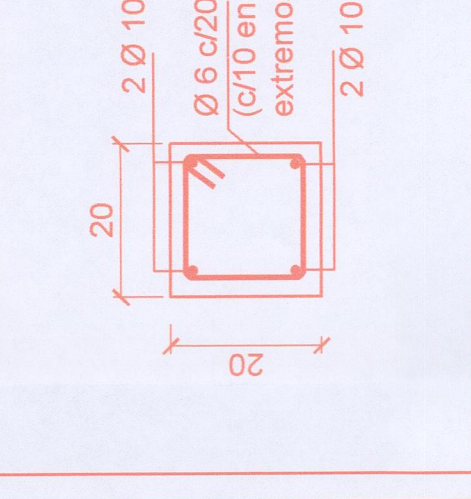

DETALLE DE VIGAS DE FUNDACION


Esc.: 1.10

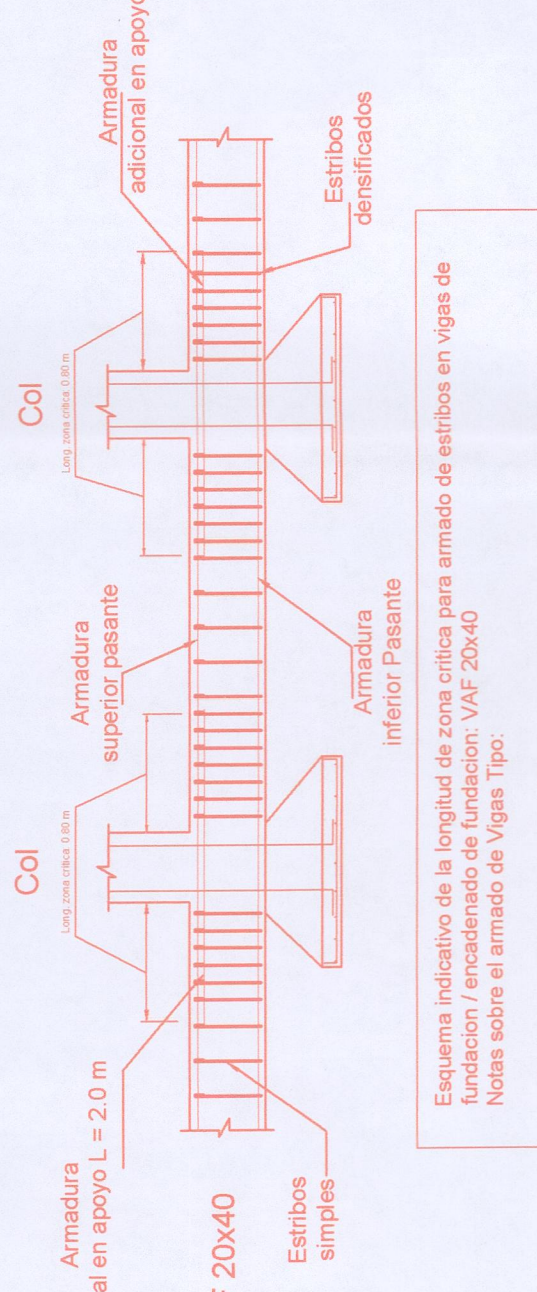

Notas sobre el armado de Vigas Tipo:

DETALLE DE COLUMNAS / VIGAS TÍPICAS



Esc.: 1:10

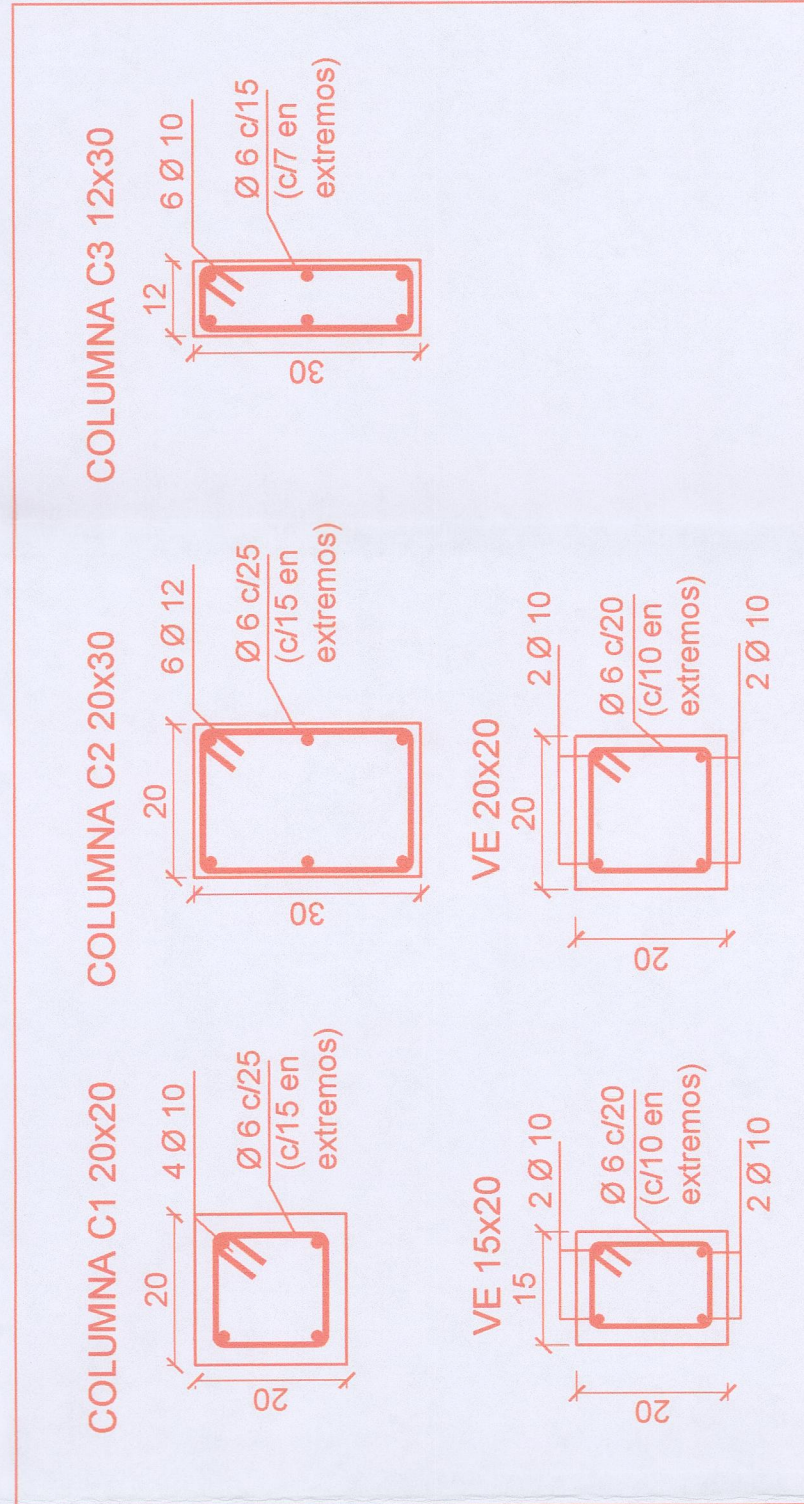


ESQUEMA ARMADO - PORTICOS HORMIGON ARMADO

Long. zona critica: 1.0 m


Long. zona critica: 1.0 m

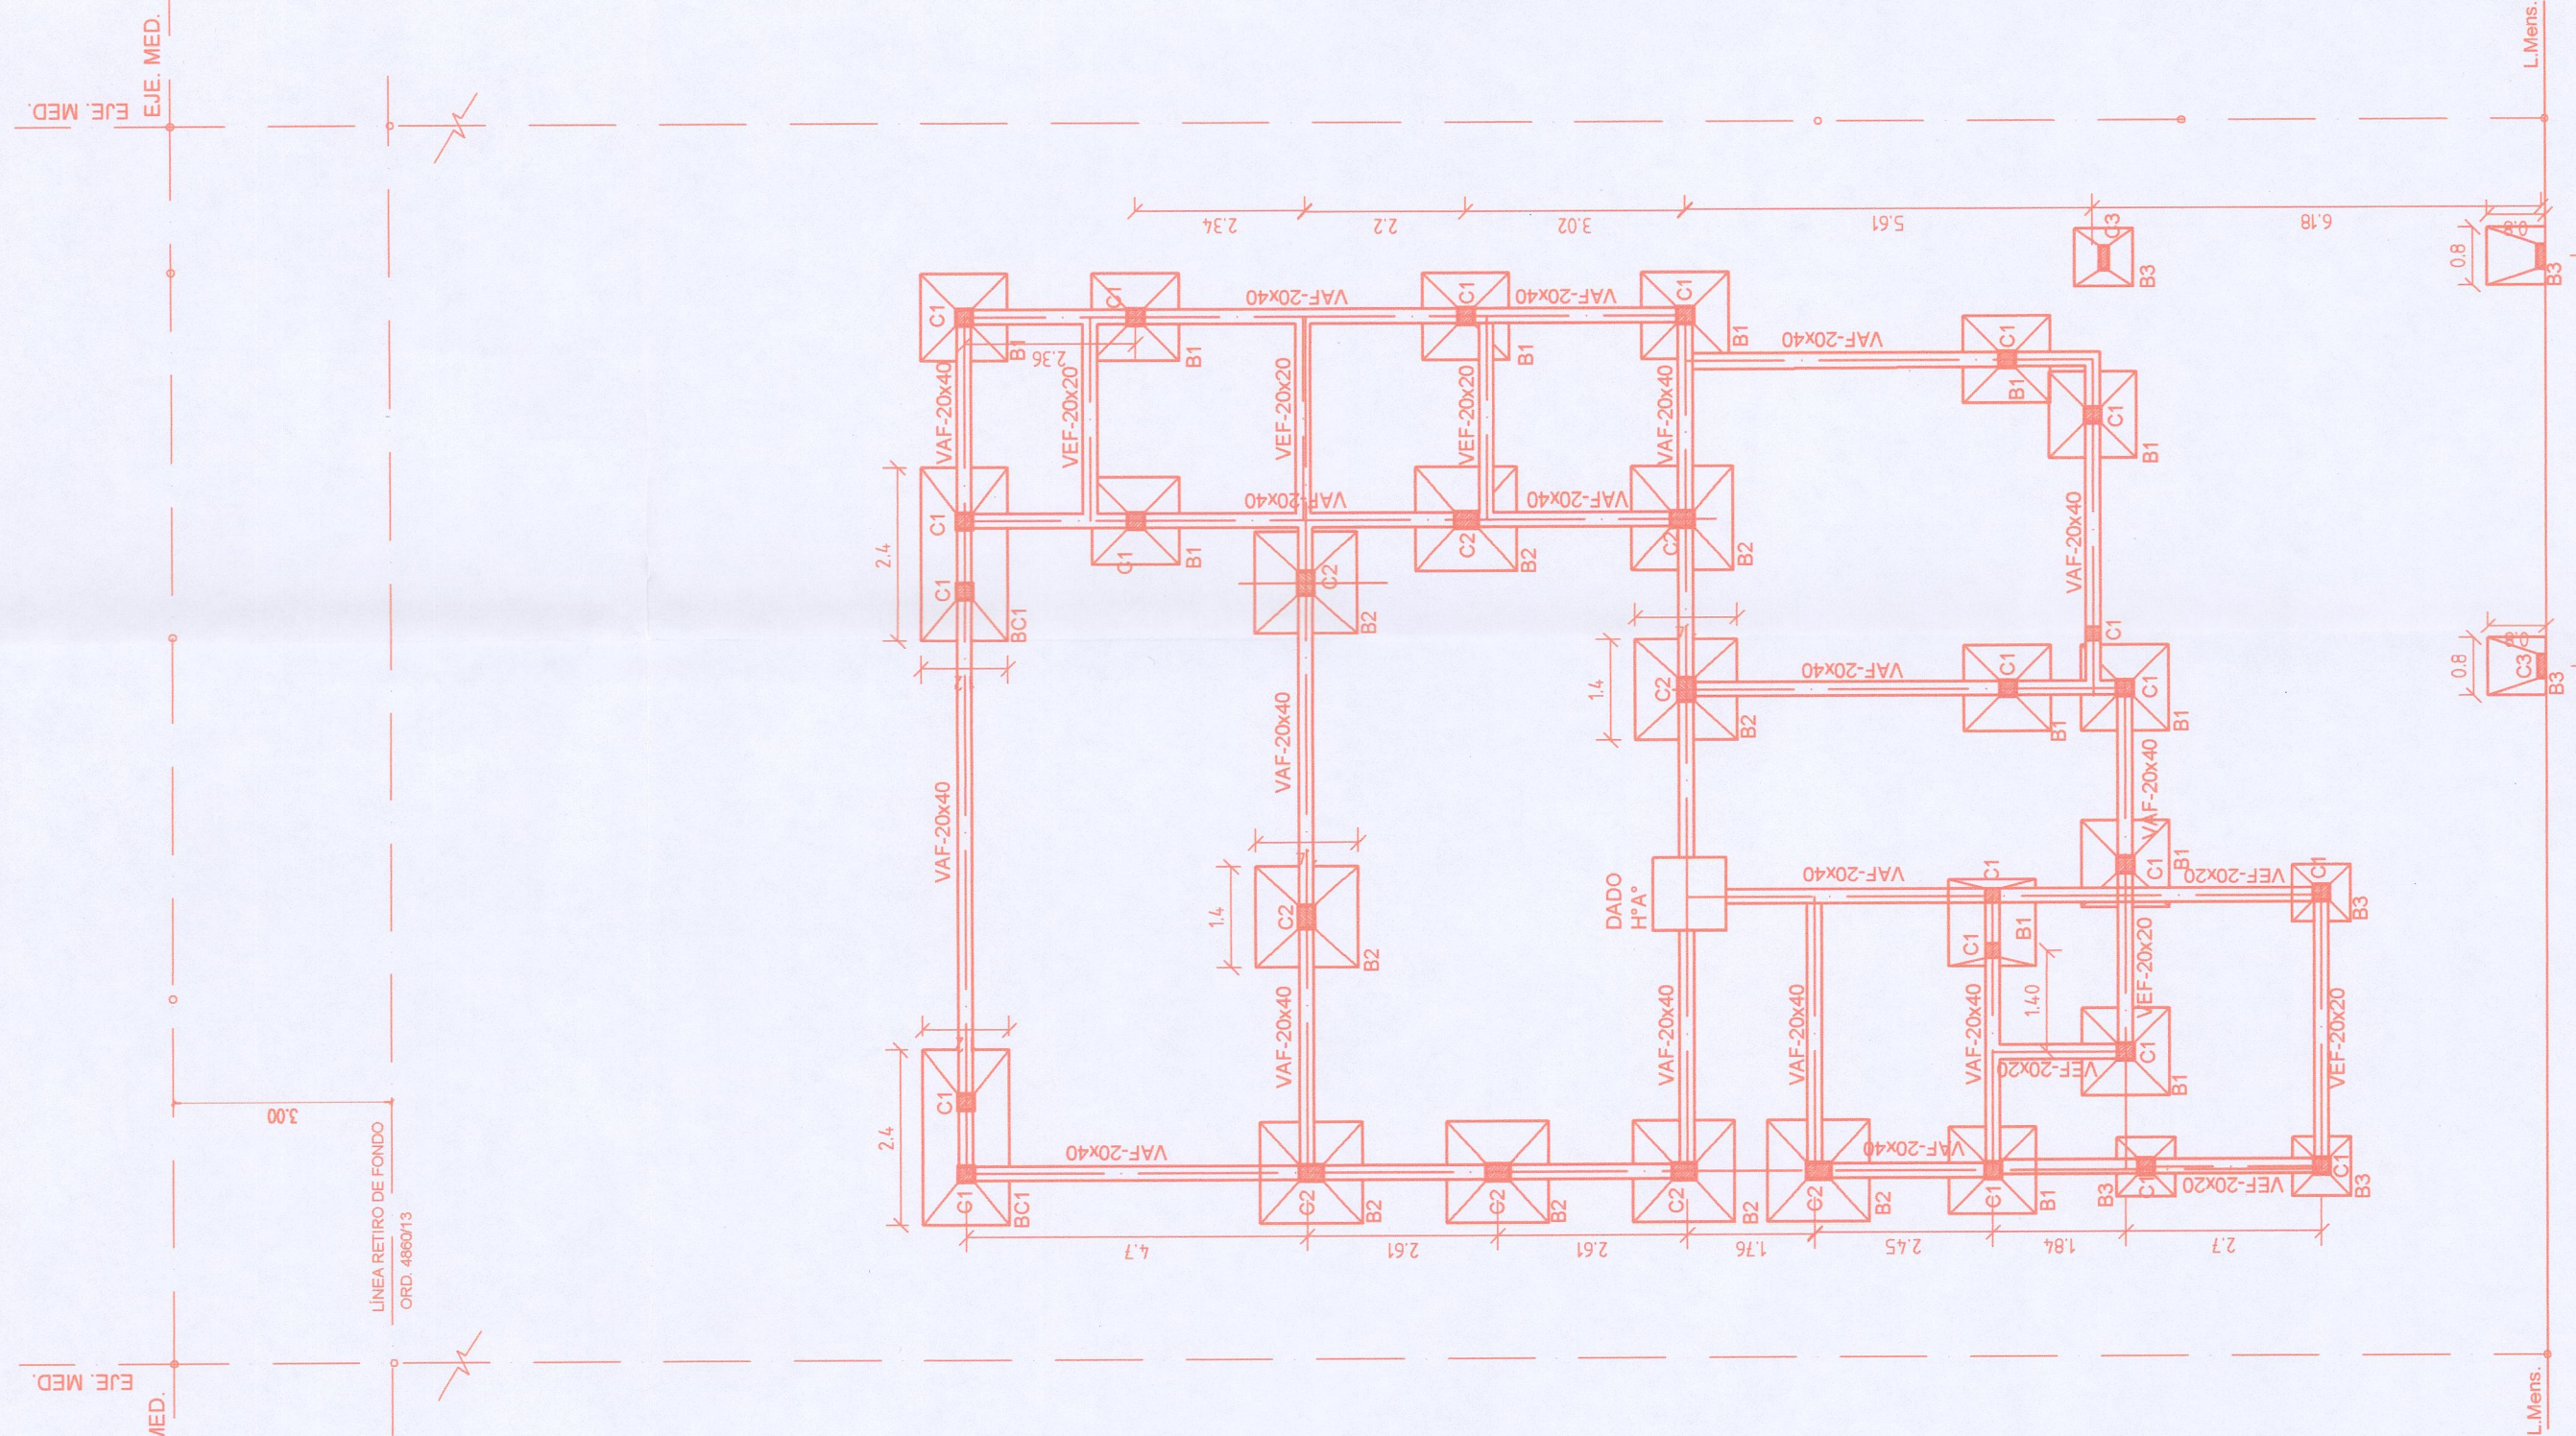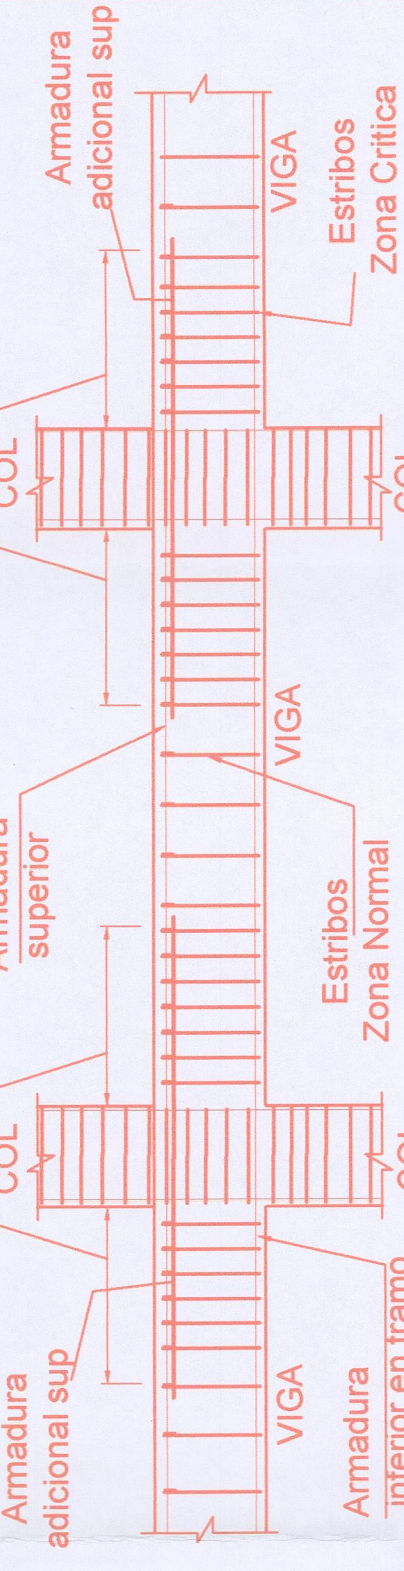



PLANTA DE FUNDACIONES

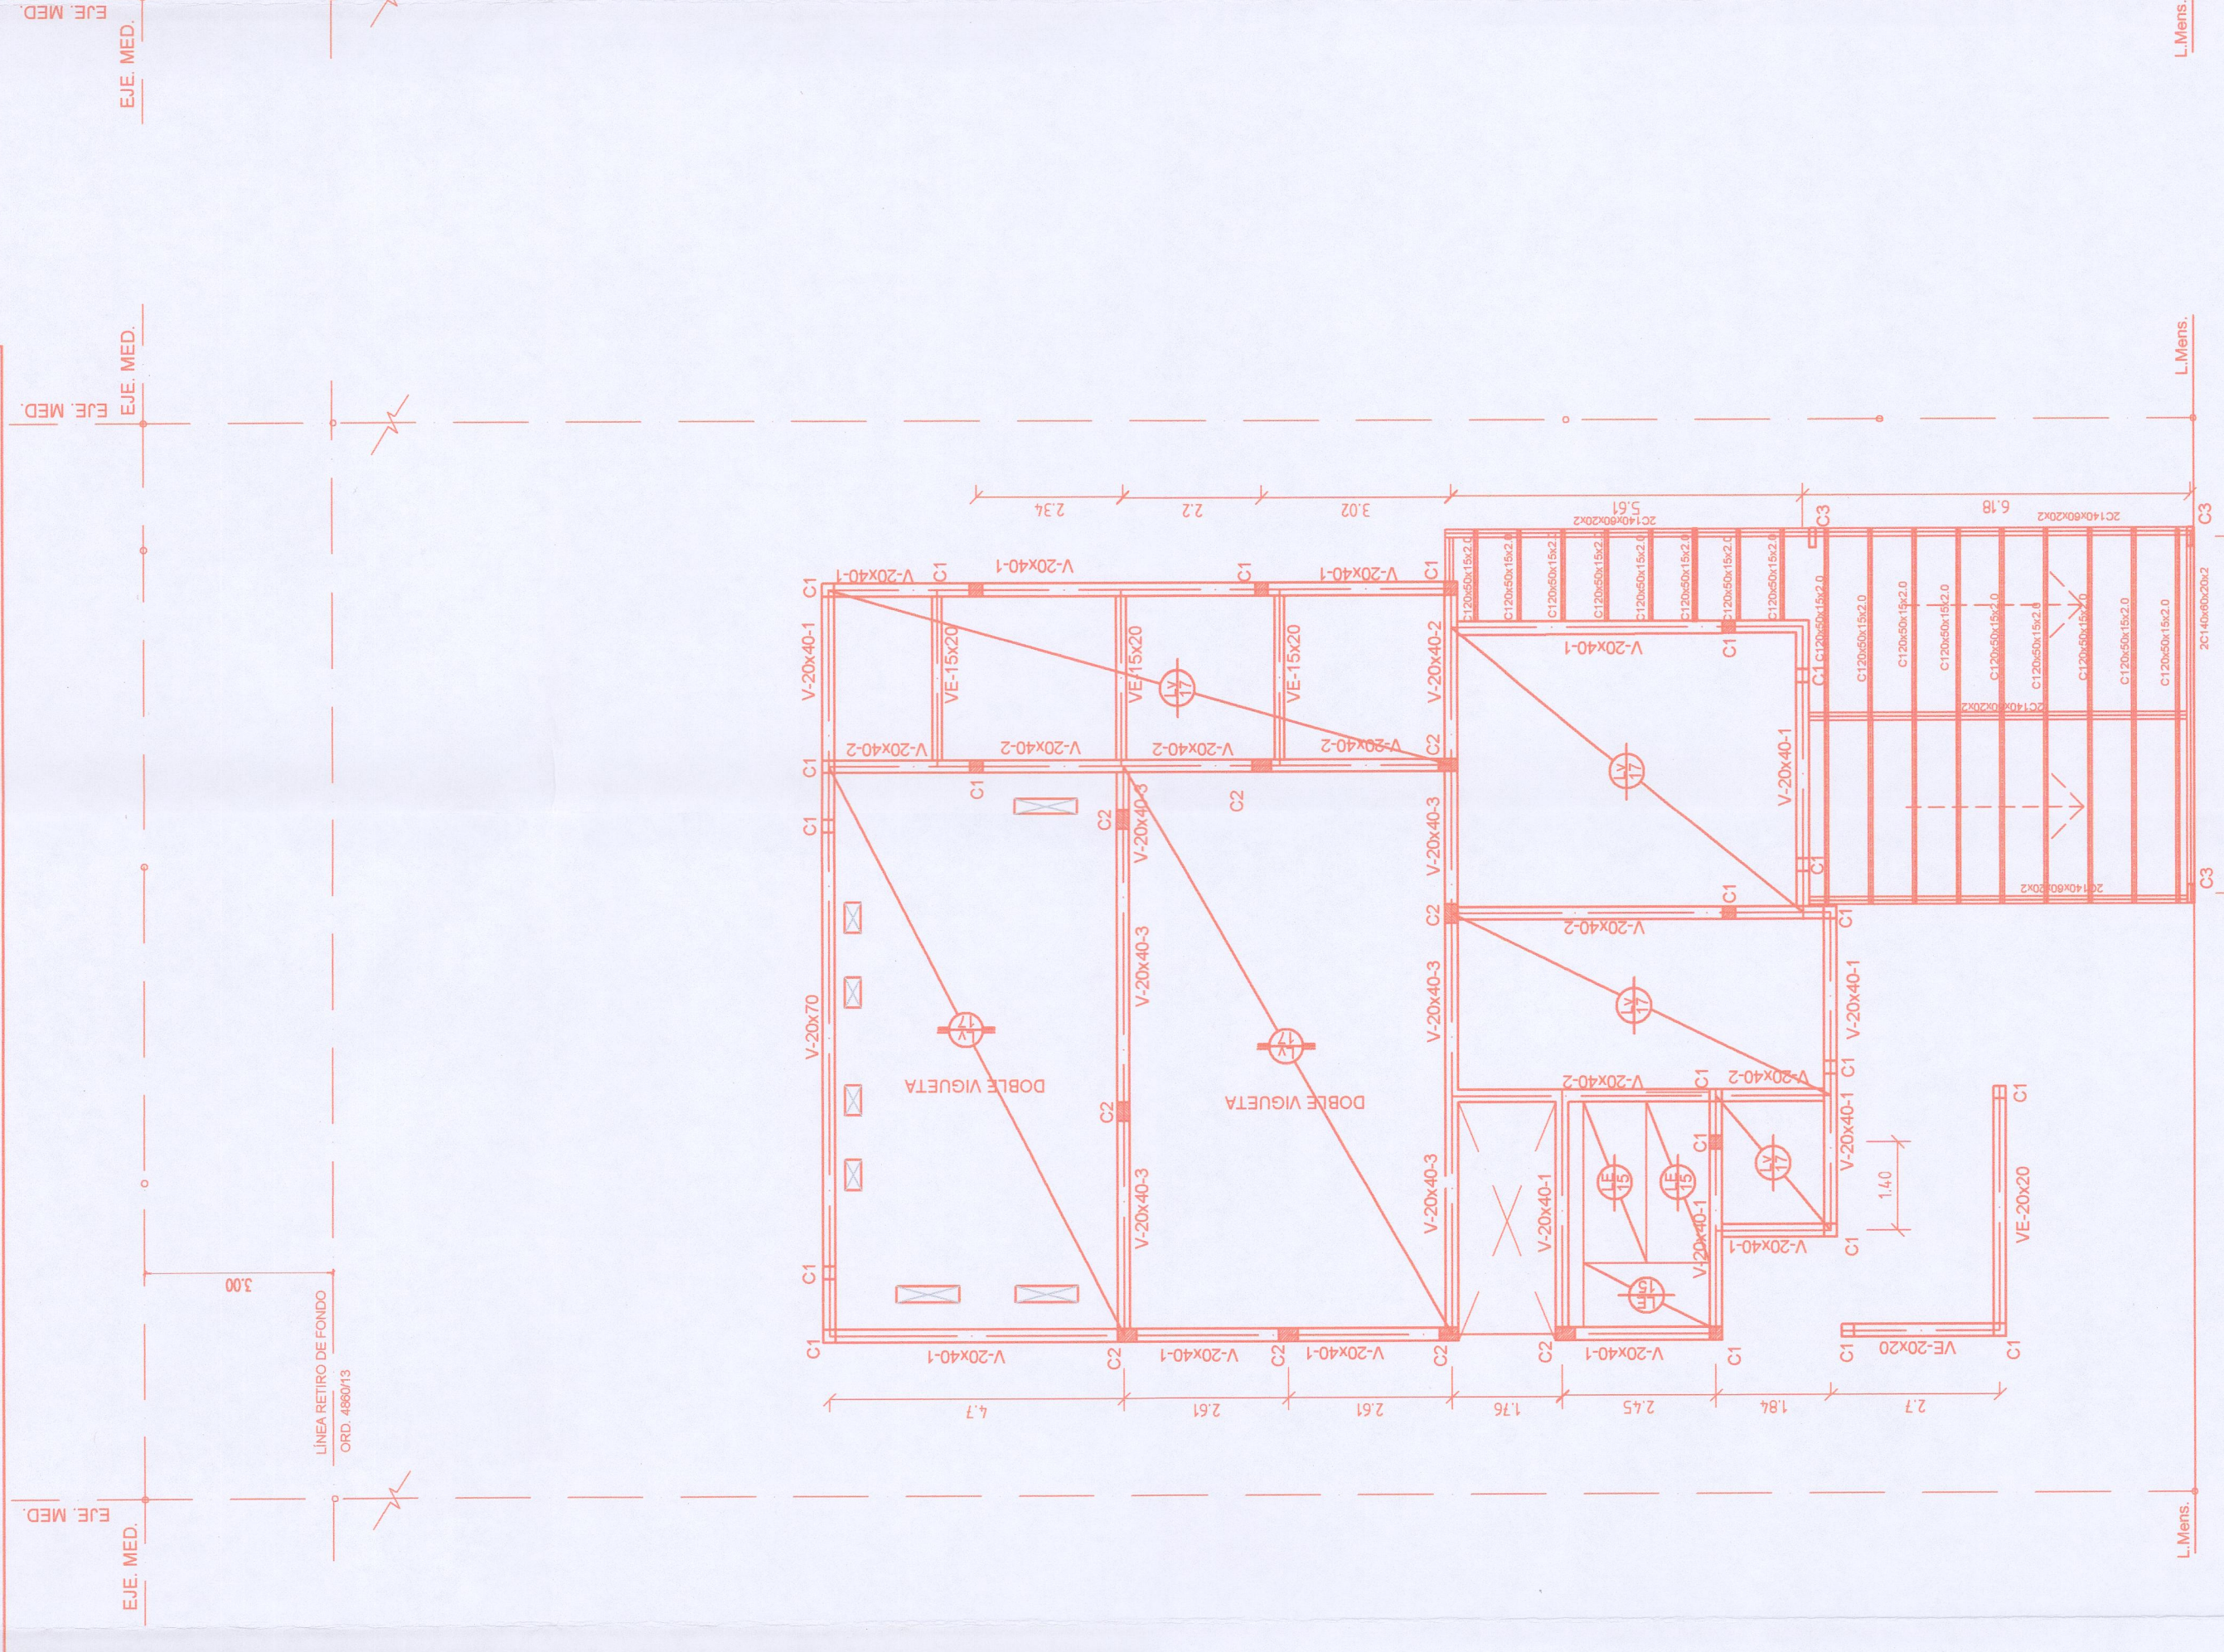

PLANTA DE ESTRUCTURAS

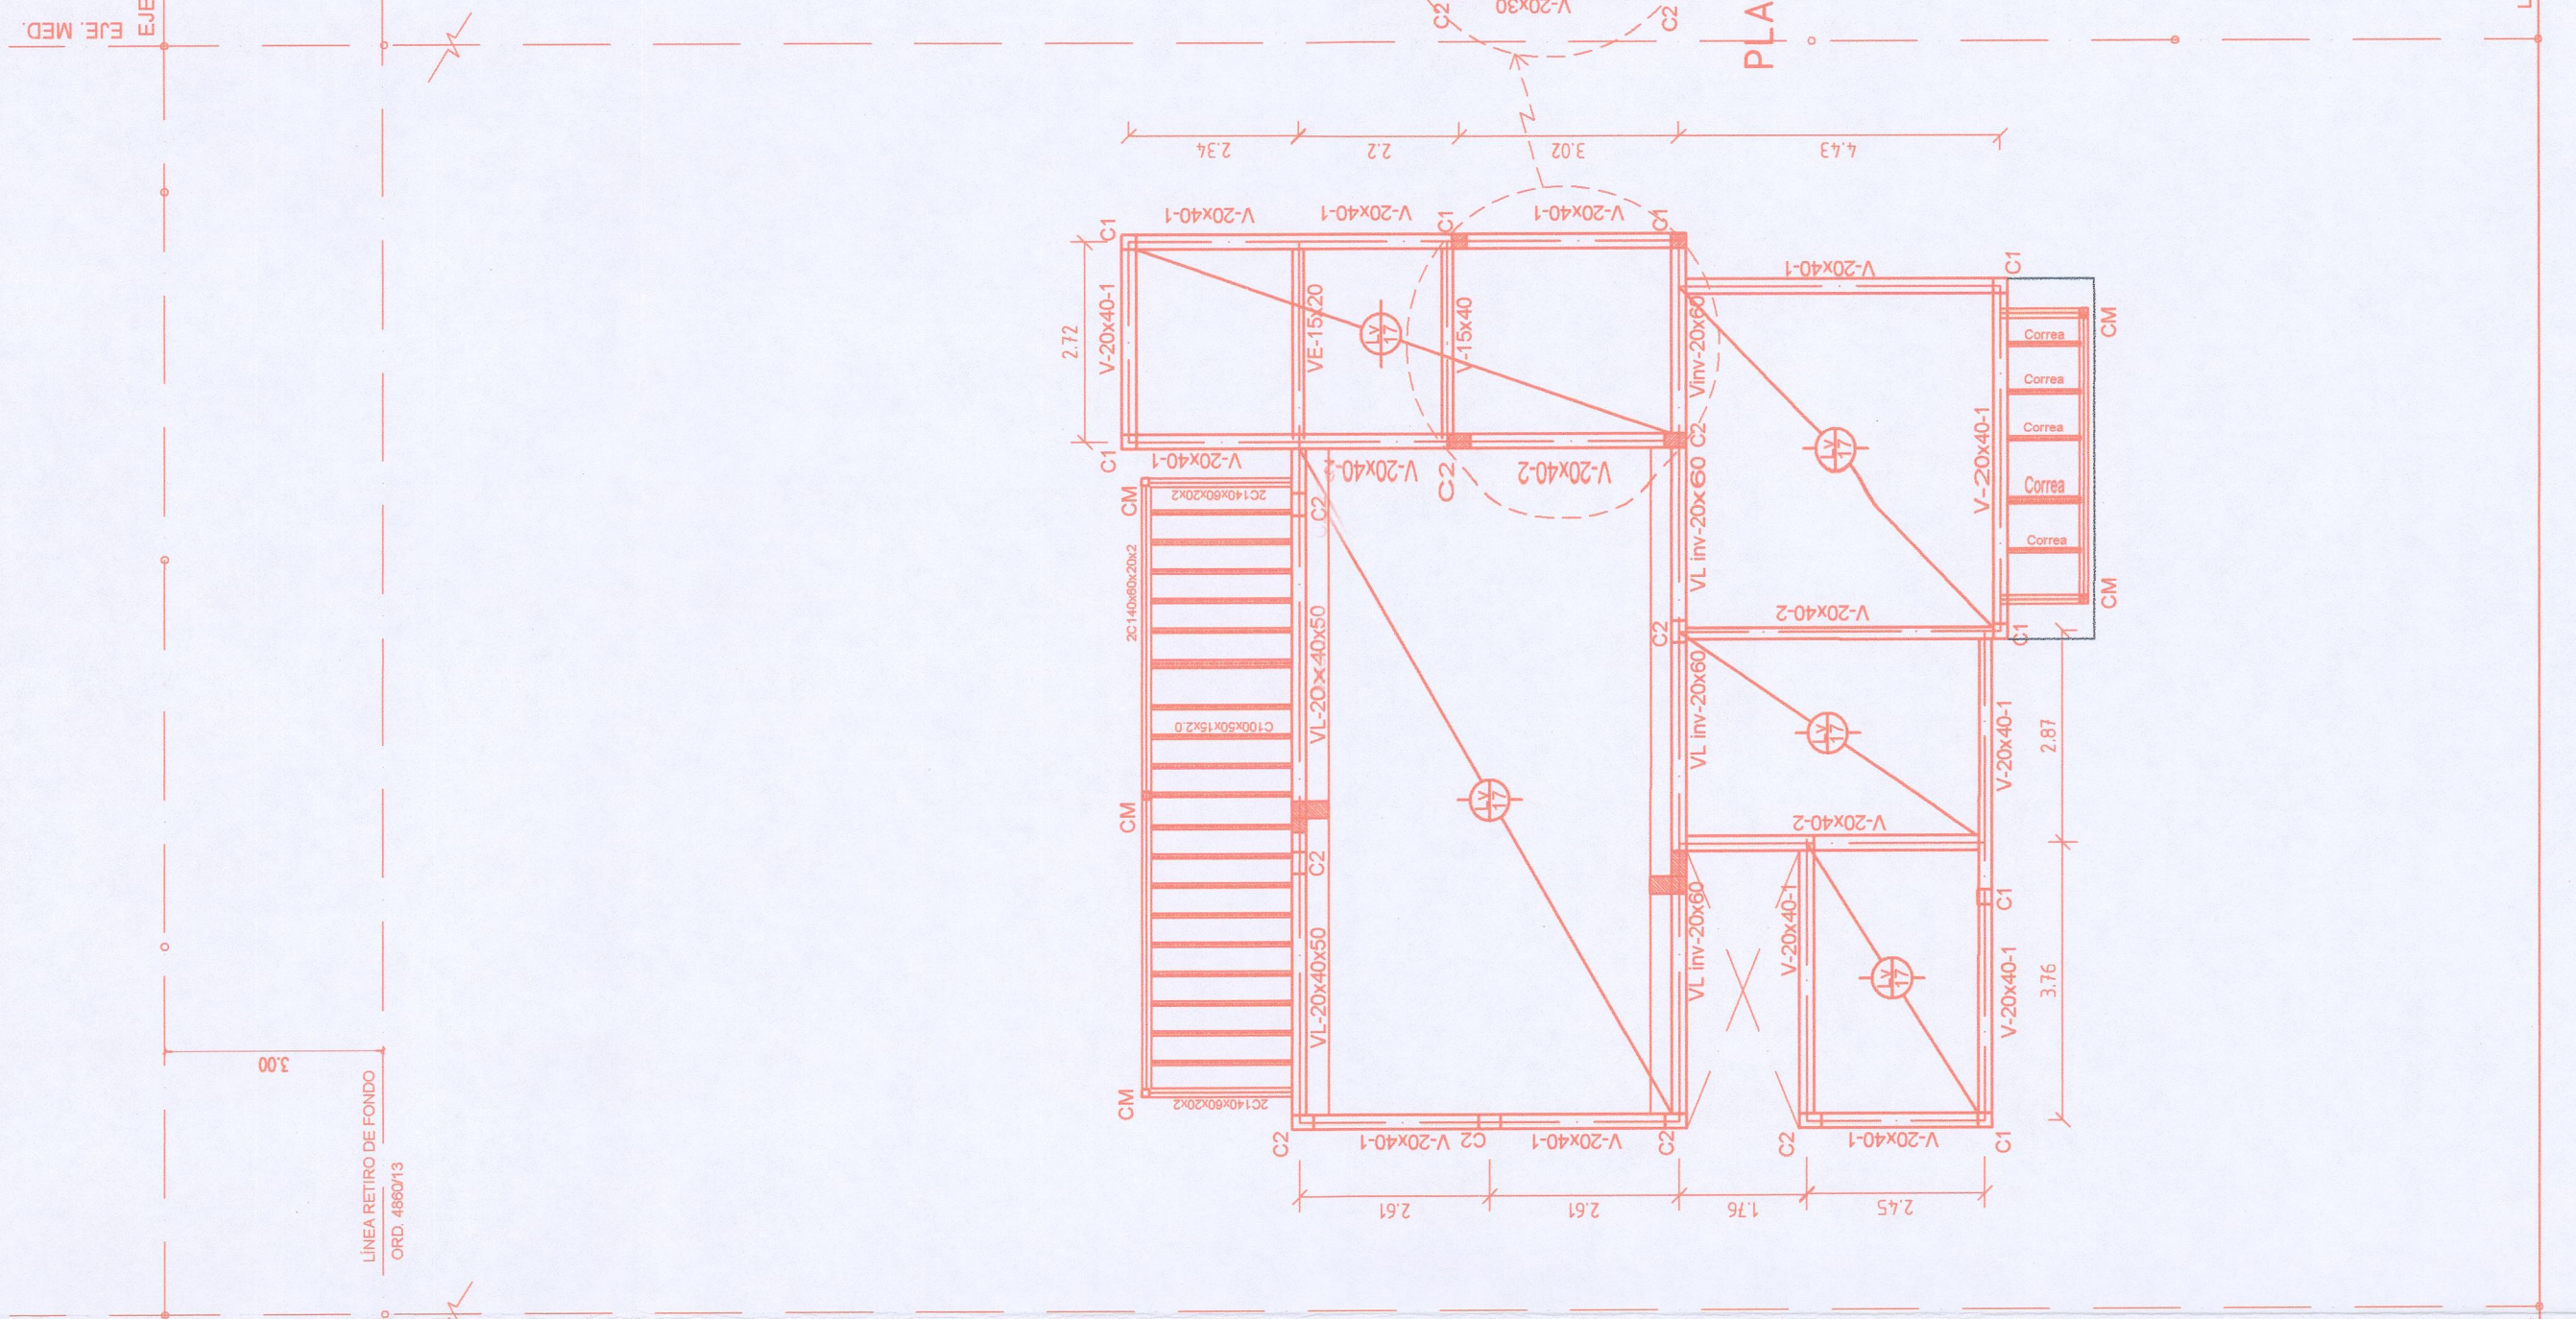

PLANTA DE ESTRUCTURAS

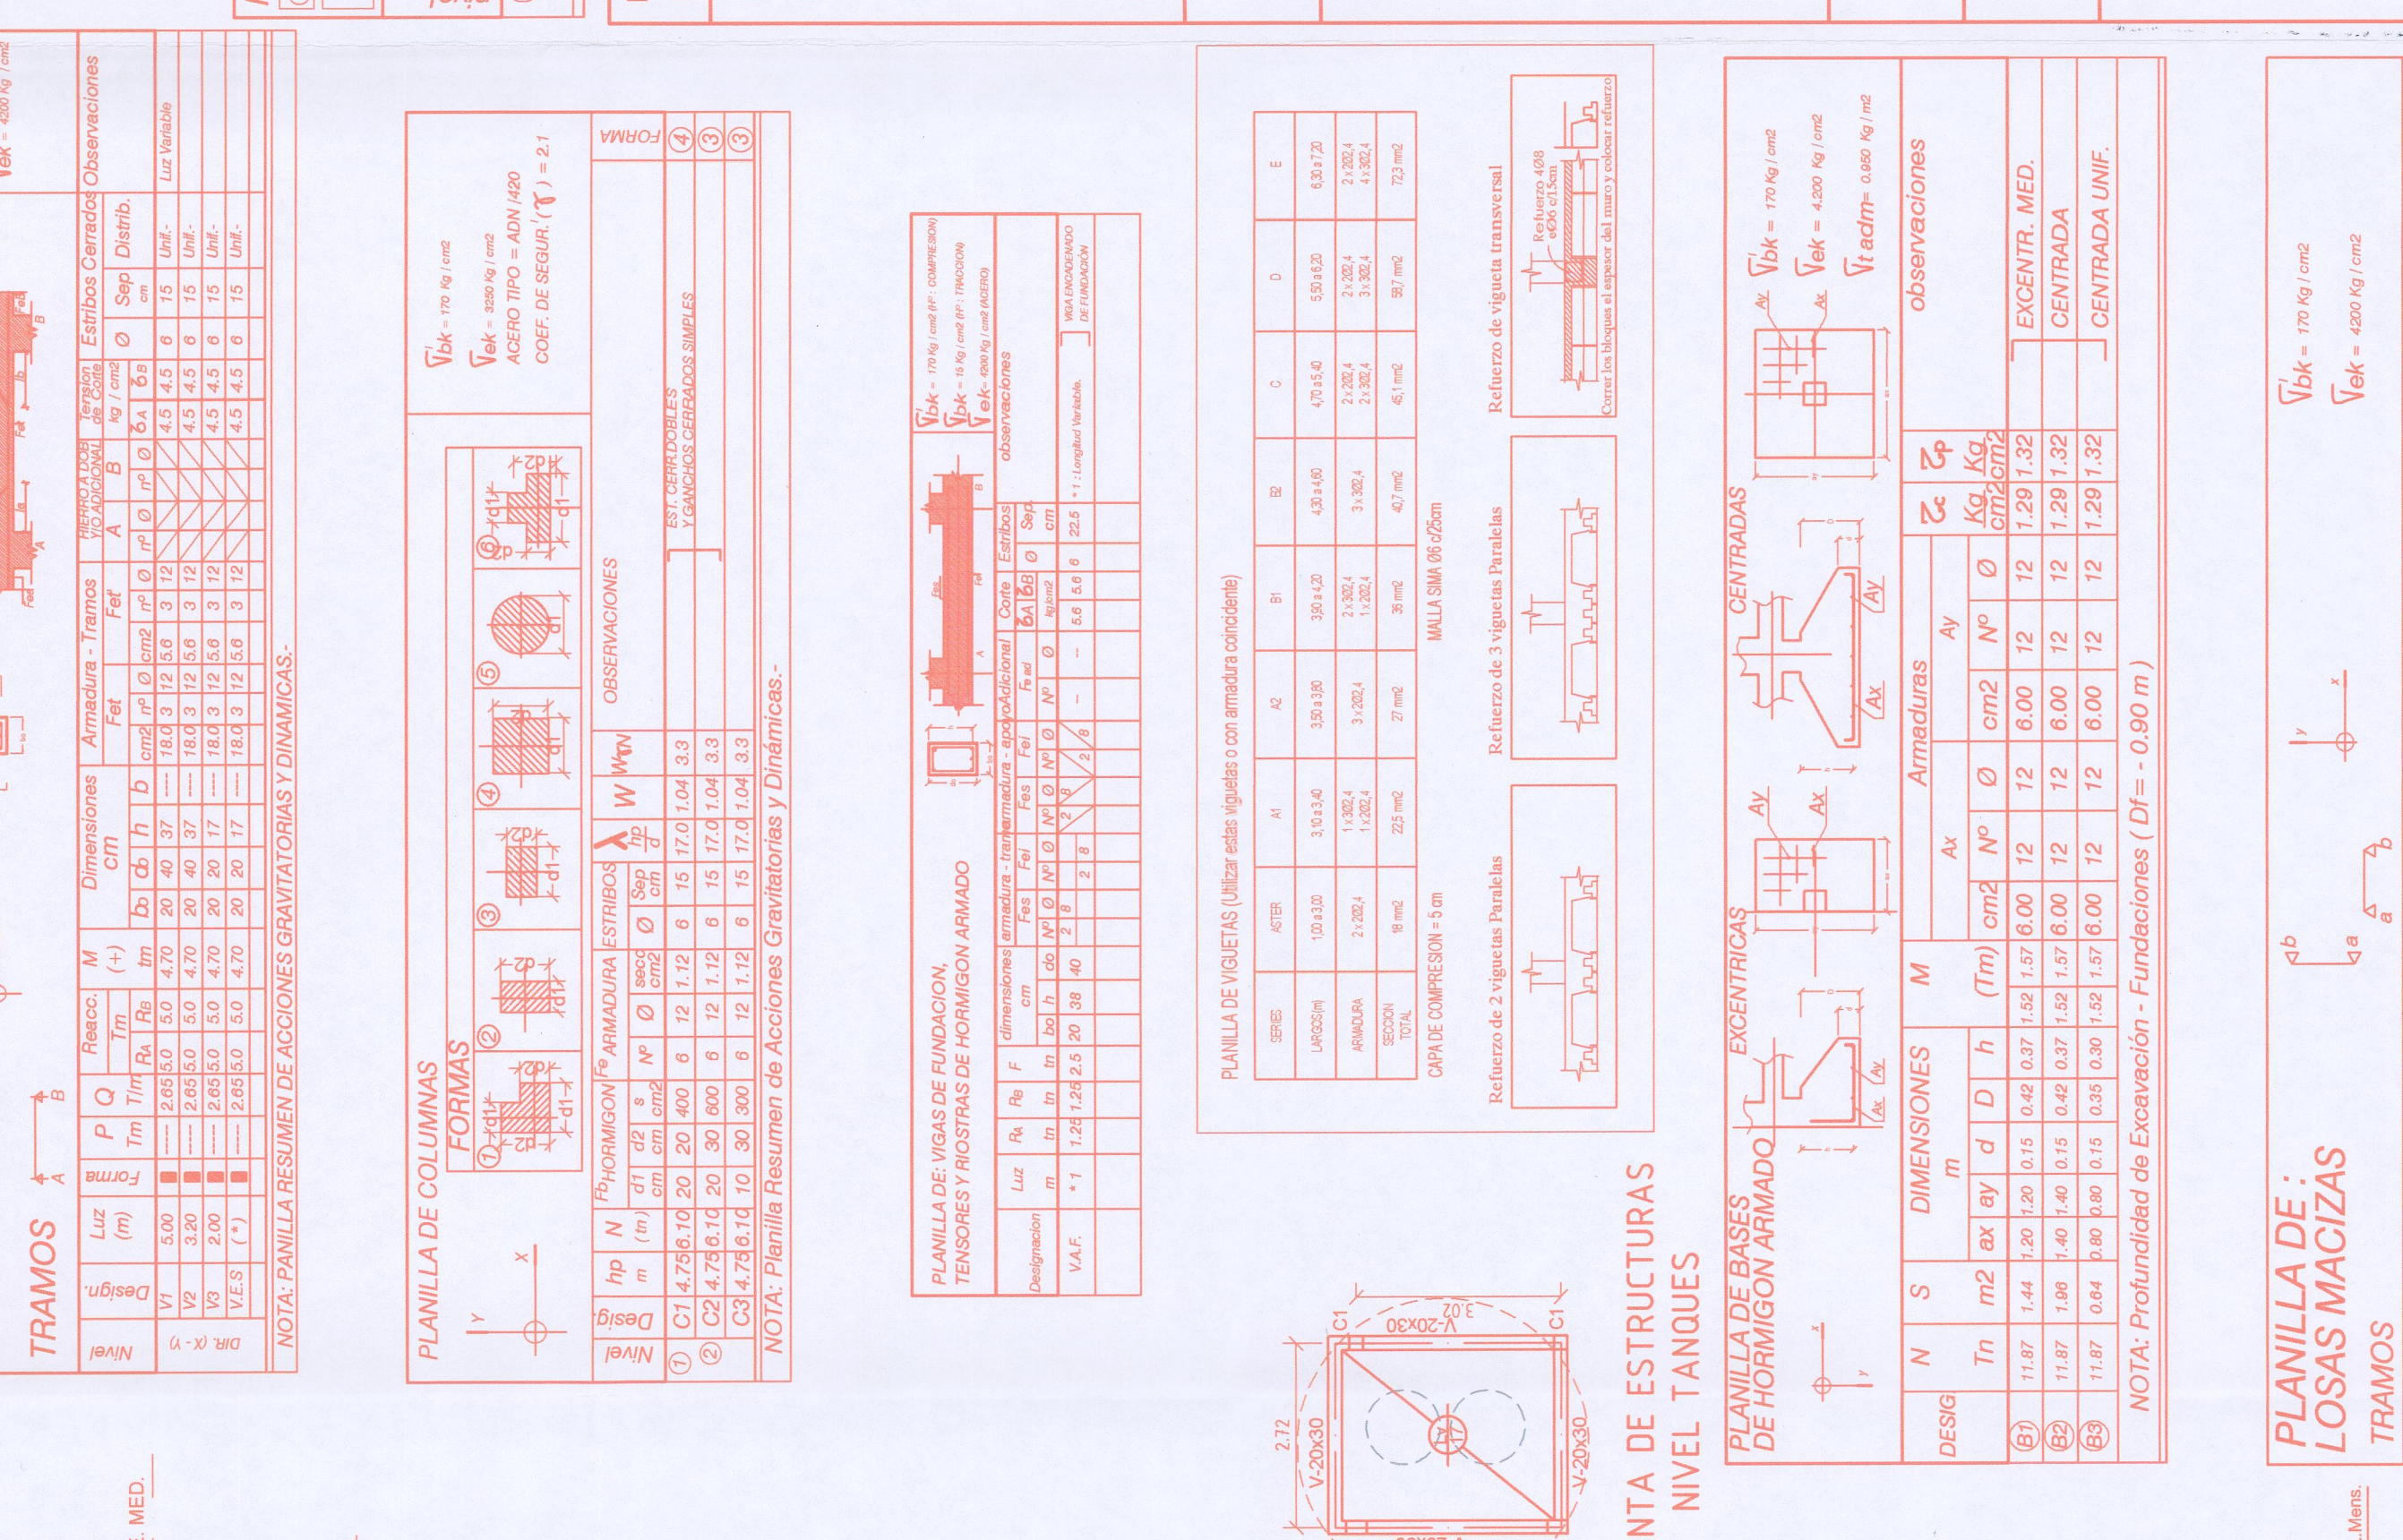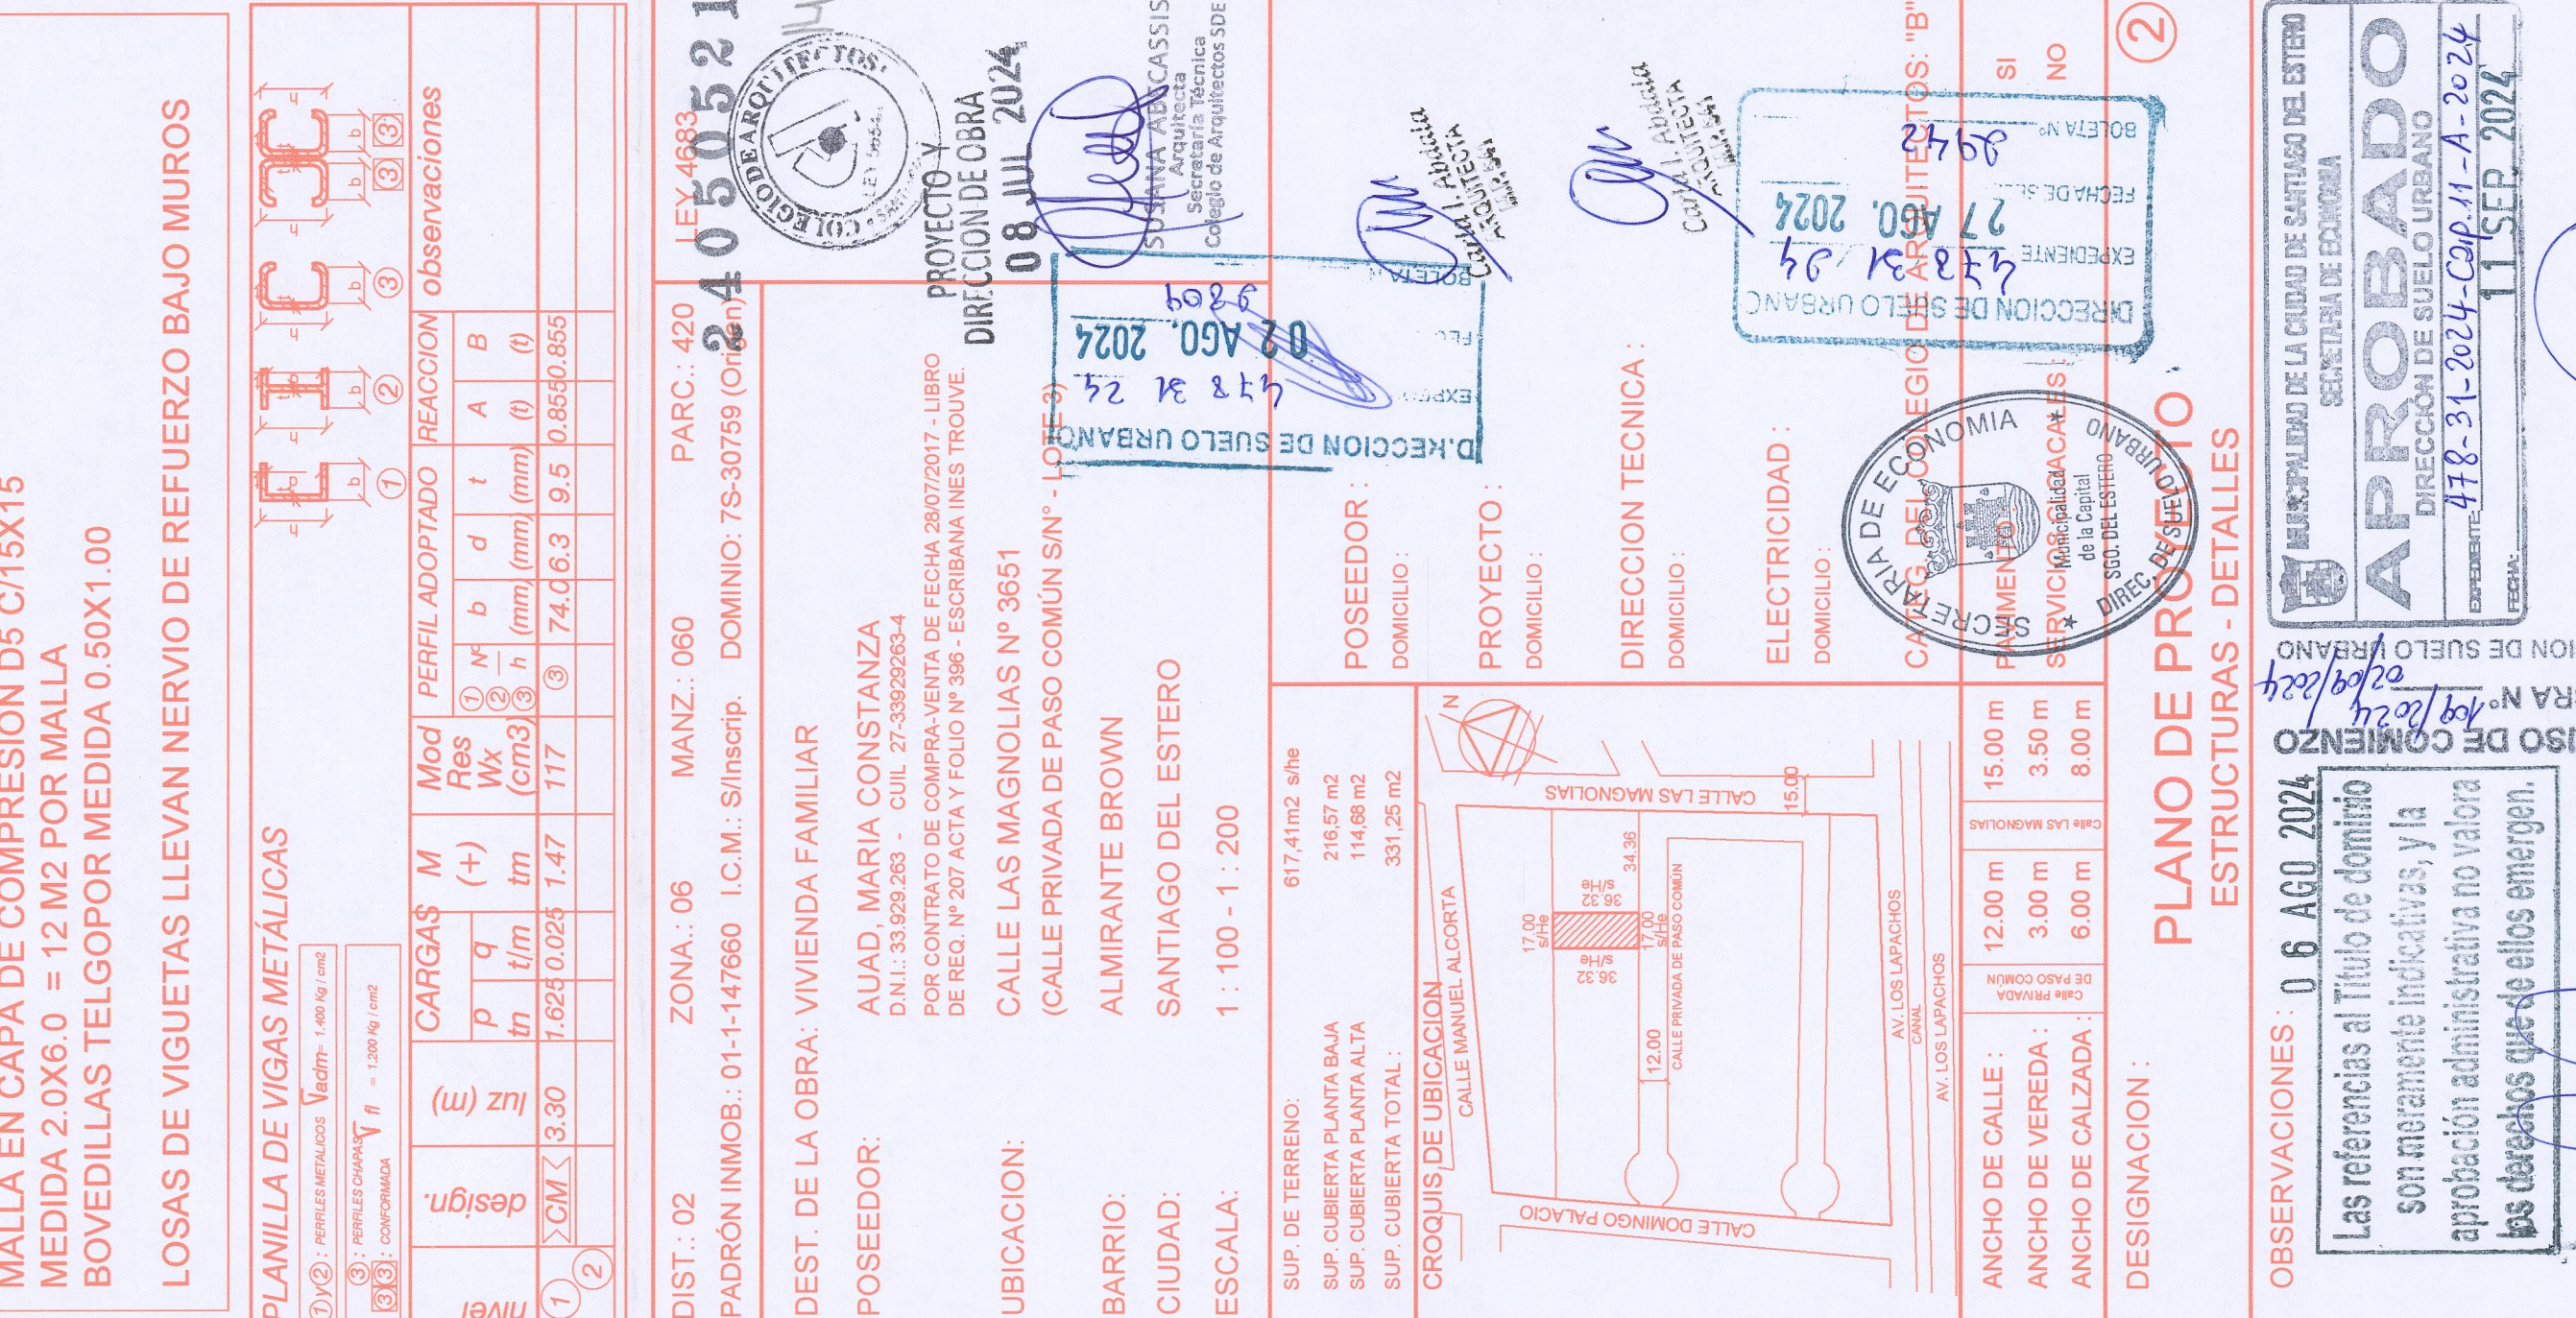[illegible]

Dr. MICHAIL BERNARDO KWANA
DIRECTOR
DIRECCION DE SANJO ORLANDO
REPUBLICA DE SAN JOSE



Dr. MICHAIL BERNARDO KWANA
DIRECTOR
DIRECCION DE SANJO ORLANDO
REPUBLICA DE SAN JOSE