

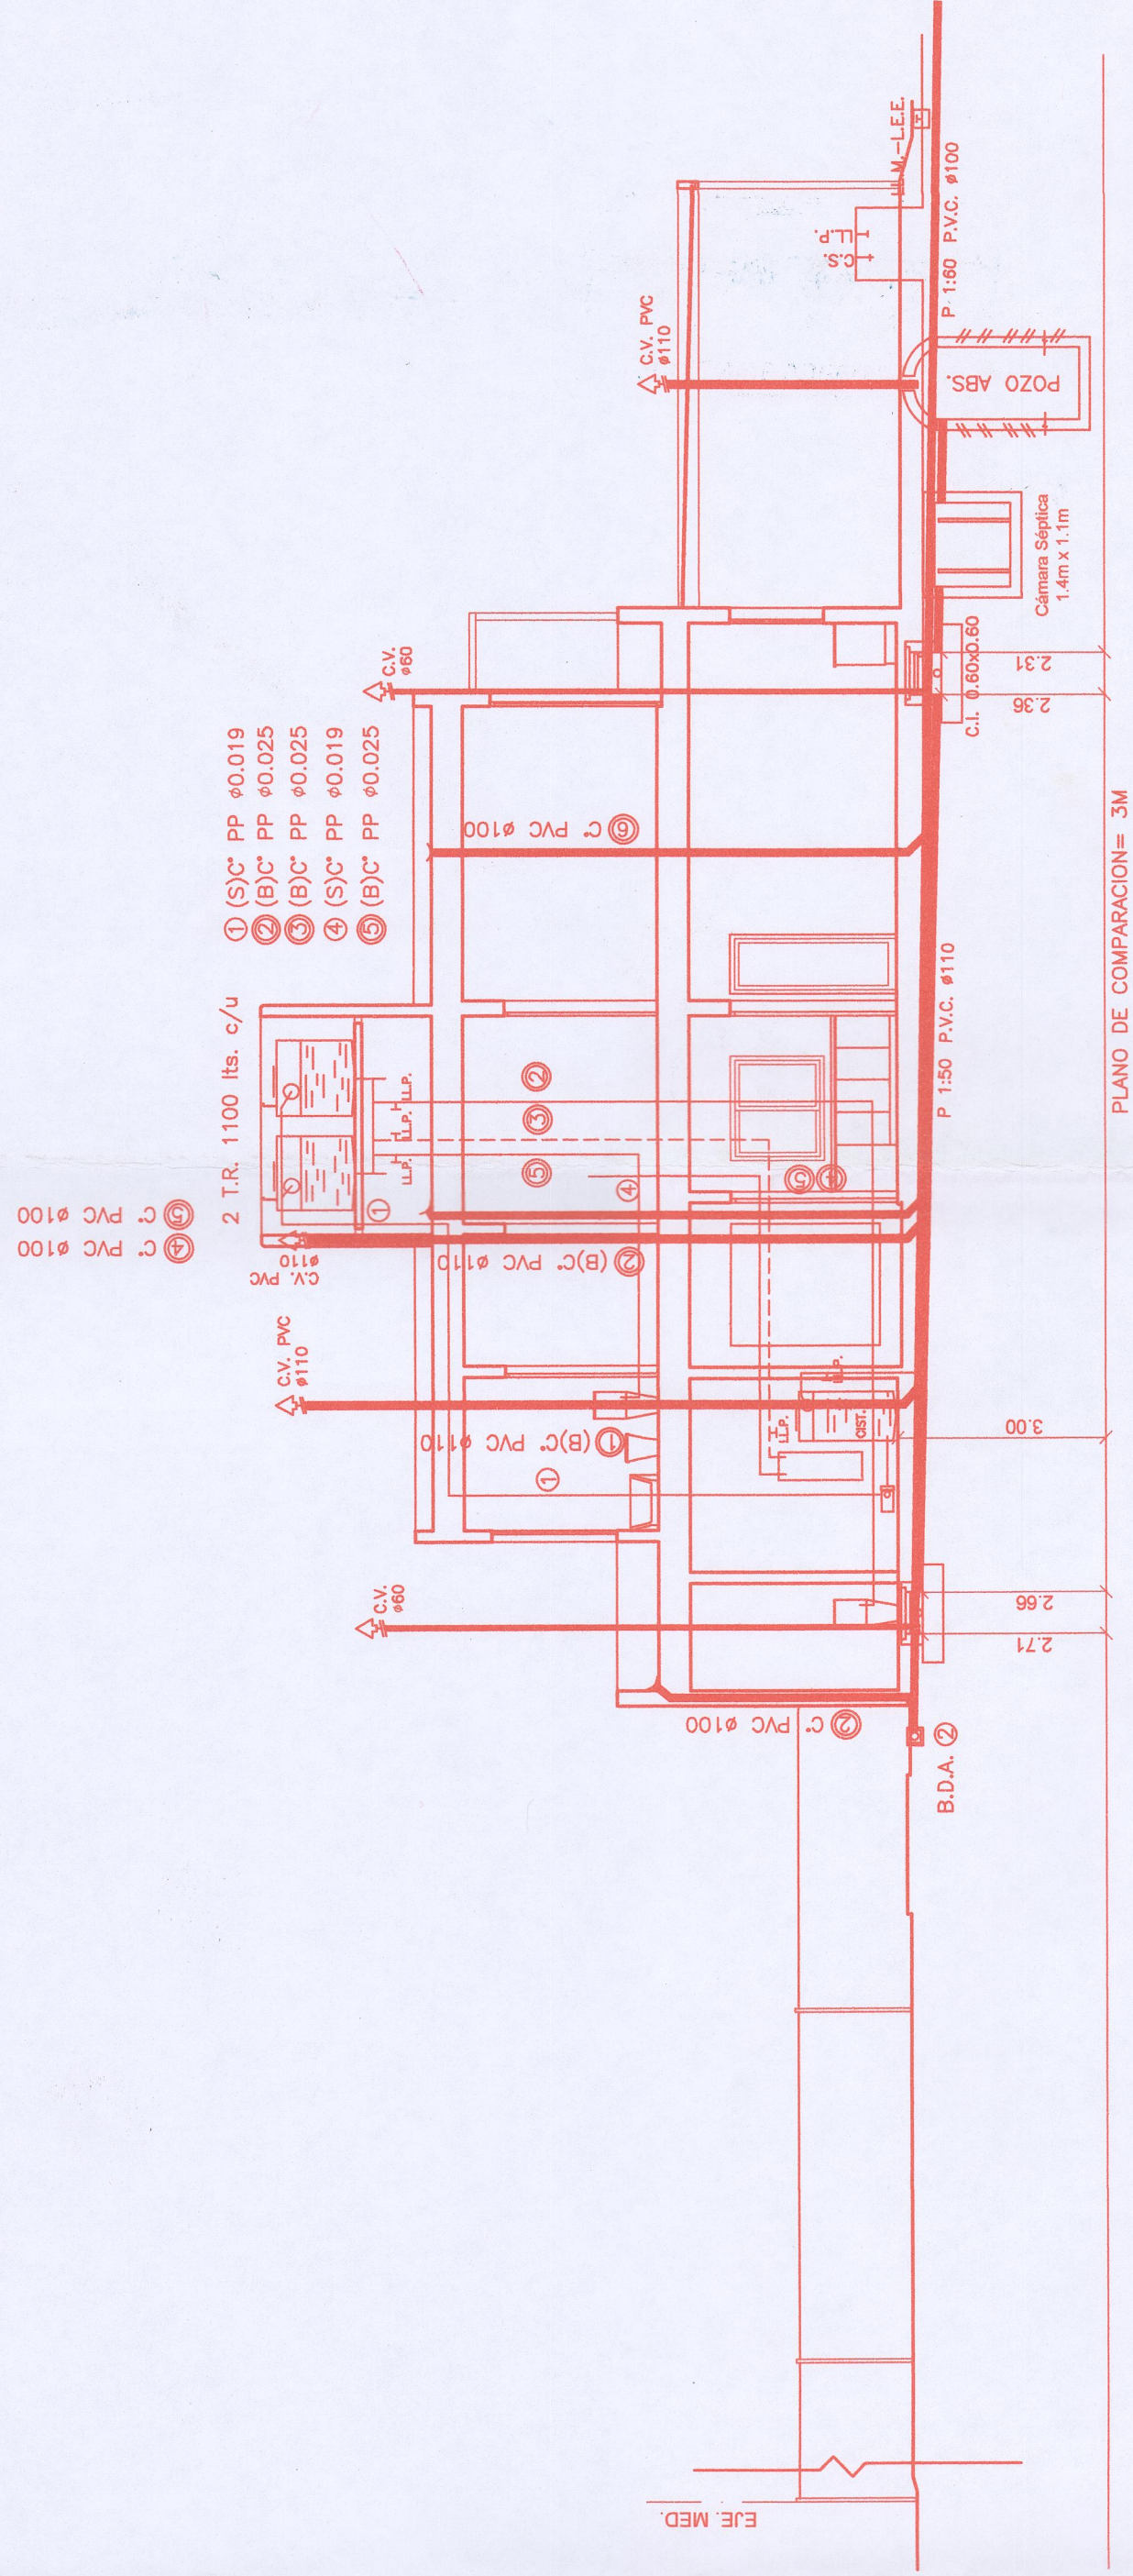


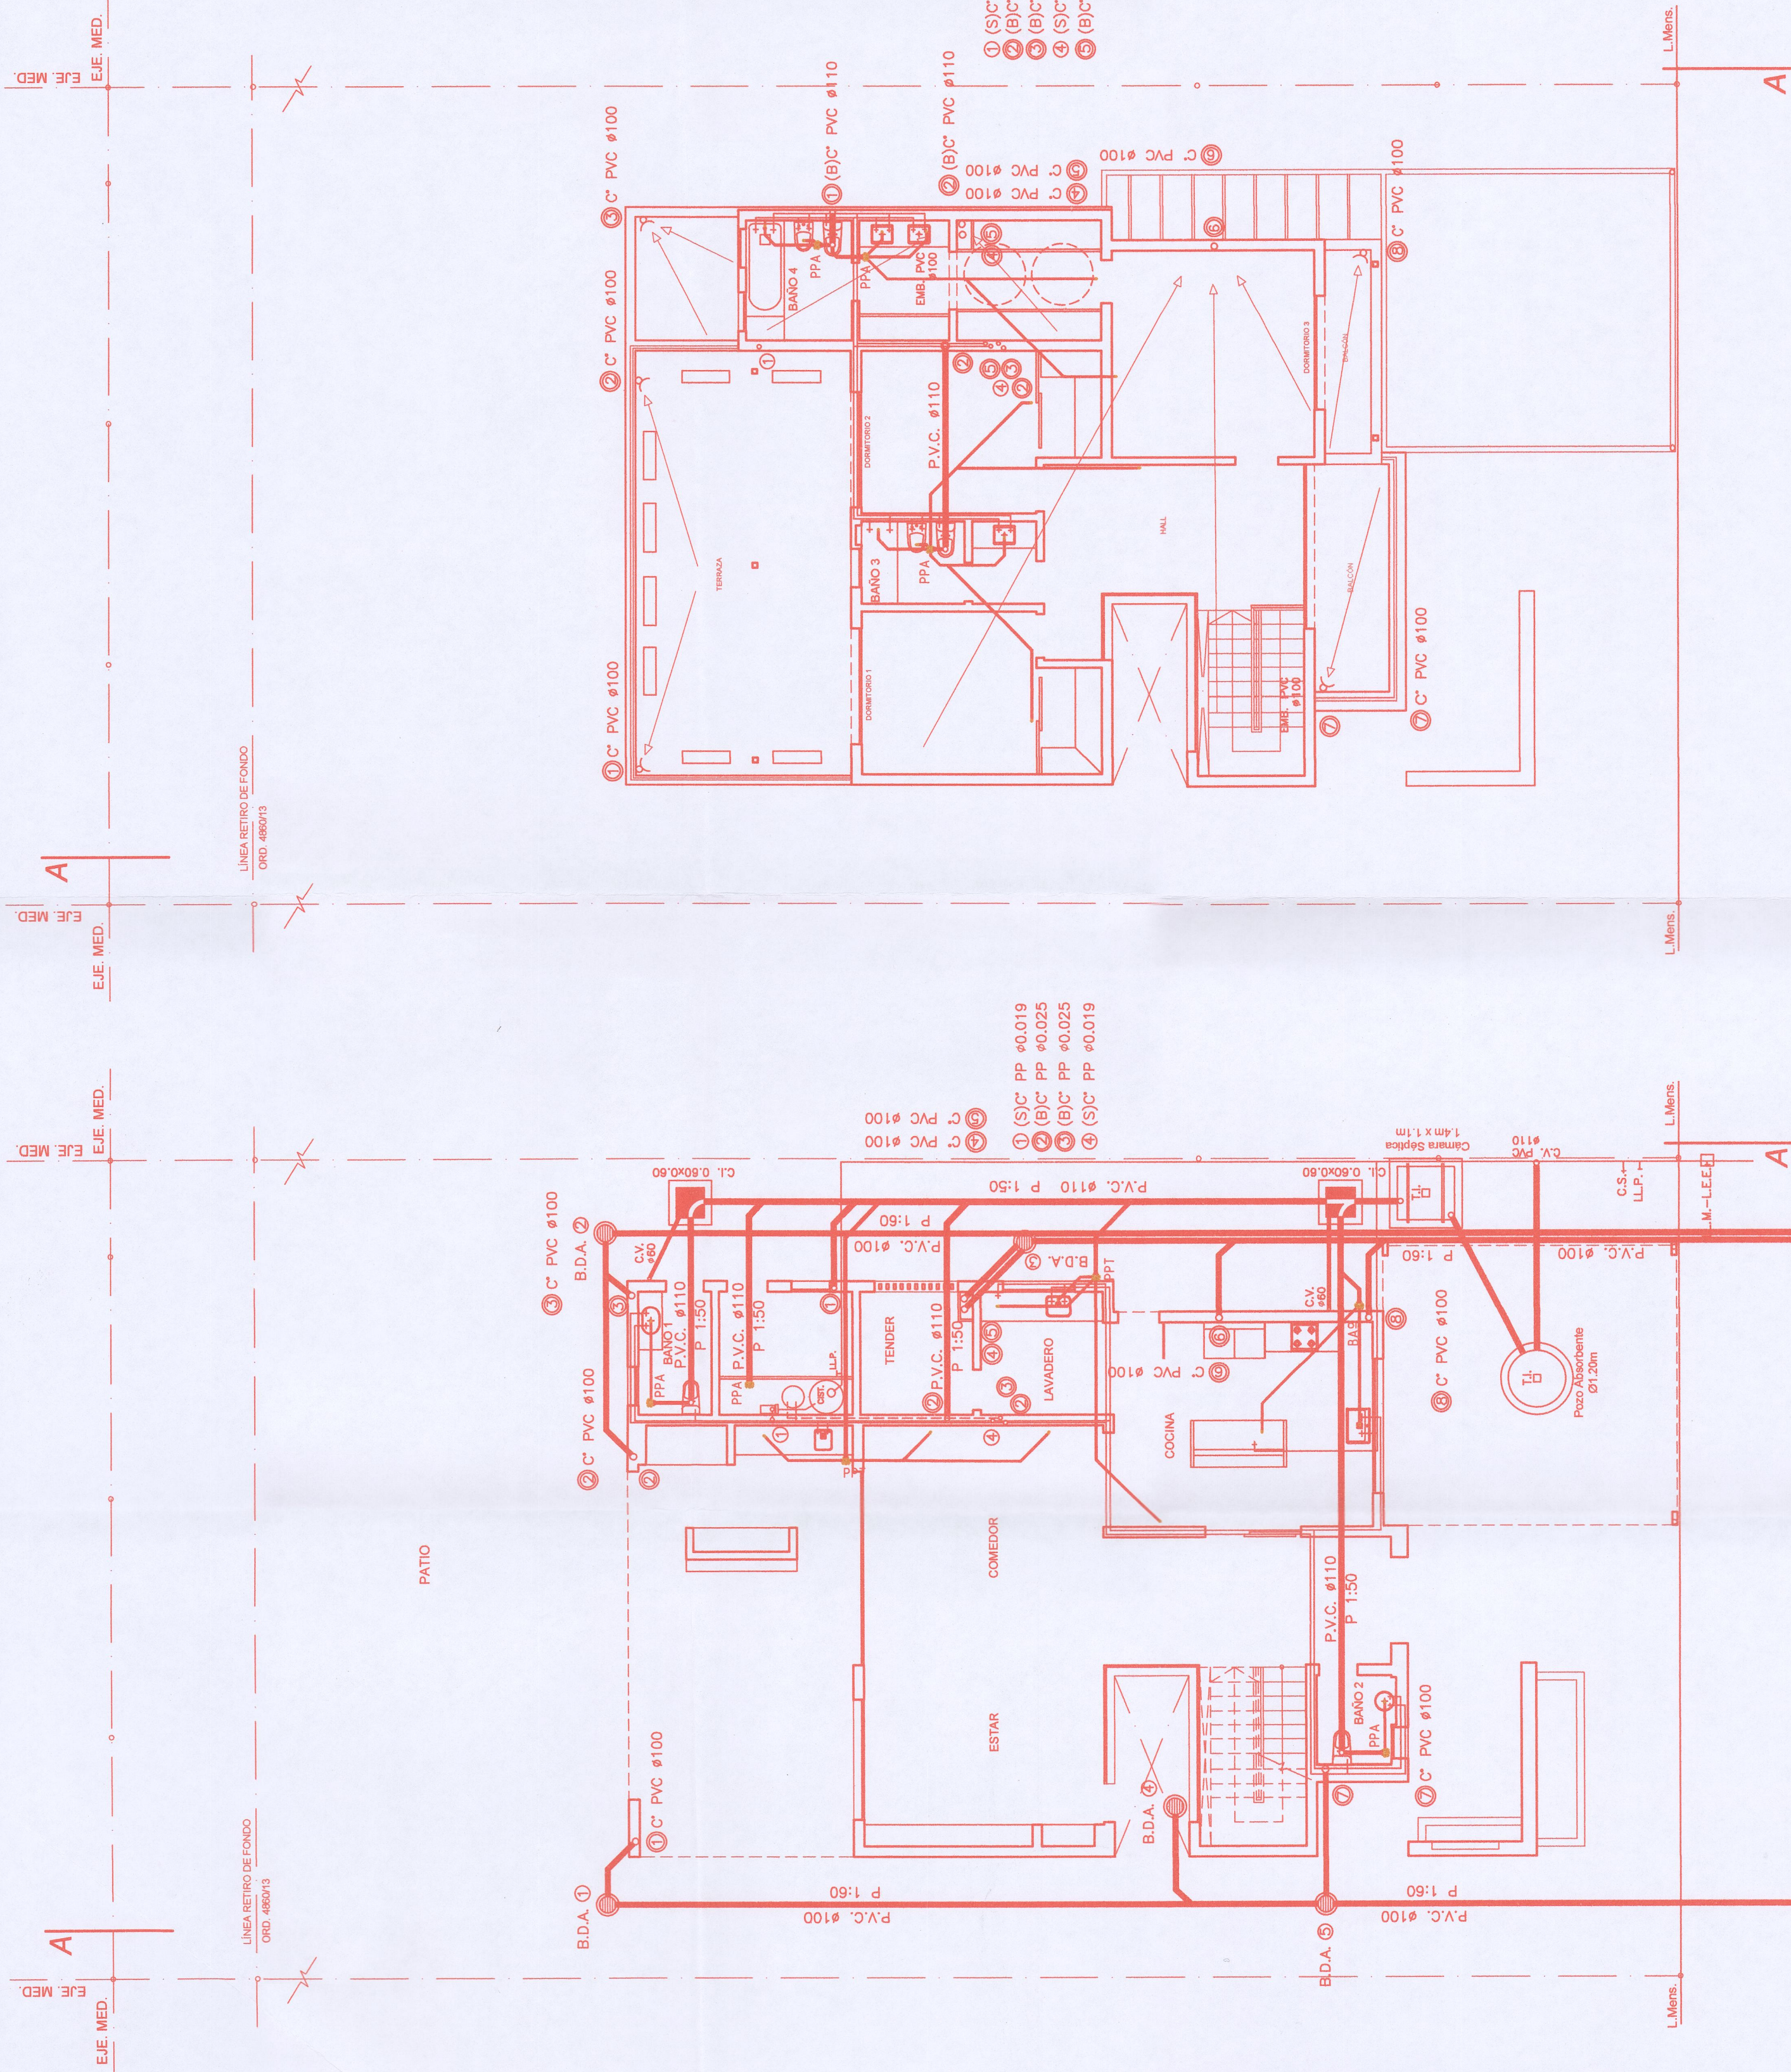


CORTE A-A

PLANTA DE TANQUES

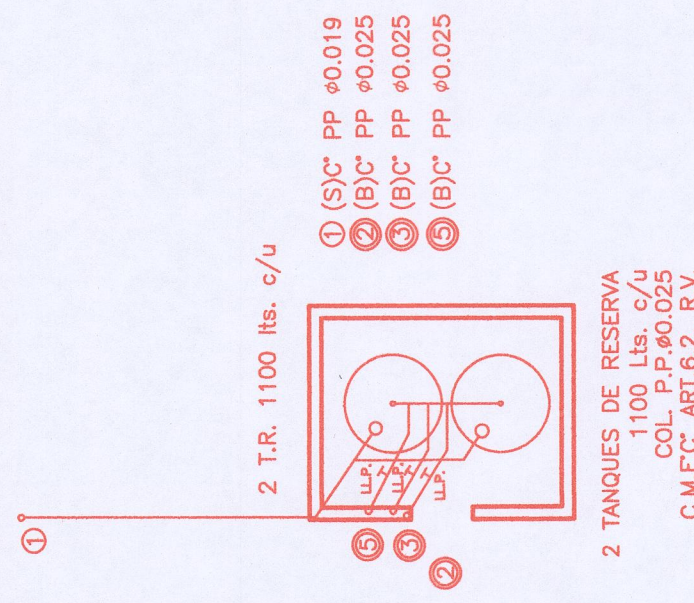

CUADRO DE RESUMEN										
DESIGNACION	CATEGORÍAS DE DESAGÜES PRIMARIAS				VENTILACION PLUVIALES					
	N°	MAT	N°	MAT	N°	MAT	N°	MAT	N°	MAT
TRAMO	1-3	PVC 110	1-5	PVC 100	1-3	PVC 110	1-3	PVC 110	---	---
HOR. COL.	5	PVC 110	6	PVC 100	---	---	---	---	---	---
COLUMNA	2	PVC 110	8	PVC 100	2	PVC 110	2	PVC 110	---	---
P.P.	7	PVC 0.63	ARTIFACTOS Y ACCESORIOS							
I.P.	4	PVC 110	Baflo 1 1"PDAL 1 2C.S.							
B. ACCESO	Baflo 3 3 1/2" L.P.		Baflo 3 3 1/2" L.P.							
	1	PVC 110	Baflo 4 1"PDAL 1 4C.S. BT. DUCH. 3 1/2" L.P.							
C. ACCESO	---	---	Luv 1 2C.S.							
P.C.										3C.S. SIF. C #60

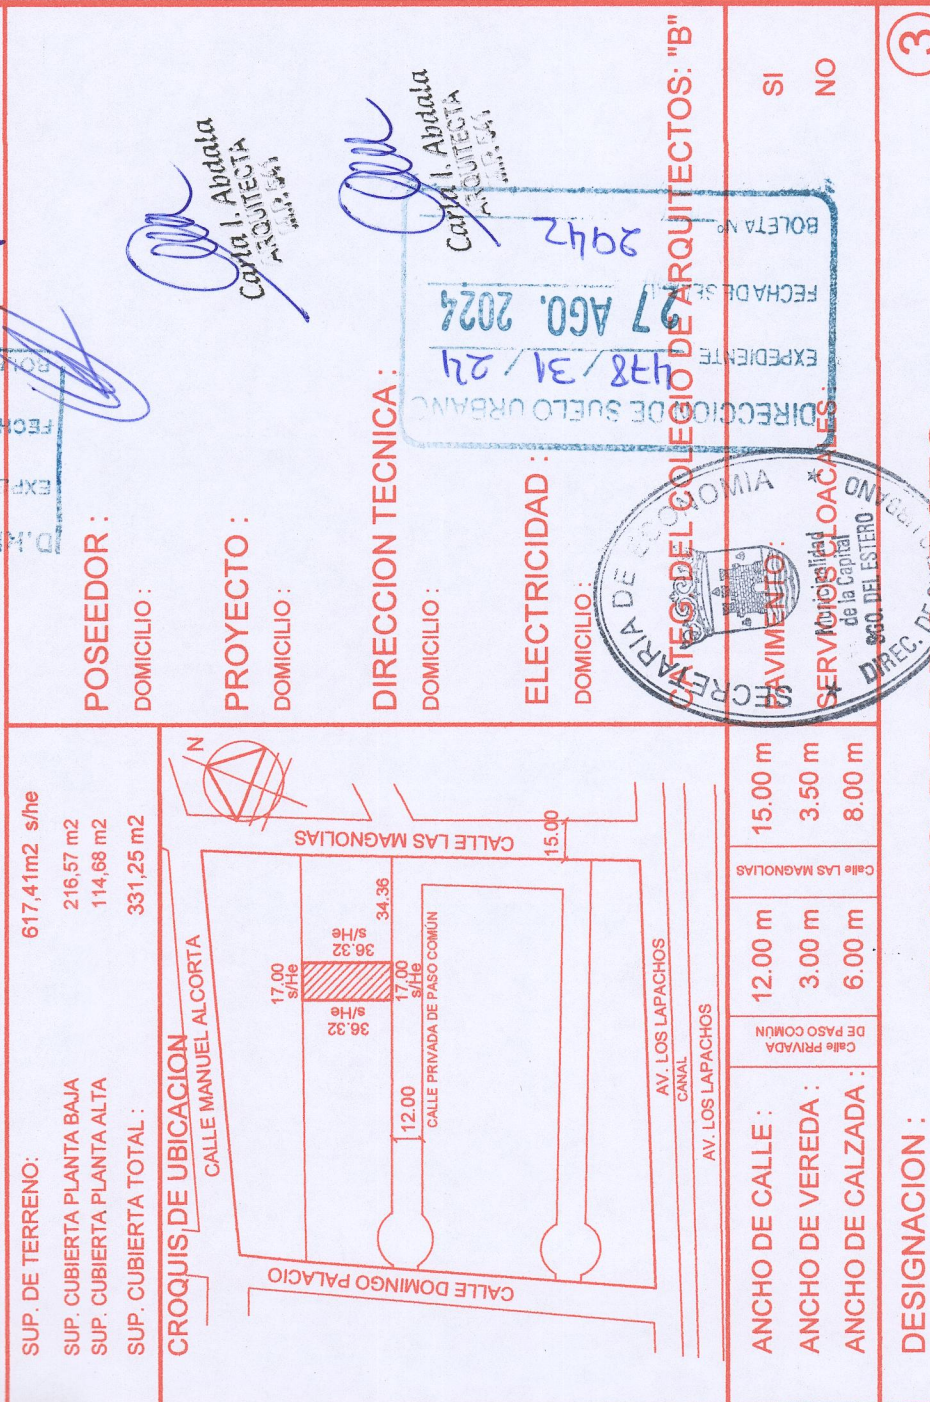

DESIGNACION : **PLANO DE PROYECTO
INSTALACIÓN SANITARIA**

OBSERVACIONES: 06 AGO 2024

Las referencias al título de dominio son meramente indicativas, y la aprobación administrativa no va a ser

Arq. **BERNARDO L. M. SANTILLAN**
DIRECTOR
DIRECCION DE SUELO URBANO
MUNICIPALIDAD DE SGO. DEL ESTERO

Ing. Agdm. J. LEANDRO ARJONA
JEFE DE AREA DE VISACIONES TECNICAS
DIRECCION DE CATASTRO MUNICIPAL