

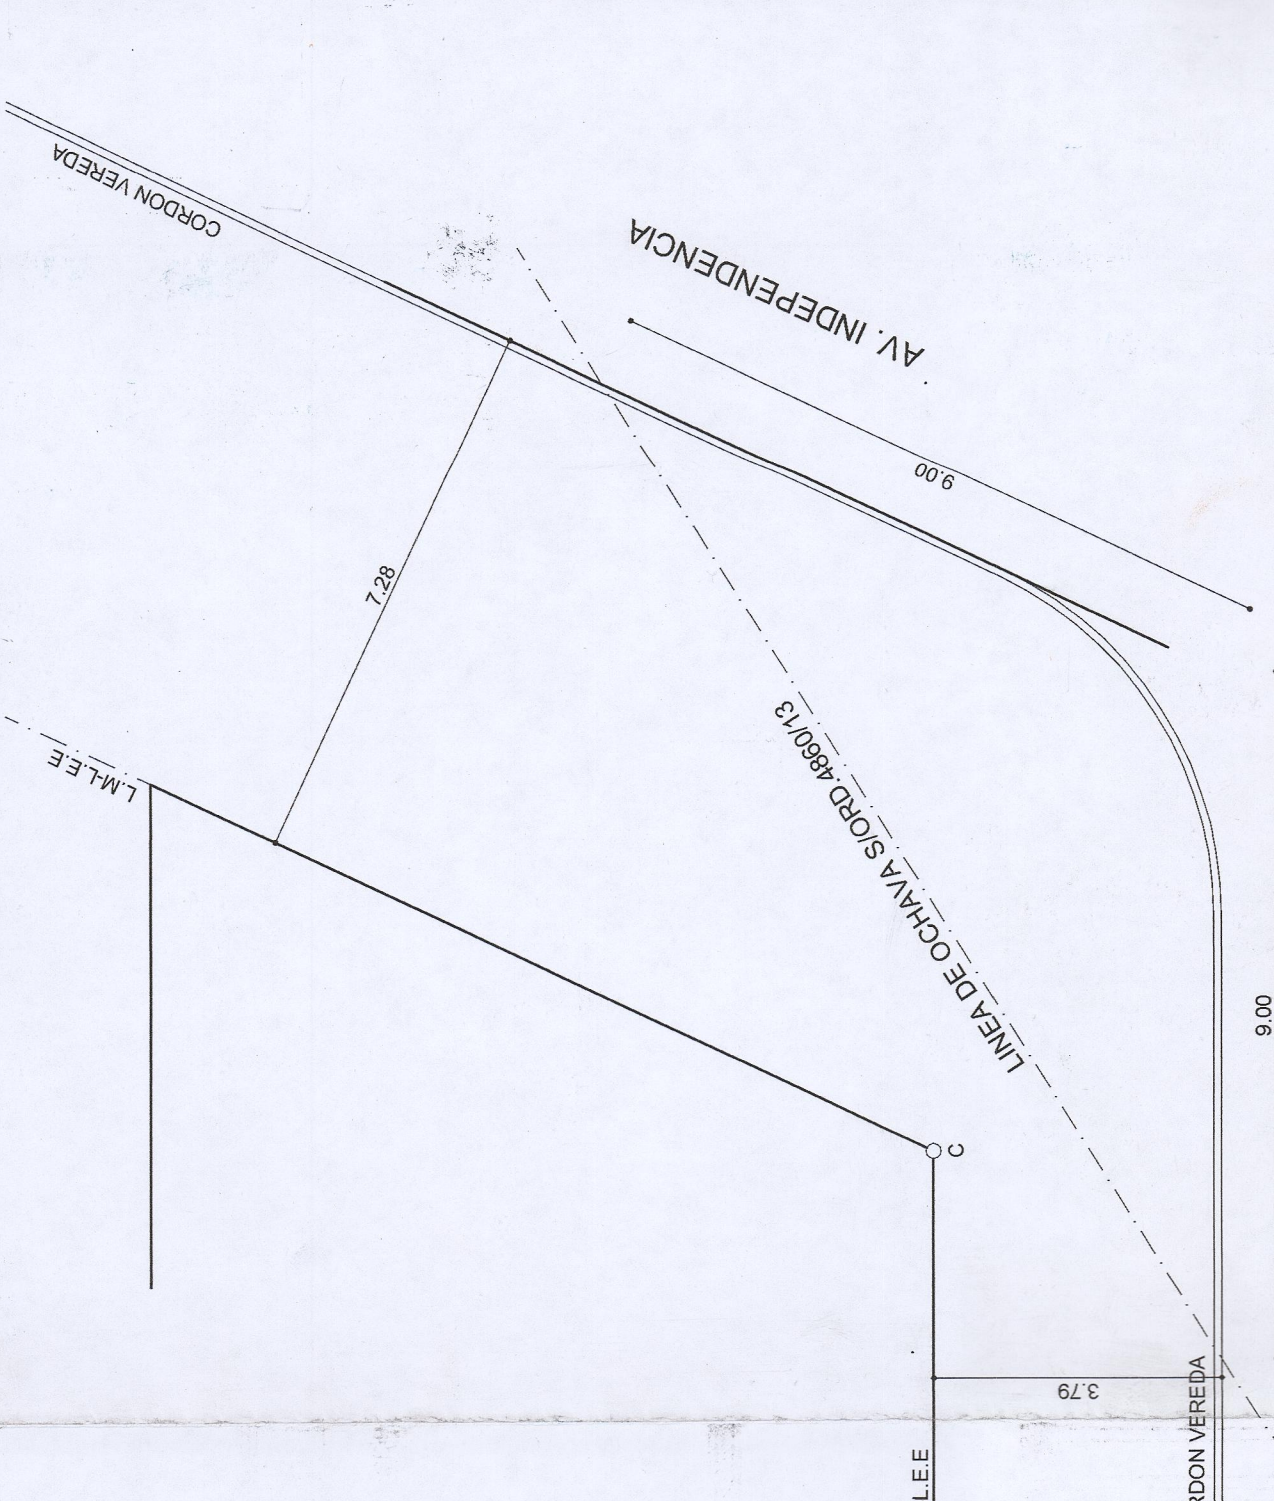
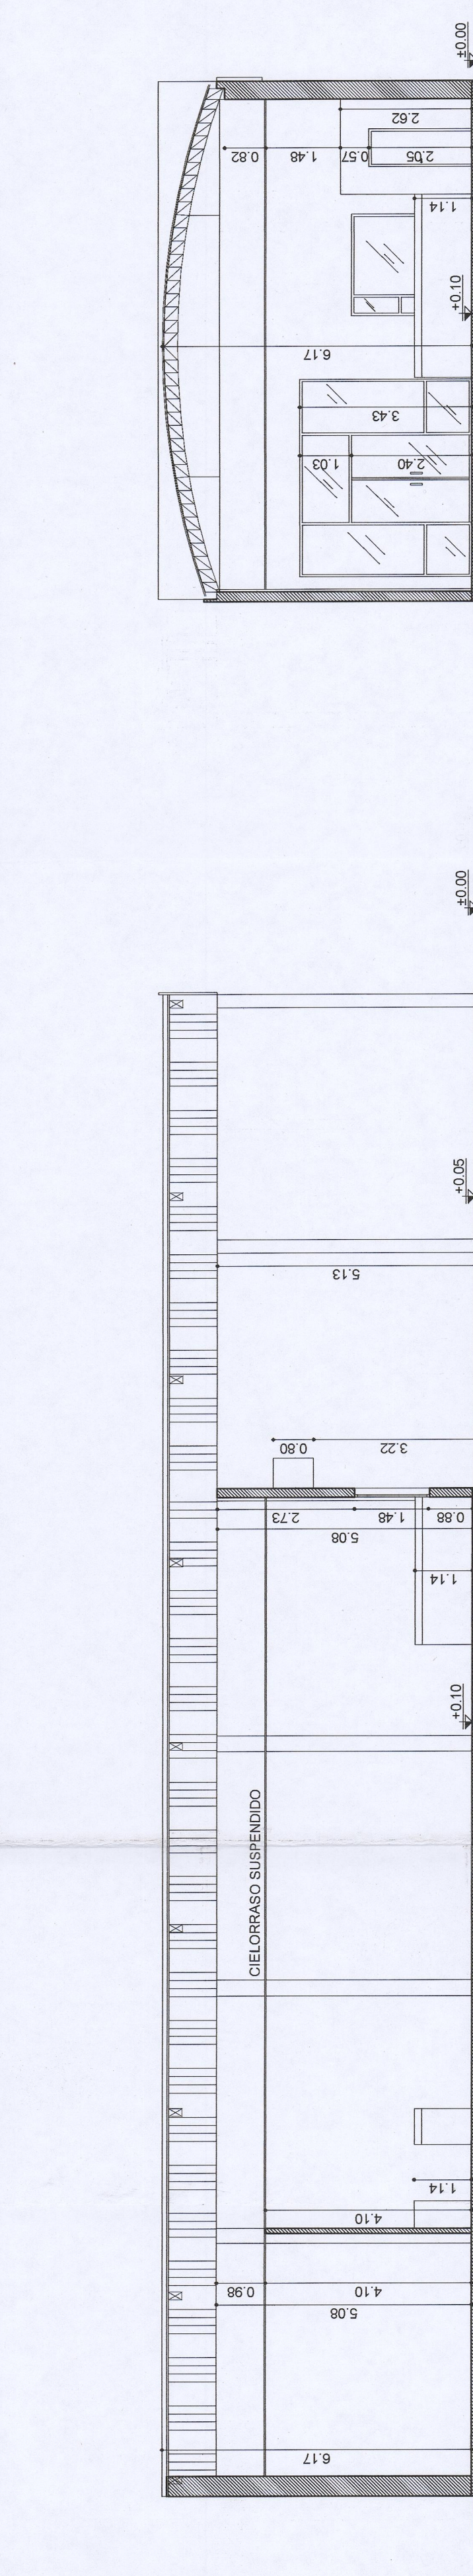
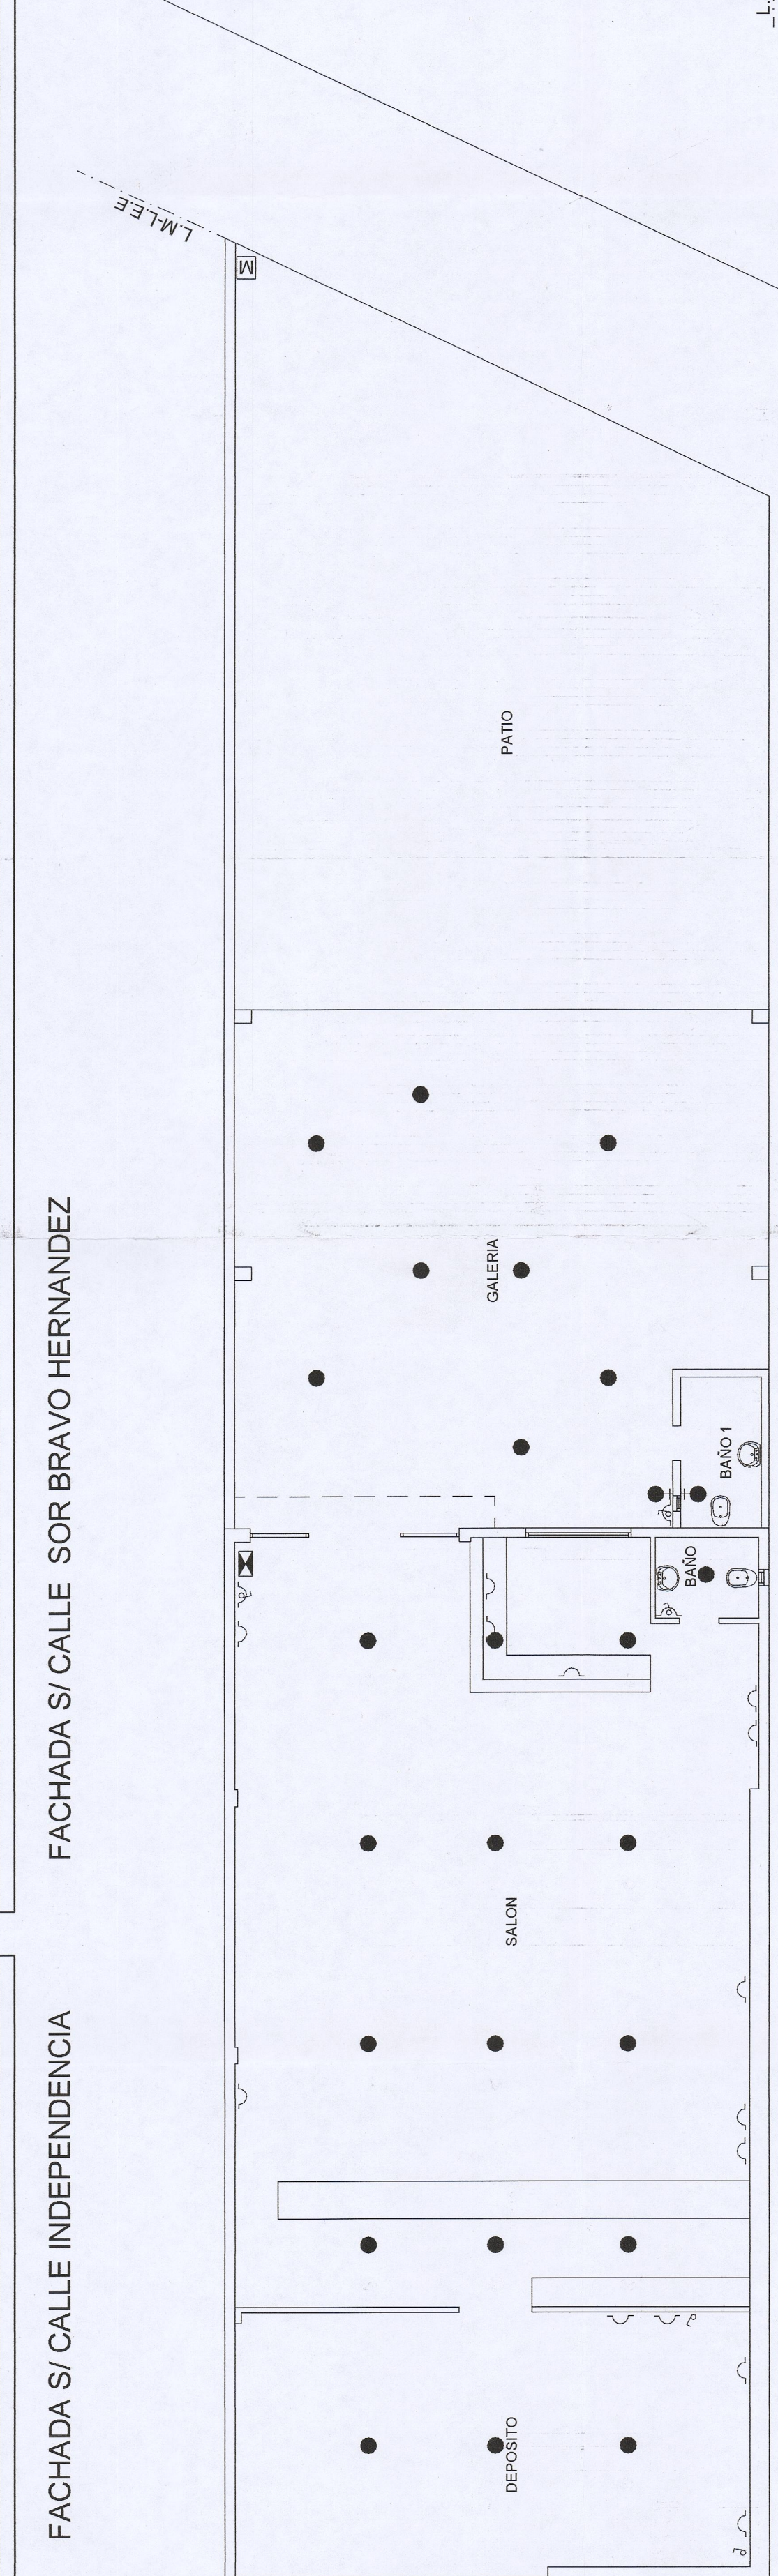


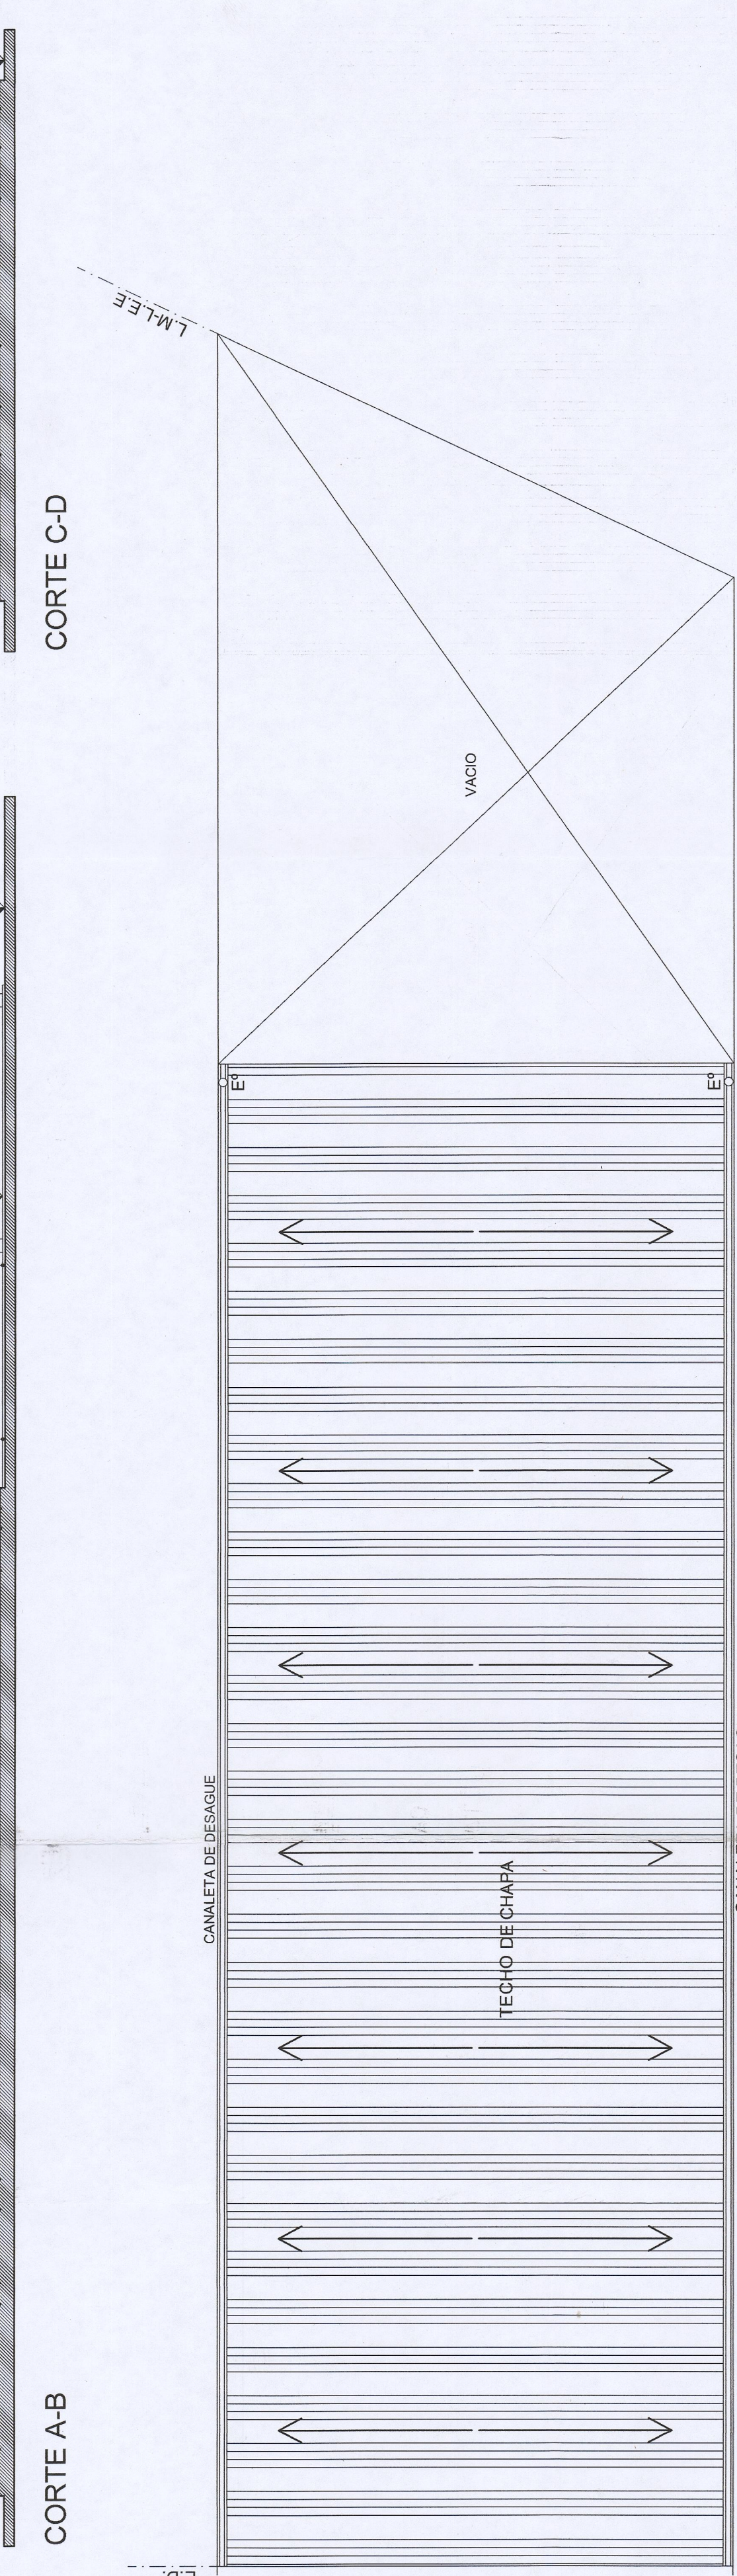

CALLE SOR BRAVO HERNANDEZ

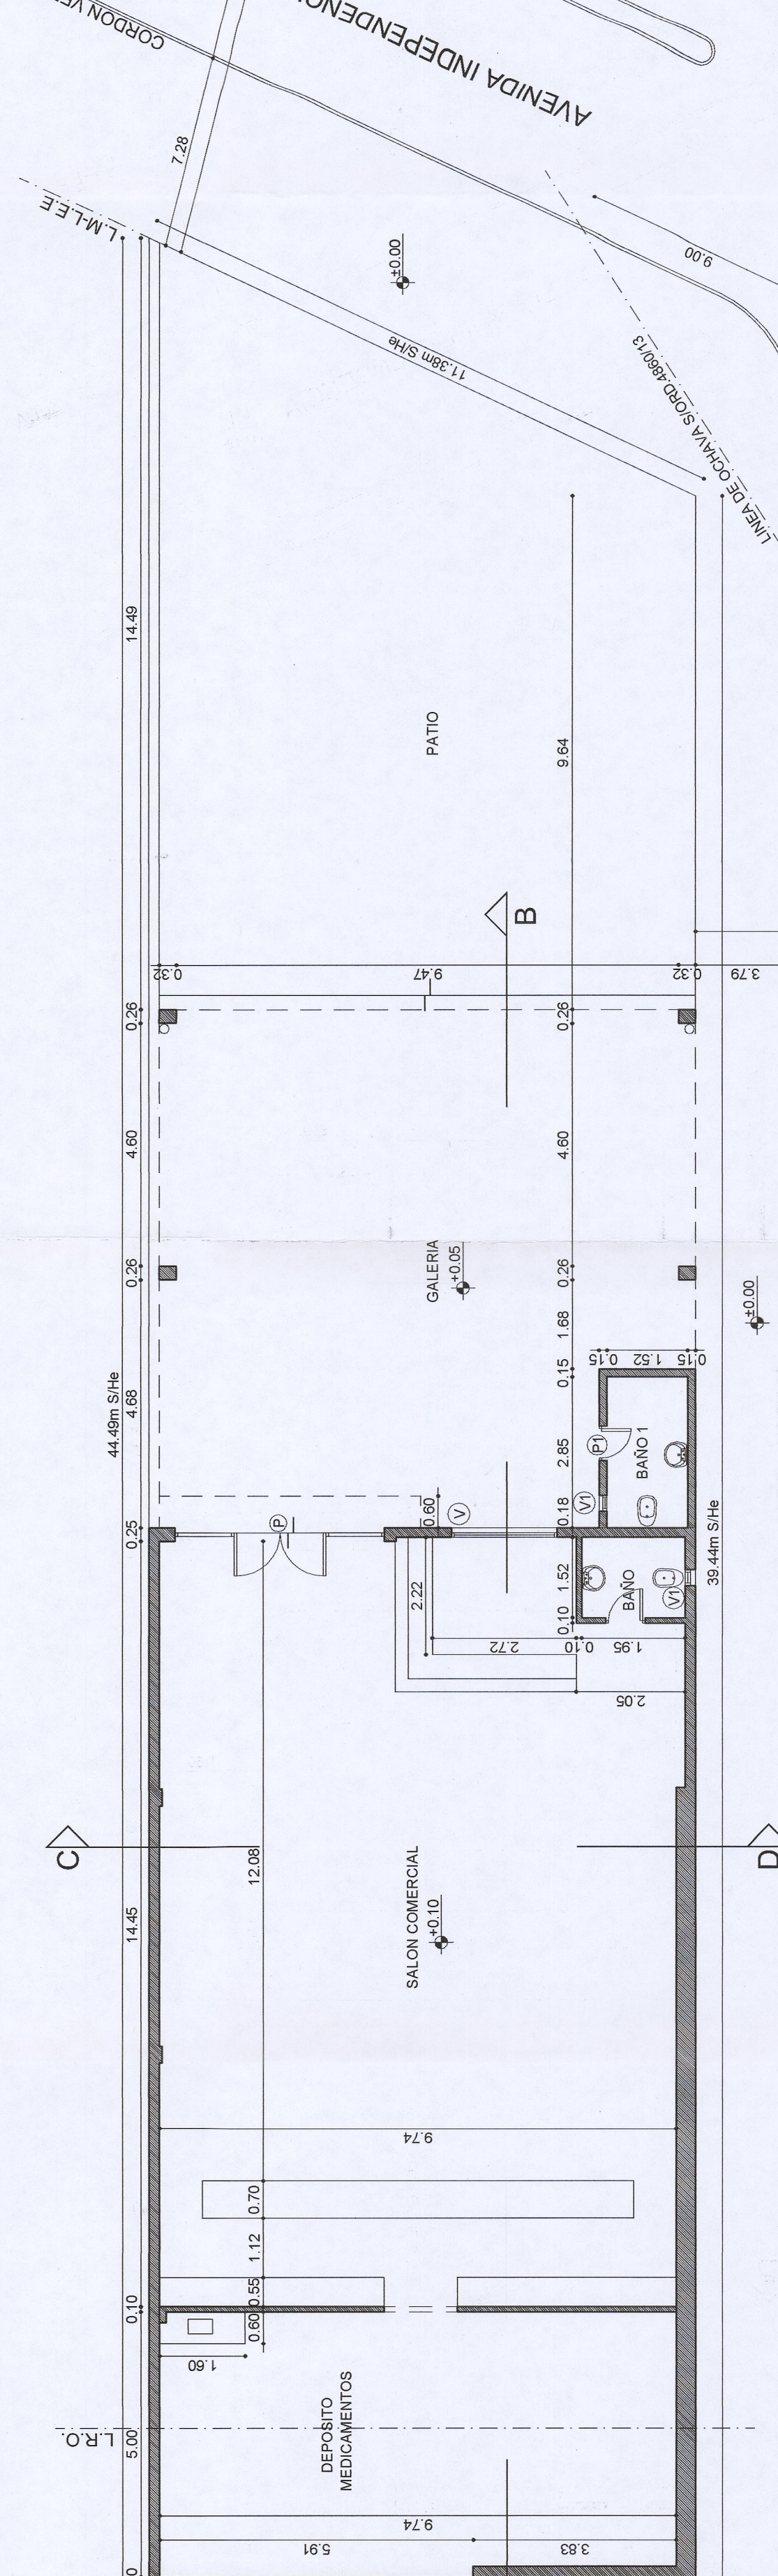


PIANTA DE TECHO

PLANTA DE ELECTRICIDAD

PLANTA

PLANILLA DE ILUMINACION Y VENTILACION

O.C.A.L.E.S	DESIGNACION	SUPERF.	ABERTURAS				OBSERVACIONES	
			TIPO	ANCHO	ALTO	AREA LUMIN. VENTIL.		
	SALON COMERCIAL	138.42	P	3.95	3.40	13.43	13.43	Planta Viduola
			V	2.00	1.50	3.00	3.00	Ventana
	DEPOSITO MEDICAM.	47.01	—	—	—	—	—	Slt y V.
	SALON	2.86	V1	0.30	0.20	0.06	0.06	Ventiluz
	SALON 1	4.53	V1	0.30	0.20	0.06	0.06	Ventiluz
			P1	0.66	2.06	—	1.33	Planta

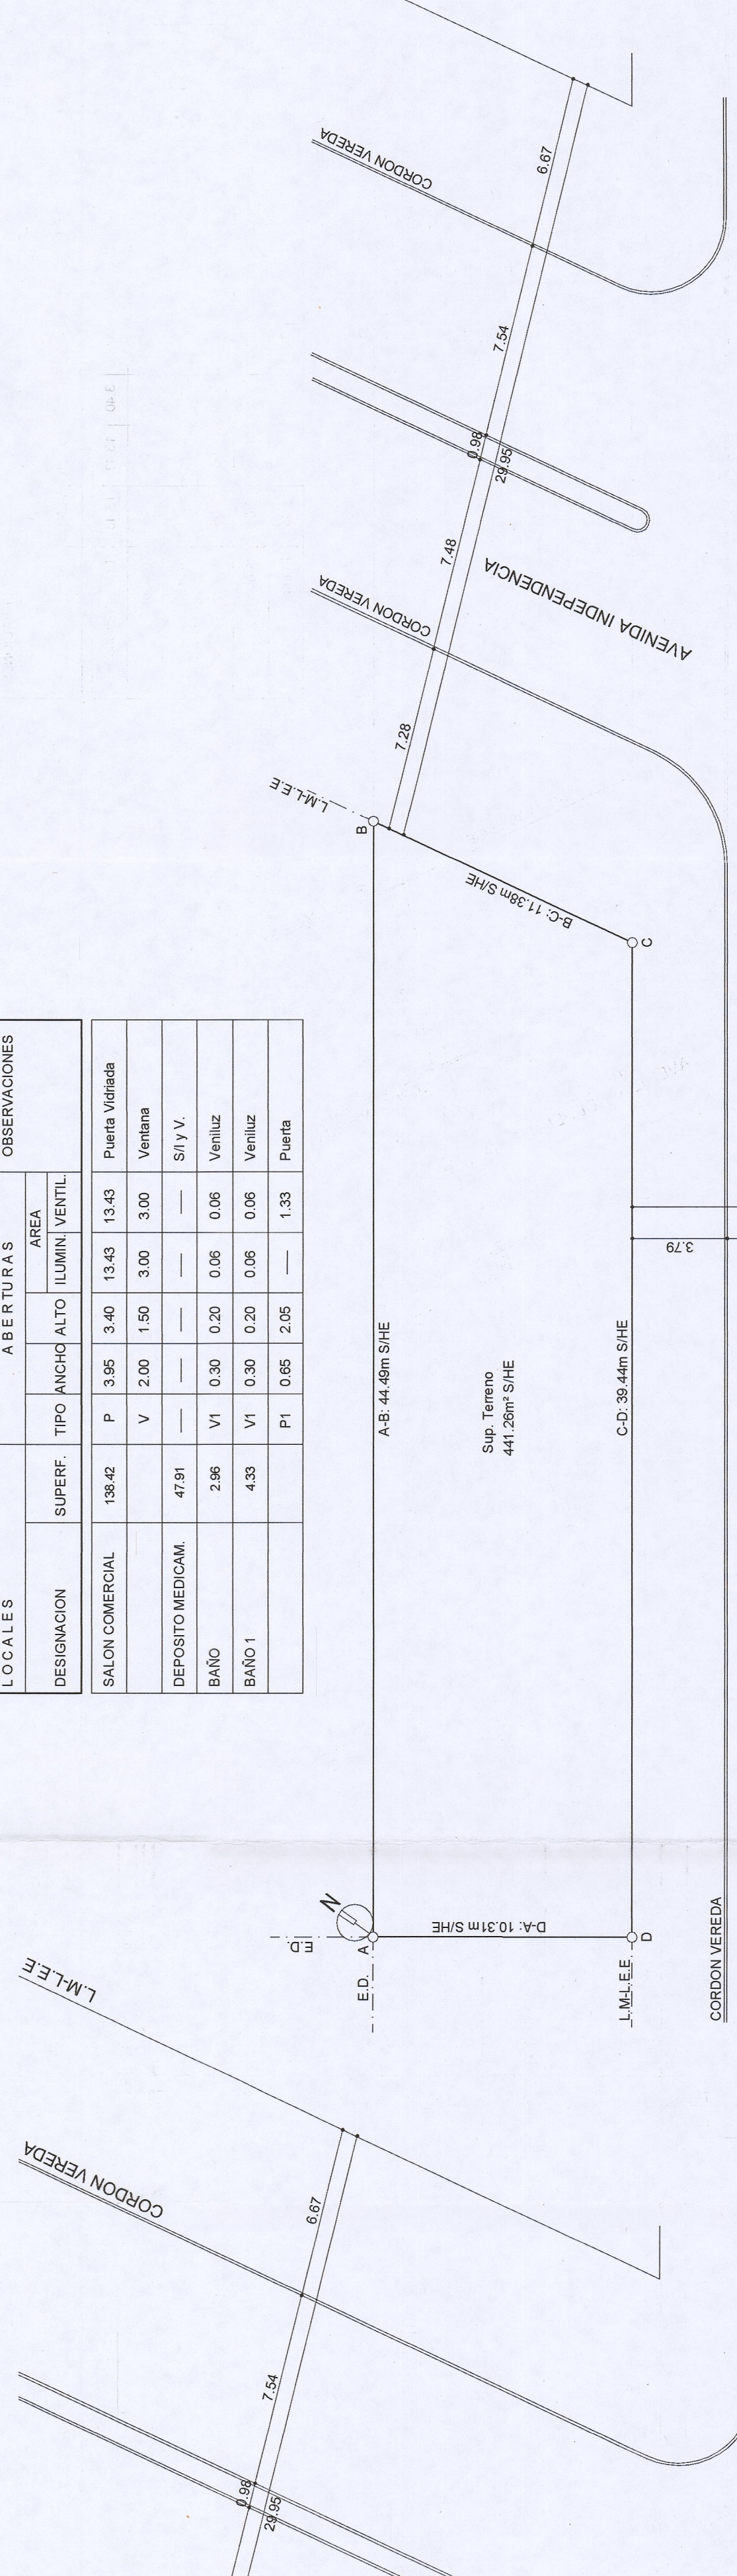

ANIMETRIA -ESC. 1:200

DISTRITO 6	ZONA 1	MANZ. 74	PARC. 322323	Señalo
PADRON INMOBILIARIO N° 010P004971		I.C.M. S/I	DOMINIO: -----	
DESTINO DE LA OBRA: LOCAL COMERCIAL NOTA: CESION DE DERECHOS A FAVOR DE LA GRAMA ESCRITURA 904 ESTE ZONERO ASOCIADO EN EL SANTIAGO DEL ESTERO 9/10/2019. POSEEDOR : JUAN BAUTISTA PAZ DE LA GRAMA DNI N°16.308.705 -CUIT N°20-16308705-8 UBICACION : CALLE SUR BRAVO HERNANDEZ esq. AV. INDEPENDENCIA N° 3895 BARRIO: ALMIRANTE BROWN CIUDAD: SANTIAAGO DEL ESTERO ESCALA: 1:100- 1:200				

SUP. DE TERRENO	SHE441.28m ²	POSEEDOR:	YURI DOR
SUP. CUBIERTA	257.78m ²	DOMICILIO:	JUAN BOBISTA POR DE LA CARRA.
SUP. TOTAL	515.70m ²		

CRONOGRAMA DE UBICACION:

RELEVAMIENTO:
Domicilio:
ROSA VALENTIN FABRICO
Maestro Mayor de Obras
Máximo Mayor de Obras

10.31.11.11
4.3.31.11.11
10.31.11.11
2.9.96

[illegible]

INDIPENDENCIA	SOR BRAVO HERNANDEZ	1427m.	PANIN	28	RECIBO DE PAGO
ANCHO DE CALLE:	23.85m.	3.78m.			
ANCHO DE VEREDA:	7.28m.	6.55m.			
ANCHO DE CALZADA:	7.48m.		SERVICIOS CLOACALES:		

PLANO DE RELEVAMIENTO

Las referencias al Título de dominio
U. R. 244-246
son meramente informativas y la
aprobación administrativa no valora
los derechos que de ellos emergen.


 José María Rodríguez
 Vicedirector General
 Dirección de Asesoría Jurídica
 Ministerio de Asesoría Jurídica