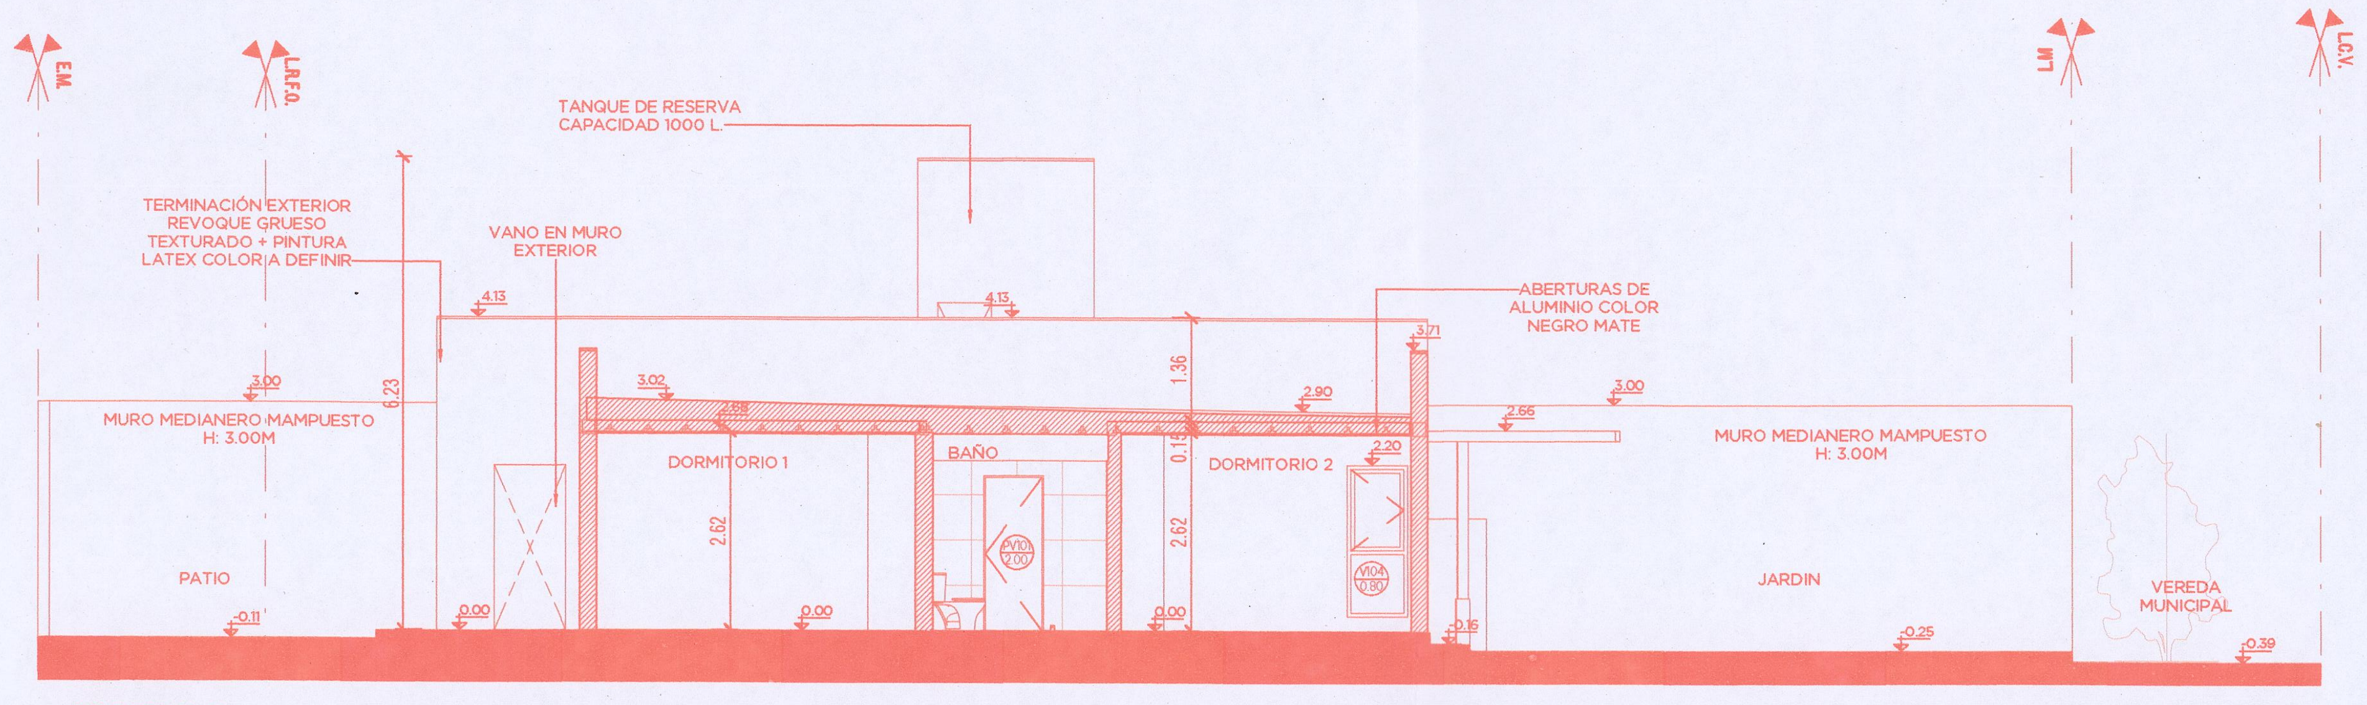
TANQUE DE RESERVA CAPACIDAD 1000 L.
TERMINACIÓN EXTERIOR REVOQUE GRUESO TEXTURADO + PINTURA LATEX COLOR A DEFINIR
VANO EN MURO EXTERIOR
ABERTURAS DE ALUMINIO COLOR NEGRO MATE
MURO MEDIANERO MAMPUESTO H: 3.00M
DORMITORIO 1
BAÑO
DORMITORIO 2
PATIO
JARDIN
VEREDA MUNICIPAL
L.M.
L.E.F.O.
L.C.V.

CORTE B-B
1:100

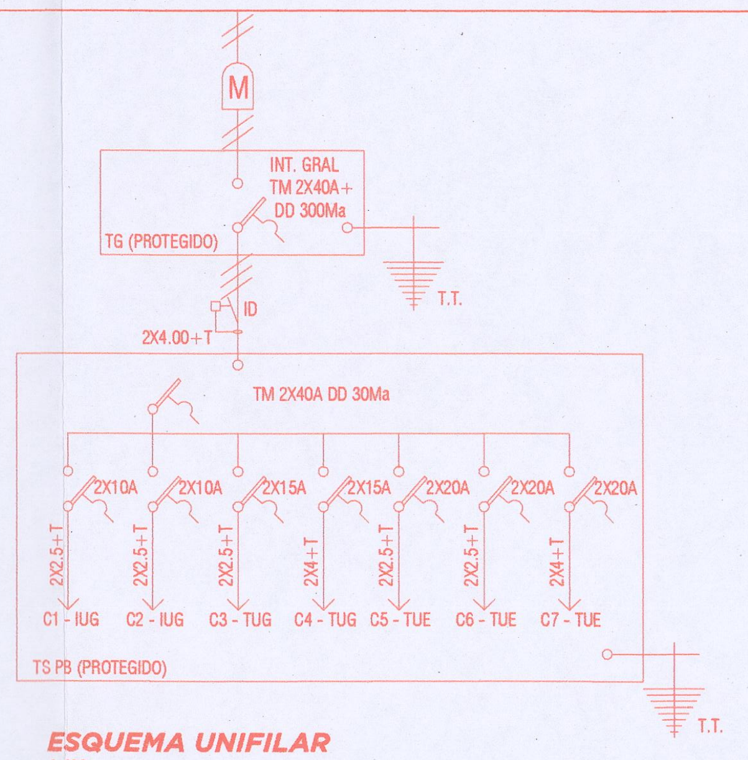

ESQUEMA UNIFILAR
1:100

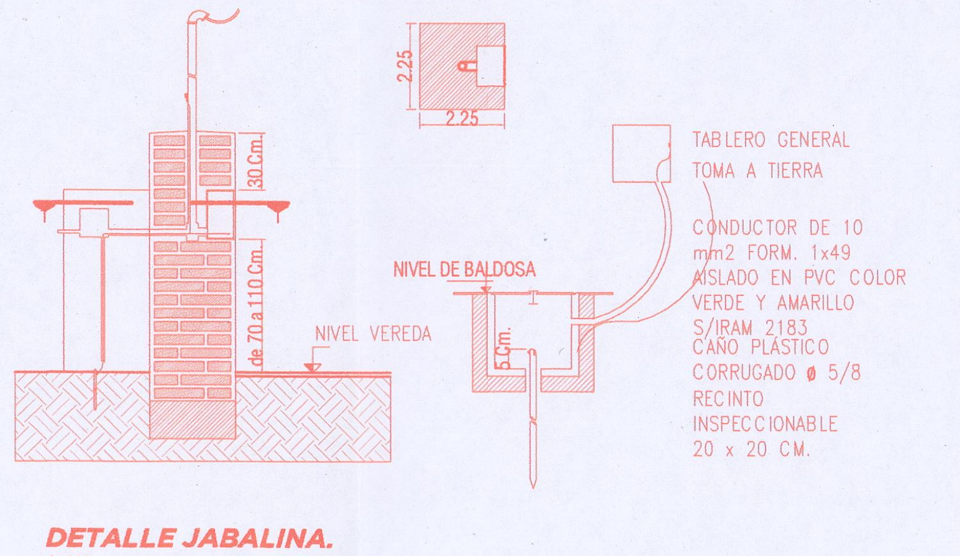

TABLERO GENERAL
TOMA A TIERRA

CONDUCTOR DE 10 mm2 FORM. 1x49 AISLADO EN PVC COLOR VERDE Y AMARILLO S/IRAM 2183
CAÑO PLÁSTICO CORRUGADO ø 5/8
RECINTO INSPECCIONABLE 20 x 20 CM.

DETALLE JABALINA.
1:200

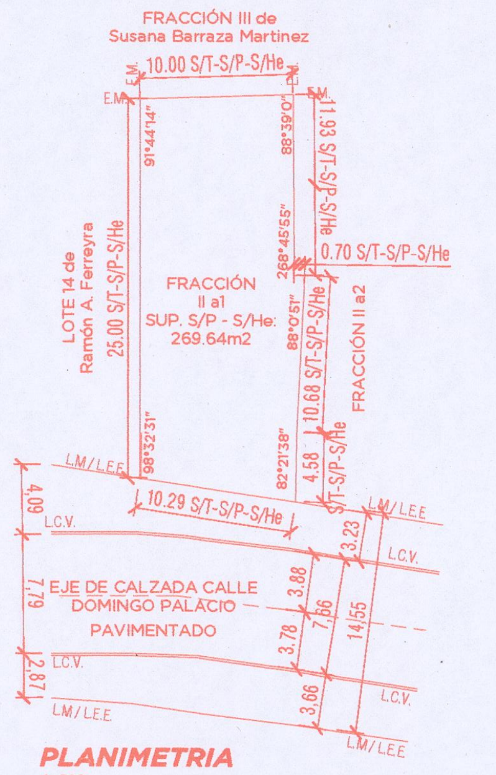

PLANIMETRIA
1:500

DETALLE LOSAS
1:10

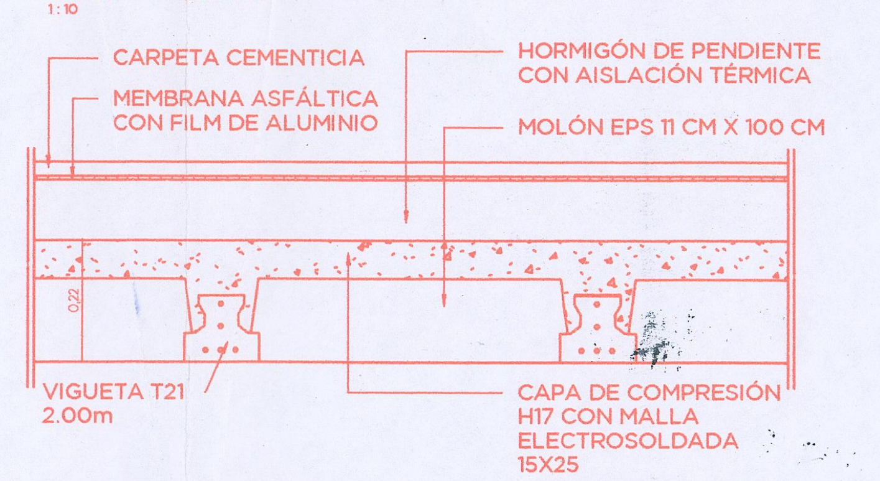
CARPETA CEMENTICIA
MEMBRANA ASFÁLTICA CON FILM DE ALUMINIO
HORMIGÓN DE PENDIENTE CON AISLACIÓN TÉRMICA
MOLÓN EPS 11 CM X 100 CM
VIGUETA T21 2.00m
CAPA DE COMPRESIÓN H17 CON MALLA ELECTROSOLDADA 15X25

PLANILLA DE LOSAS

DESIGNACIÓN	UBICACIÓN	LUZ	KG/M²	h°	B	d	VIGUETAS PRET.
L1	INGRESO	1.33	500	6 cm	16 cm	22 cm	vigueta 1.40
L2	COCINA	1.72	500	6 cm	16 cm	22 cm	vigueta 1.80
L3	ESTAR / COMEDOR	3.14	500	6 cm	16 cm	22 cm	vigueta 3.20
L4	ESTAR / COMEDOR	2.26	500	6 cm	16 cm	22 cm	vigueta 2.40
L5	DORMITORIO 2	3.02	500	6 cm	16 cm	22 cm	vigueta 3.20
L6	PASO	1.20	500	6 cm	16 cm	22 cm	vigueta 1.20
L7	BAÑO	1.82	500	6 cm	16 cm	22 cm	vigueta 2.00
L8	DORMITORIO 1	3.02	500	6 cm	16 cm	22 cm	vigueta 3.10
L9	COCINA	1.72	500	6 cm	16 cm	22 cm	vigueta 1.80
LM1	ALERO POSTERIOR	0.68	500	-	-	8 cm	H°A°
LM2	ALERO FRENTE	0.60	500	-	-	8 cm	H°A°

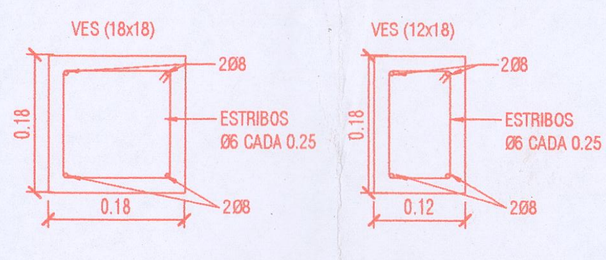

DETALLE DE VIGAS DE ENCADENADO
1:10

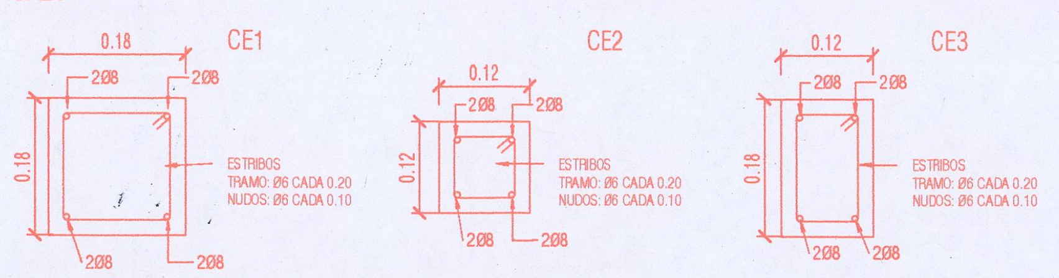

DETALLES DE COLUMNAS DE ENCADENADO
1:10

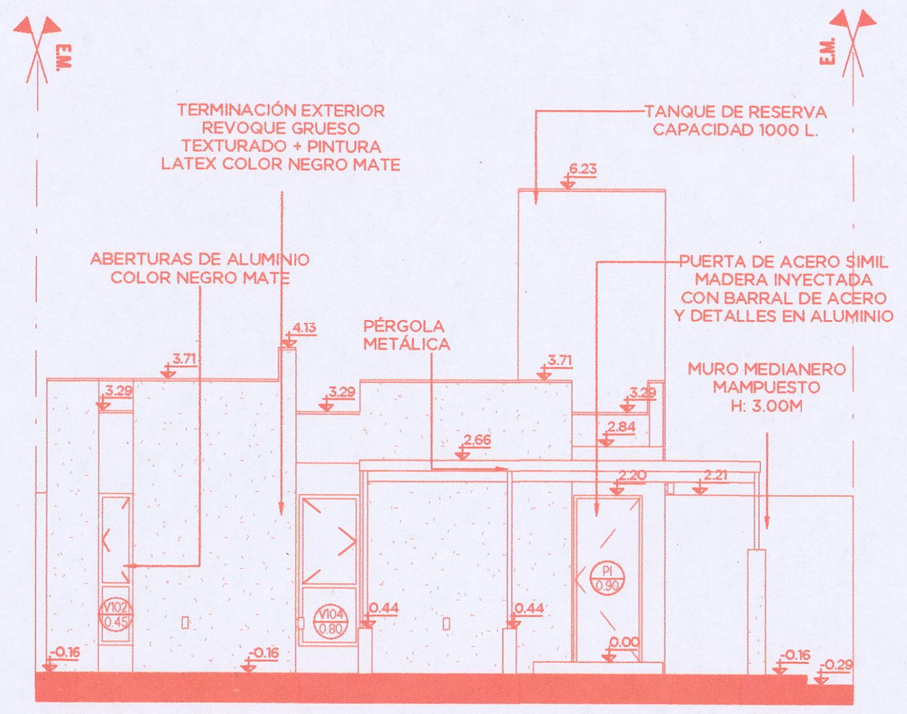
TERMINACIÓN EXTERIOR REVOQUE GRUESO TEXTURADO + PINTURA LATEX COLOR NEGRO MATE
TANQUE DE RESERVA CAPACIDAD 1000 L.
ABERTURAS DE ALUMINIO COLOR NEGRO MATE
PÉRGOLA METÁLICA
PUERTA DE ACERO SIMIL MADERA INYECTADA CON BARRAL DE ACERO Y DETALLES EN ALUMINIO
MURO MEDIANERO MAMPUESTO H: 3.00M

FACHADA FRONTAL
1:100

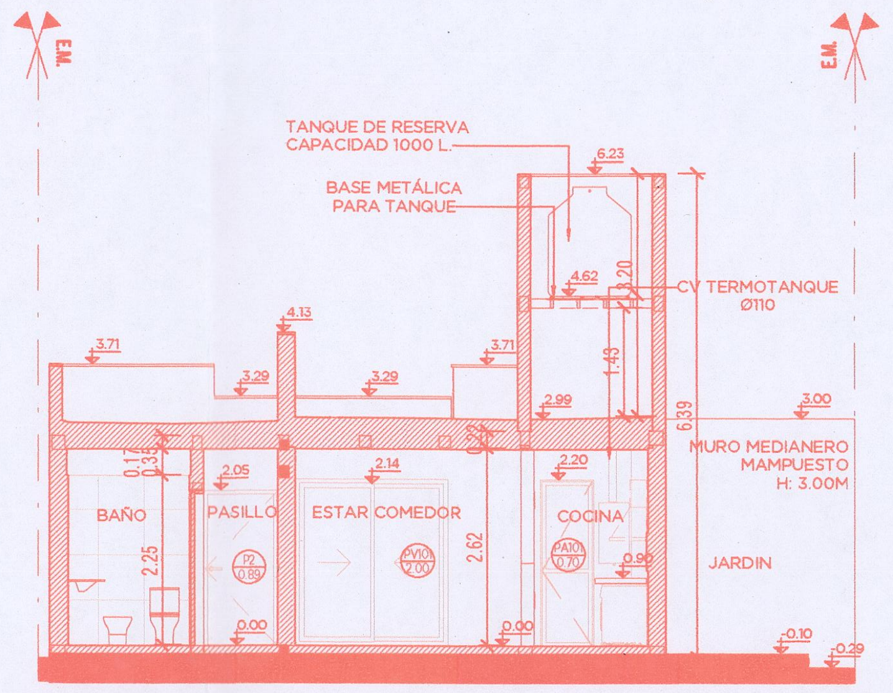
TANQUE DE RESERVA CAPACIDAD 1000 L.
BASE METÁLICA PARA TANQUE
TERMOTANQUE Ø110
MURO MEDIANERO MAMPUESTO H: 3.00M
BAÑO
PASILLO
ESTAR COMEDOR
COCINA
JARDIN

CORTE A-A
1:100

REFERENCIA DE ELECTRICIDAD

ʃ	INTERRUPTOR
ʃ	INTERRUPTOR POLAR
ʃ	LLAVE CONMUTADORA DE CAMBIO
⌂	TOMACORRIENTES CON CONTACTO A TIERRA
⊠	TOMACORRIENTES ESPECIAL
⊡	TOMACORRIENTES BLINDADO EXTERIOR
⊕	BOCA DE PARED
⊕	BOCA DE TECHO
⊙	PULSADOR TIMBRE
▭	CAMPANILLA
T	TOMA TELEFONÍA
TV	TOMA TELEVISIÓN
⊠	TABLERO GENERAL
◪	TABLERO SECCIONAL
M	CAJA MEDIDOR

PLANILLA DE BALANCE DE CARGA

CIRCUITO	TABLERO	BOCAS		POTENCIA		TOTAL POT (KW)	FACTOR SIMUL.	FACTOR UTIL	POTENCIA SIMUL. (KW)	OBSERVACIONES
		LUZ	TOMA	LUZ	TOMA					
C1 IUG	T.SECC 1	8		60		0.48	0.32	0.66	0.21	IUG- interior
C2 IUG		10		60		0.60	0.40	0.66	0.26	IUG- exterior
C3 TUG			12		100	1.20	0.80	0.66	0.52	TUG
C4 TUG			11		100	1.20	0.80	0.66	0.52	TUG
C5 TUE			1		1500	1.50	0.99	0.66	0.65	TUE - AªAª
C6 TUE			1		1500	1.50	0.99	0.66	0.65	TUE - AªAª
C7 TUE			1		1500	1.50	0.99	0.66	0.65	TUE - AªAª
TOTAL POTENCIA INSTALADA						7.98				
DEMANDA DE POTENCIA MAXIMA SIMULTANEA									3.46	

GRADO DE ELECTRIFICACIÓN SEGÚN A.E.A.: ELEVADO.
DEMANDA DE POTENCIA MÁXIMA SIMULTÁNEA: 11 KVA. / CIRCUITOS MÍNIMOS: 5

CIRCUITO	TABLERO	ILUMINACION			TOMACORRIENTES			TOTAL POT (VA)	TOTAL INT (A)	PROTECCION TERMOMAGNETICA	OBSERVACIONES
		CANT	POT. (VA)	I (A).	CANT	POT. (VA)	I (A).				
C1 IUG	T.SECC 1	8	60	0.27				480	2.18	BIPOLAR 1X10 (A)	ILUMINACION INTERIOR
C2 IUG		10	60	0.27				600	2.72	BIPOLAR 1X10 (A)	ILUMINACIONES EXTERIOR
C3 TUG					12	100	0.45	1200	5.45	BIPOLAR 1X16 (A)	TOMACORRIENTES
C4 TUG					112	100	0.45	1200	5.45	BIPOLAR 1X16 (A)	TOMACORRIENTES
C5 TUE					1	1500	0.45	1500	6.82	BIPOLAR 1X 20 (A)	AA° ESTAR COMEDOR
C6 TUE					1	1500	0.45	1500	6.82	BIPOLAR 1X 20 (A)	AA° ESTAR COMEDOR
C7 TUE					1	1500	0.45	1500	6.82	BIPOLAR 1X 20 (A)	AA° ESTAR COMEDOR
					TOTAL			7980	BIPOLAR 1X40 (A)		
					PRETECCIÓN GENERAL			35.64	DISYUNTOR DIFERENCIAL MONOFASICO DE 2X 40 A		
					POTENCIA SIMULTANEA 0.8			6384			

PLANILLA DE ILUMINACION Y VENTILACION

LOCAL		ABERTURA				LOCAL		OBSERVACIONES
DESIGNACION	SUPERFICIE (m²)	DESIG.	CANT.	ANCHO (m)	ALTO (m)	AREA ILUM	AREA VENT	
ESTAR COMEDOR	18.33	PV101	1	2.00	2.05	4.40	2.20	PUERTA VENTANA CORREDIZA
		V104	1	0.80	2.00	1.60	0.96	VENTANA BATIENTE + PAÑO FIJO
COCINA	837	V105	1	1.80	0.50	0.90	0.45	VENTANA CORREDIZA
		PA 101	1	0.70	2.20	1.54	0.35	PUERTA+ VENTANA DE ABRIR
		V131	1	0.45	2.00	0.90	0.23	VENTANA BATIENTE + PAÑO FIJO
BAÑO	5.41	-	-	-	-	-	0.03	CV FORZADA Ø200
DORMITORIO 1	11.76	V104	1	0.80	2.00	1.60	0.96	VENTANA BATIENTE + PAÑO FIJO
DORMITORIO 2	10.66	V104	1	0.80	2.00	1.60	0.96	VENTANA BATIENTE + PAÑO FIJO
		V102	1	0.45	2.00	0.90	0.54	VENTANA BATIENTE + PAÑO FIJO

PLANILLA DE VIGAS .
1:75

tramos a b

NIVEL	DESIGN ACION	Luz m	DIMENSIONES (cm)				ARMADURA - TRAMO						ESTRIB. CERR			OBSERVACIONES
							Ai			As						
			bo	d	h	B	cm2	n°	Ø	cm2	n°	Ø	Ø	Sep. cm	dist	
P.B	VES 12	*	18	18	14	12	1.00	2	8	1.00	2	8	6	10 20	nudo tramo	*Longitud varible
P.B	VES 13	*	12	18	8	18	1.00	2	8	1.00	2	8	6	10 20	nudo tramo	*Longitud varible
P.B.	D- 12	*	12	15	8	11	1.00	2	8	1.00	2	8	6	10 20	nudo tramo	*Longitud varible

PLANILLA DE COLUMNAS .
1:75

p/ mampostería de ladrillo cerámico portante

acero tipo_ADN-420

DESIGN ACION	hp. m	HORMIGON			ARMADURA			ESTRIBOS		OBSERVACIONES
		d1 cm	d2 cm	S cm²	N°	Ø	Sec cm	Ø	Sep. cm	
CE1	2.90/ 3.30	18	18	324	4	8	2.01	6	10 (t) 20 (n)	Cuadrada encadenado
CE2	2.90/ 3.30	12	12	144	4	8	2.01	6	10 (t) 20 (n)	Cuadrada encadenado
CE3	2.90/ 3.30	18	12	216	4	8	2.01	6	10 (t) 20 (n)	Rectangular encadenado
C2	2.90/ 3.30	18	18	324	4	12	4.52	8	10 (t) 20 (n)	Cuadrada estructural

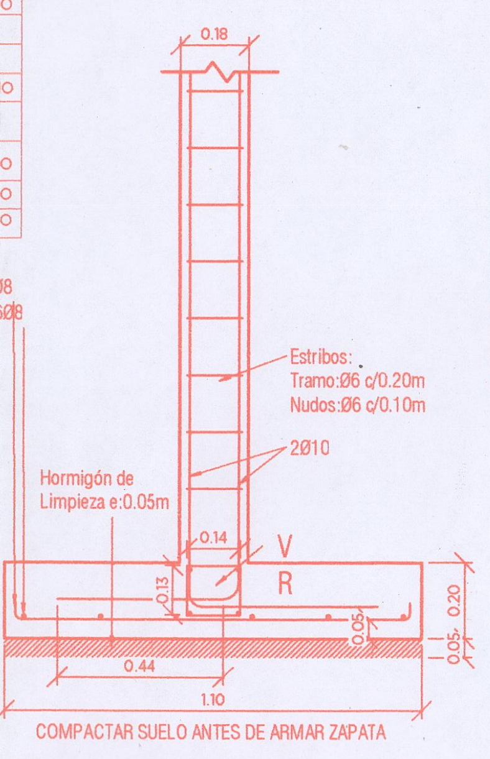

COMPACTAR SUELO ANTES DE ARMAR ZAPATA

PLANILLA DE BASES
1:100

DESIGNA CION	DIMENSIONES (cm)		Recub r (cm)	ARMADURA INF ZAPATA				OBSERVACIONES
				A1		Ao		
	d1	d2		n°	Ø	Ø	Sep.(cm)	
ZC-1	60	25	5	4	6	8	15	CORRIDA CENTRADA
ZC-2	80	25	5	4	6	8	15	CORRIDA CENTRADA
ZC-M	80	25	5	4	6	8	15	CORRIDA EXCENTRICA
ZP	60	25	5	4	8	8	15	PUNTUAL CENTRADA

DETALLE FUNDACION
1:20

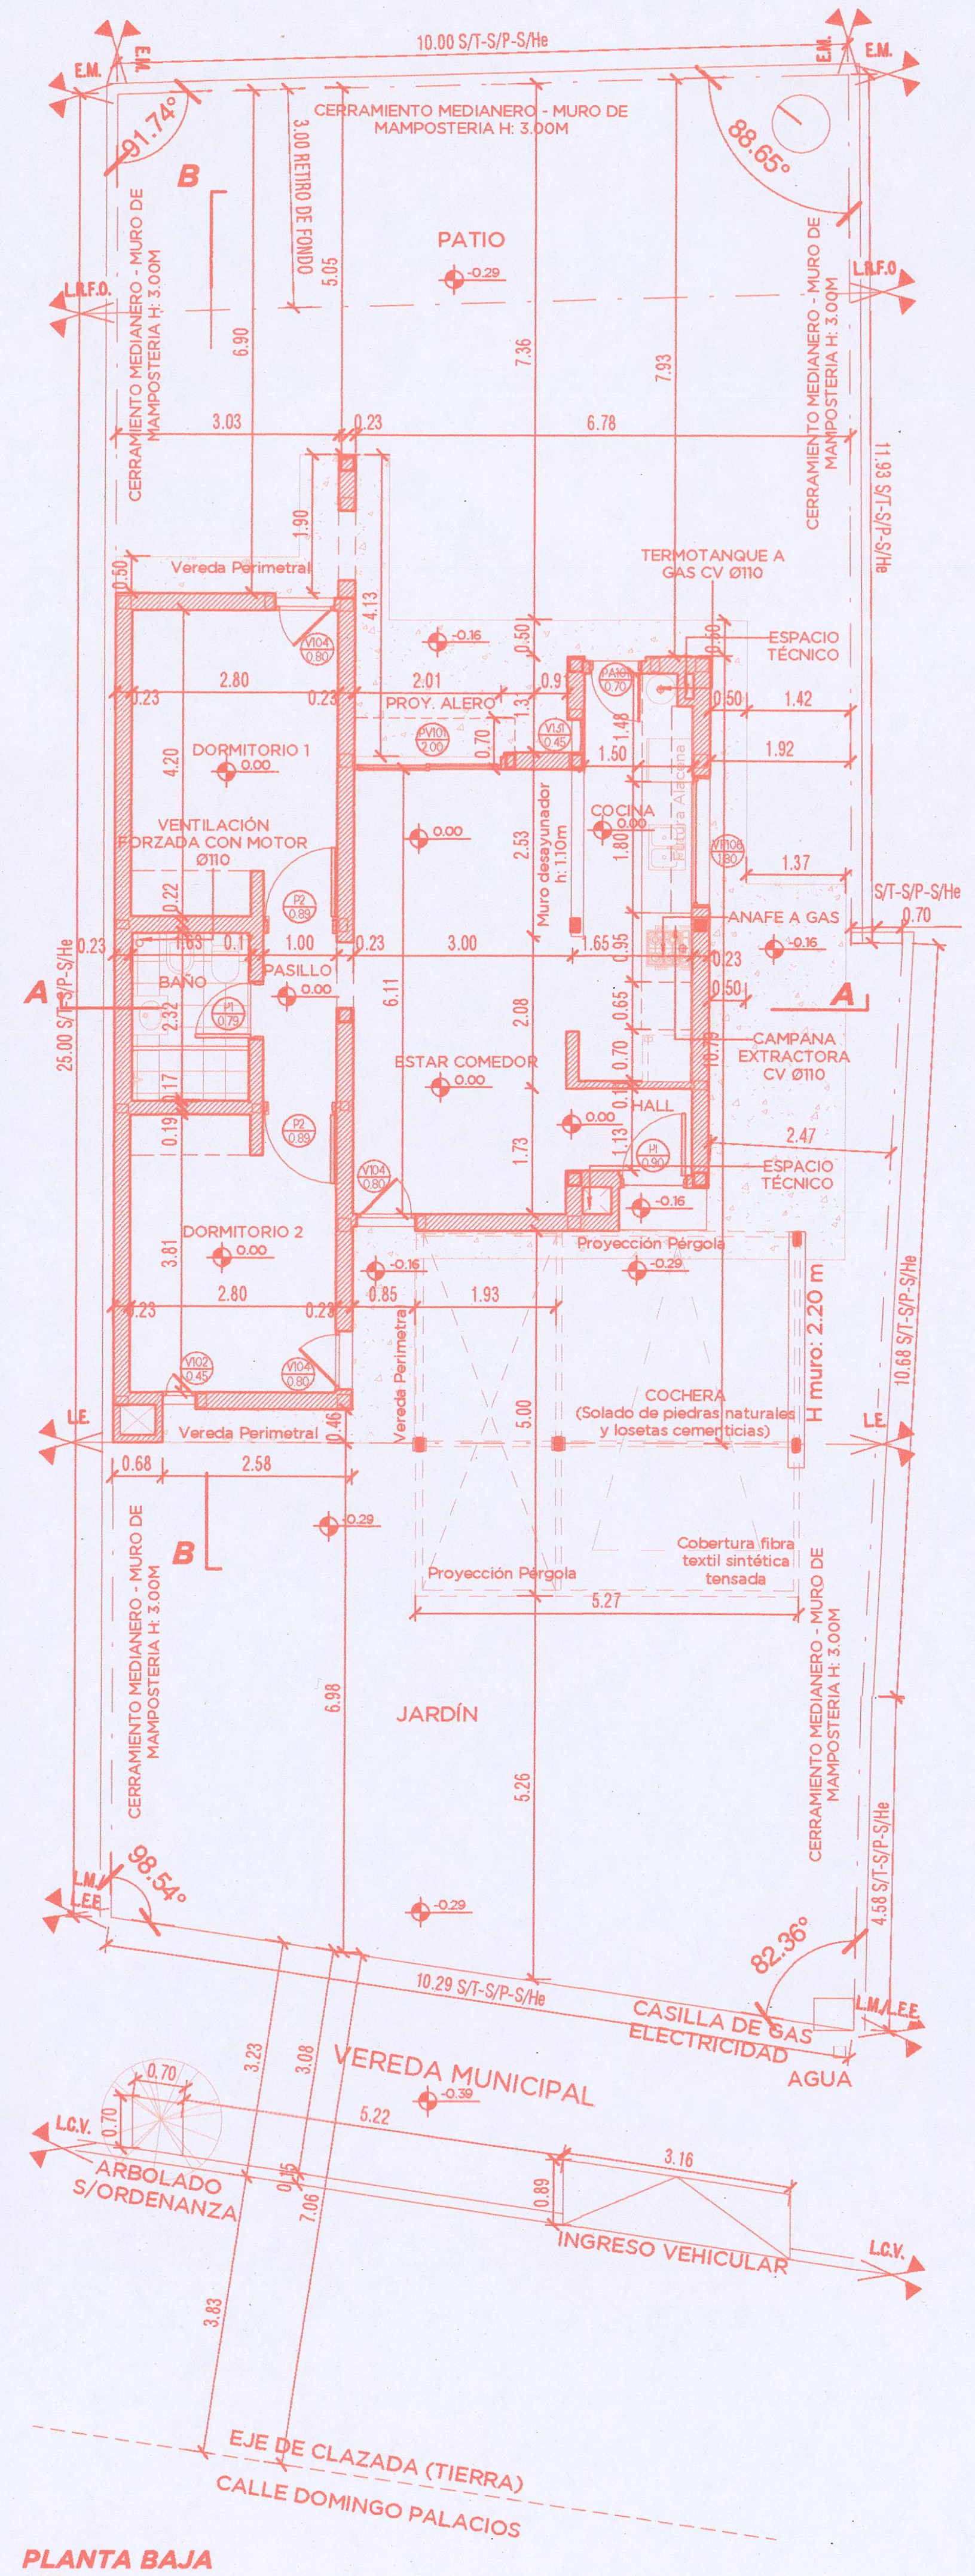

PLANTA BAJA
1:100

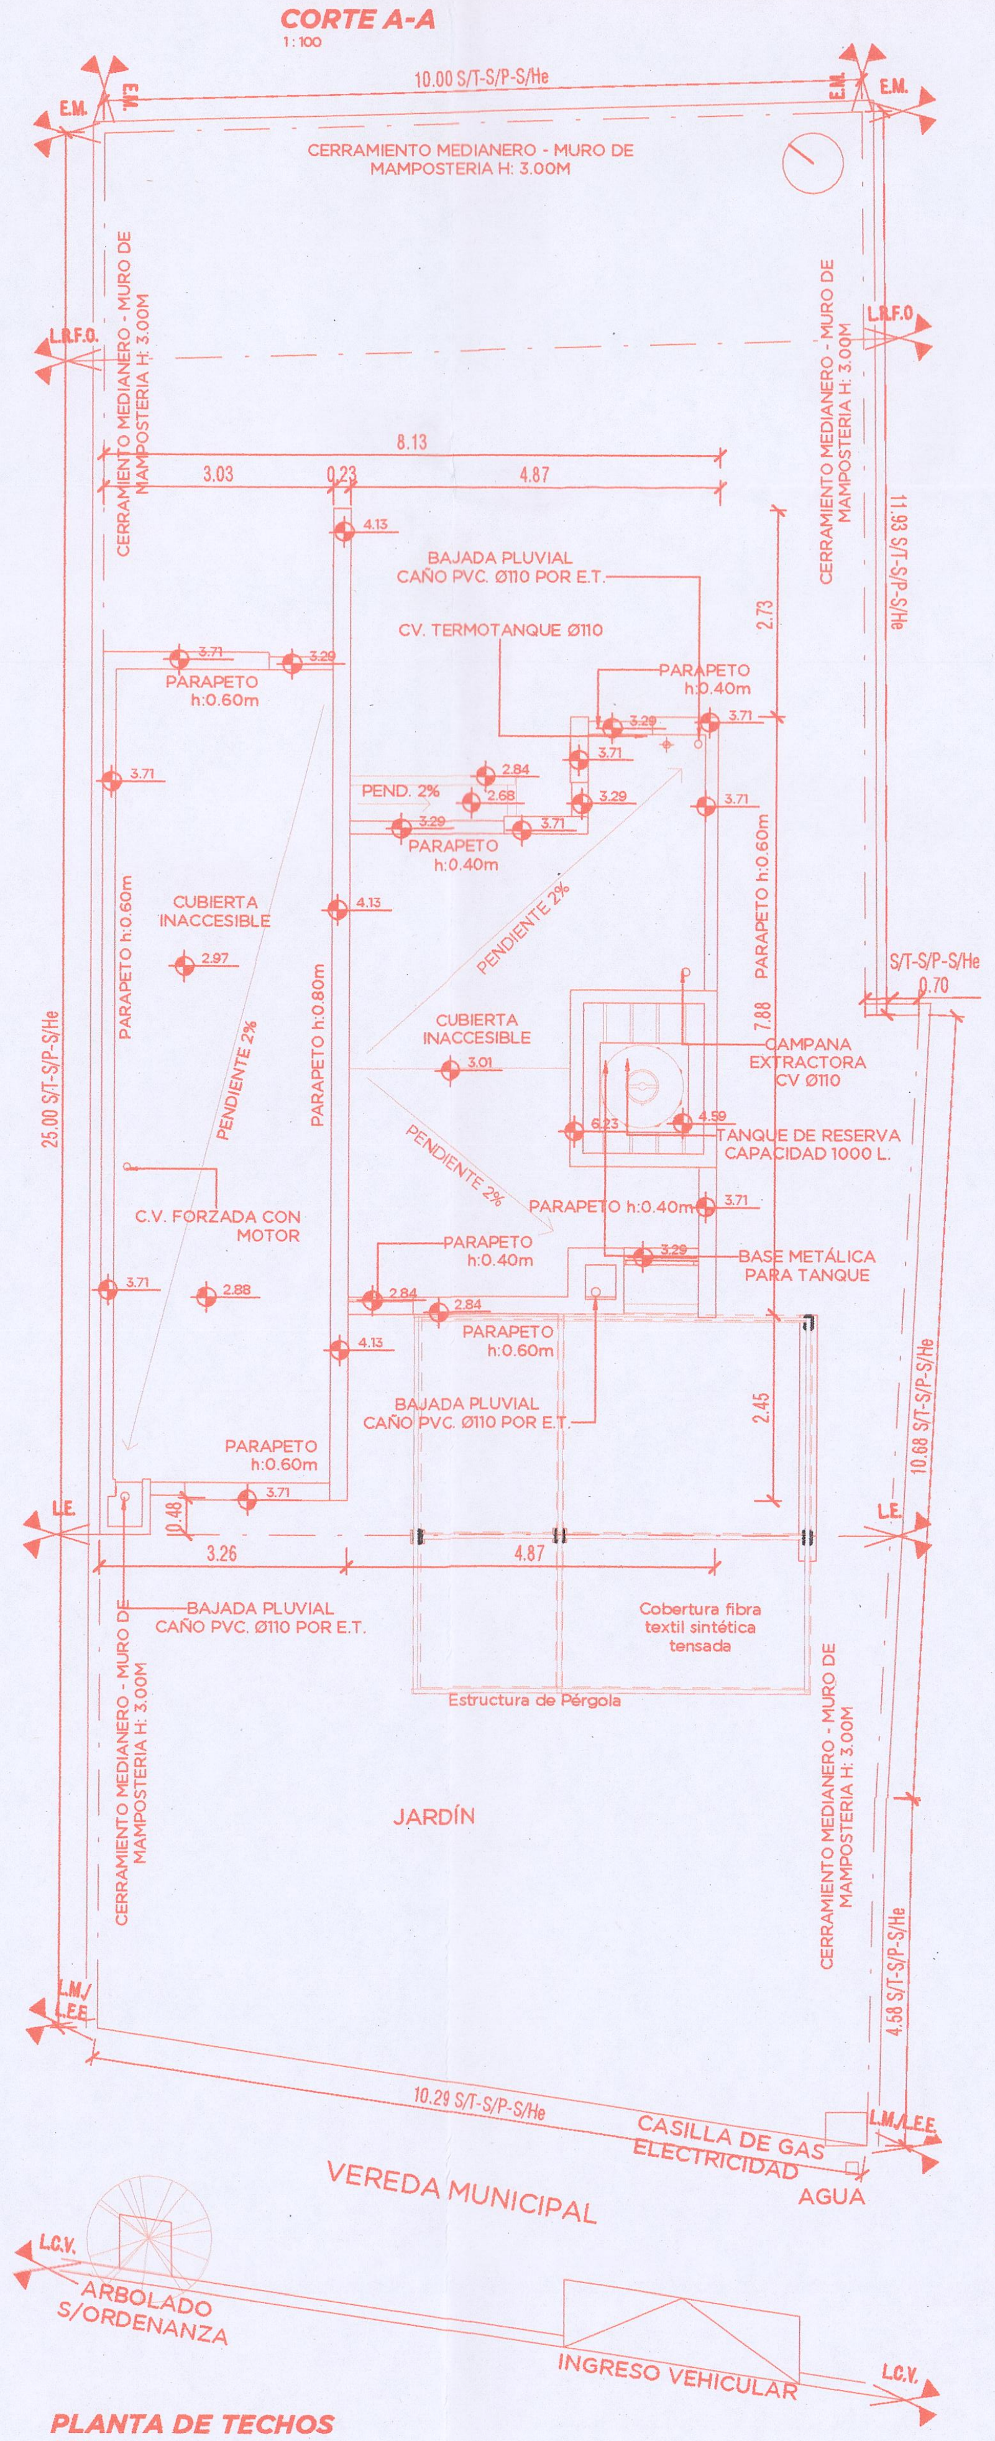
CERRAMIENTO MEDIANERO - MURO DE MAMPOSTERIA H: 3.00M
BAJADA PLUVIAL CAÑO PVC. Ø50 POR E.T.
CV. TERMOTANQUE Ø110
PARAPETO h:0.60m
PARAPETO h:0.40m
PEND. 2%
PENDIENTE 2%
CUBIERTA INACCESIBLE
CAMPANA EXTRACTORA CV Ø110
TANQUE DE RESERVA CAPACIDAD 1000 L.
BASE METÁLICA PARA TANQUE
C.V. FORZADA CON MOTOR
BAJADA PLUVIAL CAÑO PVC. Ø110 POR E.T.
Cobertura fibra textil sintética tensada
Estructura de Pérgola
JARDIN
VEREDA MUNICIPAL
CASILLA DE GAS ELECTRICIDAD AGUA
ARBOLADO S/ORDENANZA
INGRESO VEHICULAR

PLANTA DE TECHOS
1:100

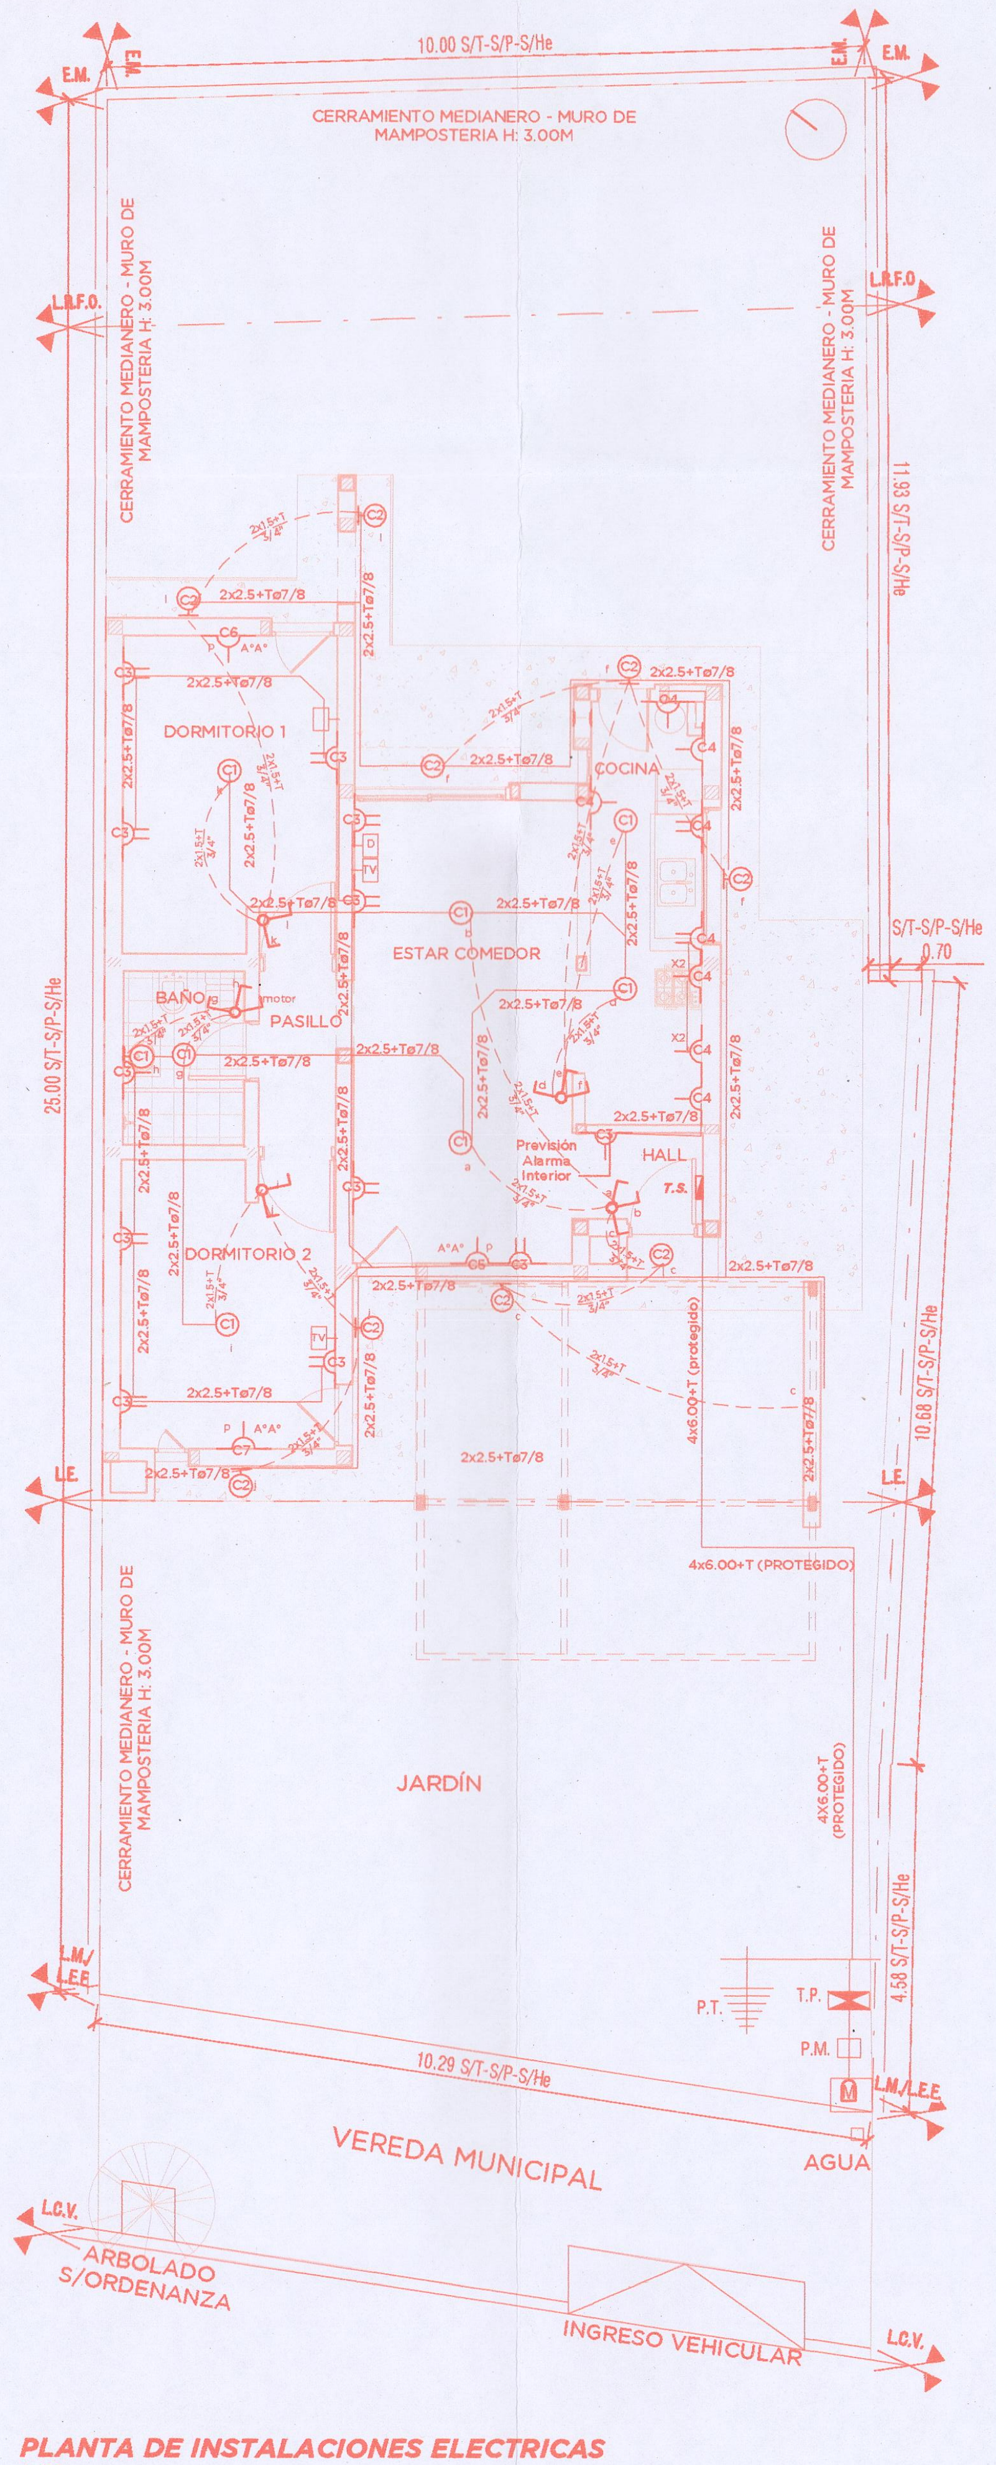

PLANTA DE INSTALACIONES ELECTRICAS
1:100

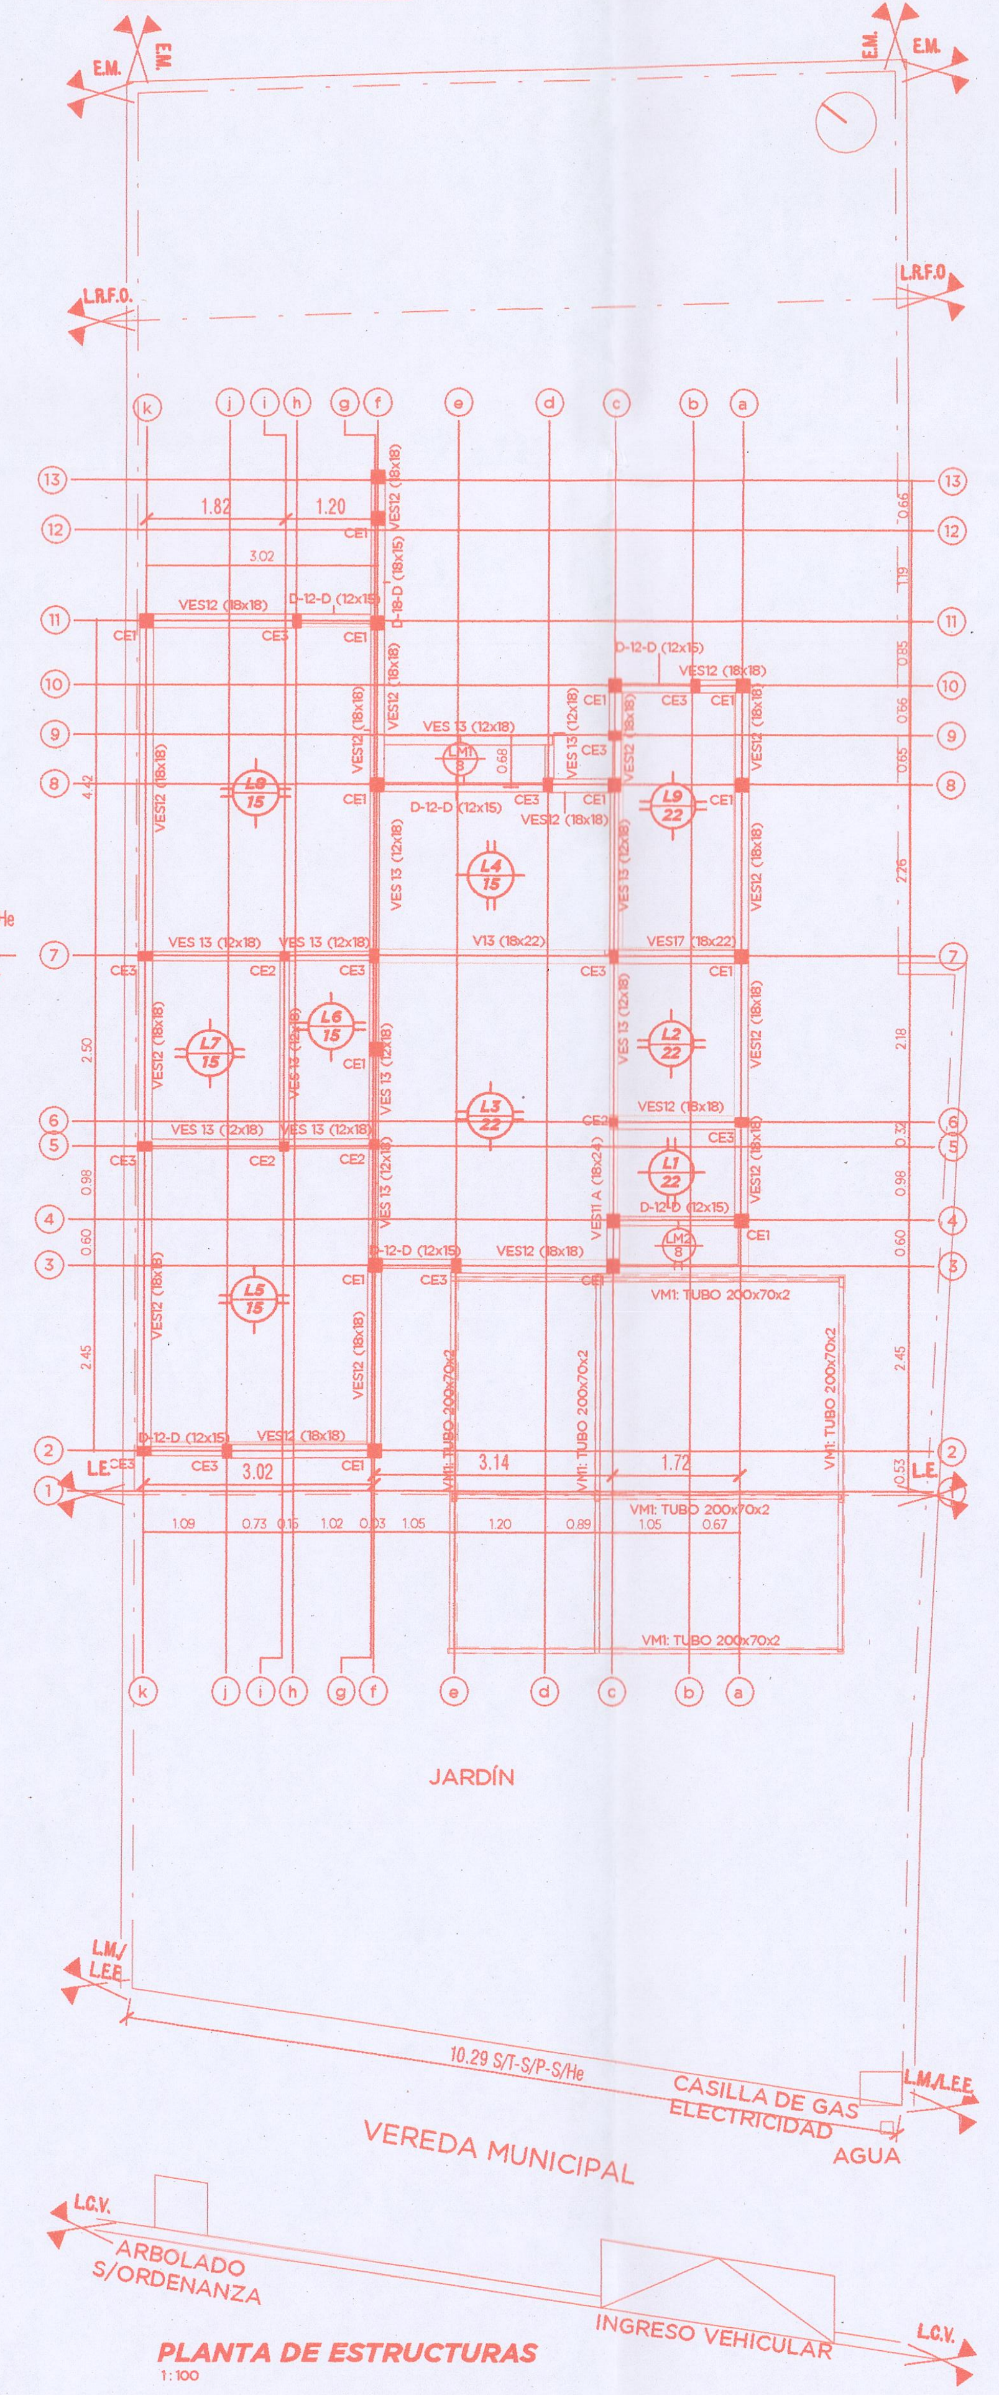

PLANTA DE ESTRUCTURAS
1:100

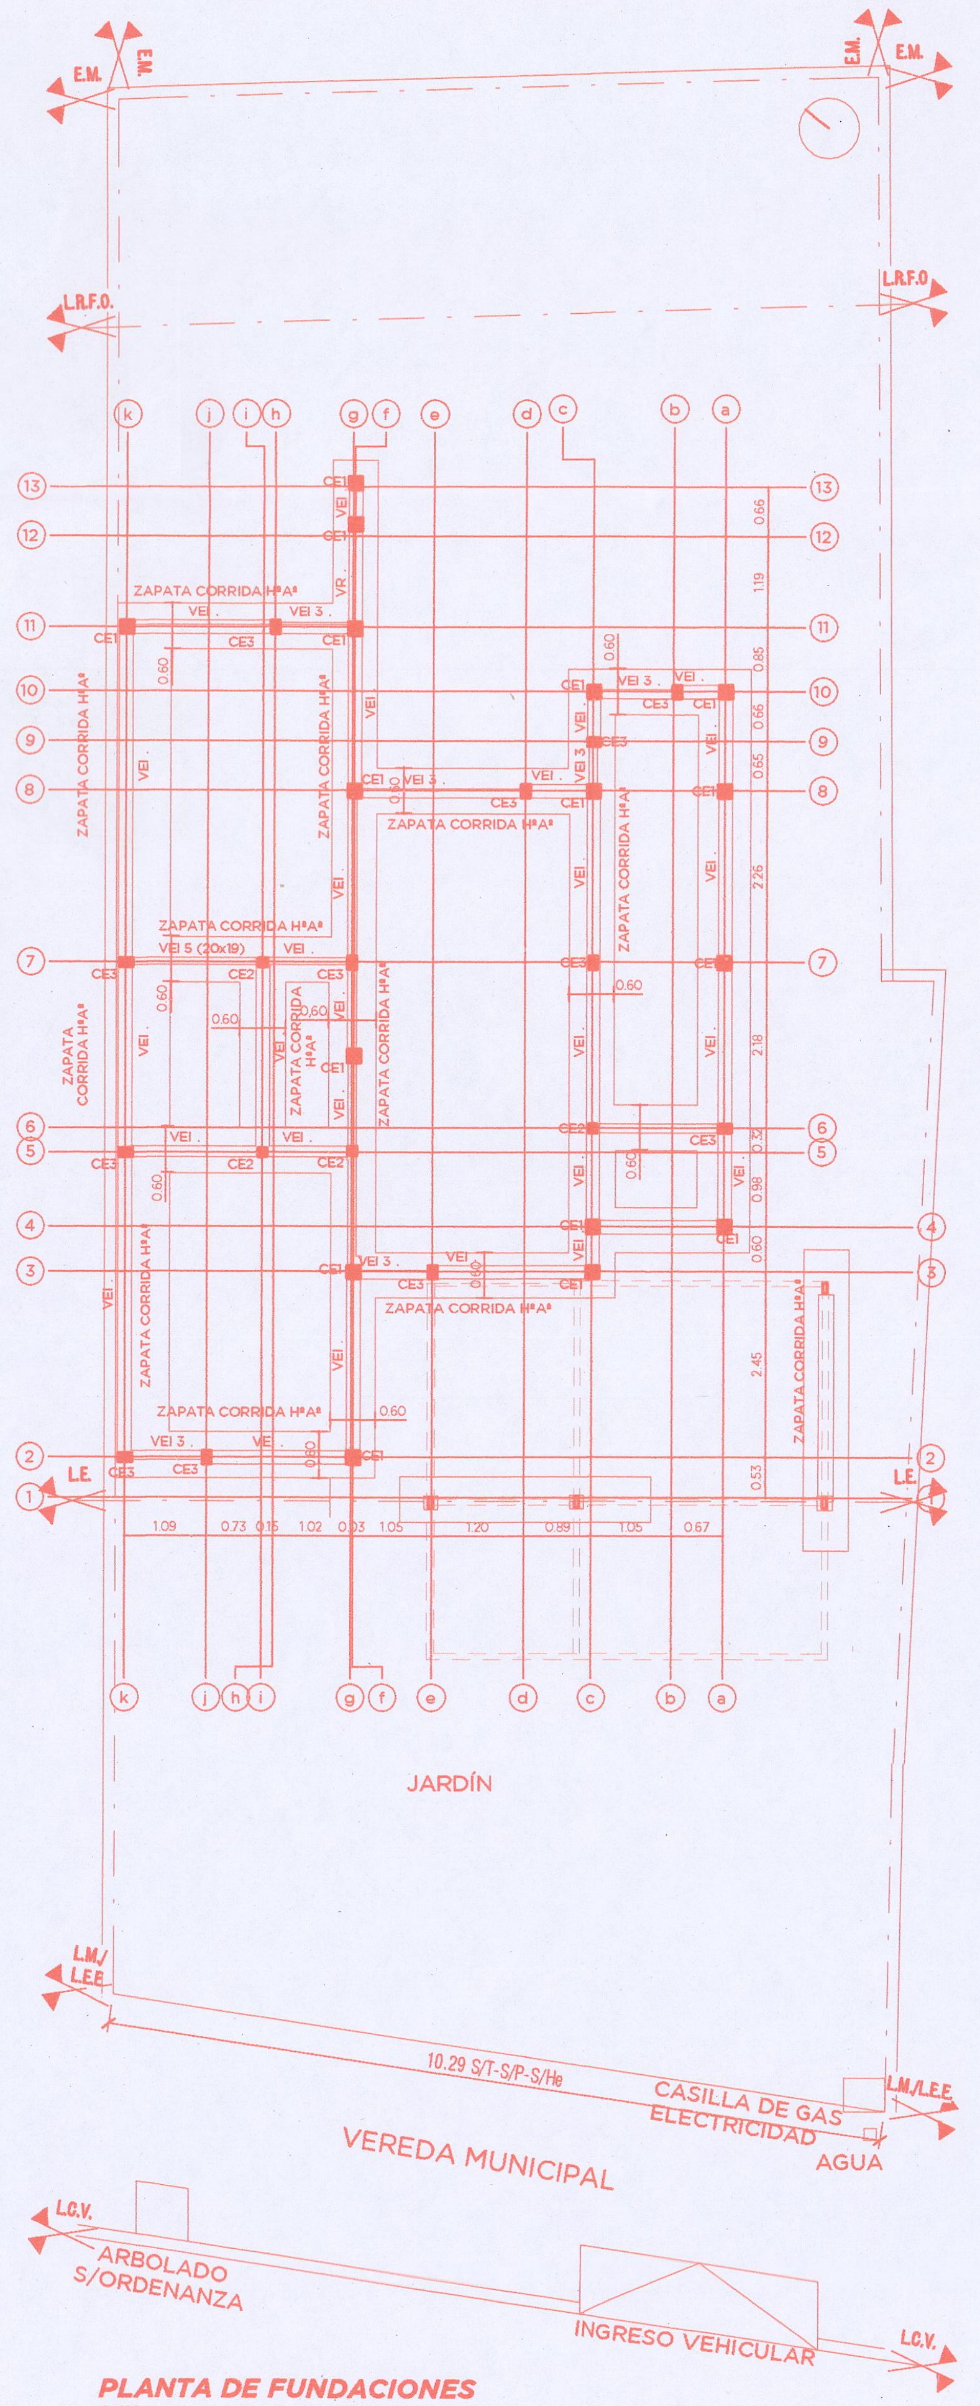

PLANTA DE FUNDACIONES
1:100

DIST.: 02 ZONA.: 06 MANZ.: 08 PARC.:148
PADRON INMOB. : 01-01-154743 I.M.C. N°: 484-T-24 DOMINIO: 7S-34926

LEY 4.683

24040406

64

11024

PROYECTO Y
DIRECCION DE OBRA

SUSANA ABECASSIS
Arquitecta
Secretaría Técnica
Colegio de Arquitectos SDE

DEST. DE LA OBRA: VIVIENDA FAMILIAR

PROPIETARIOS: TEVEZ, SILVINA PATRICIA
DNI: 32.547.945 CUIL: 27-32547945-6
TEVEZ, FLORENCIA NORALI
DNI: 40.939.765 CUIL: 23-40939765-4

UBICACIÓN: DOMINGO PALACIOS N°1046
BARRIO: ALMIRANTE BROWN
CIUDAD: SANTIAGO DEL ESTERO CAPITAL
ESCALA: 1/100

DIRECCION DE SUELO URBANO
EXPEDIENTE 430 31 24
FECHA 07 NOV. 2024
BOLETA 3395

SUPERFICIE TERRENO S/T-S/He:	S/T - S/He: 269.64m²
SUPERFICIE PROYECTADA CUBIERTA:	72.84 m²
SUPERFICIE TOTAL:	72.84 m²
SUPERFICIE LIBRE:	196.80 m²

CROQUIS DE UBICACIÓN:

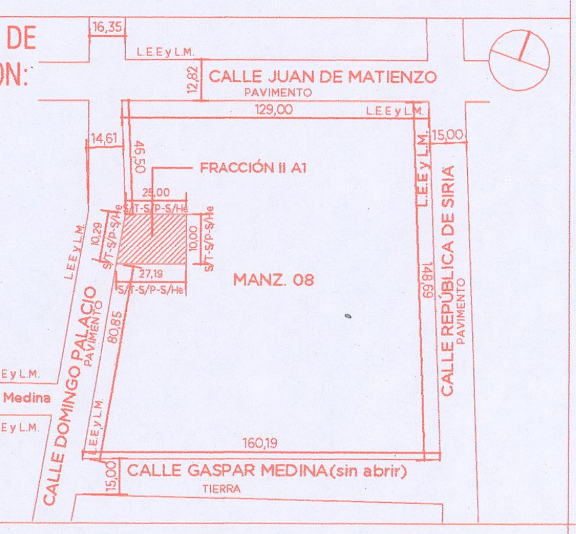

PROPIETARIO: TEVEZ, SILVINA PATRICIA
DIRECCIÓN: HERNANDO DE AGUIRRE N° 36 - BARRIO ALMIRANTE BROWN - SANTIAGO DEL ESTERO CAPITAL
DNI: 32.547.945
CUIL: 27-32547945-6

PROPIETARIO: TEVEZ, FLORENCIA NORALI
DIRECCIÓN: HERNANDO DE AGUIRRE N° 36 - BARRIO ALMIRANTE BROWN - SANTIAGO DEL ESTERO CAPITAL
DNI: 40.939.765
CUIL: 23-40939765-4

PROYECTO : Arq. Dorado, Lidia
Matricula: 560
DNI: 27.109.483
Domicilio: Calle Las Rosas N° 3342, B° Jardin, Capital, Santigo del Estero

DORADO LIDIA AZUCENA
ARQUITECTA
M.P N° 560

DIRECCIÓN TÉCNICA : Arq. Dorado, Lidia
Matricula: 560
DNI: 27.109.483
Domicilio: Calle Las Rosas N° 3342, B° Jardin, Capital, Santigo del Estero

DORADO LIDIA AZUCENA
ARQUITECTA
M.P N° 560

ANCHO DE CALLE	14.55 m	PAVIMENTO		SI
ANCHO DE DE CALZADA	7.06 m			
ANCHO DE VEREDA	3.23 m	SERVICIO CLOACALES:		SI

DIRECCION DE SUELO URBANO
EXPEDIENTE 430 / 31 / 24
09 DIC. 2024
FECHA DE SELLADO
BOLETA N° 3496

PLANO DE PROYECTO

(ARQUITECTURA - ESTRUCTURA - VISTAS - ELECTRICIDAD)

OBSERVACIONES:

12 NOV 2024
Las referencias al dominio son meramente indicativas, y la aprobación administrativa no valora los derechos que de ellos emergen.

PERMISO DE COMIENZO DE OBRA N° 136/2024 26/11/2024
DIRECCION DE SUELO URBANO

MUNICIPALIDAD DE LA CIUDAD DE SANTIAGO DEL ESTERO
SECRETARIA DE ECONOMIA
APROBADO
DIRECCIÓN DE SUELO URBANO
EXPEDIENTE: 430-31-2024 Corp. 08-T-2024
FECHA: 18 DIC 2024

Ing. Agrim. J. LEANDRO ARJONA
JEFE DE AREA DE VISACIONES TECNICAS
DIRECCION DE CATASTRO MUNICIPAL

Arq. ABRAHAM BERNARDO ROMINA
Dpto. OBRAS PRIVADAS
DIRECCION DE SUELO URBANO

Arq. ESTER R. CHALOM
SUB-DIRECTORA
DIRECCION DE SUELO URBANO