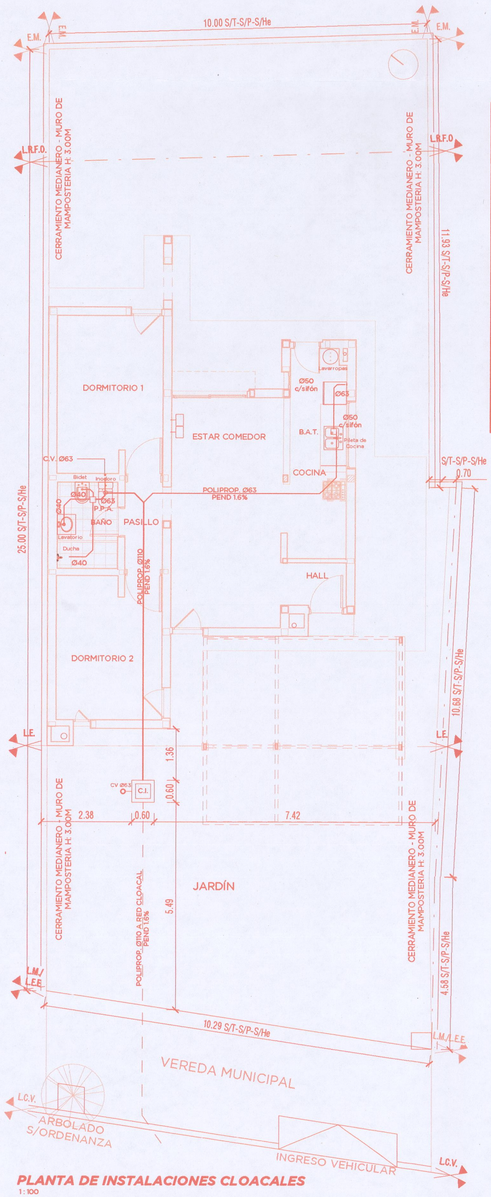


PLANTA DE INSTALACIONES CLOACALES
1: 100

CUADRO RESUMEN (en mm)


Cañerias de Desagues


DESIGNACIÓN	PRIMARIAS Nº	Materia	Diám.	PLUVIALES Nº	Materia	Diám.	VENTILACIÓN	
HORIZONTAL	1	Polip.	ø110	1	Polip.	ø110		
COLUMNAS		Polip.	ø110			ø110	Baño	
CONDUCTAL		Polip.	ø110			ø110		
CAÑOS DE LLUVIA		Polip.	ø110	1		ø110	Cocina	
Cond. Ventil.		Polip.	ø110			ø110	Lav.	


Cañerias Agua Fria y Caliente

DESIGNACIÓN	Ⓢ	Ⓒ	Ⓕ	Ramales de agua fria	Ramales de agua caliente
TANQUE	1	Polip. ø110	Polip.ø110		
PLANTA BAJA		Polip. ø110	Polip.ø110	Polip.ø110	Polip.ø110
ARTEFACTOS					

DETALLES DE TANQUE DE RESERVA
(s/ escala)

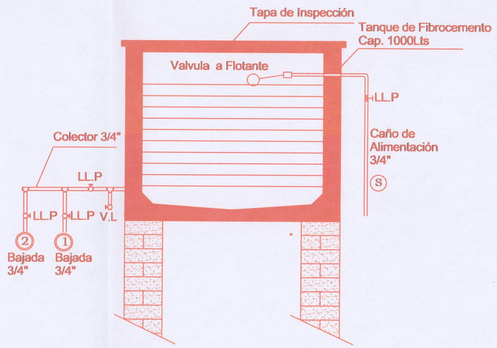

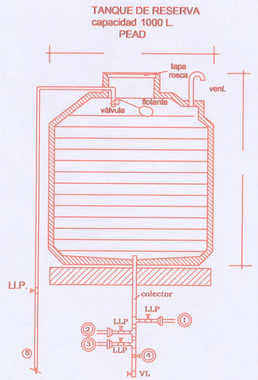

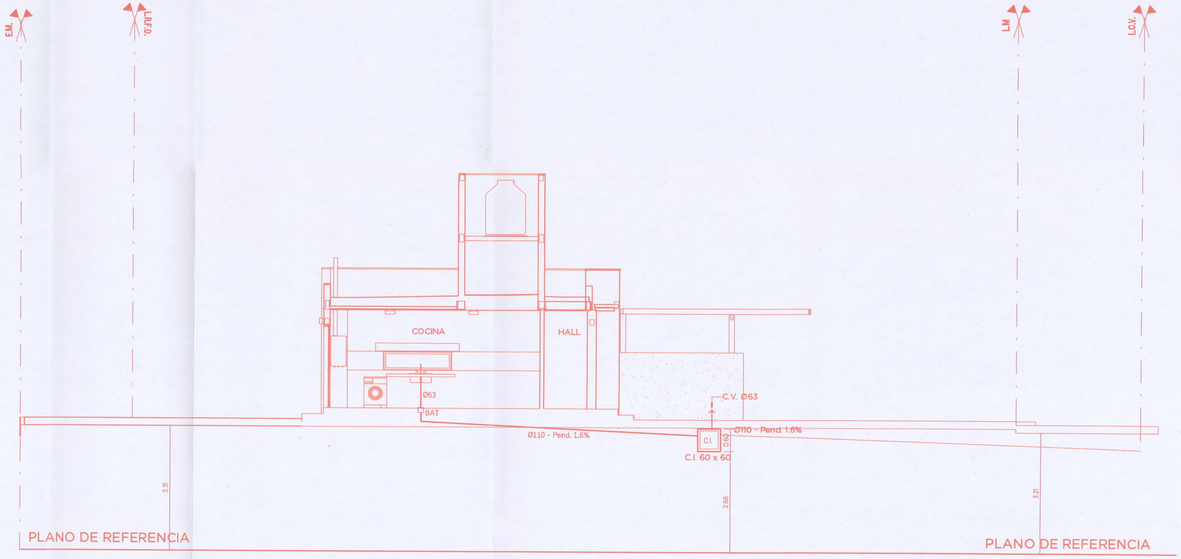

CORTE SANITARIO C-C
1: 100

DIST.: 02 ZONA.: 06 MANZ.: 08 PARC.: 148 LEY 4.683

PADRON INMOB. : 01-01-154743 I.M.C. Nº: 424-T-24 DOMINIO: 7S-3426 2404406

DEST. DE LA OBRA: VIVIENDA FAMILIAR

PROPIETARIOS: TEVEZ, SILVINA PATRICIA
DNI: 32.547.945 CUIL: 27-32547945-6
TEVEZ, FLORENCIA NORALI
DNI: 40.939.765 CUIL: 23-40939765-4

UBICACIÓN: DOMINGO PALACIOS Nº1046
BARRIO: ALMIRANTE BROWN
CIUDAD: SANTIAGO DEL ESTERO CAPITAL
ESCALA: 1/100

SECRETARIA DE ECONOMIA Municipalidad de la Ciudad de SGO. DEL ESTERO DIRECCION DE SUELO URBANO

DIRECCION DE SUELO URBANO EXPEDIENTE 430 31 24 FECHA 07 NOV 2024 BOLETA 3295

COLEGIO DE ARQUITECTOS LEY 5654/87 SANTIAGO DEL ESTERO
PROYECTO Y DIRECCION DE OBRA 02 001 2025
Fernanda Dangelis Arquitecta Secretaria Técnica Adjunta Colegio de Arquitectos S D E

SUPERFICIE TERRENO S/T-S/He:	S/T - S/He: 269.64m²
SUPERFICIE PROYECTADA CUBIERTA:	72.84 m²
SUPERFICIE TOTAL:	72.84 m²
SUPERFICIE LIBRE:	196.80 m²

PROPIETARIO: TEVEZ, SILVINA PATRICIA
DIRECCIÓN: HERNANDO DE AGUIRRE Nº 36 - BARRIO ALMIRANTE BROWN - SANTIAGO DEL ESTERO CAPITAL
DNI: 32.547.945
CUIL: 27-32547945-6

PROPIETARIO: TEVEZ, FLORENCIA NORALI
DIRECCIÓN: HERNANDO DE AGUIRRE Nº 36 - BARRIO ALMIRANTE BROWN - SANTIAGO DEL ESTERO CAPITAL
DNI: 40.939.765
CUIL: 23-40939765-4


PROYECTO : Arq. Dorado, Lidia
Matrícula: 560
DNI: 27.109.483
Domicilio: Calle Las Rosas Nº 3342, Bº Jardín, Capital, Santigo del Estero

DORADO LIDIA AZUCENA ARQUITECTA M.P Nº 560

DIRECCIÓN TÉCNICA : Arq. Dorado, Lidia
Matrícula: 560
DNI: 27.109.483
Domicilio: Calle Las Rosas Nº 3342, Bº Jardín, Capital, Santigo del Estero

DORADO LIDIA AZUCENA ARQUITECTA M.P Nº 560

CROQUIS DE UBICACIÓN:

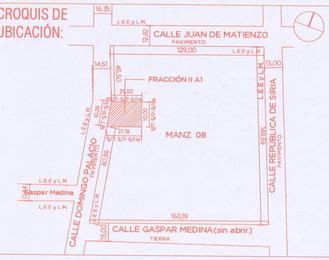

ANCHO DE CALLE	14.55 m	PAVIMENTO	SI
ANCHO DE CALZADA	7.06 m		
ANCHO DE VEREDA	3.23 m	SERVICIO CLOACALES	SI

DIRECCION DE SUELO URBANO EXPEDIENTE 430 / 31 / 24 FECHA DE SOLICITUD 09 DIC. 2024 BOLETA Nº 3496

PLANO DE PROYECTO SANITARIO
(CLOACAS A RED)

12 NOV 2024

OBSERVACIONES:
Las referencias al Título de dominio son meramente indicativas, y la aprobación administrativa no valora los derechos que de ellos emergen.

PERMISO DE COMIENZO DE OBRA Nº 430/2024 26/11/2024
DIRECCION DE SUELO URBANO

MUNICIPALIDAD DE LA CIUDAD DE SANTIAGO DEL ESTERO
SECRETARIA DE ECONOMIA
APROBADO
DIRECCIÓN DE SUELO URBANO
EXPEDIENTE: 430-31-2024-Corp.08-T-2024
FECHA: 18 DIC 2024

Mg. Agrim. J. LEANDRO ARJONA
DIRECTOR DE OBRA DE VISACIONES TECNICAS
DIRECCION DE CATASTRO MUNICIPAL

Arq. ABRAHAM BERNARDO ROMINA
Dpto. OBRAS PRIVADAS
DIRECCION DE SUELO URBANO

Arq. ESTER R. CHALOM
SUB-DIRECTORA
DIRECCION DE SUELO URBANO