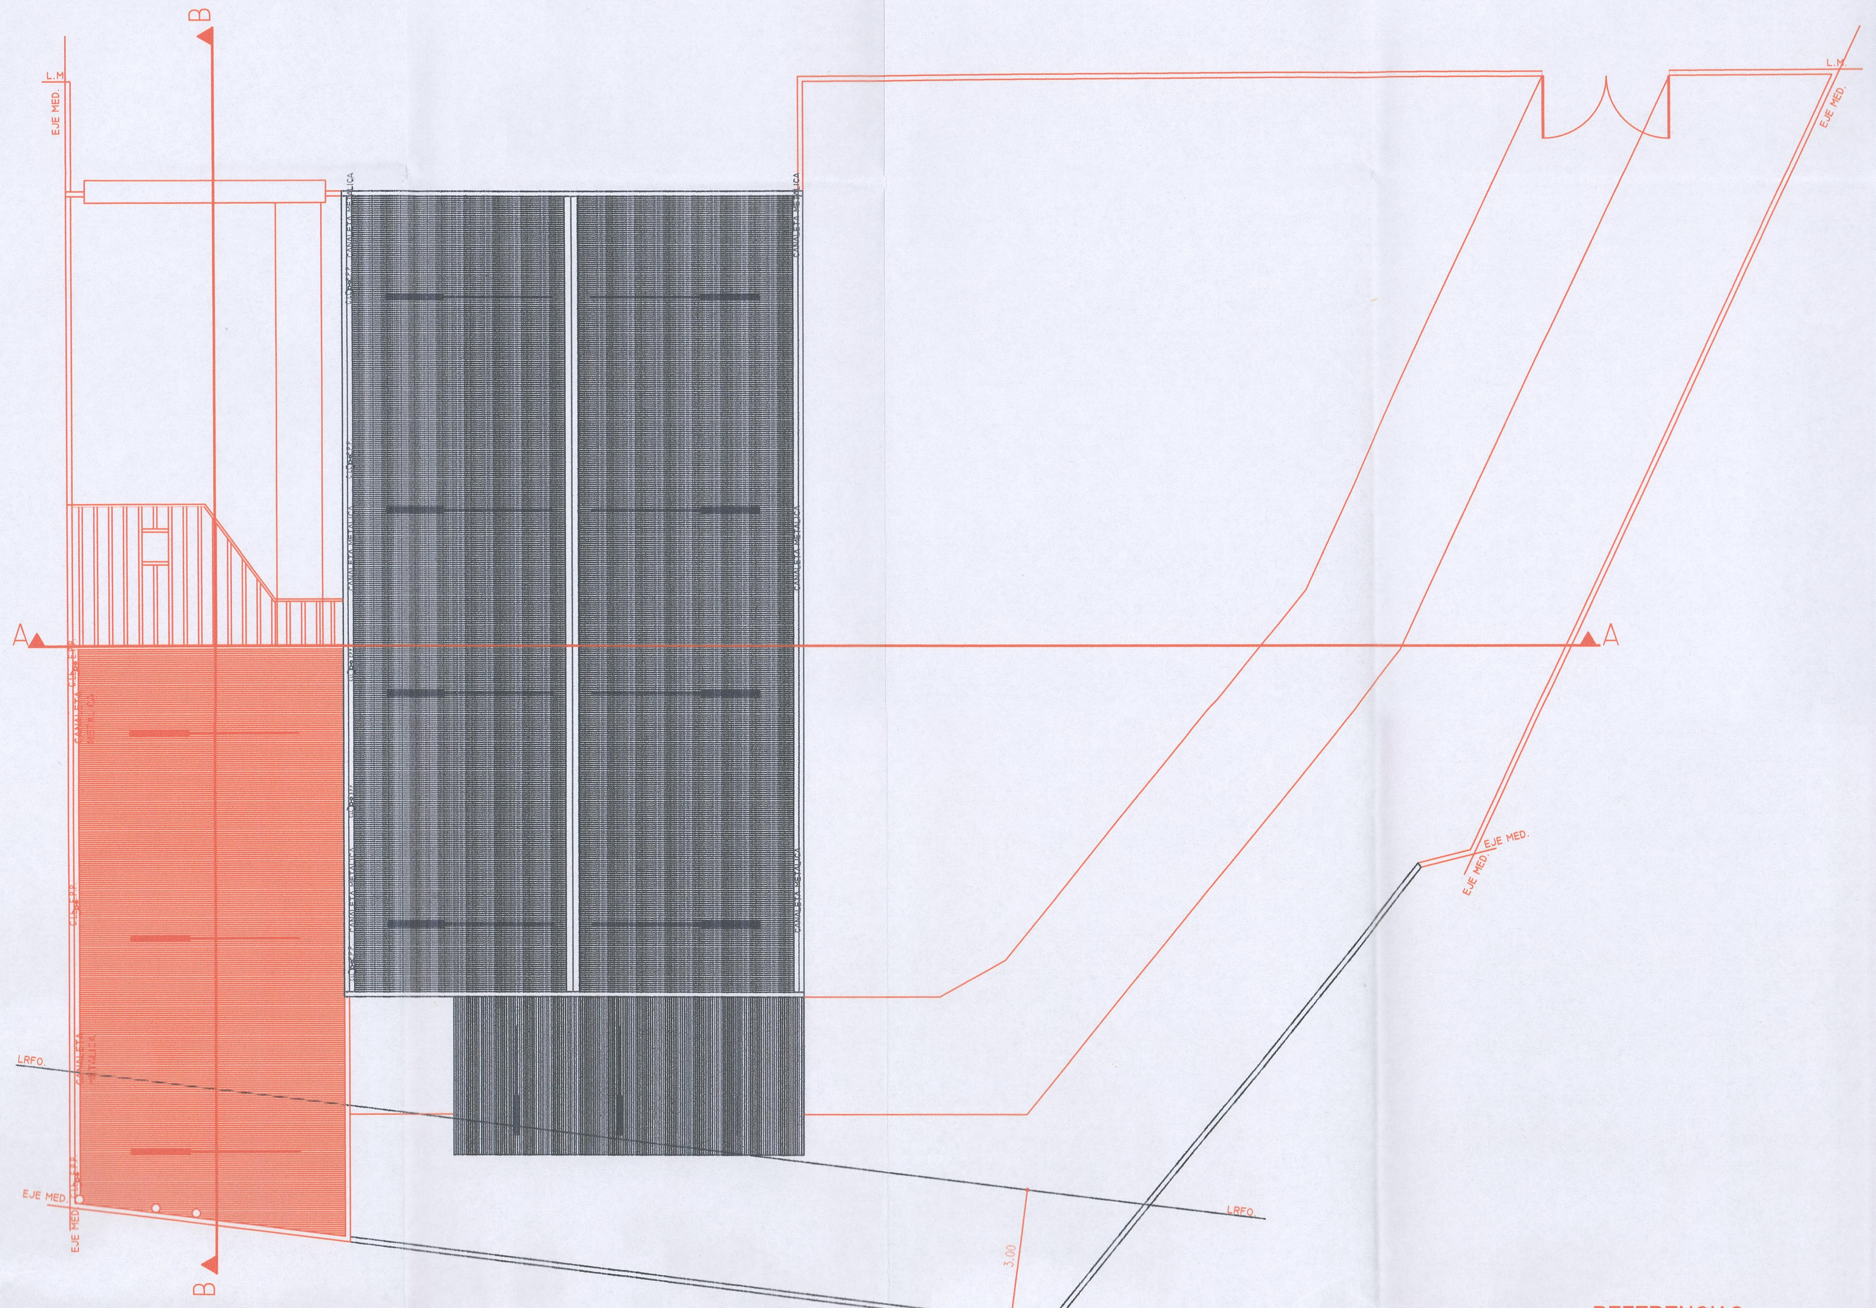

PLANTA DE TECHOS ESC. 1:200

FACHADA

CORTE A-A

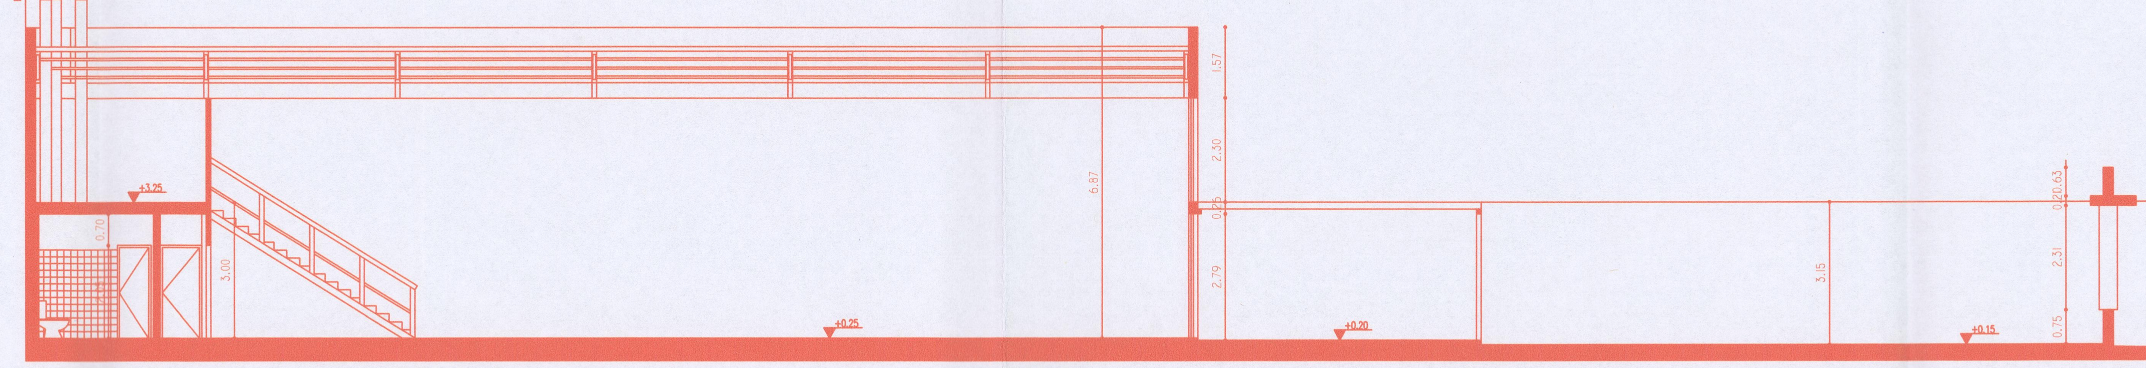

CORTE B-B

PLANILLA DE LOSAS DE VIGUETAS

Posición	Luz de Cálculo (m)	ANALISIS DE CARGA: Peso propio Kg/m2	Carga útil Kg/m2: Carga adic. perm.	Carga útil Kg/m2: Carga adic. perm.	Carga total Sobrec. reglam. Kg/m2	CARACTERISTICAS DE LA LOSA: Altura boved. (cm)	Espesor c.comp. (cm)	Espesor losa (cm)	Viguetas: Serie	Viguetas: Arm. (mm2)	Observaciones: Luces comerc. (m)	σb=170(Kg/cm2)H° σe=4.20(Tn/cm2)A°
L	4.00	260	100	200	560	12	5.00	17	B1	36	4.00	Losa con viguetas

COLUMNAS

POSICION	FORMA	Fb cm2	Fb d1	Fb d2	Fe cm2	Fe cant	Fe ø	Estribos Dobles ø	Estribos Dobles sep cm	Observaciones σb=170(Kg/cm2)Hormigon σe=4.20(Tn/cm2)Acero
C	□	400	20	20	4.52 2.01	4 4	12 8	6	15	

σt=1.00(Kg/cm2)Suelo
σb=170.00(Kg/cm2)Hormigon
σe=4.20(Tn/cm2)Acero

PLANILLA DE FUNDACIONES

DESIG.	FORMA	LUZ m.	DIMENSIONES do cm	h cm	bo cm	Platea Sup. ø	Platea Sup. sep.	Platea Inf. ø	Platea Inf. sep.	Fe (Y) Sup. N°	Fe (Y) Sup. ø	Fe (Y) Inf. N°	Fe (Y) Inf. ø	Estribos ø mm	Estribos Sep. cm	OBSERV.
VF	∟	p/m	100	95	45	6	30	8	20	4	12	4	12	6	10	Viga de Fundación.

VIGAS

DESIG.	FORMA	LUZ m.	DIMENSIONES do cm	h cm	bo cm	d cm	Fe TRAMO Inf. N°	Inf. ø	Sup. N°	Sup. ø	Fe APOYO Sup. N°	Sup. ø	Inf. N°	Inf. ø	ESTRIBOS ø mm	Sep. cm	OBSERV. σb=170(Kg/cm2)H° σe=4.20(Tn/cm2)A°
V1	□	p/m	45	43	15	–	4	12	3	12	3	12	4	12	6	8	Δ Δ
VE	□	p/m	20	18	15	–	3	12	3	12	3	12	3	12	6	8	Δ Δ

UNA FORMA DE EJECUCION DE PUESTA A TIERRA

REFERENCIAS

SIG.	DESIGNACIONES
	MEDIDOR
	TABLERO GENERAL
	TABLERO SECUNDARIO
	TOMA A TIERRA
	CENTRO DE LUZ
	BRAZO DE LUZ
	TOMA CORRIENTE
	LLAVE Y TOMA
	LLAVE DE 1 PUNTO
	LLAVE DE COMBINACION
	PULSADOR
	CAMPANILLA PARA TIMBRE

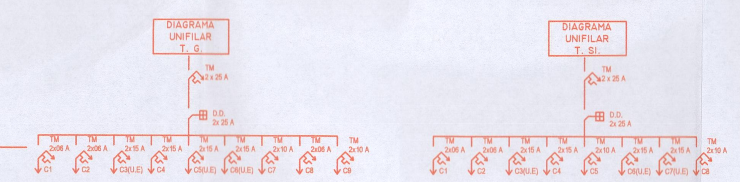

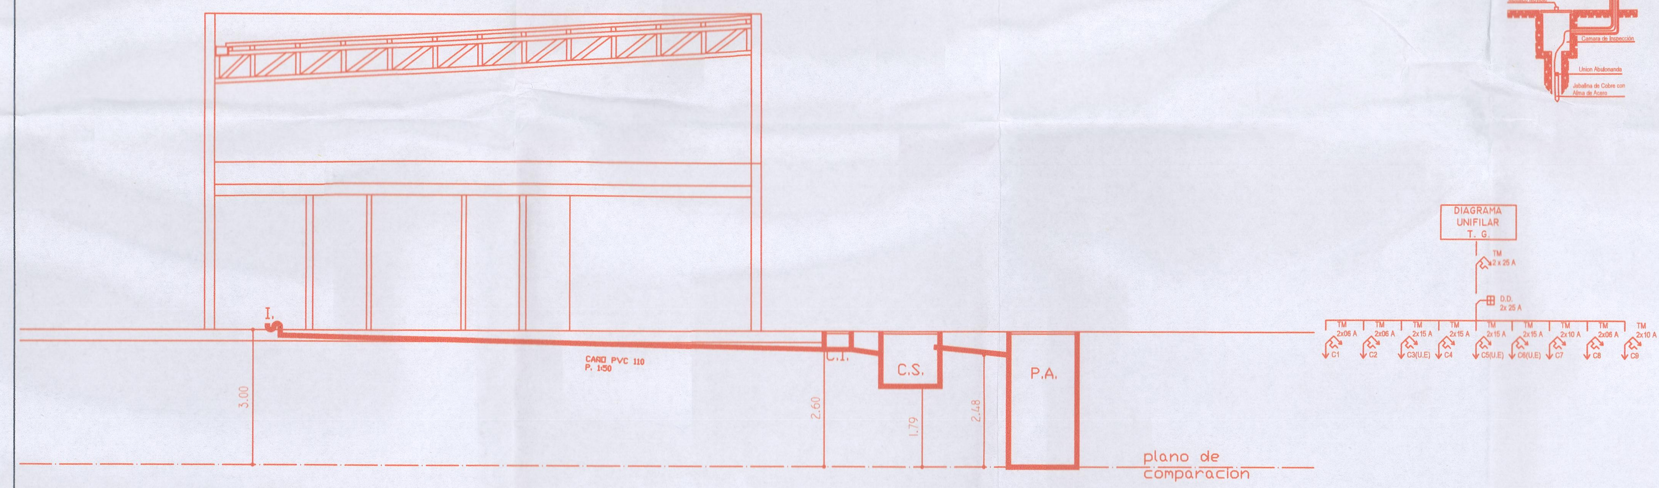

CORTE INST. SANITARIA

PLANILLA DE CARGA

NIVEL	TABLERO	CIRCUIT.	BOCAS LUZ 20W	BOCAS TOMAS 200W	BOCAS TOMAS U.E	POTENCIA LUZ	POTENCIA TOMAS	POTENCIA TOTAL(W)	CORRIENTE TOTAL(A)	PROTECC. TERMOMAG (A)	INTERRUP. DIFERENC. (A)
PLANTA BAJA	T.G.	C1	7			140		140	0.63	06	25
		C2	7			140		140	0.63	06	
		C3			1		1000	1000	4.54	15	
		C4		5		1000		1000	4.54	15	
		C5			1		1000	1000	4.54	15	
		C6			1		1000	1000	4.54	15	
		C7	10			200		200	0.90	10	
		C8	3			60		60	0.27	06	
		C9	13			260		260	1.18	10	
	SECC. I	C1	3			60		60	0.27	06	25
		C2	6			120		120	0.54	06	
		C3			1		1000	1000	4.54	15	
		C4		6			1200	1200	5.45	15	
		C5	11	2		220	400	620	2.81	10	
		C6			1		1000	1000	4.54	15	
PA		C7			1		1000	1000	4.54	15	
		C8	3	2		60	400	460	2.09	10	

POTENCIA TOTAL 10260
POT. SIMULT 60% 6156

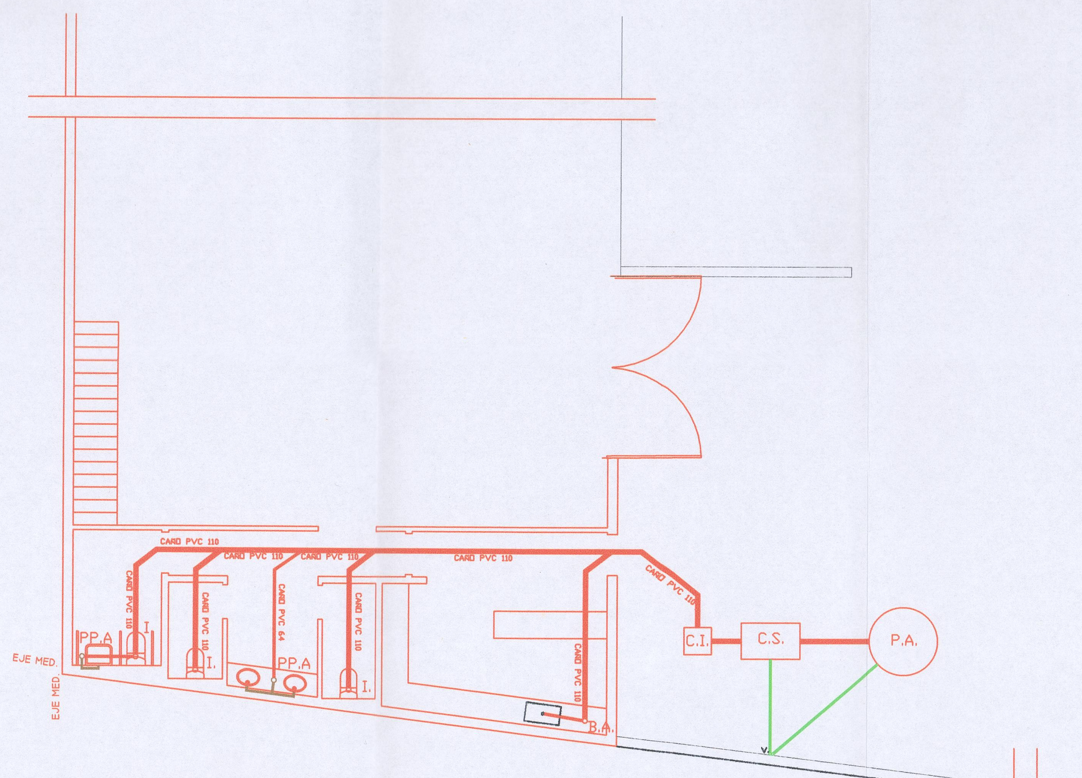

INSTALACION SANITARIA

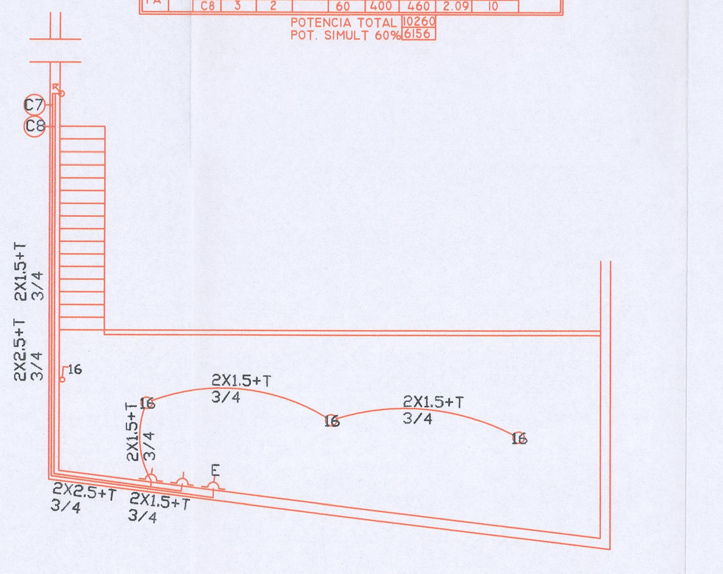

INSTALACION ELECTRICA PLANTA ALTA

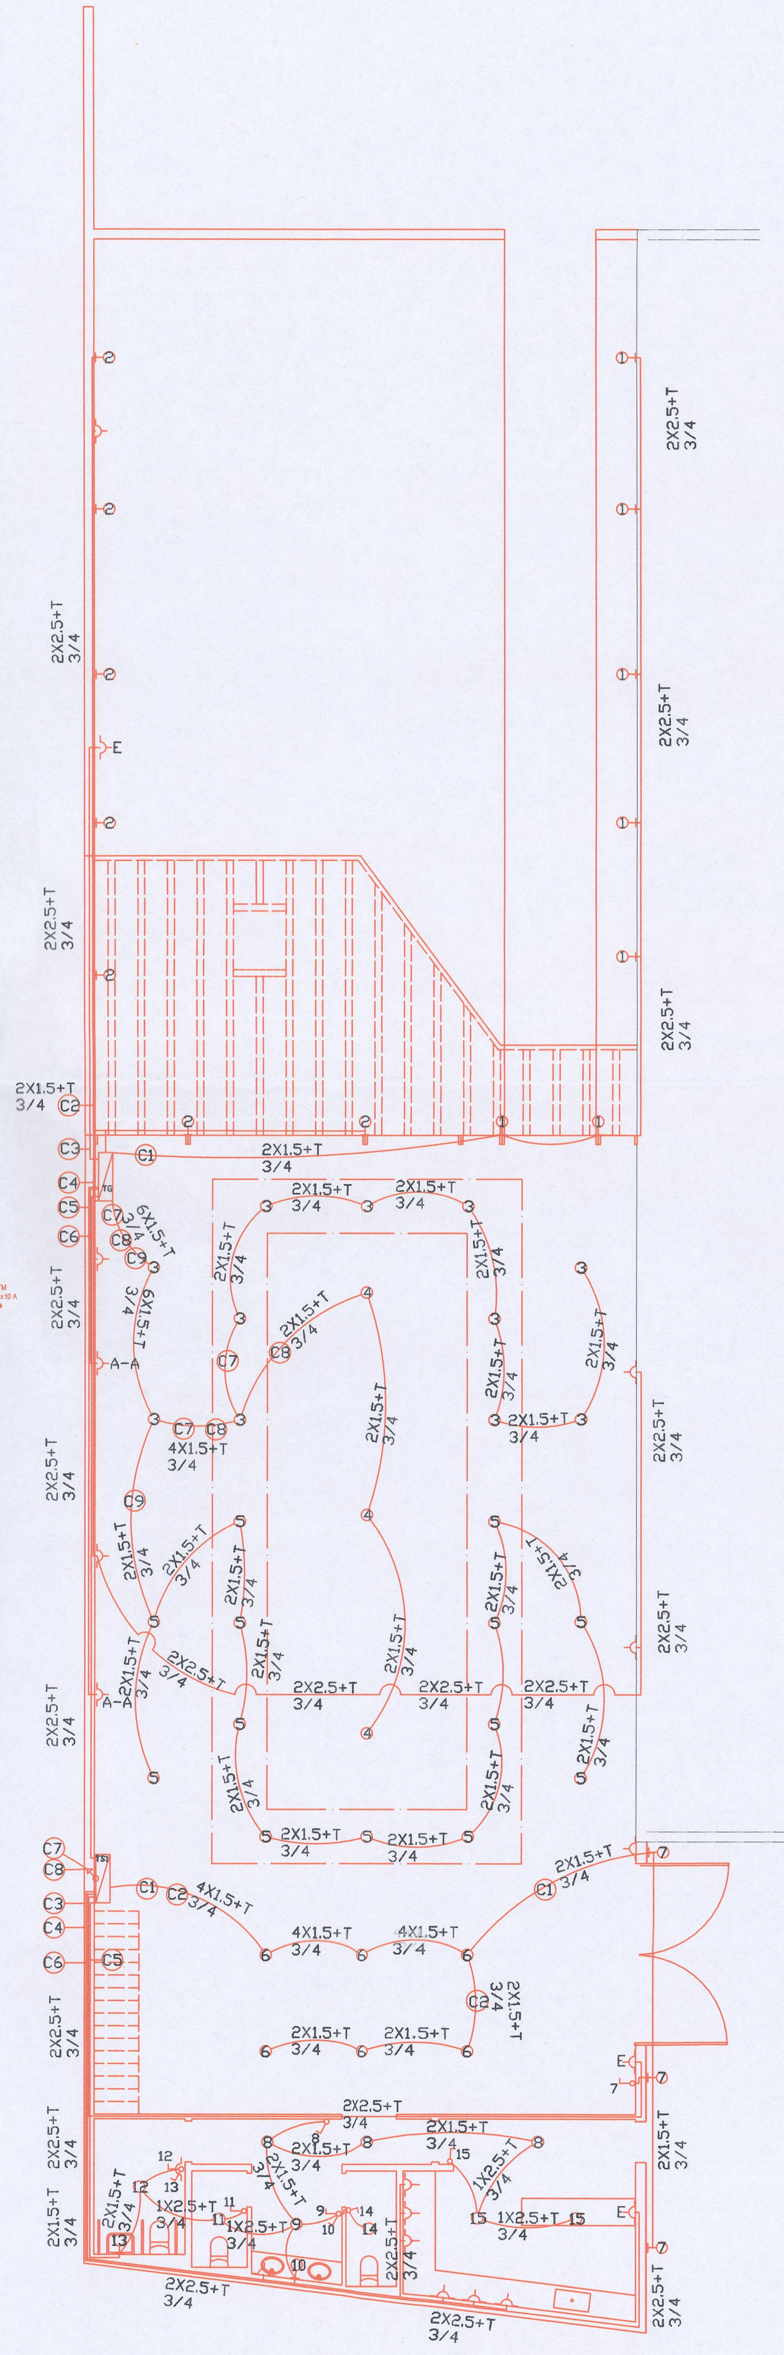

INSTALACION ELECTRICA PLANTA BAJA

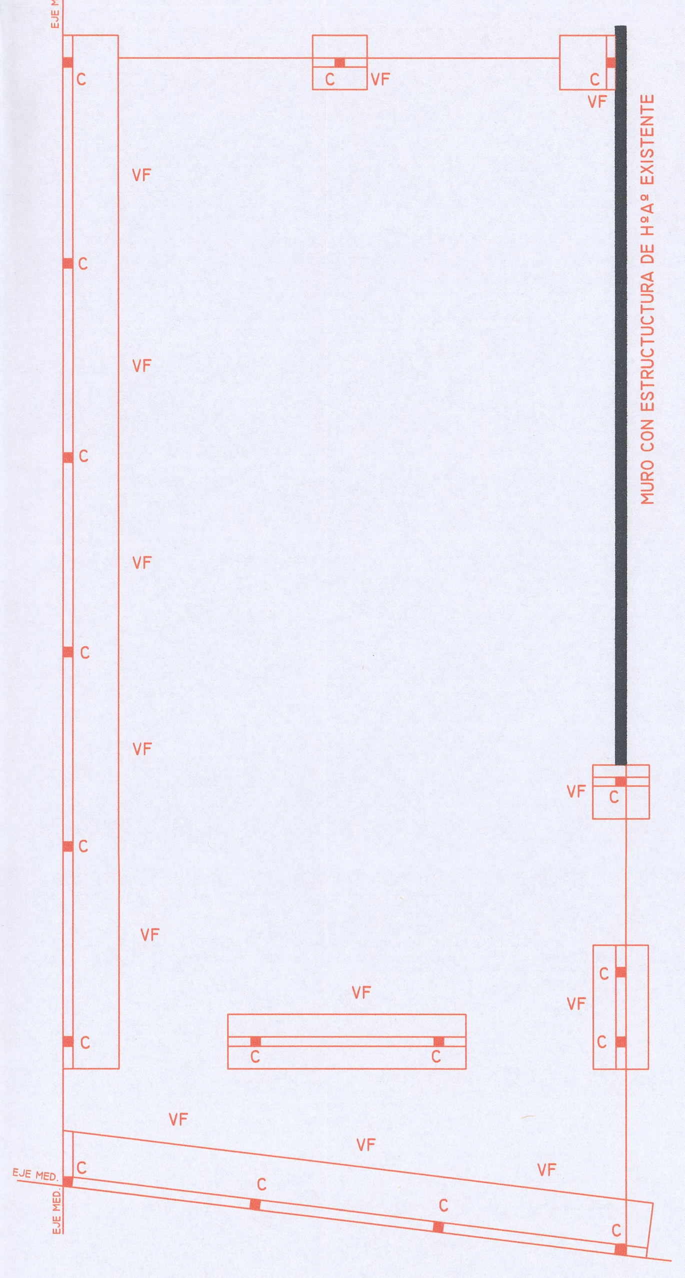

ESTRUCTURA DE FUNDACIONES

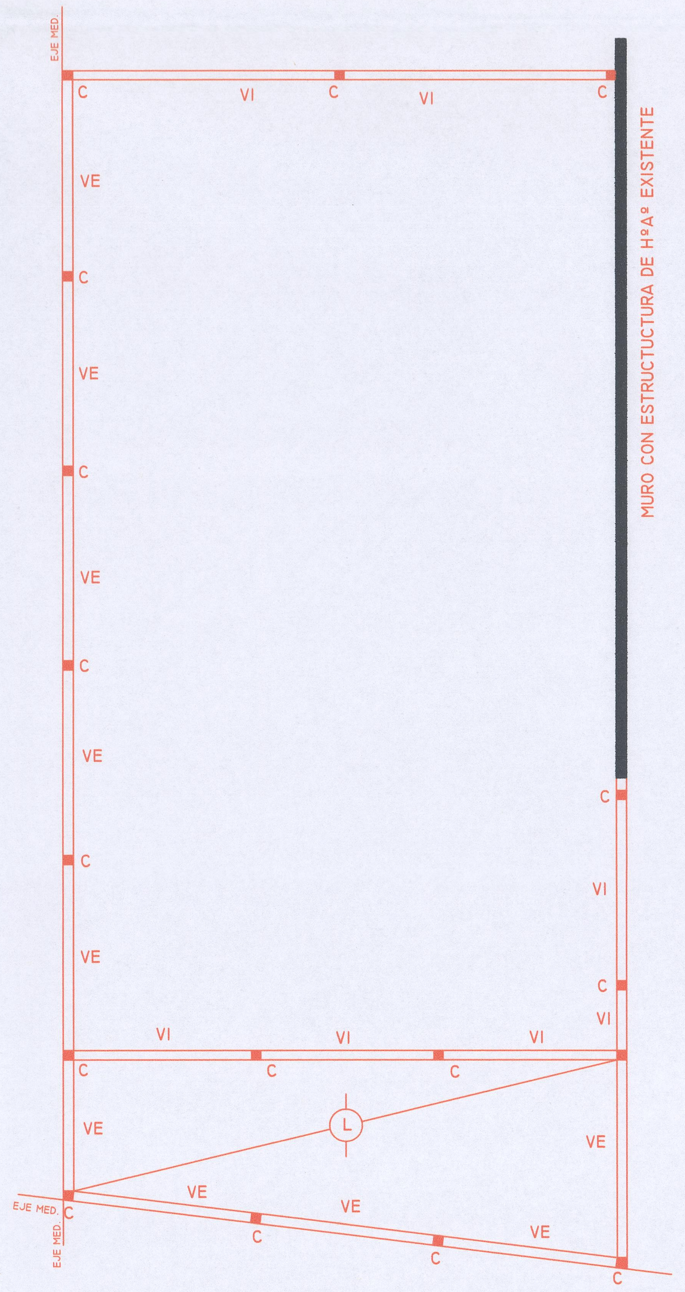

ESTRUCTURA DE ENTREPISO

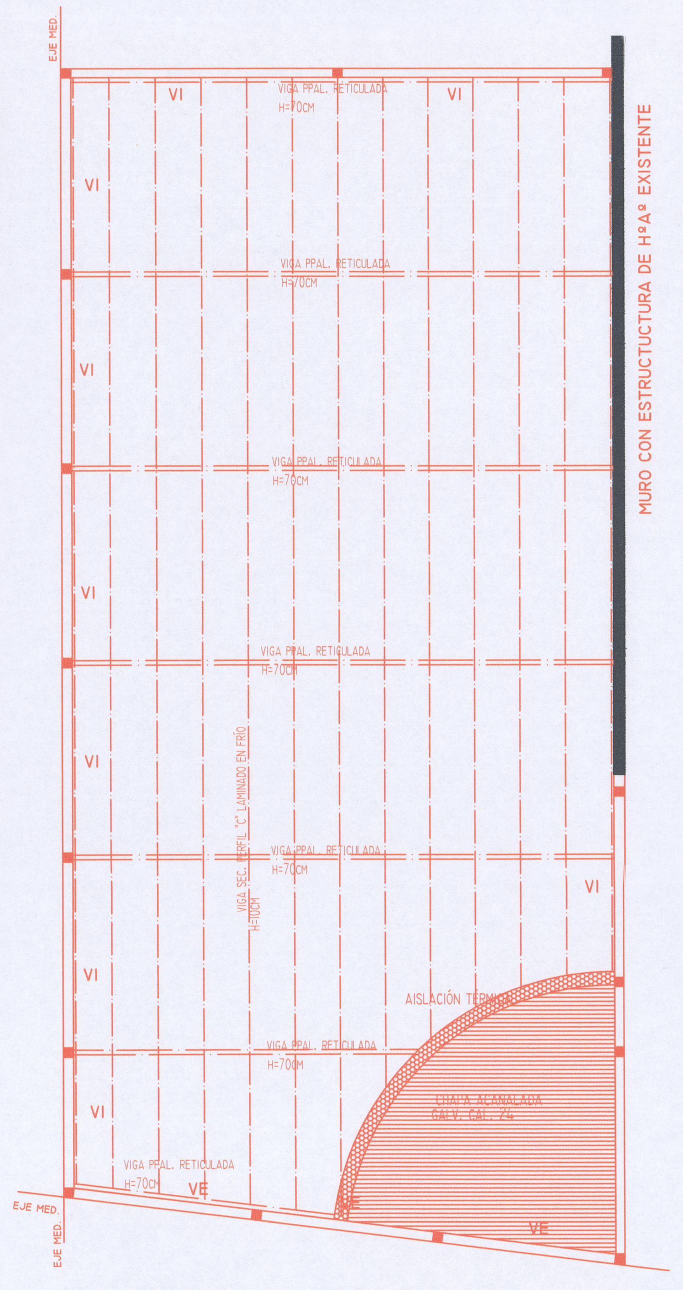

ESTRUCTURA DE CUBIERTA METALICA

DISTRITO 06	ZONA I	MANZANA 076	PARCELA 0222	LEY 4683
PADRÓN INMOBILIARIO 01-3-01375	DOMINIO: 7S-007295 ICM			24030358

DESTINO DE LA OBRA: SALONES COMERCIALES (2) Y DEPOSITOS

POSEEDOR: TRAJTENBERG, JUAN MARTIN DNI N° 31.729.268,
CUIL N° 20-31.729.268-7

TESTIMONIO DE CESION A FAVOR DE JUAN MARTIN TRAJTENBERG ANTE EL NOTARIO GUSTAVO MARTIN CURET ADSCRIPTO AL REGISTRO NOTARIAL Nº 55

UBICACIÓN: CALLE GOB.LAMI VIEYRA N° 535

BARRIO: ALMIRANTE BROWN

CIUDAD: SANTIAGO DEL ESTERO (CAPITAL)

ESCALAS: 1:100 1:500 1:200

SUP. DEL TERRENO	3.416,89M2 S/HE S/P.
SUP. DE RELEVAMIENTO	900,75 M2
SUP. DE AMPLIACION PLANTA BAJA	359,05 M2
SUP.DE AMPLIACION PLANTA ENTREPISO (H° A°)	45,63 M2
SUP. CUBIERTA TOTAL	1.305,43 M2

CROQUIS DE UBICACION

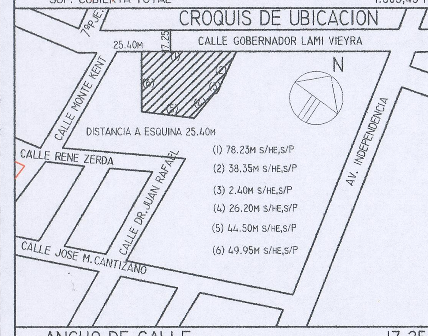

POSEEDOR
DOMICILIO

RELEVAMIENTO
DOMICILIO

PROYECTO
DOMICILIO

ELECTRICIDAD
DOMICILIO

DIRECCIÓN TÉCNICA
DOMICILIO

CATEGORÍA
PAVIMENTO SI
SERVICIOS CLOACALES NO

ANCHO DE CALLE	17.25M
ANCHO DE VEREDA	3.50M
ANCHO DE CALZADA	8.00M

DESIGNACIÓN: PLANO DE RELEVAMIENTO Y AMPLIACION INSTALACIONES, ESTRUCTURA Y PLANTA DE TECHOS

OBSERVACIONES: 01 JUL 2024

Las referencias al Titulo de dominio son meramente indicativas y la aprobación administrativa no valida los derechos que de ellos emergen.

PERMISO DE COMIENZO DE OBRA N° 106/2024 02/08/2024 DIRECCION DE SUELO URBANO

PROYECTO Y DIRECCIÓN DE OBRA 14 JUN. 2024

COLEGIO DE ARQUITECTOS LEY 5654/8

SUSANA ABECASSIS Arquitecta Secretaría Técnica Colegio de Arquitectos SDE

DIRECCIÓN DE SUELO URBANO EXPEDIENTE 319/31/24 FECHA DE SELLADO 27 SEP. 2024 BOLETA N° 9858

DIRECCIÓN DE SUELO URBANO EXPEDIENTE 319/31/24 FECHA DE SELLADO 27 JUN. 2024 BOLETA N° 9695

SECRETARIA DE ECONOMIA Municipalidad de la Capital SGO. DEL ESTERO DIREC. DE SUELO URBANO

MUNICIPALIDAD DE LA CIUDAD DE SANTIAGO DEL ESTERO
SECRETARIA DE ECONOMIA
APROBADO
DIRECCIÓN DE SUELO URBANO
EXPEDIENTE: 319-31-2024-C-P-03-T-2024
FECHA: 10 OCT 2024

Ing. Agrim. JUAN JOSE FRIAS
DIRECTOR
DIRECCION DE CATASTRO
MUNICIPALIDAD DE SGO. DEL ESTERO

Arq. ABRAHAM BERNARDO ROMINA
Dpto. OBRAS PRIVADAS
DIRECCION DE SUELO URBANO

Arq. BERNARDO L. M. SANTILLAN
DIRECTOR
DIRECCION DE SUELO URBANO
MUNICIPALIDAD DE SGO. DEL ESTERO