

PANEL DE CARGAS ELÉCTRICAS											
TAB.	LÍNEA	BOXES		POTENCIA		POTENCIA		CORRIENTE TOTAL A	PROTECCIÓN TIPO	PROTECCIÓN DIFERENCIAL	
		160V	200V	W	VA	W	VA				
91	1	3	3	180	1300	780	3,35	2 x 2,0 A			
	2	3	3	180	1300	780	3,37	2 x 2,0 A			
	3	3	3	180	1300	780	3,37	2 x 2,0 A			
	4	3	3	180	1300	780	3,37	2 x 2,0 A			
	5	6	1	360	1000	700	2,94	2 x 2,0 A		2 x 40 A	
	6	1	1	60	650	650	2,95	2 x 2,0 A			
91	1	4	1	340	1500	1500	7,07	2 x 2,0 A			
	2	3	5	540	1000	700	2 x 2,0 A	2 x 2,0 A			
	3	2	6	320	1000	1320	6,00	2 x 2,0 A			
	4	3	5	540	1000	1320	6,00	2 x 2,0 A			
	5	3	5	540	1000	1320	6,00	2 x 2,0 A		2 x 40 A	
	6	1	1	60	650	650	2,95	2 x 2,0 A			
TOTALS									13800	62,98	
INTERSECCIÓN SUMATORIA (0,08)									37,72		

[illegible]

Planilla de Iluminación y Ventilación:

Designación del local	Sup. m ²	ABERTURAS				
		Disig	Ancho	Alto	Áreas	
						V

PIANTA BAIADA

[illegible]

DIST.: 02	ZONA.: 06	MANZ.: 060	PARC.: 132
PADRÓN INMOB.: 01-1-147689			I.C.M.: 607-T-2021
DOMINIO: 7S-35.914			LEY 4683

DEST. DE LA OBRA : VIVIENDA FAMILIAR

PROPIETARIOS:
TSANG, SEBASTIAN
 DNI.: 26.398.057 - C.U.I.L. 20.26338057-4
CORREA, MARIA VALERIA
 DNI.: 38.274.810 - C.U.I.L. 97.98724810-7

UBICACION:
AV. LOS LAPACHOS S/N°, CALLE PRIVADA DE
PASO COMÚN S/N° - LOTE 32

BARRIO: ALMIRANTE BROWN
CIUDAD: SANTIAGO DEL ESTERO

ESCALA: 1 : 100 - 1 : 200

SUP. DE TERRENO:	607,26m ² s/T-s/he
SUP. CUBIERTA PLANTA BAJA	212,06 m ²

SOP. CUBIERTA PUNTA ALTA	119,35 m ²		
SUP. CUBIERTA TOTAL:	332,03 m ²		
CROQUIS DE UBICACION		AL CORTE	
		N	

PROYECTO DOMICILIO:
URBAN 21 11 21
CALLE IMPERIAL
ACIO

MANO PALA
MAGNOLIA
DIRECCION TECNICA
SELO
29
430

CALLE DON
 CALLE BARRIO DE SAN JOSE
 CALLE LAS
 DOMICILIO :

17:00 97-64% 12:00

32.32 19.96
11.220.00-3040 AV. LOS LAPACHOS
CALLE
50.00 AV. LOS LAPACHOS

AV. LOS LAPACHOS	C. PRIV. COM.	AV. LOS LAPACHOS	C. PRIV. COM.	AV. LOS LAPACHOS	C. PRIV. COM.
ANCHO DE CALLE :	12.00 m	50.00 m			
ANCHO DE VEREDA :	3.00 m	3.00 m			
ANCHO DE CALZADA :	5.00 m	4.00 m			
			PAVIMENTO :	SI	NO
			SERVICIOS CLOACALES :	NO	NO

ANCHO DE CALZADA :	6,00 m	4,00 m
DESIGNACION : PIANO GENERAL		

ARQUITECTURA Y ELECTRICIDAD

son meramente-indicativas, y la

aprobación administrativa no valora
los derechos que de ellos emanan.

21 MAR 2022

PERM DE OB
DIRECC


Ing. Aguirre, JOSE PRIMO
DIRECTOR

DIRECCION DE CATASTRO
MUNICIPALIDAD DE SANTIAGO


Ag. Bravo, Ma. Esther
COORDINADORA GENERAL

Ag. BERNABE, M. SANTILLAN
DIRECTOR
DIRECCION DE SUELO URBANO
MUNICIPALIDAD DE SANTIAGO


CHURCH PROPOSALS
DISCUSSIONS HELD URBANO

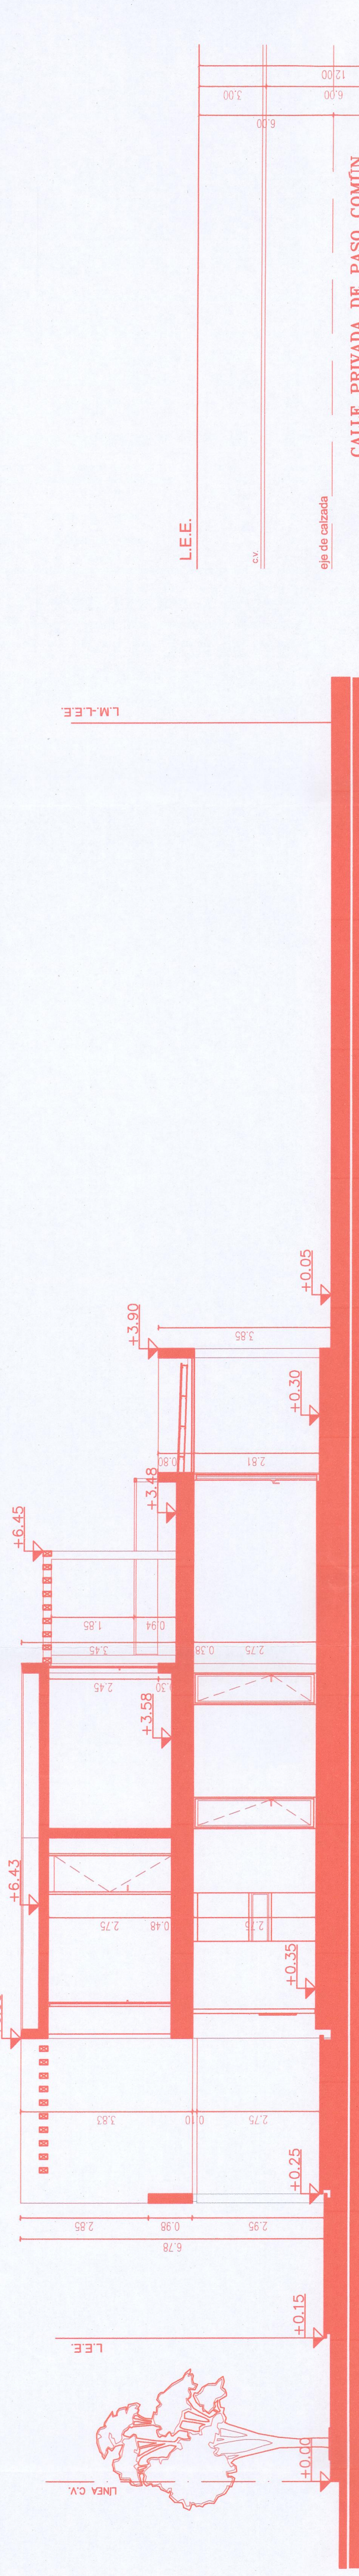


CORTE C-C

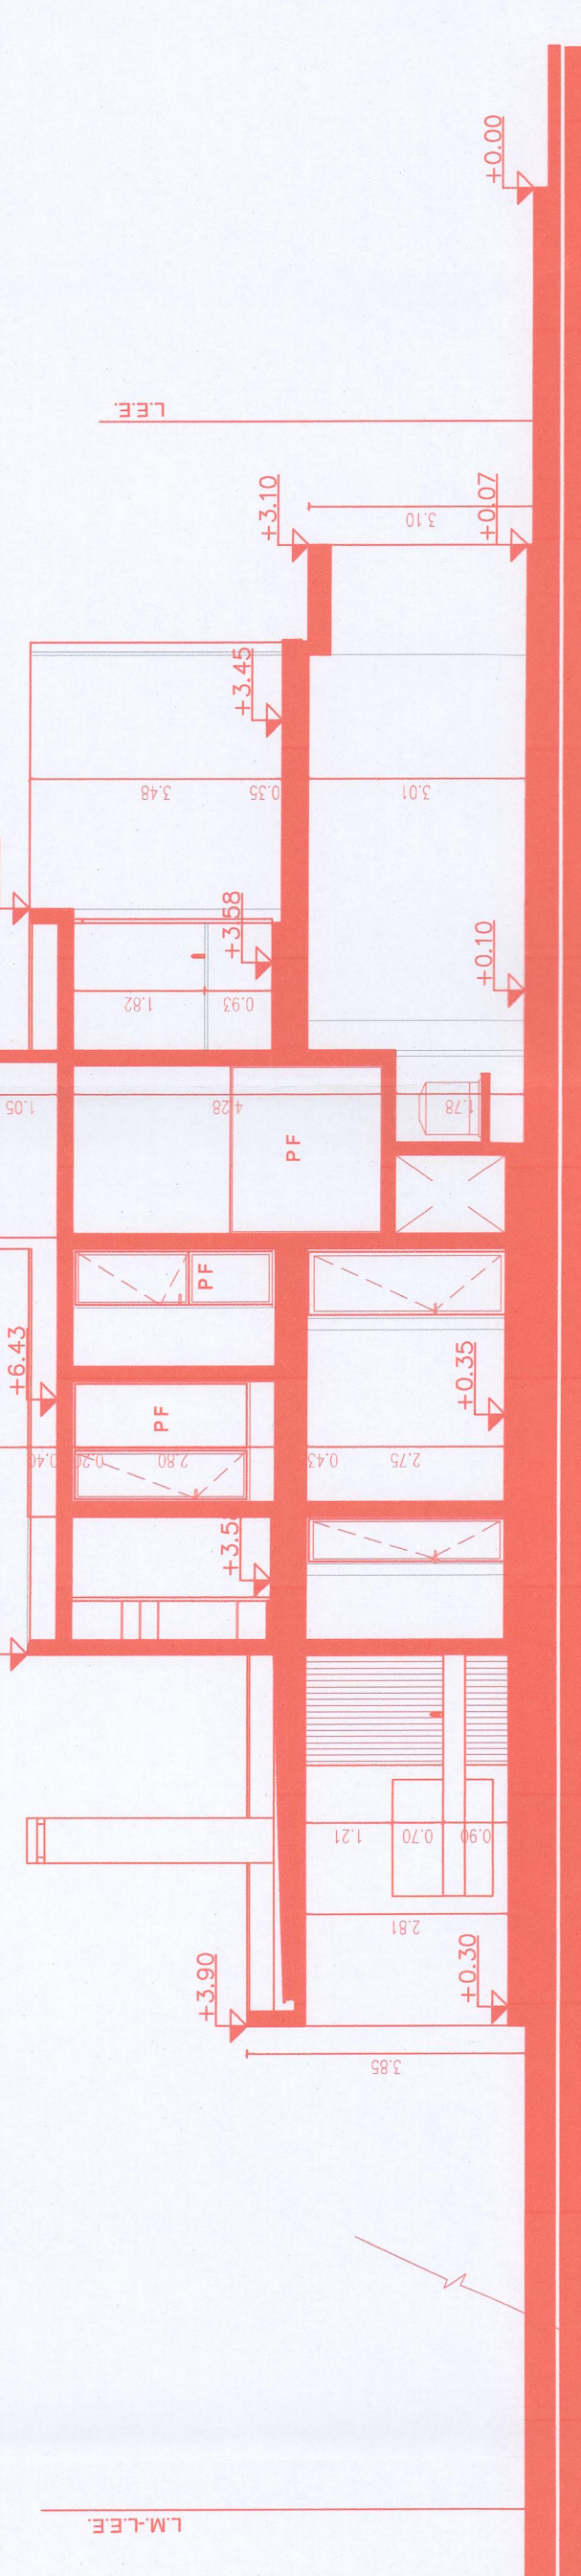

CORTE B-B

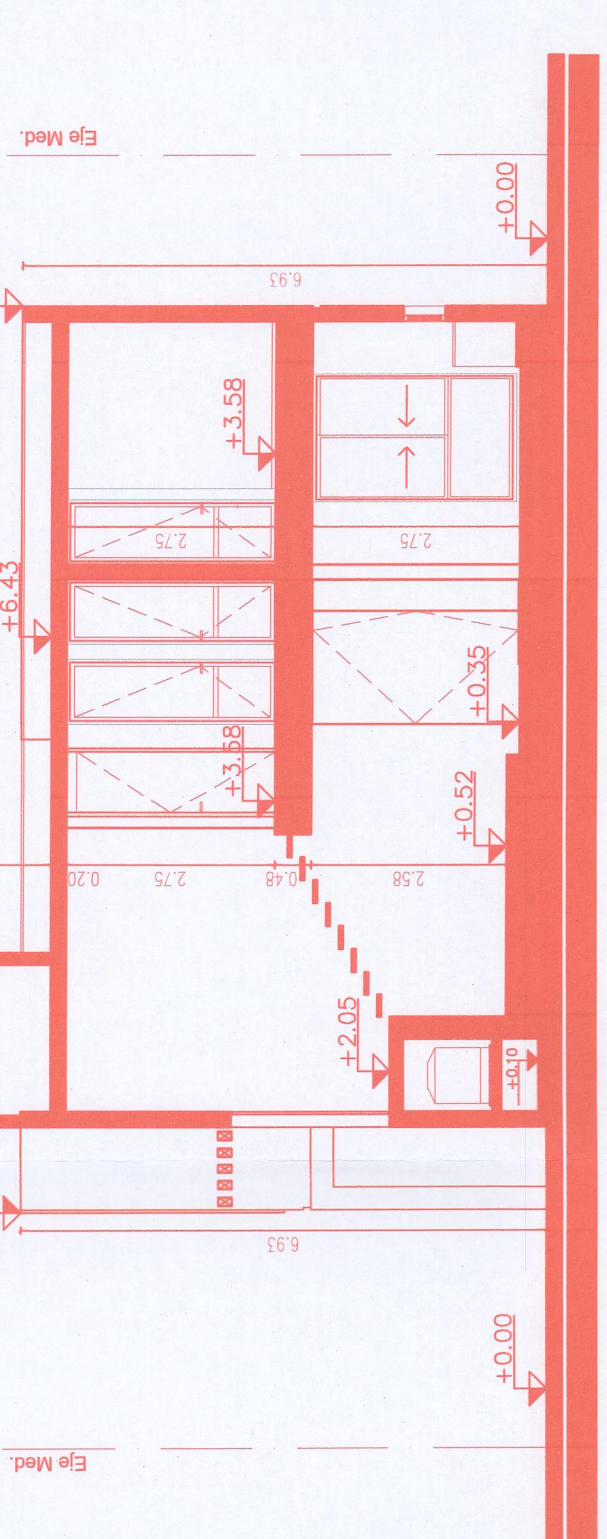

CORTE A-A

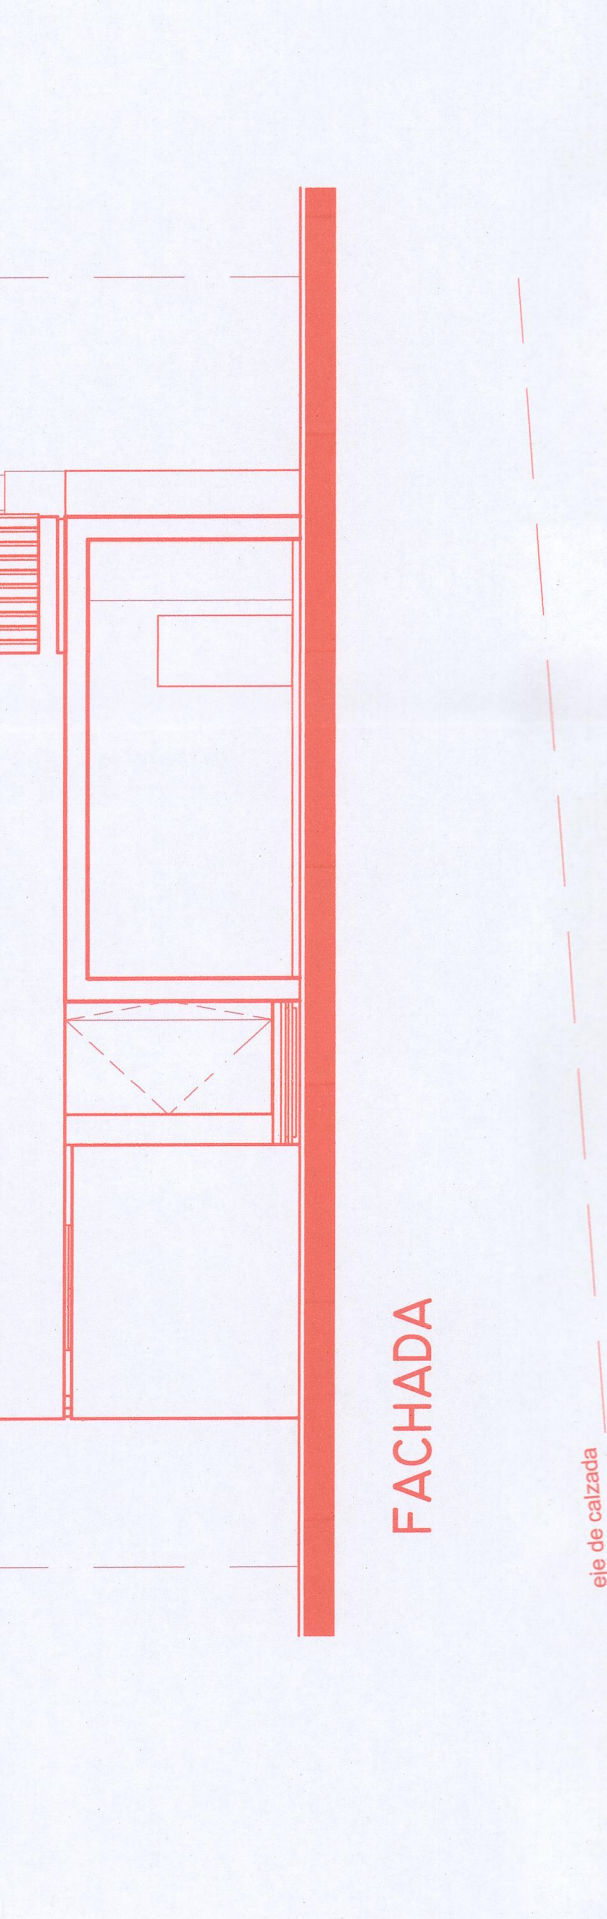

FACHADA





PIANTA ALTA DE EL ECTRICIDAD

PIANTA BAJA DE ELECTRICIDAD

PLANTA DE TECHOS

PLANTA ALTA

PLANTA BAJA

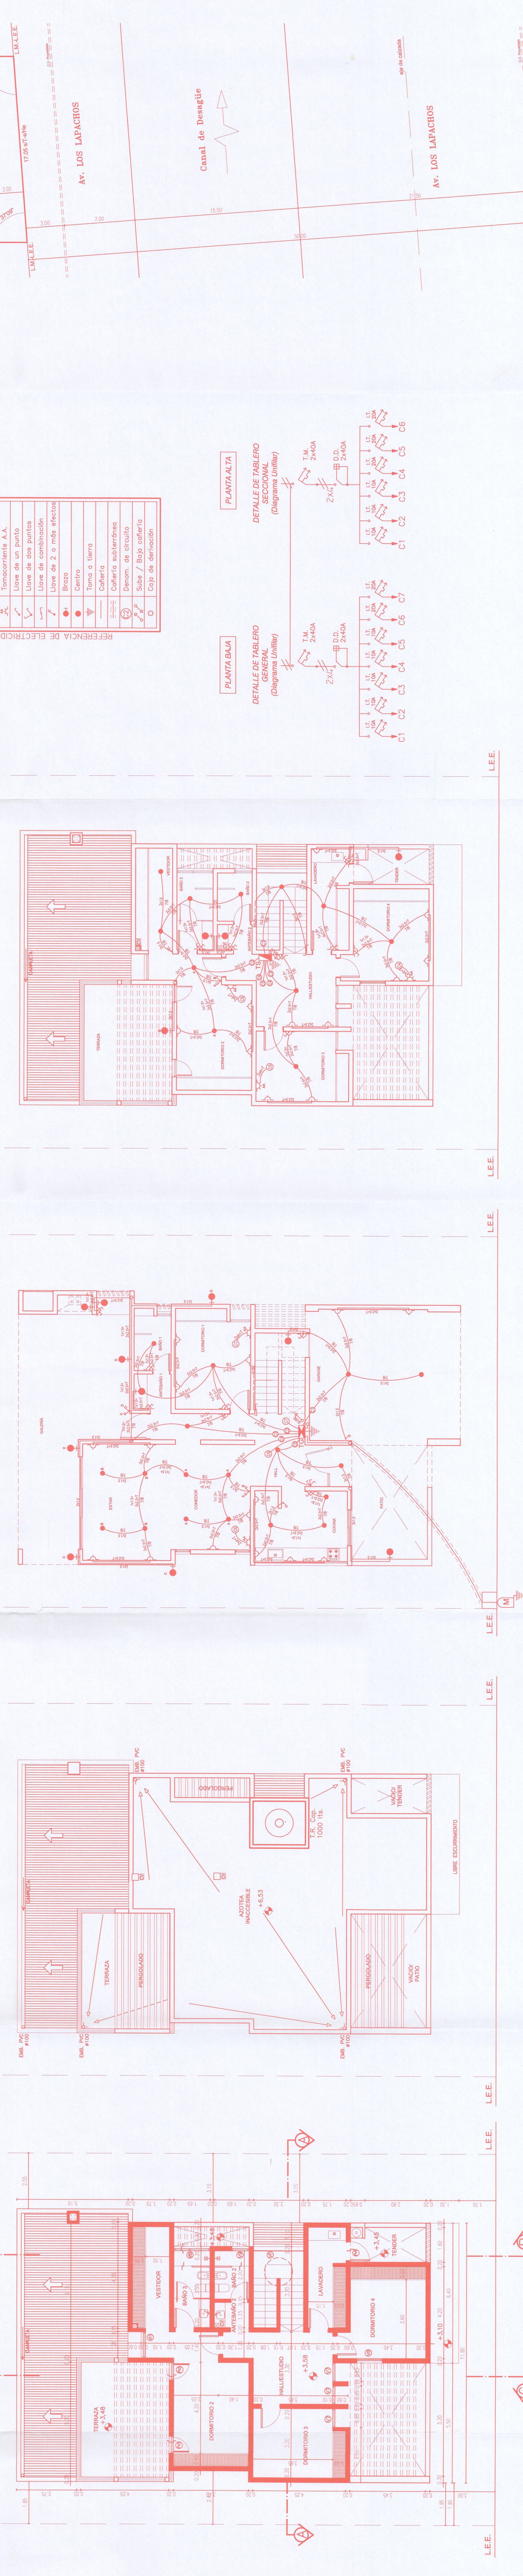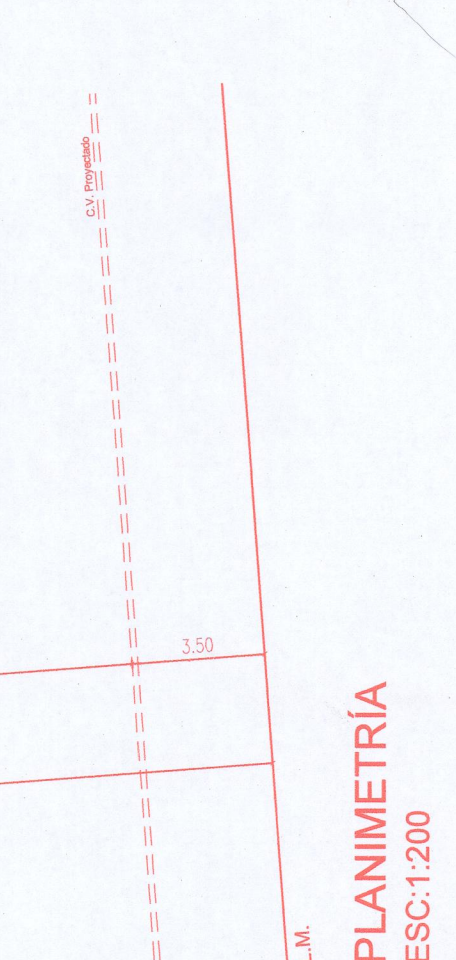[illegible]

PLANIMETRÍA