DETALLES COLUMNA METALICA

Anclaje para columna metalica columnas CM1:

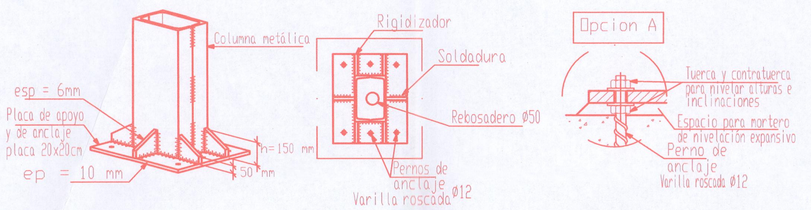

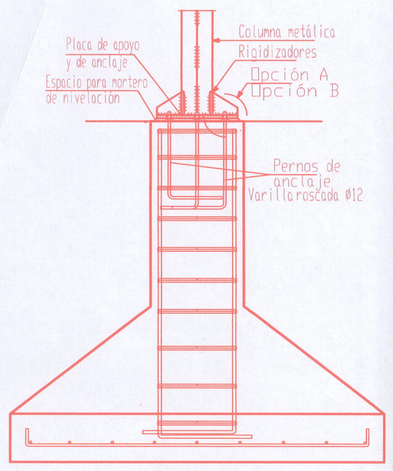

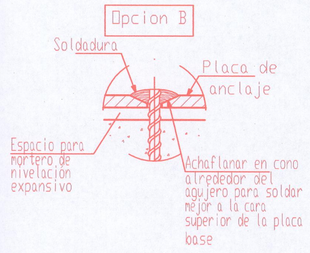

DETALLES DE DOBLADO

LOS ESTRIBOS SE CERRARÁN CON UN GANCHO DOBLADO A 135°

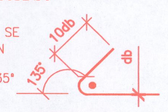

BARRAS CON GANCHOS DOBLADO A 180° | BARRAS CON GANCHOS DOBLADO A 90°

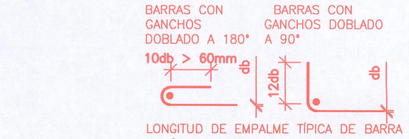

LONGITUD DE EMPALME TÍPICA DE BARRA SERÁ 60ø, SALVO SE ESPECIFIQUE LO CONTRARIO EN PLANOS Y DETALLES.

Materiales
.- Acero ADN - 420
.- Hormigón H-21

Longitud de anclaje mínima de barras 60 ø.
Los empalmes de barras longitudinales se realizarán de forma escalonada.

Todos los hierros longitudinales de vigas terminales debe finalizar en un gancho a 90º, indicado en el plano con un mínimo de 20 cm.

Los estribos se cerraran con un gancho doblado a 135° .

No se puede colocar caños de instalaciones eléctricas dentro de las vigas.

Separación entre estribos
.- Zona Normal = Según detalle de Columna (cm)
.- Zona Crítica = Separación Zona Normal / 2 (cm)

COLUMNAS

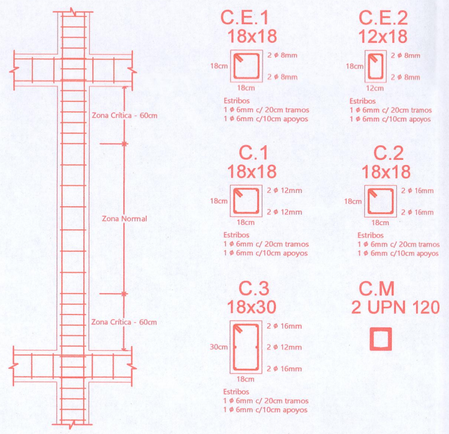

C.E.1 18x18
Estribos 1 ø 6mm c/ 20cm tramos 1 ø 6mm c/10cm apoyos

C.E.2 12x18
Estribos 1 ø 6mm c/ 20cm tramos 1 ø 6mm c/10cm apoyos

C.1 18x18
Estribos 1 ø 6mm c/ 20cm tramos 1 ø 6mm c/10cm apoyos

C.2 18x18
Estribos 1 ø 6mm c/ 20cm tramos 1 ø 6mm c/10cm apoyos

C.3 18x30
Estribos 1 ø 6mm c/ 20cm tramos 1 ø 6mm c/10cm apoyos

C.M 2 UPN 120

DETALLE DE CIMENTACION

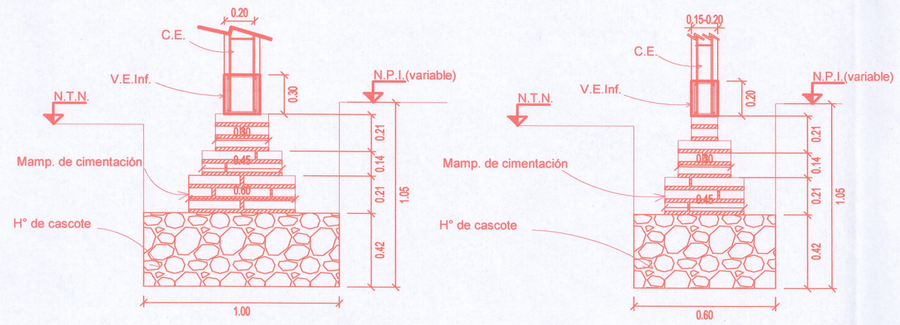

ESQUEMA VIGAS DE FUNDACION

VT1 0.20 x 0.25
Estribo 1Ø 6 c/10 cm en extremos
1Ø 6 c/20 cm en tramos
2Ø10
3Ø10

VF1 0.20 x 0.20
Estribo 1Ø 6 c/10 cm en extremos
1Ø 6 c/20 cm en tramos
2Ø10
2Ø10

VF2 0.20 x 0.30
Estribo 1Ø 6 c/10 cm en extremo
1Ø 6 c/20 cm en tramos
2Ø10
2Ø10

COTA DE FUNDACION:
- LA COTA ES UNA REFERENCIA, EN TODOS LOS CASOS SE DEBE LLEGAR AL MANTO PORTANTE, INDEPENDIENTEMENTE DE LA COTA

NOTA:
- LOS NIVELES INDICADOS SON DE PROYECTO.
- LAS MEDIDAS SE VERIFICARAN EN OBRA.

TENSIONES Y COTA DE FUNDACION HORMIGONES

G' bk= 170 kg/cm2
G' ek=4200 kg/cm2 (acero)
G' adm suelo= 0.50 kg/cm2
C.F. =tentativa= -1.00 m

REGLAMENTOS Y NORMAS DE APLICACIÓN:

- CIRSOC 201: Reglamento Argentino de Estructuras de Hormigón – Año 2005
- CIRSOC 103: Normas Argentinas para Construcciones Sismoresistentes. Tomos III – Año 1991.
- CIRSOC 101: Reglamento Argentino de Cargas Permanentes y Sobrecargas Mínimas de Diseño para Edificios y Otras Estructuras – Año 2005.

CARGAS CONSIDERADAS:

- Sobrecarga Accidental Indicada en cada caso.
- Peso hormigón armado: 2500 kg/m.3
- Peso Mampostería de ladrillo hueco portante con Revoque: 1200 kg/m.3

MATERIALES:

HORMIGÓN ARMADO
HORMIGÓN PARA COLUMNAS, VIGAS Y LOSAS H-20 (H-17 CIRSOC 1982)
HORMIGÓN PARA FUNDACIONES H-20 (H-17 CIRSOC 1982)

Cemento (suelo y agua sin sulfatos): Portland Normal
Cemento (suelo y agua con sulfatos): Portland ARS

ARMADURAS: BARRAS DE ACERO PARA HORMIGÓN ARMADO ADN-420
MALLAS DE ACERO ELECTROSOLDADAS ML-500

PERFILERÍA DE ACERO PARA ESTRUCTURA RESISTENTE:

CALIDAD MÍNIMA ACERO F-24 (Tensión de fluencia mínima = 2400 kg/cm2) según norma IRAM-IAS U 500-42 e IRAM-IAS U 500-503.

ELECTRODOS PARA SOLDADURA: E7018. (Realizada por un soldador profesional)

RECUBRIMIENTOS MÍNIMOS:

- CON AIRE: 2 cm
- CON AGUA: 3.5 cm
- CON SUELO: 5.0 cm

LONGITUDES DE EMPALMES MÍNIMAS:

- Barra ⌀8mm = 45cm
- Barra ⌀10mm = 55cm
- Barra ⌀12mm = 65cm
- Barra ⌀16mm = 95cm
- Barra ⌀20mm = 140cm
- Barra ⌀25mm = 170cm

RECOMENDACIONES GENERALES:

- El constructor deberá revisar la información recibida, reportar incongruencias, indicar situaciones de difícil ejecución e informar cambios que desee realizar a la dirección técnica.
- En caso de haber incongruencias vale la condición más rigurosa y debe informarse a la dirección técnica.
- Los planos representan el estado de la estructura terminada, siendo responsabilidad del constructor los medios para lograrla sin riesgos durante la construcción.
- En todo el proceso de montaje se deberá garantizar la estabilidad de las distintas partes que conforman la estructura.
- Es de vital importancia para evitar asentamientos diferenciales canalizar los conductos cloacales, pluviales y asegurar desniveles que alejen el agua de la construcción. Realizar veredas perimetrales, alejar cisternas, pozos absorbentes, cámaras sépticas y riego por aspersión de la obra. Tomar todos las medidas necesarias para mantener la humedad natural del suelo de fundación.
- Todas las medidas en los planos deberán verificarse en obra.
- Longitud de anclaje mínima de barras 60 ⌀.Los empalmes de barras longitudinales se realizarán de forma escalonada.
- Los estribos se cerraran con un gancho doblado a 135° .

Todos los hierros longitudinales de vigas terminales debe finalizar en un gancho a 90°, indicado en el plano con un mínimo de 20 cm.

RECOMENDACIONES DE FUNDACIONES

- Cota de fundación = -1.00 m
- La tensión admisible del suelo adoptada para este caso es de 0.50kg/cm²
- Evitar el aumento del contenido de humedad del estrato de apoyo ya que el mismo puede presentar inestabilidad ante dicho aumento.

ESQUEMA ARMADO BASES

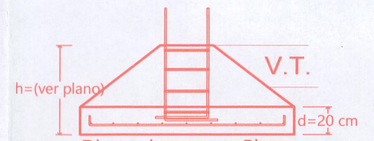

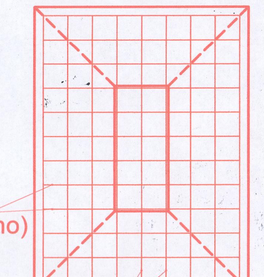

L.M.-L.E.E.

Eje Med.

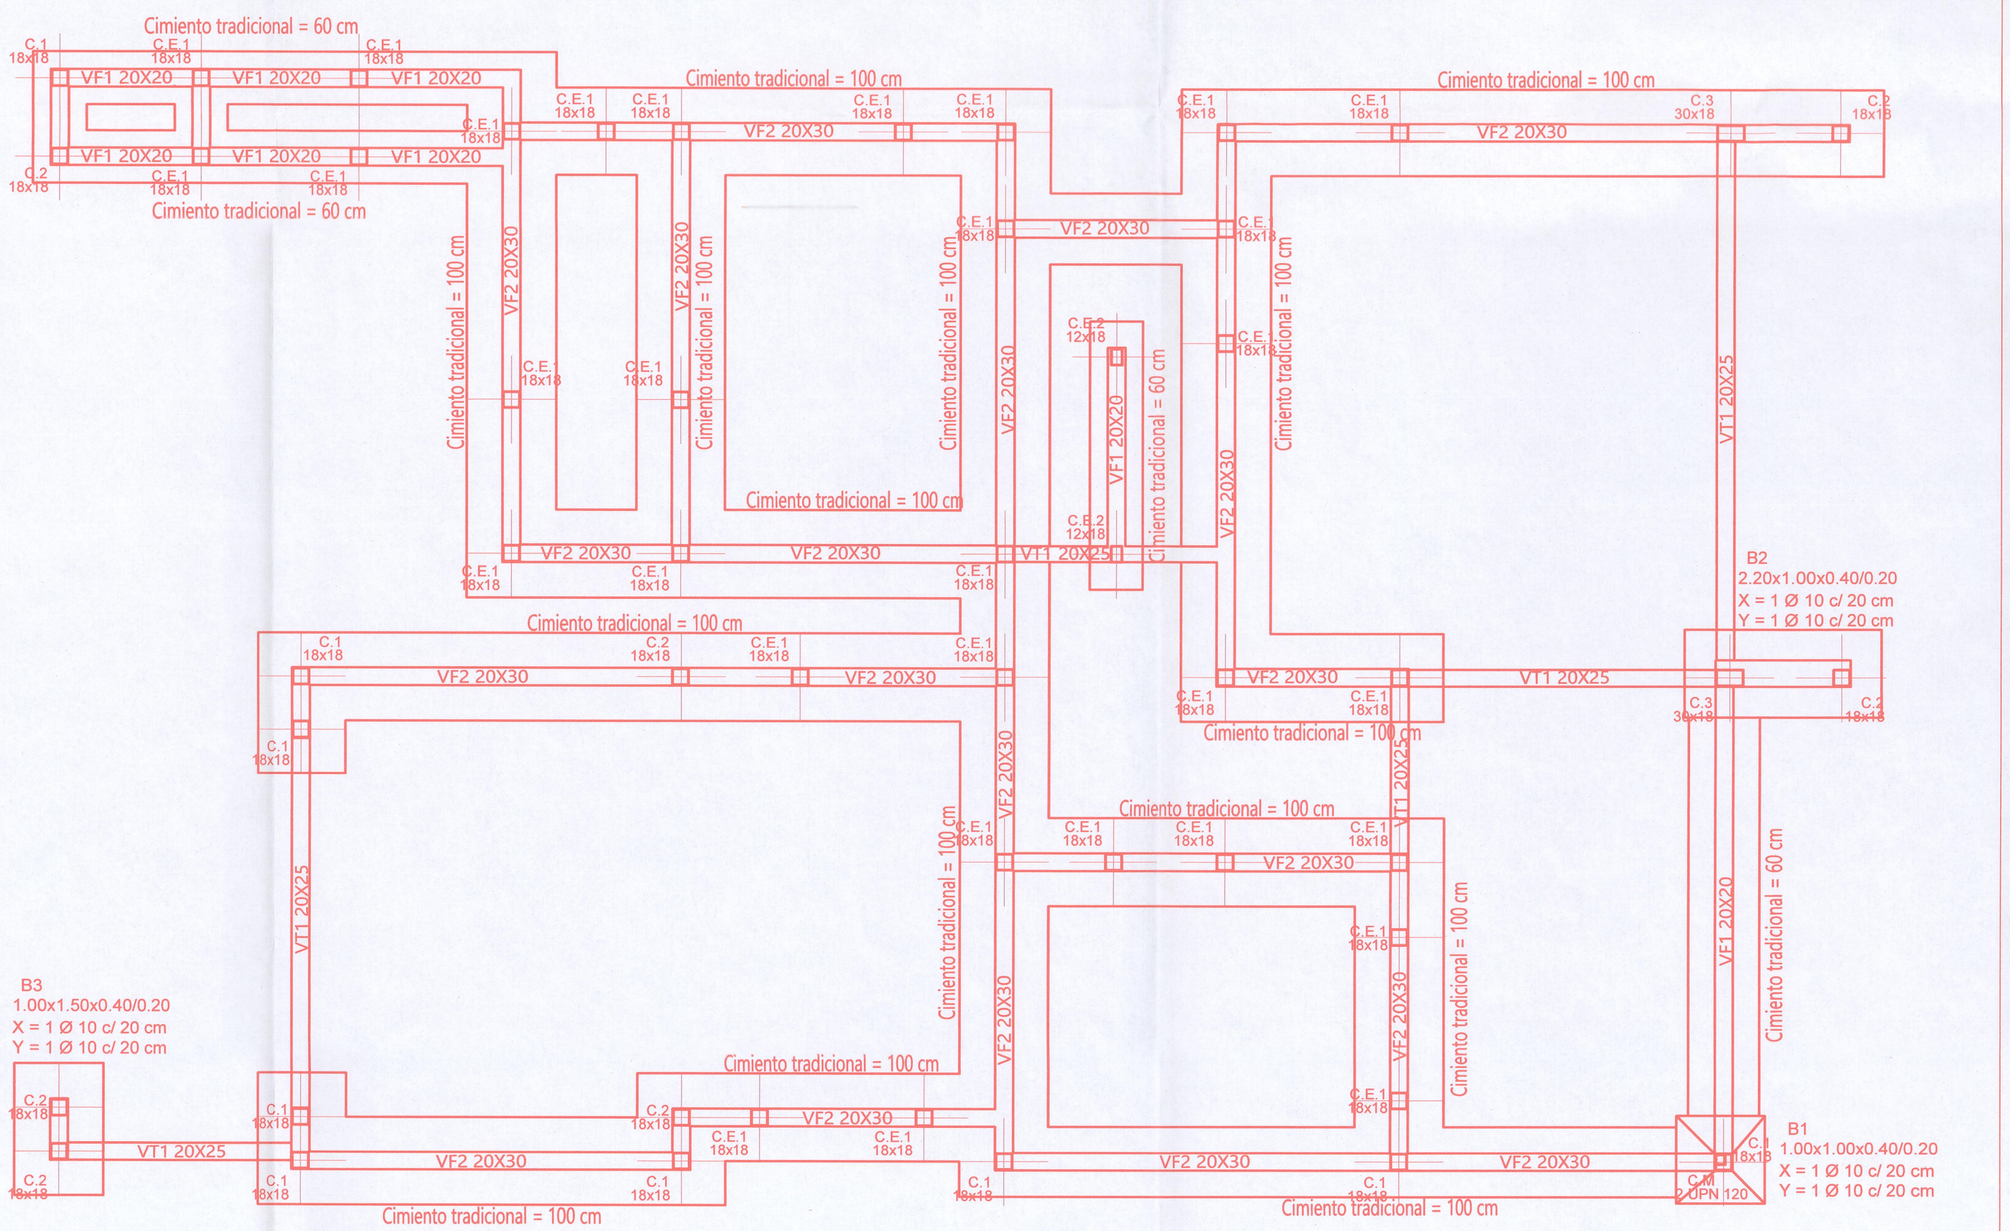

PLANTA DE FUNDACION

Eje Med.

L.M.-L.E.E.

L.E.E.

DIST.: 02 ZONA.: 06 MANZ.: 060 PARC.: 132

PADRÓN INMOB.: 01-1-147689 I.C.M.: 607-T-2021 DOMINIO: 7S-35.914

LEY 4683
211611

DEST. DE LA OBRA :VIVIENDA FAMILIAR

PROPIETARIOS: TSANG, SEBASTIAN
D.N.I.: 26.398.057 - CUIL 20-26398057-4
CORVERA, MARIA VALERIA
D.N.I.: 26.774.810 CUIL 27-26774810-7

UBICACION: AV. LOS LAPACHOS S/N°. CALLE PRIVADA DE PASO COMÚN S/N° - LOTE 32

BARRIO: ALMIRANTE BROWN

CIUDAD: SANTIAGO DEL ESTERO

ESCALA: 1 : 100 - 1 : 200

COLEGIO DE ARQUITECTOS DE LA PROVINCIA DEL ESTERO LEY 4683/87

PROYECTO Y DIRECCION DE OBRA
26 NOV. 2021
Arq. Eva Tuk Khairallah
SECRETARIA

SECRETARIA DE ECONOMIA
Municipalidad de la Capital SGO. DEL ESTERO
DIREC. DE SUELO URBANO

SUP. DE TERRENO:	607,26m2 s/T -s/he
SUP. CUBIERTA PLANTA BAJA	212,68 m2
SUP. CUBIERTA PLANTA ALTA	119,35 m2
SUP. CUBIERTA TOTAL :	332,03 m2

CROQUIS DE UBICACION

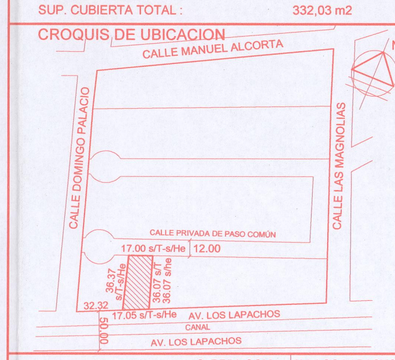

	C. PRIV. COM.	AV. LOS LAPACHOS
ANCHO DE CALLE :	12.00 m	50.00 m
ANCHO DE VEREDA :	3.00 m	3.00 m
ANCHO DE CALZADA :	6.00 m	4.00 m

PROPIETARIOS :
DOMICILIO :

PROYECTO :
DOMICILIO :

DIRECCION TECNICA :
DOMICILIO :

ELECTRICIDAD
DOMICILIO :

CATEG. DEL COLEGIO DE ARQUITECTOS: "B"

	C. PRIV. COM.	AV. LOS LAPACHOS
PAVIMENTO :	SI	NO
SERVICIOS CLOACALES :	NO	NO

DIRECCION DE SUELO URBANO
EXPEDIENTE 11-T-2021
FECHA DE SELLADO 29/11/21
FOLIO 64301

GONZALO MEDINA
ARQUITECTO M.P. 854

DESIGNACION : ②

PLANO DE ESTRUCTURAS

OBSERVACIONES: 1-2 PAG
Las referencias al Título de Dominio son meramente indicativas, y la aprobación administrativa no valora los derechos que de ellos pudieren emergen.

Ing. Agrim. JUAN JOSE FARIAS
DIRECTOR
DIRECCION DE CATASTRO
MUNICIPALIDAD DE SGO. DEL ESTERO

MUNICIPALIDAD DE LA CIUDAD DE SANTIAGO DEL ESTERO
SECRETARIA DE ECONOMIA
APROBADO
DIRECCION DE SUELO URBANO
11-T-2021
EXPEDIENTE
FOLIO
21 MAR 2022

PERMISO DE COMERCIO
DE OBRA N° 4672
DIRECCION DE SUELO URBANO

Arq. BERNARDO L. M. SANTILLAN
DIRECTOR
DIRECCION DE SUELO URBANO
MUNICIPALIDAD DE SGO. DEL ESTERO

Arq. Bravo, Ma. Esther
Dpto. OBRAS PRIVADAS
DIRECCION DE SUELO URBANO