

Detalle losa continua
Apoyo en muro portante Viguetas paralelas.

Version	Release Date
V.E.1	1992
V.E.2	1992
V.E.3	1992

C.E.1
18x18

- Acero ADN - 420
- Hormigón H-21

Todos los hierros longitudinales de vigas terminales debe finalizar en un gancho a 90°, indicado en el plano con un mínimo de 20 cm.

No se puede colocar caños de instalaciones eléctricas dentro de las vigas.

Separación entre estribos

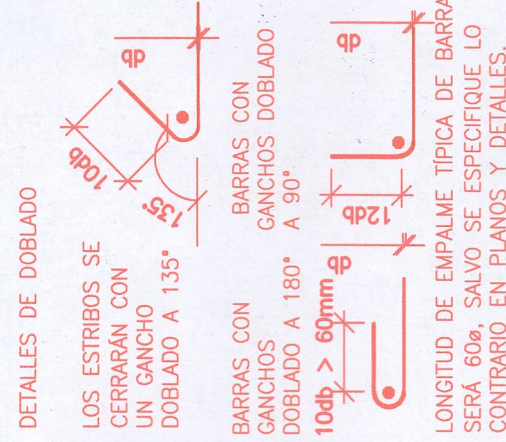
- Zona Normal = Según detalle de Columna (cm)
- Zona Crítica = Separación Zona Normal / 2 (cm)

Losa	EPS	capa comp.	H	NOTA	Serie Tensilite	Aclaramiento	Cantidad
LV1	17	5	22	VIG. DOBLE	SERIE A1	ALUMINUM® ALUMINUM® ALUMINUM®	17un-6,20m
LV2	17	5	22	VIG. SIMPLE	SERIE A1	ALUMINUM® ALUMINUM® ALUMINUM®	8un-3,40m
LV3	17	5	22	VIG. SIMPLE	ASTER	ALUMINUM® ALUMINUM® ALUMINUM®	8un-2,20m
LV4	17	5	22	VIG. SIMPLE	SERIE C	ALUMINUM® ALUMINUM® ALUMINUM®	8un-5,00m
LV5	17	5	22	VIG. SIMPLE	ASTER	ALUMINUM® ALUMINUM® ALUMINUM®	112un-1,40m
LV6	17	5	22	VIG. SIMPLE	SERIE A2	ALUMINUM® ALUMINUM® ALUMINUM®	1047un-3,80m
LV7	17	5	22	VIG. DOBLE	SERIE A2	ALUMINUM® ALUMINUM® ALUMINUM®	12un-5,60m
LV8	17	5	22	VIG. SIMPLE	ASTER	ALUMINUM® ALUMINUM® ALUMINUM®	12un-5,60m
LV9	17	5	22	VIG. SIMPLE	SERIE D	ALUMINUM® ALUMINUM® ALUMINUM®	8un-5,60m
LV10	17	5	22	VIG. SIMPLE	ASTER	ALUMINUM® ALUMINUM® ALUMINUM®	8un-2,00m
LV11	17	5	22	VIG. SIMPLE	SERIE B2	ALUMINUM® ALUMINUM® ALUMINUM®	9un-4,50m
LV12	17	5	22	VIG. SIMPLE	ASTER	ALUMINUM® ALUMINUM® ALUMINUM®	7un-2,60m
LV13	17	5	22	VIG. SIMPLE	SERIE A2	ALUMINUM® ALUMINUM® ALUMINUM®	9un-3,80m
LV14	17	5	22	VIG. SIMPLE	ASTER	ALUMINUM® ALUMINUM® ALUMINUM®	2un-2,80m

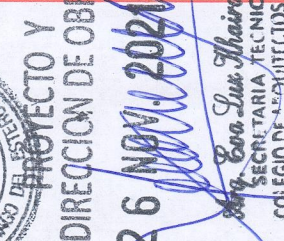
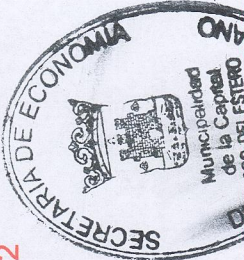
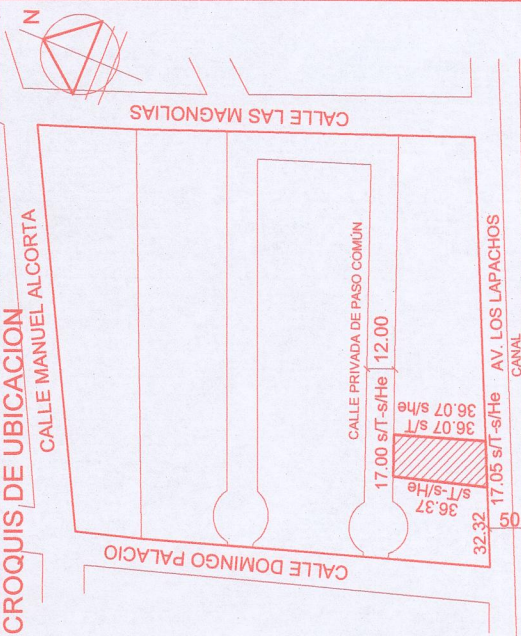
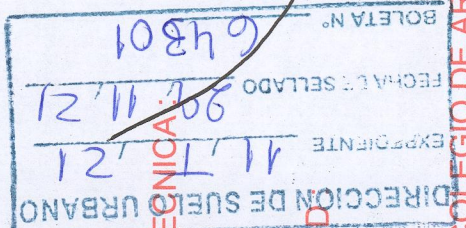
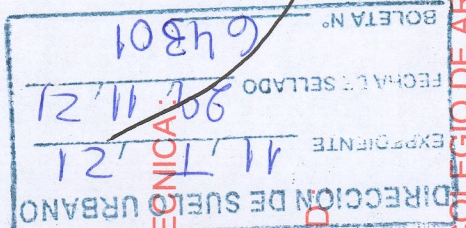
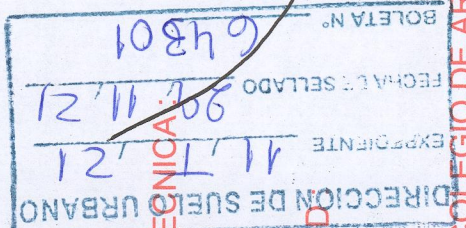
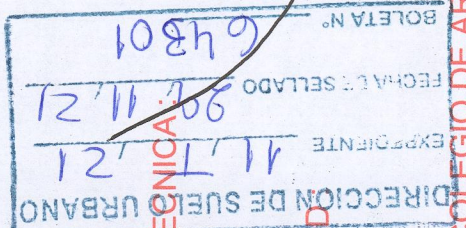
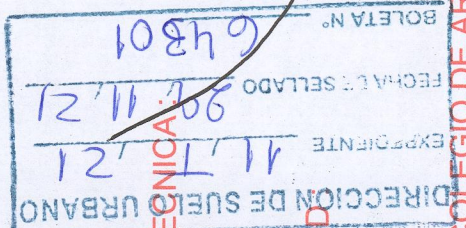
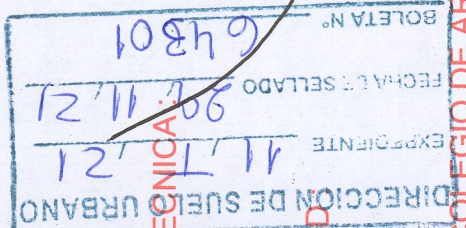
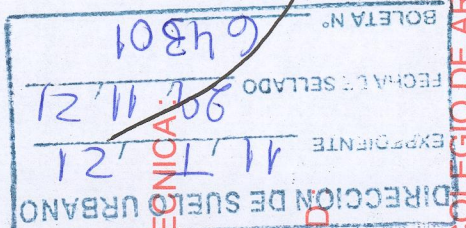
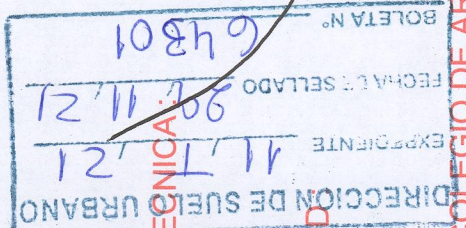
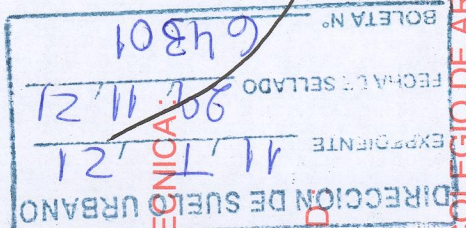
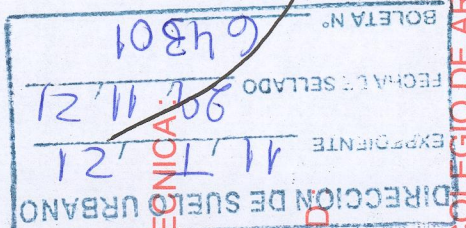
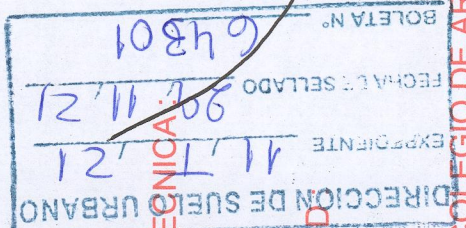
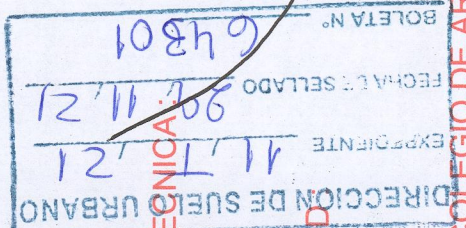
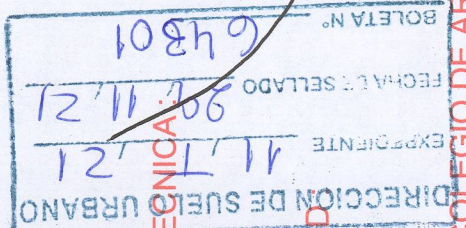
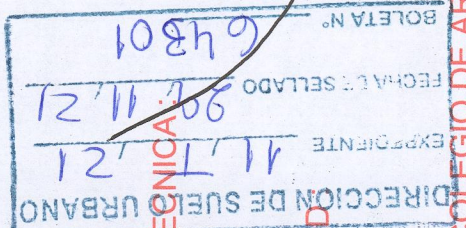
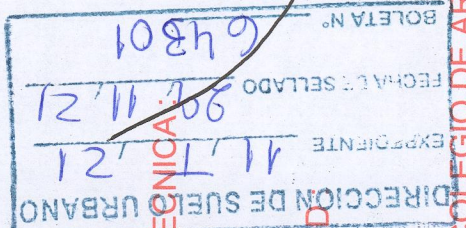
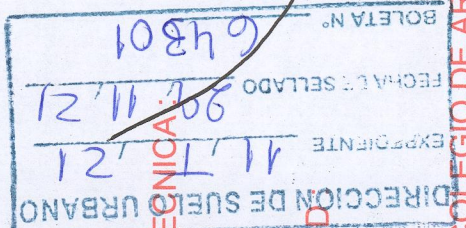
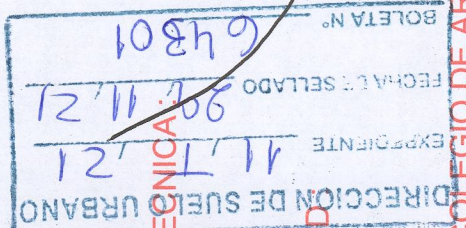
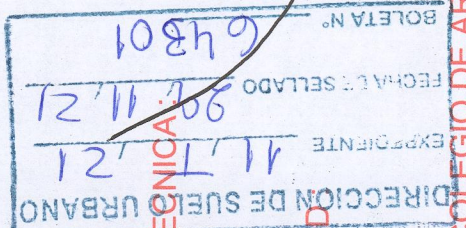
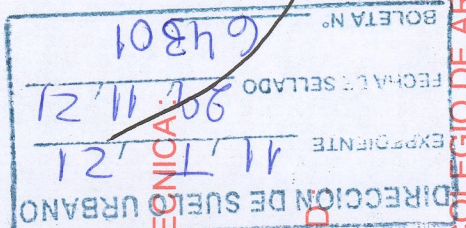
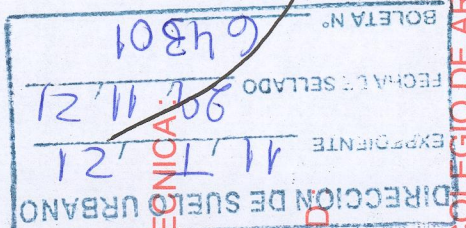
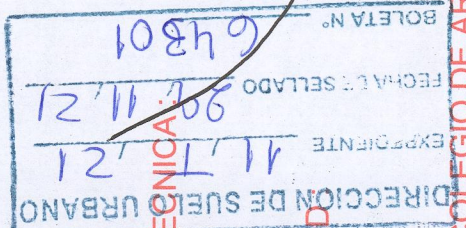
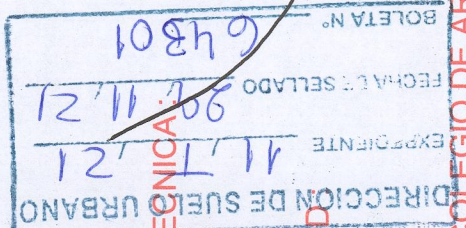
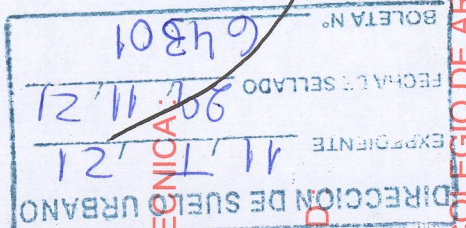
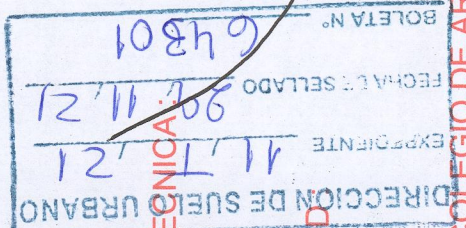
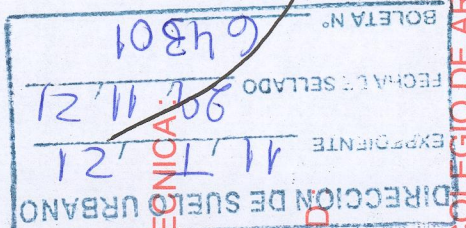
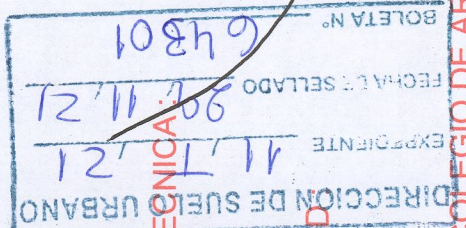
Diagrama de un puente de tres luces con las siguientes especificaciones:

- Deflexión en el centro:** Deflexión en el centro $\leq \frac{1}{250}$ del espesor total t en el punto que a $2/3$ de la luz más larga.
- Barra superior:** Barra superior en empalmes en punto central del vano de Viga. Longitud de empalma $10d$ entre $20d$ y empalmar.
- Barra inferior:** Barra inferior en empalmes en punto central del vano de Viga. Longitud de empalma $10d$ entre $20d$ y empalmar.
- Condiciones de apoyo:** No interrumpe anclaje en columna en intersección con Viga.

.-Armadura de repartición Malla de 20x20 ϕ 6mm



Losa sobre Planta Baja

DIST.: 02	ZONA.: 06	MANZ.: 060	PARC.: 132	LEY 4683	21611	 
PADRÓN INMOB.: 01-1-147689 I.C.M.: 607-T-2021 DOMINIO: 7S-35.914						
DEST. DE LA OBRA: VIVIENDA FAMILIAR		PROPIETARIOS: TSANG, SEBASTIAN D.N.I.: 26.394.057 - CUIL: 20-2338057-4 CORVERA, MARIA VALERIA D.N.I.: 26.774.810 CUIL: 27-2877481-07		UBICACION: AV. LOS LAPACHOS S/N° - LOTE 32		
BARRIO: ALMIRANTE BROWN		PASO COMÚN S/N° - LOTE 32		CATEG. DEL COLEGIO DE ARQUITECTOS: "B"		
CIUDAD: SANTIAGO DEL ESTERO		ESCALA: 1 : 100 - 1 : 200				
SUP. DE TERRENO: 607,25m2, 87T -d/ha		SUP. CUBIERTA PLANTA ALTA 212,68 m2		PROYECTO		
SUP. CUBIERTA PLANTA BAJA 119,35 m2		SUP. CUBIERTA PLANTA TOTAL 332,03 m2		DOMICILIO:		
CROQUIS DE UBICACION: 				DIRECCION TECNICA		
				ELECTRICIDAD		
				DOMICILIO:		
				DOMICILIO:		
						

PLANO DE ESTRUTURAS

OBSERVACIONES: Las referencias al título de Dominio son meramente indicativas, y la aprobación administrativa no valora los derechos que de ellos emanan.

PERMISO DE COMIENZO DE OBRA N.º 4672

DIRECCION DE SUELO URBANO

APROBADO

SECRETARIA DE ECONOMIA

MUNICIPALIDAD DE LA CIUDAD DE SANTIAGO DEL ESTERO

EXPEDIENTE: 11 - T - 2021

FECHA: 21 MAR 2017

Ing. Bernardo M. Santillan
D.E.E. - C.E. SUELO URBANO
N.º CALIDAD DE SUELO DEL ESTERO

Ing. Roberto J. Estigarribia
Dir. de Obras y Planificación
DIRECCION DE SUELO URBANO