

Detalle Armado Losa de Viguetas


Apoyo en extremo de vano sobre pared de mamposteria resistente: Losa unidireccional. Viguetas perpendicular

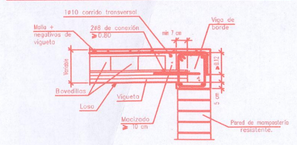


Detalle losa continua
Apoyo en muro portante: Viguetas paralelas.

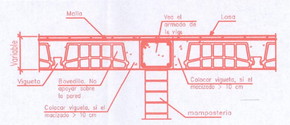


Detalle losa continua
Apoyo en muro portante: Viguetas perpendiculares.

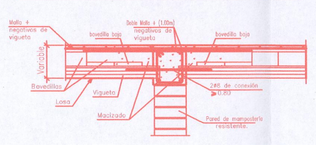

Mamposteria sobre Losa de Viguetas
Losa unidireccional. Viguetas paralelas.

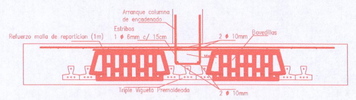

Remate en extremo de vano sobre pared de mamposteria
Losa unidireccional. Viguetas paralelas.

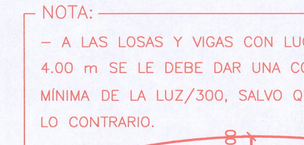


Detalle losa continua
Apoyo en viga invertida: Viguetas perpendiculares.

Mamposteria sobre Losa de Viguetas
Losa unidireccional. Viguetas perpendiculares




- Capa de compresion de 5 cm de espesor
- Armadura de repartición Malla de 20x20 ϕ6mm
- Bovedilla de 17 cm de altura
- Todas las losas llevaran nervio transversal c/ 1.50 m

VIGAS

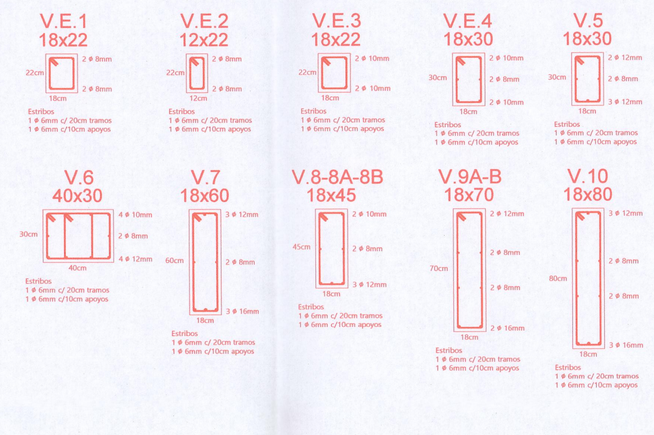


COLUMNAS

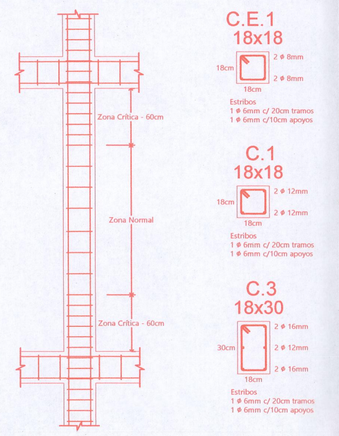


- Materiales
 - Acero ADN - 420
 - Hormigón H-21
- Longitud de anclaje mínima de barras 60 ϕ. Los empalmes de barras longitudinales se realizarán de forma escalonada.
- Todos los hierros longitudinales de vigas terminales debe finalizar en un gancho a 90º, indicado en el plano con un mínimo de 20 cm.
- Los estribos se cerraran con un gancho doblado a 135° .
- No se puede colocar caños de instalaciones eléctricas dentro de las vigas.
- Separación entre estribos
 - Zona Normal = Según detalle de Columna (cm)
 - Zona Crítica = Separación Zona Normal / 2 (cm)

DETALLES COLUMNA METALICA

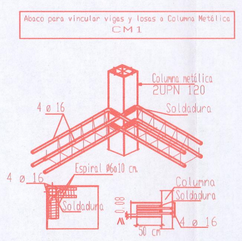


DETALLES DE DOBLADO

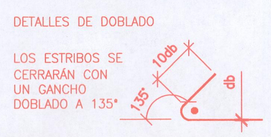

LONGITUD DE EMPALME TÍPICA DE BARRA SERÁ 60ϕ, SALVO SE ESPECIFIQUE LO CONTRARIO EN PLANOS Y DETALLES.

NOTA:
- ESTRUCTURA DE MAMPOSTERIA PORTANTE ECADENADA. SE UTILIZARAN BLOQUES CERAMICOS PORTANTES DE ESPESOR 18cm Y 12 cm SEGUN INDICA PLANO.

NOTA:
– A LAS LOSAS Y VIGAS CON LUCES MAYORES A 4.00 m SE LE DEBE DAR UNA CONTRA FLECHA MÍNIMA DE LA LUZ/300, SALVO QUE SE ESPECIFIQUE LO CONTRARIO.

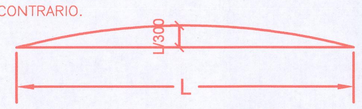


NOTA:
–LAS LOSAS Y VIGAS DEBERÁN PERMANECER APUNTALADAS UN MÍNIMO DE 28 DÍAS.

NOTA-1:
- TODOS LOS NERVIOS EN VOLADIZO SE DEBEN ANCLAR SUS ARMADURAS 1.5 VECES LA LUZ DEL VOLADIZO SALVO QUE SE INDIQUE LO CONTRARIO

NOTA:
- NOTA IMPORTANTE: HACER LOS RELLENOS DE CARGAS DE TECHOS ALIVINADAS CON TELGOPOR.

NOTA:
– LAS MEDIDAS SE VERIFICARÁN EN OBRA. MEDIANTE EL PLANO DE OBRA O DE REPLANTEO Y NO CON EL PLANO DE ESTRUCTURA, AL IGUAL QUE LOS CORTES ESTRUCTURALES.

LOSA TANQUE

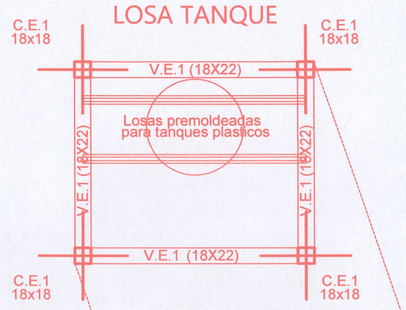

Esquema general empalmes barras

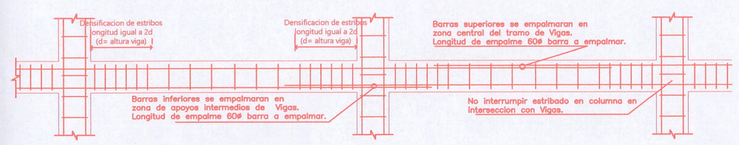


TABLA DE LOSAS

Losa	EPS	capa Comp.	H	NOTA	Serie Tensolite	Aclaracion	Cantidad
Lv1	17	5	22	VIG. DOBLE	SERIE D	ALIVIANAR carga sobre losa	17un-6.20m
Lv2	17	5	22	VIG. SIMPLE	SERIE A1	ALIVIANAR carga sobre losa	8un-3.40m
Lv3	17	5	22	VIG. SIMPLE	ASTER	ALIVIANAR carga sobre losa	8un-2.20m
Lv4	17	5	22	VIG. SIMPLE	SERIE C	ALIVIANAR carga sobre losa	6un-5.00m
Lv5	17	5	22	VIG. SIMPLE	ASTER	ALIVIANAR carga sobre losa	11x2un-1.40m
Lv6	17	5	22	VIG. SIMPLE	SERIE A2	ALIVIANAR carga sobre losa	10+7un-3.80m
Lv7	17	5	22	VIG. DOBLE	SERIE D	ALIVIANAR carga sobre losa	12un-5.60m
Lv8	17	5	22	VIG. SIMPLE	ASTER	ALIVIANAR carga sobre losa	12+12un-2.00m
Lv9	17	5	22	VIG. SIMPLE	SERIE D	ALIVIANAR carga sobre losa	8un-5.60m
Lv10	17	5	22	VIG. SIMPLE	ASTER	ALIVIANAR carga sobre losa	4un-2.00m
Lv11	17	5	22	VIG. SIMPLE	SERIE B2	ALIVIANAR carga sobre losa	9un-4.50m
Lv12	17	5	22	VIG. SIMPLE	ASTER	ALIVIANAR carga sobre losa	7un-2.60m
Lv13	17	5	22	VIG. SIMPLE	SERIE A2	ALIVIANAR carga sobre losa	9un-3.80m
LvT	17	5	22	VIG. SIMPLE	ASTER	ALIVIANAR carga sobre losa	2un-2.60m

L.M.-L.E.E.

Eje Med.

Losa sobre Planta Alta

L.E.E.

DIST.: 02 ZONA.: 06 MANZ.: 060 PARC.: 132

PADRÓN INMOB.: 01-1-147689 I.C.M.: 607-T-2021 DOMINIO: 7S-35.914

DEST. DE LA OBRA :VIVIENDA FAMILIAR

PROPIETARIOS: TSANG, SEBASTIAN D.N.I.: 26.398.057 - CUIL 20-26398057-4
CORVERA, MARIA VALERIA D.N.I.: 26.774.810 CUIL 27-26774810-7

UBICACION: AV. LOS LAPACHOS S/N°. CALLE PRIVADA DE PASO COMÚN S/N° - LOTE 32

BARRIO: ALMIRANTE BROWN

CIUDAD: SANTIAGO DEL ESTERO

ESCALA: 1 : 100 - 1 : 200

LEY 4683

211611


COLEGIO DE ARQUITECTOS LEY 1054/87 PROVINCIA DEL ESTERO

PROYECTO Y DIRECCION DE OBRA
26 JUN. 2021
Arq. Eva Ines Khairallah
SECRETARIA TECNICA
COLEGIO DE ARQUITECTOS S.D.E.

SECRETARIA DE ECONOMIA
DIRECC. DE SUELO URBANO
Municipalidad de la Capital SGO. DEL ESTERO

SUP. DE TERRENO: 607,26m2 s/T -s/he
SUP. CUBIERTA PLANTA BAJA 212,68 m2
SUP. CUBIERTA PLANTA ALTA 119,35 m2
SUP. CUBIERTA TOTAL : 332,03 m2

CROQUIS DE UBICACION

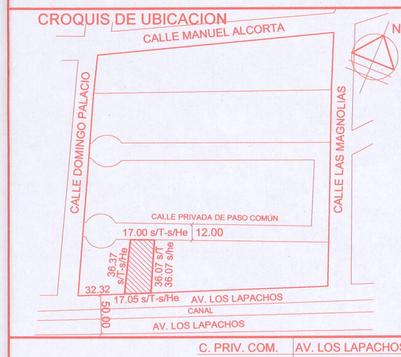

	C. PRIV. COM.	AV. LOS LAPACHOS
ANCHO DE CALLE :	12.00 m	50.00 m
ANCHO DE VEREDA :	3.00 m	3.00 m
ANCHO DE CALZADA :	6.00 m	4.00 m

	C. PRIV. COM.	AV. LOS LAPACHOS
PAVIMENTO :	SI	NO
SERVICIOS CLOACALES :	NO	NO

PROPIETARIOS :
DOMICILIO :

PROYECTO :
DOMICILIO :

DIRECCION TECNICA :
DOMICILIO :

ELECTRICIDAD :
DOMICILIO :

CATEG. DEL COLEGIO DE ARQUITECTOS : C

DESIGNACION :

PLANO DE ESTRUCTURAS

OBSERVACIONES: Las referencias al Título de Dominio son meramente indicativas, y la aprobación administrativa no valora los derechos que títulos emergen.

MUNICIPALIDAD DE LA CIUDAD DE SANTIAGO DEL ESTERO
SECRETARIA DE ECONOMIA
APROBADO
DIRECCION DE SUELO URBANO
11-T-2021
21 MAR 2022

PERMISO DE COMIENZO DE OBRA Nº 4672
DIRECCION DE SUELO URBANO

Ing. Civil JUAN JOSE FRIAS
DIRECTOR
DIRECCION DE CATASTRO
MUNICIPALIDAD DE SGO. DEL ESTERO

Arq. BERNARDO M. SANTILLAN
DIRECTOR
DIRECCION DE SUELO URBANO
MUNICIPALIDAD DE SGO. DEL ESTERO

Arq. Bravo, Ma. Esther
DIRECCION DE OBRAS PRIVADAS
DIRECCION DE SUELO URBANO