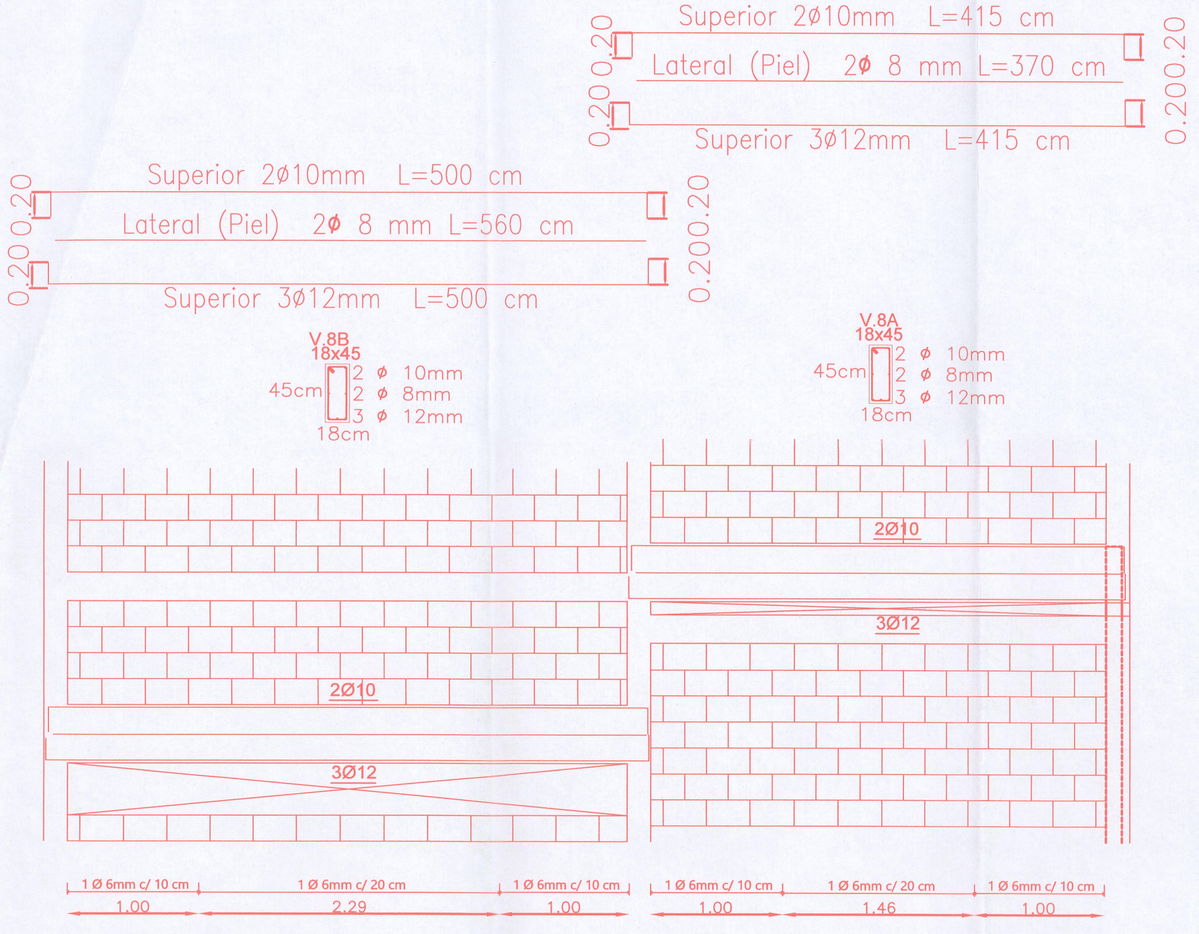

DETALLES DE DOBLADO

LOS ESTRIBOS SE CERRARÁN CON UN GANCHO DOBLADO A 135°

BARRAS CON GANCHOS DOBLADO A 180°

BARRAS CON GANCHOS DOBLADO A 90°

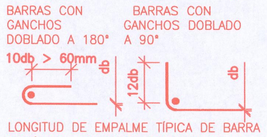

LONGITUD DE EMPALME TÍPICA DE BARRA SERÁ 60ø, SALVO SE ESPECIFIQUE LO CONTRARIO EN PLANOS Y DETALLES.

Materiales
.- Acero ADN - 420
.- Hormigón H-21

Longitud de anclaje mínima de barras 60 ø.
Los empalmes de barras longitudinales se realizarán de forma escalonada.

Todos los hierros longitudinales de vigas terminales debe finalizar en un gancho a 90º, indicado en el plano con un mínimo de 20 cm.

Los estribos se cerraran con un gancho doblado a 135º .

No se puede colocar caños de instalaciones eléctricas dentro de las vigas.

Separación entre estribos
.- Zona Normal = Según detalle de Columna (cm)
.- Zona Crítica = Separación Zona Normal / 2 (cm)

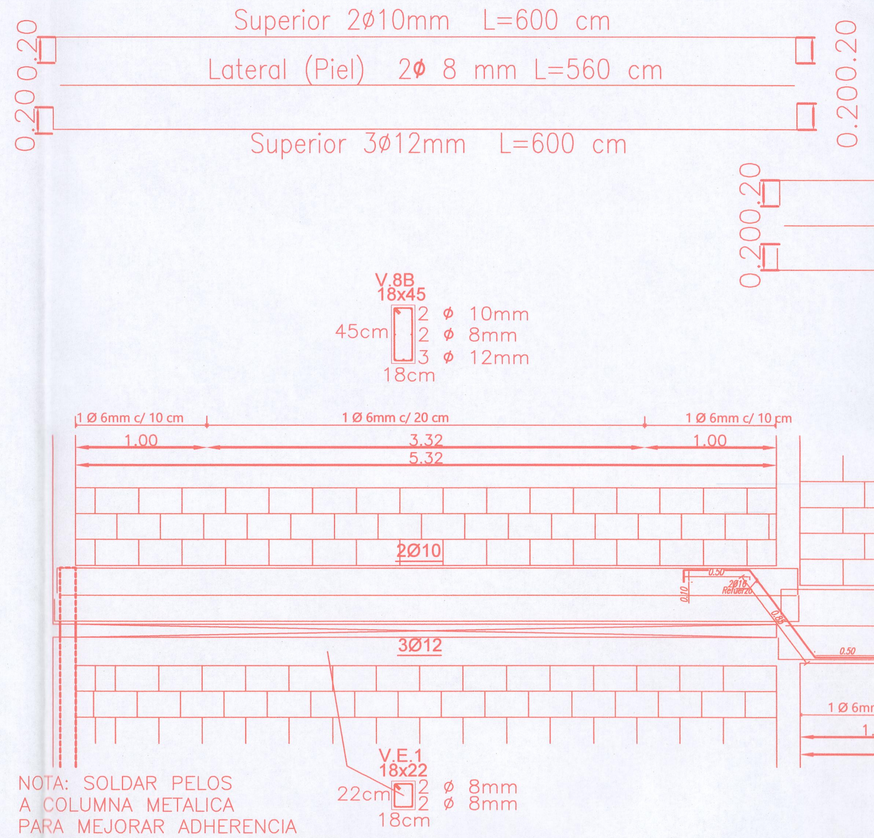

NOTA: SOLDAR PELOS A COLUMNA METALICA PARA MEJORAR ADHERENCIA CON ENCADENADO DE HORMIGON

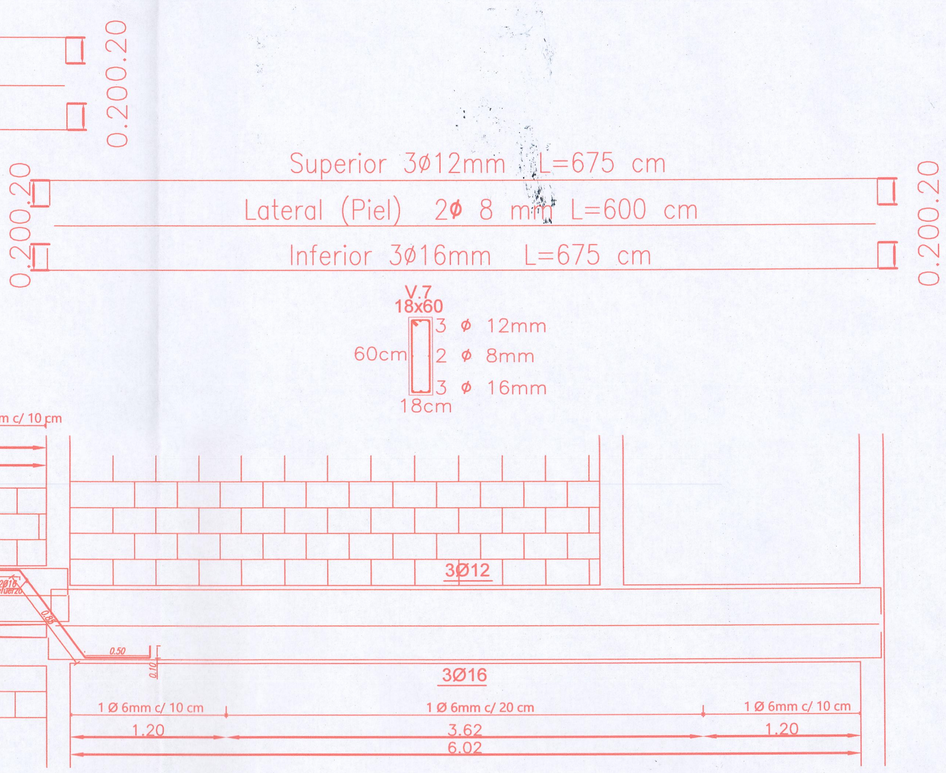

Esquema general empalmes barras

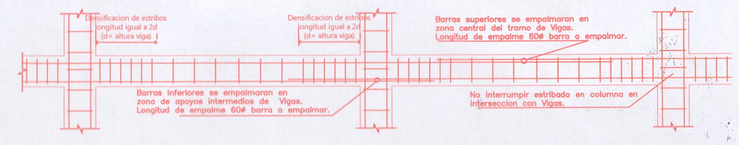

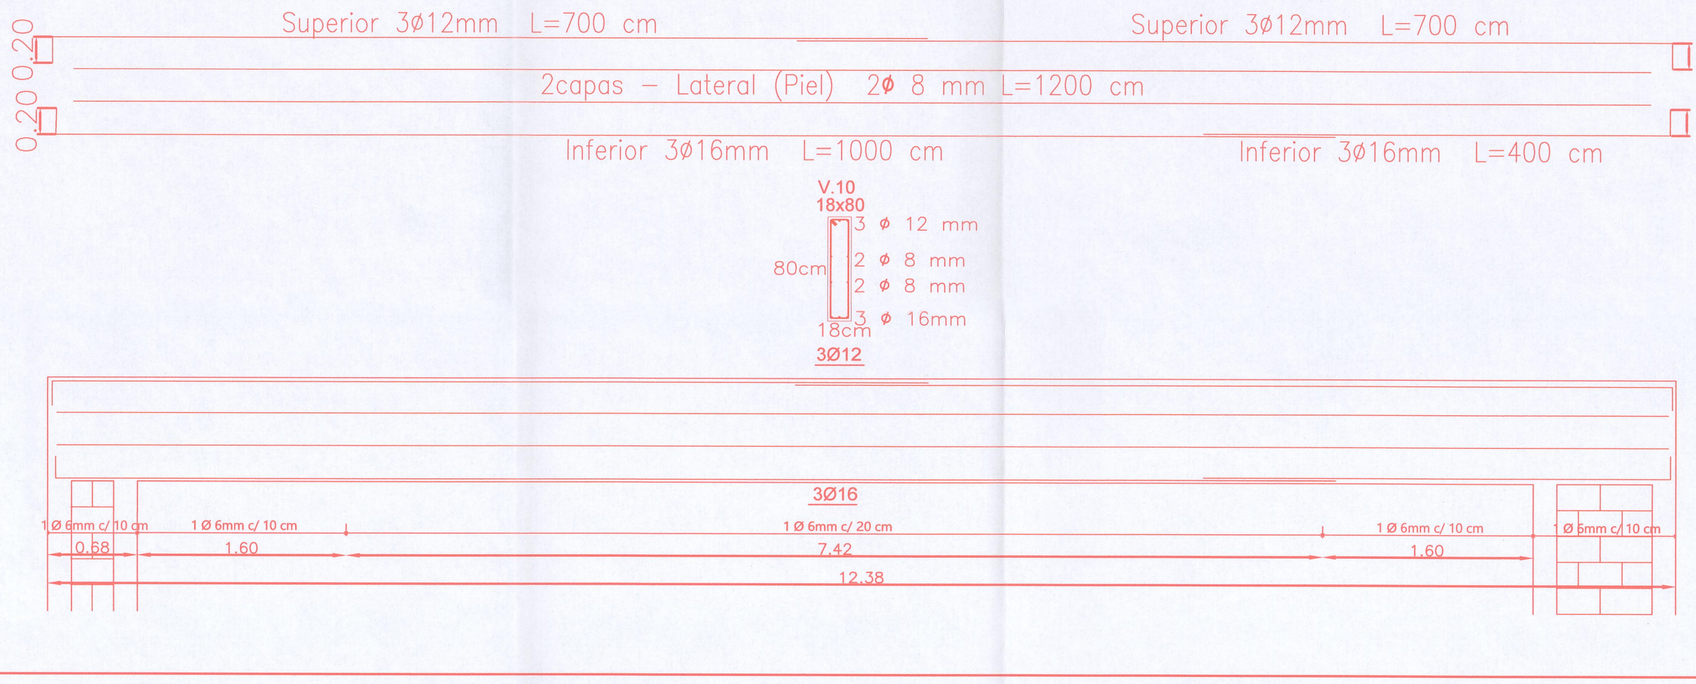

VIGAS

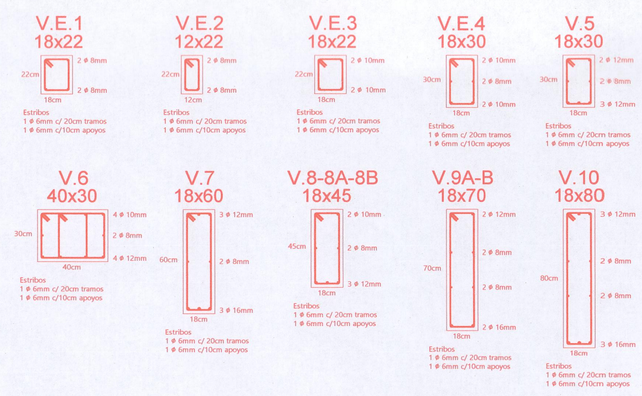

DETALLE 1

APOYO VIGA METALICA EN VIGA DE HORMIGON

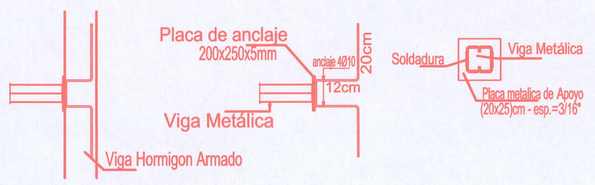

DETALLE 2

APOYO VIGA METALICA EN MAMPOSTERIA

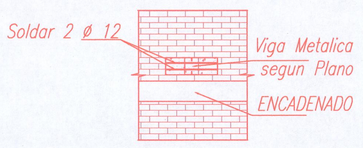

DIST.: 02 ZONA.: 06 MANZ.: 060 PARC.: 132

PADRÓN INMOB.: 01-1-147689 I.C.M.: 607-T-2021 DOMINIO: 7S-35.914

DEST. DE LA OBRA : VIVIENDA FAMILIAR

PROPIETARIOS: TSANG, SEBASTIAN
D.N.I.: 26.398.057 - CUIL 20-26398057-4
CORVERA, MARIA VALERIA
D.N.I.: 26.774.810 CUIL 27-26774810-7

UBICACION: AV. LOS LAPACHOS S/N°. CALLE PRIVADA DE PASO COMÚN S/N° - LOTE 32

BARRIO: ALMIRANTE BROWN

CIUDAD: SANTIAGO DEL ESTERO

ESCALA: 1 : 100 - 1 : 200

LEY 4683
211611

PROYECTO Y DIRECCION DE OBRA
26 NOV. 2021
Arq. Eva Lia Mohrlattel
SECRETARIA TECNICA
COLEGIO DE ARQUITECTOS S.E.

SECRETARIA DE ECONOMIA
Municipalidad de la Capital SGO. DEL ESTERO
DIRECC. DE SUELO URBANO

SUP. DE TERRENO:	607,26m2 s/T -s/Ne
SUP. CUBIERTA PLANTA BAJA	212,68 m2
SUP. CUBIERTA PLANTA ALTA	119,35 m2
SUP. CUBIERTA TOTAL :	332,03 m2

CROQUIS DE UBICACION

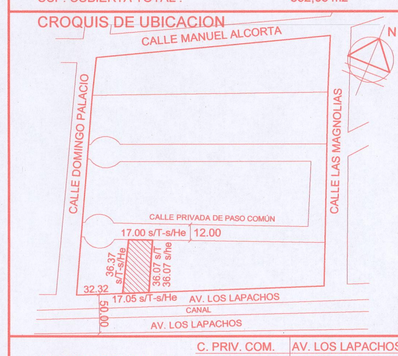

	C. PRIV. COM.	AV. LOS LAPACHOS
ANCHO DE CALLE :	12.00 m	50.00 m
ANCHO DE VEREDA :	3.00 m	3.00 m
ANCHO DE CALZADA :	6.00 m	4.00 m

PROPIETARIOS :
DOMICILIO :

PROYECTO :
DOMICILIO :

DIRECCION TECNICA :
DOMICILIO :

ELECTRICIDAD :
DOMICILIO :

CATEG. DEL COLEGIO DE ARQUITECTOS: "B"

	C. PRIV. COM.	AV. LOS LAPACHOS
PAVIMENTO :	SI	SI
SERVICIOS CLOACALES :	NO	NO

DESIGNACION :

PLANO DE ESTRUCTURAS

12 ENE 2022

OBSERVACIONES: Título de Dominio
meramente indicativas, y la
pación administrativa no valora
rechos que de ellos emergen.

PERMISO DE COMIENZO DE OBRA N° 4672
DIRECCION DE SUELO URBANO

MUNICIPALIDAD DE LA CIUDAD DE SANTIAGO DEL ESTERO
SECRETARIA DE ECONOMIA
APROBADO
DIRECCION DE SUELO URBANO
EXPEDIENTE 11-T-2021
FECHA 21 MAR 2022

Ing. Agrim. JUAN JOSE FRIAS
DIRECTOR
DIRECCION DE CATASTRO
MUNICIPALIDAD DE SGO. DEL ESTERO

Arq. BERNARDO M. SANTILLAN
DIRECTOR
DIRECCION DE SUELO URBANO
MUNICIPALIDAD DE SGO. DEL ESTERO

Arq. Nieva, Ma. Esther
Direc. OBRAS PRIVADAS
DIRECCION DE SUELO URBANO

DIRECCION DE SUELO URBANO
EXPEDIENTE 11-T-2021
FECHA 21 OCT 2021
BOLETIN 15