PLANILLA DE FUNDACION

Zapata de Fundación						Viga de Fundación					
Desig.	Ancho (m)	Alto (m)	Armadura			Desig.	Ancho (cm)	Alto (cm)	Armadura		
			Ai	As	Estribos				Ai	As	Est
Z1	0.90	0.20	4 ø 12	4 ø 12	6 C/15	VF	18	40	4 ø 10	4 ø 10	6 C/20

PLANILLA DE BASES

Posicion	Dimensiones								Fe 1				Fe 2				σt / σe kg/cm2	Observaciones
	a1	a2	d1	d2	c1	c2	d	ds	Cant.	ø	Sep.	cm2	Cant.	ø	Sep.	cm2		
B1	95	190	16	16	20	20	30	80	14	10	12	12.00	7	10	12	5.50	40/2400	EXCENTRICA
B2	140	140	16	16	20	20	30	80	9	10	15	7.07	9	10	15	7.07	40/2400	CENTRADA
B3	130	130	16	16	20	20	30	80	8	10	15	6.28	8	10	15	6.28	40/2400	CENTRADA
B4	90	170	16	16	20	20	30	80	11	12	15	12.05	5	12	15	12.05	40/2400	EXCENTRICA

PLANILLA DE VIGAS

Designación	Luz n	Forma	Dimensiones bo	do	h	Hierros Fe Abajo cm2	Nº	ø	Fe' Arriba cm2	Nº	ø	Estribos ø	sep. (cm)	Observaciones
V1	3.95		20	35	31	2.36	3	10	2.36	3	10	6	16	----------
V2	3.38		20	35	31	2.36	3	10	2.36	3	10	6	16	----------
V3	3.10		20	35	31	2.36	3	10	2.36	3	10	6	16	----------
v4	3.08		20	35	31	3.14	4	10	3.14	4	10	6	16	VIGA C/VOLADIZO
V5	3.08		20	35	31	3.14	4	10	3.14	4	10	6	16	VIGA C/VOLADIZO
V6	3.08		20	35	31	3.14	4	10	3.14	4	10	6	16	VIGA C/VOLADIZO
V7	3.10		20	35	31	2.36	4	10	3.14	4	10	6	16	VIGA C/VOLADIZO

PLANILLA DE COLUMNAS

Designación	Hormigon d1 (cm)	d2 (cm)	s (cm2)	Hierros Nº	ø	cm2	Estribos ø	sep. (cm)	Observaciones
C1	20	20	4.00	4	12	3,77	6	20	
C2	20	20	4.00	4	12	3,77	6	20	
C3	20	20	4.00	4	12	3,77	6	20	
C4	20	20	4,00	4	12	3,77	6	20	
C5	20	20	4,00	4	12	3,77	6	20	
C6	20	20	4,00	4	12	3,77	6	20	
C7	20	20	4,00	4	12	3,77	6	20	
C8	20	20	4,00	4	12	3,77	6	20	

PLANILLA DE LOSA DE VIGUETAS PRETENSADAS DE Hº

Tramos

Desig.	Luz (m)	Serie	Separ. b (m)	Altura h (cm)	Capa de comp. a (cm)	Altura Total d (m)	Ladrillo Ceram. Altura (cm)	Armadura por metro Dir. x Ø mm	Dir. x Sep. cm	Dir. y Ø mm	Dir. y Sep. cm	Observaciones
L1	2.60	ASTER	0,50	17	4	0,21	17	6	15	6	15	Hormigón H-21
L2	2.60	ASTER	0,50	17	4	0,21	17	6	15	6	15	Hormigón H-21
L3	3.95	B1	0,50	17	4	0,21	17	6	15	6	15	Hormigón H-21
L4	3.38	A2	0,50	17	4	0,21	17	6	15	6	15	Hormigón H-21
L5	3.10	A1	0,50	17	4	0,21	17	6	15	6	15	Hormigón H-21

bk= 210Kgs./cm2
ak= 4200Kgs./cm2
LADRILLO CERAMICO P/TECHO

PLANILLA DE ILUMINACION Y VENTILACION

Local		Aberturas					Obsv.
Designaciones	Sup.	Desig.	Ancho	Alto	Area I	Area V	
Comedor-Cocina	19.98	V1	1.10	1.00	1.10	1.10	Madera
Dormitorio 1	13.89	V2	1.60	1.00	1.60	1.60	Madera
Dormitorio 2	13.32	P.V1	1.60	2.00	3.20	3.20	Aluminio
Baño DISC	1.78	V3	0.50	0.30	0.15	0.15	Madera
Consultorio 1	10.17	V4	1.00	1.20	1.20	1.20	Madera
Consultorio 2	12.34	V4	1.00	1.20	1.20	1.20	Madera
Consultorio 3	12.98	V5	1.50	1.00	1.50	1.50	Aluminio
Consultorio 4	10.03	V3	1.50	1.00	1.50	1.50	Aluminio
Loc Comercial	11.36	P2	1.00	2.00	2.00	—	VIDRIO
Loc Comercial	11.36	V6	1.17	1.55	1.81	—	VIDRIO
SALA ESPERA	13.08	V7	1.63	2.00	3.26	—	VIDRIO
SALA ESPERA	13.08	P3	1.00	2.00	2.00	—	VIDRIO
SALA ESPERA	13.08	V6	2.42	1.55	3.71	—	VIDRIO
Dormitorio 3	13.41	V8	1.40	1.00	1.40	1.40	Aluminio
Dormitorio 4	14.60	V9	1.40	1.00	1.40	1.40	Aluminio
Lavadero	12.65	P1	0.80	2.00	1.60	1.60	Aluminio
Lavadero	12.65	V10	1.20	1.00	1.20	1.20	Aluminio
Living	12.00	V11	2.25	1.00	2.25	2.25	Aluminio
Comedor	11.25	V12	3.25	1.00	3.25	3.25	Aluminio
Cocina	9.00	V13	2.75	1.00	2.75	2.75	Aluminio

Plantas gral

NOTA:
EXISTE UN EXCEDENTE O DIFERENCIAS DE MEDIDA SEGUN HECHOS EXISTENTES CON RESPECTO AL TITULO QUE ES EXCLUSIVA RESPONSABILIDAD DEL O LOS PROPIETARIOS.

FIRMA DEL O LOS PROPIETARIOS

Dist:02 Zona:10 Manz:09 Parc:80 — Ley 4.683
PADRON INMOBILIARIO01_010_21994 I.C.M:369-D-24 DOMINIO:7S-6193

Destino de la Obra: Vivienda en Propiedad Horizontal, Local comercial y Consultorio.-

Propietario: Silvia Eugenia Delgado
DNI Nº22.242.894-CUIL: 27-22242894-5

Ubicación: Avda. Belgrano Sur Nº 3893.-

Barrio: América del Sur.-

Localidad: Capital - Santiago del Estero

Escala: 1:100 - 1:500- 1:50

Superficie Terreno:	S/he. 365.37 m2
Superficie Existente:	S/he. 177.47 m2
Superficie Demolicion:	S/he. 16.99 m2
Superficie Proy. PB:	S/he. 69.55 m2
Superficie Proy. PA:	S/he. 126.97 m2
Superficie Proy. Total	S/he. 196.52 m2

Ancho de Calle:	49.94m
Ancho de vereda:	6.85m
Ancho de Calzada:	9.85m

Propietarios: Silvia E. Delgado
Dom: 22.242.894

Proyecto: Dom: M.M.O. JORGE E. LEDESMA Mat. Nº 50.5.5 COLEGIO DEL ESTERO

Electricidad Dom: M.M.O. JORGE E. LEDESMA Mat. Nº 50.5.5 COLEGIO DEL ESTERO

Direccion Tecnica: Dom: M.M.O. JORGE E. LEDESMA Mat. Nº 50.5.5 COLEGIO DEL ESTERO

Pje. PASCO — VENEZUELA — Avda. BELGRANO — IGUAZU

Pavimento: SI
Serv. Cloacales: SI

Designación: PLANO DE RELEVAMIENTO, MODIFICACION Y PROYECTO DE AMPLIACION

Observaciones: 20 DIC 2024

Las referencias al Titulo de dominio son meramente indicativas, y la aprobación administrativa no valora los derechos que de ellos emergen.

MUNICIPALIDAD DE LA CIUDAD DE SANTIAGO DEL ESTERO
SECRETARIA DE ECONOMIA
APROBADO
DIRECCION DE SUELO URBANO
EXPEDIENTE 965-31-2024 (14-D-24)
FECHA 16 DIC 2024

PERMISO DE COMIENZO DE OBRA Nº 186/2025
DIRECCION DE SUELO URBANO

Arq. ABRAHAM BERNARDO ROMINA
Dpto. OBRAS PRIVADAS
DIRECCION DE SUELO URBANO

Arq. Cesar Marcelo Alcorta
Director D.S.U.

Ing. Agrim. J. LEANDRO ARJONA
DIRECCION DE CATASTRO MUNICIPAL

DIRECCION DE SUELO URBANO
SECRETARIA DE ECONOMIA
MUNICIPALIDAD de la Capital
DPTO. SOCIO DEL ESTERO
EXPEDIENTE 965-31-2024
FOLIO 39
FECHA 28 NOV. 2024
BOLETA 3924

REFERENCIAS

- Medidor c/Toma a Tierra
- Tablero Principal
- Tablero Secundario
- Centro y Brazo de Luz
- Toma Corriente
- Toma Corriente Aire Ac.
- Llave y Toma
- Llave de 1, 2 y 3 Ptos
- Llave de Combinación
- Campanilla y Pulsador
- Numero de Circuito

PLANILLA DE CARGAS ELECTRICAS P.B

NIVEL	TABLERO	CIRCUIT.	BOCAS LUZ 40W	TOMAS 200W	TOMAS U.E	POTENCIA LUZ	POTENCIA TOMAS	POTENCIA TOTAL(W)	CORRIENTE TOTAL(A)	PROTECC. TERMOMAG. (A)	INTERRUP. DIFERENC. (A)
P	T1	C1	5				600	600	2.82	10	25
B	T1	C2	0	0	1		1500	1500	6.81	16	
A	T2	C1	3	1		120	200	320	1.45	10	
J	T2	C2	0	0	1		1500	1500	6.82	16	
A	T3	C1	3	4		120	800	920	4.18	10	
	T4	C2	0	0	1		1500	1500	6.82	16	
	T4	C1	3	2		120	400	520	2.36	10	

POTENCIA TOTAL (W) 6.660
POTENCIA SIMU. 60 % 3.996

PLANILLA DE CARGAS ELECTRICAS P.A

NIVEL	TABLERO	CIRCUIT.	BOCAS LUZ 40W	TOMAS 200W	TOMAS U.E	POTENCIA LUZ	POTENCIA TOMAS	POTENCIA TOTAL(W)	CORRIENTE TOTAL(A)	PROTECC. TERMOMAG. (A)	INTERRUP. DIFERENC. (A)
P.A	T.P	C1	7	9		320	1800	2120	1.45	10	25
		C2	7	8		280	1600	1880	8.18	10	
		C3	0	8	2	240	3000	3240	13.63	16	

POTENCIA TOTAL (W) 7240
POTENCIA SIMU. 60 % 3.072

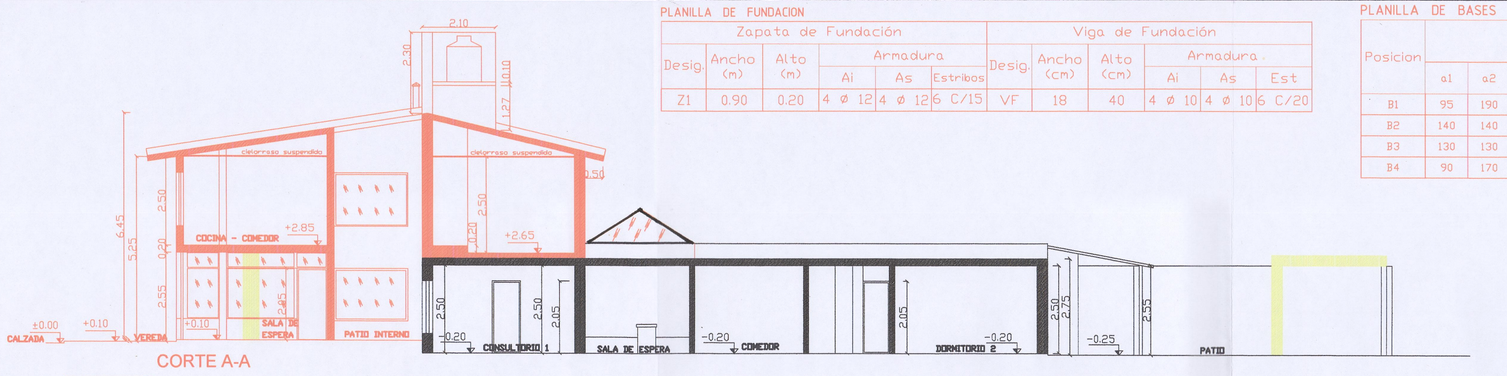

CORTE A-A

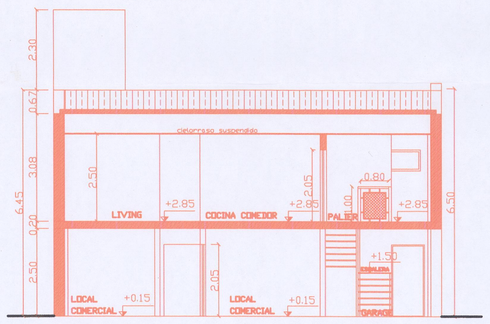

CORTE B-B

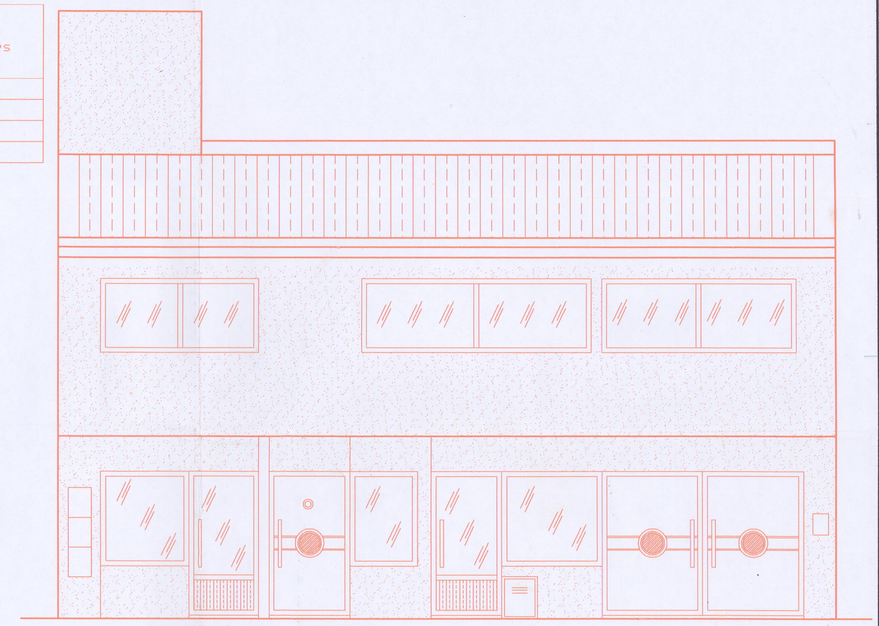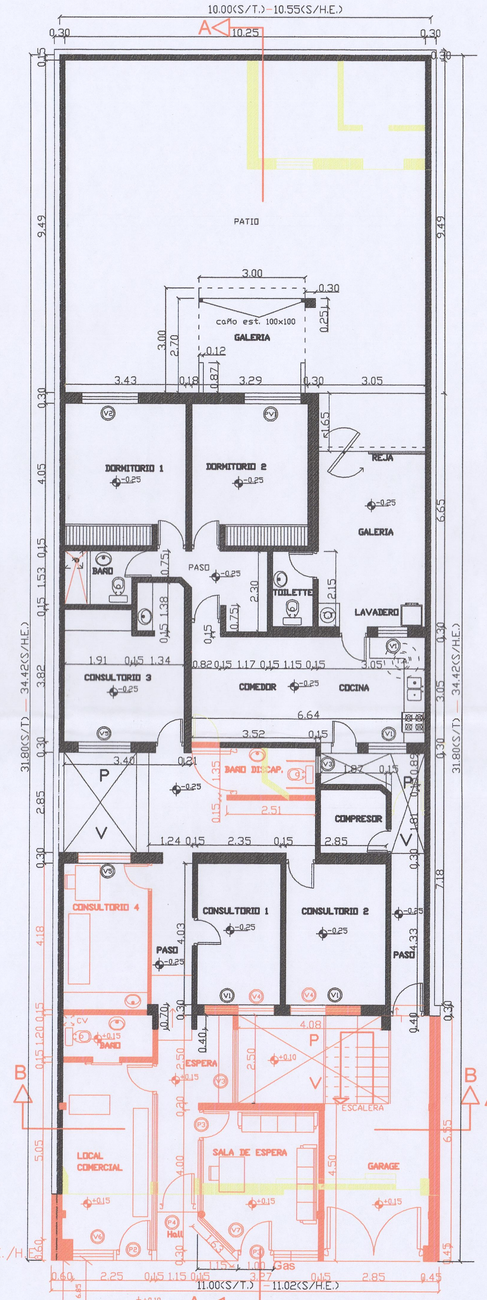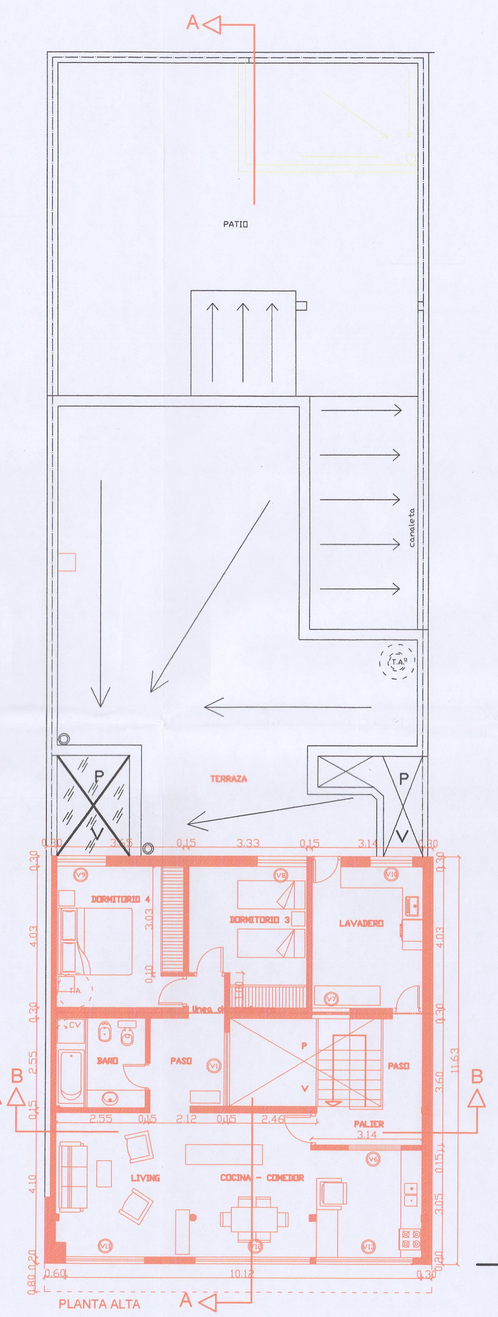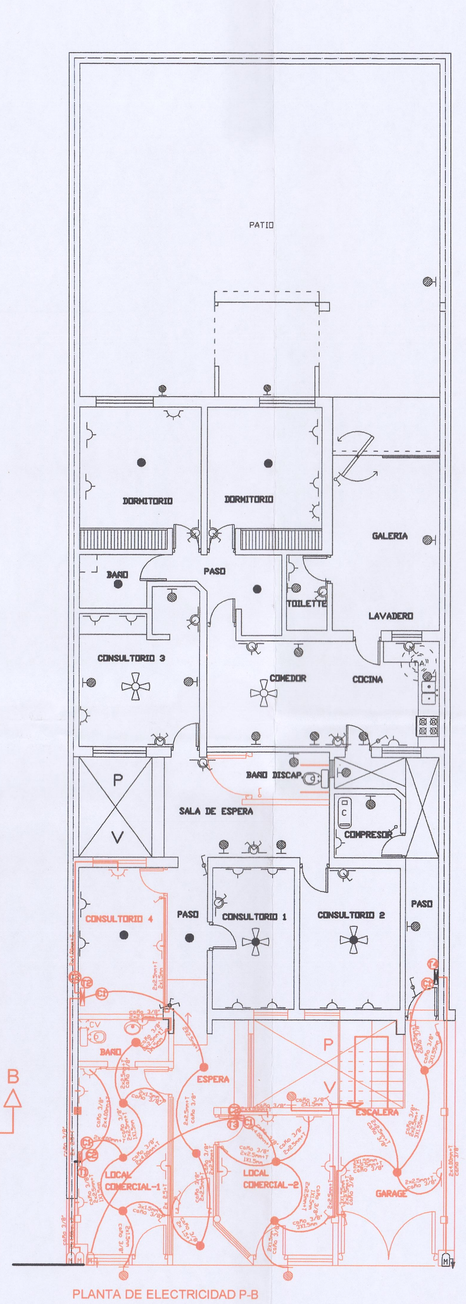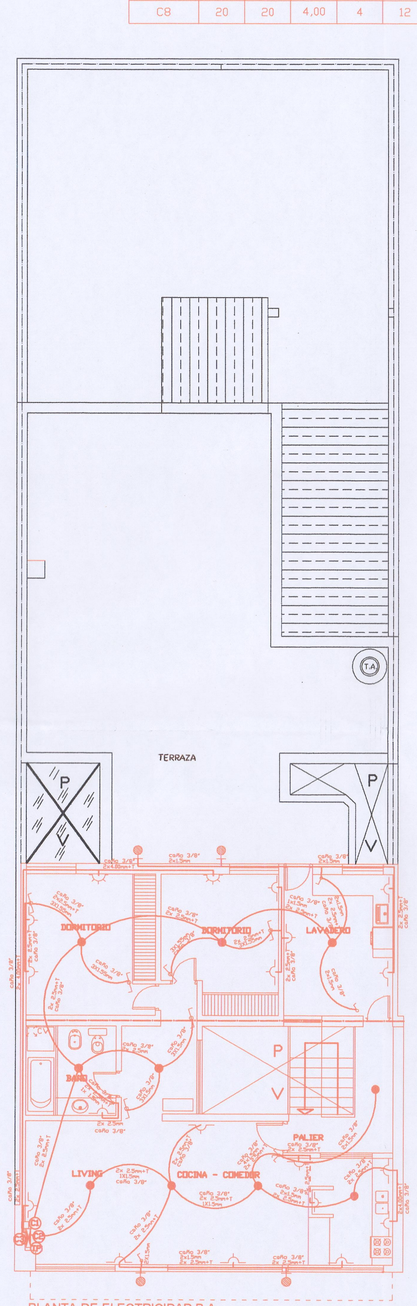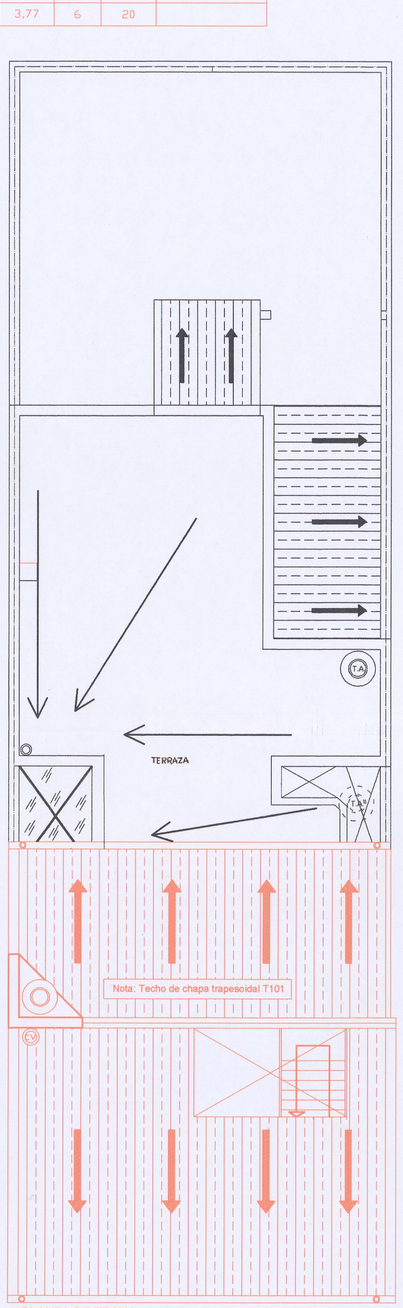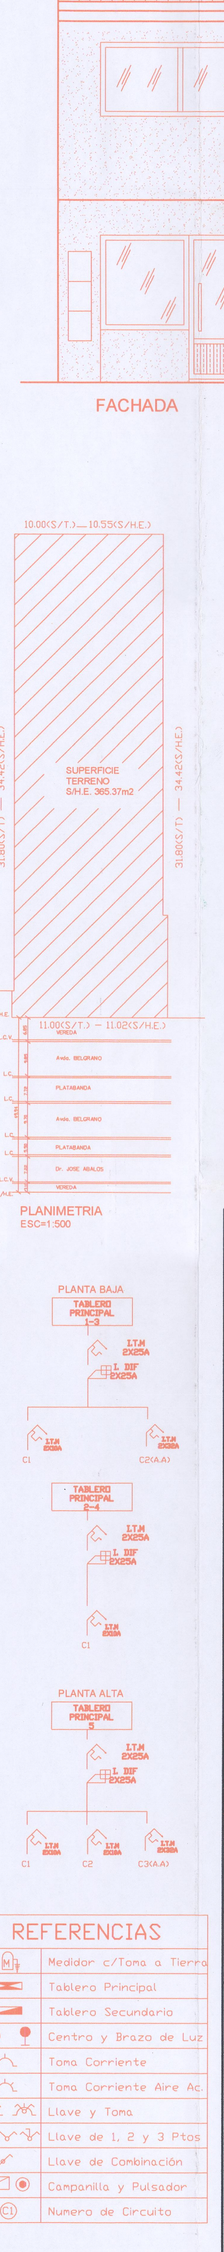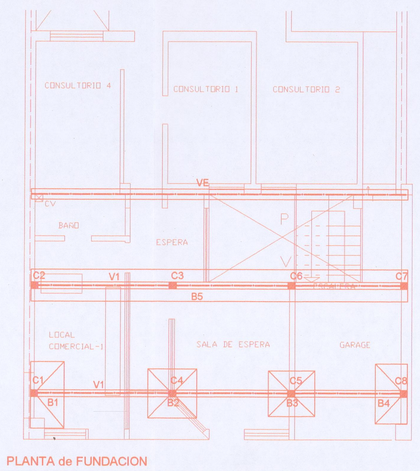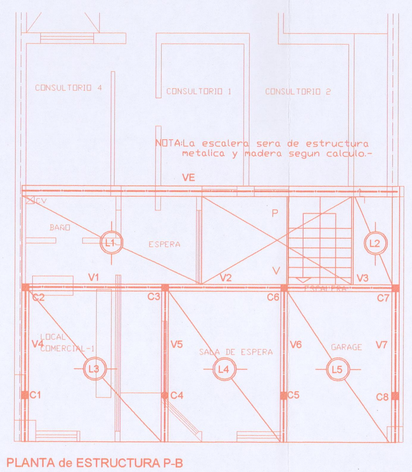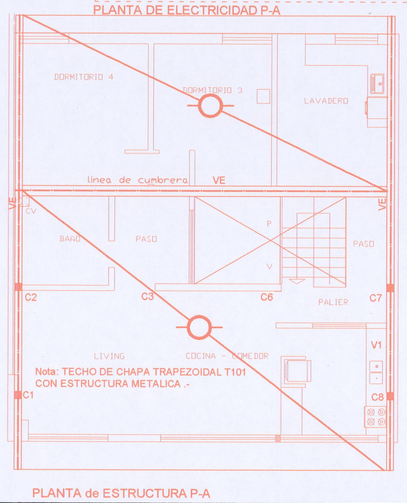
FACHADA