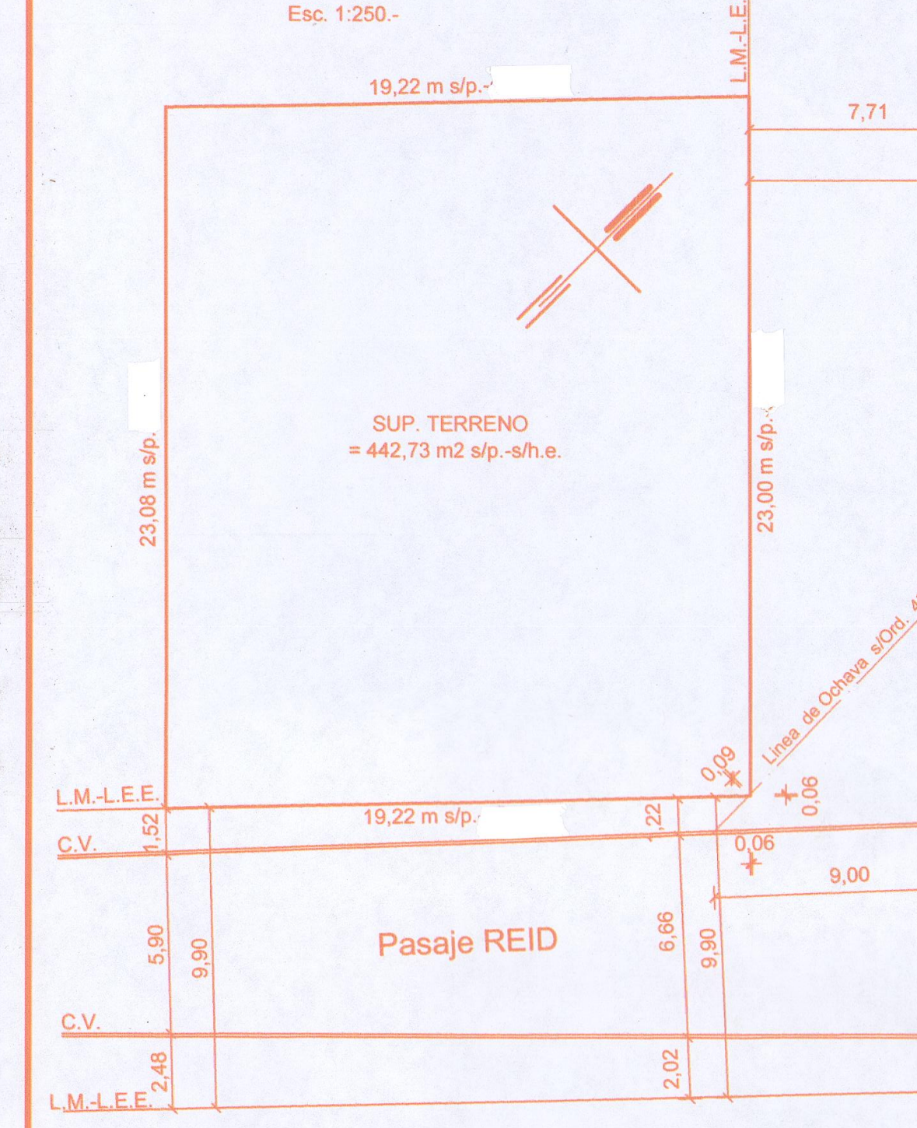
Planimetria
Esc. 1:250.-

SUP. TERRENO
= 442,73 m2 s/p.-s/h.e.
Avenida BELGRANO
Pasaje REID
19,22 m s/p.
23,08 m s/p.
33,18
7,71
6,31
8,37
7,22
3,57
C. Paseo
C.V.
L.M.-L.E.E.
Linea de Ochava s/Ord. 4860/813

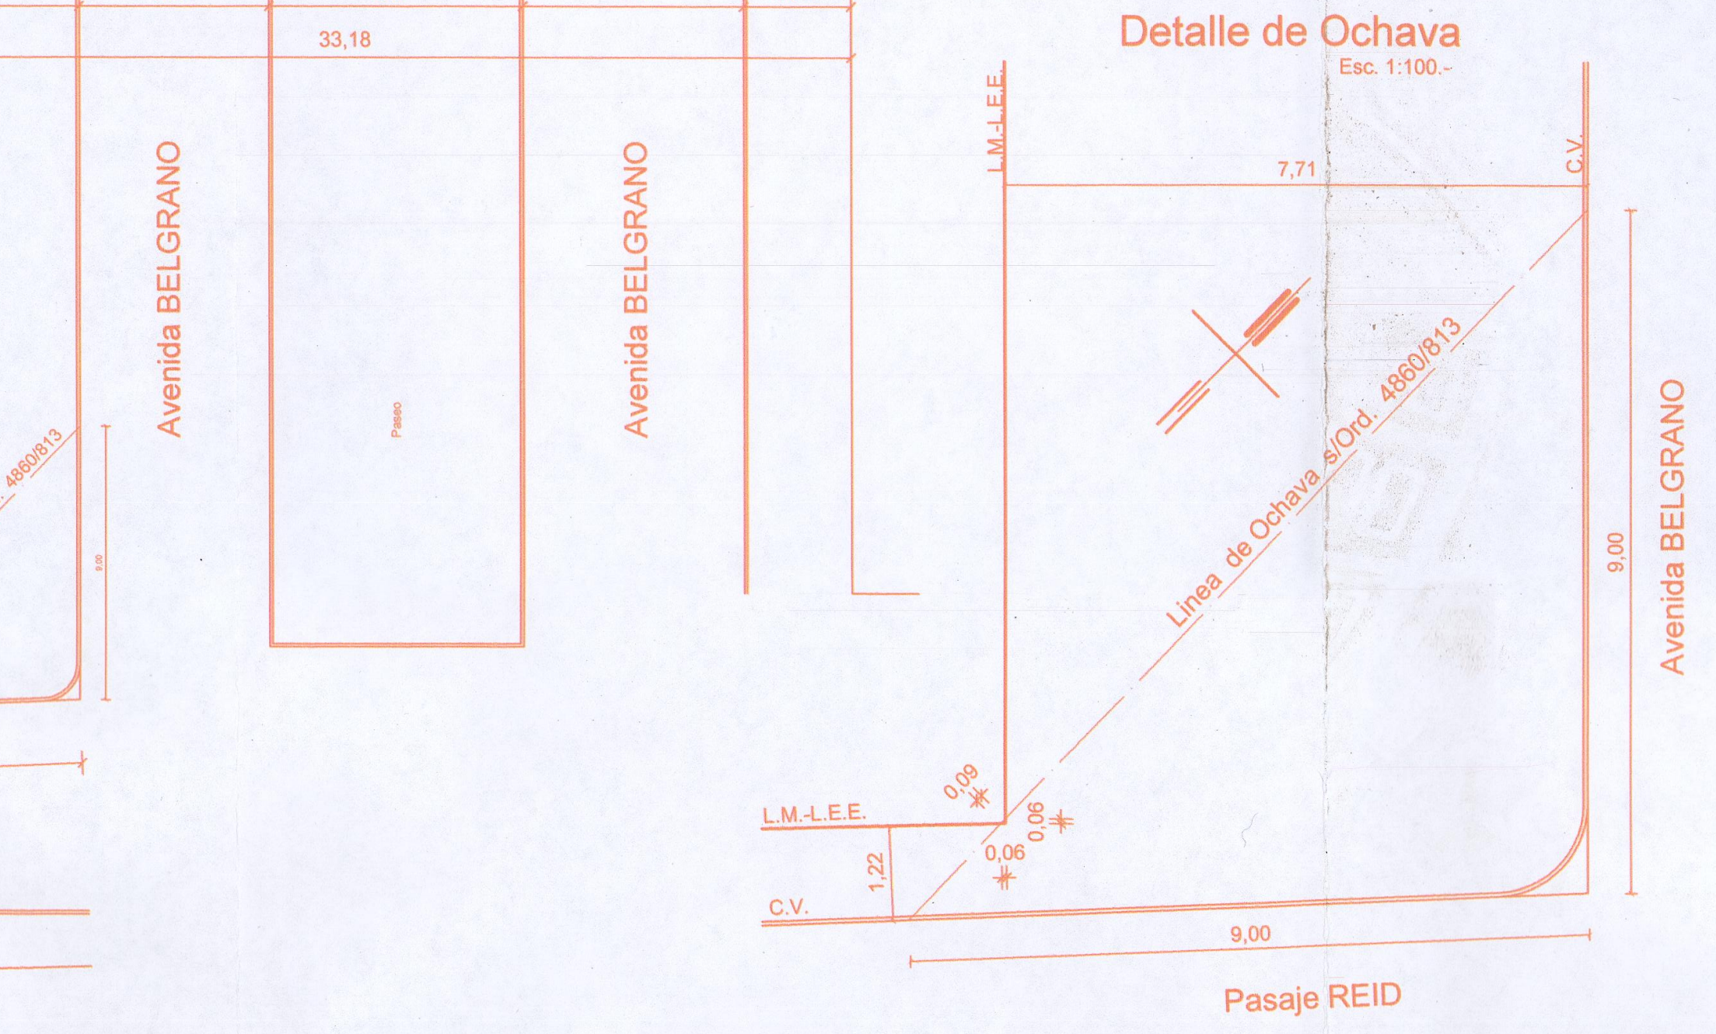
Detalle de Ochava
Esc. 1:100.-

Avenida BELGRANO
Pasaje REID
Linea de Ochava s/Ord. 4860/813
9,00
7,71
1,22
0,06
C.V.
L.M.-L.E.E.

Planilla de Iluminacion y Ventilación

LOCAL		ABERTURAS					Obser.
Designación	Sup.	Desig.	Ancho	Alto	Areas		
					I.	V.	
PLANTA BAJA							
Galeria	5,11	Vo1	3,60	2,55	9,18	9,18	
Hall de Ingreso	9,18	P 1	1,00	2,20	2,20	2,20	De Vidrio
"	"	V 3	2,50	2,50	6,25	-----	Vidriera
Palier	6,37						
Escalera	3,17						
Local Comercial 1	181,79	PV1	2,00	2,20	4,40	4,40	De Vidrio
"	"	V 1	7,90	2,75	21,72	-----	Vidriera
Baño 1	2,49	V 4	0,40	0,30	0,12	0,12	
Cocina 1	4,44	V 5	0,60	1,05	0,63	0,63	
Local Comercial 2	89,98	PV1	2,00	2,20	4,40	4,40	De Vidrio
"	"	V 2	2,34	2,45	5,75	-----	Vidriera
Baño 2	2,49	V 4	0,40	0,30	0,12	0,12	
Cocina 2	4,44	V 5	0,60	1,05	0,63	0,63	
PLANTA 1º PISO							
Estar Cocina Comedor Paso 1	19,11	PV1	1,30	2,05	2,66	2,66	Dpto. A
Paso 2	1,29						
Baño	3,77	C V	0,20	0,20	-----	0,04	
Dormitorio	11,19	V 1	1,30	1,05	1,36	1,36	
Estar Cocina Comedor Paso 1	17,95	V 2	2,00	1,05	2,10	2,10	Dpto. B
Paso 2	1,29						
Baño	3,93	C V	0,20	0,20	-----	0,04	
Dormitorio	10,96	V 1	1,30	1,05	1,36	1,36	
							Dpto. C
Paso	1,44						
Baño	3,90	C V	0,20	0,20	-----	0,04	
Monoambiente	22,21	V 2	2,20	1,05	2,31	2,31	
Estar Cocina Comedor Paso 1	19,21	PV1	1,30	2,05	2,66	2,66	Dpto. D
Paso 2	1,29						
Baño	4,04	C V	0,20	0,20	-----	0,04	
Dormitorio	12,04	V 1	1,30	1,05	1,36	1,36	
Estar Cocina Comedor Paso 1	18,05	V 2	2,00	1,05	2,10	2,10	Dpto. E
Paso 2	1,29						
Baño	4,04	C V	0,20	0,20	-----	0,04	
Dormitorio	10,87	V 1	1,30	1,05	1,36	1,36	
Estar Cocina Comedor Paso 1	19,21	PV1	1,30	2,05	2,66	2,66	Dpto. F
Paso 2	1,29						
Baño	4,45	C V	0,20	0,20	-----	0,04	
Dormitorio	13,61	V 1	1,30	1,05	1,36	1,36	
Estar Cocina Comedor Paso 1	18,05	V 2	2,00	1,05	2,10	2,10	Dpto. G
Paso 2	1,29						
Baño	4,06	C V	0,20	0,20	-----	0,04	
Dormitorio	10,24	V 1	1,30	1,05	1,36	1,36	
					Sup. Comunes 1º y 3º Piso		
Palier	4,02						
Escalera	5,52						
Circulación	20,17	V 3	1,20	1,05	2,52	2,52	Cant. 2

Planilla de Iluminacion y Ventilación

					Sup. Comun 2º Piso		
Palier	4,02	P 1	1,00	2,05	-----	2,05	
Escalera	5,52						
Circulación	20,17	V 3	1,20	1,05	2,52	2,52	Cant. 2
PLANTA 2º y 3º PISO							
Estar Cocina Comedor Paso 1	19,11	PV1	1,30	2,05	2,66	2,66	Dpto. A
Paso 2	1,29						
Baño	3,77	C V	0,20	0,20	-----	0,04	
Dormitorio	11,19	V 1	1,30	1,05	1,36	1,36	
Estar Cocina Comedor Paso 1	17,95	PV2	2,00	2,05	4,10	4,10	Dpto. B
Paso 2	1,29						
Baño	3,93	C V	0,20	0,20	-----	0,04	
Dormitorio	10,96	V 1	1,30	1,05	1,36	1,36	
							Dpto. C
Paso	1,44						
Baño	3,90	C V	0,20	0,20	-----	0,04	
Monoambiente	22,21	V 2	2,20	1,05	2,31	2,31	
Estar Cocina Comedor Paso 1	19,21	PV1	1,30	2,05	2,66	2,66	Dpto. D
Paso 2	1,29						
Baño	4,04	C V	0,20	0,20	-----	0,04	
Dormitorio	12,04	V 1	1,30	1,05	1,36	1,36	
Estar Cocina Comedor Paso 1	18,05	PV2	2,00	2,05	4,10	4,10	Dpto. E
Paso 2	1,29						
Baño	4,04	C V	0,20	0,20	-----	0,04	
Dormitorio	10,87	V 1	1,30	1,05	1,36	1,36	
Estar Cocina Comedor Paso 1	19,21	PV1	1,30	2,05	2,66	2,66	Dpto. F
Paso 2	1,29						
Baño	4,45	C V	0,20	0,20	-----	0,04	
Dormitorio	13,61	V 1	1,30	1,05	1,36	1,36	
Estar Cocina Comedor Paso 1	18,05	PV2	2,00	2,05	4,10	4,10	Dpto. G
Paso 2	1,29						
Baño	4,06	C V	0,20	0,20	-----	0,04	
Dormitorio	10,24	V 1	1,30	1,05	1,36	1,36	
					Sup. Comunes 1º y 3º Piso		
Palier	4,02						
Escalera	5,52						
Circulación	20,17	V 3	1,20	2,46	2,46	2,46	Cant. 2
					Sup. Comune 2º Piso		
Palier	4,02	P 1	1,00	2,05	-----	2,05	
Escalera	5,52						
Circulación	20,17	V 3	1,20	2,05	2,46	2,46	Cant. 2
PLANTA DE TERRAZA							
Escalera	6,24						
Paso	4,76	V 1	1,00	1,05	1,05	1,05	
"	"	P 1	1,00	2,05	4,10	-----	
Baño	2,74	V 2	0,30	0,30	0,09	0,09	

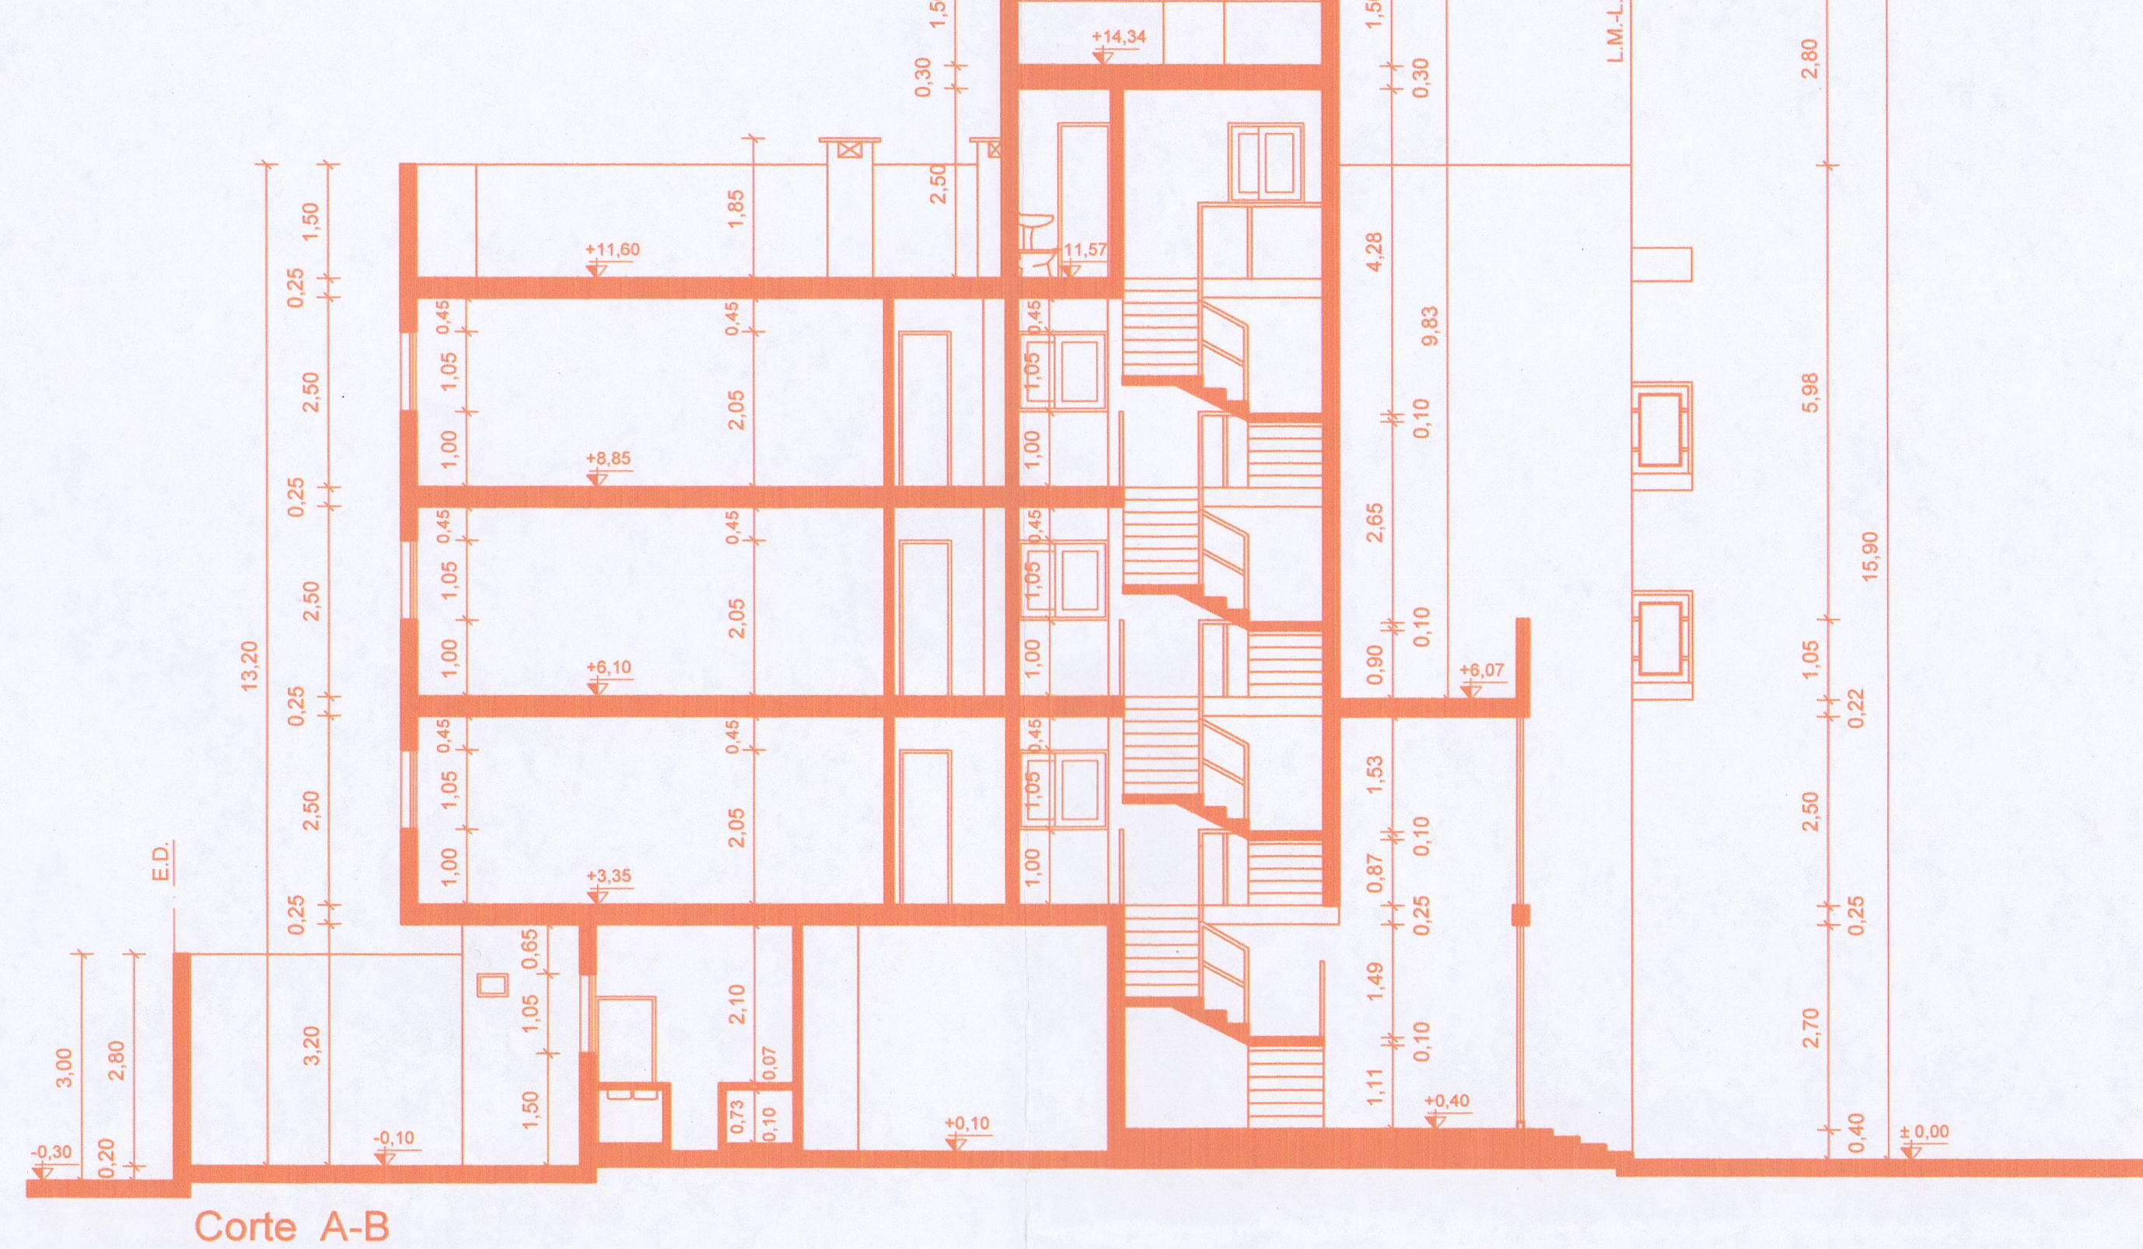
Corte A-B

L.M.-L.E.E.
E.D.
L.C.V.
+14,34
+11,60
+8,85
+6,10
+3,35
+0,10
13,20
15,90

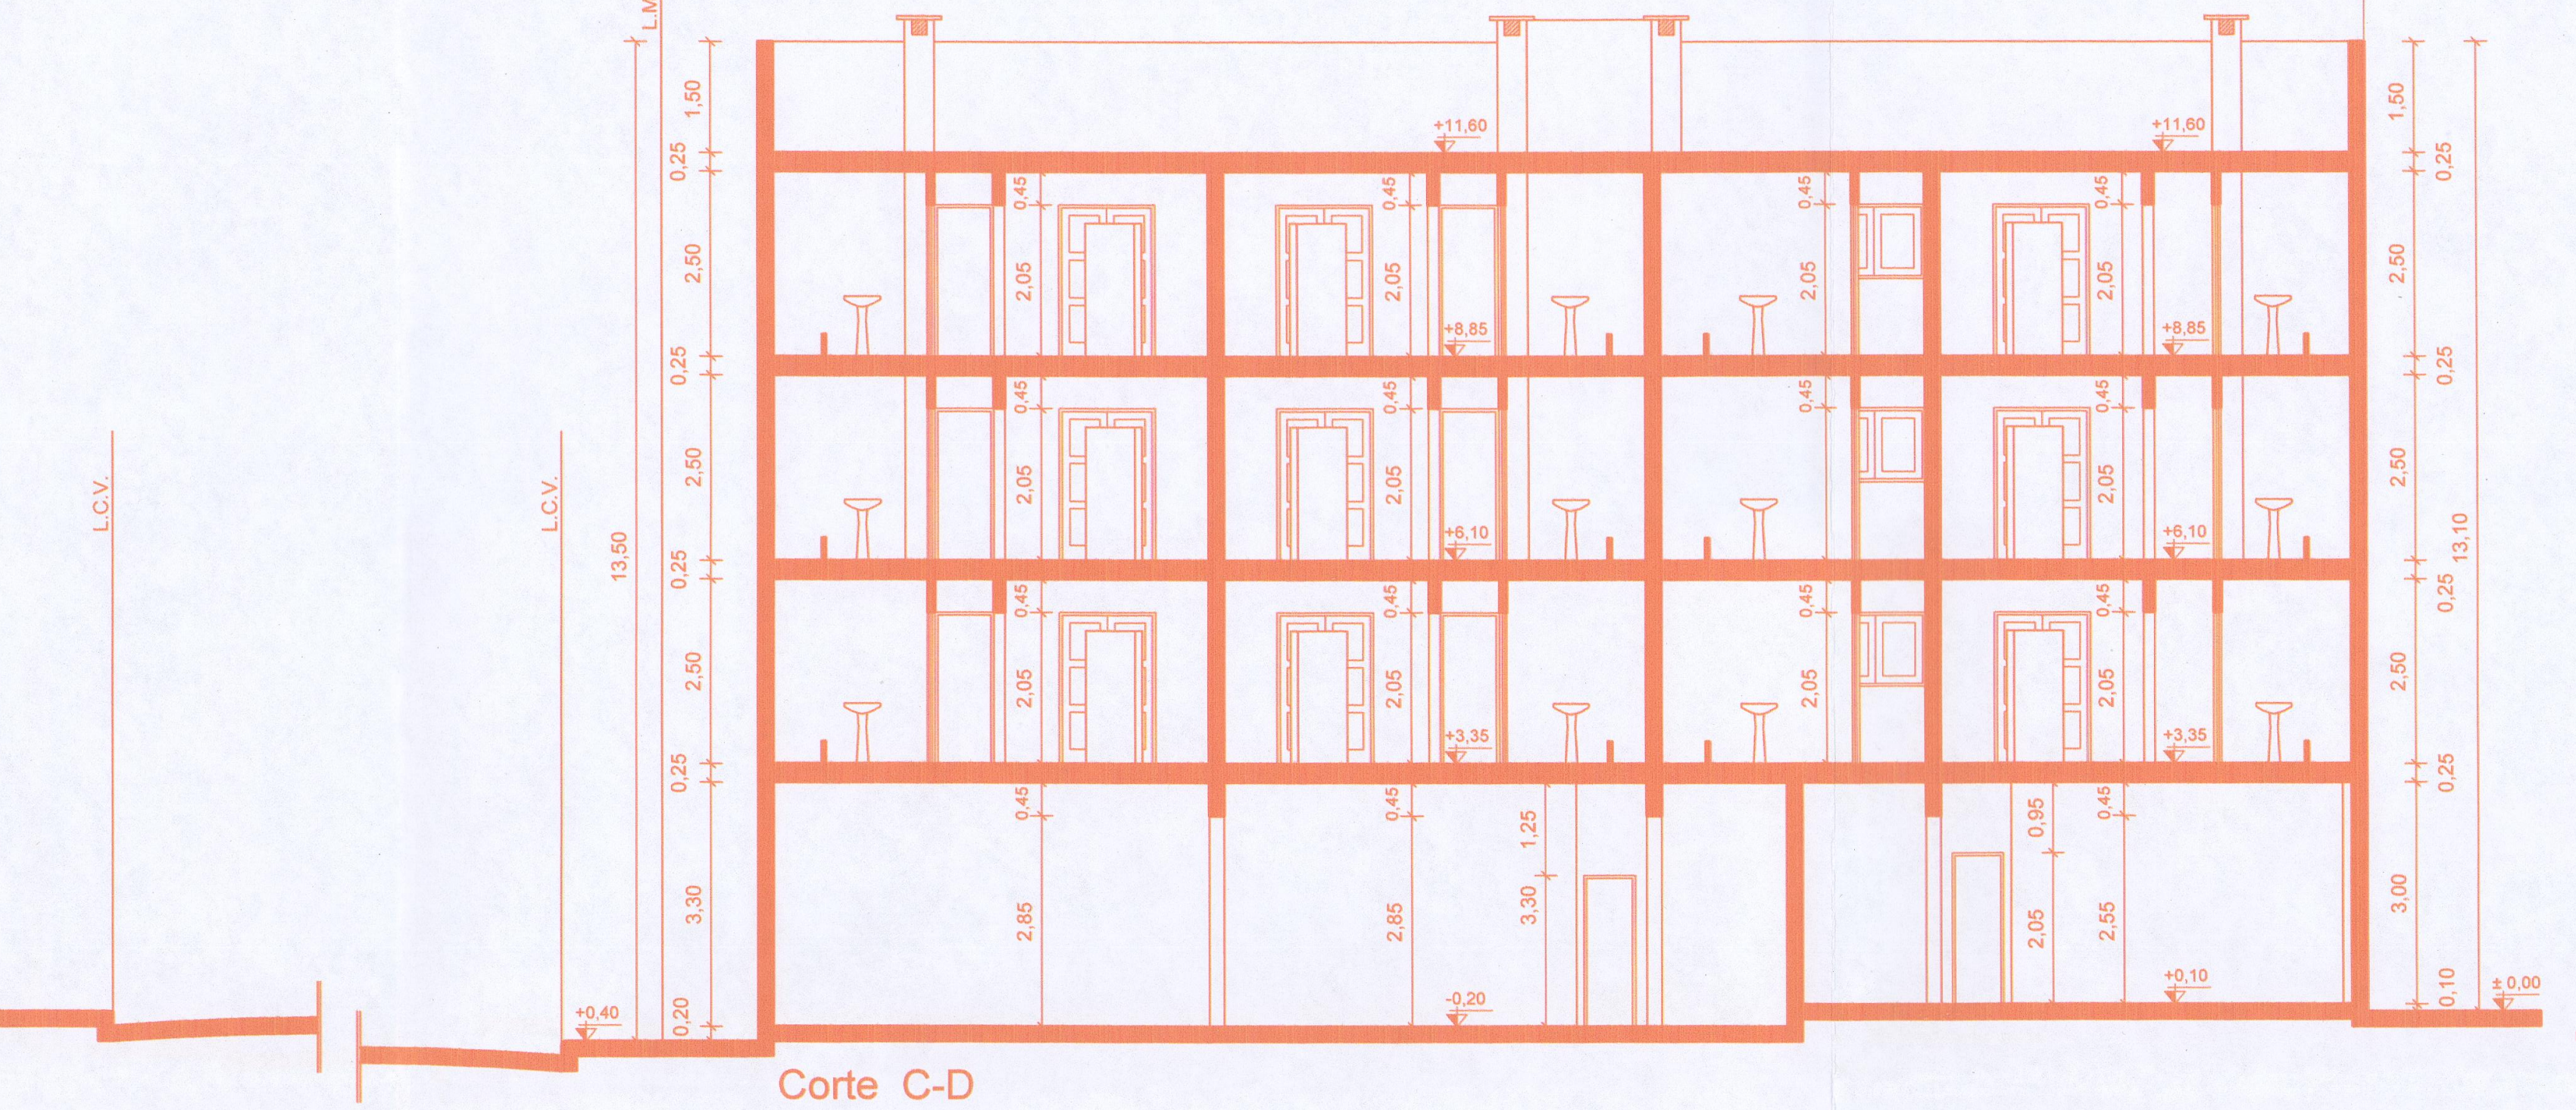
Corte C-D

L.M.-L.E.E.
E.D.
L.C.V.
+11,60
+8,85
+6,10
+3,35
+0,10
13,10
13,50

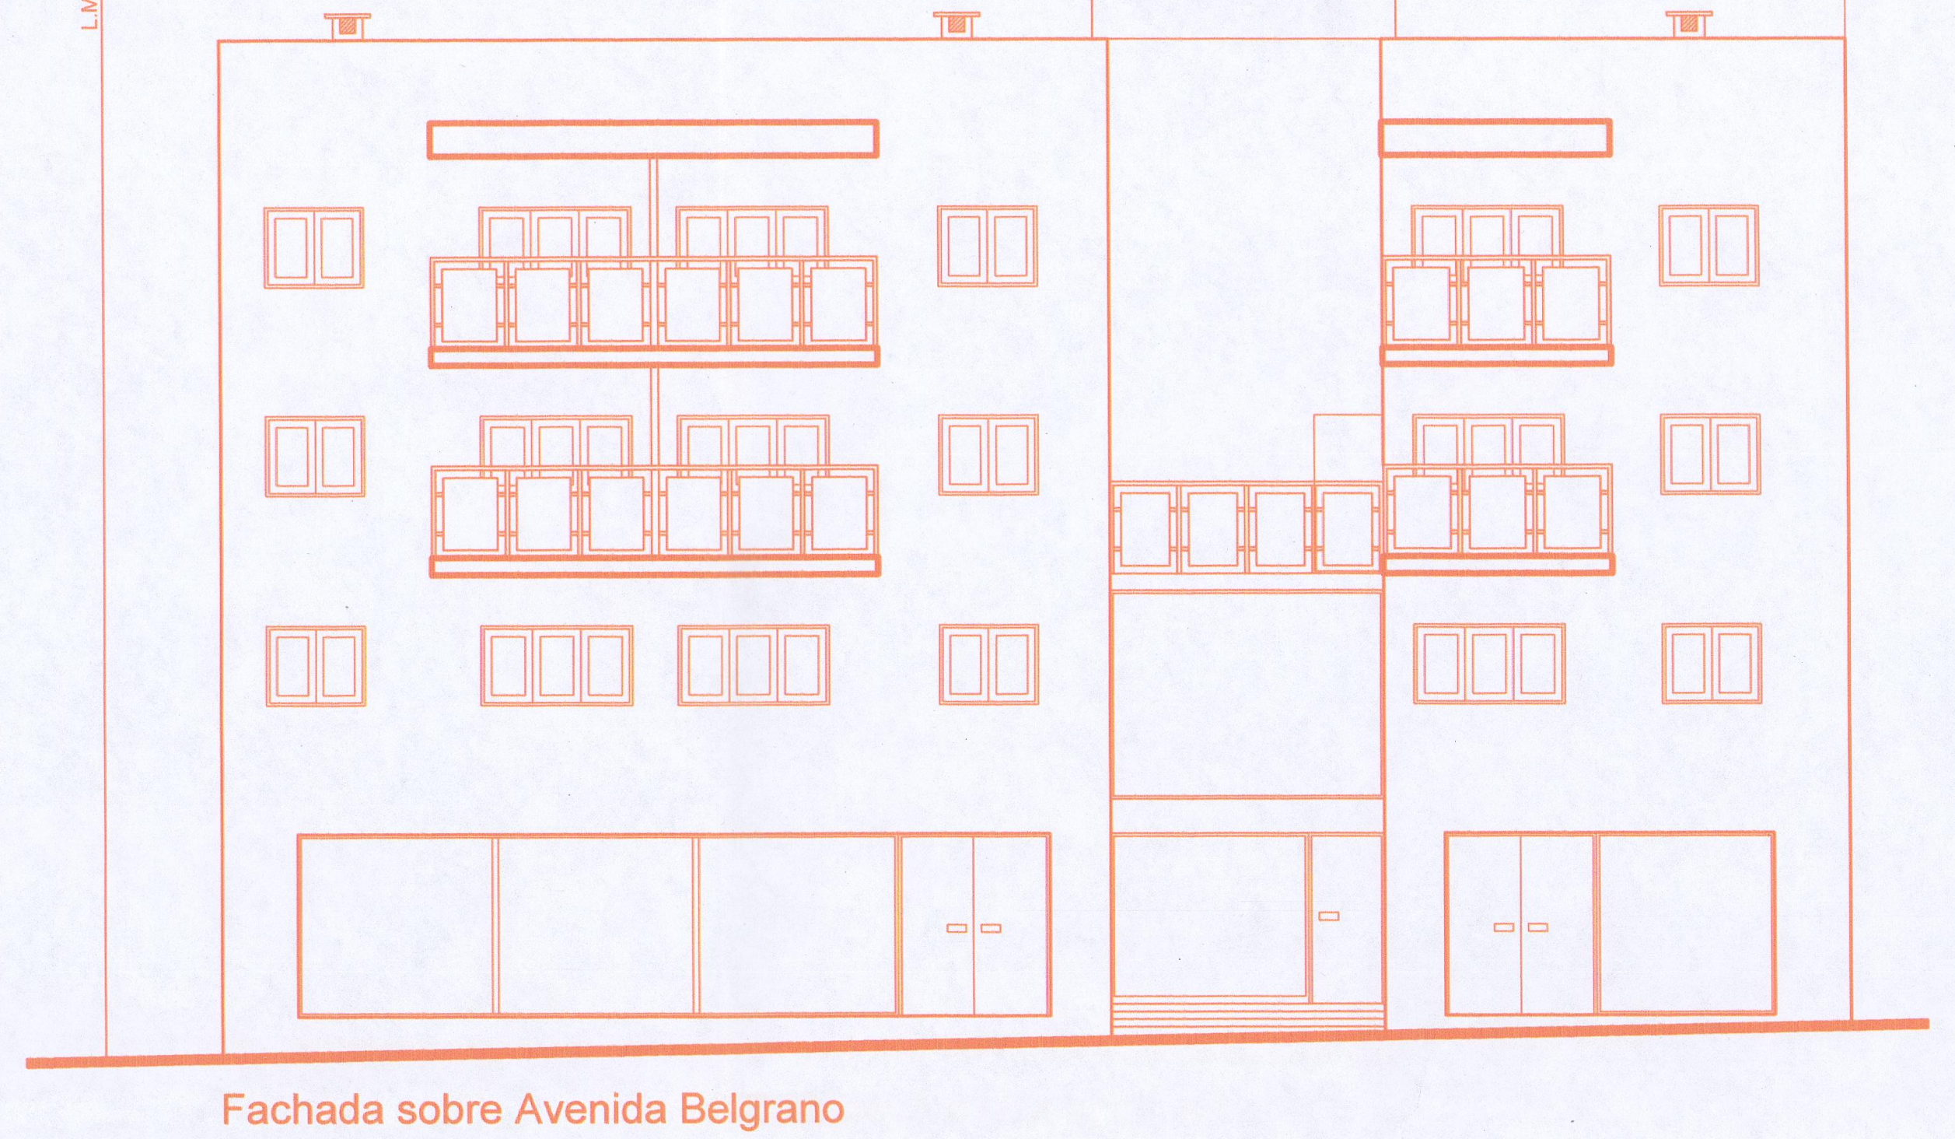
Fachada sobre Avenida Belgrano

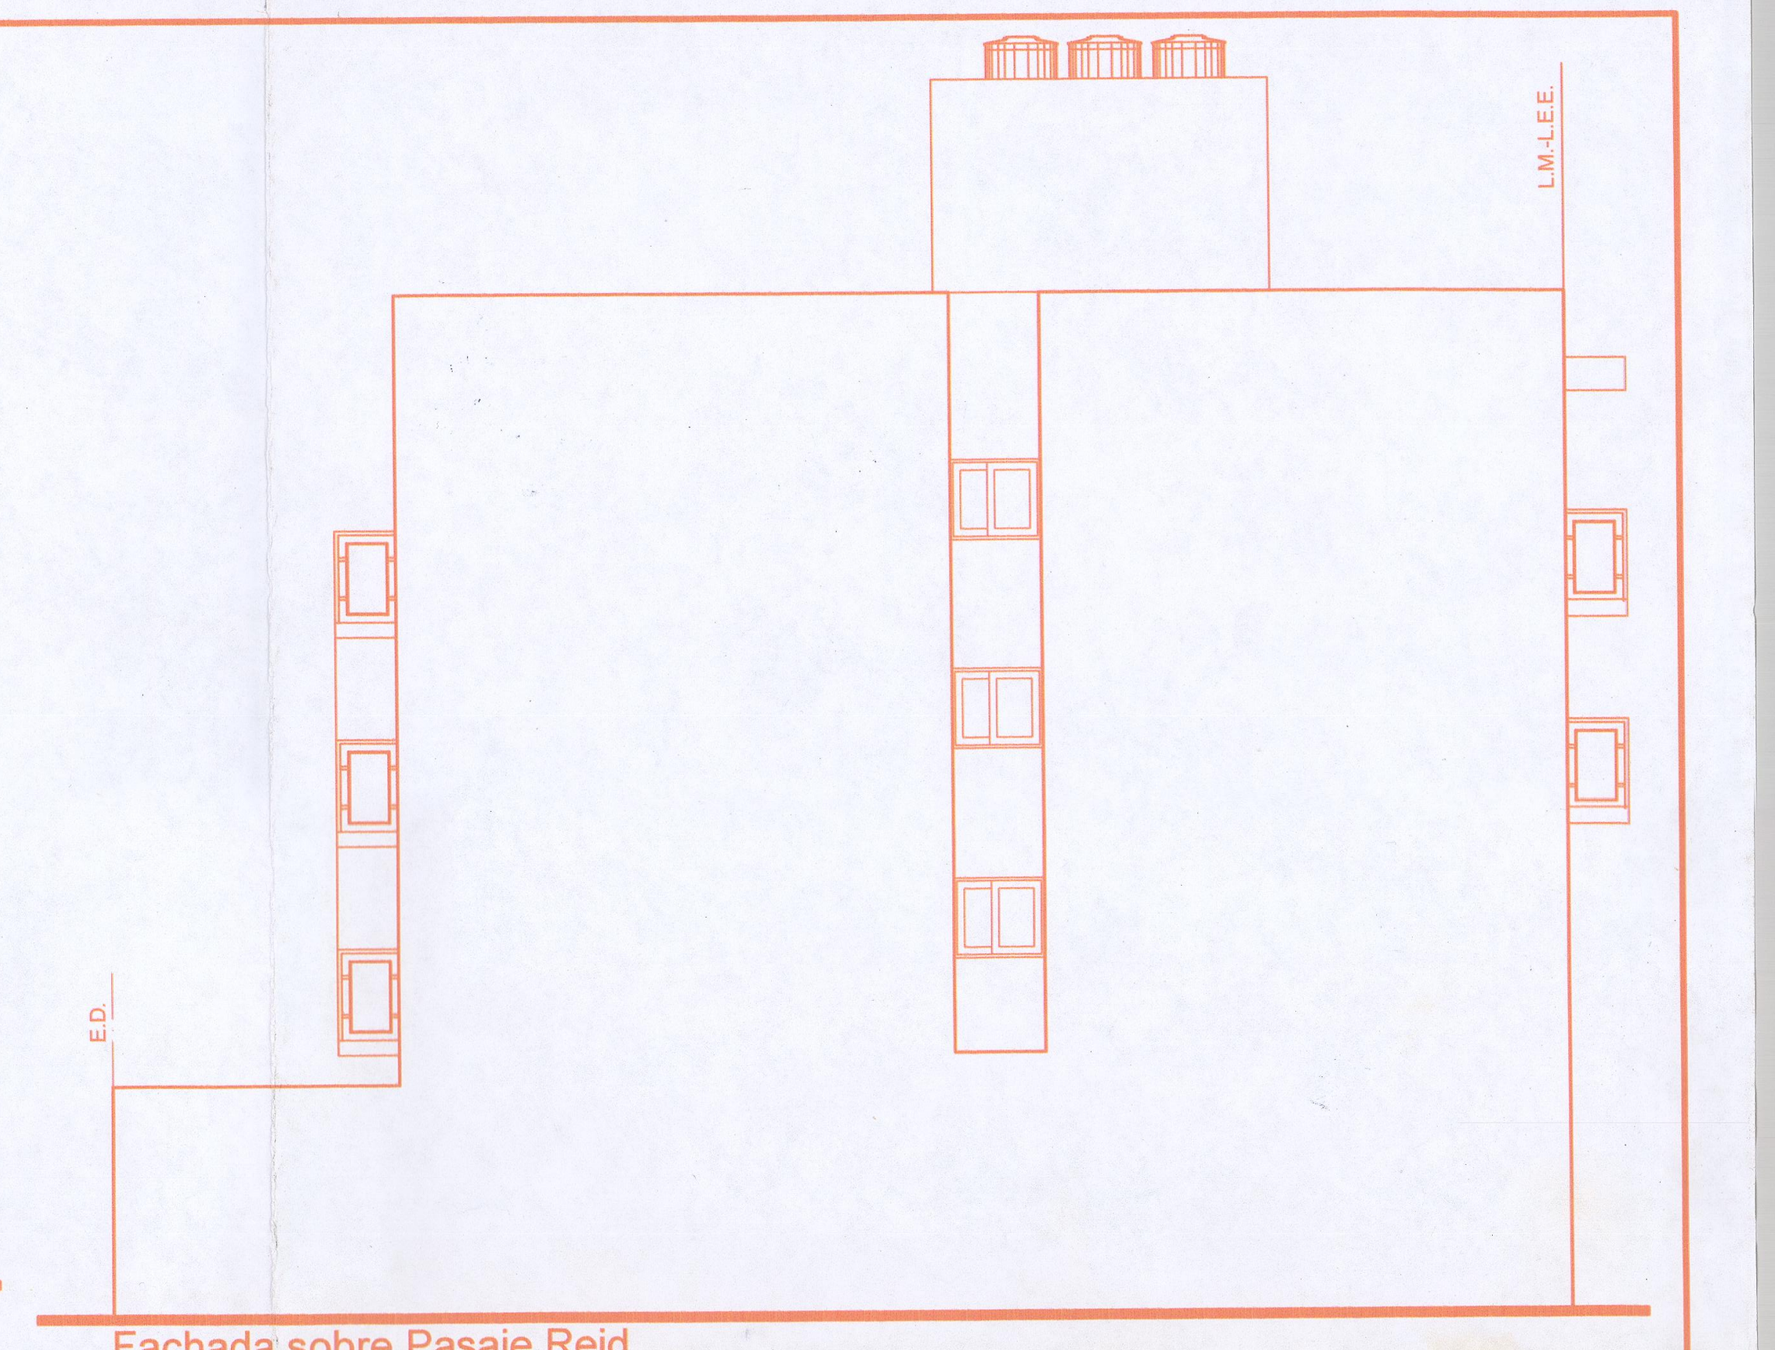
Fachada sobre Pasaje Reid

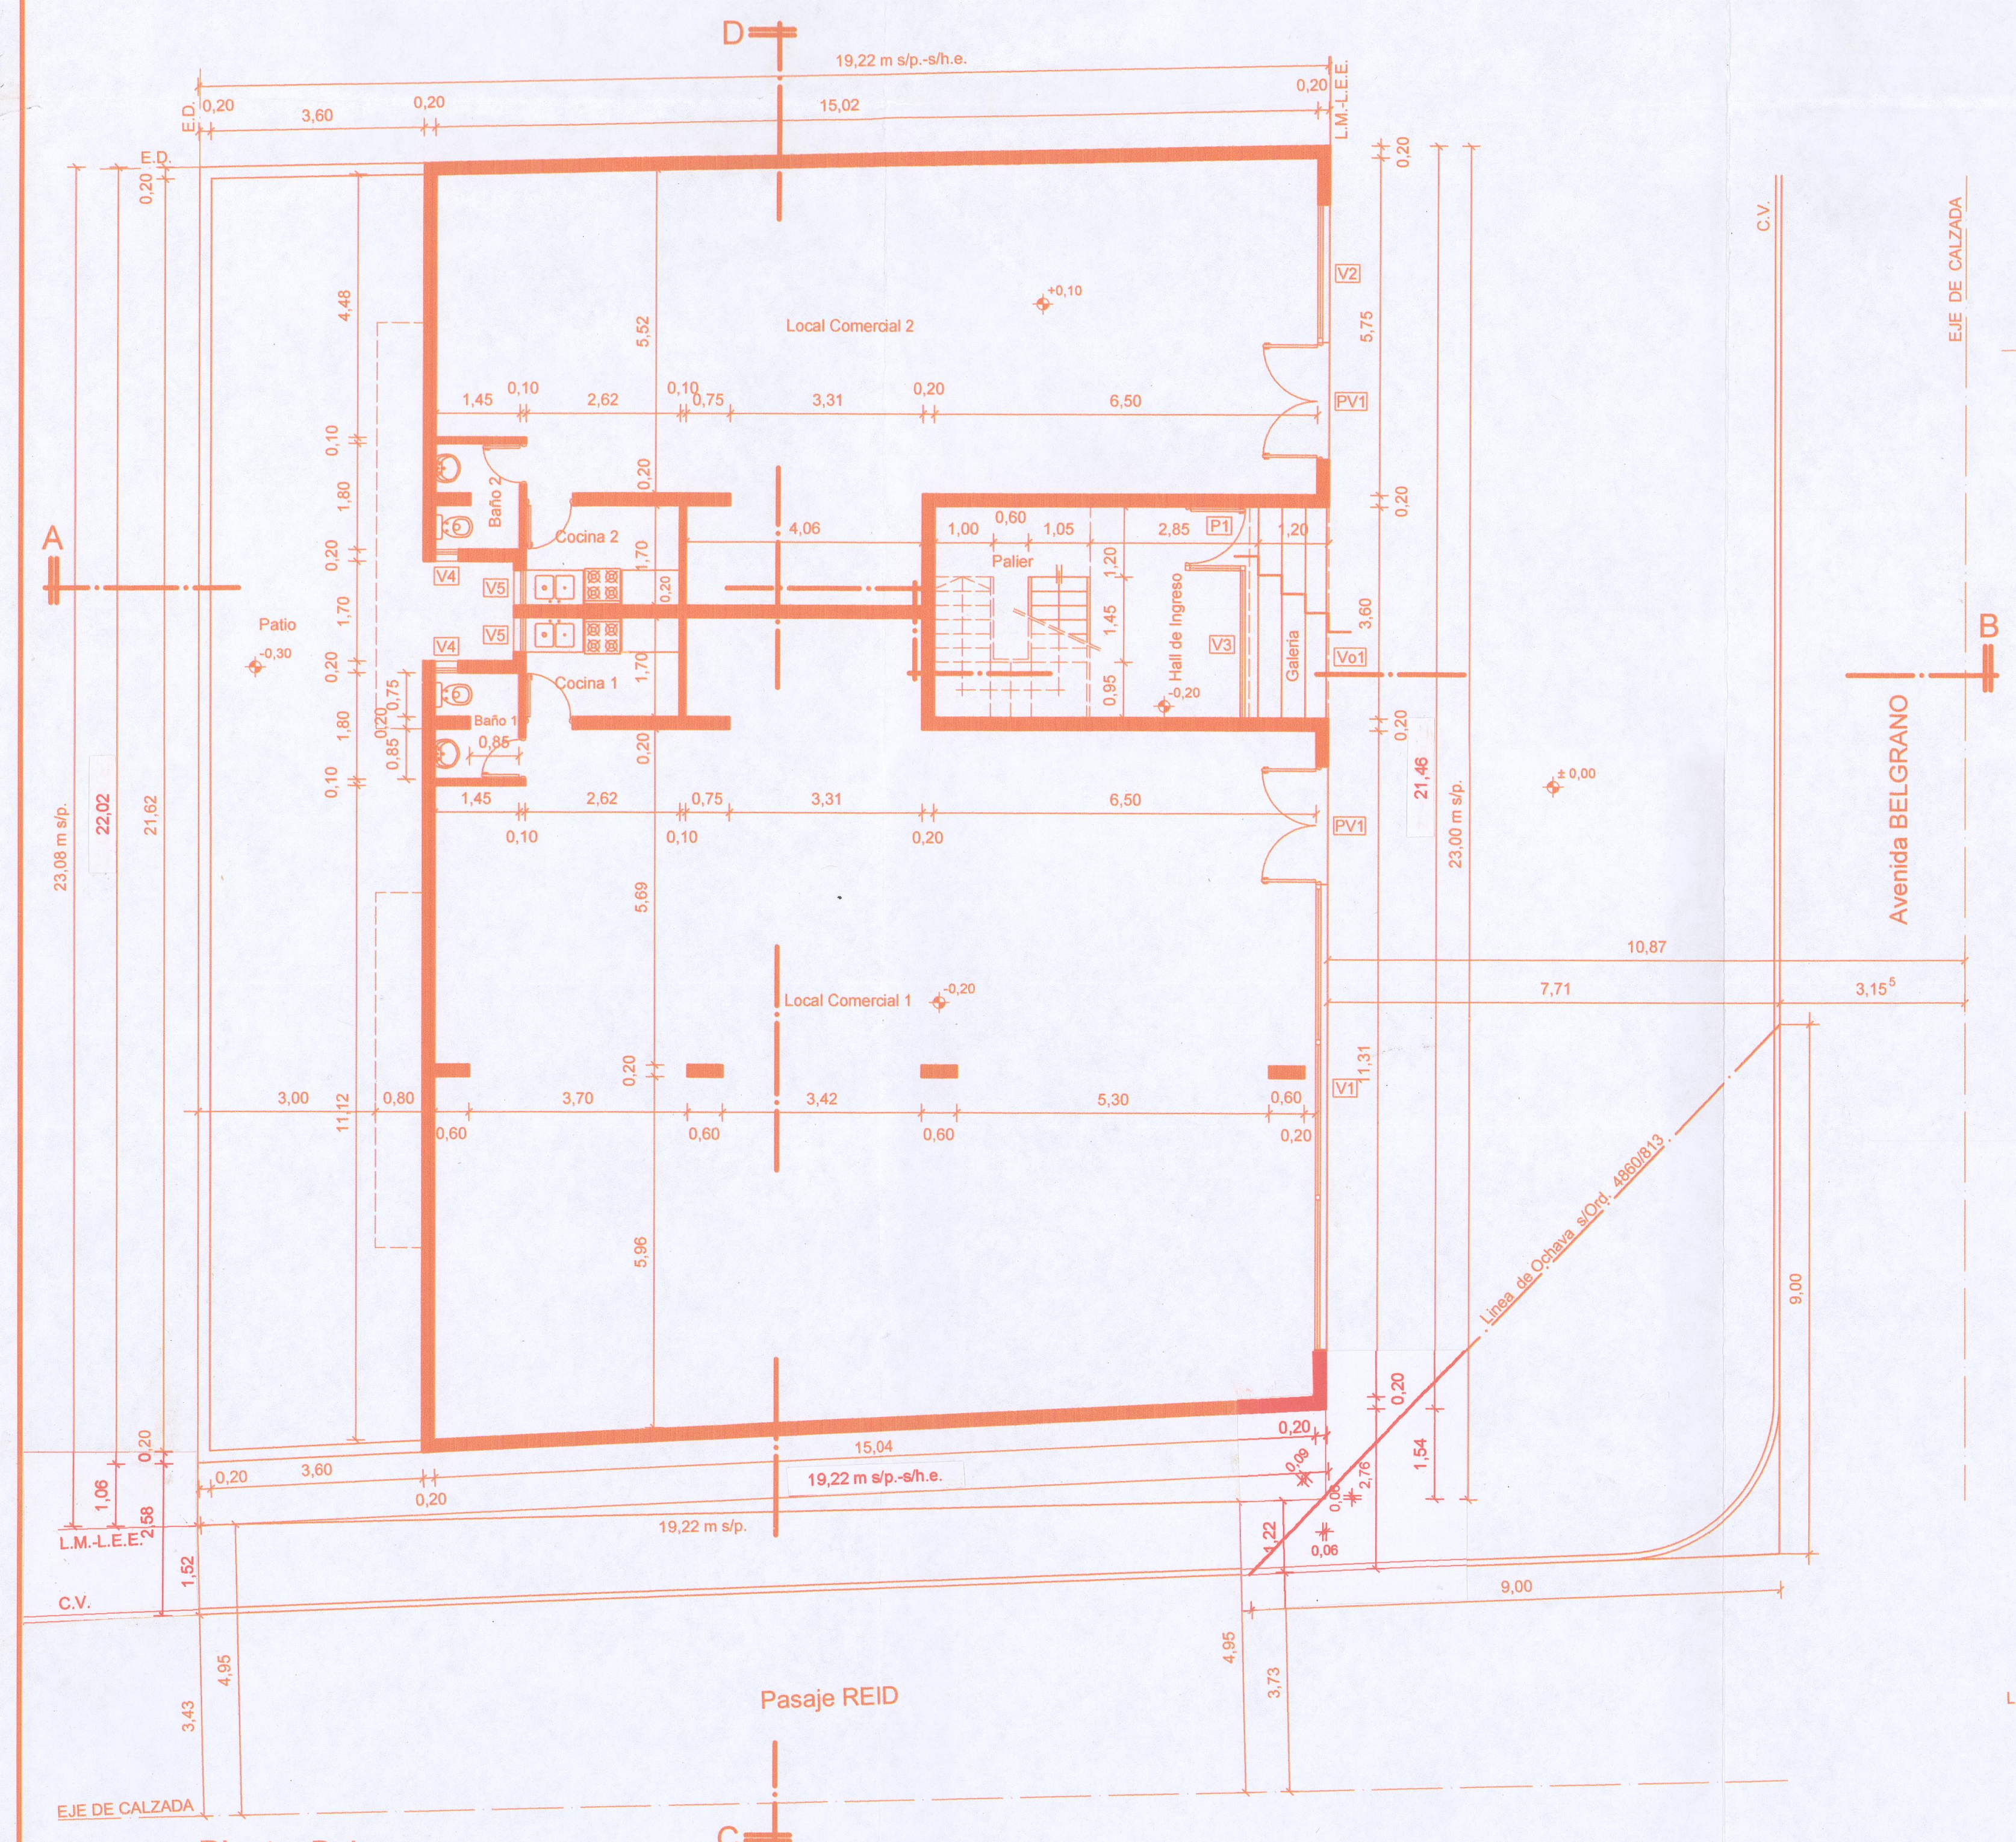
Planta Baja

Local Comercial 1
Local Comercial 2
Hall de Ingreso
Galeria
Palier
Cocina 1
Cocina 2
Baño 1
Baño 2
Patio
Avenida BELGRANO
Pasaje REID
Linea de Ochava s/Ord. 4860/813
19,22 m s/p.-s/h.e.
23,00 m s/p.
EJE DE CALZADA
L.M.-L.E.E.
C.V.
A
B
C
D

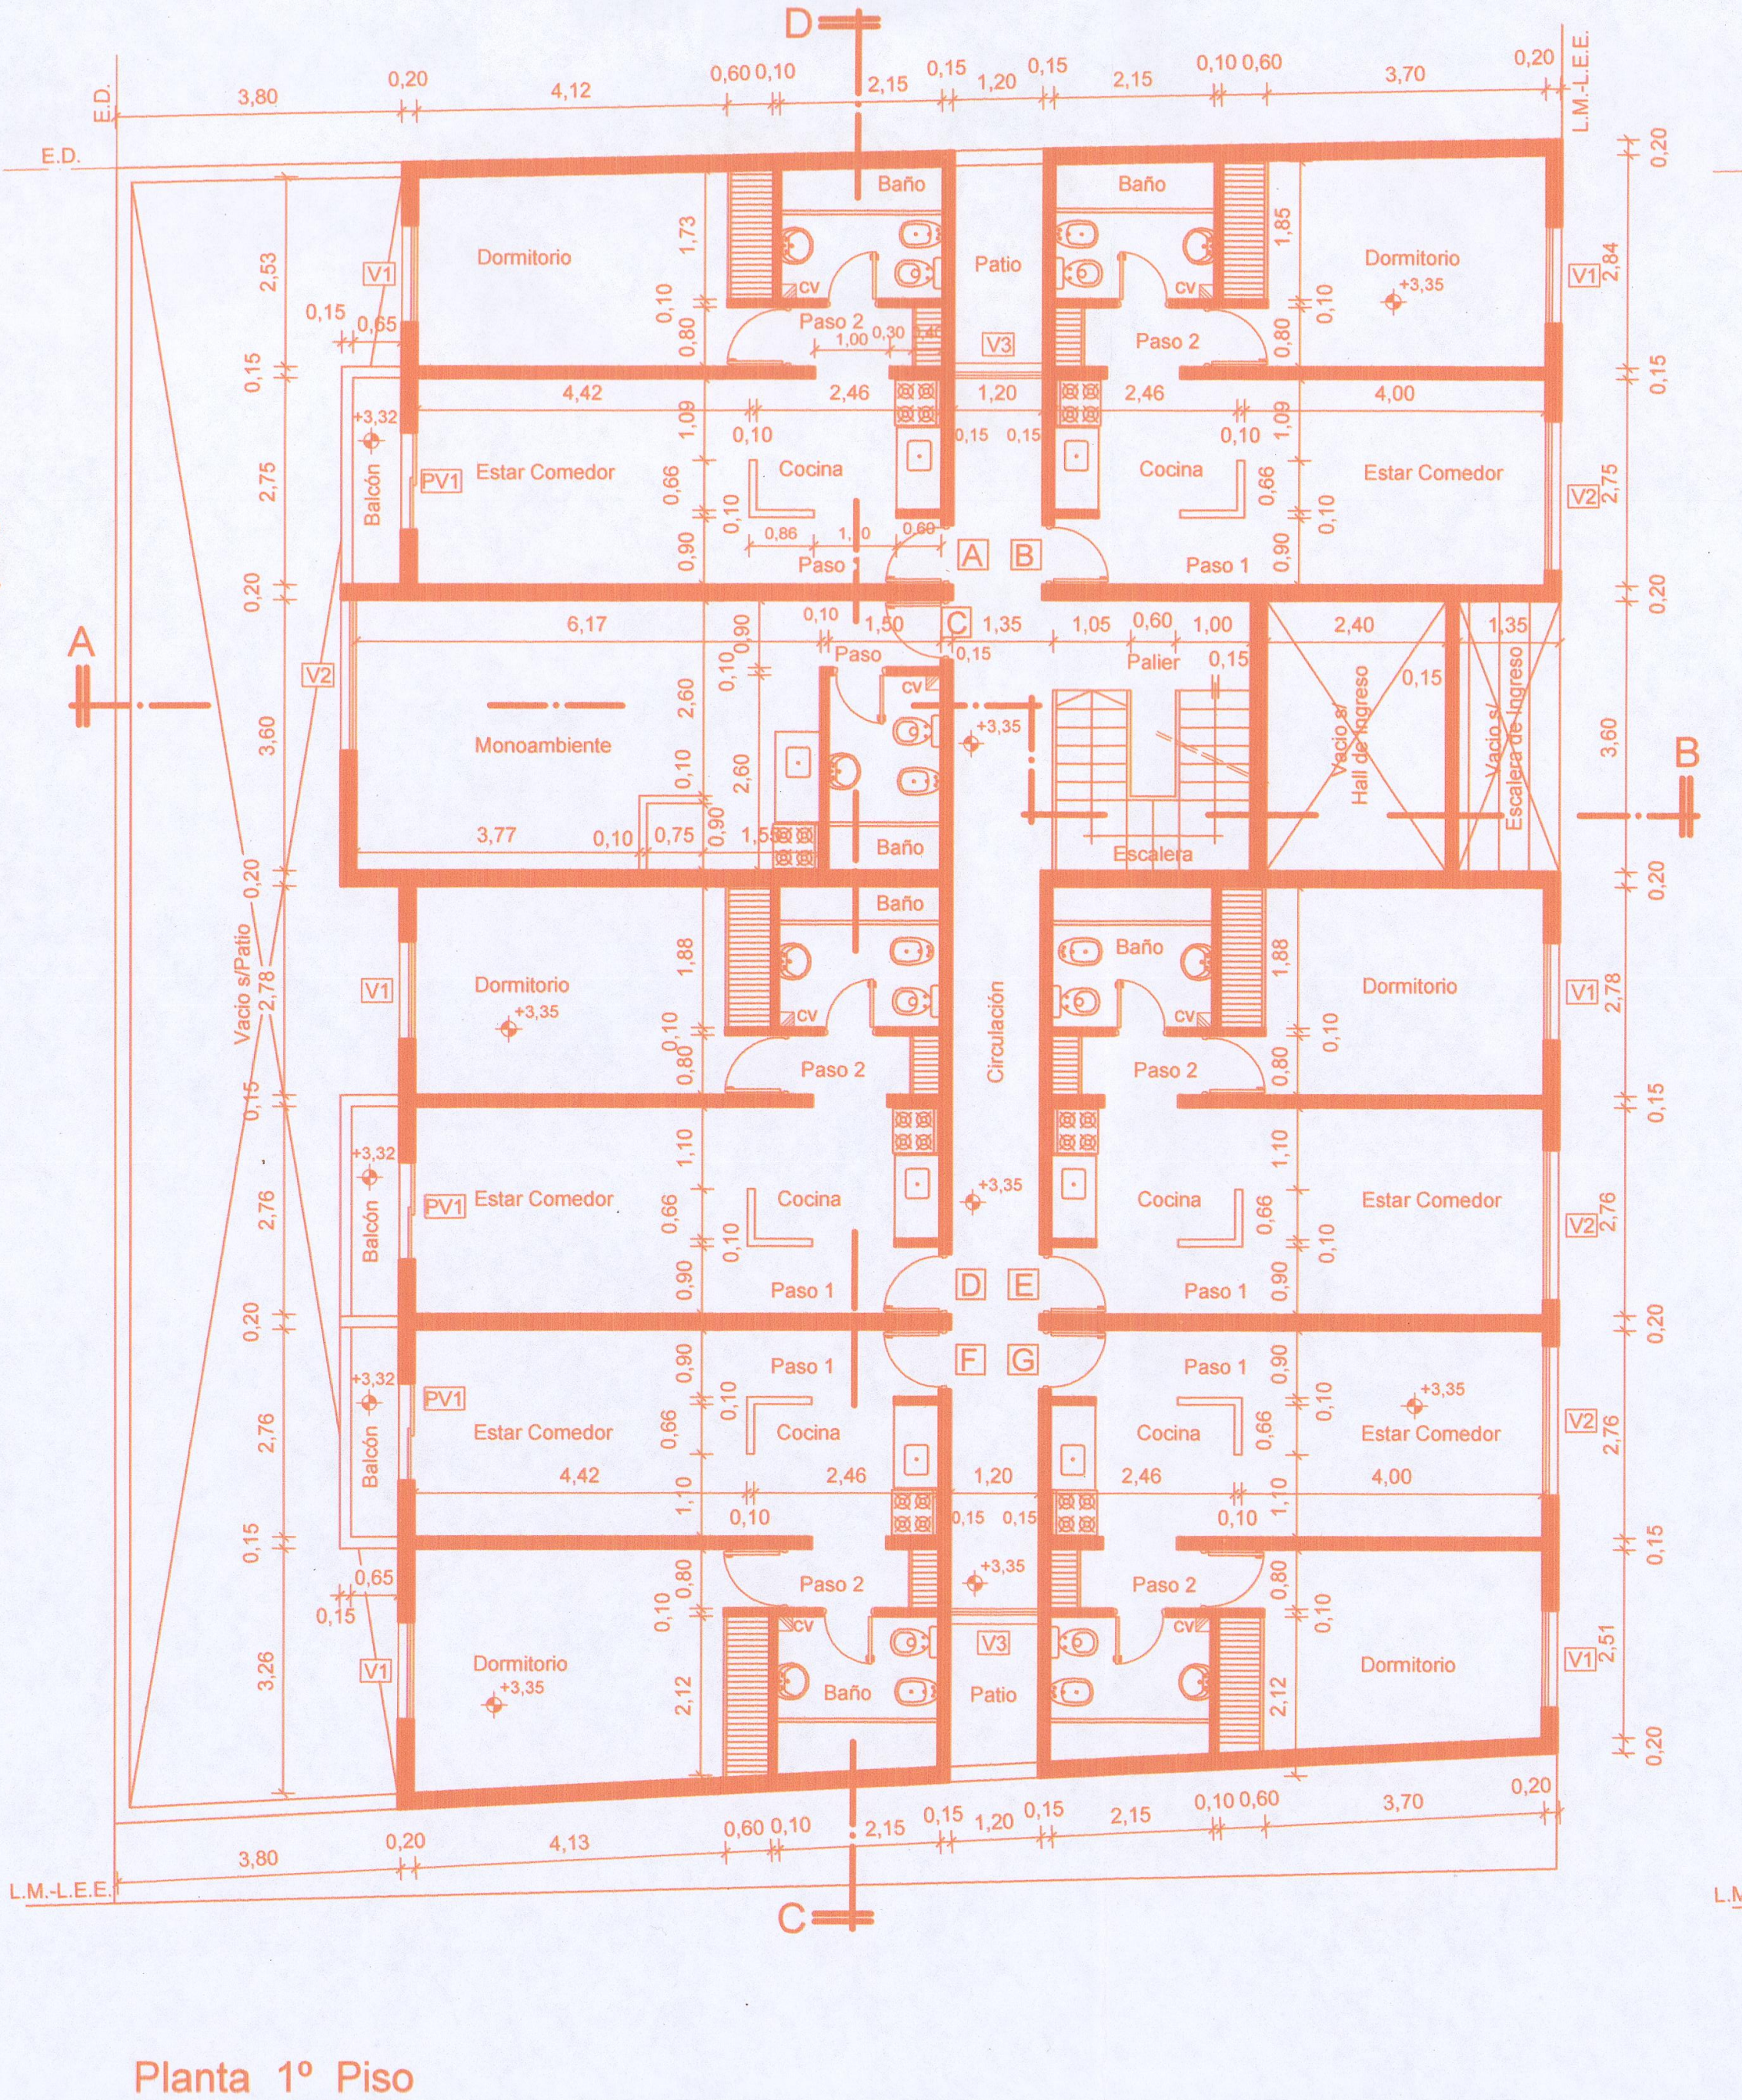
Planta 1º Piso

Dormitorio
Estar Comedor
Cocina
Paso 1
Paso 2
Baño
Patio
Balcón
Monoambiente
Circulación
Palier
Escalera
Vacío s/ Hall de Ingreso
Escalera de Ingreso
Vacío s/Patio
+3,35
A
B
C
D
E
F
G
L.M.-L.E.E.

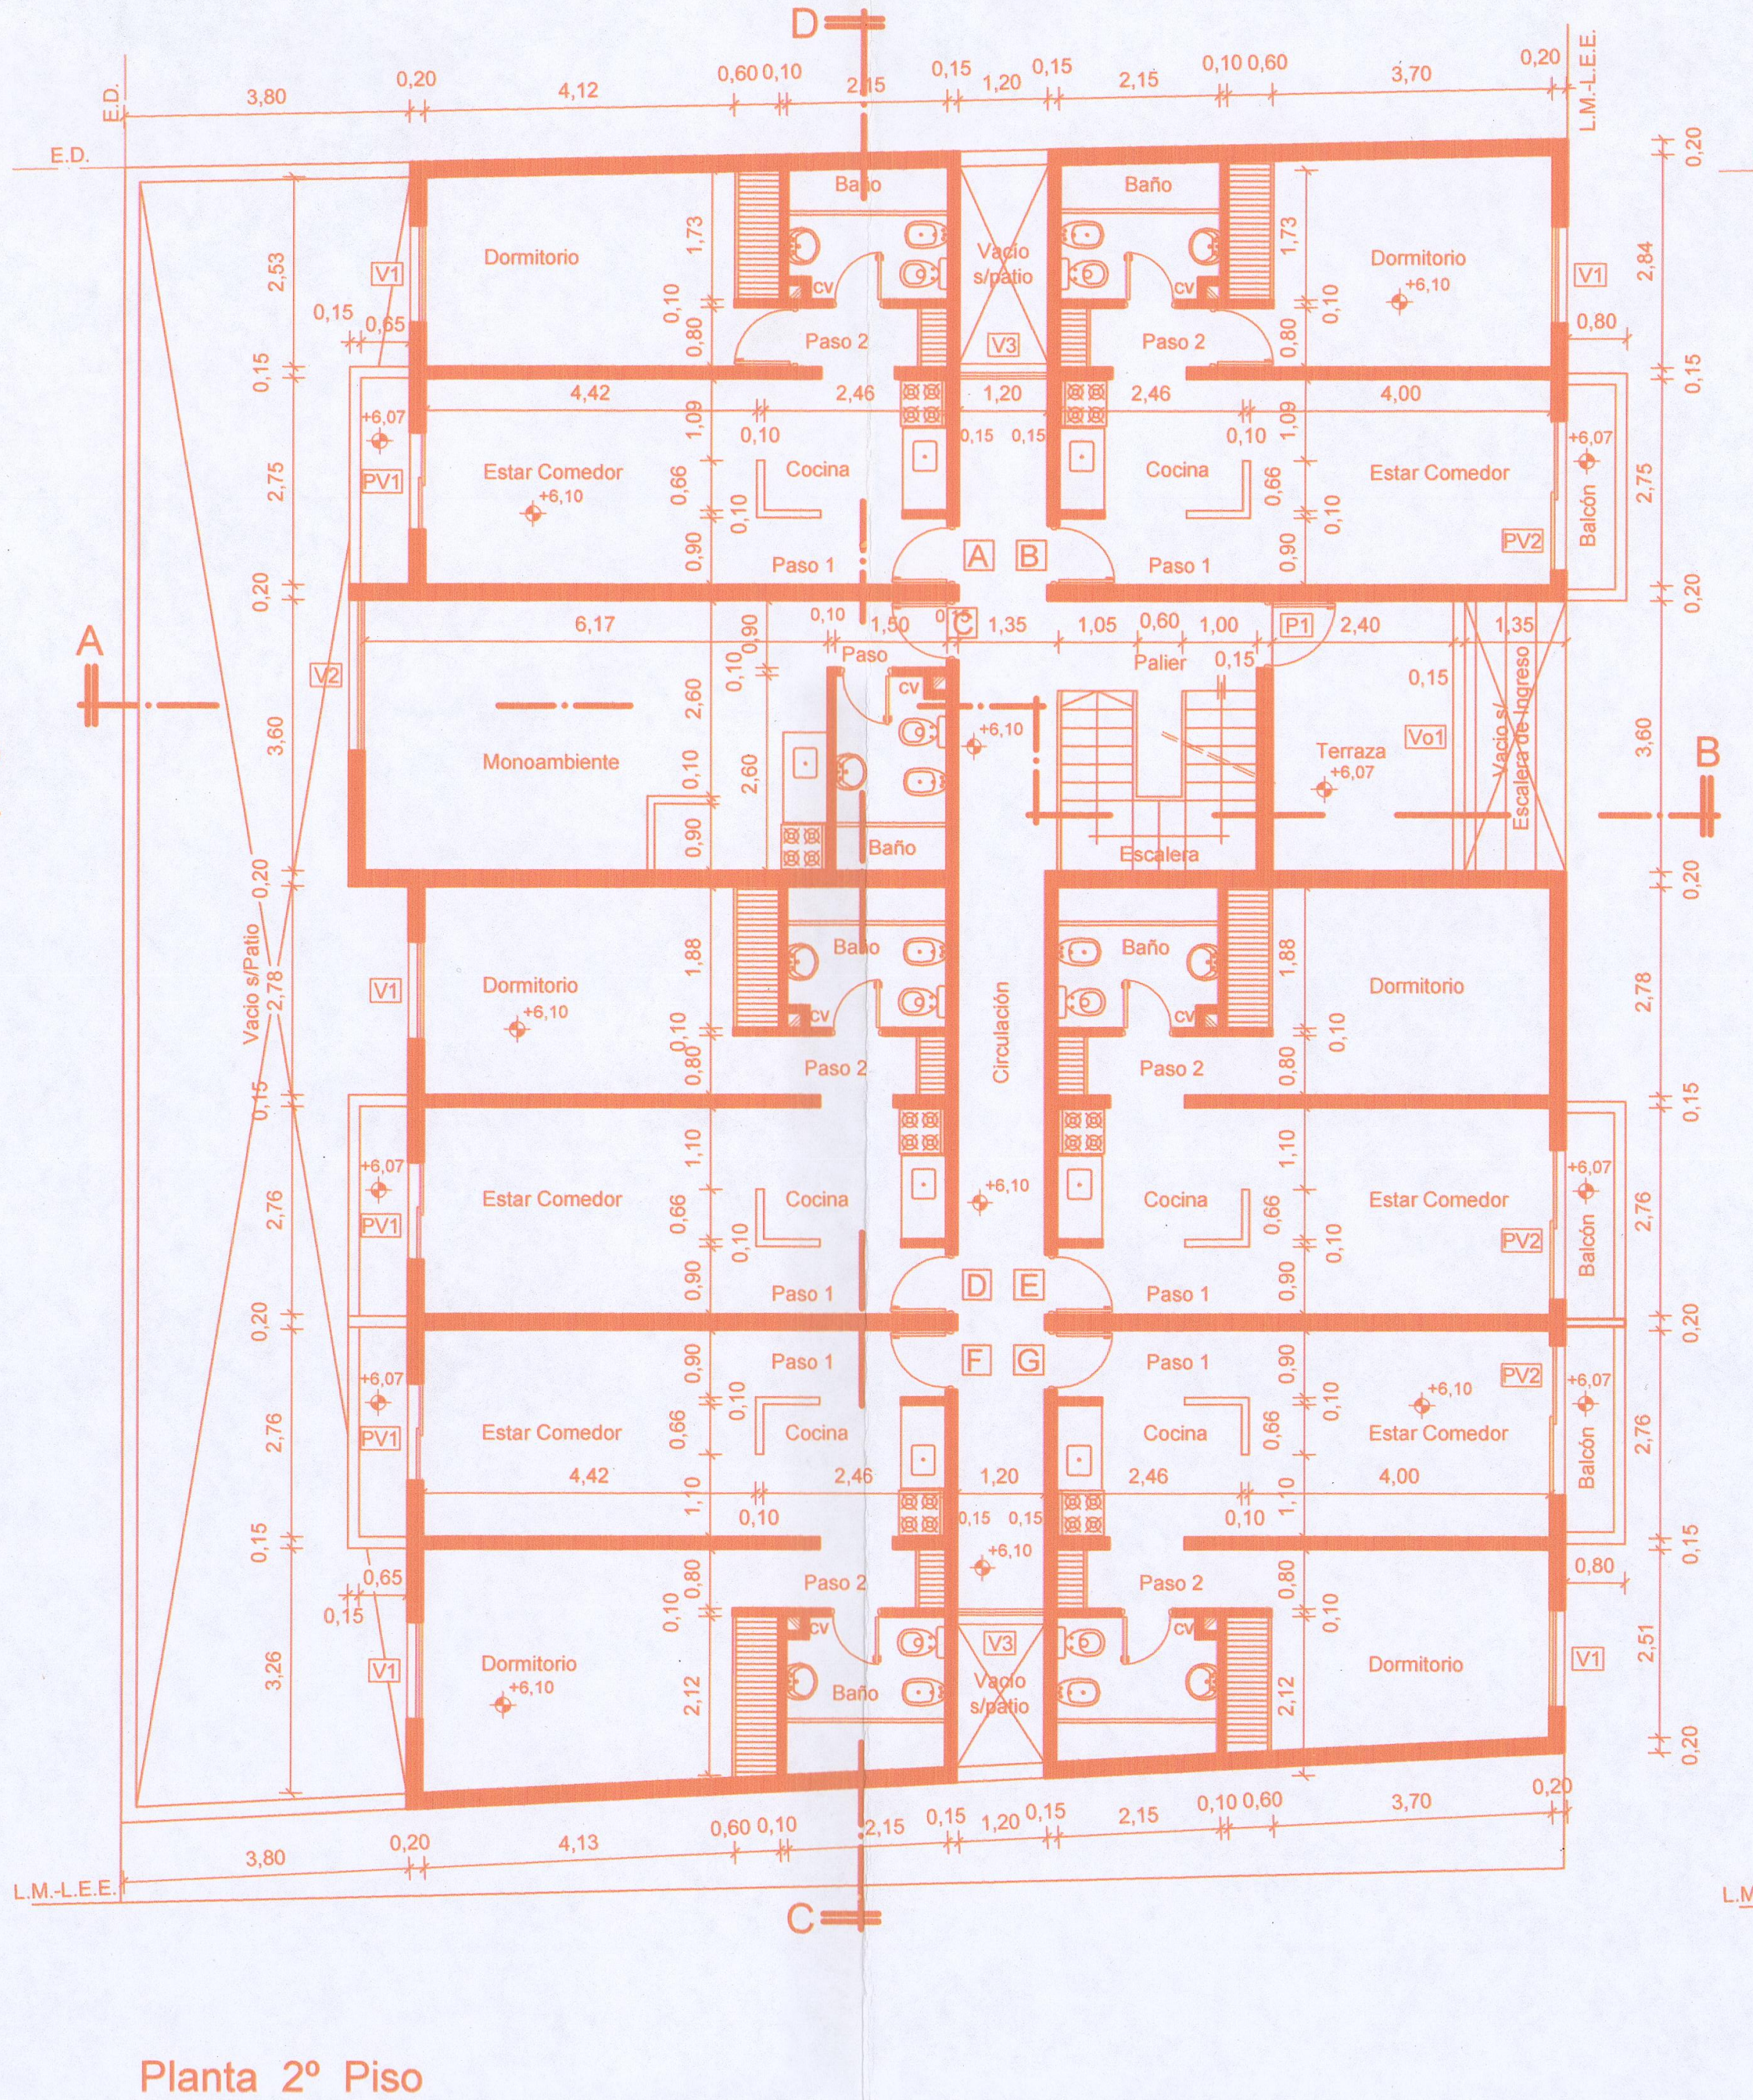
Planta 2º Piso

Dormitorio
Estar Comedor
Cocina
Paso 1
Paso 2
Baño
Balcón
Monoambiente
Circulación
Palier
Escalera
Terraza +6,07
Vacío s/Patio
+6,10
A
B
C
D
E
F
G
L.M.-L.E.E.

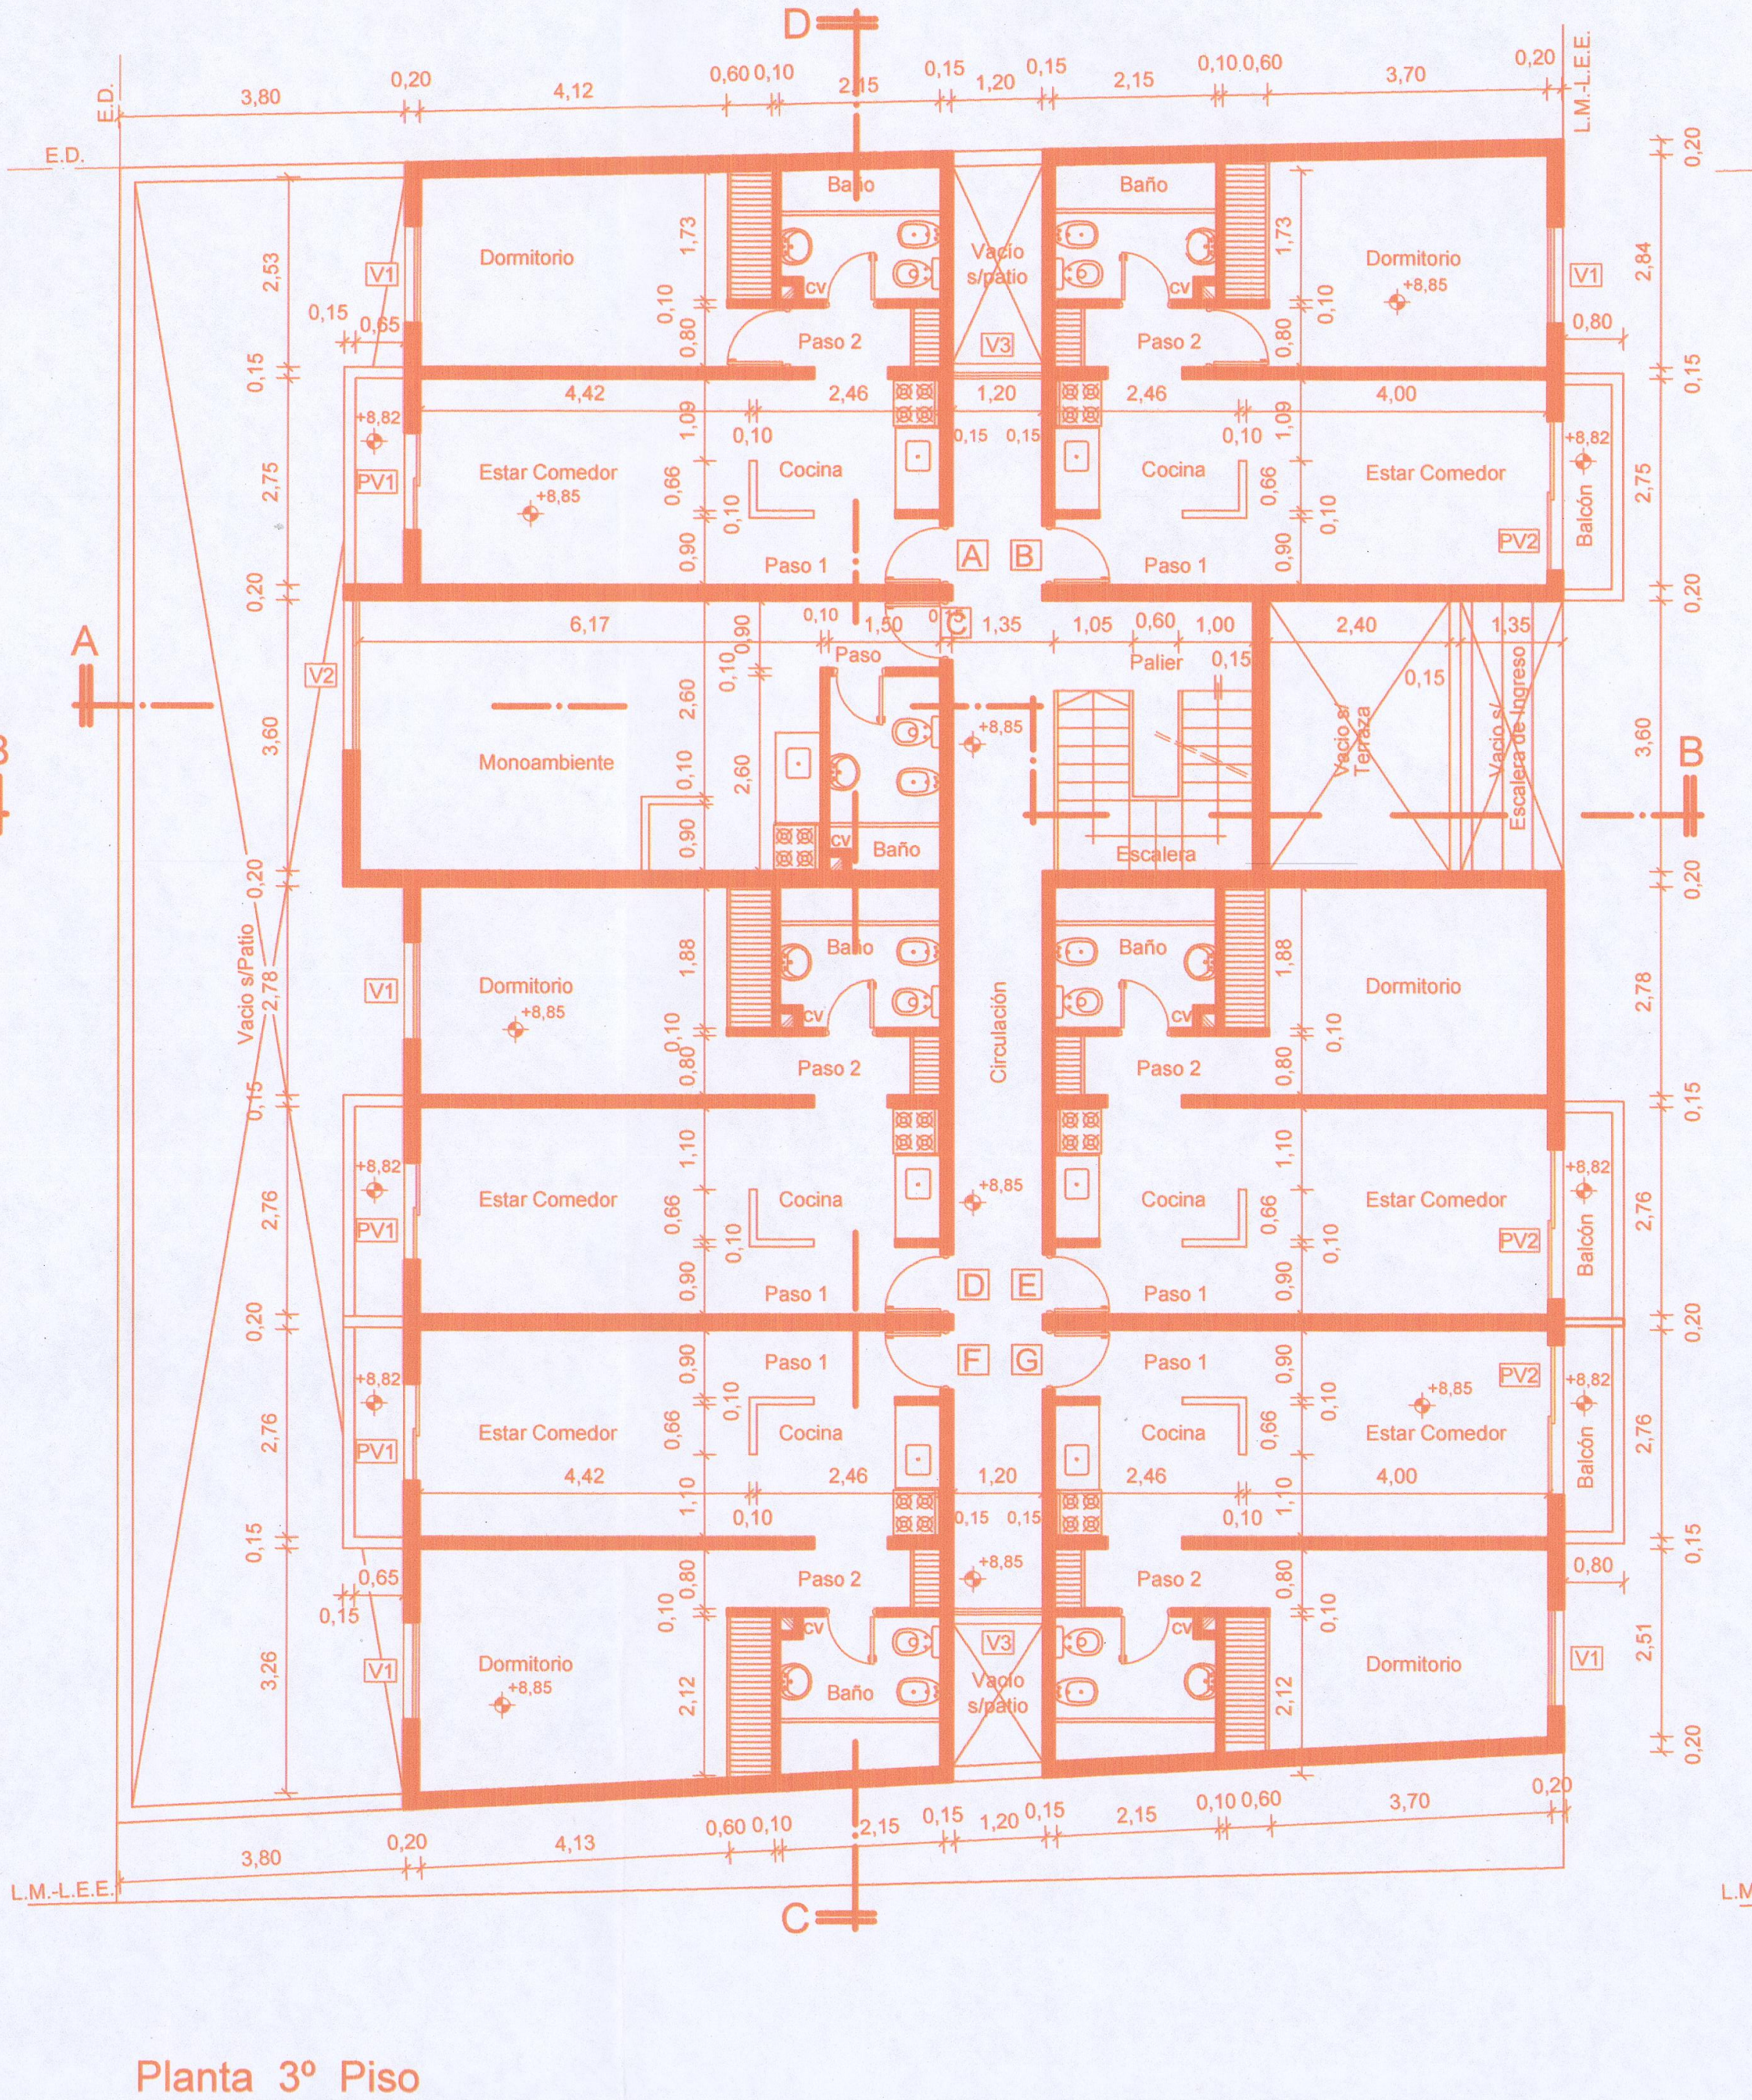
Planta 3º Piso

Dormitorio
Estar Comedor
Cocina
Paso 1
Paso 2
Baño
Balcón
Monoambiente
Circulación
Palier
Escalera
Vacío s/ Terraza
Vacío s/Patio
+8,85
A
B
C
D
E
F
G
L.M.-L.E.E.

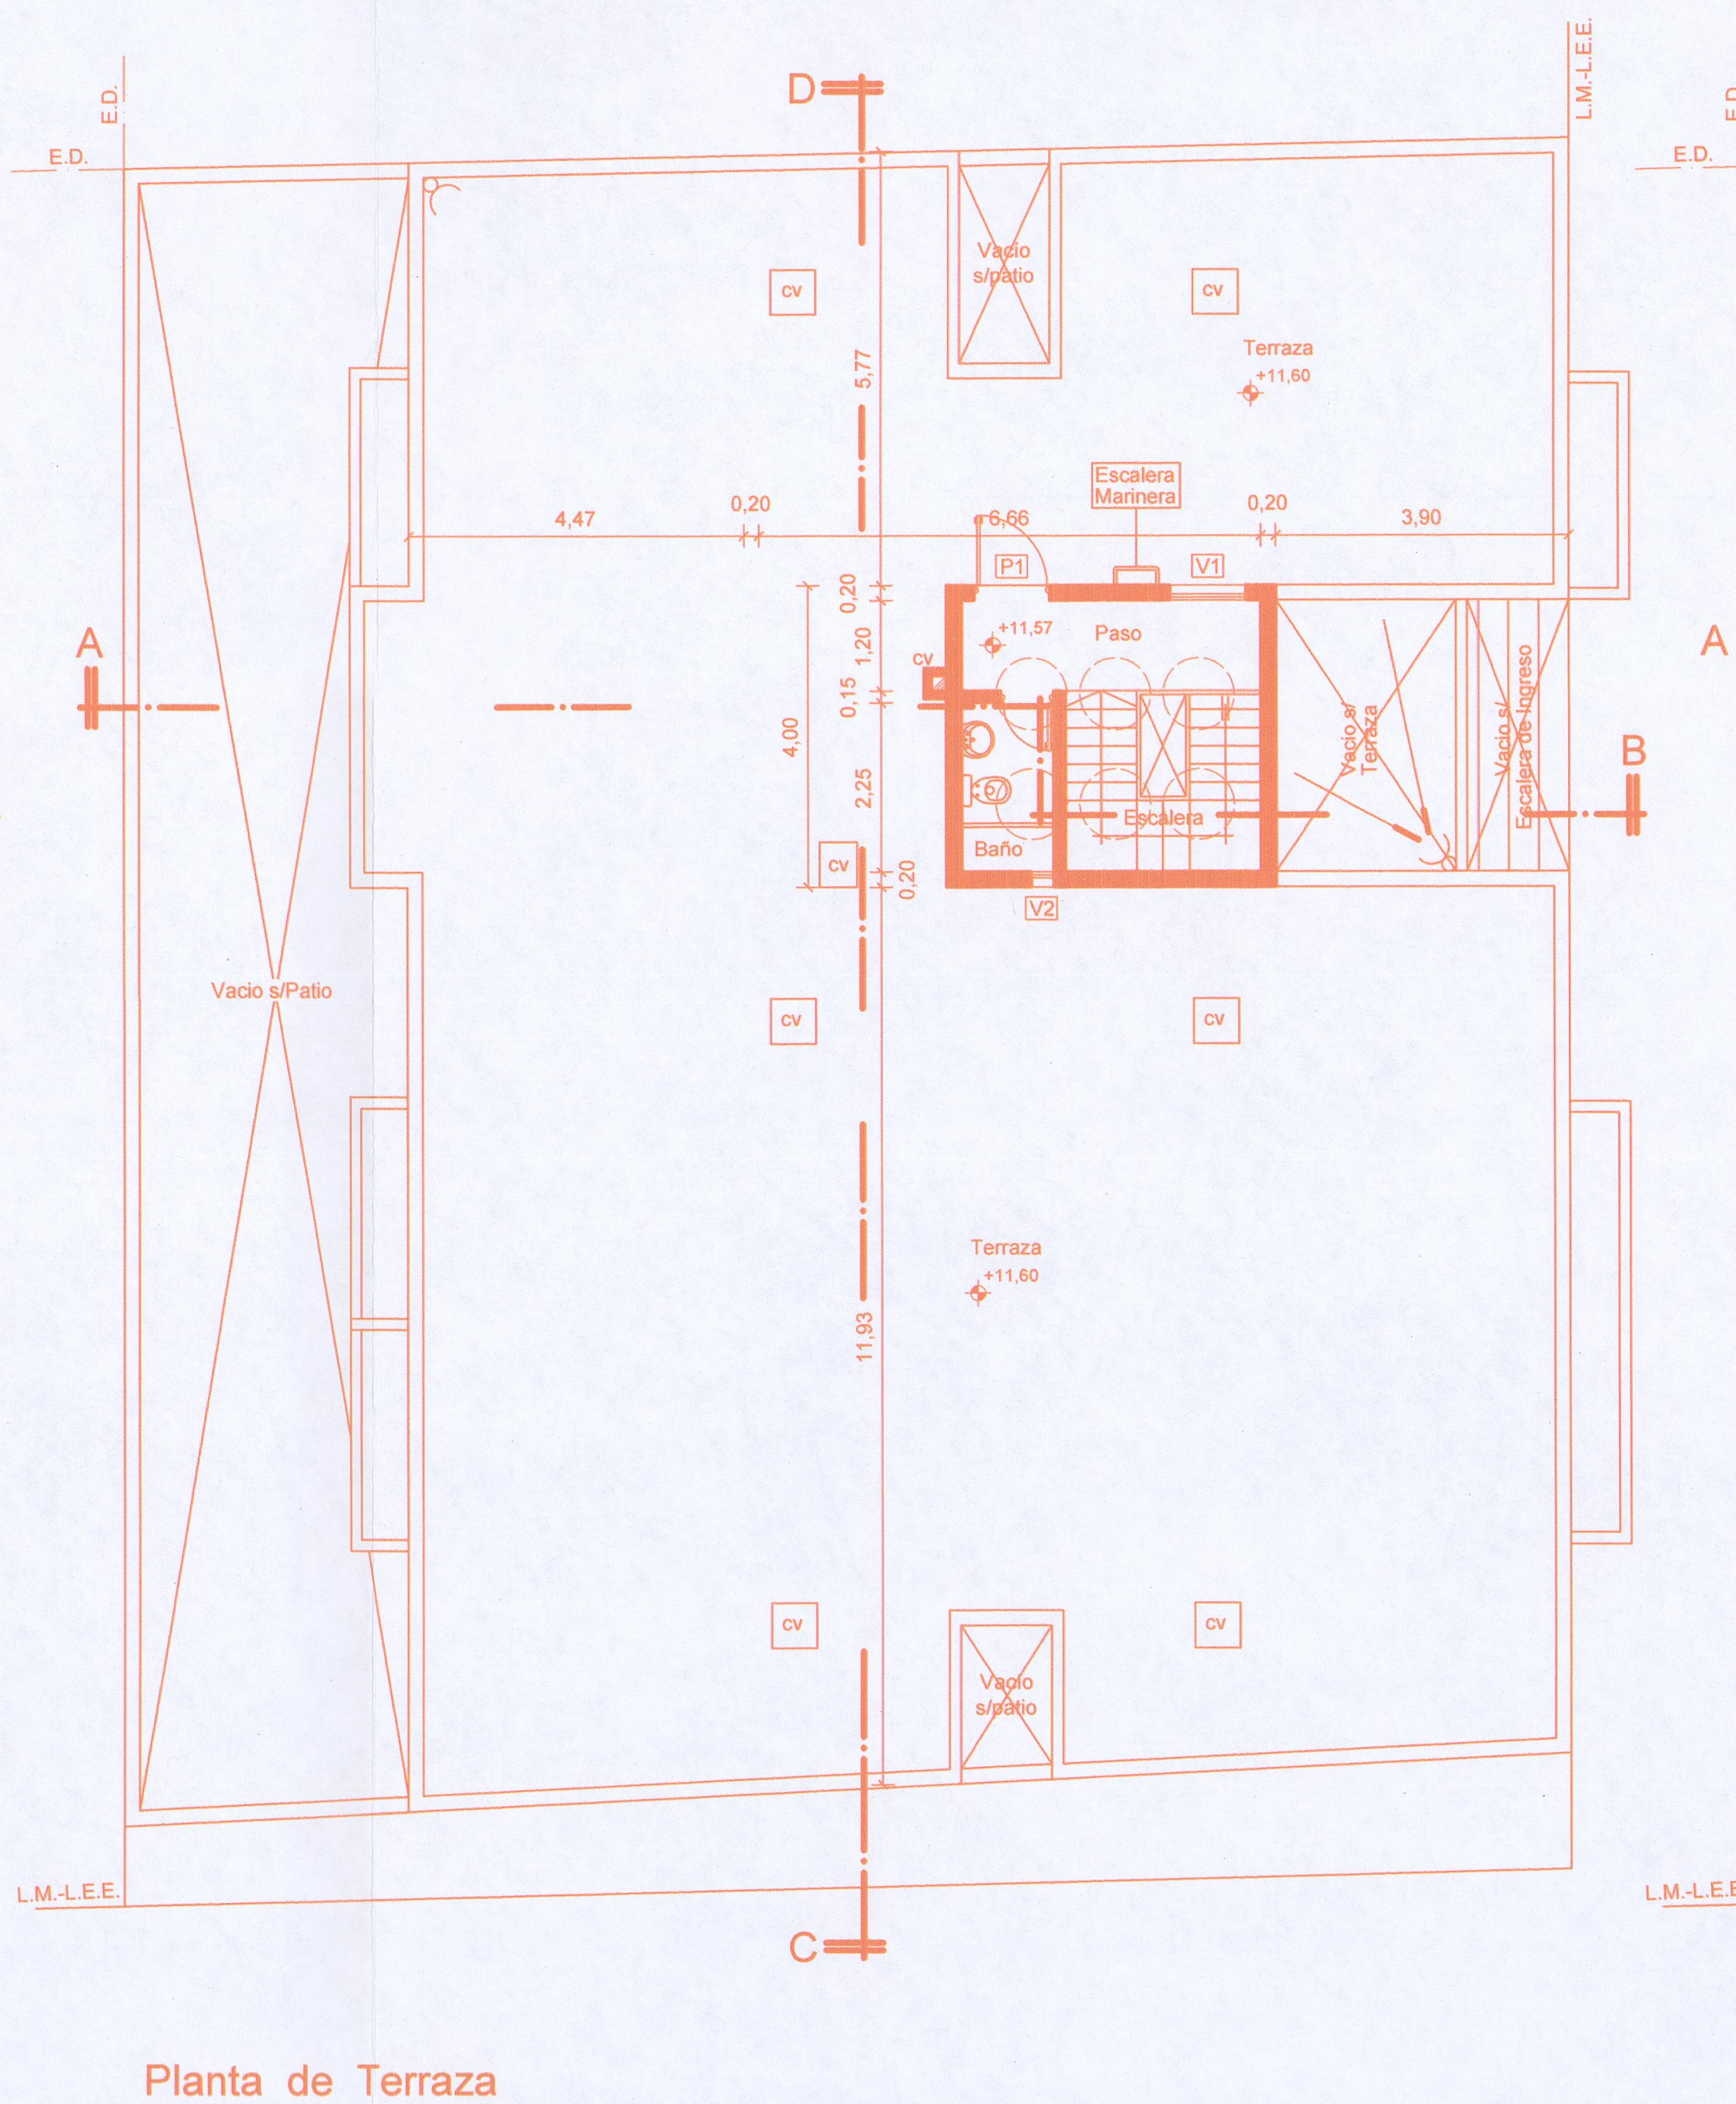
Planta de Terraza

Terraza +11,60
Escalera Marinera
Paso
Escalera
Baño
Vacío s/patio
Vacío s/Patio
cv
11,93
5,77
4,47
A
B
C
D
L.M.-L.E.E.

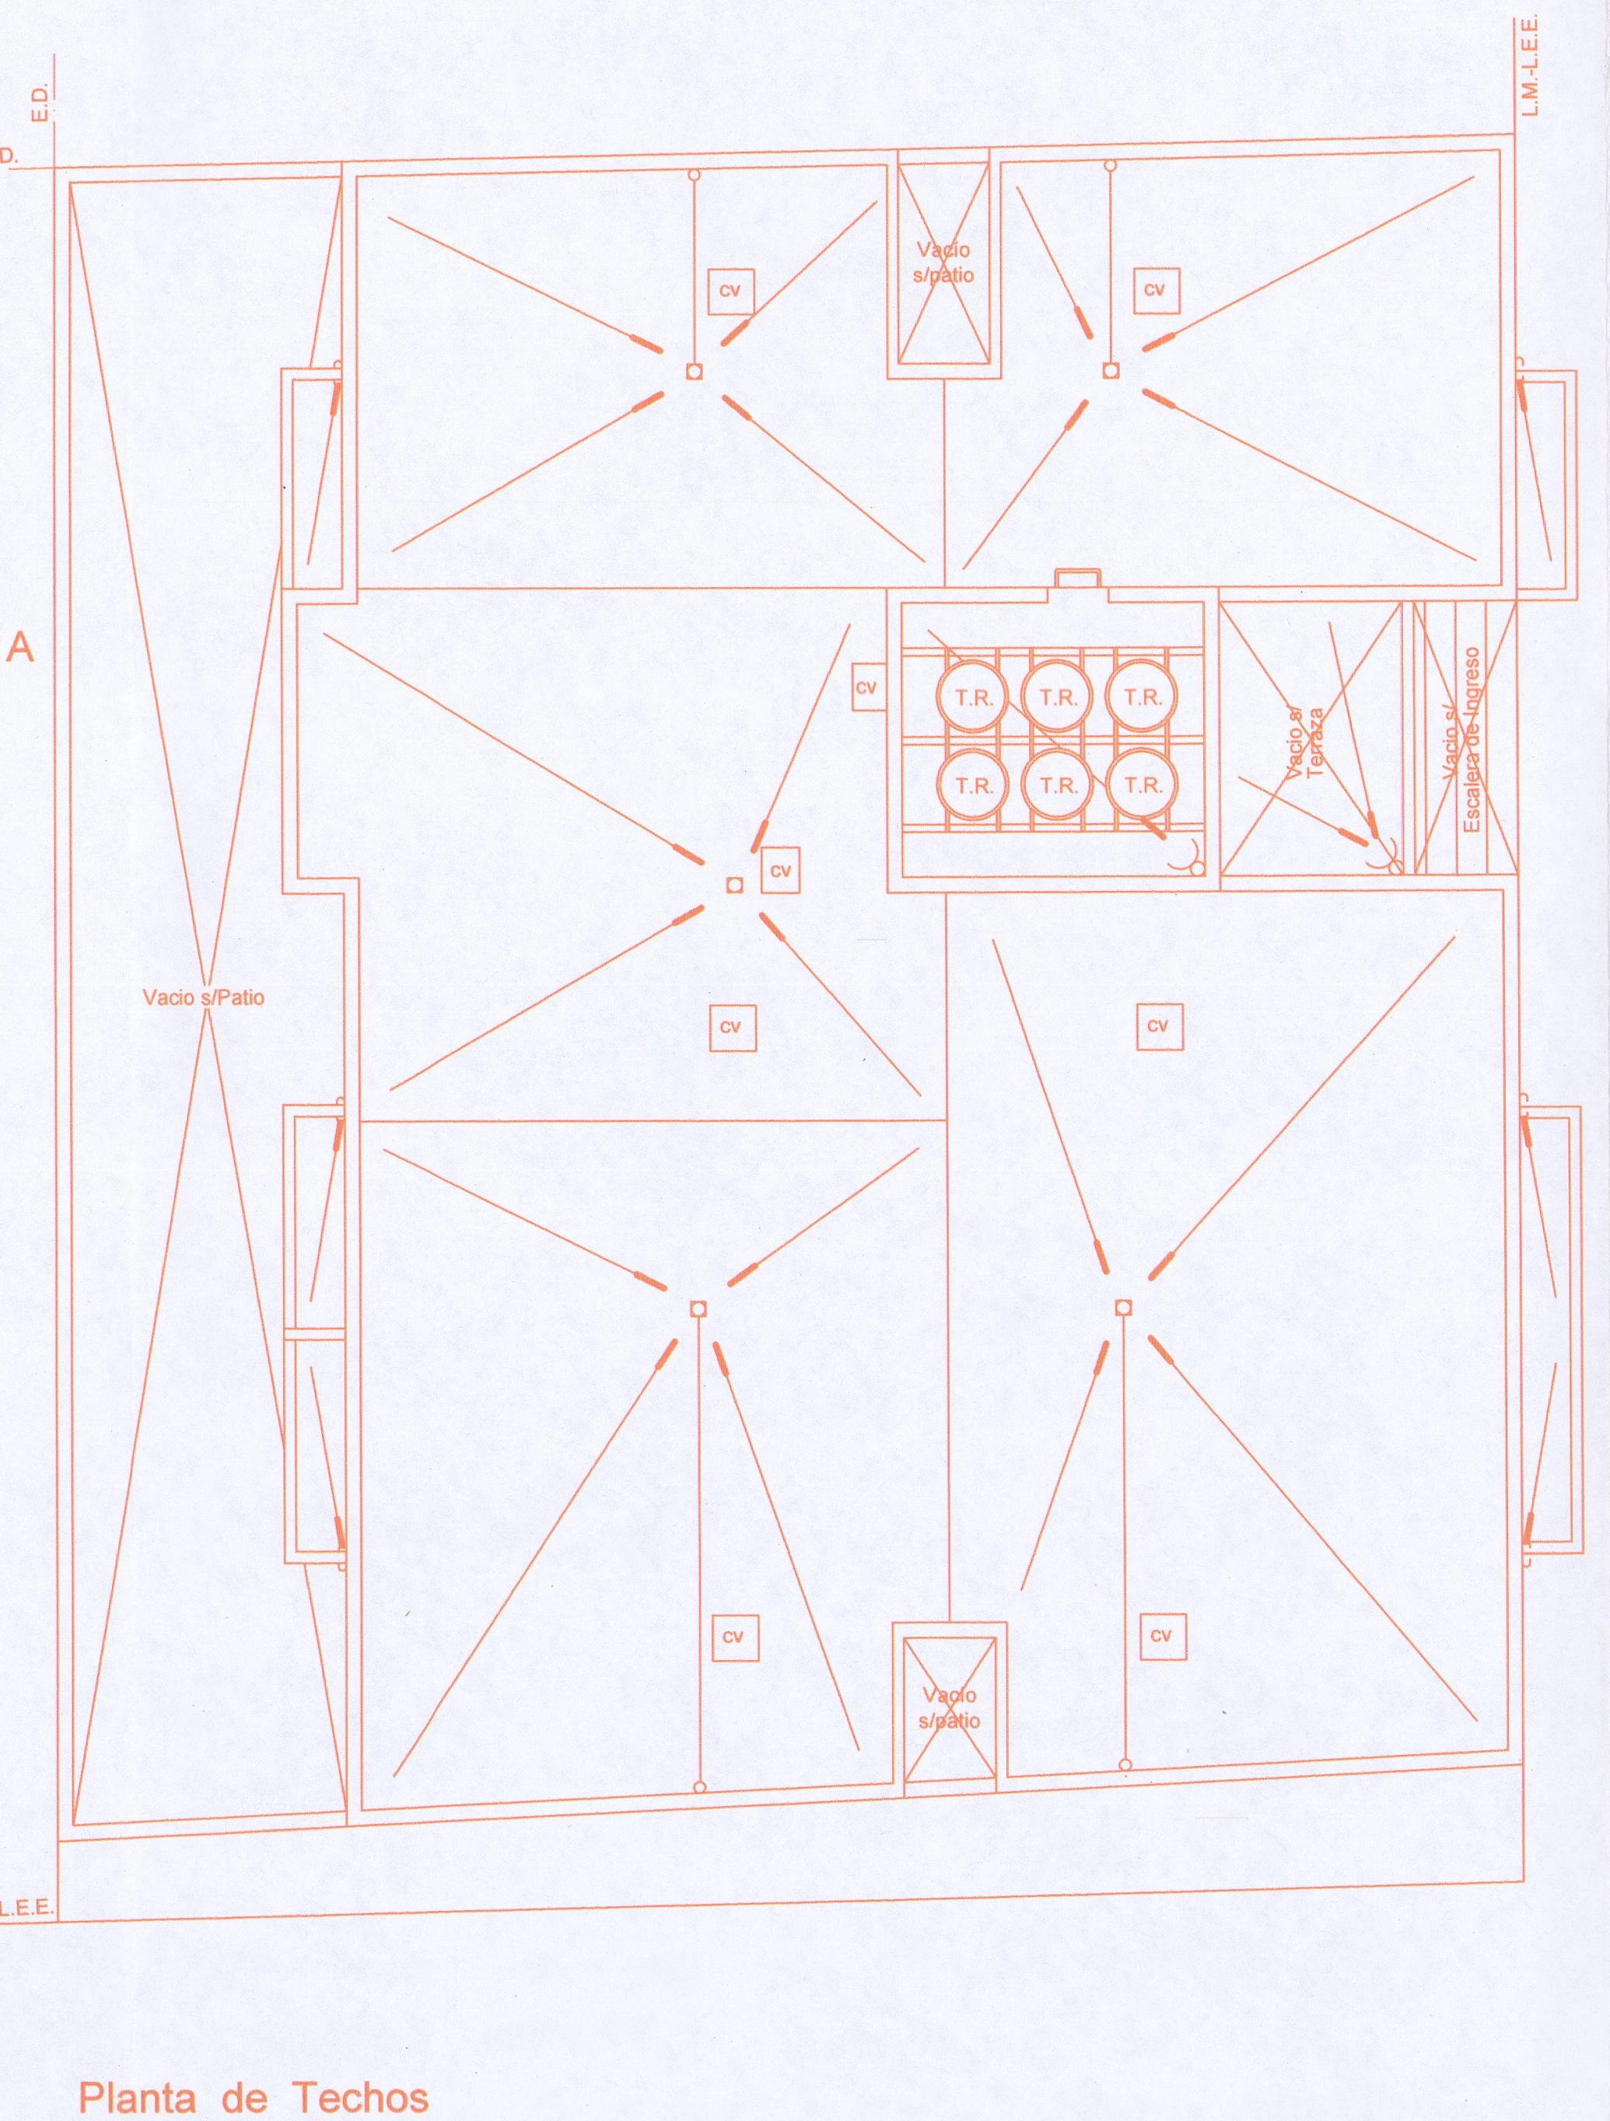
Planta de Techos

T.R.
cv
Vacío s/patio
Vacío s/Patio
Vacío s/ Terraza
Escalera de Ingreso
A
L.M.-L.E.E.

DIST. 3 ZONA 6 MZA. 1 PARC. 50/51
PADRON INMOBILIARIO Nº 01-01-7841 (origen) DOMINIO Nº I.C.M. Exp. Nº ——

~~LEY 4.683~~
19063

Destino de la Obra : Local Comercial (2) y Departamentos (21)

POSEEDOR : **Los Gallegos Sociedad de Responsabilidad Limitada**
D.N.I. Nº CUIT Nº 30-71097323-3
Adquirido mediante boleto de Compraventa de fecha 21 de Diciembre del 2017 ante Escribano Titular Dr. Elio A. Curet Registro Notarial Nº 1 .-

UBICACION : Avenida Belgrano (N) Nº 1.006 ESQ.
Pasaje Reid s/Nº

BARRIO : CENTENARIO

CIUDAD : CAPITAL - SANTIAGO DEL ESTERO

ESCALA : 1:100 - 1:500.-

COLEGIO DE ARQUITECTOS LEY 5654/87 SANTIAGO DEL ESTERO
PROYECTO Y
DIRECCION DE OBRA
24 SET. 2019
Arq. Eva Luz Khairallah
SECRETARIA TECNICA
COLEGIO DE ARQUITECTOS S.D.E.

SUP. TERRENO 442,73 m2 s/p
SUP. CUBIERTA P/BAJA - de Losa 326,88 m2
SUP. CUBIERTA P/1º PISO - de Losa 333,96 m2
SUP. CUBIERTA P/2º PISO - de Losa 333,96 m2
SUP. CUBIERTA P/3º Piso - de Losa 333,96 m2
SUP. CUBIERTA P/Terraza - de Losa 28,22 m2
SUP. CUBIERTA TOTAL 1.356,98 m2

CROQUIS DE UBICACION

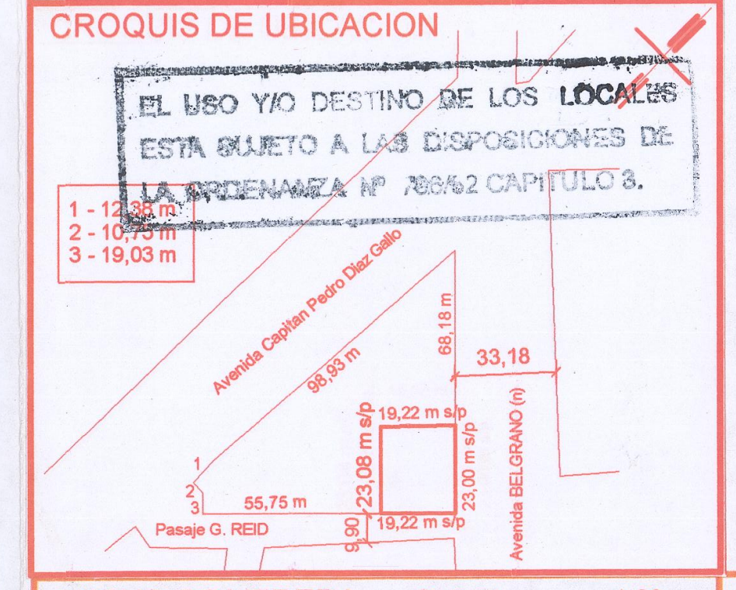
1 - 12,38 m
2 - 10,75 m
3 - 19,03 m
Avenida Capitan Pedro Diaz Gallo
98,93 m
68,18 m
33,18
19,22 m s/p
23,08 m s/p
23,00 m s/p
55,75 m
9,90
Pasaje G. REID
Avenida BELGRANO (n)
1
2
3

EL USO Y/O DESTINO DE LOS LOCALES
ESTA SUJETO A LAS DISPOSICIONES DE
LA ORDENANZA Nº 706/62 CAPITULO 8.

LOS GALLEGOS S.R.L.
... A. GONZALEZ
SOCIO GERENTE

POSEEDOR
Domicilio

PROYECTO
Domicilio
MIGUEL CARABAJAL
ARQUITECTO M.P. 0027

DIRECCION TECNICA
Domicilio
MIGUEL CARABAJAL
ARQUITECTO - M.P. 0027

INSTACION ELECTRICA
Domicilio
MIGUEL CARABAJAL
ARQUITECTO - M.P. 0027

CATEGORIA COLEGIO DE ARQUITECTOS

		Calle BELGRANO	Pasaje REID
ANCHO DE VEREDA		7,71 m	1,22 m
ANCHO DE CALZADA		6,31 m	6,66 m
ANCHO DE CALLE		33,18 m	9,90 m

PAVIMENTO SI
SERVICIOS CLOACALES SI

DESIGNACION : ①

Plano General .-
-Plantas,Cortes,Fachadas de Arquitectura y Planimetria-

OBSERVACIONES

07 ENE 2020
Las referencias al Título de Dominio son meramente indicativas, y la aprobación administrativa no valora los derechos que de ellos emergen

Ing. Agrim. MARIO J. LOPEZ
DIRECCION DE CATASTRO
MUNICIPALIDAD DE SGO. DEL ESTERO

PERMISO DE COMIENZO
DE OBRA Nº 4542
DIRECCION DE SUELO URBANO

Arq. ABRAHAM BERNARDO ROMINA
Dpto. OBRAS PRIVADAS
DIRECCION DE SUELO URBANO

MUNICIPALIDAD DE LA CIUDAD DE SANTIAGO DEL ESTERO
SECRETARIA DE PLANEAMIENTO Y OBRAS PUBLICAS
APROBADO
DIRECCIÓN DE SUELO URBANO
EXPEDIENTE 08_L_19
FECHA 26 AGO 2020

Arq. ESTER R. CHALOM
SUB-DIRECTORA
DIRECCION DE SUELO URBANO