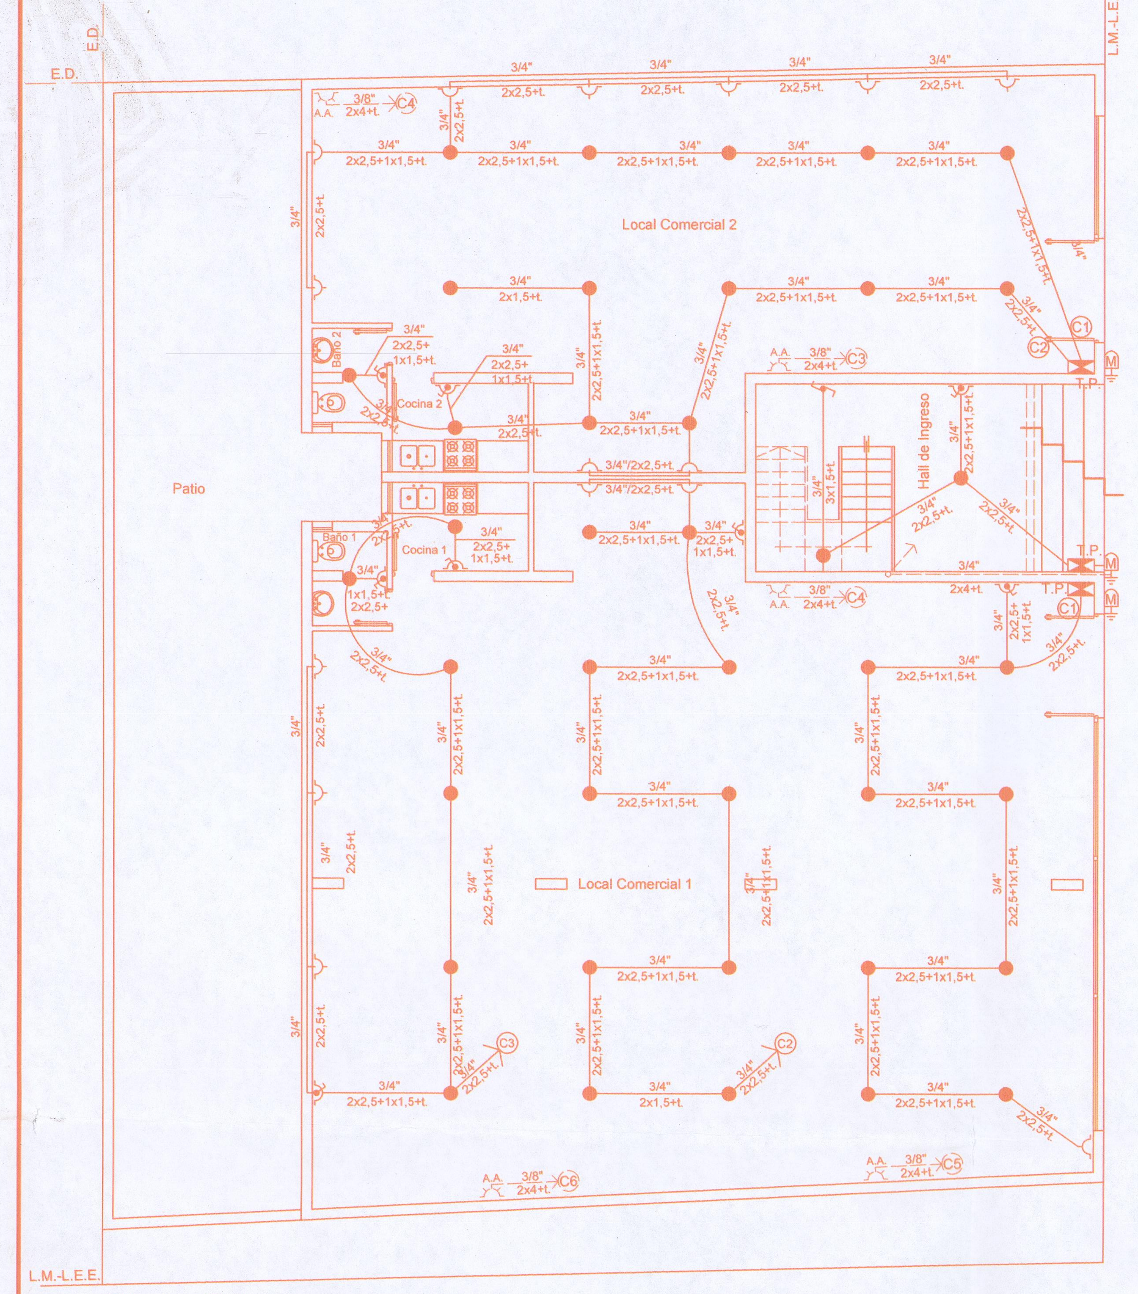

Planta Baja

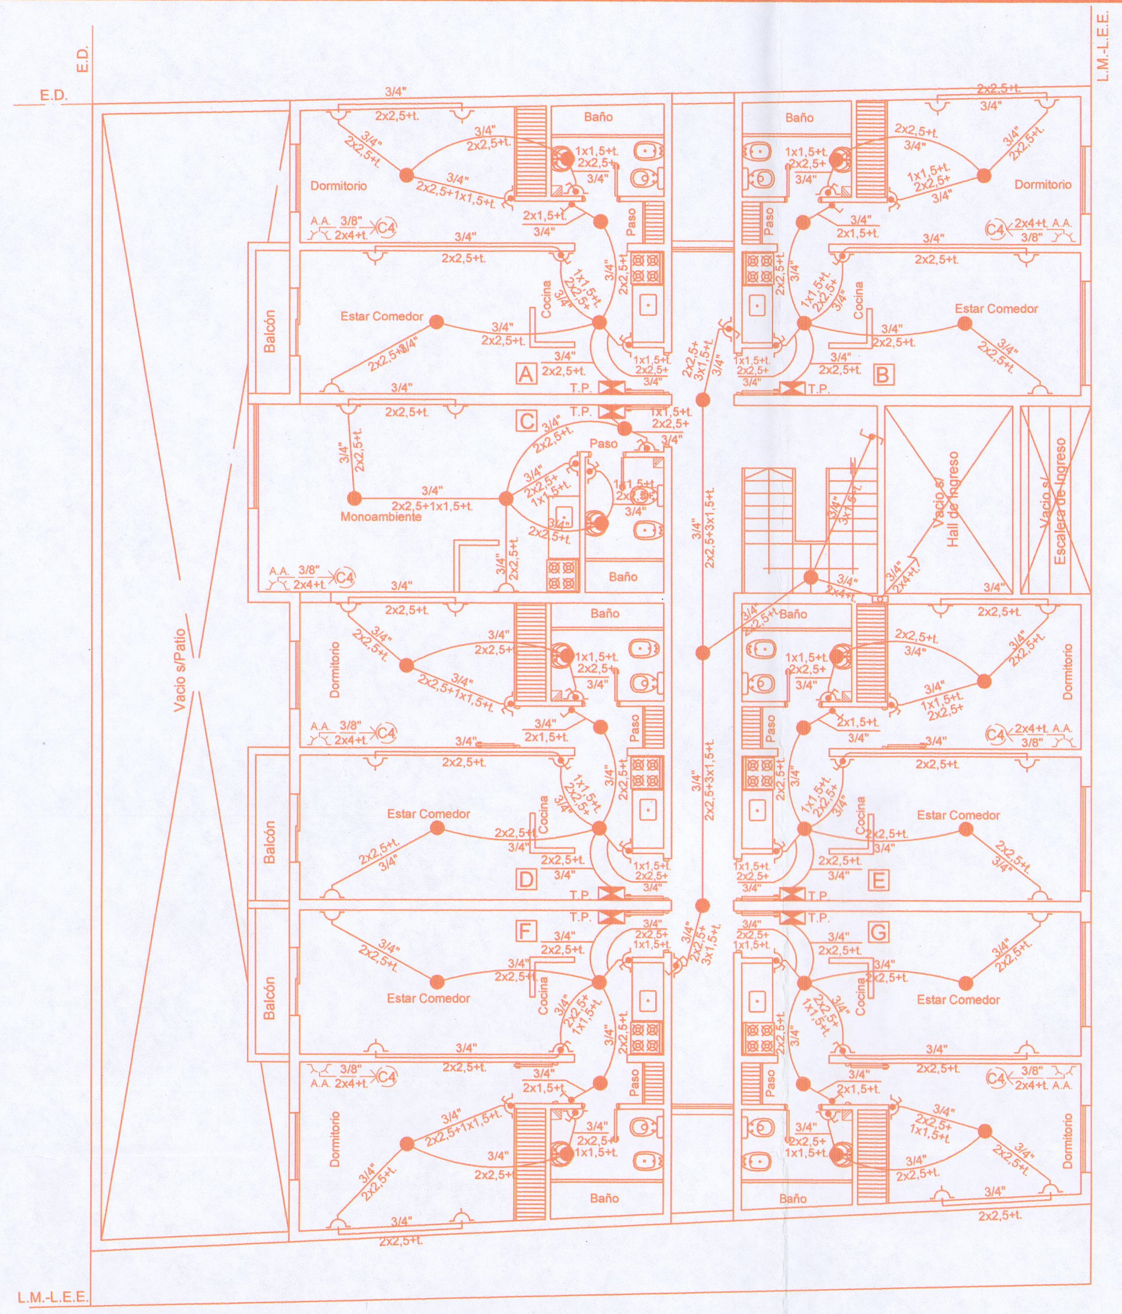

Planta 1° Piso

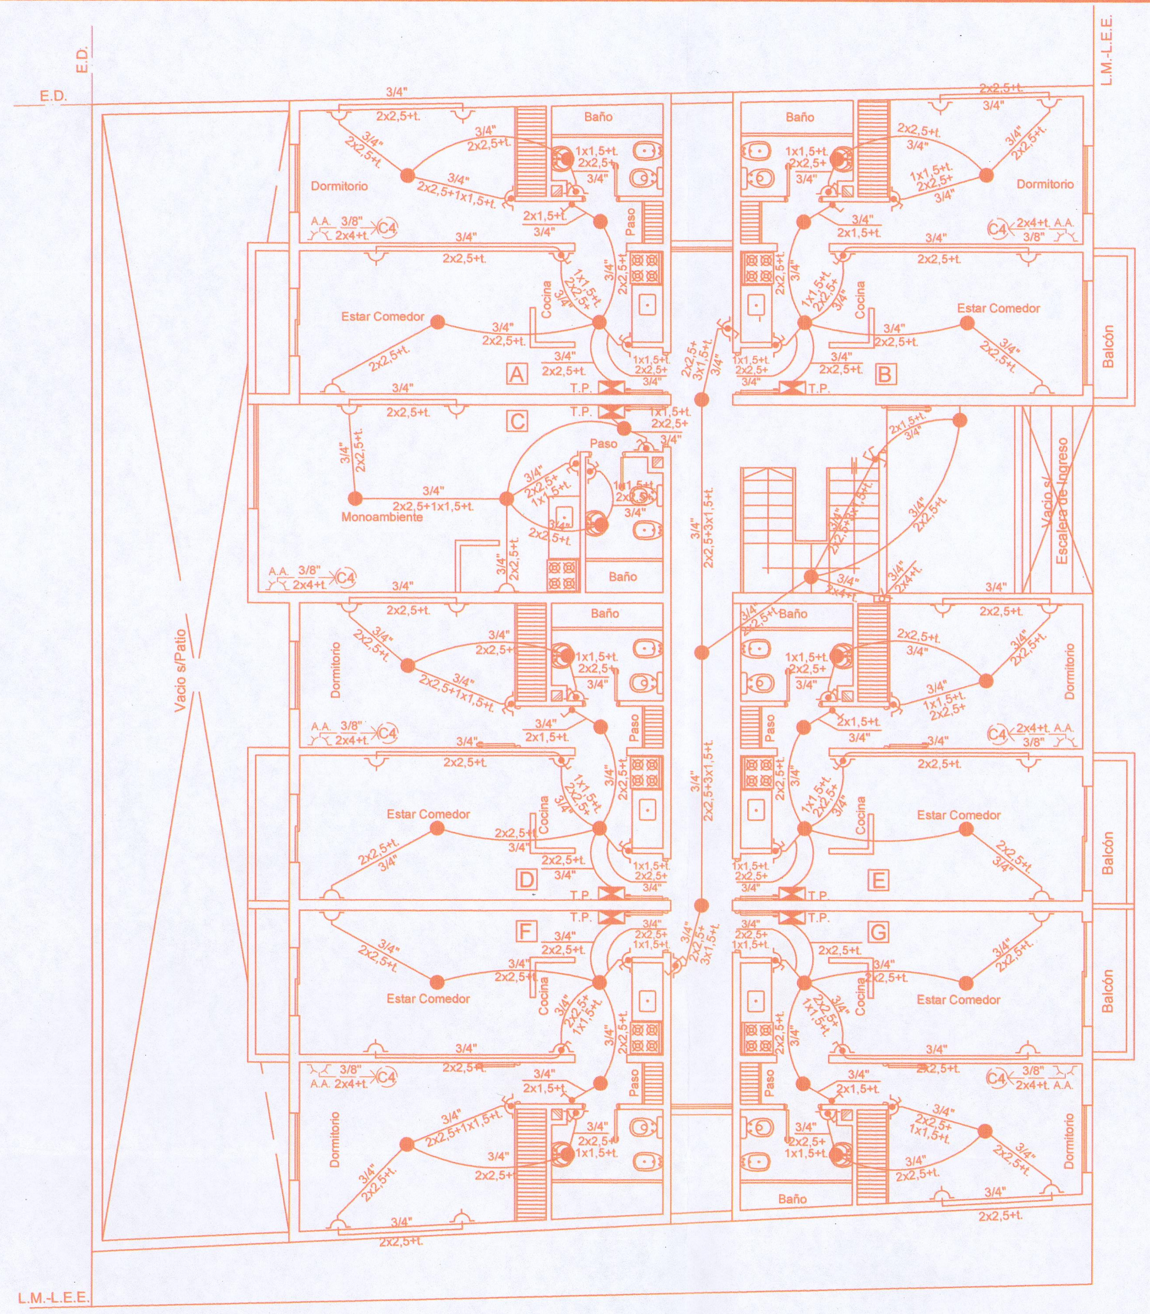

Planta 2° Piso

Planilla de Cargas

Tablero	Circuito	Bocas Luz 75 w	Bocas Tomas 200 w	Bocas Tomas 1000 w	Potencia Luz	Potencia Tomas	Potencia Total (W)	Corriente (A)	Portección Termomagnética	Disyuntor Diferencial
T.P. P/Baja Local Com. 1	1	8	2	—	600	400	1000	4,54	2x10 A	2x25 A
	2	10	1	—	750	200	950	4,31	2x10 A	
	3	6	6	—	450	1200	1650	7,50	2x10 A	
	4	—	—	1	—	1000	1000	4,54	2x10 A	
	5	—	—	1	—	1000	1000	4,54	2x10 A	
	6	—	—	1	—	1000	1000	4,54	2x10 A	
T.P. P/Baja Local Com. 2	1	5	7	—	375	1400	1775	8,06	2x10 A	2x25 A
	2	9	3	—	675	600	1275	5,79	2x10 A	
	3	—	—	1	—	1000	1000	4,54	2x10 A	
	4	—	—	1	—	1000	1000	4,54	2x10 A	
T.P. P/1°/P Dpto A	1	3	4	—	225	800	1025	4,65	2x10 A	2x25 A
	2	2	4	—	150	800	950	4,31	2x10 A	
	3	—	—	1	—	1000	1000	4,54	2x10 A	
T.P. P/1°/P Dpto B	1	3	4	—	225	800	1025	4,65	2x10 A	2x25 A
	2	2	4	—	150	800	950	4,31	2x10 A	
	3	—	—	1	—	1000	1000	4,54	2x10 A	
T.P. P/1°/P Dpto C	1	4	5	—	300	1000	1300	5,90	2x10 A	2x25 A
	3	—	—	1	—	1000	1000	4,54	2x10 A	
T.P. P/1°/P Dpto D	1	3	4	—	225	800	1025	4,65	2x10 A	2x25 A
	2	2	4	—	150	800	950	4,31	2x10 A	
	3	—	—	1	—	1000	1000	4,54	2x10 A	
T.P. P/1°/P Dpto E	1	3	4	—	225	800	1025	4,65	2x10 A	2x25 A
	2	2	4	—	150	800	950	4,31	2x10 A	
	3	—	—	1	—	1000	1000	4,54	2x10 A	
T.P. P/1°/P Dpto F	1	3	4	—	225	800	1025	4,65	2x10 A	2x25 A
	2	2	4	—	150	800	950	4,31	2x10 A	
	3	—	—	1	—	1000	1000	4,54	2x10 A	
T.P. P/1°/P Dpto G	1	3	4	—	225	800	1025	4,65	2x10 A	2x25 A
	2	2	4	—	150	800	950	4,31	2x10 A	
	3	—	—	1	—	1000	1000	4,54	2x10 A	
T.P. P/2°/P Dpto A	1	3	4	—	225	800	1025	4,65	2x10 A	2x25 A
	2	2	4	—	150	800	950	4,31	2x10 A	
	3	—	—	1	—	1000	1000	4,54	2x10 A	
T.P. P/2°/P Dpto B	1	3	4	—	225	800	1025	4,65	2x10 A	2x25 A
	2	2	4	—	150	800	950	4,31	2x10 A	
	3	—	—	1	—	1000	1000	4,54	2x10 A	
T.P. P/2°/P Dpto C	1	4	5	—	300	1000	1300	5,90	2x10 A	2x25 A
	3	—	—	1	—	1000	1000	4,54	2x10 A	
T.P. P/2°/P Dpto D	1	3	4	—	225	800	1025	4,65	2x10 A	2x25 A
	2	2	4	—	150	800	950	4,31	2x10 A	
	3	—	—	1	—	1000	1000	4,54	2x10 A	
T.P. P/2°/P Dpto E	1	3	4	—	225	800	1025	4,65	2x10 A	2x25 A
	2	2	4	—	150	800	950	4,31	2x10 A	
	3	—	—	1	—	1000	1000	4,54	2x10 A	
T.P. P/2°/P Dpto F	1	3	4	—	225	800	1025	4,65	2x10 A	2x25 A
	2	2	4	—	150	800	950	4,31	2x10 A	
	3	—	—	1	—	1000	1000	4,54	2x10 A	
T.P. P/2°/P Dpto G	1	3	4	—	225	800	1025	4,65	2x10 A	2x25 A
	2	2	4	—	150	800	950	4,31	2x10 A	
	3	—	—	1	—	1000	1000	4,54	2x10 A	
T.P. P/B/, 1° y 2° Piso	1	10	5	—	750	1000	1750	7,95	2x10 A	
T.S. P/3° y P/Terraza	1	3	2	—	225	400	625	2,84	2x10 A	

Potencia Total 55.475
Fac. de Simultaneidad 60% 33.285

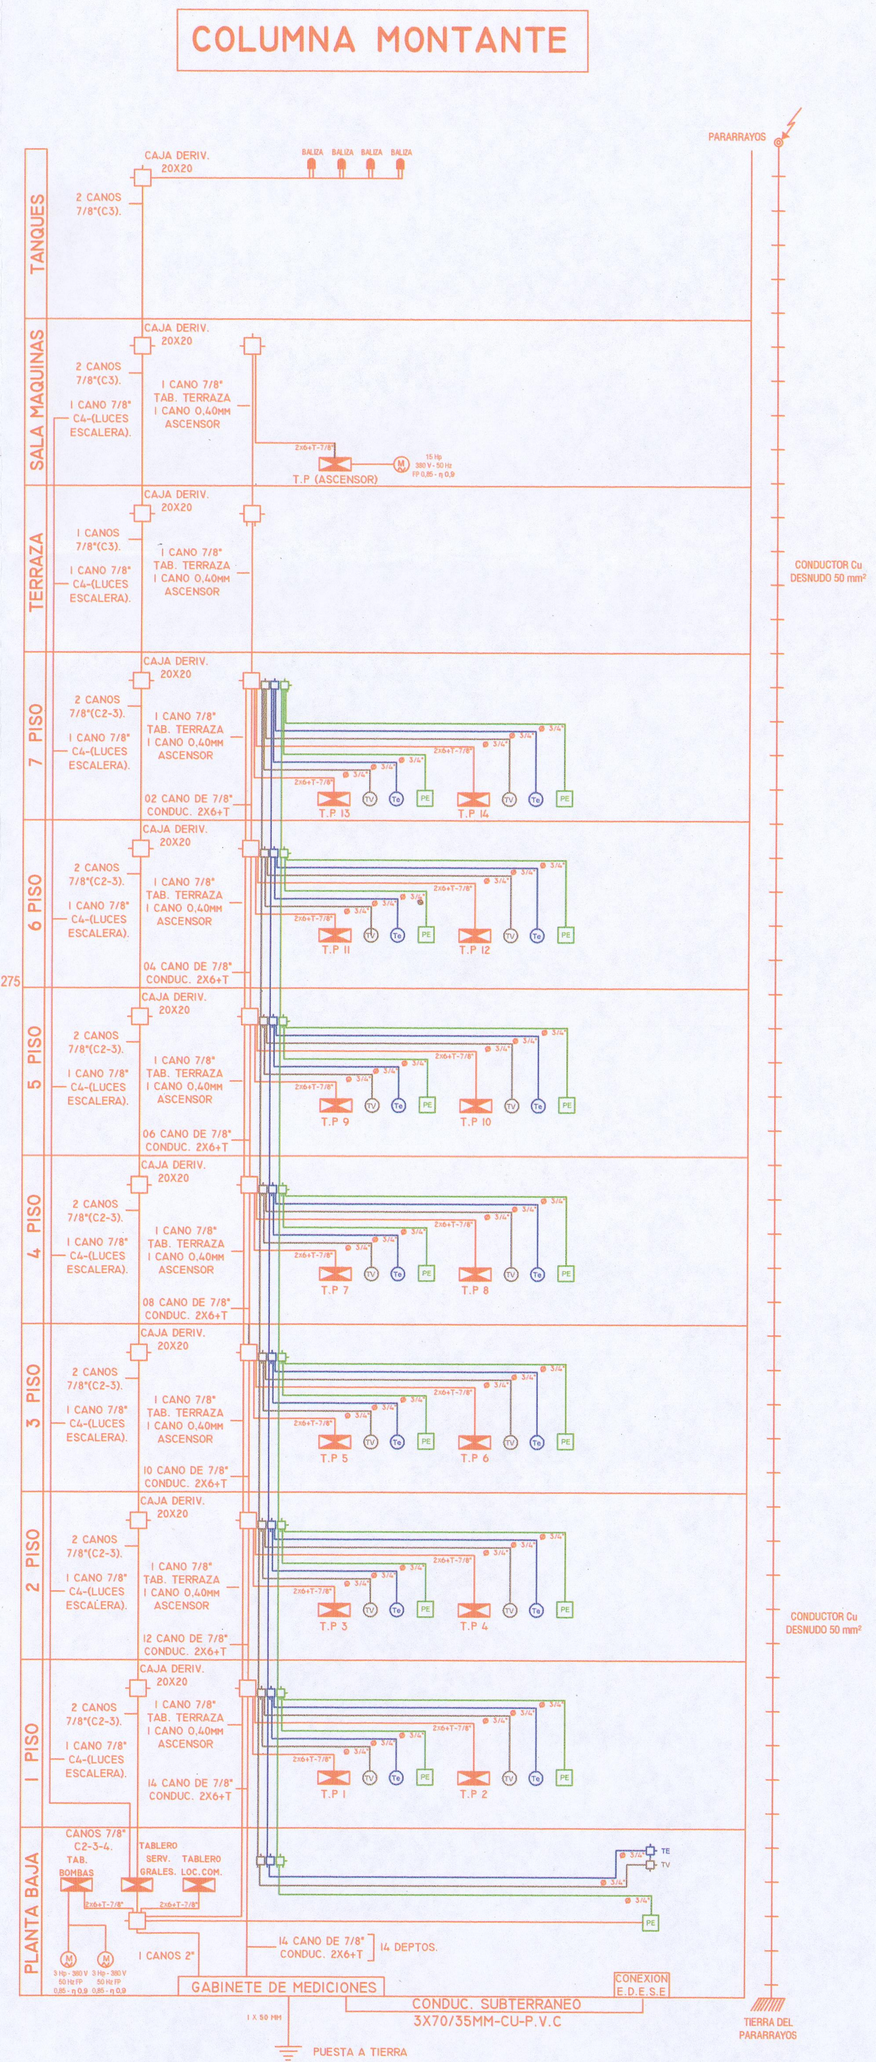

COLUMNA MONTANTE

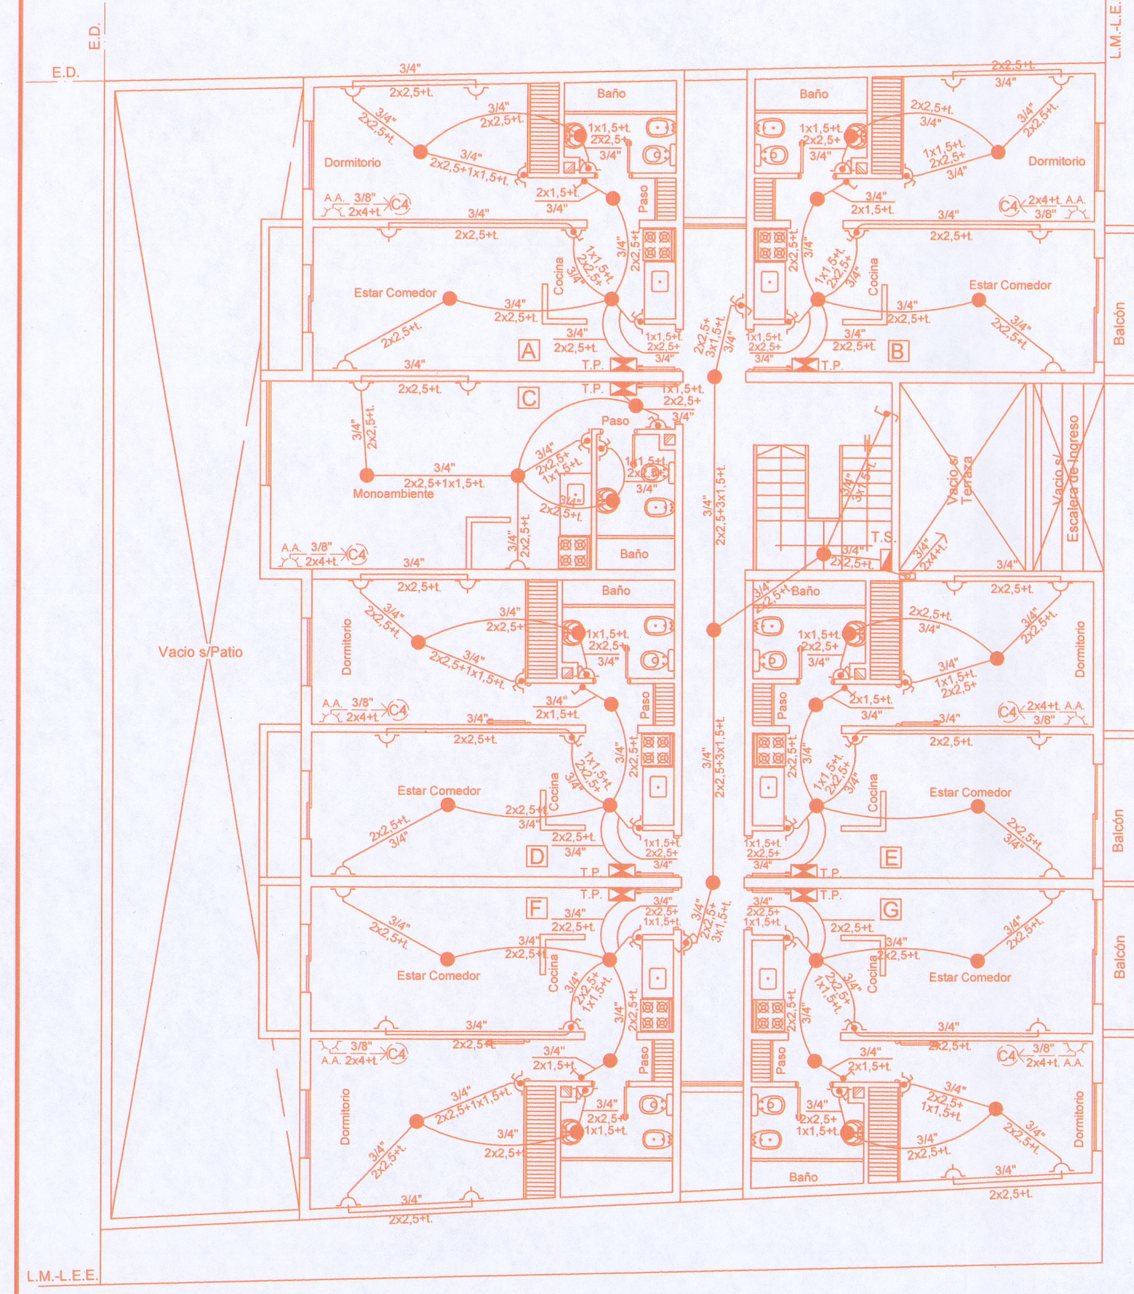

Planta 3° Piso

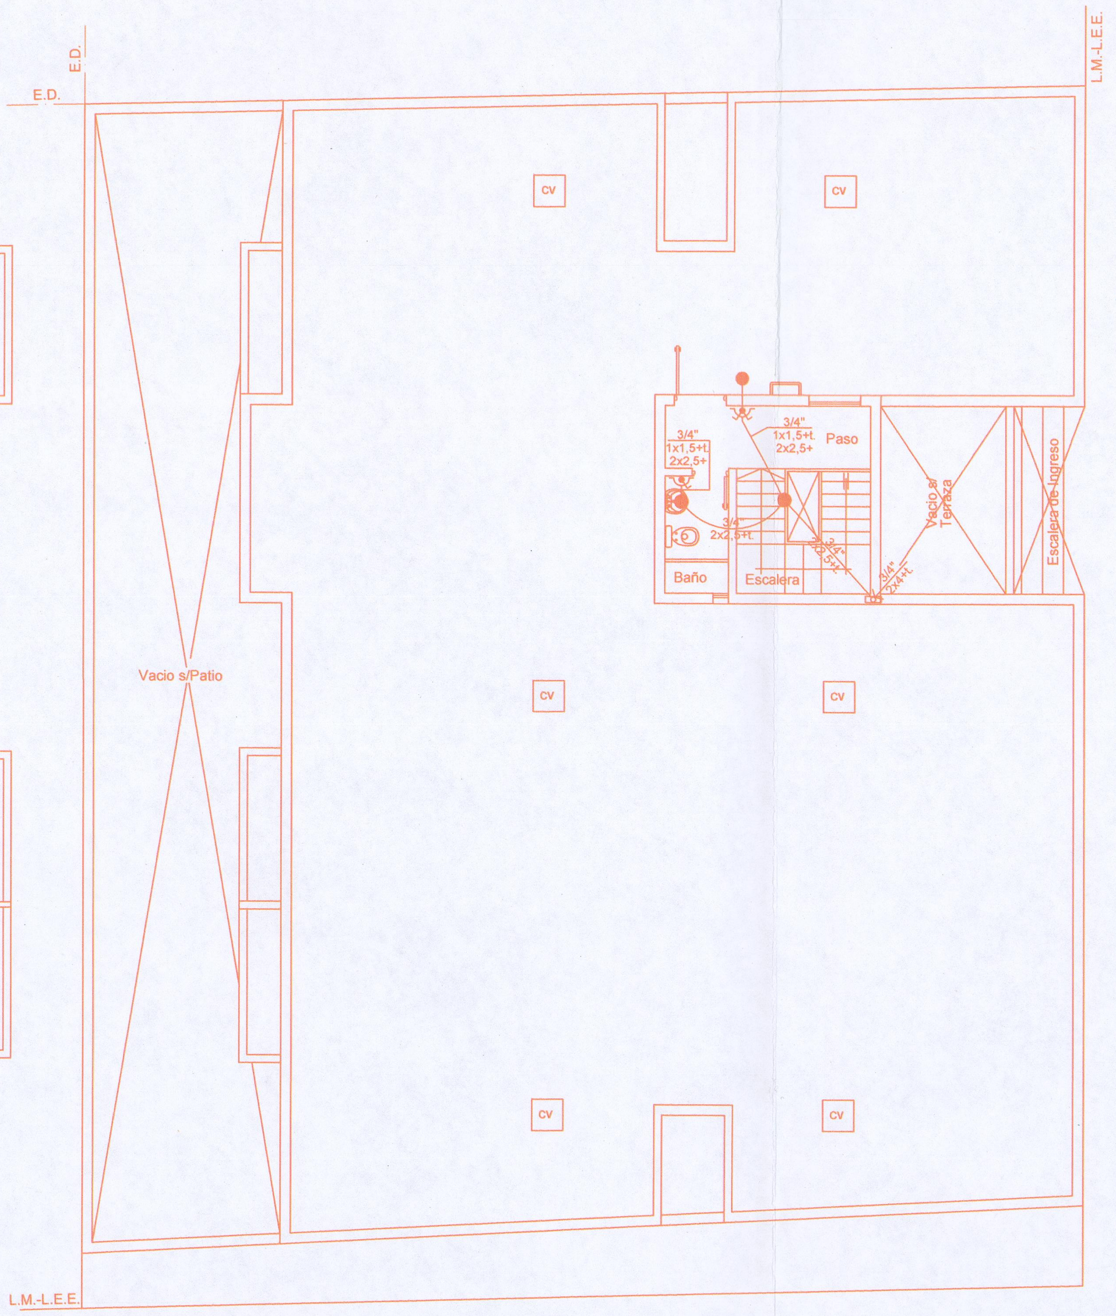

Planta de Terraza

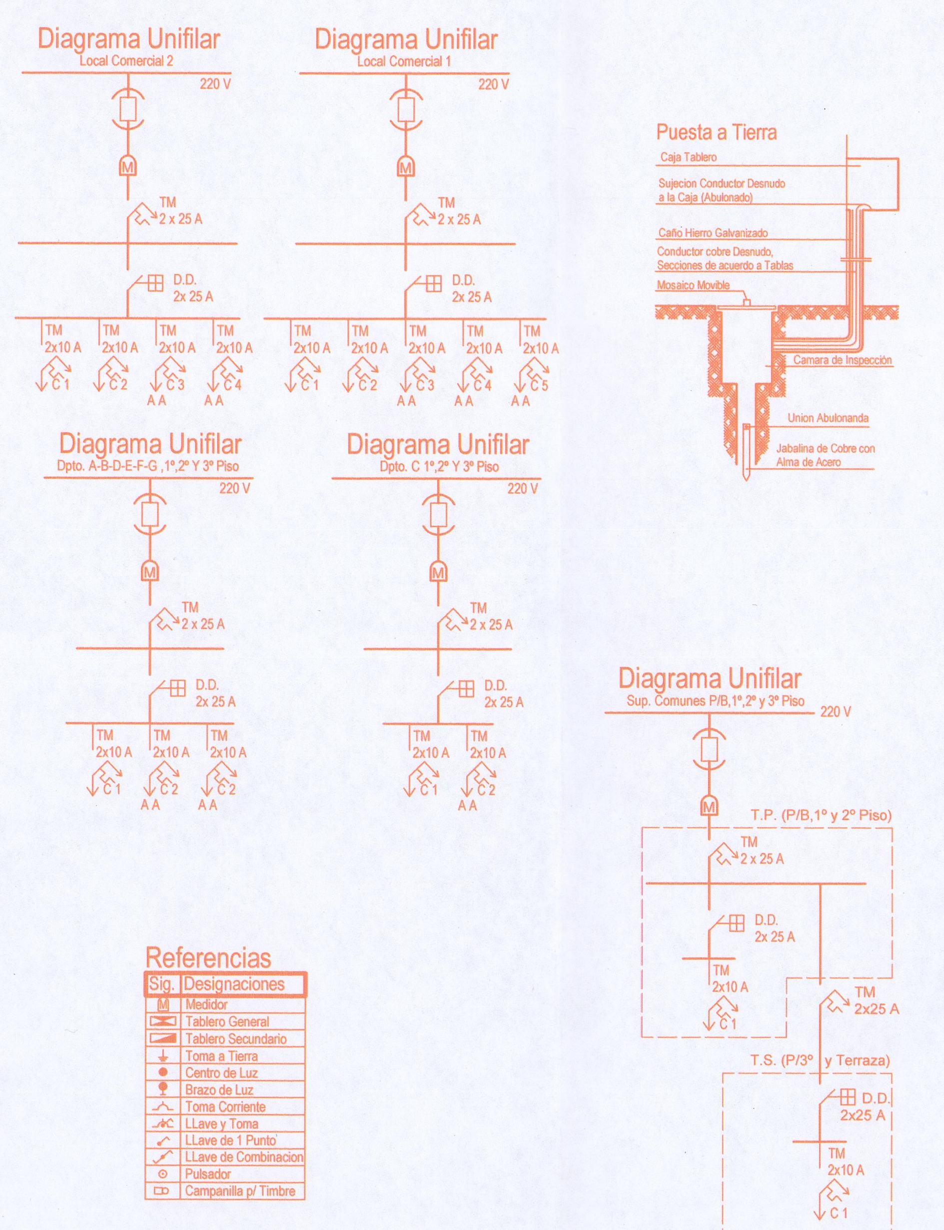

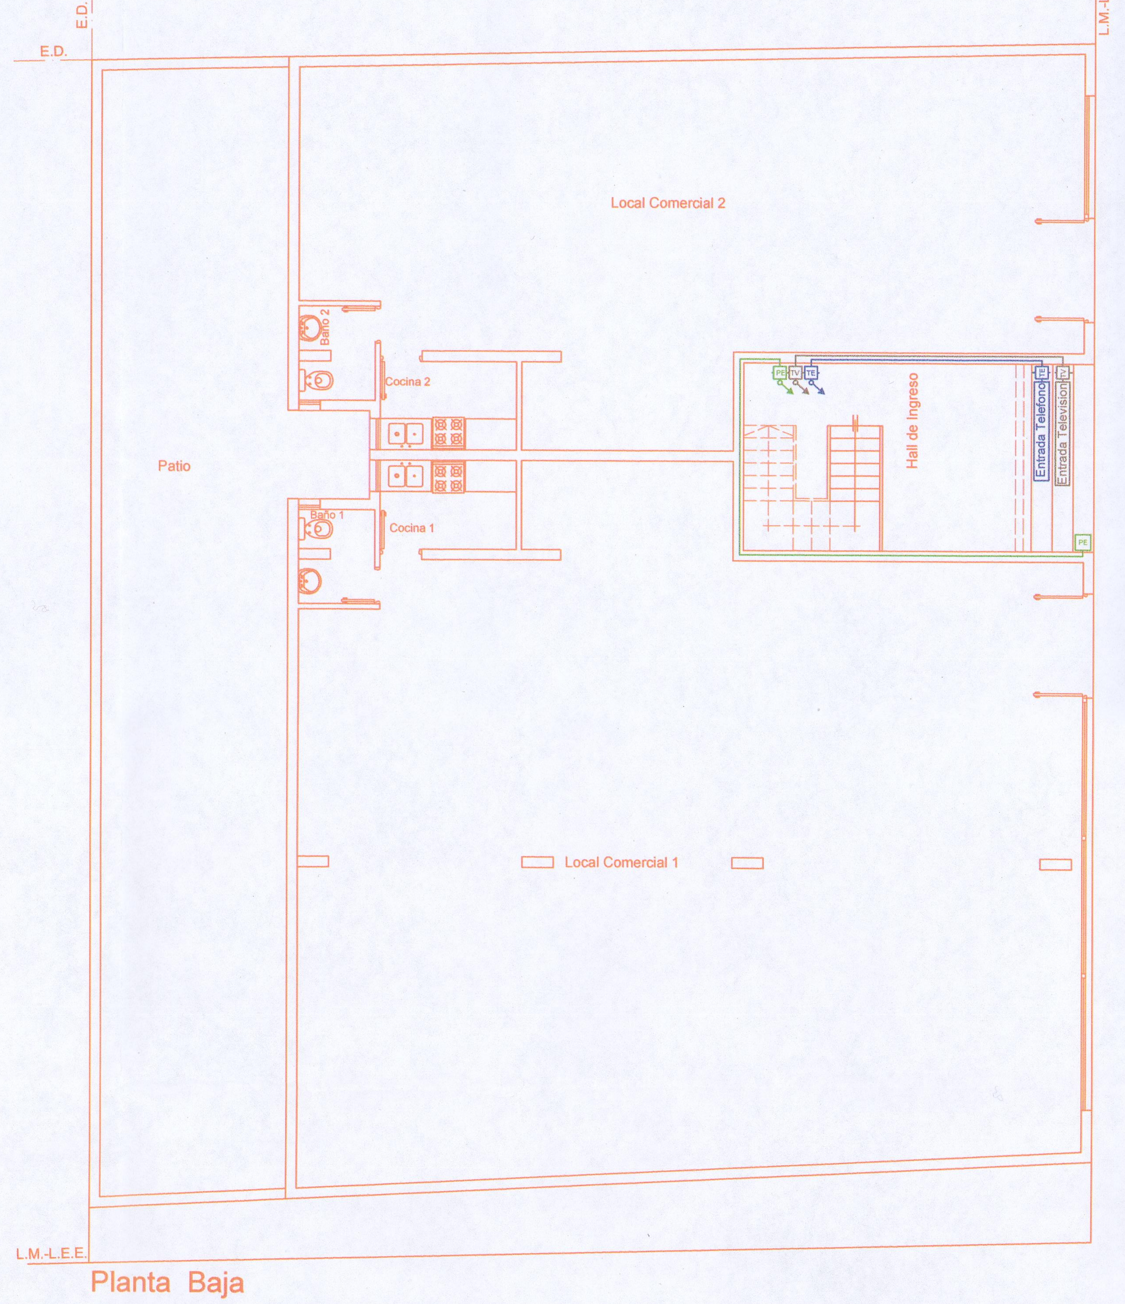

Planta Baja

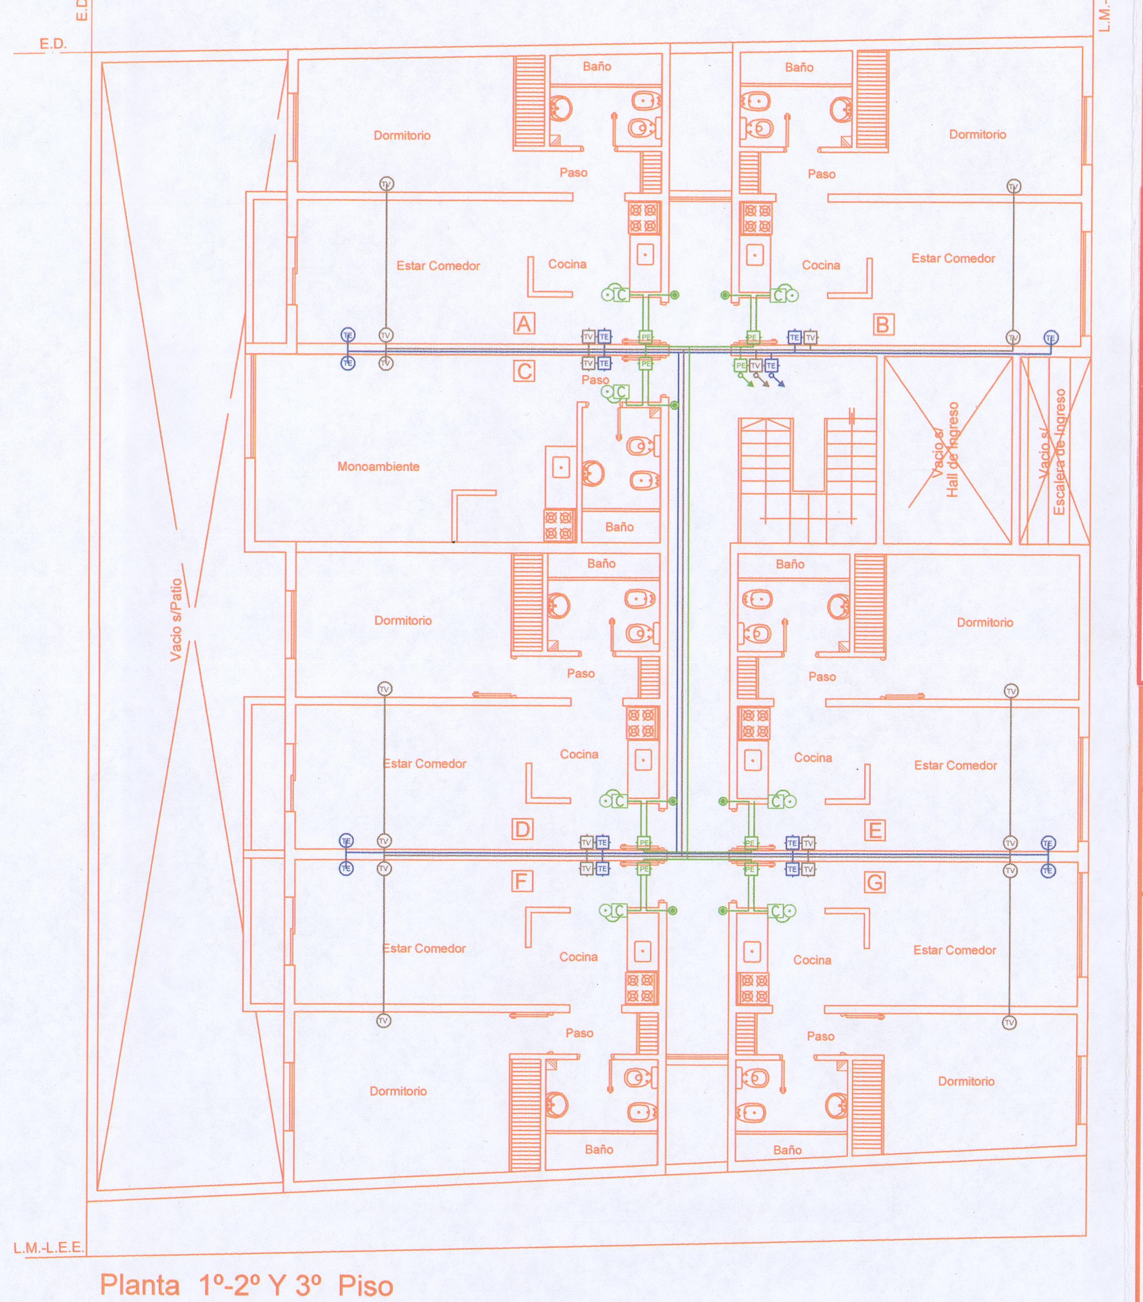

Planta 1°-2° Y 3° Piso

DIST. 3	ZONA 6	MZA. 1	PARC. 50/51	LEY 4.683
PADRON INMOBILIARIO Nº 01-01-7841 (origen)	DOMINIO Nº		I.C.M. Exp. Nº ——	19063

Destino de la Obra : Local Comercial (2) y Departamentos (21)

POSEEDOR : Los Gallegos Sociedad de Responsabilidad Limitada
D.N.I. Nº CUIT Nº 30-71097323-3
Adquirido mediante boleto de Compraventa de fecha 21 de Di... ante Escribano Titular Dr. Elio A. Curet Registro Notarial Nº ...

UBICACION : Avenida Belgrano (N) Nº 1.006 ESQ. Pasaje Reid s/Nº

BARRIO : CENTENARIO

CIUDAD : CAPITAL - SANTIAGO DEL ESTERO

ESCALA : 1:100 - 1:500.-

SUP. TERRENO 442,73 m2 s/p	
SUP. CUBIERTA P/BAJA - de Losa	326,88 m2
SUP. CUBIERTA P/1° PISO - de Losa	333,96 m2
SUP. CUBIERTA P/2° PISO - de Losa	333,96 m2
SUP. CUBIERTA P/3° Piso - de Losa	333,96 m2
SUP. CUBIERTA P/Terraza - de Losa	28,22 m2
SUP. CUBIERTA TOTAL	1.356,98 m2

CROQUIS DE UBICACION

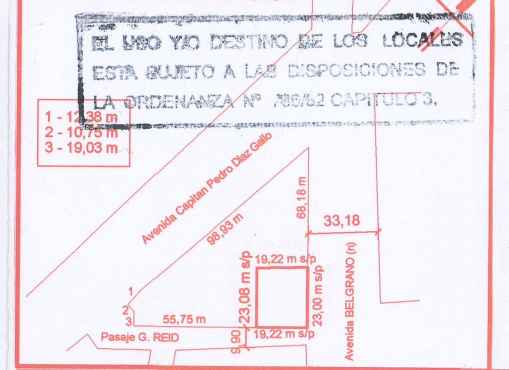

POSEEDOR Domicilio — LOS GALLEGOS S.R.L. GUILLERMO A. GONZALEZ SOCIO GERENTE

PROYECTO Domicilio — MIGUEL CARABAJAL ARQUITECTO - M.P 0027

DIRECCION TECNICA Domicilio — MIGUEL CARABAJAL ARQUITECTO - M.P 0027

INSTACION ELECTRICA Domicilio — MIGUEL CARABAJAL ARQUITECTO - M.P 0027

CATEGORIA COLEGIO DE ARQUITECTOS

	Calle BELGRANO	Pasaje REID
ANCHO DE VEREDA	7,71 m	1,22 m
ANCHO DE CALZADA	6,31 m	6,66 m
ANCHO DE CALLE	33,18 m	9,90 m

PAVIMENTO

SERVICIOS CLOACALES

DESIGNACION :

Plano General .-

-Plantas de Electricidad,Diagramas,Detalle y Planilla de Cargas-

OBSERVACIONES

Las referencias al Título de Dominio son meramente indicativas, y la aprobación administrativa no valora los derechos que de ellos emergen

COLEGIO DE ARQUITECTOS LEY 5654/87 SANTIAGO DEL ESTERO
PROYECTO Y DIRECCION DE OBRA
24 SET. 2019
Arq. Eva Luz Khairallah SECRETARIA TECNICA COLEGIO DE ARQUITECTOS S.D.E.
SECRETARIA DE PLANEAMIENTO Y OBRAS PUBLICAS Municipalidad de la Capital SGO. DEL ESTERO DIRECCION DE SUELO URBANO
07 ENE 2020
PERMISO DE OBRA Nº 45412 DIRECCION DE SUELO URBANO
MUNICIPALIDAD DE LA CIUDAD DE SANTIAGO DEL ESTERO SECRETARIA DE PLANEAMIENTO Y OBRAS PUBLICAS
APROBADO
DIRECCION DE SUELO URBANO
EXPEDIENTE 08-L-19
26 AGO 2020
Arq. ESTER R. CHALOM SUB-DIRECTORA DIRECCION DE SUELO URBANO
Arq. ABRAHAM BERNARDO GOMONA Dpto. OBRAS PRIVADAS DIRECCION DE SUELO URBANO