

IP TERRENO 442,73 m² s/p
IP CUBIERTA PBAVA - de Losa 326,88 m²
IP CUBIERTA P1/P1 PSO - de Losa 333,96 m²
IP CUBIERTA P1/P2 PSO - de Losa 333,96 m²
IP CUBIERTA P1/P3 PSO - de Losa 333,96 m²
IP CUBIERTA P1/P4 PSO - de Losa 333,96 m²
IP CUBIERTA TOTAL * 355,00 m²

1000000112

PROQUIS DE UBICACION

~~EL USO Y/O DESTINO DE LOS LOCALS~~

POSEEDOR
Domicilio

LA ORDENANZA Nº 739/02 CAPITULO 3.

PROYECTO - MDP-0027

MIGUEL CARABAJAL

ARQUITECTO

PROYECTO

Domicilio

12.38 m

10.75 m

0 - 19.03 m

56.18 m

Capitán Pedro Díaz Cevallos

DIRECCION TECNICA

Domicilio

MIGUEL CARABALLAN

INSTACION ELECTRICA

Domicilio

89' 13" 00
Avenida

08 m s/d
19.22 m s/d
33.16 m s/d

GRANO (m)

ARQUITECTO - M.P. 19927

Avenida BE
 23.00
 23.00
 55.75 m
 18.22 m ap
 Pasaje C. REID
 8
 5
 MIGUEL CARABALLA
 ARQUITECTO
 1512 M.P. 0027
 CATEGORIA COLEGIO DE ARQUITECTOS

	PAVIMENTO	SERVICIOS CLOACALES
NCHO DE VEREDA	1,22 m	9,90 m
NCHO DE CALZADA	6,66 m	9,90 m
NCHO DE CALLE	9,90 m	9,90 m

DESIGNACION : **Plano General -**

OBSERVACIONES

-Plantas de Estructuras-

MUNICIPALIDAD DE LA CIUDAD DE SANTIAGO DEL ESTERO
CORREO ELECTRÓNICO: municipio@ciudaddeesteros.com.ar
TELÉFONO: 0343-4422100 FAX: 0343-4422101

07/ENE/2011

Las referencias al Título de Dominio son meramente indicativas, y la

SECRETARIA DE PLANEAMIENTO Y OBRAS PUBLICAS

APROBADO

DIRECCION DE SUELO URBANO

URBANO

MIEN 0542

aprobación administrativa no valora
los derechos que de ellos emergen


RMISO
OBRA N
ECCION D

1977 MARIO J. LOPEZ
COMISION DE CATASTRO
Dpto. NEGOS

Art. ABRAHAM BERNARDO ROMINA
Dpto. NEGOS

Atq. ESTER R. CHALOM
SUB-DIRECTORA
DIRECCION DE SUELO URBANO

REPUBLICA DE SULO DEL ESTERO
DIRECCION DE SUELO URBANO.

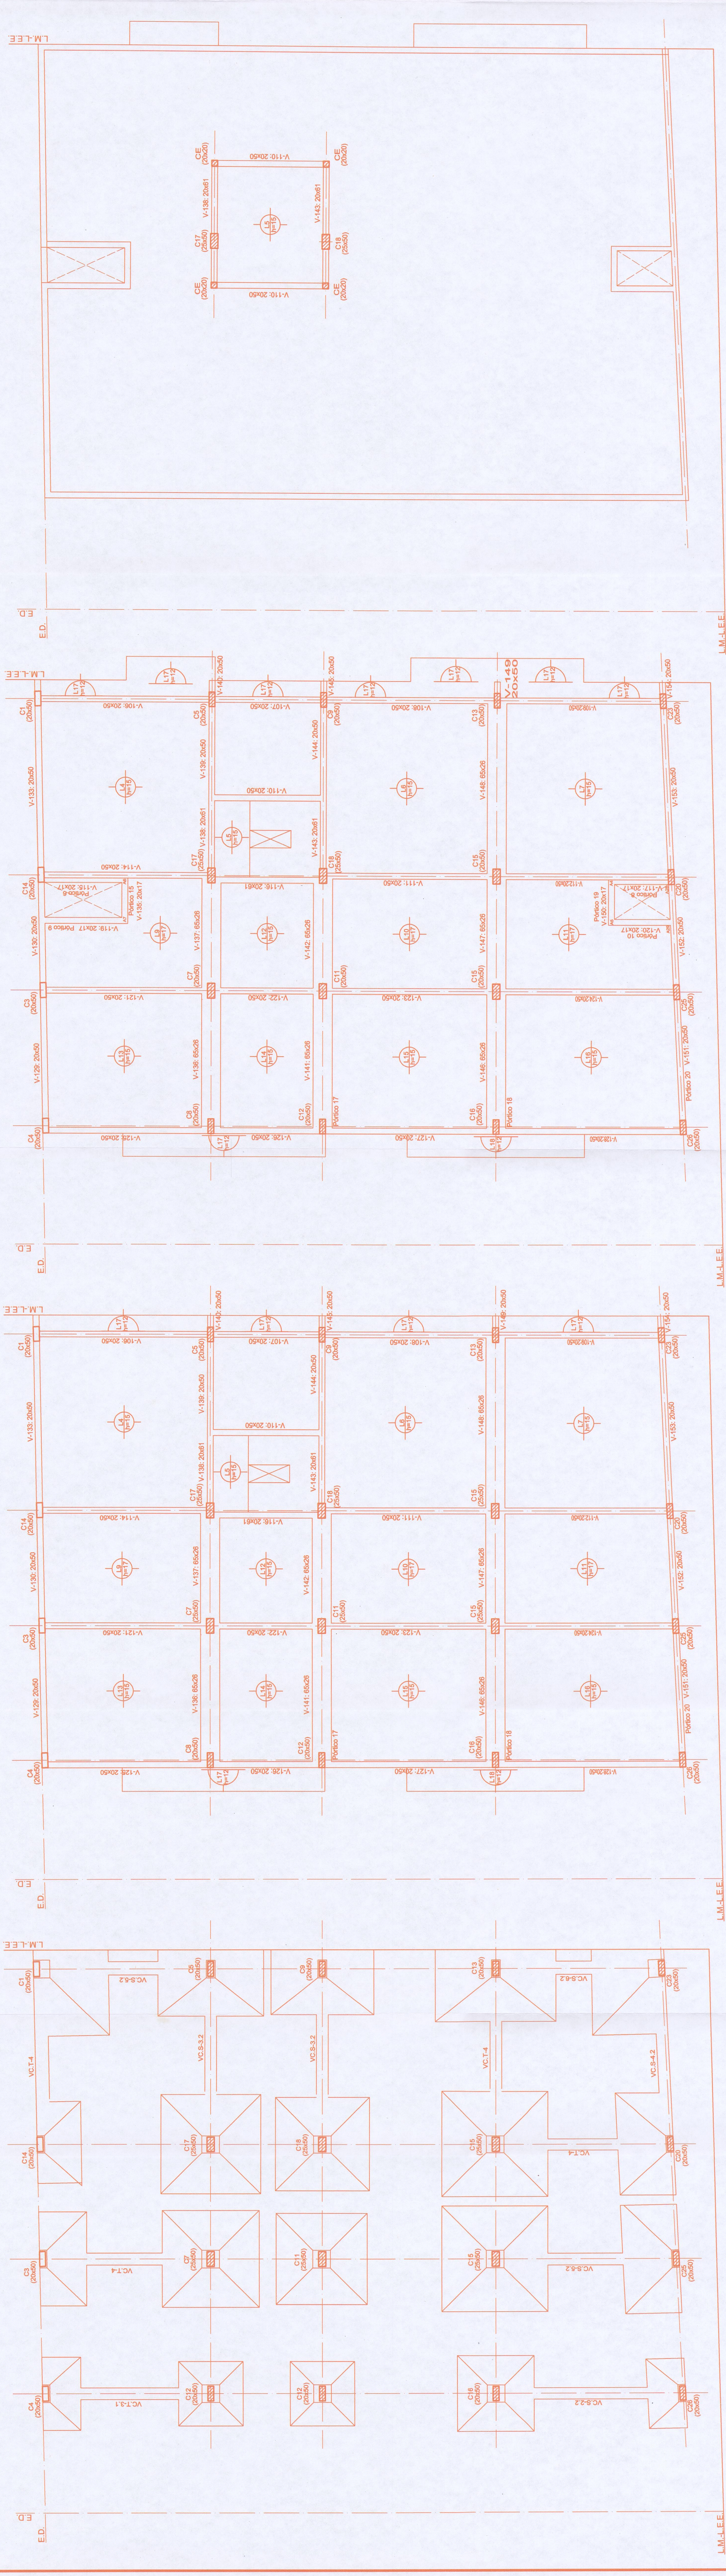

Planta de Fundación

Planta de Estructuras Nivel 1

Planta de Estructuras Nivel 5