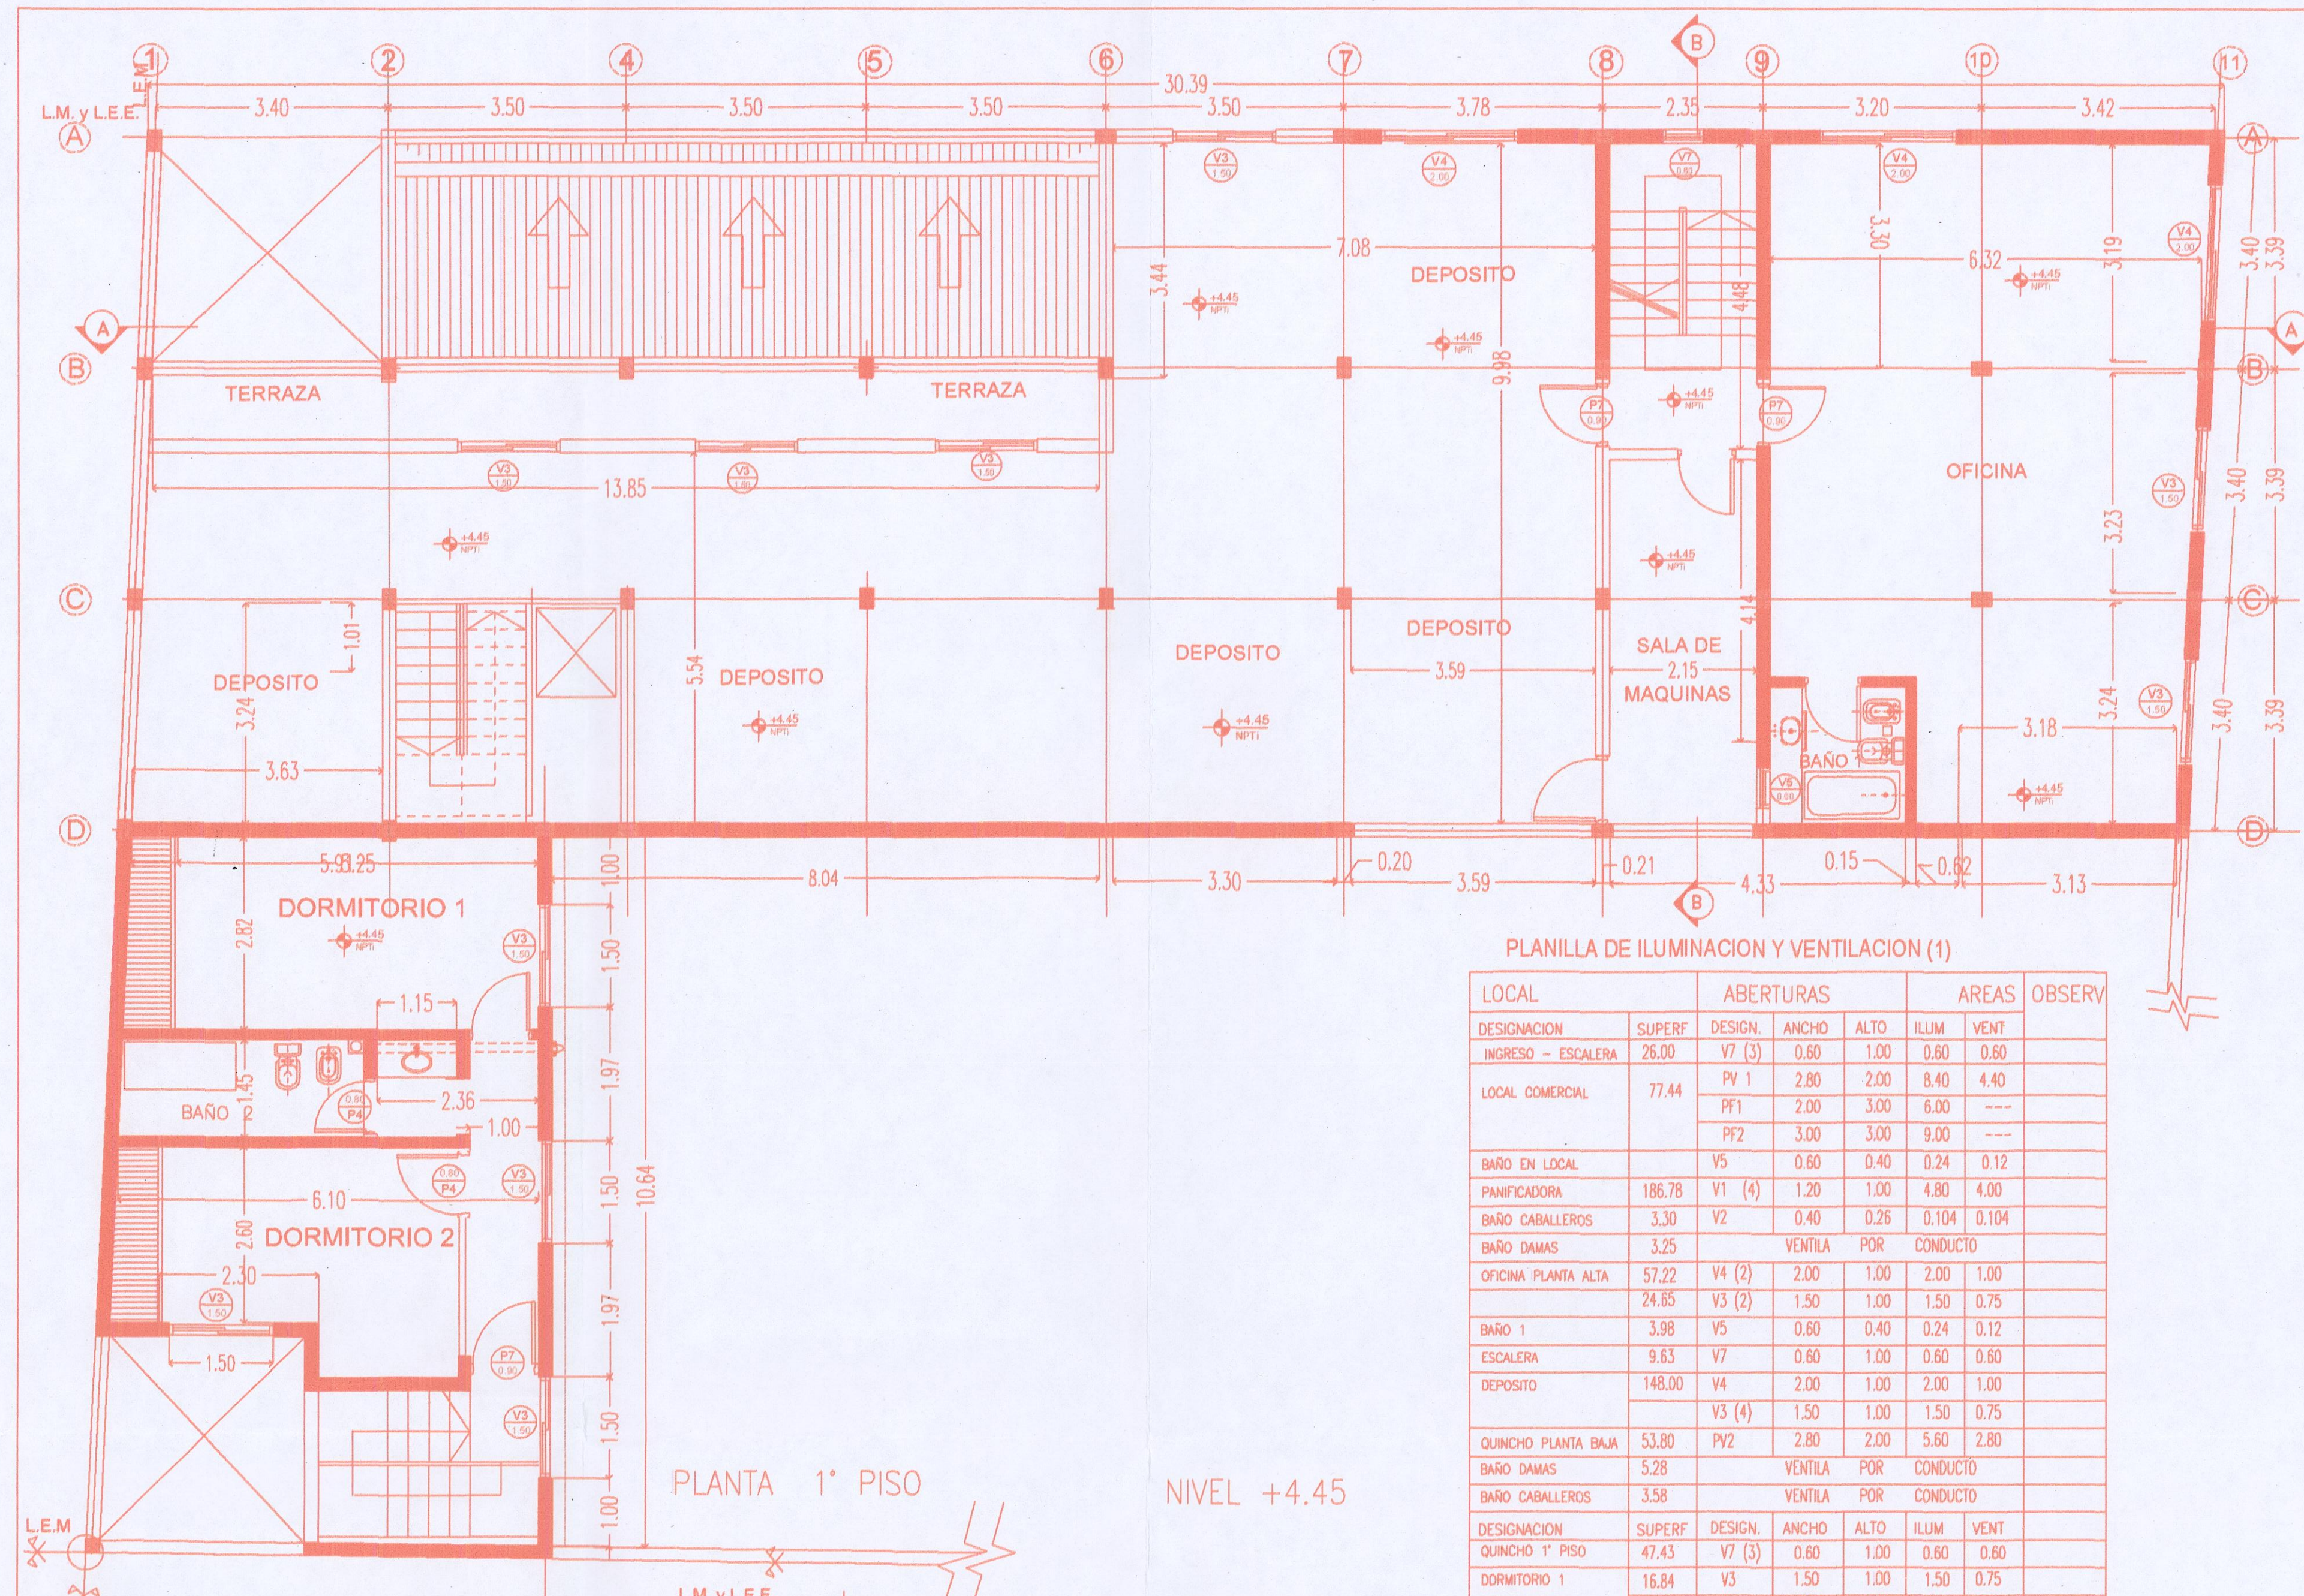
PLANTA 1° PISO

NIVEL +4.45

PLANILLA DE ILUMINACION Y VENTILACION (1)

LOCAL		ABERTURAS			AREAS		OBSERV
DESIGNACION	SUPERF	DESIGN.	ANCHO	ALTO	ILUM	VENT	
INGRESO - ESCALERA	26.00	V7 (3)	0.60	1.00	0.60	0.60	
LOCAL COMERCIAL	77.44	PV 1	2.80	2.00	8.40	4.40	
		PF1	2.00	3.00	6.00	---	
		PF2	3.00	3.00	9.00	---	
BAÑO EN LOCAL		V5	0.60	0.40	0.24	0.12	
PANIFICADORA	186.78	V1 (4)	1.20	1.00	4.80	4.00	
BAÑO CABALLEROS	3.30	V2	0.40	0.26	0.104	0.104	
BAÑO DAMAS	3.25		VENTILA	POR	CONDUCTO		
OFICINA PLANTA ALTA	57.22	V4 (2)	2.00	1.00	2.00	1.00	
	24.65	V3 (2)	1.50	1.00	1.50	0.75	
BAÑO 1	3.98	V5	0.60	0.40	0.24	0.12	
ESCALERA	9.63	V7	0.60	1.00	0.60	0.60	
DEPOSITO	148.00	V4	2.00	1.00	2.00	1.00	
		V3 (4)	1.50	1.00	1.50	0.75	
QUINCHO PLANTA BAJA	53.80	PV2	2.80	2.00	5.60	2.80	
BAÑO DAMAS	5.28		VENTILA	POR	CONDUCTO		
BAÑO CABALLEROS	3.58		VENTILA	POR	CONDUCTO		
DESIGNACION	SUPERF	DESIGN.	ANCHO	ALTO	ILUM	VENT	
QUINCHO 1° PISO	47.43	V7 (3)	0.60	1.00	0.60	0.60	
DORMITORIO 1	16.84	V3	1.50	1.00	1.50	0.75	
DORMITORIO 2	14.50	V3	1.50	1.00	1.50	0.75	
BAÑO QUINCHO 1°PISO	6.96		VENTILA	POR	CONDUCTO		

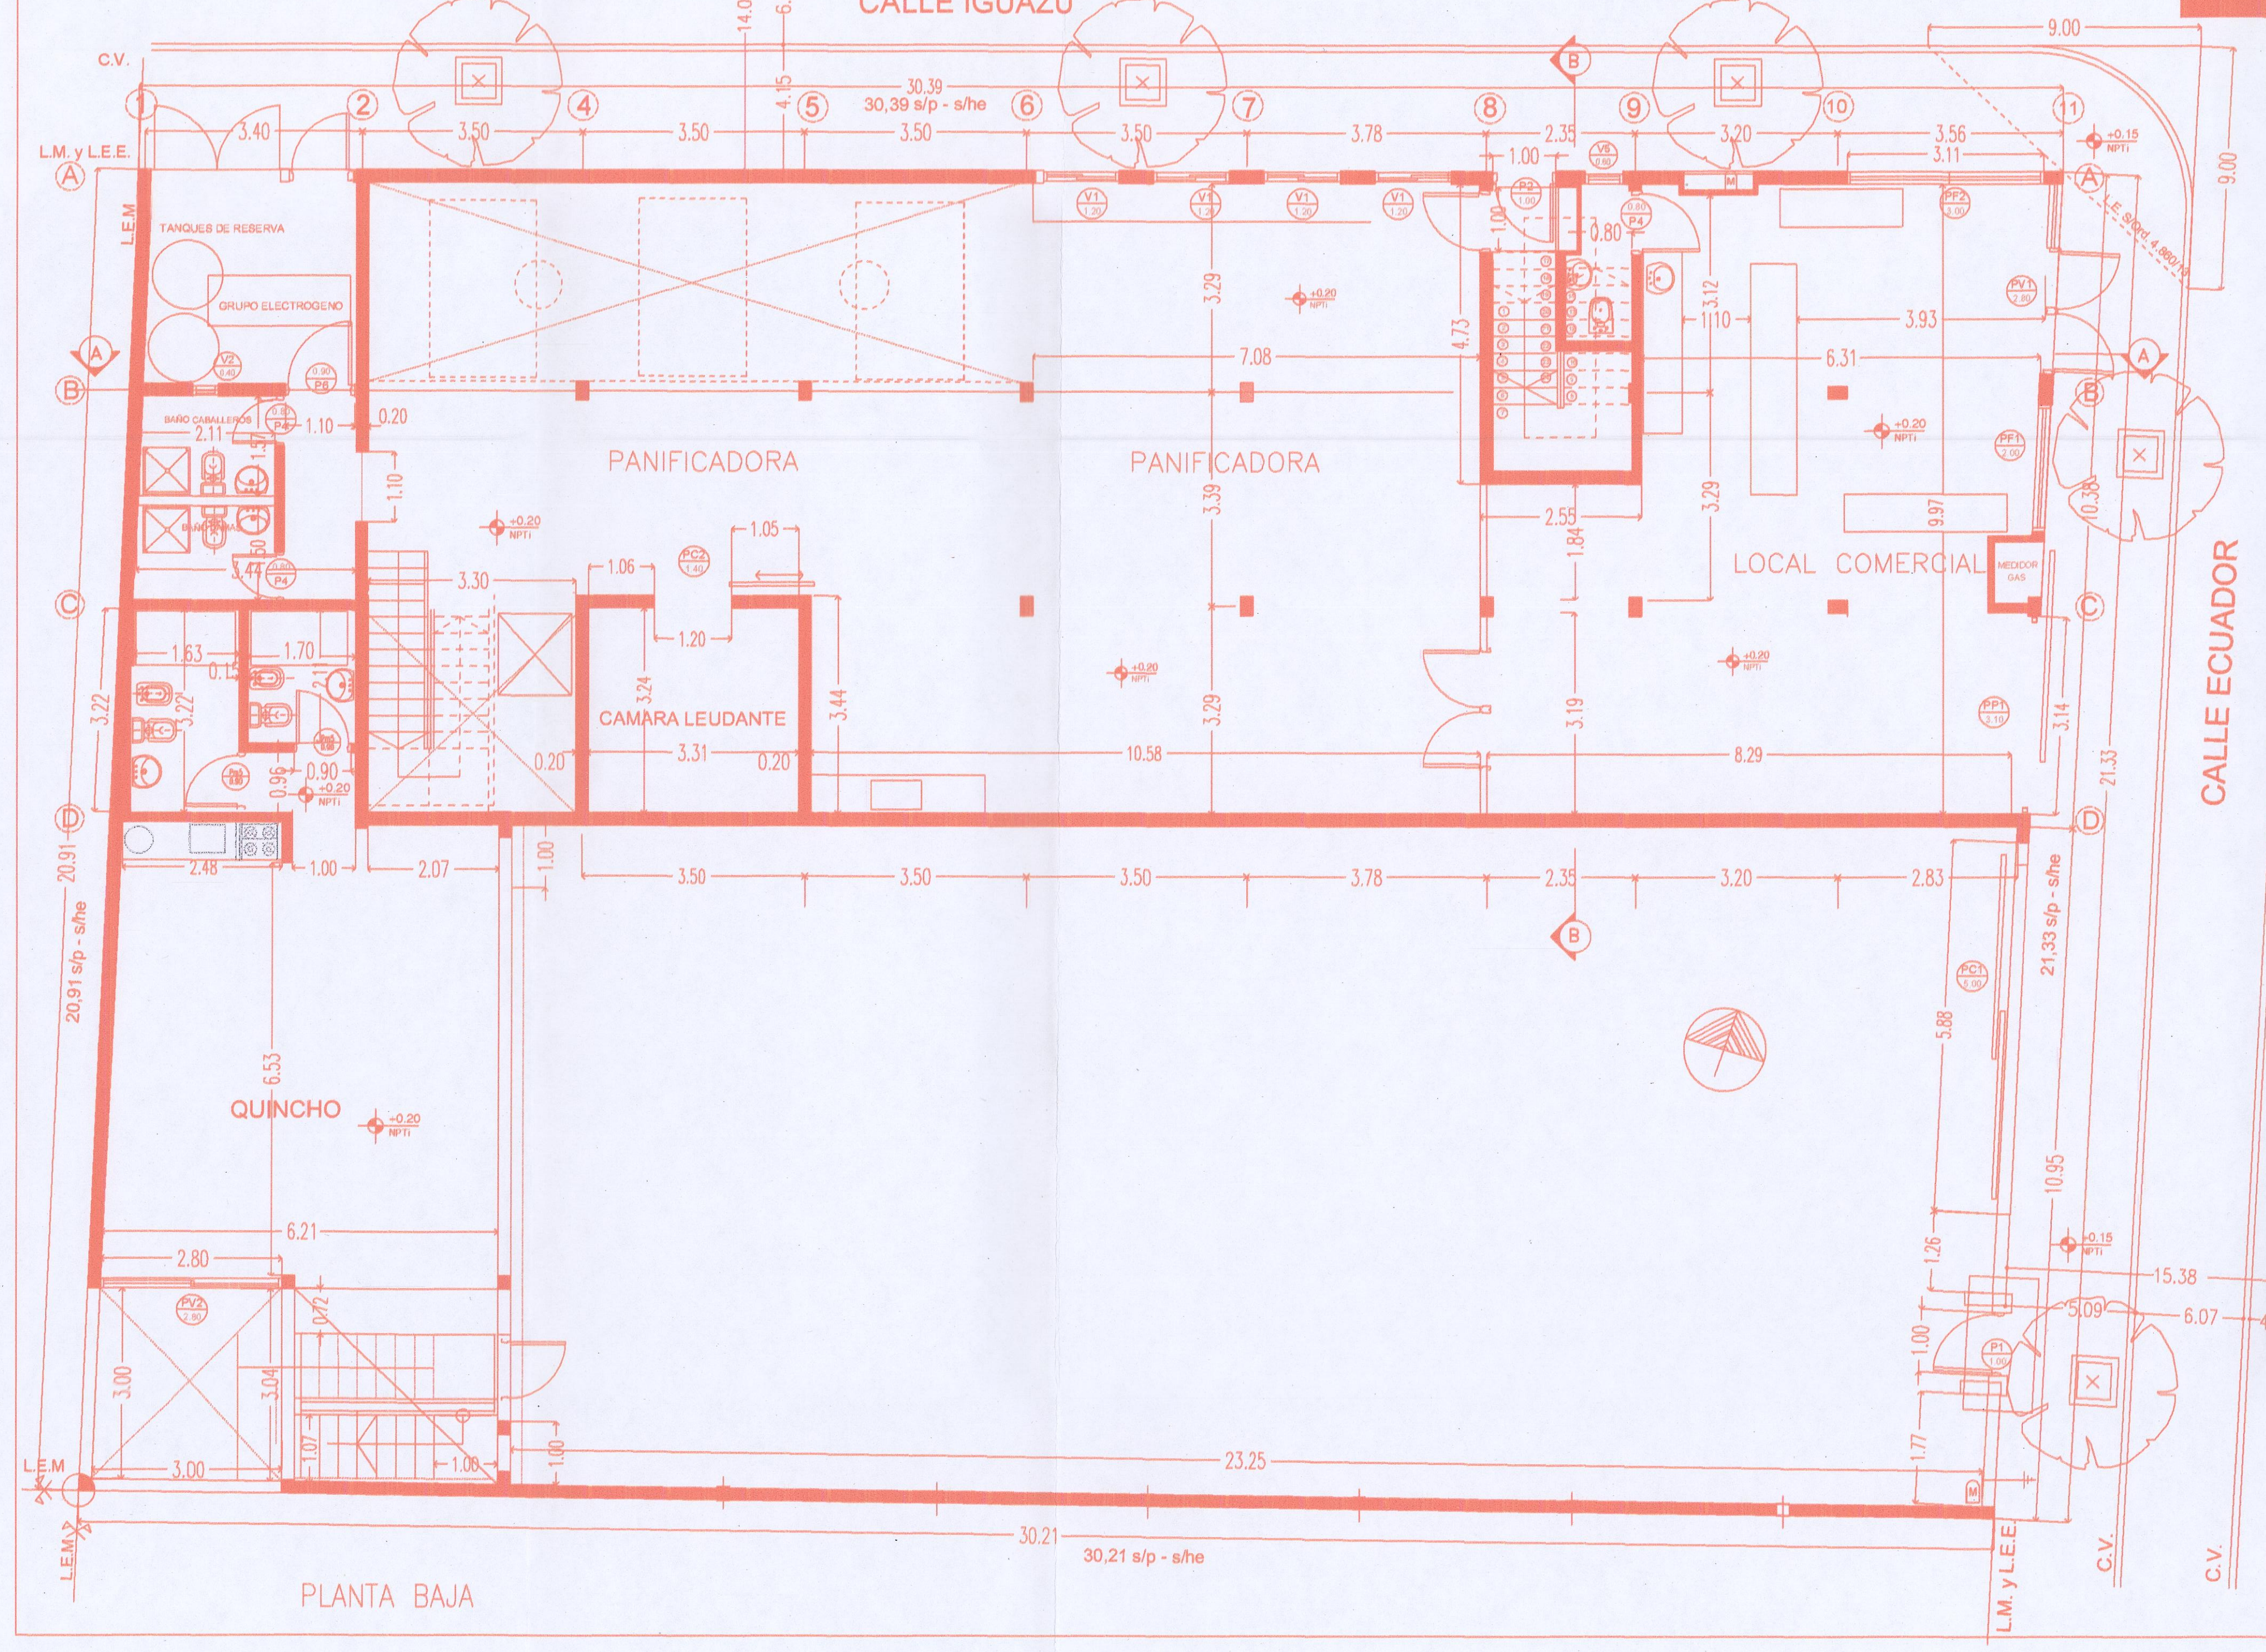
PLANTA BAJA

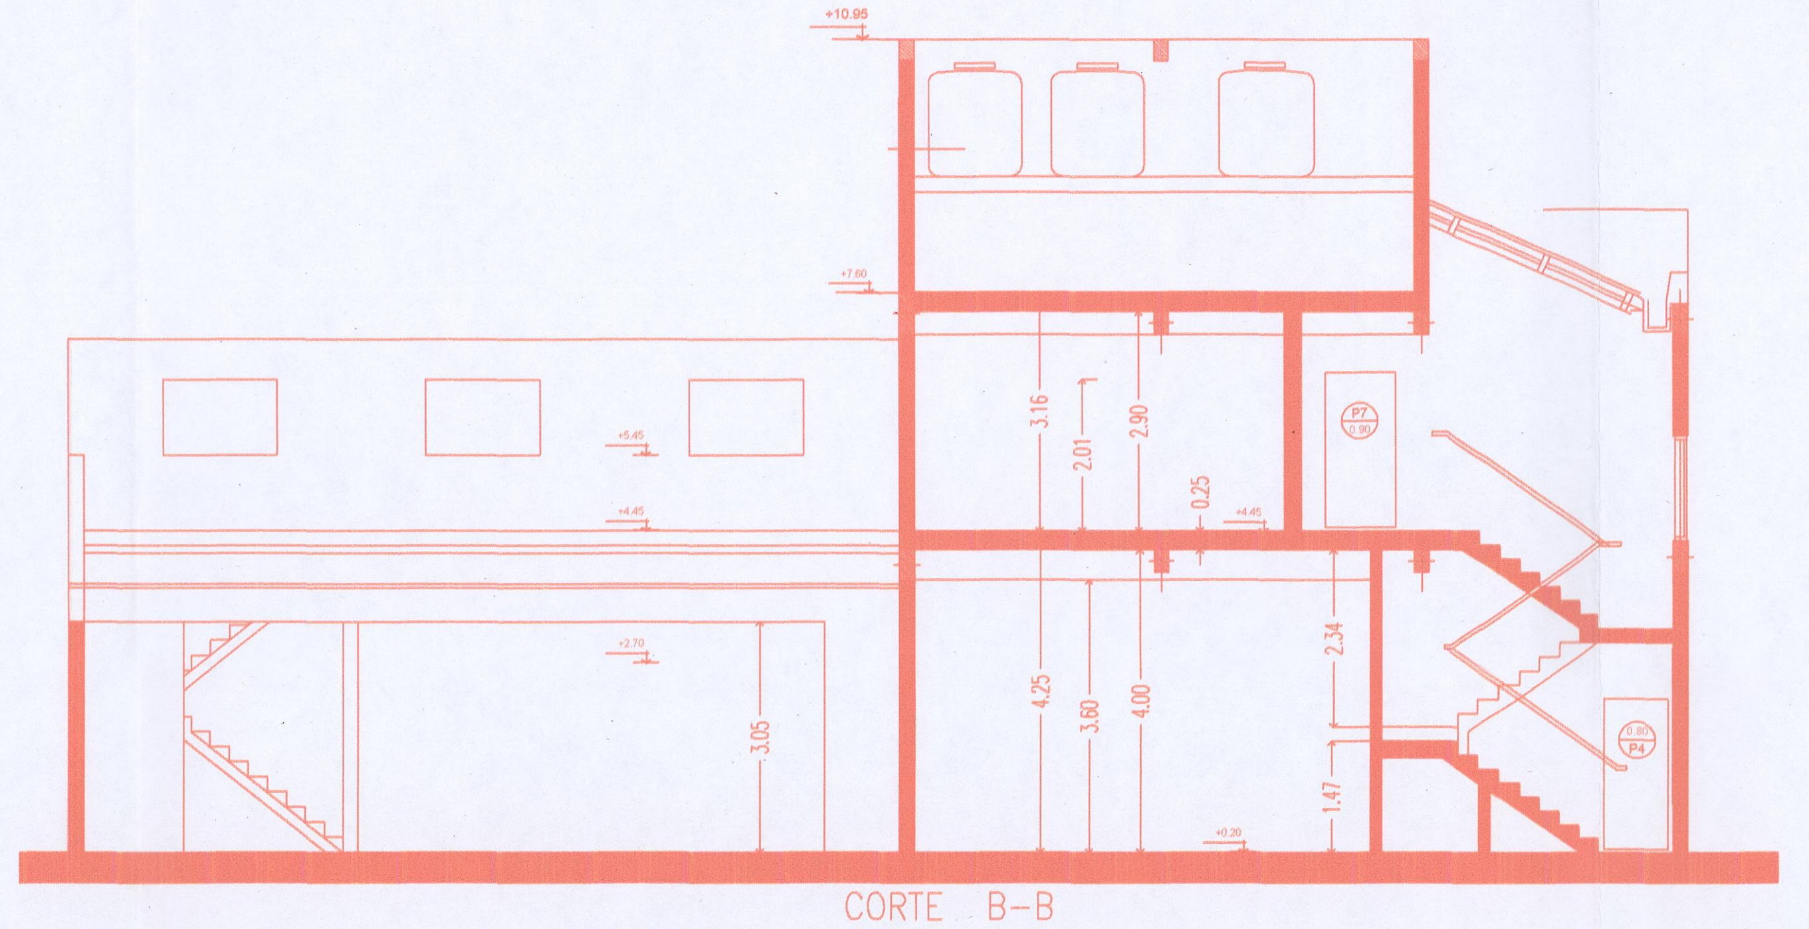
CORTE B-B

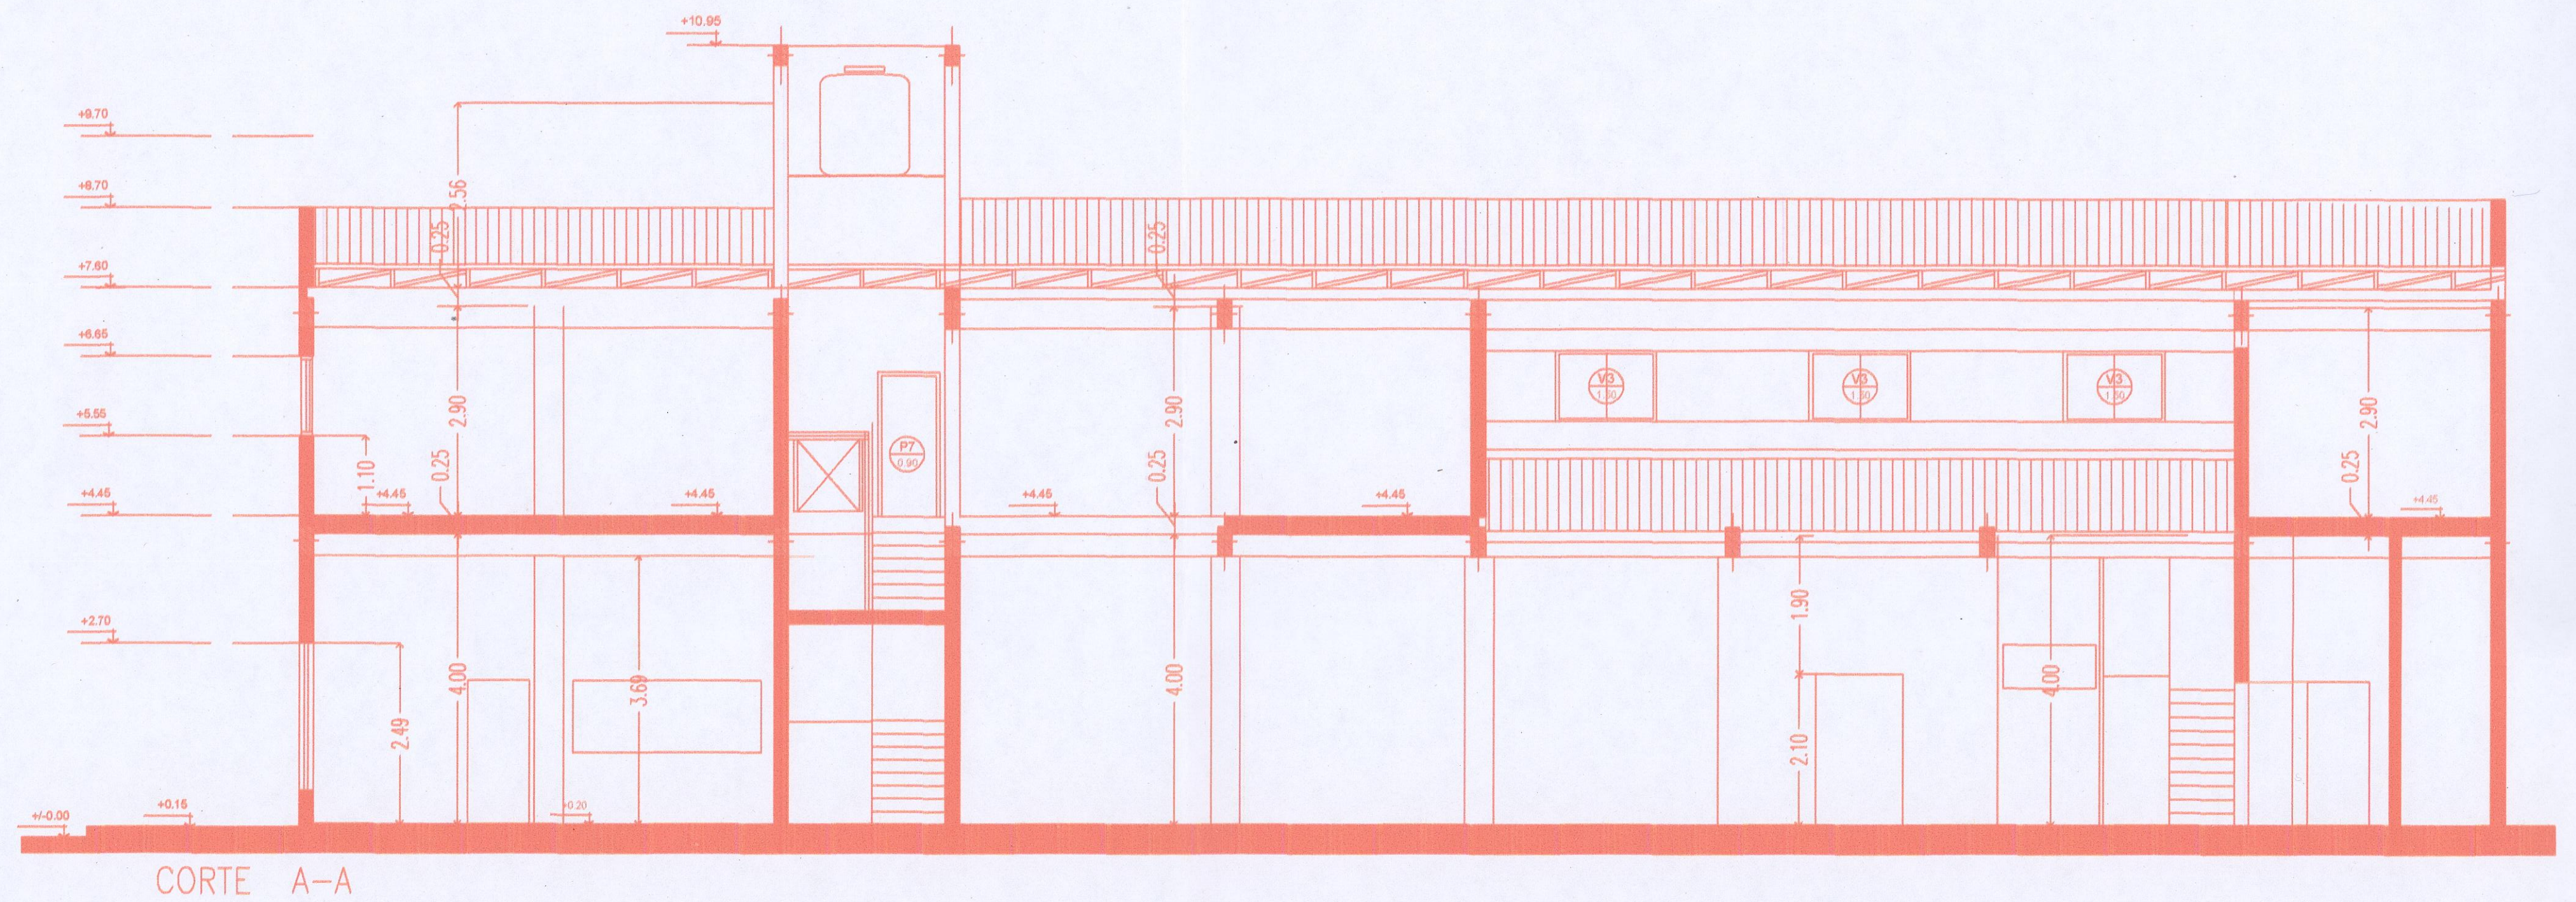
CORTE A-A

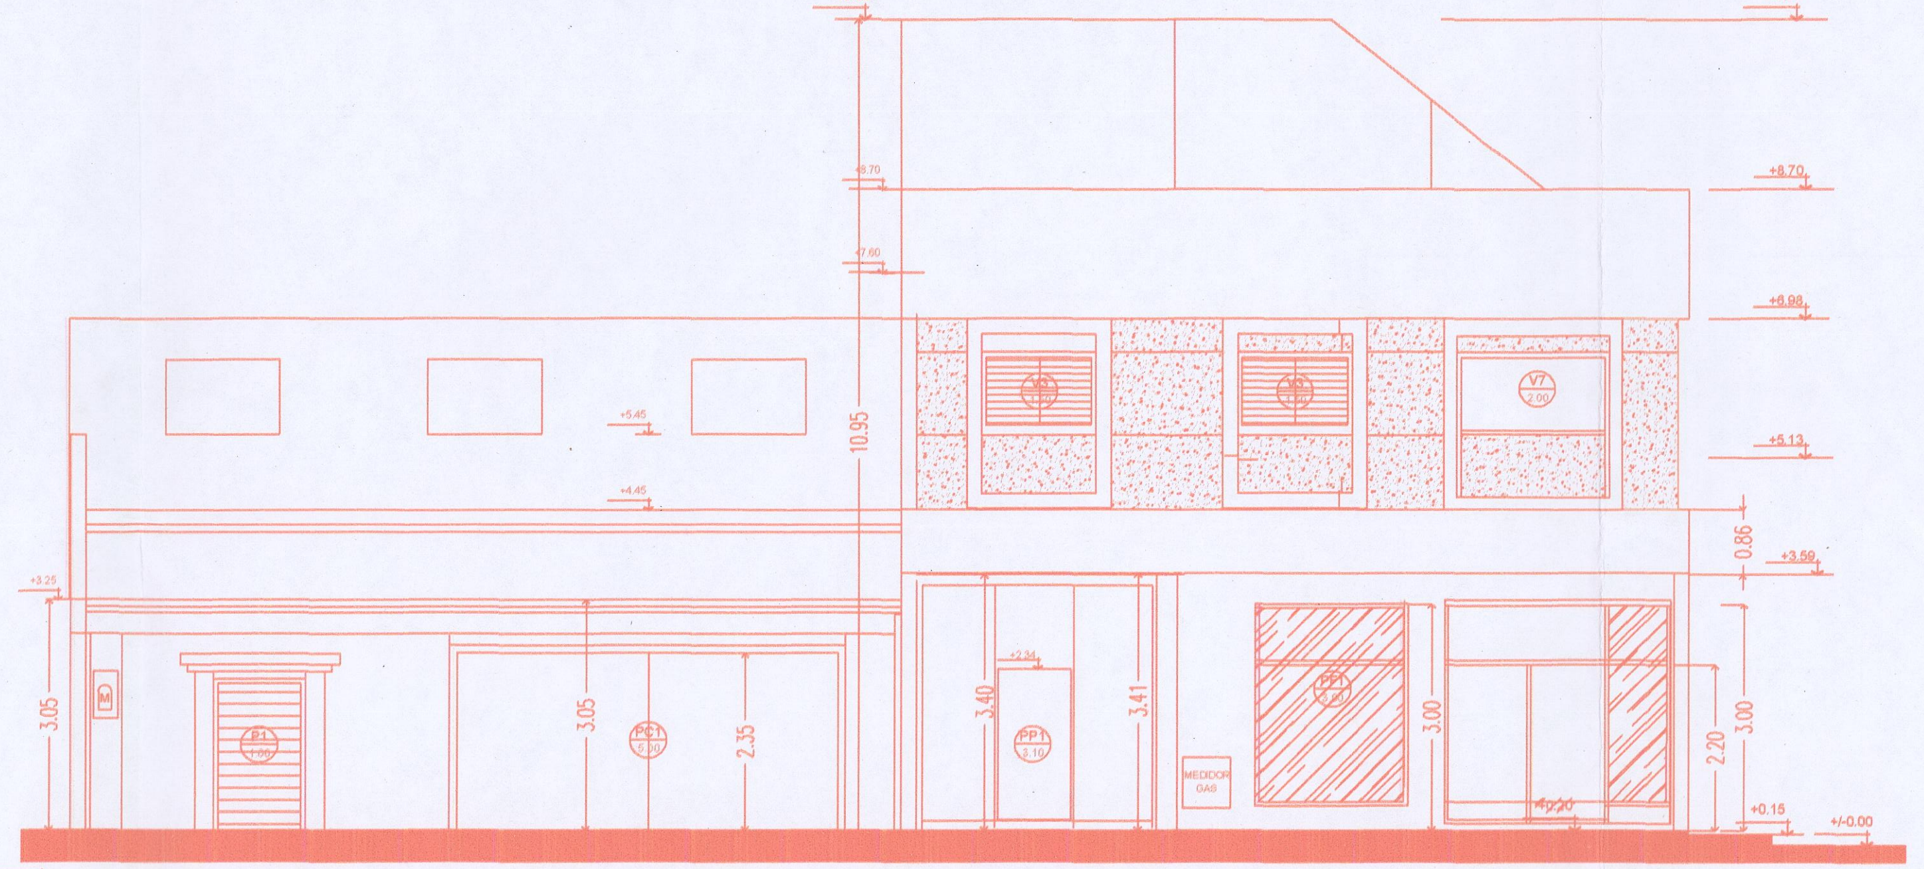
FACHADA SOBRE CALLE ECUADOR

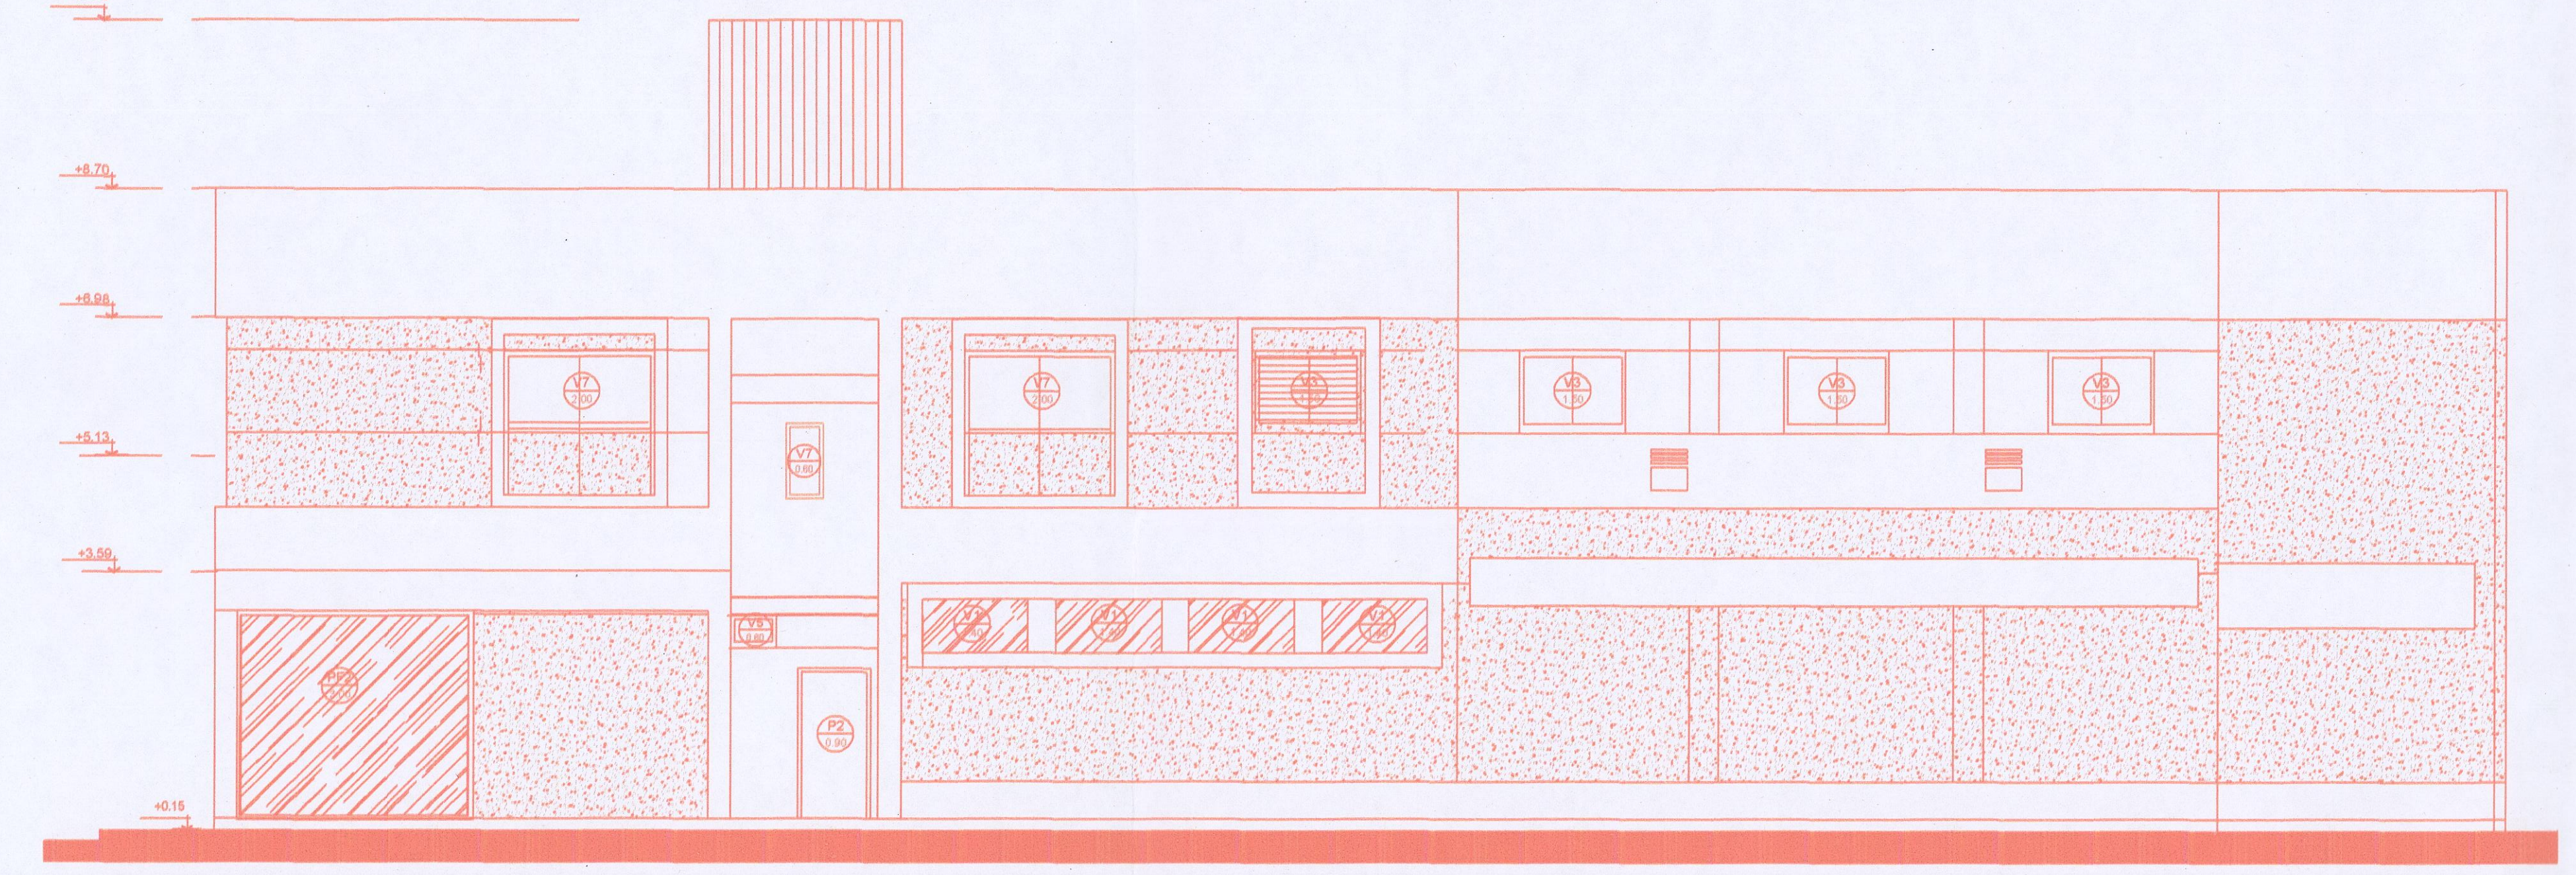
FACHADA SOBRE CALLE IGUAZU

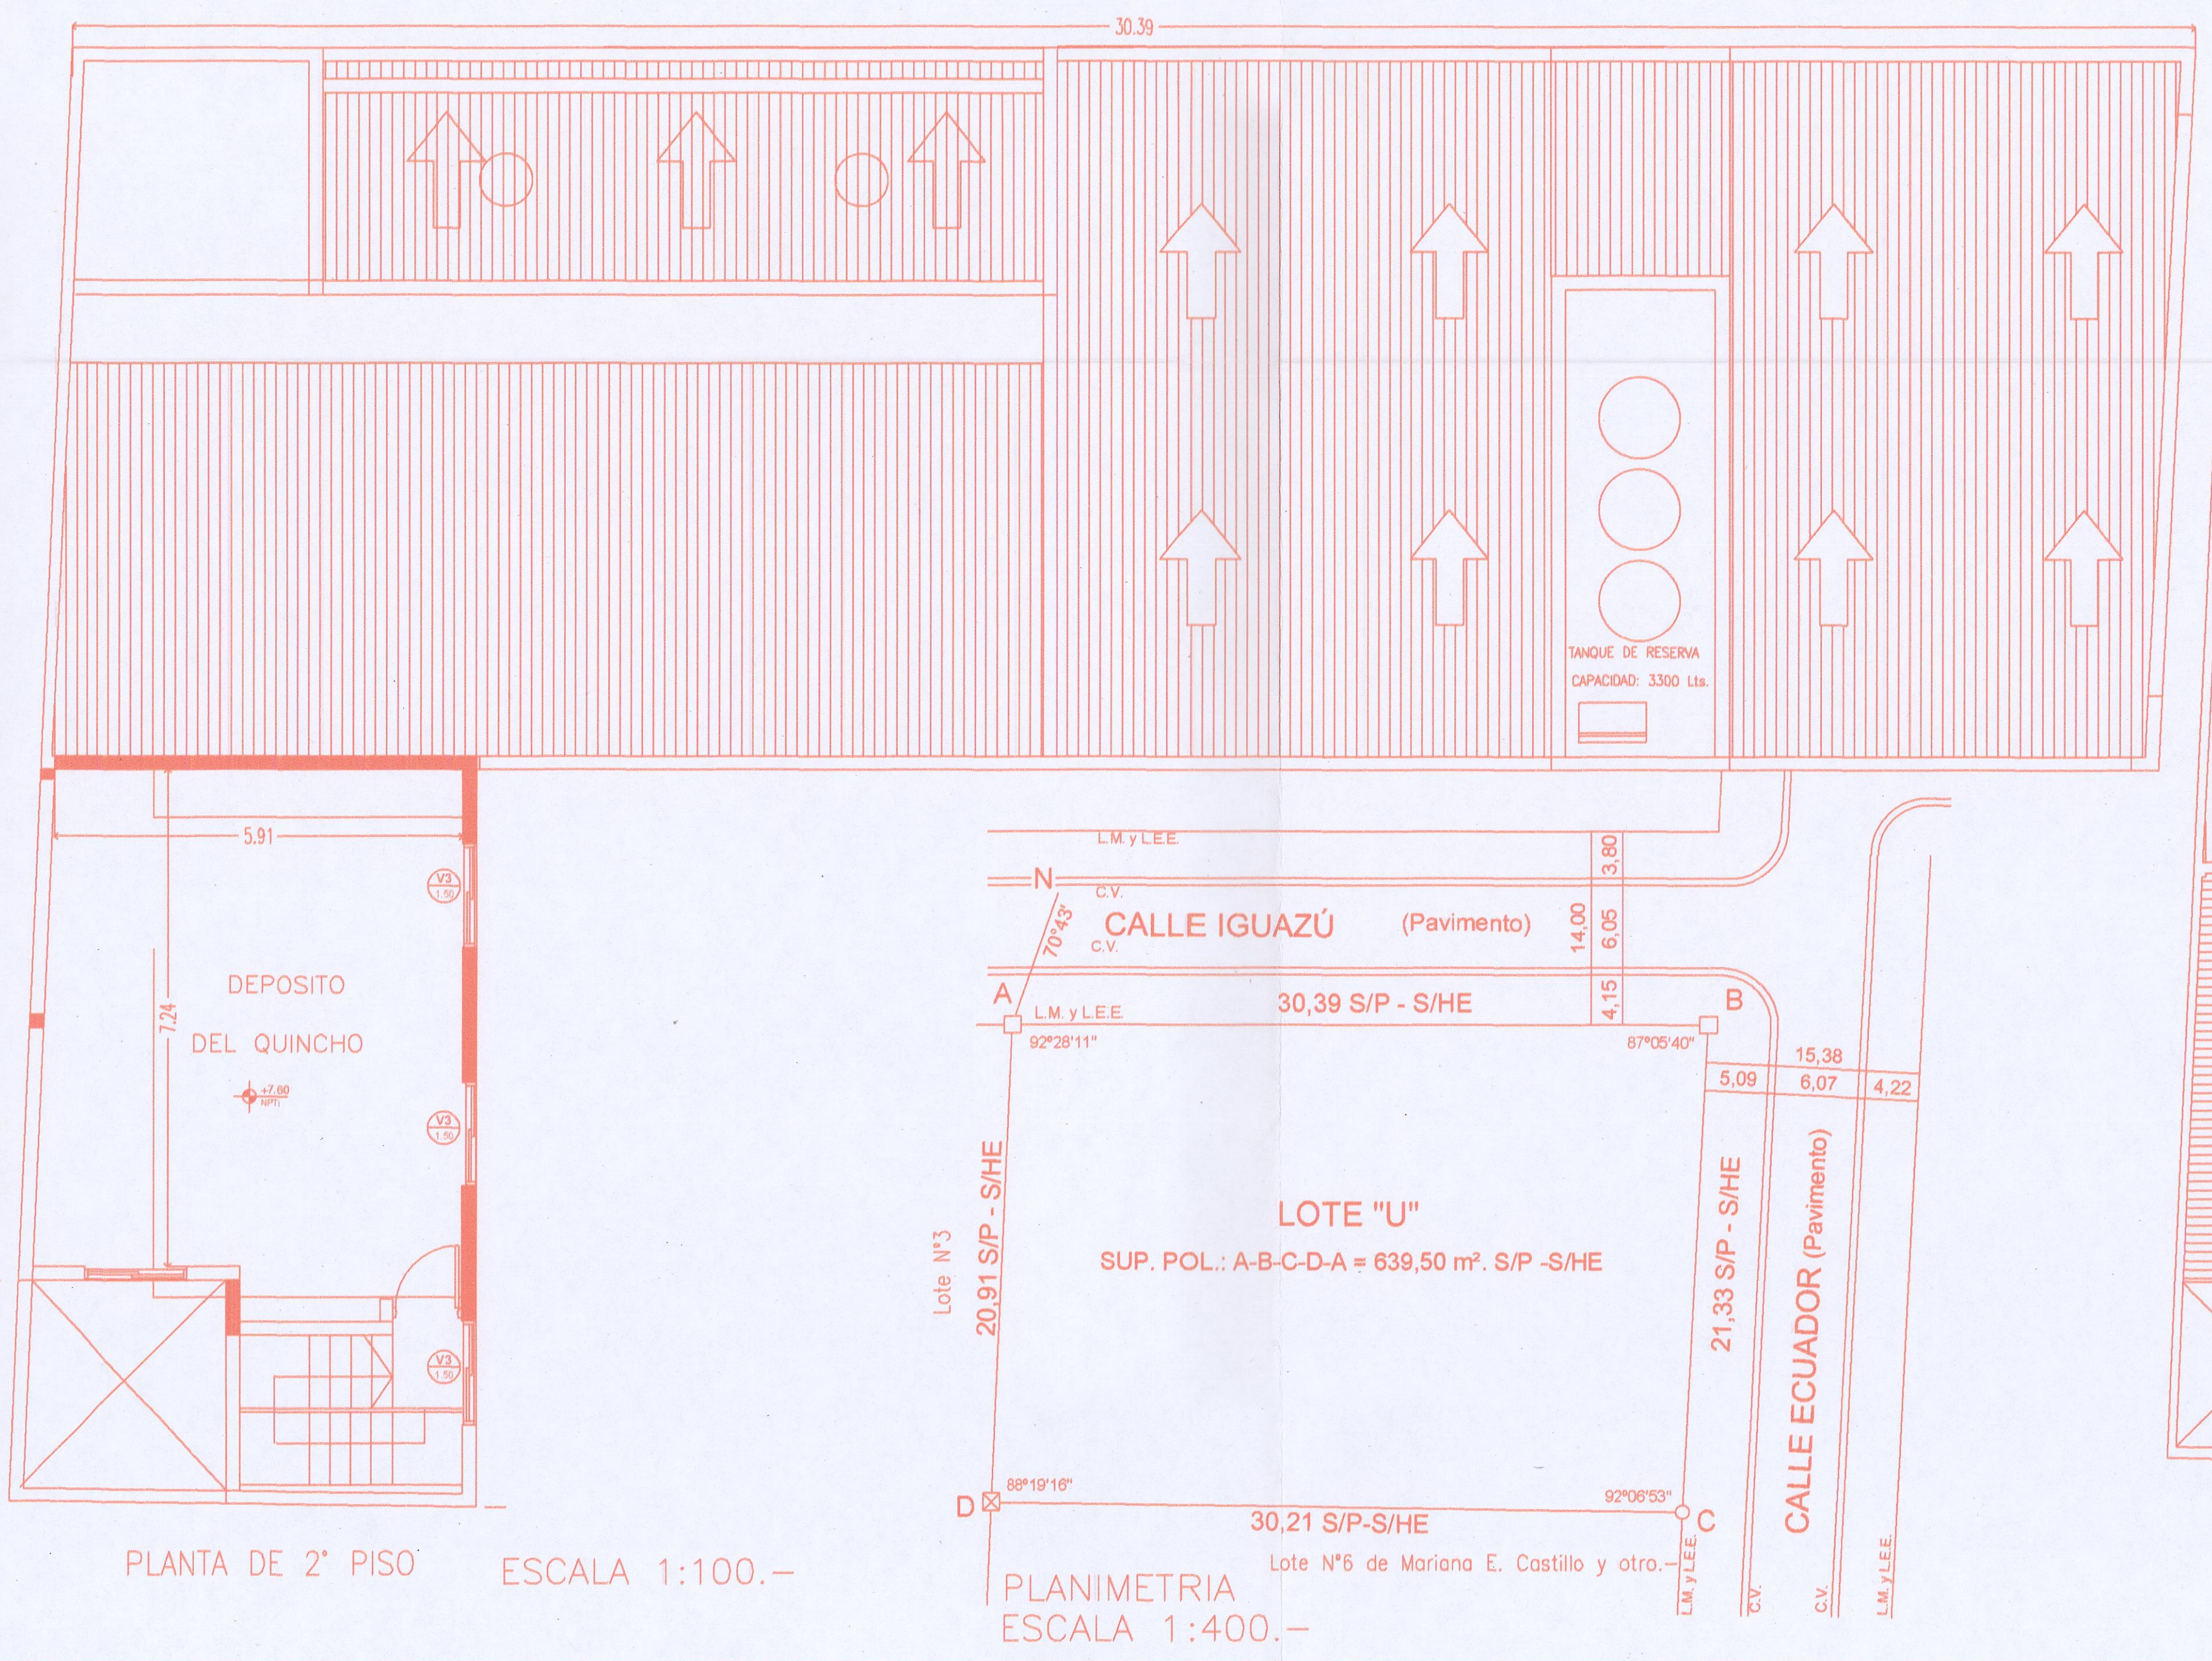
PLANTA DE 2° PISO

ESCALA 1:100.-

PLANIMETRIA
ESCALA 1:400.-

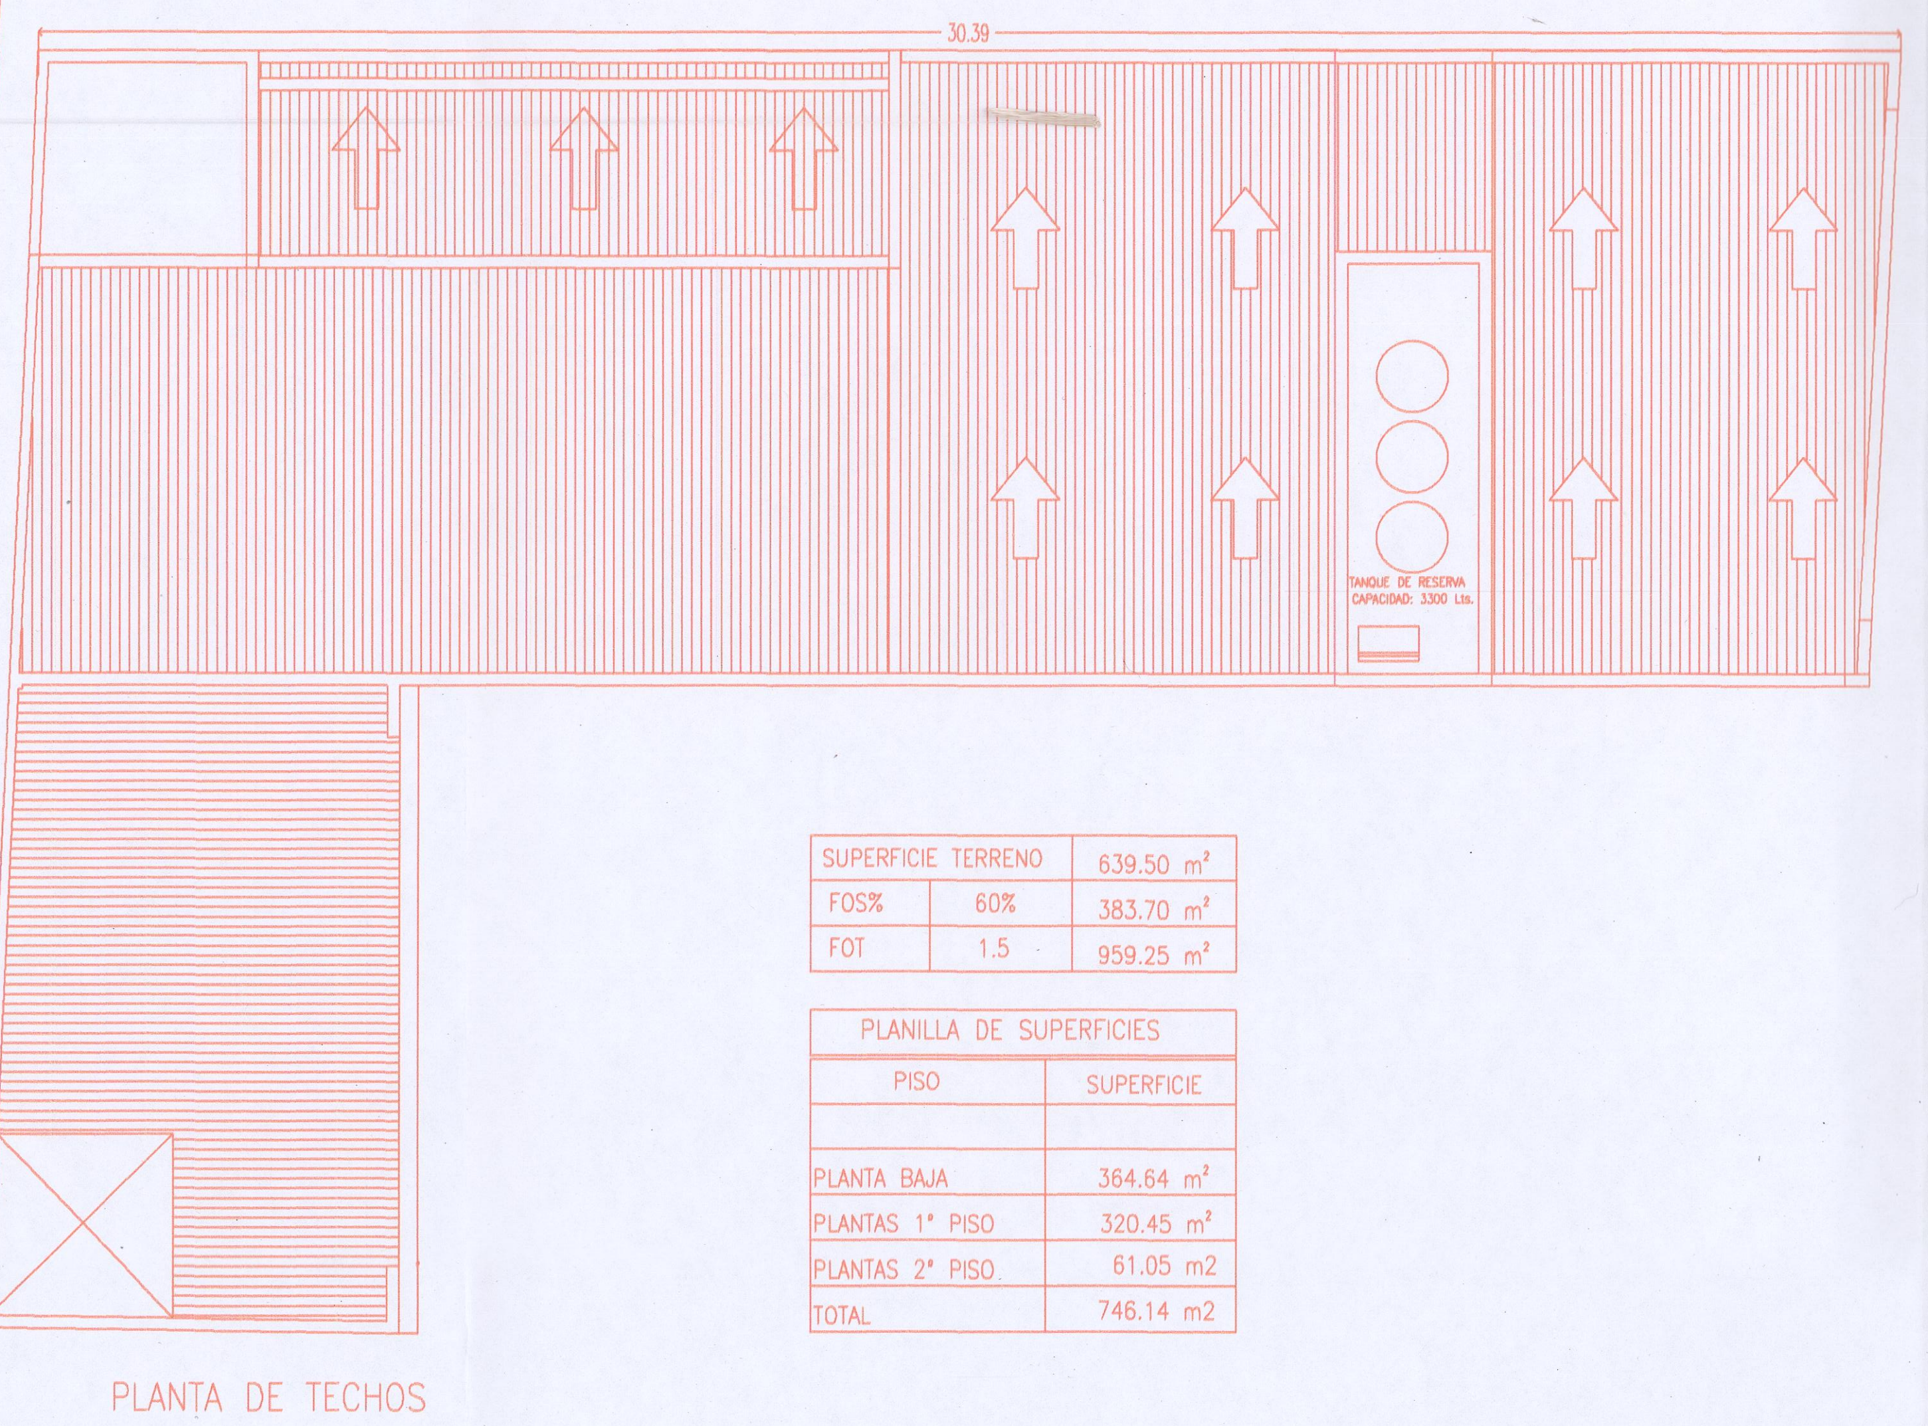
PLANTA DE TECHOS

SUPERFICIE TERRENO		639.50 m²
FOS%	60%	383.70 m²
FOT	1.5	959.25 m²

PLANILLA DE SUPERFICIES	
PISO	SUPERFICIE
PLANTA BAJA	364.64 m²
PLANTAS 1° PISO	320.45 m²
PLANTAS 2° PISO	61.05 m2
TOTAL	746.14 m2

DIST. : 02 ZONA : 10 MANZ. : 15 (D2) PARC.:015/016-020
PADRON INMOB.: 01-1-148890 / 01-1-148891 I.C.M.: N°161-F-2024 DOMINIO : 7S-38-291 / 7S-38-292

LEY 4683

24080769

COLEGIO DE ARQUITECTOS
LEY 6654/8
SANTIAGO DEL ESTERO

04 ENE 2025

PROYECTO Y
DIRECCION DE OBRA

SUSANA ABECASSIS
Arquitecta
Secretaría Técnica
Colegio de Arquitectos SDE

DEST. DE LA OBRA : LOCAL COMERCIAL
PANADERIA _ DEPOSITO_
DEPARTAMENTOS

PROPIETARIO: **GRACIELA ELIZABETH FERNANDEZ**

DNI : 22.243.740 CUIL : 27-22243740-2

UBICACION : CALLE ECUADOR ESQUINA IGUAZU S/N

BARRIO : AMERICA DEL SUR

CIUDAD : CAPITAL - SANTIAGO DEL ESTERO

ESCALA : 1:100 - 1:200

DIRECCION DE SUELO URBANO
EXPEDIENTE 777/31/24
FECHA DE SELLADO 03 ABR. 2025
BOLETA N° 336

SUP. DE TERRENO :	s/p - s/he 639.50 m²
SUP. CUBIERTA :	746.14 m²
SUP. FUERA DE L. MUNICIPAL:	00.00 m²
SUP. CUBIERTA TOTAL :	746.14 m²

CROQUIS DE UBICACION

ESCALA 1:2000.-

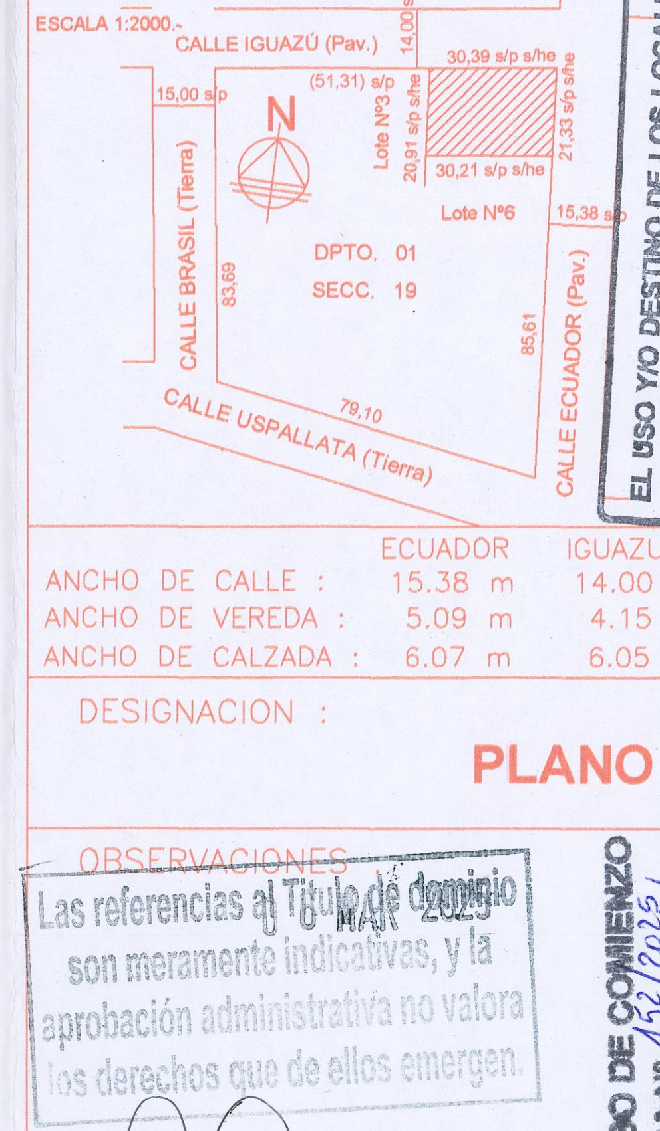

EL USO Y/O DESTINO DE LOS LOCALES
ESTA SUJETO A LAS DISPOSICIONES DE
LA ORDENANZA N°7968 CAPITULO 3

PROPIETARIO : GRACIELA ELIZABETH FERNANDEZ

DOMICILIO : PUEYRREDON N°16 - B°BELGRANO

Alejandro Rodriguez Paz
ARQUITECTO
Mat. Prof. N° 626

PROYECTO : ALEJANDRO E. RODRIGUEZ PAZ ARQUITECTO

DOMICILIO : JOSE OLAECHEA N°206 - B° AUTONOMIA

Alejandro Rodriguez Paz
ARQUITECTO
Mat. Prof. N° 626

DIRECCION TECNICA : ALEJANDRO E. RODRIGUEZ PAZ ARQUITECTO

DOMICILIO : JOSE OLAECHEA N°206 - B° AUTONOMIA

CATEGORIA COLEGIO DE ARQUITECTOS

	ECUADOR	IGUAZU
ANCHO DE CALLE :	15.38 m	14.00 m
ANCHO DE VEREDA :	5.09 m	4.15 m
ANCHO DE CALZADA :	6.07 m	6.05 m

PAVIMENTO : SI

SERVICIOS CLOACALES : SI

SECRETARIA DE ECONOMIA
Municipalidad de la Capital
SGO. DEL ESTERO
DIREC. DE SUELO URBANO

DIRECCION DE SUELO URBANO
EXPEDIENTE 777/31/2024
FECHA DE SELLADO 27 DIC. 2024
BOLETA N° 3370

DESIGNACION :

PLANO GENERAL

OBSERVACIONES :

Las referencias al Título de dominio
son meramente indicativas, y la
aprobación administrativa no valora
los derechos que de ellos emergen.

0 6 MAR 2025

PERMISO DE COMIENZO
DE OBRA N° 152/2025 31/3/2025
DIRECCION DE SUELO URBANO

MUNICIPALIDAD DE LA CIUDAD DE SANTIAGO DEL ESTERO
SECRETARIA DE ECONOMIA
APROBADO
DIRECCIÓN DE SUELO URBANO
EXPEDIENTE: 777-31-2024_Corp. 05-E-2024
FECHA: 0 8 ABR 2025

Ing. Agrim. J. LEANDRO ARJONA
JEFE DE AREA DE VISACIONES TECNICAS
DIRECCION DE CATASTRO MUNICIPAL

Arq. ABRAHAM BERNARDO ROMINA
Dpto. OBRAS PRIVADAS
DIRECCION DE SUELO URBANO

Arq. Cesar Marcelo Alc
Director D.S.U.
Municipalidad de la C