




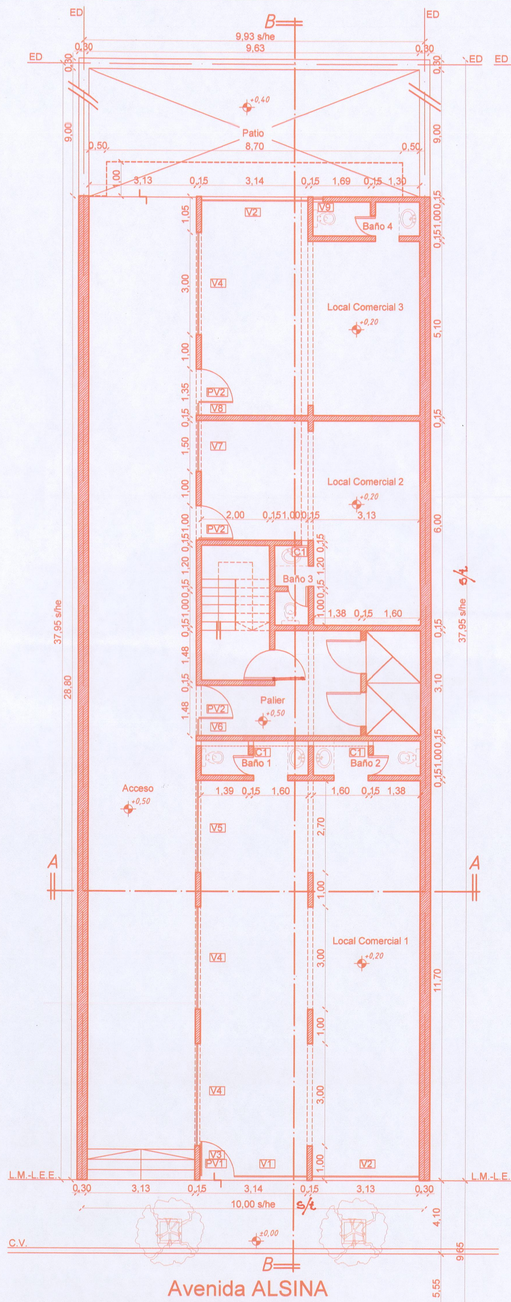


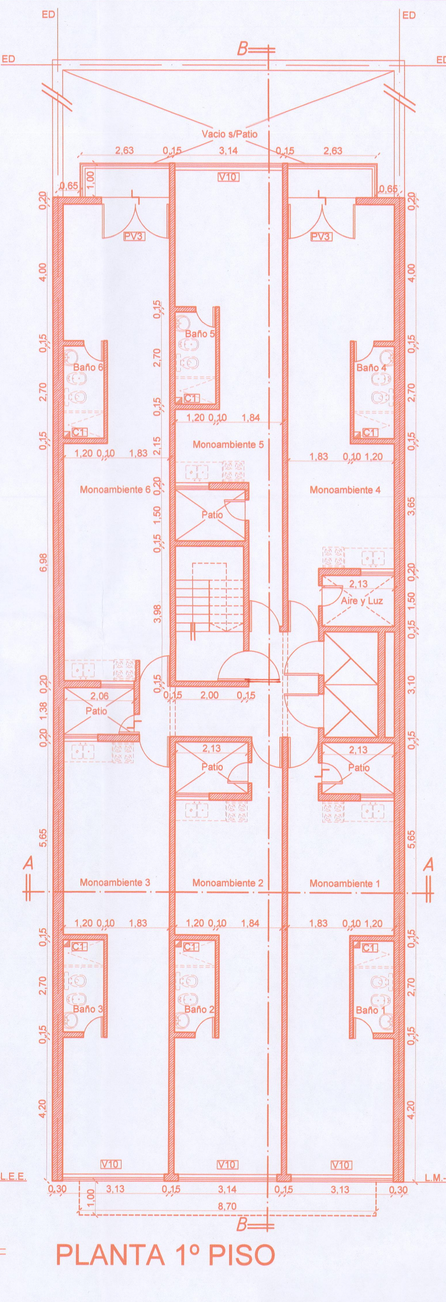

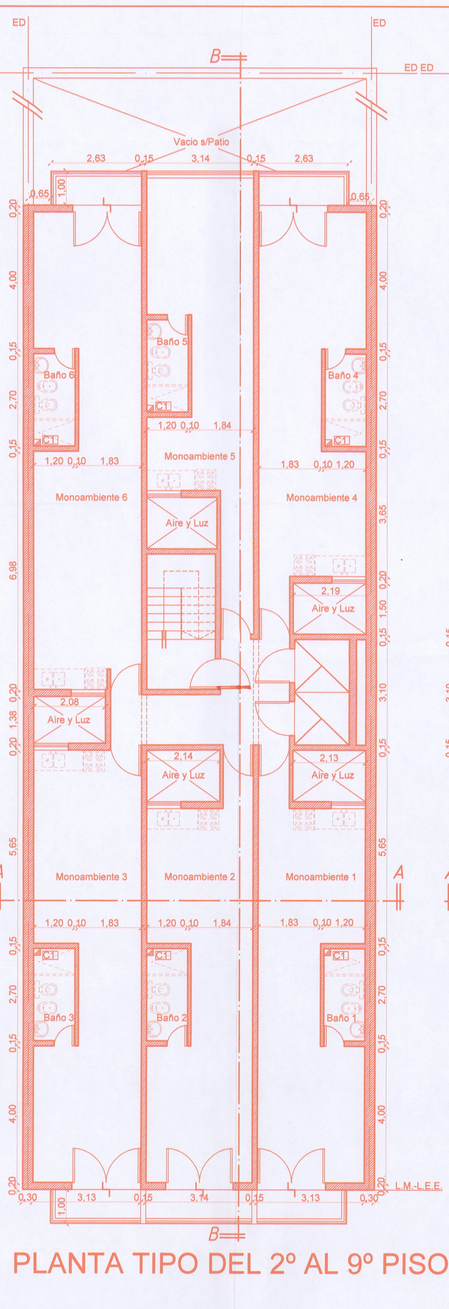

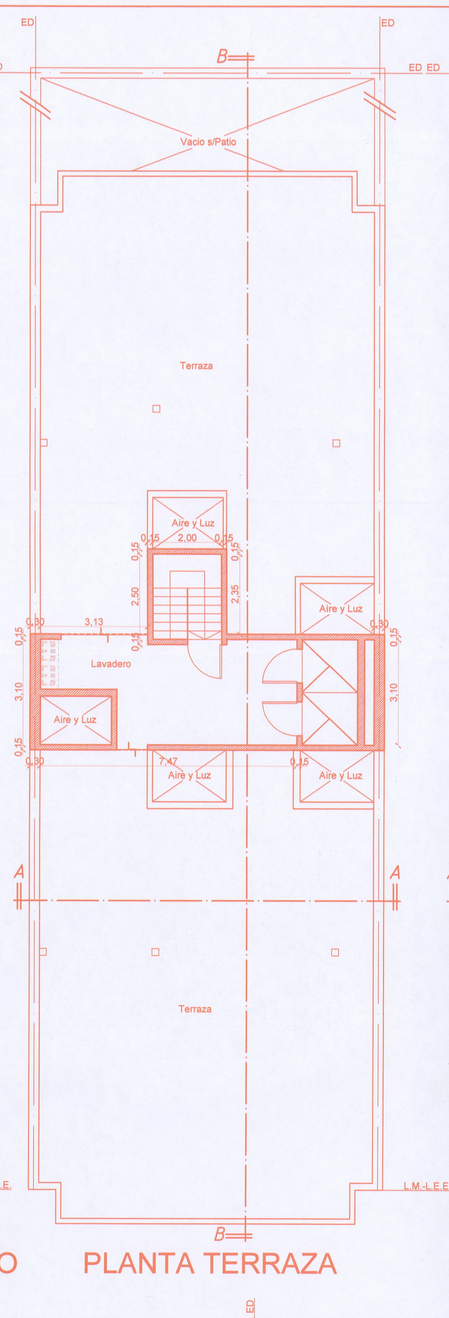

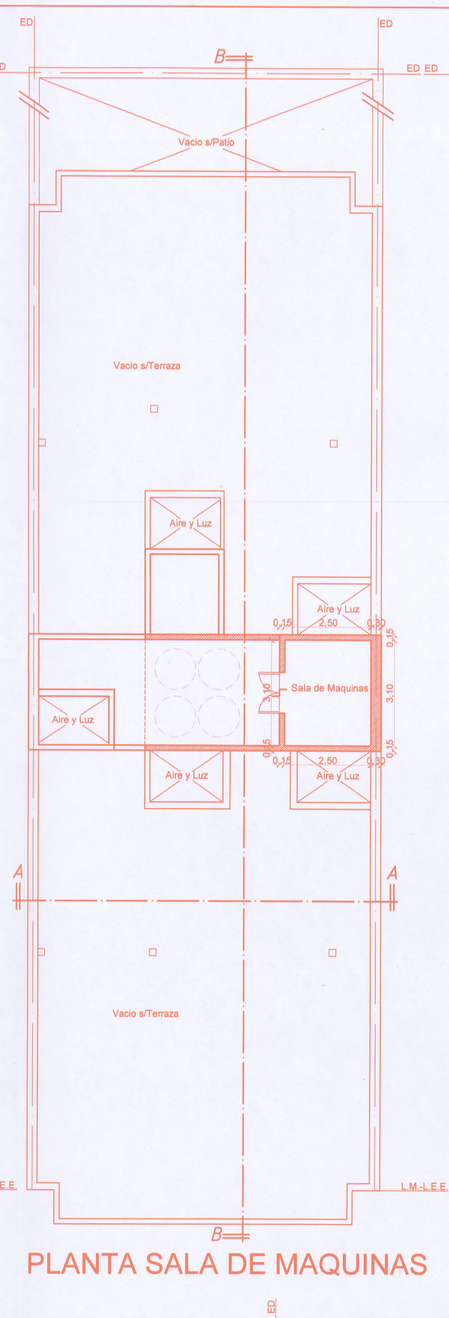

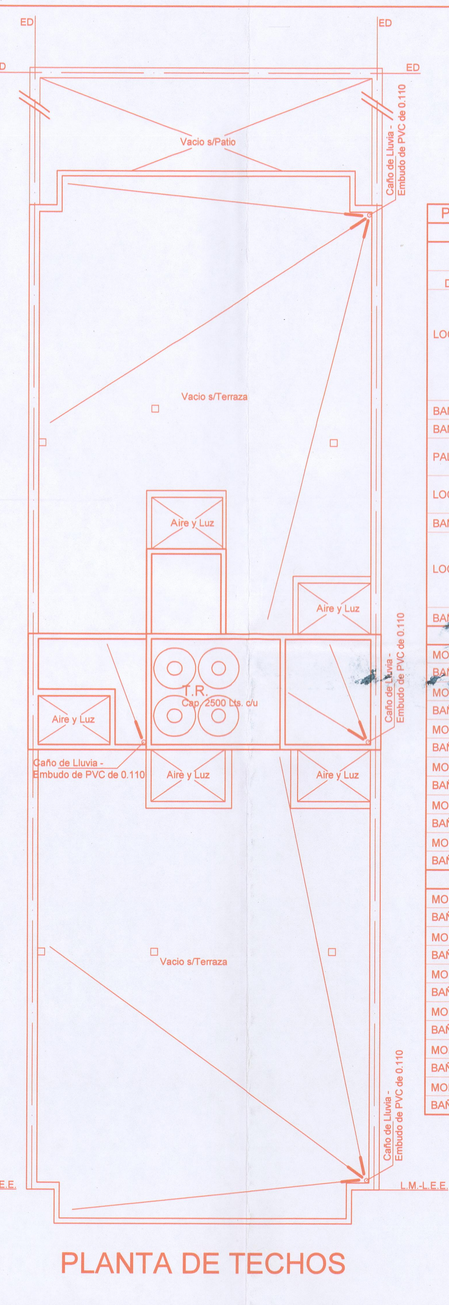

PLANILLA DE ILUMINACION, VENTILACION Y SUPERFICIES

PLANTA BAJA

LOCAL		ABERTURAS			AREAS		OBSERV.
DESIGNACION	SUPERF. m2	DESIG.	ANCHO	ALTO	ILUM	VENT.	
LOC. COMERC. 1	74.14	PV1	1.00	2.20	2.20		Vidriera
		V1	2.11	3.18	6.70		Vidriera
		V2	3.13	3.18	9.95	2.20	Vidriera
		V3	1.00	0.98	0.98		Vidriera
		V4	3.00	2.50	15.00		2 Unid./Vidrieras
		V5	2.70	2.50	9.75		Vidriera
BAÑO 1	3.14	C1	0.15	0.15	0.02	0.02	
BAÑO 2	3.14	C1	0.15	0.15	0.02	0.02	
PALIER	14.47	PV2	1.00	2.50	2.50	2.50	Vidriera
		V6	0.75	2.50	3.75		2 Unid./Vidrieras
LOC. COMERC. 2	30.27	PV2	1.00	2.50	2.50		Vidriera
		V6	1.50	2.50	3.75		Vidriera
BAÑO 3	2.32	---	---	---	---		Vent. Mecanica
LOC. COMERC. 3	36.41	PV2	1.00	2.50	2.50		Vidriera
		V2	3.13	3.18	9.95		Vidriera
		V4	3.00	2.50	7.50		Vidriera
		V8	0.35	2.50	0.87		Vidriera
BAÑO 4	3.14	V9	0.30	0.30	0.09	0.09	


PLANTA 1º PISO


MONOAMB. 1	35.09	V10	3.00	1.50	4.50	4.50	
BAÑO 1	3.24	C2	0.20	0.20	0.04	0.04	
MONOAMB. 2	35.82	V10	3.00	1.50	4.50	4.50	
BAÑO 2	3.24	C2	0.20	0.20	0.04	0.04	
MONOAMB. 3	39.07	V10	3.00	1.50	4.50	4.50	
BAÑO 3	3.24	C2	0.20	0.20	0.04	0.04	
MONOAMB. 4	34.57	PV3	2.00	2.10	4.20	4.20	
BAÑO 4	3.24	C2	0.20	0.20	0.04	0.04	
MONOAMB. 5	30.14	V10	3.00	1.50	4.50	4.50	
BAÑO 5	3.24	C2	0.20	0.20	0.04	0.04	
MONOAMB. 6	39.63	PV3	2.00	2.10	4.20	4.20	
BAÑO 6	3.24	C2	0.20	0.20	0.04	0.04	


PLANTA 2º AL 9º PISO


MONOAMB. 1	35.09	PV3	2.00	2.10	4.20	4.20	
BAÑO 1	3.24	C2	0.20	0.20	0.04	0.04	
MONOAMB. 2	35.82	PV3	2.00	2.10	4.20	4.20	
BAÑO 2	3.24	C2	0.20	0.20	0.04	0.04	
MONOAMB. 3	39.07	PV3	2.00	2.10	4.20	4.20	
BAÑO 3	3.24	C2	0.20	0.20	0.04	0.04	
MONOAMB. 4	34.57	PV3	2.00	2.10	4.20	4.20	
BAÑO 4	3.24	C2	0.20	0.20	0.04	0.04	
MONOAMB. 5	30.14	V10	3.00	1.50	4.50	4.50	
BAÑO 5	3.24	C2	0.20	0.20	0.04	0.04	
MONOAMB. 6	39.63	PV3	2.00	2.10	4.20	4.20	
BAÑO 6	3.24	C2	0.20	0.20	0.04	0.04	

SUP. DEL TERRENO:	S/T 356.80 m² - S/P y S/HE 357.21 m²
SUP. CUBIERTA P.B.:	296.70 m²
SUP. CUBIERTA 1º P.:	296.70 m²
SUP. CUBIERTA 2º P.:	296.70 m²
SUP. CUBIERTA 3º P.:	296.70 m²
SUP. CUBIERTA 4º P.:	296.70 m²
SUP. CUBIERTA 5º P.:	296.70 m²
SUP. CUBIERTA 6º P.:	296.70 m²
SUP. CUBIERTA 7º P.:	296.70 m²
SUP. CUBIERTA 8º P.:	296.70 m²
SUP. CUBIERTA 9º P.:	296.70 m²
SUP. CUBIERTA TERRAZA:	39.75 m²
SUP. CUBIERTA S/MAQUINAS:	9.52 m²
SUP. FUERA DE L. MUNICIPAL:	78.30 m²
SUP. CUBIERTA TOTAL:	3094.57 m²

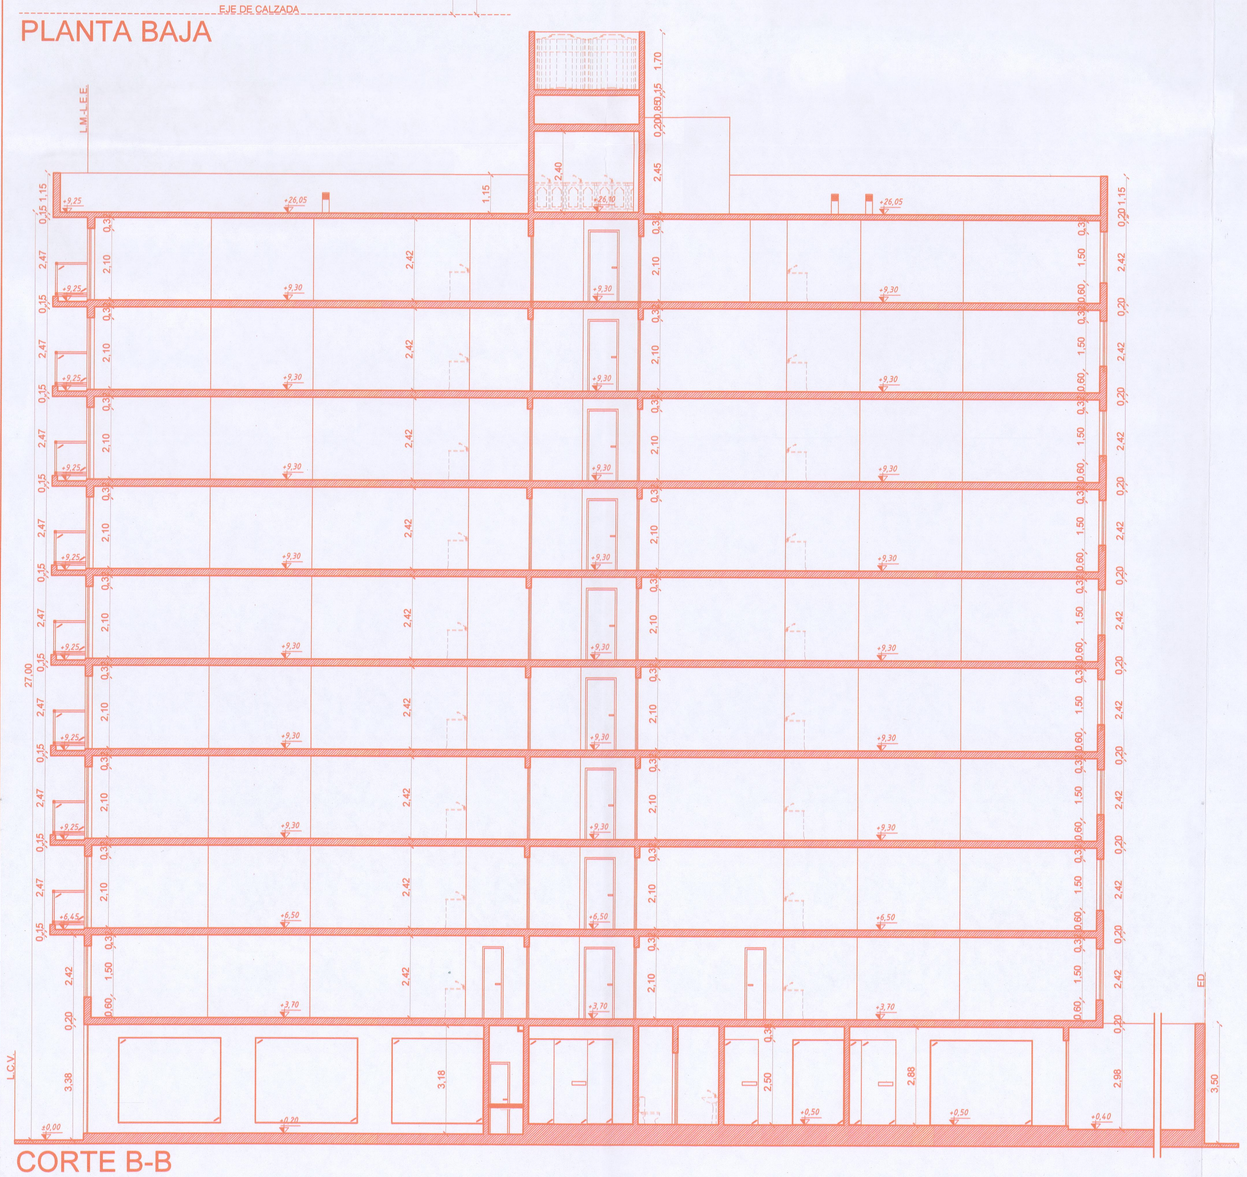

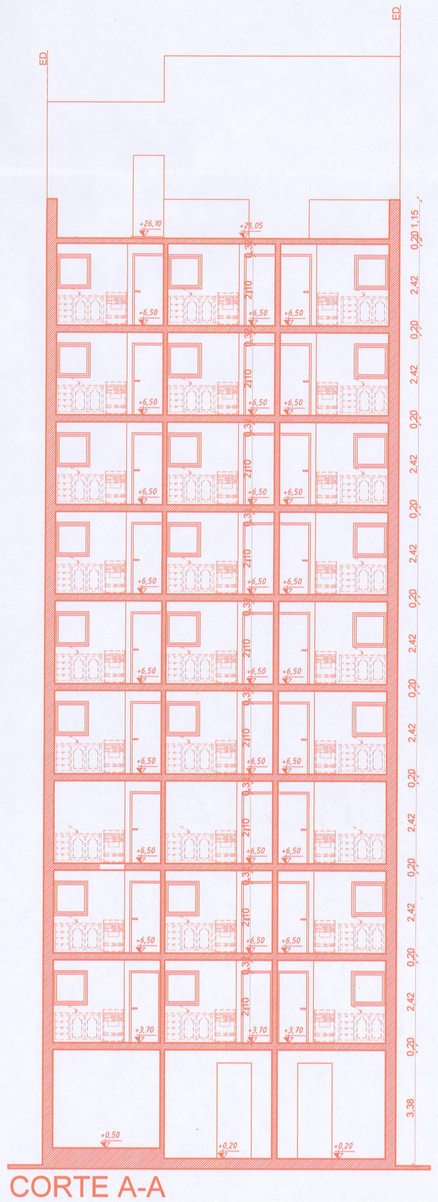

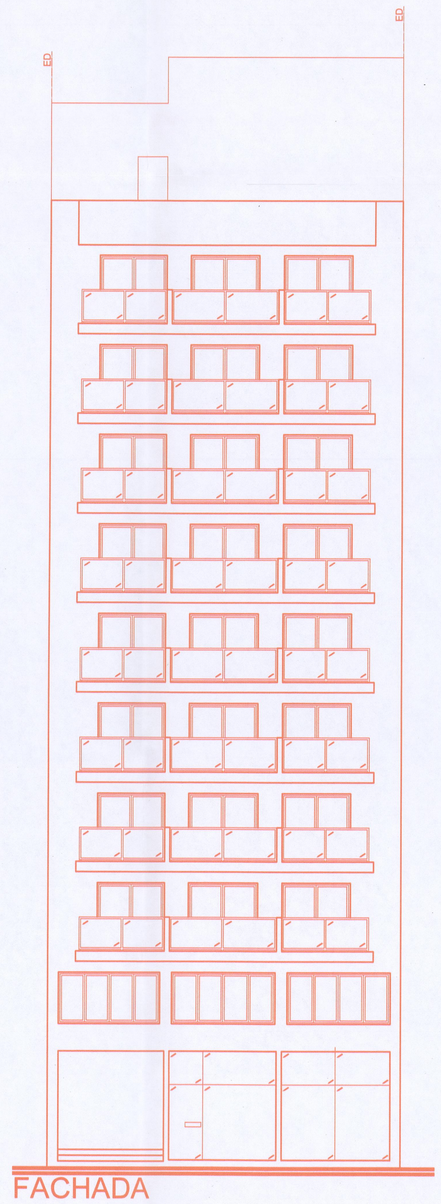

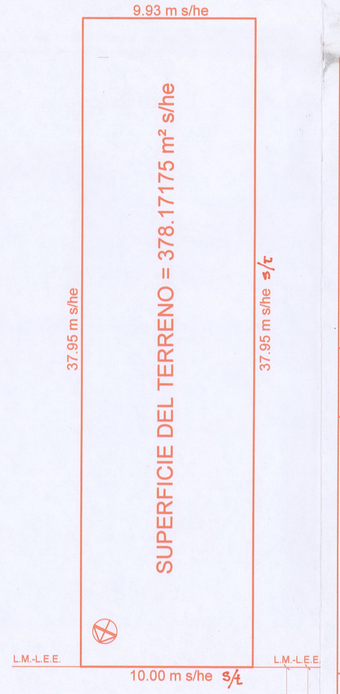

DIST.: 02 ZONA: 04 MANZ.: 18 PARC.: 250
PADRON INMOB.: 01-01-8871 ICM: 530 M-21 DOMINIO: 7S-34099

LEY 4683 1885591

DEST. DE LA OBRA : LOCALES COMERCIALES (3) Y MONOAMBIENTES (54)

PROPIETARIO : **MOSSO NORBERTO MARCELO**
DNI : 11.864.911 CUIL : 20-11964911-8
PROPIETARIO : **ALCORTA CESAR MARCELO**
DNI : 16.802.666 CUIL : 20-16802666-9
PROPIETARIO : **ALCORTA JUAN CARLOS**
DNI : 16.771.297 CUIL : 20-16771297-6

UBICACION : AVENIDA ALSINA (O) Nº 478
BARRIO : BELGRANO
CIUDAD : CAPITAL - SANTIAGO DEL ESTERO
ESCALA : 1:100 - 1:200


COLEGIO DE ARQUITECTOS DE SANTIAGO DEL ESTERO
19 NOV. 2020
PROYECTO Y DIRECCION DE OBRA
SUSANA DE CASSIS
Arquitecta
Secretaria Técnica
Colegio de Arquitectos

SUP. DE TERRENO : s/t 356.80 - s/p y s/he 357.21 m²
SUP. CUBIERTA : (ver en lamina)
SUP. FUERA DE L. MUNICIPAL:
SUP. CUBIERTA TOTAL : 3094.57 m²

PROPIETARIO
DOMICILIO :
PROYECTO :
DOMICILIO :
D. TECNICA :
DOMICILIO :
ELECTRICIDAD :
DOMICILIO :
ESTRUCTURA :
DOMICILIO :
CATEGORIA COLEGIO DE ARQUITECTOS

JUAN CARLOS ALCORTA
Arquitecto
M.P. 0555

CROQUIS DE UBICACION

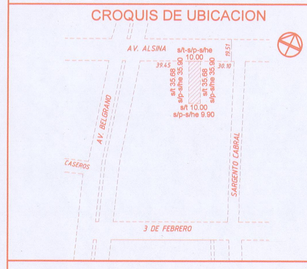

ANCHO DE CALLE : 19.51 m
ANCHO DE VEREDA : 4.10 m
ANCHO DE CALZADA : 11.10 m

PAVIMENTO :
SERVICIOS CLOACALES :

DIRECCION DE SUELO URBANO
EXPEDIENTE 10-M-21
FECHA DE SELLADO 13-08-21
63201

DESIGNACION :

PLANO GENERAL

- PLANTAS - FACHADA - CORTES - PLANIMETRIA -

OBSERVACIONES: S/D 2021
Las referencias a medidas y linderos son meramente indicativas, y la aprobación administrativa no valora los derechos que de ellos emergen.

PERMISO DE COMIENZO DE OBRA Nº 4655
DIRECCION DE SUELO URBANO

MUNICIPALIDAD DE LA CIUDAD DE SANTIAGO DEL ESTERO
SECRETARIA DE FISCALIZACION
APROBADO
DIRECCION DE SUELO URBANO
EXPEDIENTE: 10-M-21
FECHA: 27 MAYO 2022

Arq. BERNARDO J. SANTILLAN
DIRECTOR
DIRECCION DE SUELO URBANO
MUNICIPALIDAD DE CIUDAD DEL ESTERO

P/ Arq. Ma. Esther
Subsecretaria de Obras Privadas
Direccion de Suelo Urbano

Ad. Adm. MARIO J. LOPEZ
DIRECCION DE CATASTRO
MUNICIPALIDAD DE CIUDAD DEL ESTERO