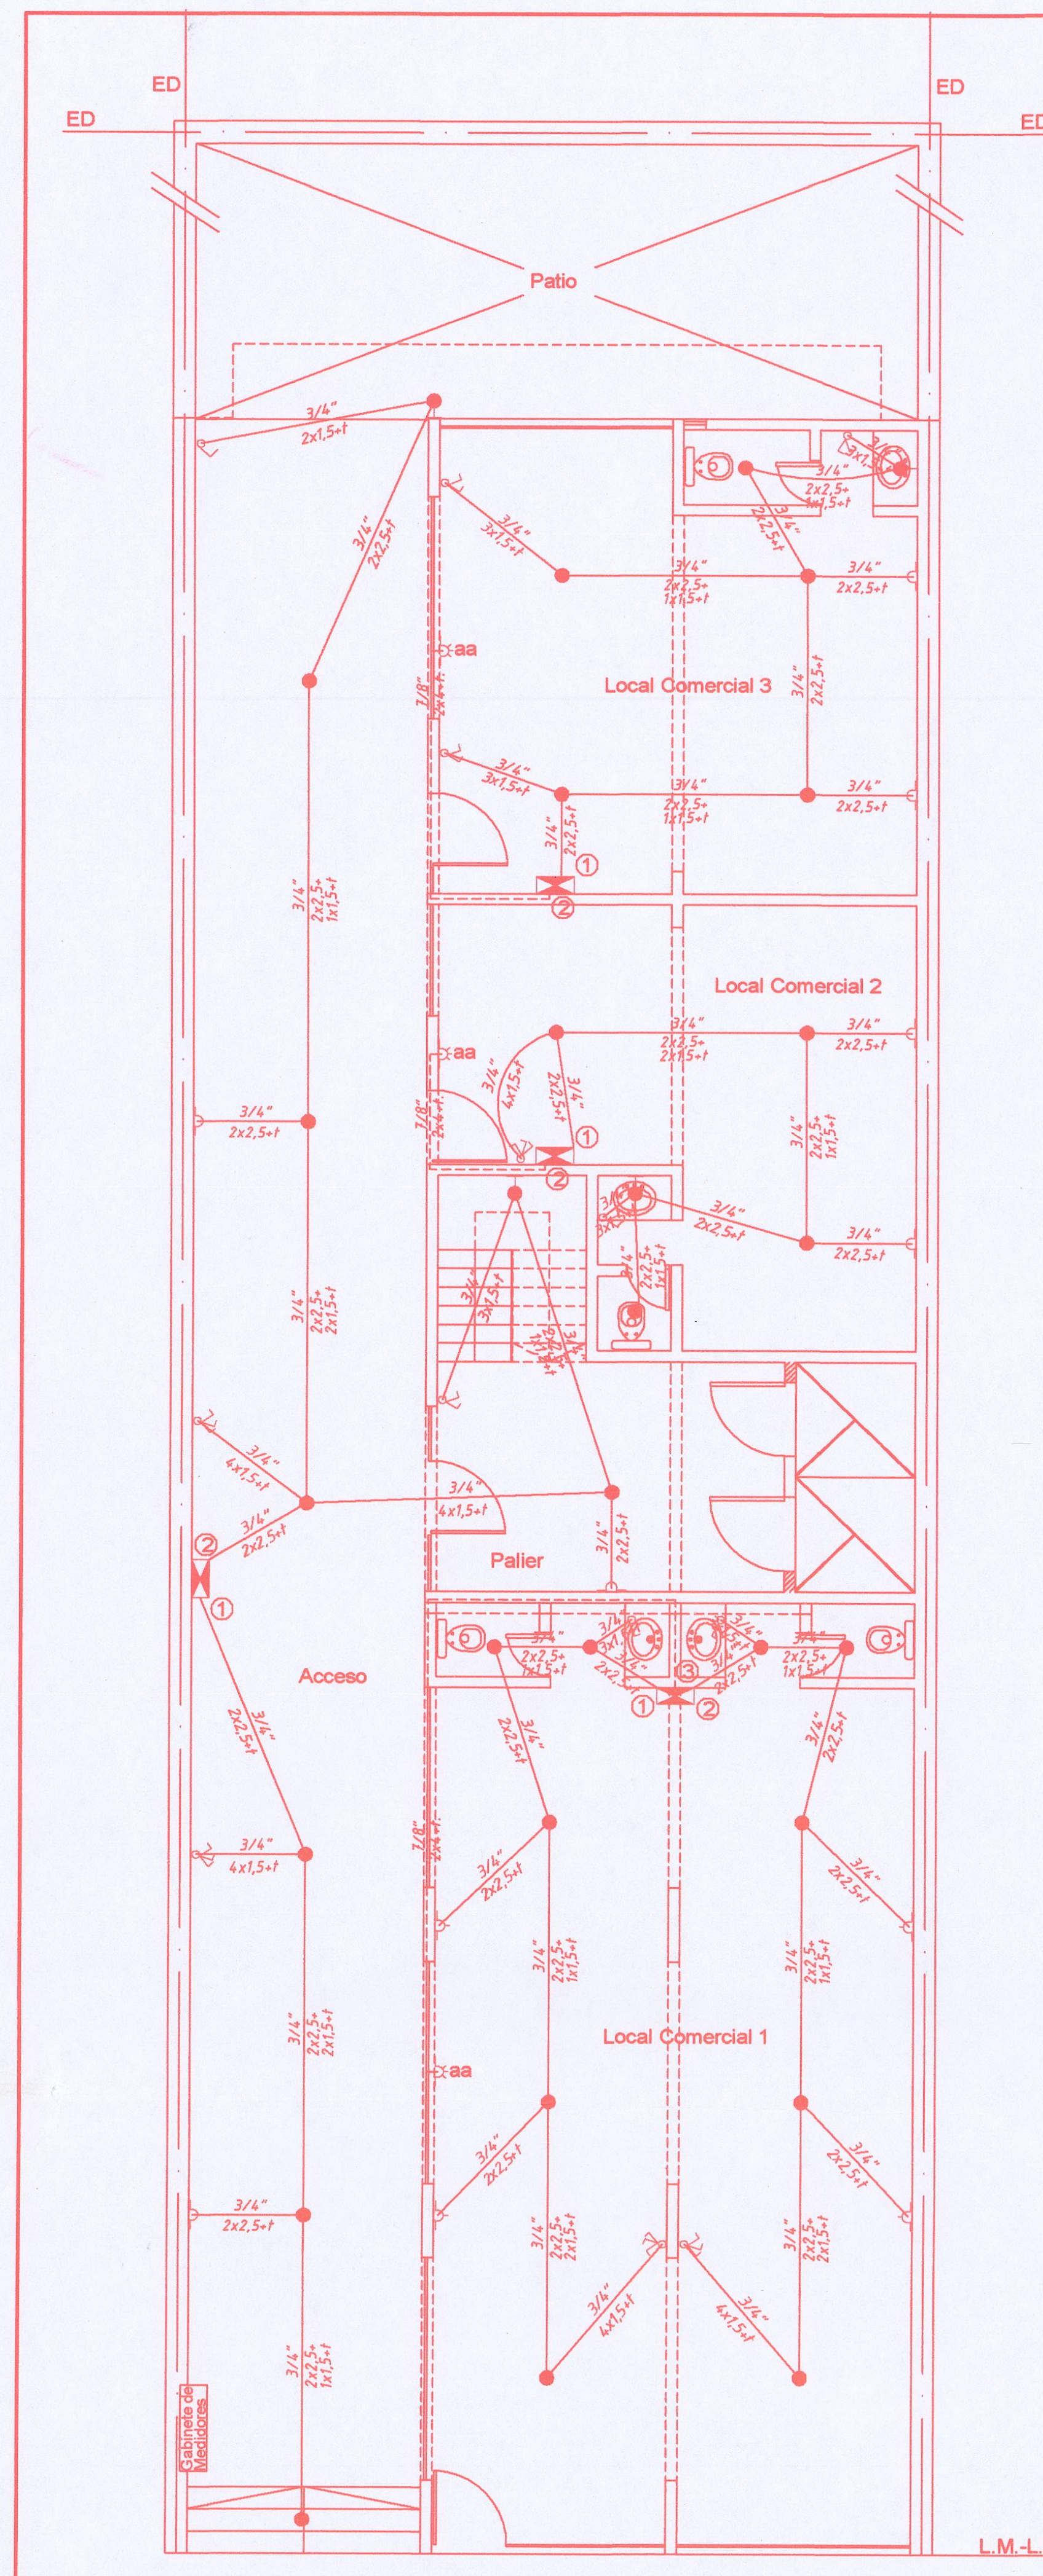
ED
Patio
Local Comercial 3
Local Comercial 2
Palier
Acceso
Local Comercial 1
3/4"
2x2,5+t
4x1,5+t
aa
L.M.-L.E.E.

PLANTA BAJA

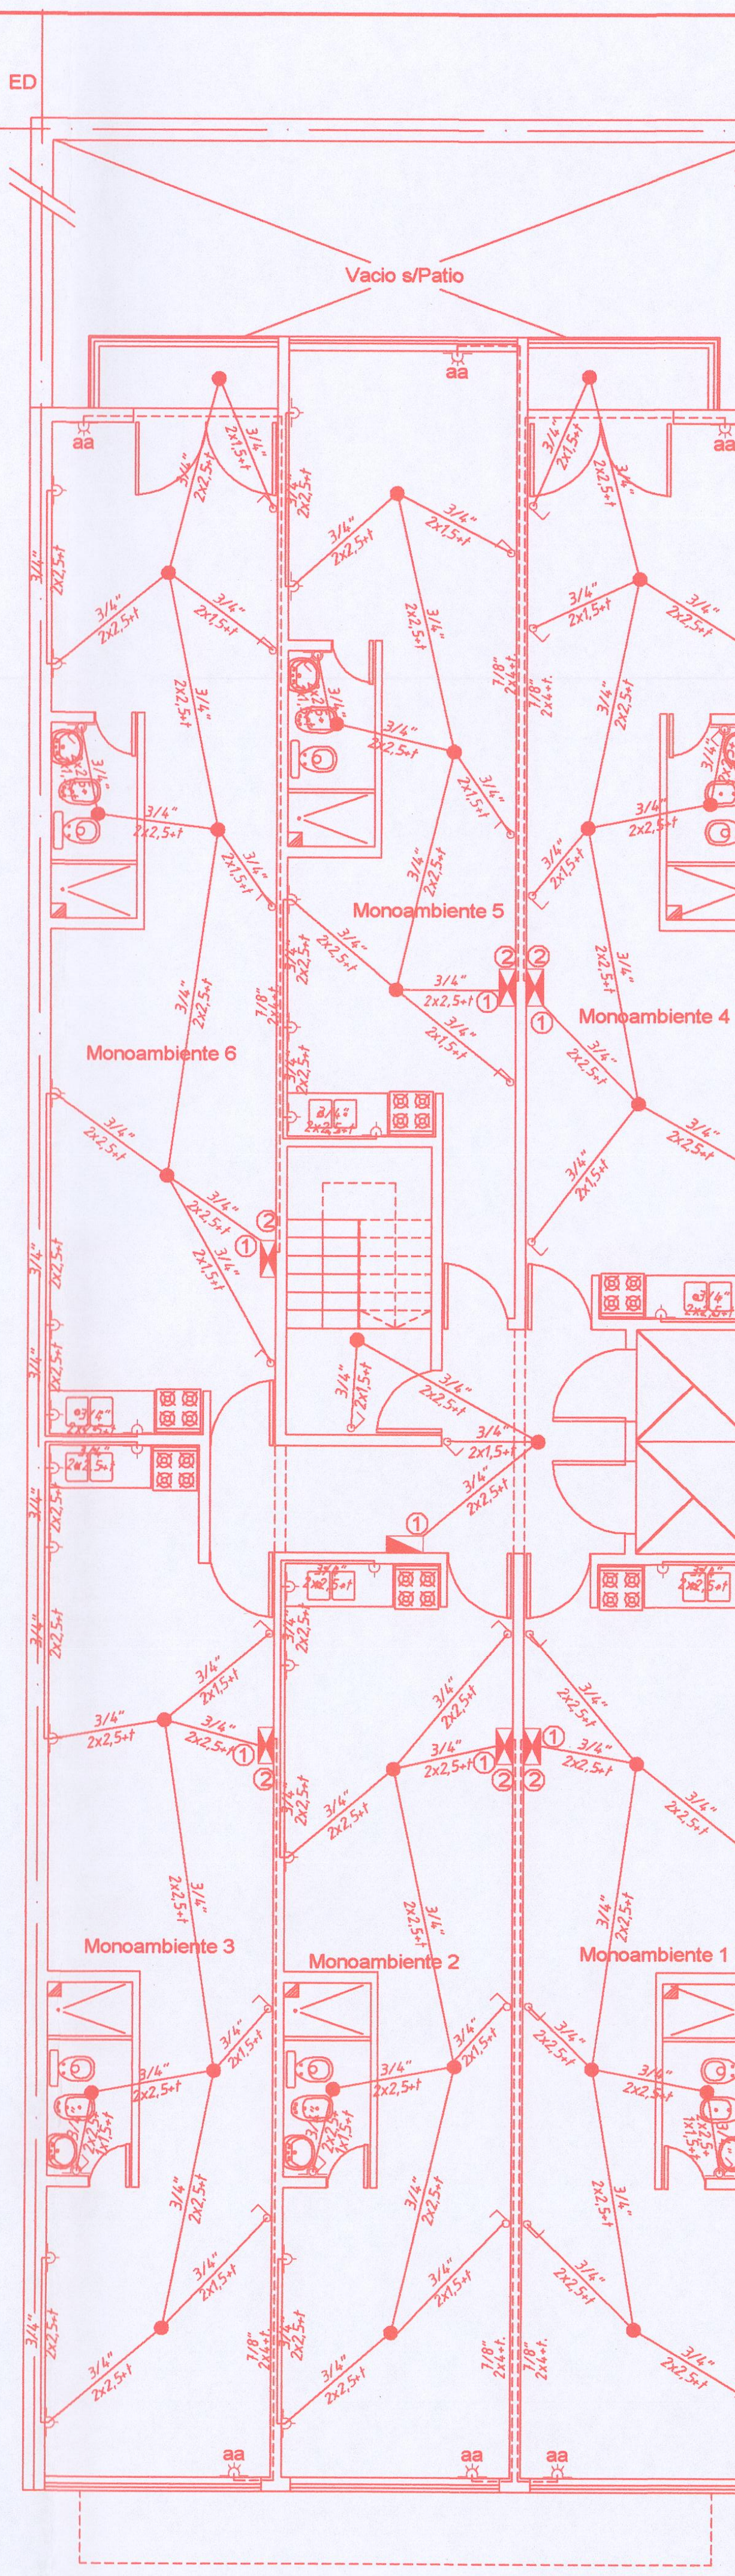
ED
Vacio s/Patio
Monoambiente 6
Monoambiente 5
Monoambiente 4
Monoambiente 3
Monoambiente 2
Monoambiente 1
3/4"
2x2,5+t
aa
L.M.-L.E.E.

PLANTA 1º PISO

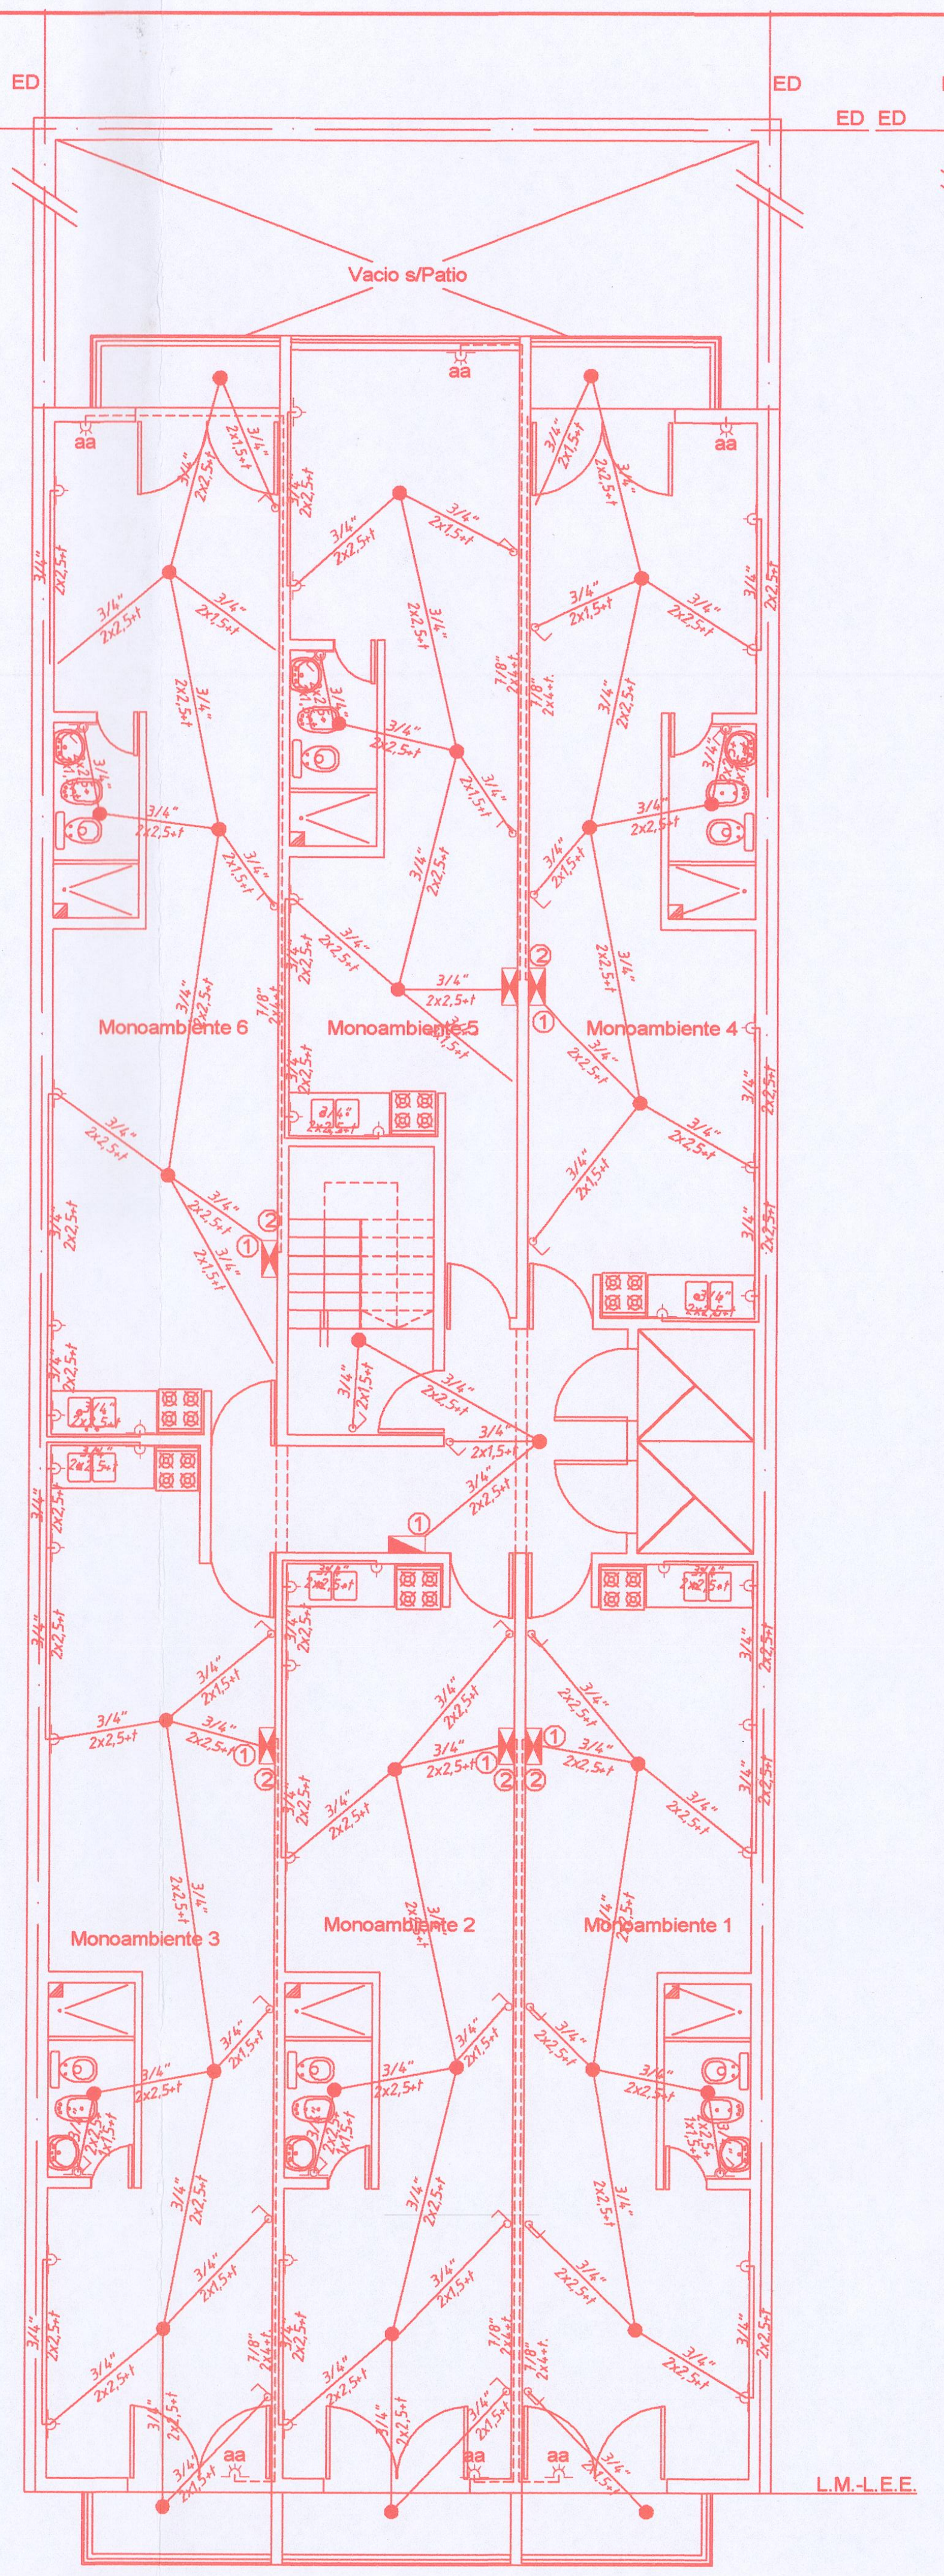
ED
Vacio s/Patio
Monoambiente 6
Monoambiente 5
Monoambiente 4
Monoambiente 3
Monoambiente 2
Monoambiente 1
3/4"
2x2,5+t
aa
L.M.-L.E.E.

PLANTA TIPO DEL 2º AL 9º PISO

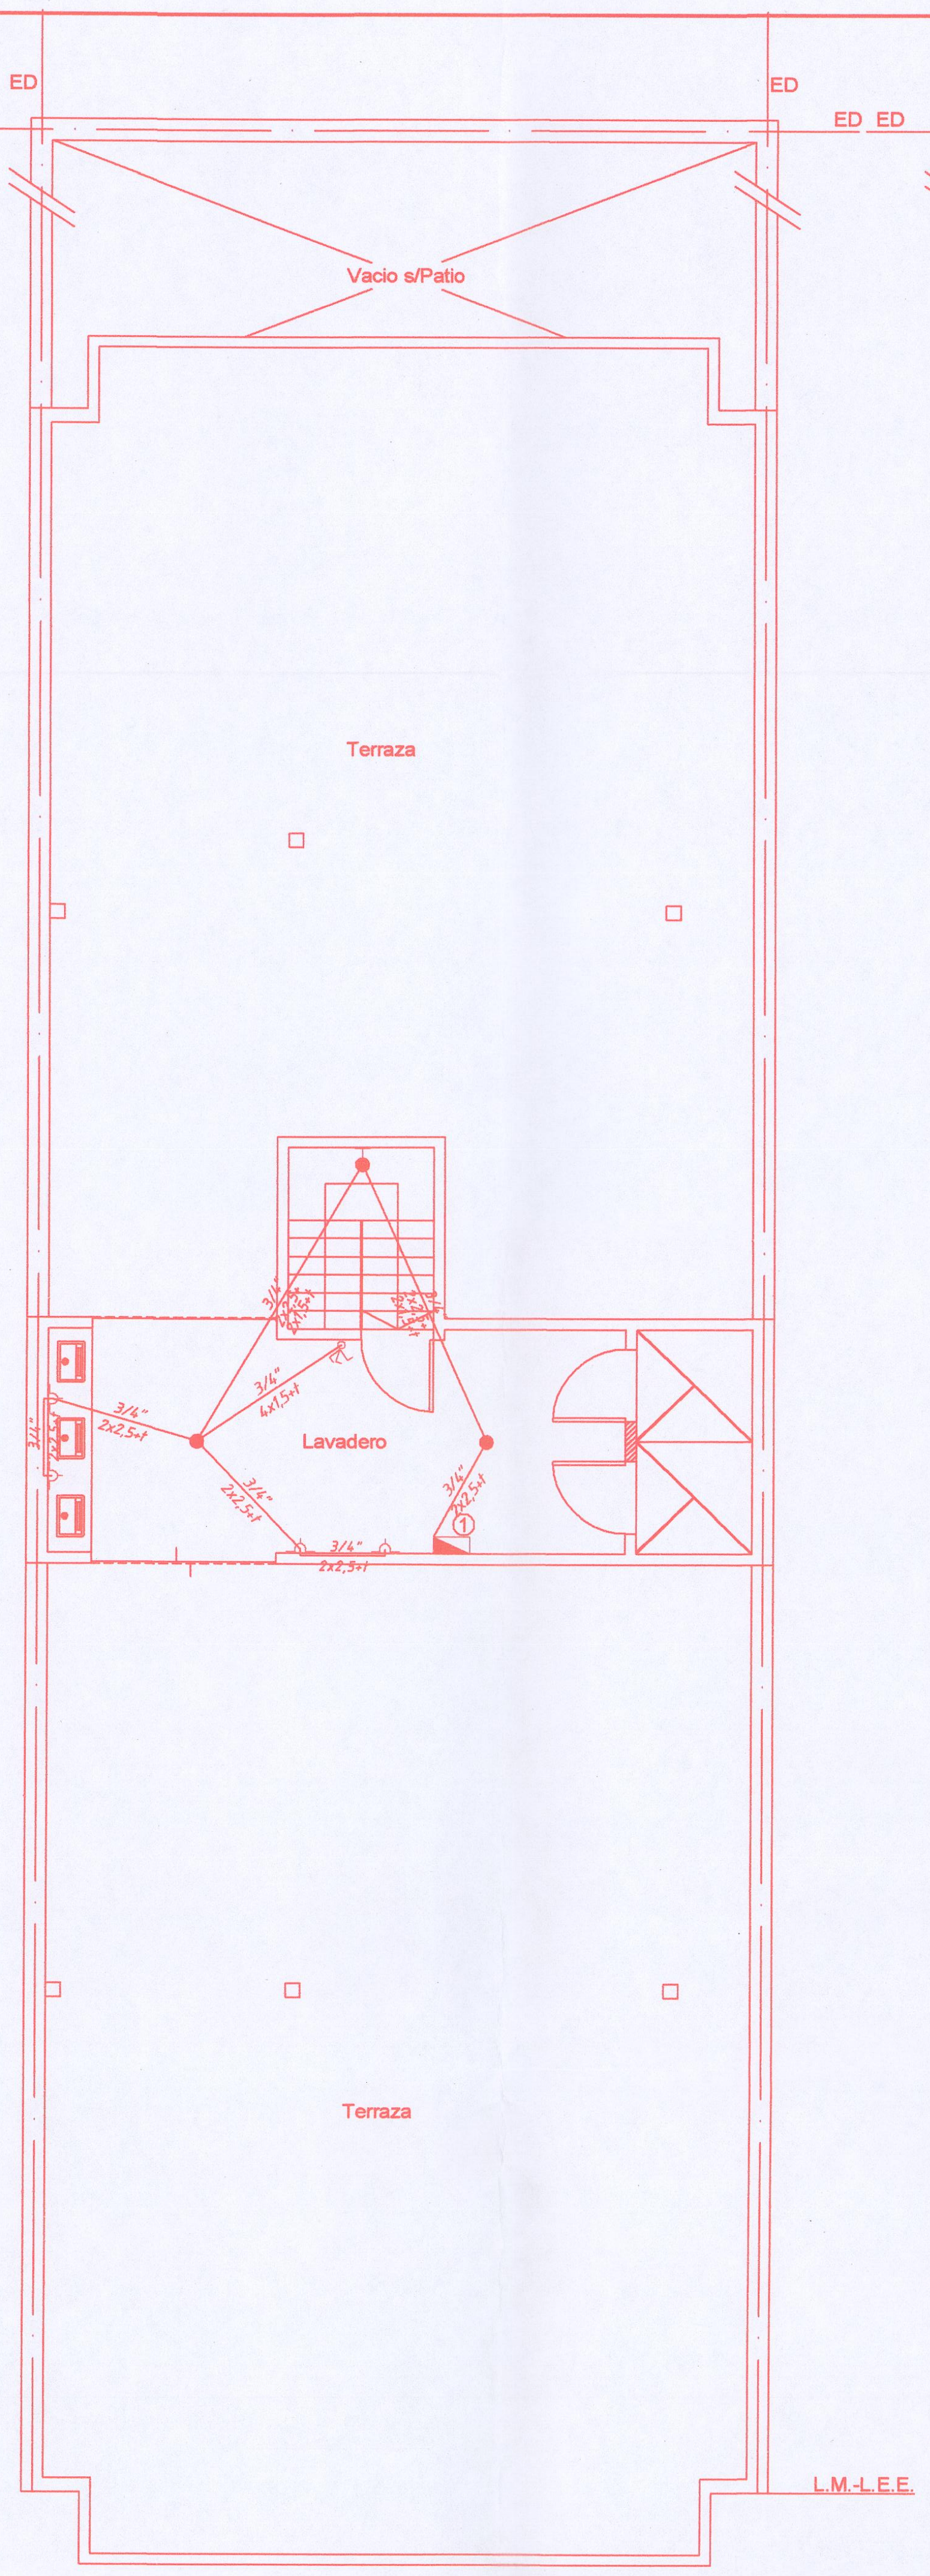
ED
Vacio s/Patio
Terraza
Lavadero
Terraza
L.M.-L.E.E.

PLANTA TERRAZA

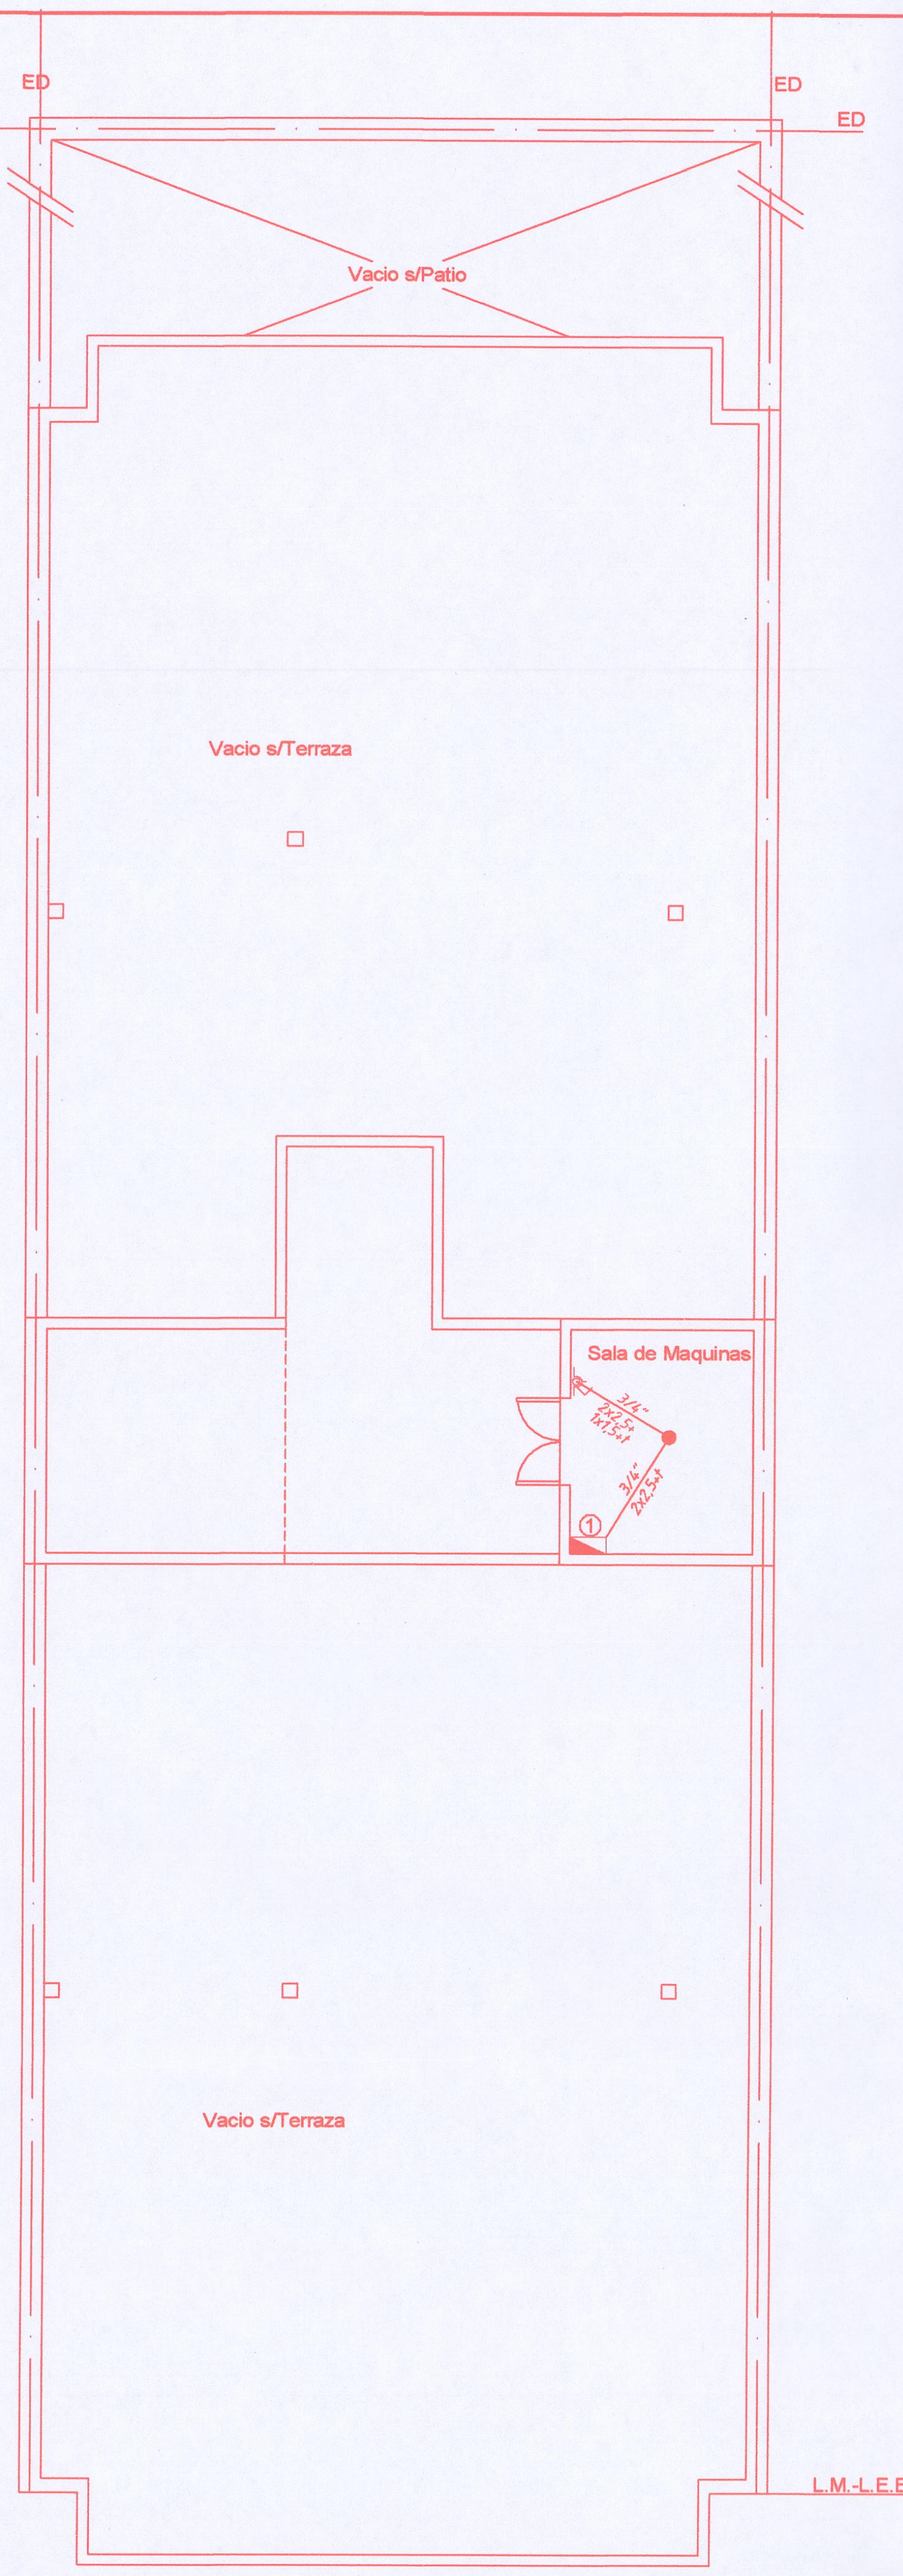
ED
Vacio s/Patio
Vacio s/Terraza
Sala de Maquinas
Vacio s/Terraza
L.M.-L.E.E.

PLANTA SALA DE MAQUINAS

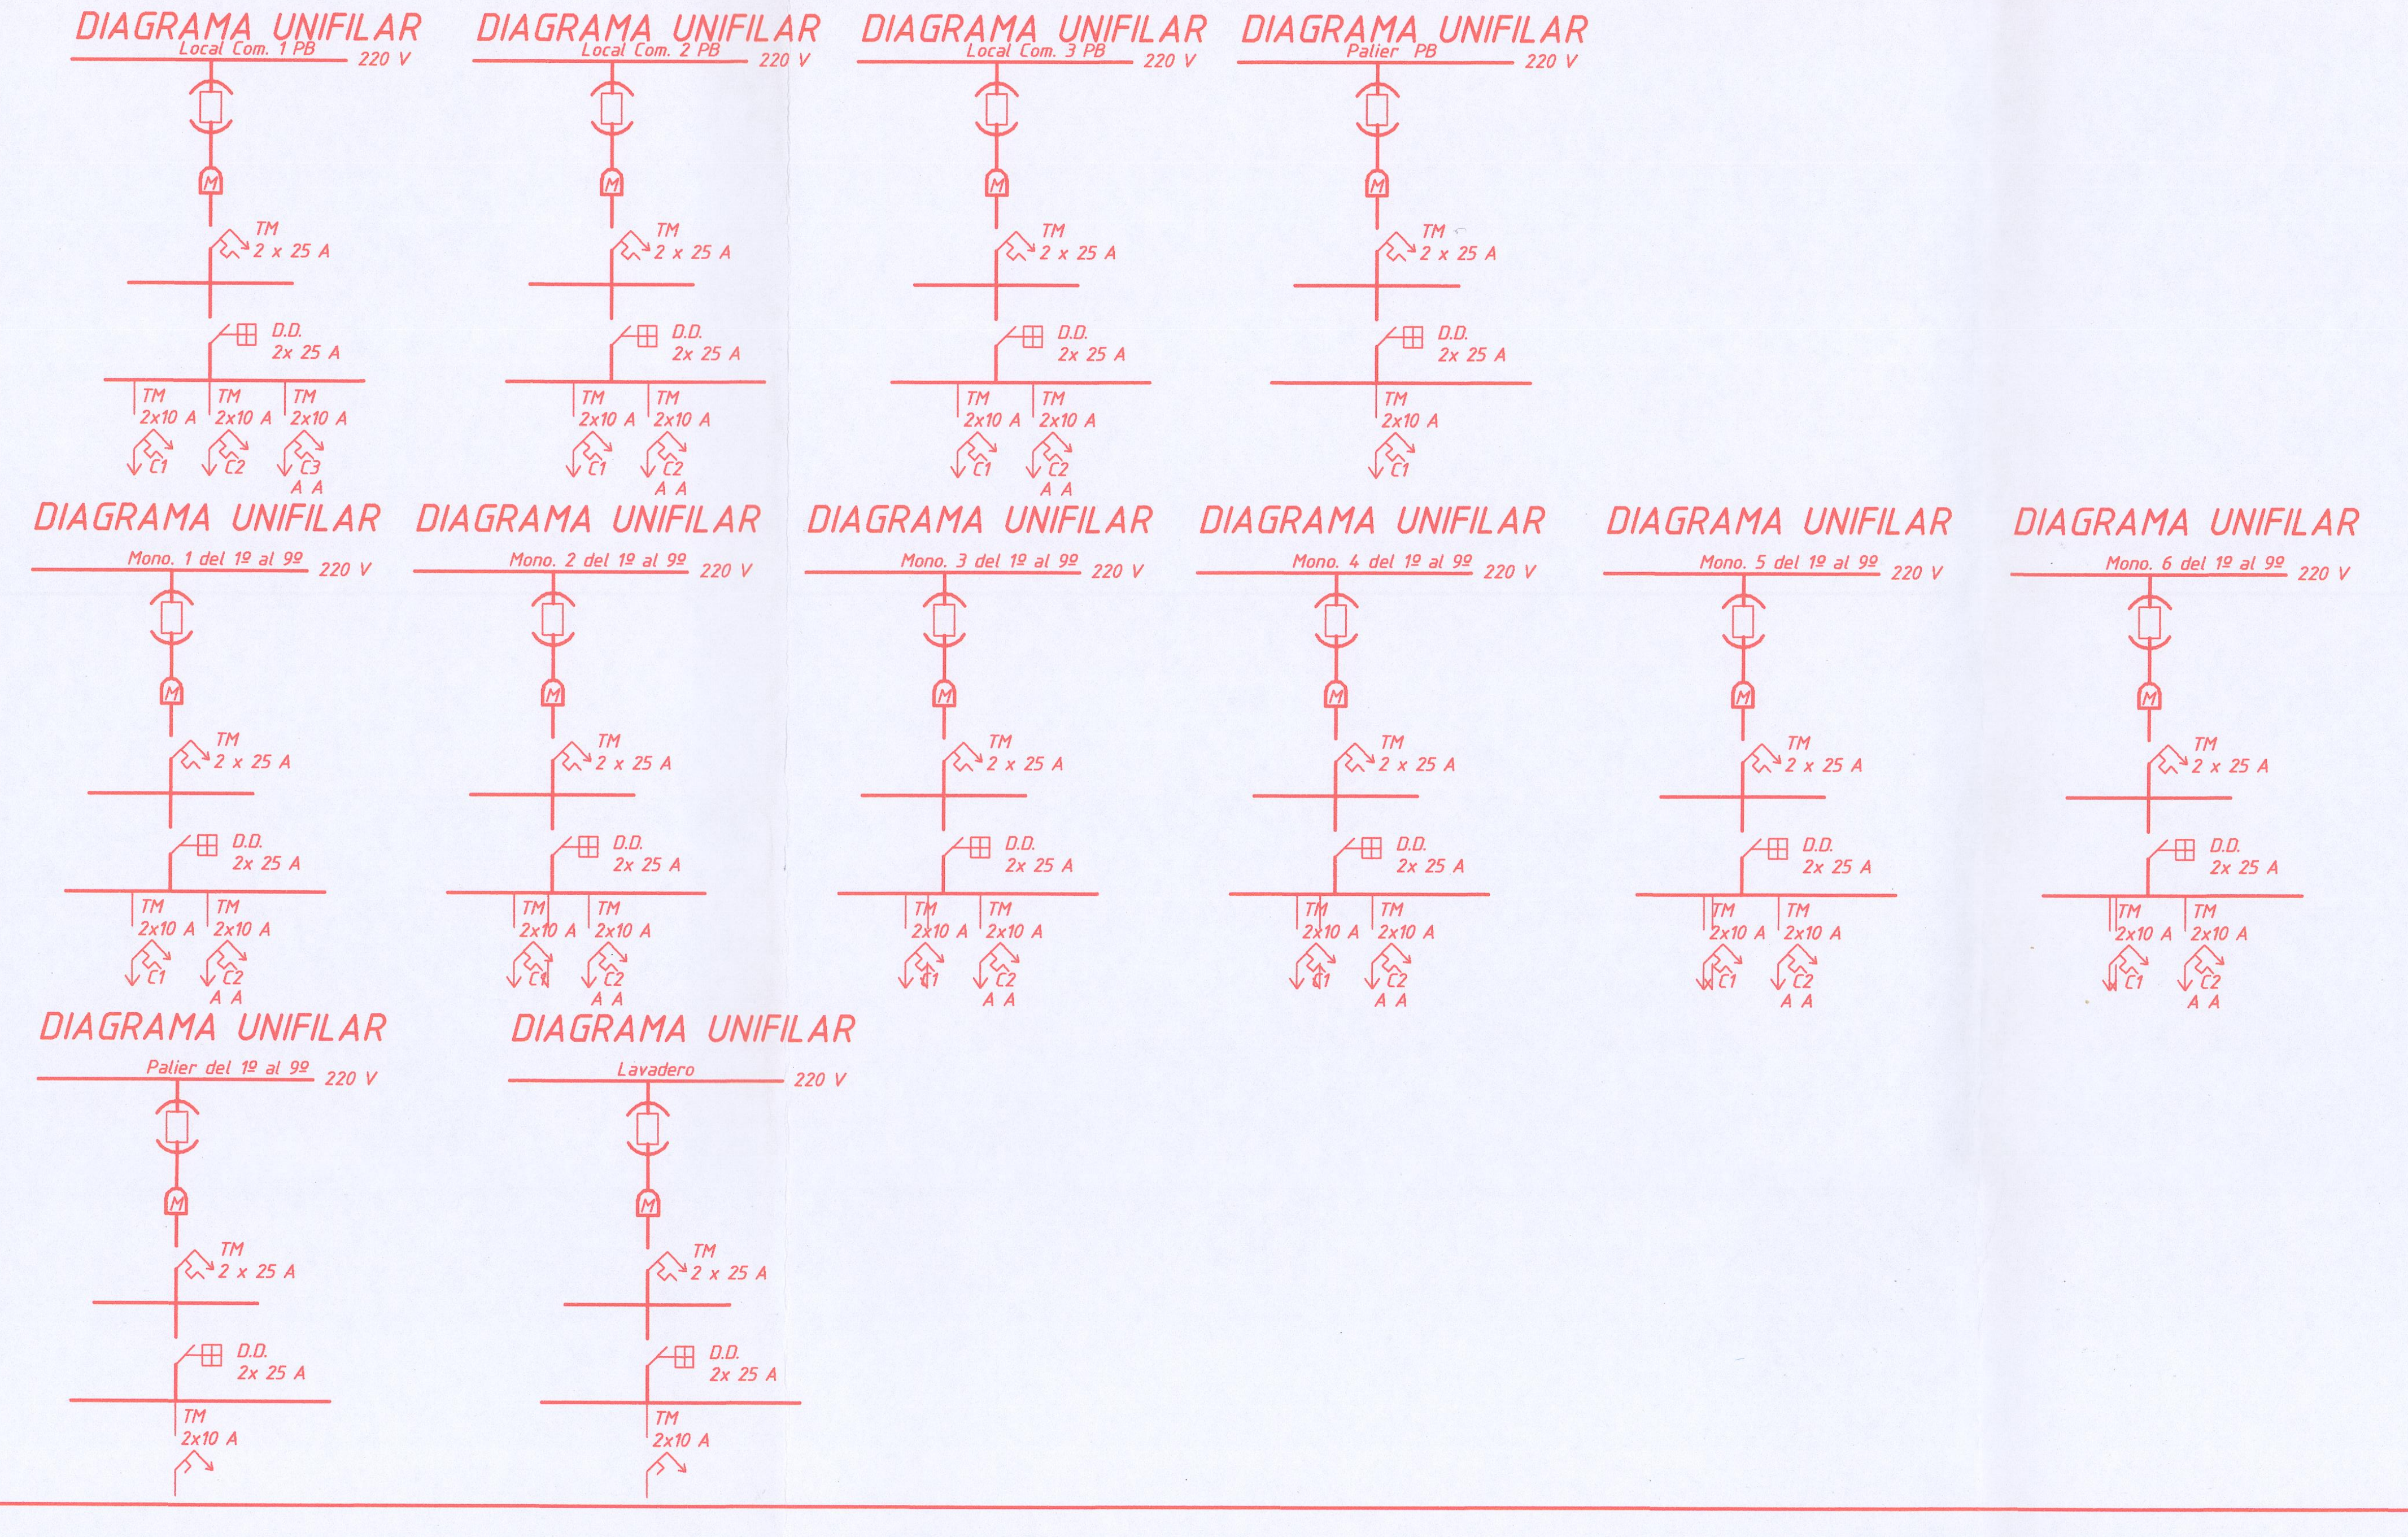
DIAGRAMA UNIFILAR
Local Com. 1 PB
220 V
DIAGRAMA UNIFILAR
Local Com. 2 PB
220 V
DIAGRAMA UNIFILAR
Local Com. 3 PB
220 V
DIAGRAMA UNIFILAR
Palier PB
220 V
DIAGRAMA UNIFILAR
Mono. 1 del 1º al 9º
220 V
DIAGRAMA UNIFILAR
Mono. 2 del 1º al 9º
220 V
DIAGRAMA UNIFILAR
Mono. 3 del 1º al 9º
220 V
DIAGRAMA UNIFILAR
Mono. 4 del 1º al 9º
220 V
DIAGRAMA UNIFILAR
Mono. 5 del 1º al 9º
220 V
DIAGRAMA UNIFILAR
Mono. 6 del 1º al 9º
220 V
DIAGRAMA UNIFILAR
Palier del 1º al 9º
220 V
DIAGRAMA UNIFILAR
Lavadero
220 V
M
TM
2 x 25 A
D.D.
2x 25 A
TM
2x10 A
C1
C2
C3
A A

REFERENCIAS ELÉCTRICAS	
M	MEDIDOR Y TOMA A TIERRA
⊠	TABLERO PRINCIPAL
◪	TABLERO SECCIONAL
● ◉	BOCA DE UNO Y DOS EFECTOS
●⊣	BOCA DE PARED
⌒	TOMA CORRIENTE
⌖	CAJA DE DISTRIBUCIÓN
♂	LLAVES, UNO,DOS y TRES PUNTOS
⌒	LINEA GENERAL
⌒	CIRCUITO DE AIRE ACONDICIONADO
♂	CAÑO DE SUBIDA Y ENTRADA DE ENERGIA
⊓	LLAVE DE COMBINACION SIMPLE

UNA FORMA DE EJECUCION DE PUESTA A TIERRA

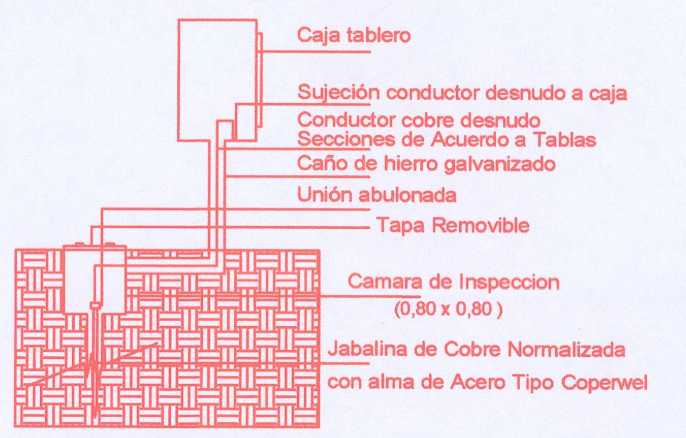
Caja tablero
Sujeción conductor desnudo a caja
Conductor cobre desnudo
Secciones de Acuerdo a Tablas
Caño de hierro galvanizado
Unión abulonada
Tapa Removible
Camara de Inspeccion
(0,80 x 0,80)
Jabalina de Cobre Normalizada
con alma de Acero Tipo Coperwel

PLANILLA DE CARGAS

Tablero		Circuito	Bocas			Potencia		Potencia Total	Corriente	Portección Termomag-nética	Disyuntor Diferencial
			Luz	Tomas		Luz	Tomas				
			20 w	200 w	500 w			(W)	(A)		
T.P. Planta Baja	Palier	1	3	1	—	60	200	260	1.18	2 x 10 A	2 x 25 A
		2	6	2	—	120	400	520	2.36	2 x 10 A	
	Local 1	1	5	2	—	100	400	500	2.27	2 x 10 A	2 x 25 A
		2	5	2	—	100	400	500	2.27	2 x 10 A	
		3	—	—	1	—	500	500	2.27	2 x 10 A	
	Local 2	1	4	2	—	80	400	480	2.17	2 x 10 A	2 x 25 A
		2	—	—	1	—	500	500	2.27	2 x 10 A	
	Local 3	1	6	2	—	120	400	520	2.36	2 x 10 A	2 x 25 A
		2	—	[illegible]	1	—	500	500	2.27	2 x 10 A	
T.S. 1ºP.	Palier	1	2	—	—	40	—	40	2.83	2 x 10 A	2 x 25 A
T.P. 1ºP.	Mono. 1	1	3	7	—	60	1400	1460	6.62	2 x 10 A	2 x 25 A
		2	—	—	1	—	500	500	2.27	2 x 10 A	
	Mono. 2	1	3	7	—	60	1400	1460	6.62	2 x 10 A	2 x 25 A
		2	—	—	1	—	500	500	2.27	2 x 10 A	
	Mono. 3	1	3	7	—	60	1400	1460	6.62	2 x 10 A	2 x 25 A
		2	—	—	1	—	500	500	2.27	2 x 10 A	
	Mono. 4	1	4	7	—	80	1400	1480	6.62	2 x 10 A	2 x 25 A
		2	—	—	1	—	500	500	2.27	2 x 10 A	
	Mono. 5	1	3	7	—	60	1400	1460	6.62	2 x 10 A	2 x 25 A
		2	—	—	1	—	500	500	2.27	2 x 10 A	
	Mono. 6	1	4	7	—	80	1400	1480	6.71	2 x 10 A	2 x 25 A
		2	—	—	1	—	500	500	2.27	2 x 10 A	
T.S. 2ºP.	Palier	1	2	—	—	40	—	40	0.18	2 x 10 A	2 x 25 A
T.P. 2ºP.	Mono. 1	1	4	7	—	80	1400	1480	6.71	2 x 10 A	2 x 25 A
		2	—	—	1	—	500	500	2.27	2 x 10 A	
	Mono. 2	1	4	7	—	80	1400	1480	6.71	2 x 10 A	2 x 25 A
		2	—	—	1	—	500	500	2.27	2 x 10 A	
	Mono. 3	1	4	7	—	80	1400	1480	6.71	2 x 10 A	2 x 25 A
		2	—	—	1	—	500	500	2.27	2 x 10 A	
	Mono. 4	1	4	7	—	80	1400	1480	6.71	2 x 10 A	2 x 25 A
		2	—	—	1	—	500	500	2.27	2 x 10 A	
	Mono. 5	1	3	7	—	60	1400	1460	6.62	2 x 10 A	2 x 25 A
		2	—	—	1	—	500	500	2.27	2 x 10 A	
	Mono. 6	1	4	7	—	80	1400	1480	6.71	2 x 10 A	2 x 25 A
		2	—	—	1	—	500	500	2.27	2 x 10 A	
T.S. 3ºP.	Palier	1	2	—	—	40	—	40	0.18	2 x 10 A	2 x 25 A
T.P. 3ºP.	Mono. 1	1	4	7	—	80	1400	1480	6.71	2 x 10 A	2 x 25 A
		2	—	—	1	—	500	500	2.27	2 x 10 A	
	Mono. 2	1	4	7	—	80	1400	1480	6.71	2 x 10 A	2 x 25 A
		2	—	—	1	—	500	500	2.27	2 x 10 A	
	Mono. 3	1	4	7	—	80	1400	1480	6.71	2 x 10 A	2 x 25 A
		2	—	—	1	—	500	500	2.27	2 x 10 A	
	Mono. 4	1	4	7	—	80	1400	1480	6.71	2 x 10 A	2 x 25 A
		2	—	—	1	—	500	500	2.27	2 x 10 A	
	Mono. 5	1	3	7	—	60	1400	1460	6.62	2 x 10 A	2 x 25 A
		2	—	—	1	—	500	500	2.27	2 x 10 A	
	Mono. 6	1	4	7	—	80	1400	1480	6.71	2 x 10 A	2 x 25 A
		2	—	—	1	—	500	500	2.27	2 x 10 A	
T.S. 4ºP.	Palier	1	2	—	—	40	—	40	0.18	2 x 10 A	2 x 25 A
T.P. 4ºP.	Mono. 1	1	4	7	—	80	1400	1480	6.71	2 x 10 A	2 x 25 A
		2	—	—	1	—	500	500	2.27	2 x 10 A	
	Mono. 2	1	4	7	—	80	1400	1480	6.71	2 x 10 A	2 x 25 A
		2	—	—	1	—	500	500	2.27	2 x 10 A	
	Mono. 3	1	4	7	—	80	1400	1480	6.71	2 x 10 A	2 x 25 A
		2	—	—	1	—	500	500	2.27	2 x 10 A	
	Mono. 4	1	4	7	—	80	1400	1480	6.71	2 x 10 A	2 x 25 A
		2	—	—	1	—	500	500	2.27	2 x 10 A	
	Mono. 5	1	3	7	—	60	1400	1460	6.62	2 x 10 A	2 x 25 A
		2	—	—	1	—	500	500	2.27	2 x 10 A	
	Mono. 6	1	4	7	—	80	1400	1480	6.71	2 x 10 A	2 x 25 A
		2	—	—	1	—	500	500	2.27	2 x 10 A	
T.S. 5ºP.	Palier	1	2	—	—	40	—	40	0.18	2 x 10 A	2 x 25 A
T.P. 5ºP.	Mono. 1	1	4	7	—	80	1400	1480	6.71	2 x 10 A	2 x 25 A
		2	—	—	1	—	500	500	2.27	2 x 10 A	
	Mono. 2	1	4	7	—	80	1400	1480	6.71	2 x 10 A	2 x 25 A
		2	—	—	1	—	500	500	2.27	2 x 10 A	
	Mono. 3	1	4	7	—	80	1400	1480	6.71	2 x 10 A	2 x 25 A
		2	—	—	1	—	500	500	2.27	2 x 10 A	
	Mono. 4	1	4	7	—	80	1400	1480	6.71	2 x 10 A	2 x 25 A
		2	—	—	1	—	500	500	2.27	2 x 10 A	
	Mono. 5	1	3	7	—	60	1400	1460	6.62	2 x 10 A	2 x 25 A
		2	—	—	1	—	500	500	2.27	2 x 10 A	
	Mono. 6	1	4	7	—	80	1400	1480	6.71	2 x 10 A	2 x 25 A
		2	—	—	1	—	500	500	2.27	2 x 10 A	

PLANILLA DE CARGAS

Tablero		Circuito	Bocas			Potencia		Potencia Total	Corriente	Portección Termomag-nética	Disyuntor Diferencial
			Luz	Tomas		Luz	Tomas				
			20 w	200 w	500 w			(W)	(A)		
T.S. 6ºP.	Palier	1	2	—	—	40	—	40	0.18	2 x 10 A	2 x 25 A
T.P. 6ºP.	Mono. 1	1	3	7	—	60	1400	1460	6.71	2 x 10 A	2 x 25 A
		2	—	—	1	—	500	500	2.27	2 x 10 A	
	Mono. 2	1	3	7	—	60	1400	1460	6.71	2 x 10 A	2 x 25 A
		2	—	—	1	—	500	500	2.27	2 x 10 A	
	Mono. 3	1	3	7	—	60	1400	1460	6.71	2 x 10 A	2 x 25 A
		2	—	—	1	—	500	500	2.27	2 x 10 A	
	Mono. 4	1	4	7	—	80	1400	1480	6.71	2 x 10 A	2 x 25 A
		2	—	—	1	—	500	500	2.27	2 x 10 A	
	Mono. 5	1	3	7	—	60	1400	1460	6.71	2 x 10 A	2 x 25 A
		2	—	—	1	—	500	500	2.27	2 x 10 A	
	Mono. 6	1	4	7	—	80	1400	1480	6.71	2 x 10 A	2 x 25 A
		2	—	—	1	—	500	500	2.27	2 x 10 A	
T.S. 7ºP.	Palier	1	2	—	—	40	—	40	0.18	2 x 10 A	2 x 25 A
T.P. 7ºP.	Mono. 1	1	4	7	—	80	1400	1480	6.71	2 x 10 A	2 x 25 A
		2	—	—	1	—	500	500	2.27	2 x 10 A	
	Mono. 2	1	4	7	—	80	1400	1480	6.71	2 x 10 A	2 x 25 A
		2	—	—	1	—	500	500	2.27	2 x 10 A	
	Mono. 3	1	4	7	—	80	1400	1480	6.71	2 x 10 A	2 x 25 A
		2	—	—	1	—	500	500	2.27	2 x 10 A	
	Mono. 4	1	4	7	—	80	1400	1480	6.71	2 x 10 A	2 x 25 A
		2	—	—	1	—	500	500	2.27	2 x 10 A	
	Mono. 5	1	3	7	—	60	1400	1460	6.71	2 x 10 A	2 x 25 A
		2	—	—	1	—	500	500	2.27	2 x 10 A	
	Mono. 6	1	4	7	—	80	1400	1480	6.71	2 x 10 A	2 x 25 A
		2	—	—	1	—	500	500	2.27	2 x 10 A	
T.S. 8ºP.	Palier	1	2	—	—	40	—	40	0.18	2 x 10 A	2 x 25 A
T.P. 8ºP.	Mono. 1	1	4	7	—	80	1400	1480	6.71	2 x 10 A	2 x 25 A
		2	—	—	1	—	500	500	2.27	2 x 10 A	
	Mono. 2	1	4	7	—	80	1400	1480	6.71	2 x 10 A	2 x 25 A
		2	—	—	1	—	500	500	2.27	2 x 10 A	
	Mono. 3	1	4	7	—	80	1400	1480	6.71	2 x 10 A	2 x 25 A
		2	—	—	1	—	500	500	2.27	2 x 10 A	
	Mono. 4	1	4	7	—	80	1400	1480	6.71	2 x 10 A	2 x 25 A
		2	—	—	1	—	500	500	2.27	2 x 10 A	
	Mono. 5	1	3	7	—	60	1400	1460	6.71	2 x 10 A	2 x 25 A
		2	—	—	1	—	500	500	2.27	2 x 10 A	
	Mono. 6	1	4	7	—	80	1400	1480	6.71	2 x 10 A	2 x 25 A
		2	—	—	1	—	500	500	2.27	2 x 10 A	
T.S. 9ºP.	Palier	1	2	—	—	40	—	40	0.18	2 x 10 A	2 x 25 A
T.P. 9ºP.	Mono. 1	1	4	7	—	80	1400	1480	6.71	2 x 10 A	2 x 25 A
		2	—	—	1	—	500	500	2.27	2 x 10 A	
	Mono. 2	1	4	7	—	80	1400	1480	6.71	2 x 10 A	2 x 25 A
		2	—	—	1	—	500	500	2.27	2 x 10 A	
	Mono. 3	1	4	7	—	80	1400	1480	6.71	2 x 10 A	2 x 25 A
		2	—	—	1	—	500	500	2.27	2 x 10 A	
	Mono. 4	1	4	7	—	80	1400	1480	6.71	2 x 10 A	2 x 25 A
		2	—	—	1	—	500	500	2.27	2 x 10 A	
	Mono. 5	1	3	7	—	60	1400	1460	6.71	2 x 10 A	2 x 25 A
		2	—	—	1	—	500	500	2.27	2 x 10 A	
	Mono. 6	1	4	7	—	80	1400	1480	6.71	2 x 10 A	2 x 25 A
		2	—	—	1	—	500	500	2.27	2 x 10 A	
T.S. Ter.	Lavad.	1	3	4	—	60	800	860	3.90	2 x 10 A	2 x 25 A
							Potencia Total	112220			
							Fac. de Simultaneidad 60%	67332			

DIST.: 02 ZONA: 04 MANZ.: 18 PARC.: 250
PADRON INMOB.: 01-01-8871 ICM: 530-M-21 DOMINIO: 7S-34099

LEY 4683

182591'

LEY 5654/87

16 NOV. 2020

PROYECTO Y
DIRECCION DE OBRA
SUSANA ABECASSIS
Arquitecta
Secretaria Técnica Adjunta
Colegio de Arquitectos S D E

DEST. DE LA OBRA : LOCALES COMERCIALES (3) Y MONOAMBIENTES (54)
PROPIETARIO : **MOSSO NORBERTO MARCELO**
DNI : 11.864.911 CUIL : 20-11964911-8
PROPIETARIO : **ALCORTA CESAR MARCELO**
DNI : 16.802.666 CUIL : 20-16802666-9
PROPIETARIO : **ALCORTA JUAN CARLOS**
DNI : 16.771.297 CUIL : 20-16771297-6
UBICACION : AVENIDA ALSINA (O) Nº 478
BARRIO : BELGRANO
CIUDAD : CAPITAL - SANTIAGO DEL ESTERO
ESCALA : 1:100 - 1:200

SUP. DE TERRENO : s/t 356.80 - s/p y s/he 357.21 m²
SUP. CUBIERTA : (ver en lamina)
SUP. FUERA DE L. MUNICIPAL:
SUP. CUBIERTA TOTAL : 3094.57 m²

CROQUIS DE UBICACION

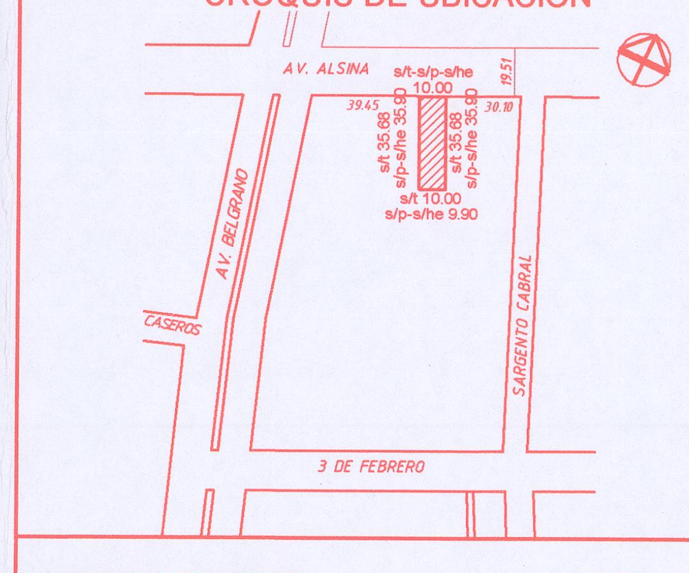
AV. ALSINA
s/t-s/p-s/he
10.00
19.51
39.45
30.10
s/t 35.68
s/p-s/he 35.90
s/t 35.68
s/p-s/he 35.90
s/t 10.00
s/p-s/he 9.90
AV. BELGRANO
CASEROS
SARGENTO CABRAL
3 DE FEBRERO

PROPIETARIO :
DOMICILIO :
PROYECTO :
DOMICILIO :
D. TECNICA :
DOMICILIO :
ELECTRICIDAD :
DOMICILIO :
ESTRUCTURA :
DOMICILIO :

JUAN CARLOS ALCORTA
Arquitecto
M.P. 0220

CATEGORIA COLEGIO DE ARQUITECTOS

DIRECCION DE SUELO URBANO
EXPEDIENTE 10 / M / 2021
FECHA DE SELLADO 17 / 07 / 21
BOLETA Nº 63201 ③

ANCHO DE CALLE : 19.51 m
ANCHO DE VEREDA : 4.10 m
ANCHO DE CALZADA : 11.10 m

PAVIMENTO :
SERVICIOS CLOACALES :

DESIGNACION :

PLANO GENERAL

- ELECTRICIDAD -

OBSERVACIONES:

30 SEP 2021

Las referencias al Título de Dominio son meramente indicativas, y la aprobación administrativa no valora los derechos que de ellos emergen.

PERMISO DE COMIENZO DE OBRA Nº 4693
DIRECCION DE SUELO URBANO

MUNICIPALIDAD DE LA CIUDAD DE SANTIAGO DEL ESTERO
SECRETARIA DE ECONOMIA
APROBADO
DIRECCIÓN DE SUELO URBANO
EXPEDIENTE: 10 – M – 21
FECHA: 27 MAYO 2022

Ing. Agrim. MARIO J. LOPEZ
DIRECCION DE CATASTRO
MUNICIPALIDAD DE SGO. DEL ESTERO

Arq. Bravo, Ma. Esther
Dpto. OBRAS PRIVADAS
DIRECCION DE SUELO URBANO

Arq. BERNARDO SANTILLAN
DIRECTOR
DIRECCION DE SUELO URBANO
MUNICIPALIDAD DE SGO. DEL ESTERO