


SIG.	DESIGNACIONES
	CAJA DERIV. 20 X 20 TV.
	CAJA DERIV. 20 X 20 TE.
	CAJA DERIV. 20 X 20 PE.
	COND. COAXIAL 75 OHMS
	CONDUCTOR 2 PARES EXT.
	CONDUCTOR 2 PARES EXT.
	TOMA EMB. HEMBRA TV.
	TOMA EMB. TE RJ 11.
	PULSADOR
	PORTERO CON SONIDO.
	FRENTE P.E.M.U. TIPLE.
	DERIVACION HACIA ARRIBA
	DERIVACION DESDE ABAJO

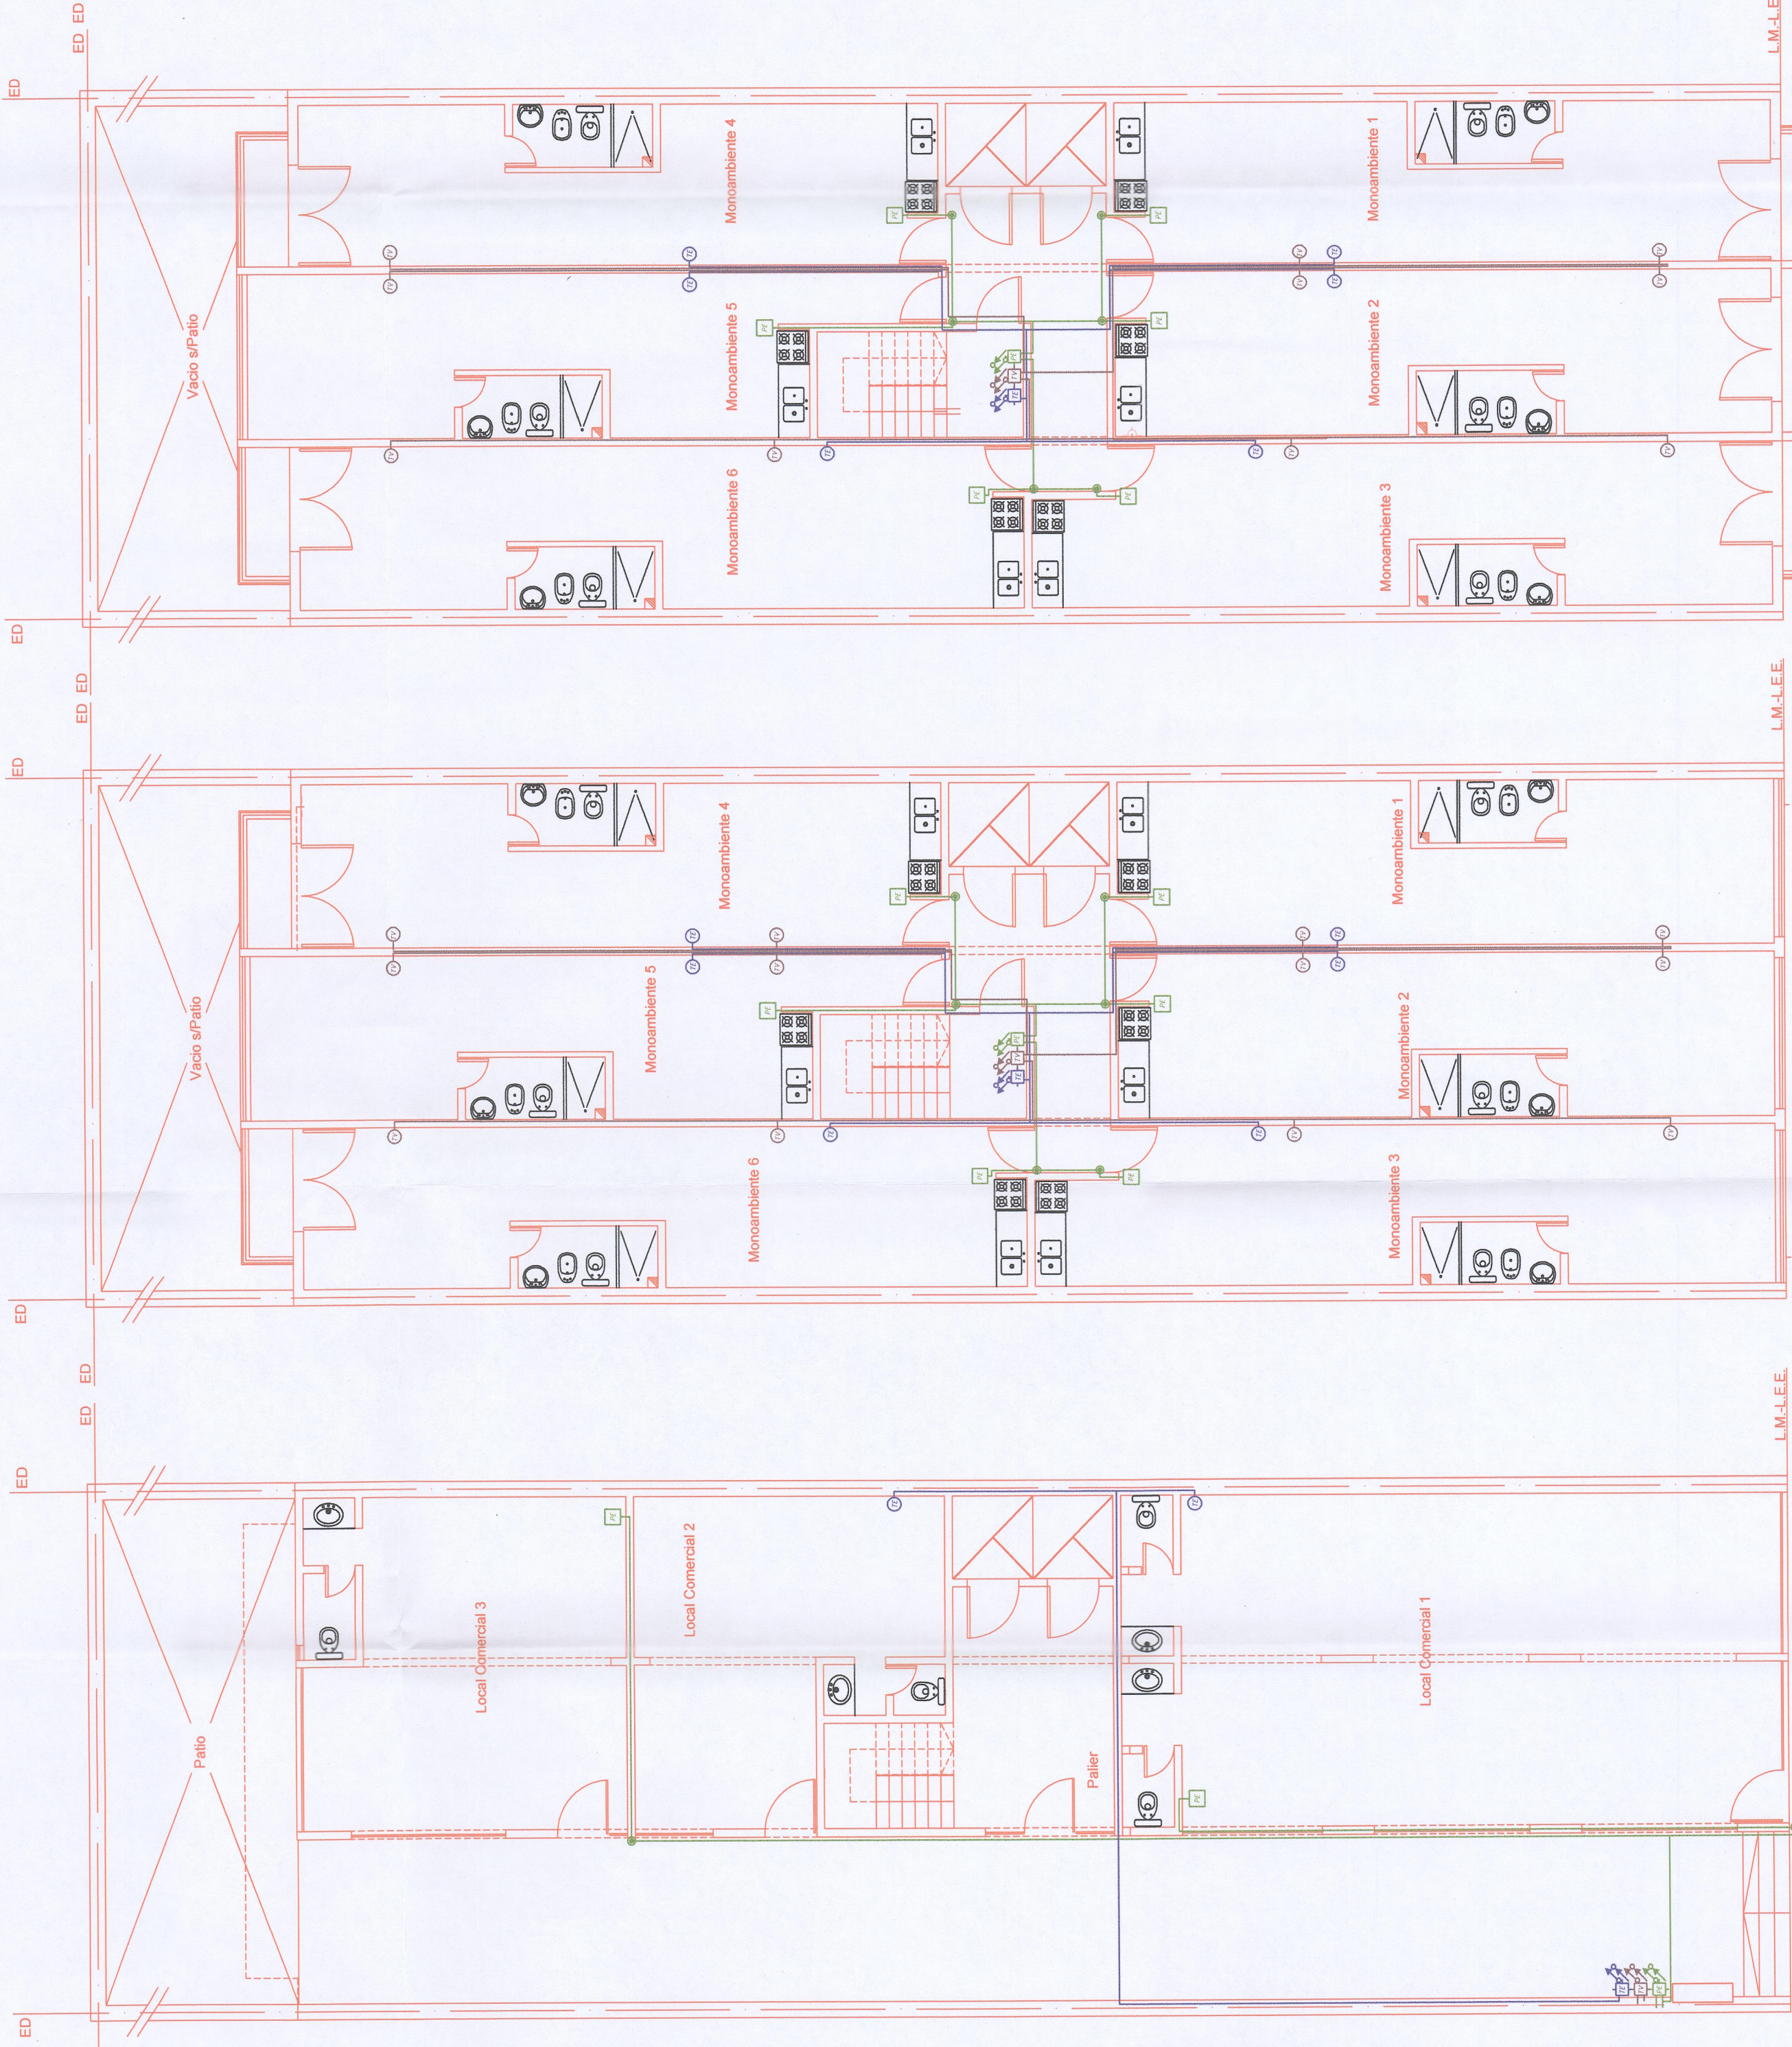

PLANTA TIPO DEL 2º AL 9º PISO

PROYECTO Y
DIRECCION DE OBRAS
01 JUN, 2022
Sra. Eva Luc Navarro
SECRETARIA TECNICA
CONSEJO DE ARQUITECTOS S.D.E.

CROQUIS DE UBICACION


PROYECTO :

DOMICILIO :

AD :
RA :
JUAN CARLOS ALCORTA
Argenteo
M. 0220

	PAVIMENTO :
ANCHO DE CALLE :	19.51 m
ANCHO DE VEREDA :	4.10 m
ANCHO DE CALZADA :	11.10 m
	SERVICIOS CLOACALES :

OBSERVACIONES:

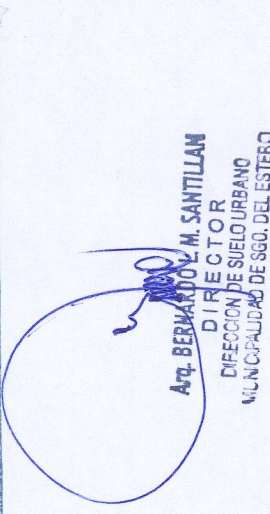

Al Excmo. Ma. Esther
DGO. OBRAS PRIVADAS
DIRECCION DE SUELO URBANO